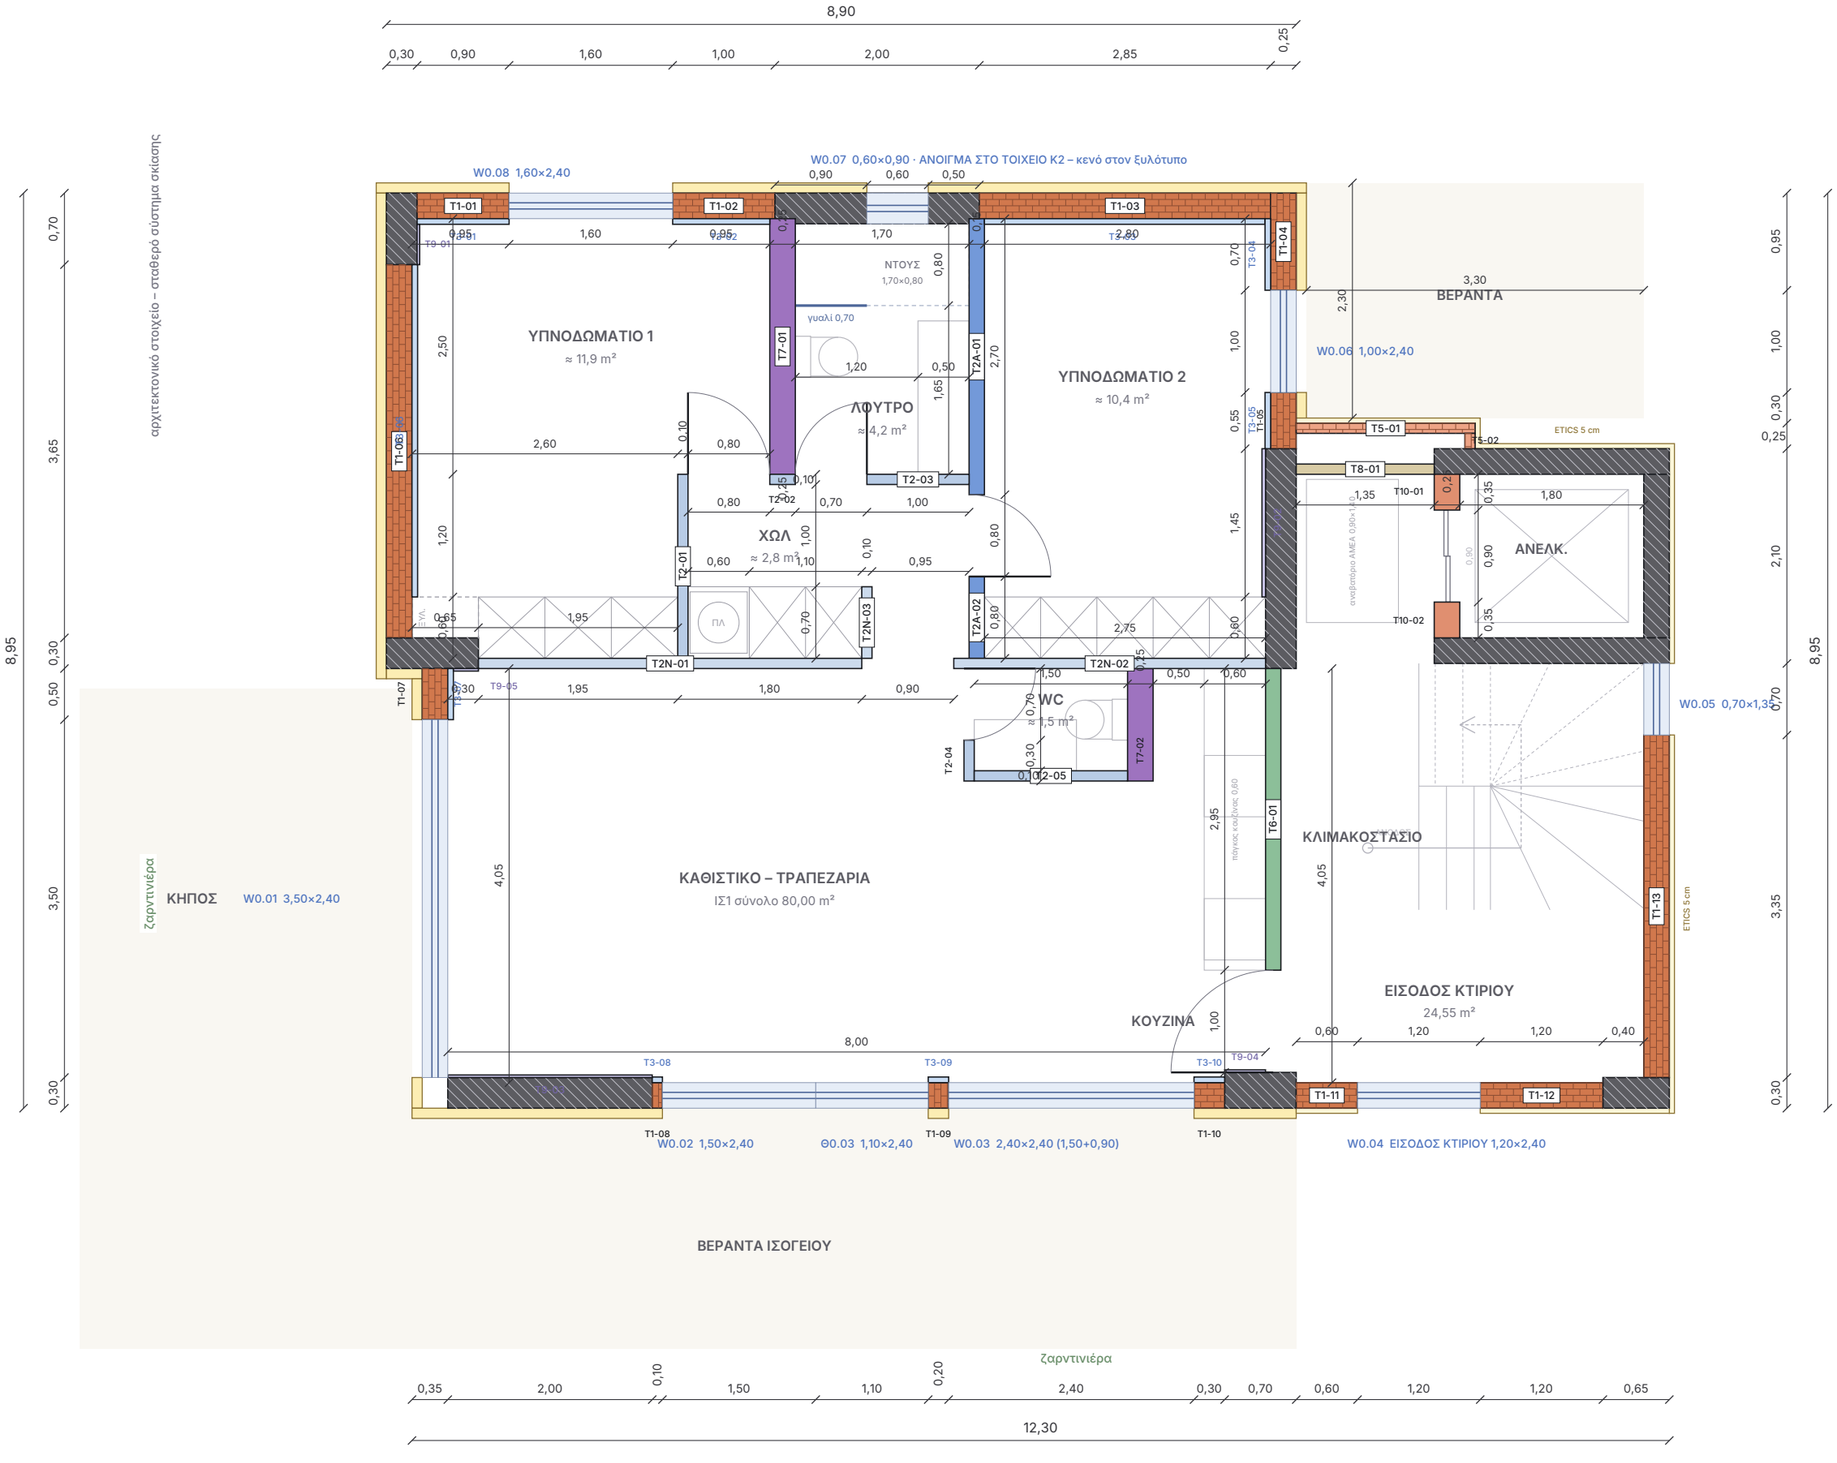


ΙΣΟΓΕΙΟ R00 – ΠΑΡΑΔΟΧΕΣ (05/11/2026)


- Οι δύο «Αποθήκες εκτός Σ.Δ.» του αρχιτέκτονα γίνονται ντουλάπες 0,60 χωνευτές (Γιάννης 05/11)
- Ντουλάπες: Υπν.1 1,95 + ξυλουργικό 0,40 μπροστά στο υποστύλωμα · Υπν.2 2,75 · πλυντήριο 0,60 + ντουλάπα 1,10 (0,70)
- Λουτρό: ντους 1,70×0,80 βάρεια, γυαλί 0,70 · λεκάνη στον Τ7-01 · πάγκος 0,50 ανατολικά
- WC 1,50×1,00: λεκάνη στον Τ7-02 (ανατολικά) · πάγκος 0,50 νότια · πόρτα γωνιακή από το καθιστικό
- Πόρτες μέσα στον χώρο, ισοπαχείς παραστάδες, ορθοστάτες UA 2 mm · είσοδος 1,00 μεντεσές νότια (ο αρχιτέκτονας την έχει προς την είσοδο κτιρίου)
- Τ6 15 cm προς είσοδο κτιρίου · μέτωπο ανελκυστήρα Τ10 25 cm · Τ3 και στις δύο παραστάδες κάθε κουφώματος
- W0.07 μέσα στο τοιχείο Κ2: κενό 0,60×0,90 στον ξυλότυπο (ποδιά +1,50)
- Θερμοπρόσοψη 10 cm διαμέρισμα · 5 cm είσοδος / πυρήνας · εξωτερικές παρειές όπως Α-10-GF
- Βεράντες / κήπος κατά Α-10-GF (χωρίς στηθαία) · σκάλα, ανελκυστήρας, αναβατόριο ΑΜΕΑ αχνά

ΕΡΓΟ	ΘΕΜΑ ΣΧΕΔΙΟΥ	ΒΑΣΗ	ΑΡ. ΣΧΕΔΙΟΥ
ΠΕΝΤΑΟΡΟΦΟ ΚΤΗΡΙΟ ΚΑΤΟΙΚΙΩΝ – ΑΡΓΥΡΟΥΠΟΛΗ Κωνσταντινουπόλεως 12 & Αγ. Βαρβάρας · Ο.Τ. 103-15 Εργοδότης: INTERKAT Α.Ε. · Κατασκευή: ARKAD Ι.Κ.Ε.	**ΚΑΤΟΨΗ ΤΟΙΧΟΠΟΙΙΩΝ – ΙΣΟΓΕΙΟΥ** Είδη τοιχοποιιών · διαστάσεις χάραξης · κουφώματα · εξώστες ΙΣΟΓΕΙΟ – ΙΣ1	Βάση: κάτοψη Α-10-GF (μελέτη εφαρμογής) · ξυλότυπος Σ3_ΕΦ · κανόνες Β1 R26	**Τ-01** **Κλίμακα 1:60 · Α3** 05/11/2026 · R00

T1 Εξωτερική οπτοπλινθοδομή

1:4

πάχος 25 cm

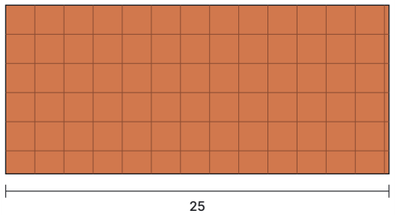

θερμομονωτικό τούβλο κάθετων οπών 25 cm · θερμοπρόσοψη 10 cm έξω · επένδυση T3 μέσα όπου σημειώνεται




Τοίχοι: T1-01, T1-02, T1-03, T1-04, T1-05, T1-06, T1-07, T1-08, T1-09, T1-10, T1-11, T1-12, T1-13

Μήκος 16,35 m · επιφάνεια ≈ 49,1 m²


T5 Οπτοπλινθοδομή πυρήνα

1:4

πάχος 10 cm

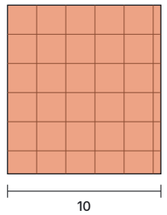

θερμομονωτικό τούβλο κάθετων οπών 10 cm · γύρω από τον πυρήνα (ανελκυστήρας – ηλεκτροστάσιο)

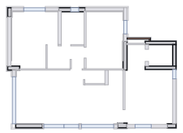


Τοίχοι: T5-01, T5-02

Μήκος 1,90 m · επιφάνεια ≈ 5,7 m²


T10 Μέτωπο ανελκυστήρα

1:4

πάχος 25 cm

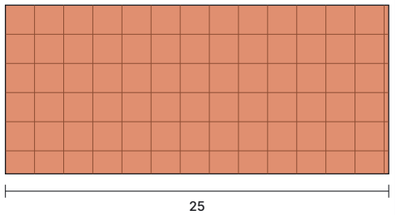

θερμομονωτικό τούβλο κάθετων οπών 25 cm · μέτωπο φρεατίου εκατέρωθεν της πόρτας 0,90 · ισοπαχές με τα τοιχεία 25 του φρεατίου (Σ5), περασιά και στις δύο παρειές, ώστε να κάθεται σωστά η κάσα της πόρτας ορόφου · θέση πόρτας προς επιβεβαίωση από τον προμηθευτή

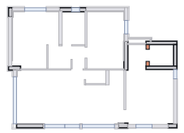


Τοίχοι: T10-01, T10-02

Μήκος 0,70 m · επιφάνεια ≈ 2,1 m²


T3 Επένδυση τοίχου

1:4

πάχος 5,5 cm

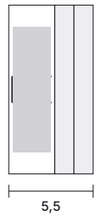

σκελετός 30 · 2 × γυψοσανίδα 12,5 · στις εσωτερικές παρειές των T1 – ΟΧΙ όπου πλακάκι ή ντουλάπα, ΟΧΙ στα έρκερ

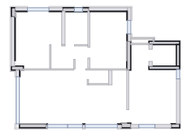


Τοίχοι: T3-01, T3-02, T3-03, T3-04, T3-05, T3-06, T3-07, T3-08, T3-09, T3-10

Μήκος 10,20 m · επιφάνεια ≈ 30,6 m²


T9 Επένδυση υποστυλώματος

1:4

πάχος 2,5 cm

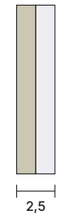

κόλλα + 1 × γυψοσανίδα 12,5 (ένα φύλλο) · στις παρειές υποστυλωμάτων μέσα στα διαμερίσματα – ΟΧΙ όπου πλακάκι ή ντουλάπα

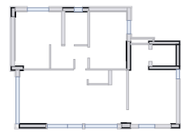


Τοίχοι: T9-01, T9-02, T9-03, T9-04, T9-05

Μήκος 4,49 m · επιφάνεια ≈ 13,5 m²

T2 Χώρισμα γυψοσανίδας

1:4

πάχος 10 cm

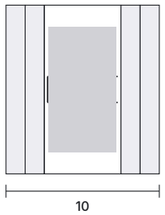

2 × γυψοσανίδα 12,5 · σκελετός CW 50 · 2 × γυψοσανίδα 12,5 · εσωτερικά χωρίσματα · ανθυγρή γυψοσανίδα στην πλευρά των λουτρών · ανοίγματα πορτών με ορθοστάτες UA 50 (2 mm)




Τοίχοι: T2-01, T2-02, T2-03, T2-04, T2-05

Μήκος 4,95 m · επιφάνεια ≈ 14,9 m²


T2N Χώρισμα γυψ. – πλευρά ντουλάπας

1:4

πάχος 8,75 cm

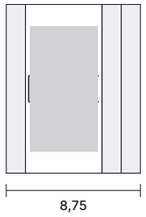

1 × γυψοσανίδα 12,5 (πλευρά ντουλάπας) · σκελετός CW 50 · 2 × γυψοσανίδα 12,5 · όπου η μία παρειά βλέπει σε ντουλάπα: ένα φύλλο αρκεί (κανόνας R15)

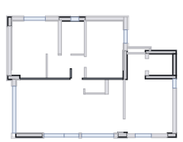


Τοίχοι: T2N-01, T2N-02, T2N-03

Μήκος 7,50 m · επιφάνεια ≈ 22,5 m²


T2A Χώρισμα γυψοσανίδας 15

1:4

πάχος 15 cm

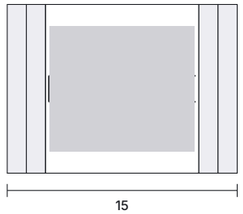

2 × γυψοσανίδα 12,5 · σκελετός CW 100 + πετροβάμβακας · 2 × γυψοσανίδα 12,5 · λουτρό γονέων / χωλ · υπνοδωμάτια · ανοίγματα πορτών με ορθοστάτες UA 100 (2 mm)

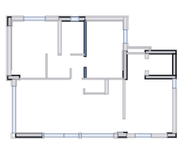


Τοίχοι: T2A-01, T2A-02

Μήκος 3,50 m · επιφάνεια ≈ 10,5 m²


T7 Τοίχος λεκάνης WC

1:4

πάχος 25 cm

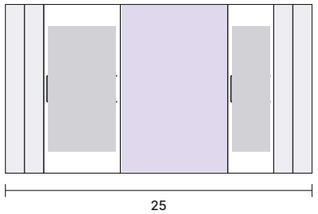

2 × γυψοσανίδα 12,5 · σκελετός CW 50 · κενό 12 cm (καζανάκι γυψοσανίδας στον σκελετό + κατακόρυφη στήλη Ø110, έξοδος Ø90) · σκελετός CW 30 · 2 × γυψοσανίδα 12,5 · ΟΛΟΙ οι τοίχοι λεκανών · ανθυγρή προς το λουτρό · στην πλευρά ντουλάπας 1 φύλλο · ανοίγματα πορτών με ορθοστάτες UA 50 (2 mm)

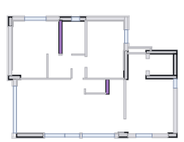


Τοίχοι: T7-01, T7-02

Μήκος 3,60 m · επιφάνεια ≈ 10,8 m²


T6 Τοίχος κλιμακοστασίου

1:4

πάχος 15 cm

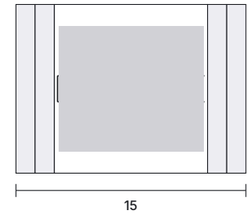

2 × γυψοσανίδα 12,5 πυράντοχη · σκελετός CW 100 + πετροβάμβακας · 2 × γυψοσανίδα 12,5 πυράντοχη · προς κοινόχρηστους χώρους · 15 cm · άνοιγμα πόρτας εισόδου (ασφαλείας) με ορθοστάτες UA 100 (2 mm) κατά Knauf

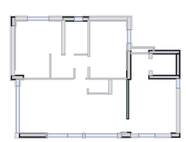


Τοίχοι: T6-01

Μήκος 2,95 m · επιφάνεια ≈ 8,8 m²


T8 Τοίχος shaft

1:4

πάχος 10 cm

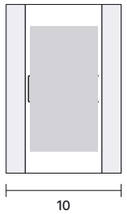

πλαίσιο + ανοιγόμενα φύλλα γυψοσανίδας · μέτωπο shaft ηλεκτρολογικών

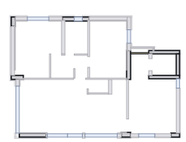

Τοίχοι: T8-01

Μήκος 1,35 m · επιφάνεια ≈ 4,1 m²

Επιφάνειες ενδεικτικές: μήκος × ύψος 3,00 m (τελικό δάπεδο – πλάκα) – οι τοίχοι ορίζονται μεταξύ ανοιγμάτων, χωρίς αφαίρεση κασών. T3 = επένδυση στην εσωτερική παρειά των T1 · T9 = περίμετρος υποστυλώματος × ύψος. R15: T2N = 1 φύλλο στην πλευρά ντουλάπας (T2N-01, T2N-02) · T7-01 1 φύλλο προς Υπν.1.

ΕΡΓΟ

ΠΕΝΤΑΟΡΟΦΟ ΚΤΗΡΙΟ ΚΑΤΟΙΚΙΩΝ – ΑΡΓΥΡΟΥΠΟΛΗ
Κωνσταντινουπόλεως 12 & Αγ. Βαρβάρας · Ο.Τ. 103-15
Εργοδότης: INTERKAT Α.Ε. · Κατασκευή: ARKAD Ι.Κ.Ε.

ΘΕΜΑ ΣΧΕΔΙΟΥ

ΕΙΔΗ ΤΟΙΧΟΠΟΙΙΩΝ – ΙΣΟΓΕΙΟΥ
Είδη τοιχοποιιών · ΙΣΟΓΕΙΟ – ΙΣ1
τομές 1:4 · μήκη – εμβαδά ανά είδος

ΒΑΣΗ

Βάση: κάτοψη τοιχοποιιών T-01 · κάτοψη A-10-GF

ΑΡ. ΣΧΕΔΙΟΥ

T-02
Κλίμακα 1:4 · A3
05/11/2026 · R00

ΠΡΟΜΕΤΡΗΣΗ ΤΟΙΧΟΠΟΙΙΩΝ – ΙΣΟΓΕΙΟ – ΙΣ1

τετραγωνικά ανά τυπολογία τοίχου · H = 3,00 m (τελικό δάπεδο – κάτω παρειά πλάκας) · μήκη στον άξονα, χωρίς αφαίρεση κουφωμάτων · R00

	Τύπος	Περιγραφή	Πάχος cm	Τοίχοι	Μήκος m	Επιφάνεια m²
ΤΟΥΒΛΑ						
	T1	Εξωτερική οπτοπλινθοδομή	25	13	16,35	**49,1**
	T5	Οπτοπλινθοδομή πυρήνα	10	2	1,90	**5,7**
	T10	Μέτωπο ανελκυστήρα	25	2	0,70	**2,1**
	Σύνολο τουβλα					**56,9 m²**
ΧΩΡΙΣΜΑΤΑ ΓΥΨΟΣΑΝΙΔΑΣ						
	T2	Χώρισμα γυψοσανίδας	10	5	4,95	**14,9**
	T2N	Χώρισμα γυψ. – πλευρά ντουλάπας	8,8	3	7,50	**22,5**
	T2A	Χώρισμα γυψοσανίδας 15	15	2	3,50	**10,5**
	T7	Τοίχος λεκάνης WC	25	2	3,60	**10,8**
	T6	Τοίχος κλιμακοστασίου	15	1	2,95	**8,8**
	T8	Τοίχος shaft	10	1	1,35	**4,1**
	Σύνολο χωρισματα γυψοσανιδας					**71,6 m²**
ΕΠΕΝΔΥΣΕΙΣ						
	T3	Επένδυση τοίχου	5,5	10	10,20	**30,6**
	T9	Επένδυση υποστυλώματος	2,5	5	4,49	**13,5**
	Σύνολο επενδυσεις					**44,1 m²**
	ΣΥΝΟΛΟ ΤΟΙΧΟΠΟΙΙΩΝ ΙΣ1					**172,5 m²**

ΘΕΡΜΟΠΡΟΣΟΨΗ (ETICS)

10 cm στις όψεις των διαμερισμάτων · 5 cm στο κλιμακοστάσιο / πυρήνα · ύψος 3,20 m (με τη μετώπη πλάκας) · καθαρά = όψη − κουφώματα + λαμπάδες/ανώφλια

Ζώνη	Μήκος όψης m	Μικτά m²	Κουφώματα m²	Λαμπάδες m²	Καθαρά m²
ETICS 10 cm – διαμερίσματα	29,30	93,8	−27,2	+5,9	**72,5**
ETICS 5 cm – κλιμακοστάσιο / πυρήνας	14,10	45,1	−3,8	+1,2	**42,5**
Σύνολο ETICS					**115,1 m²**

ΣΗΜΕΙΩΣΕΙΣ ΚΑΤΟΨΗΣ

• Θέσεις τοίχων και ανοιγμάτων κατά την κάτοψη ισογείου A-10-GF (EDGE 23/07/2026) με τους κανόνες του B1 R20. Διαστάσεις στο τούβλο / μπετό, χωρίς τη θερμοπρόσοψη. Υποστυλώματα / τοιχεία από τα μαύρα γεμίσματα του A-10-GF – ταυτίζονται με τον ξυλότυπο Σ3 (να επιβεβαιωθούν στον Σ3 πριν τη χάραξη).

• ΑΠΟΘΗΚΕΣ → ΝΤΟΥΛΑΠΕΣ (Γιάννης 05/11): η αποθήκη του Υπν.1 (1,10–3,57 × 3,80–5,00) και η αποθήκη του Υπν.2 (6,65–9,45 × 3,40–4,85) καταργούνται· τα δωμάτια μεγαλώνουν ως το y 4,45 και παίρνουν ντουλάπα 0,60 χωνευτή στο y 4,45–5,05. Οι εσωτερικοί τοίχοι τους (y 3,63–3,80 και y 3,25–3,40 ανατολικά) δεν κτίζονται.

• Υπν.1: ντουλάπα 1,70–3,65 (1,95) ανάμεσα στο Δ υποστύλωμα (0,80–1,70 × 4,85–5,15) και τον T2-01. Μπροστά από το υποστύλωμα (x 1,05–1,70) ξυλουργικό βάθους 0,40 που συνεχίζει τη ντουλάπα (ως το γυμνό μπετό, χωρίς T9). Πόρτα 0,80 γωνιακή 3,75–4,55 στο βόρειο άκρο του χωλ (όπως B1).

• ΧΩΛ 2,75 × 1,00 (y 3,35–4,35) με ντουλάπα πλυντηρίου 0,70 στο y 4,35–5,05 (πλυντήριο 3,75–4,35 + ντουλάπα 4,35–5,45), T2N-03 επιστροφή 5,45–5,55, άνοιγμα προς καθιστικό 5,45–6,35 (0,90). Τοίχοι που βλέπουν σε ντουλάπα: 1 φύλλο (T2N-01, T2N-02, T2N-03).

• ΛΟΥΤΡΟ 1,70 × 2,50 (x 4,80–6,50 · y 0,75–3,25): T7-01 λεκάνης δυτικά (σταθερή η παρειά Υπν.1 4,55), ντους 1,70×0,80 βόρεια (y 0,80–1,60) με γυάλινο διαχωριστικό 0,70 στο y 1,60 από τον T7-01, λεκάνη στον T7-01 (y 2,10), πάγκος 0,50 στον ανατολικό τοίχο (6,00–6,50 × 1,75–3,25), πόρτα 0,70 στο 4,80–5,50 (μεντεσές 5,50). W0.07 0,60×0,90 μέσα στο τοιχείο K2 (x 5,50–6,10): κενό στον ξυλότυπο από τώρα (ποδιά +1,50).

• WC 1,50 × 1,00 (x 6,55–8,05 · y 5,15–6,15): ο αρχιτέκτονας το έχει 1,50 × 0,95 με λεκάνη στον βόρειο τοίχο· εδώ η λεκάνη πάει στον ανατολικό τοίχο T7-02 (25 cm) ώστε ο βόρειος τοίχος να μείνει T2N-02 (πλάτη ντουλάπας Υπν.2), πάγκος 0,50 νότια, πόρτα 0,70 γωνιακή 5,15–5,85 στον δυτικό τοίχο (μεντεσές 5,15, διπλώνει στον βόρειο τοίχο).

• ΚΟΥΖΙΝΑ: πάγκος 0,60 στον ανατολικό τοίχο (x 8,80–9,40, y 5,15–8,10) κατά A-10-GF· τελειώνει στο 8,10 για την πόρτα εισόδου. Πίσω από τον πάγκο χωρίς επένδυση (ο T6-01 είναι γυψοσανίδα). Χωρίς T3 στους πεσσούς του νότιου τοίχου πίσω από πάγκο.

• ΕΙΣΟΔΟΣ ΔΙΑΜΕΡΙΣΜΑΤΟΣ: πόρτα ασφαλείας 1,00 στον T6-01 (y 8,10–9,10, ως το N υποστύλωμα), ανοίγει ΜΕΣΑ με μεντεσέ νότια (9,10) και διπλώνει στον νότιο τοίχο (κανόνας B1 R20). Ο αρχιτέκτονας τη δείχνει να ανοίγει προς την είσοδο κτιρίου – να επιβεβαιωθεί. Ορθοστάτες UA 100 + ψευτόκασα προμηθευτή.

• ΕΙΣΟΔΟΣ ΚΤΙΡΙΟΥ 24,55 m²: πόρτα W0.04 1,20×2,40 στον νότιο τοίχο (10,30–11,50), W0.05 0,70×1,35 ανατολικά (5,10–5,80), αναβατόριο ΑΜΕΑ 0,90×1,40 δυτικά (κύκλος R0,75), σκάλα και ανελκυστήρας αχνά. Μέτωπο ανελκυστήρα T10-01/T10-02 25 cm (= τοιχεία φρεατίου), πόρτα 0,90 στο y 3,60–4,50. Shaft H/M T8-01 στο 3,15–3,25 (όπως B1).

• ΚΟΥΦΩΜΑΤΑ (πίνακας κουφωμάτων A-10-GF): W0.08 1,60×2,40 (2,00–3,60) · W0.07 0,60×0,90 · W0.06 1,00×2,40 (1,45–2,45) · W0.01 3,50×2,40 (5,65–9,15) · W0.02 1,50 (3,50–5,00) · Θ0.03 πόρτα 1,10 (5,00–6,10) · W0.03 2,40 = 1,50 + 0,90 (6,30–8,70, ΠΡΟΣ ΕΠΙΒΕΒΑΙΩΣΗ στον πίνακα) · W0.04 1,20 · W0.05 0,70×1,35. Οι πεσσοί 3,40–3,50 (0,10), 6,10–6,30 (0,20), 8,70–9,00 (0,30) όπως ο αρχιτέκτονας – να ελεγχθούν με τον πίνακα κουφωμάτων. T3 και στις δύο παραστάδες.

• ΘΕΡΜΟΠΡΟΣΟΨΗ: 10 cm στο διαμέρισμα (Β, Δ, Ν όψεις και Α του Υπν.2), 5 cm στον πυρήνα / είσοδο κτιρίου (T5-01, τοιχείο ανελκυστήρα, T1-13, νότιος τοίχος εισόδου). Η δυτική όψη κάνει σκαλοπάτι στο y 5,15 (από x 0,80 σε 1,15) – η λωρίδα γυρίζει στη νότια παρειά του Δ υποστυλώματος.

• ΥΨΟΣ ισογείου 3,00 (πλάκα οροφής +3,65 κατά Σ3) – οι επιφάνειες του T-03 με H = 3,00. Ηκαθ. 2,50 των πρώην αποθηκών δεν ισχύει πλέον.