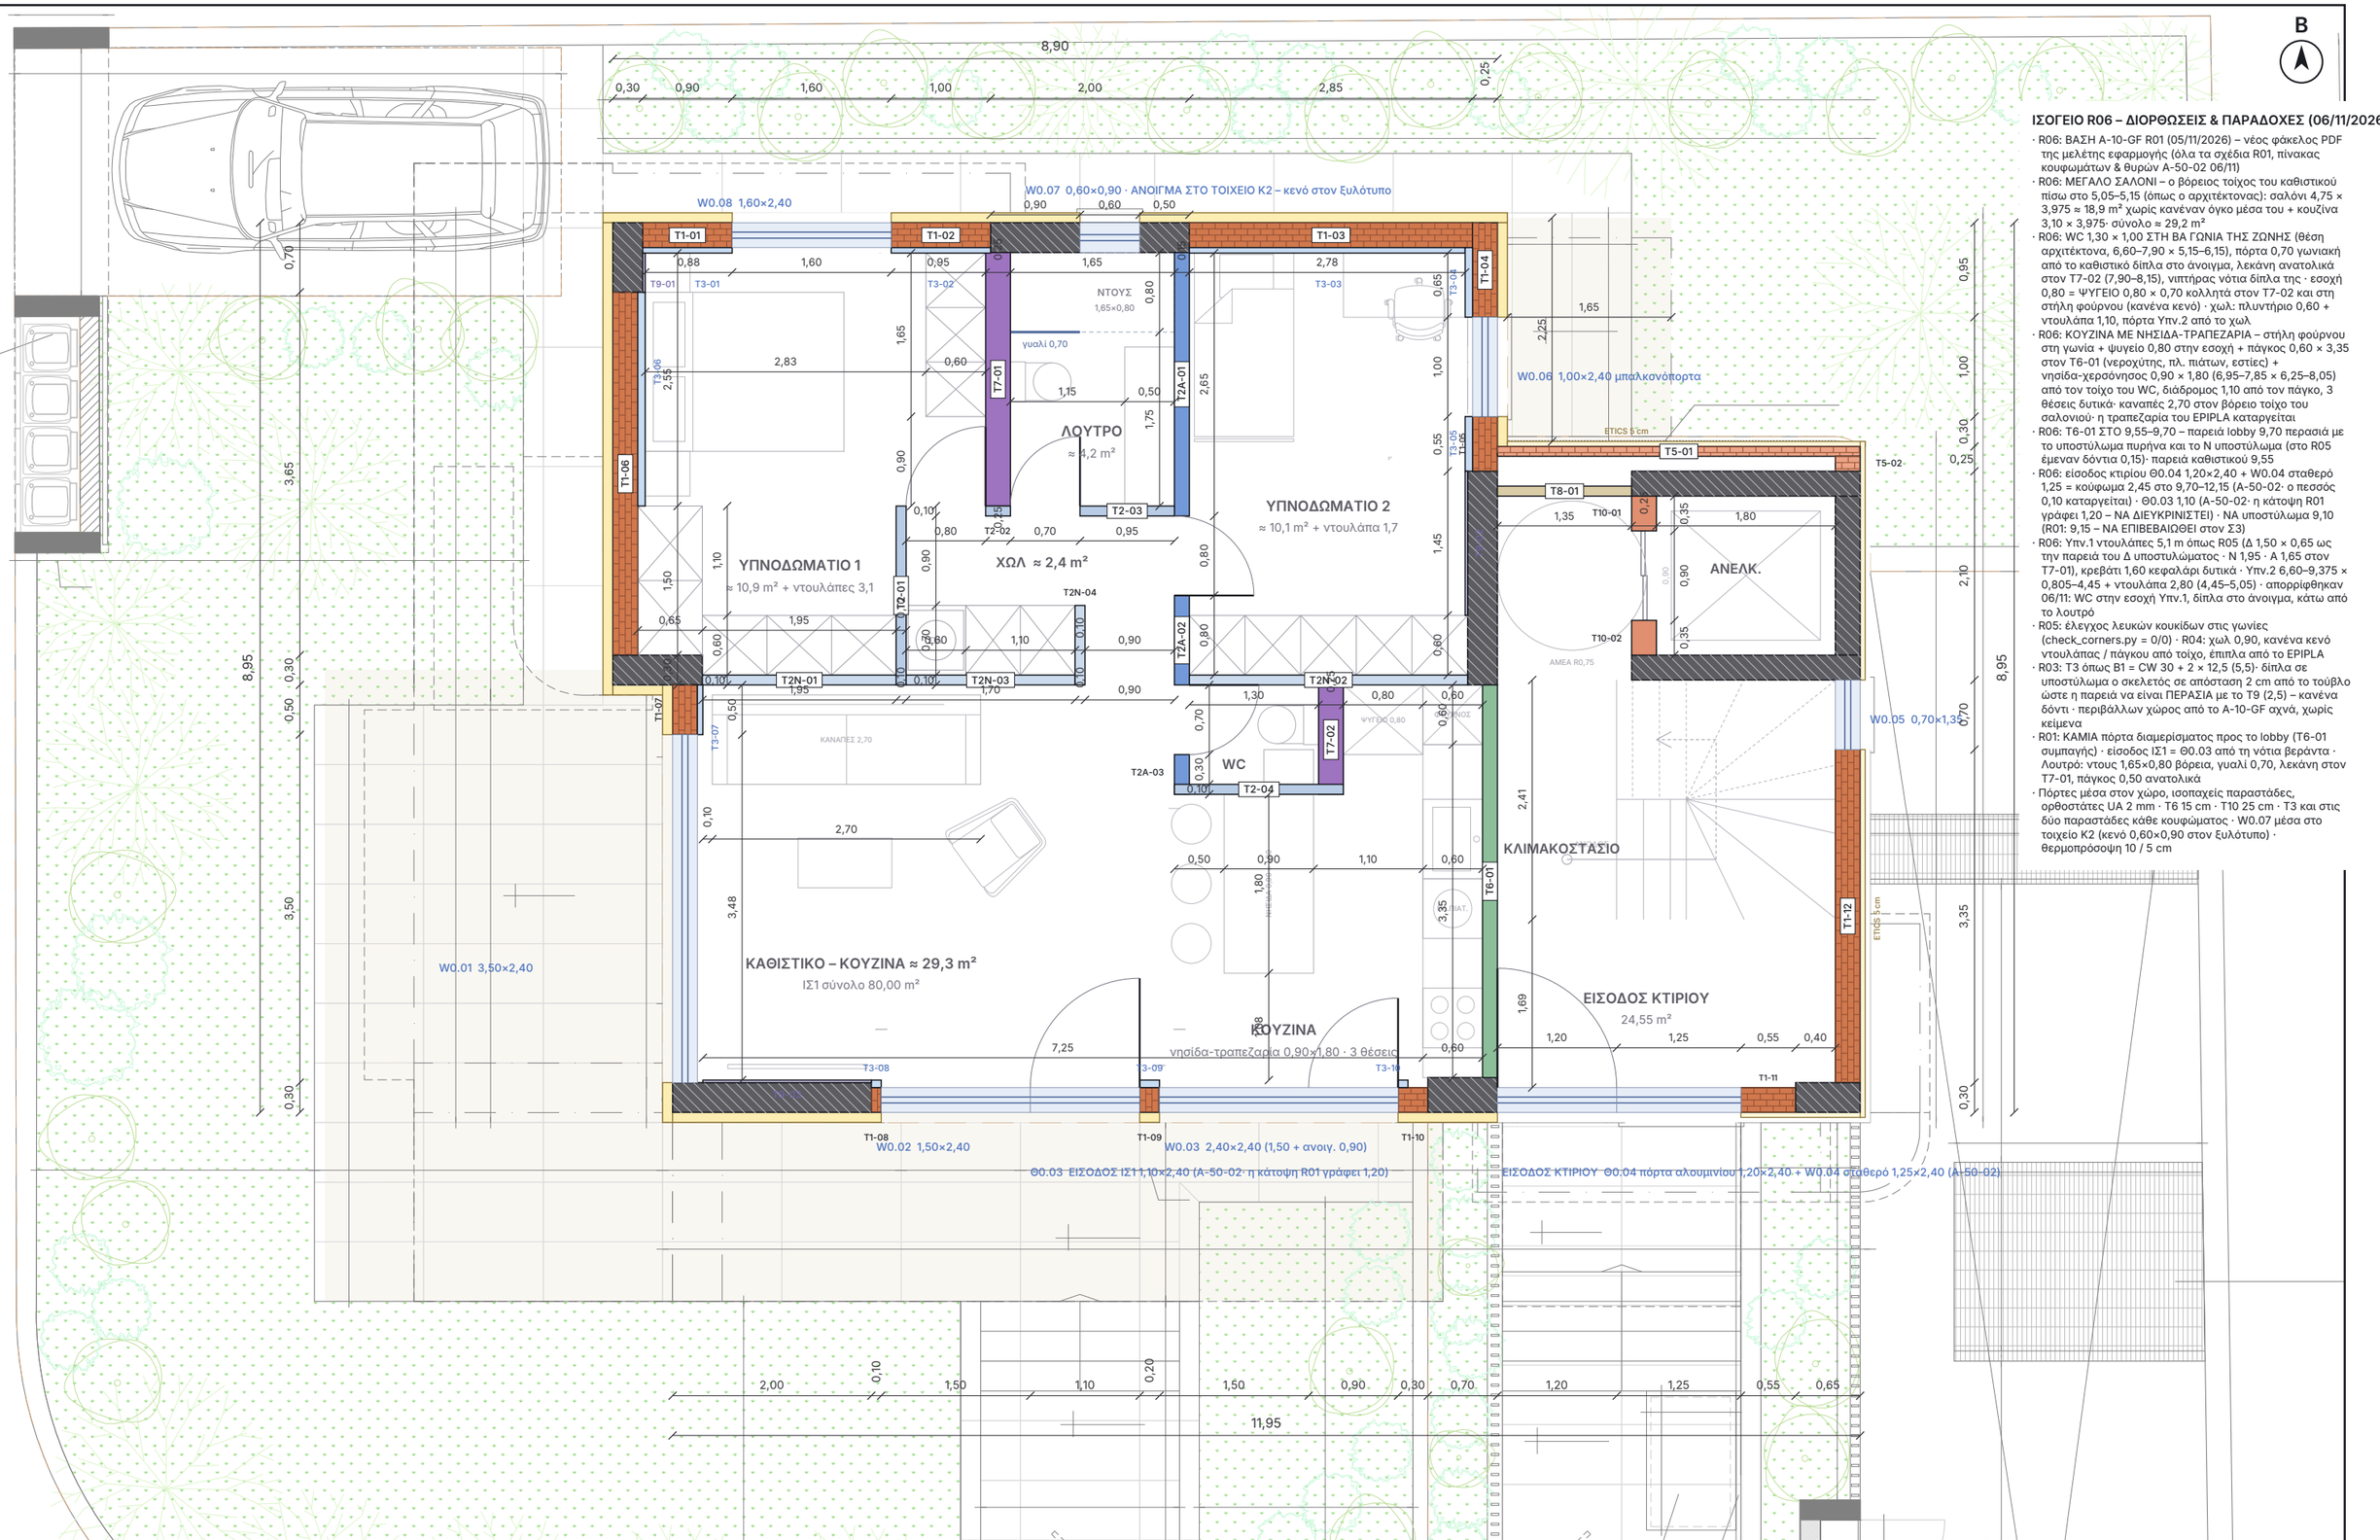



ΙΣΟΓΕΙΟ R06 – ΔΙΟΡΘΩΣΕΙΣ & ΠΑΡΑΔΟΧΕΣ (06/11/2026)

- R06: ΒΑΣΗ A-10-GF R01 (05/11/2026) – νέος φάκελος PDF της μελέτης εφαρμογής (όλα τα σχέδια R01, πίνακας κουφωμάτων & θυρών A-50-02 06/11)
- R06: ΜΕΓΑΛΟ ΣΑΛΟΝΙ – ο βορειος τοίχος του καθιστικού πίσω στο 5,05–5,15 (όπως ο αρχιτέκτονας): σαλόνι 4,75 × 3,975 ≈ 18,9 m² χωρίς κανέναν όγκο μέσα του + κουζίνα 3,10 × 3,975· σύνολο ≈ 29,2 m²
- R06: WC 1,30 × 1,00 ΣΤΗ ΒΑ ΓΩΝΙΑ ΤΗΣ ΖΩΝΗΣ (θέση αρχιτέκτονα, 6,60–7,90 × 5,15–6,15), πόρτα 0,70 γωνιακή από το καθιστικό δίπλα στο άνοιγμα, λεκάνη ανατολικά στον T7-02 (7,90–8,15), νιπτήρας νότια δίπλα της · εσοχή 0,80 = ΨΥΓΕΙΟ 0,80 × 0,70 κολλητά στον T7-02 και στη στήλη φούρνου (κανένα κενό) · χωλ: πλυντήριο 0,60 + ντουλάπα 1,10, πόρτα Υπν.2 από το χωλ
- R06: ΚΟΥΖΙΝΑ ΜΕ ΝΗΣΙΔΑ-ΤΡΑΠΕΖΑΡΙΑ – στήλη φούρνου στη γωνία + ψυγείο 0,80 στην εσοχή + πάγκος 0,60 × 3,35 στον T6-01 (νεροχύτης, πλ. πιάτων, εστίες) + νησίδα-χερσόνησος 0,90 × 1,80 (6,95–7,85 × 6,25–8,05) από τον τοίχο του WC, διάδρομος 1,10 από τον πάγκο, 3 θέσεις δυτικά· καναπές 2,70 στον βόρειο τοίχο του σαλονιού· η τραπεζαρία του EPIPLA καταργείται
- R06: T6-01 ΣΤΟ 9,55–9,70 – παρειά lobby 9,70 περασιά με το υποστύλωμα πυρήνα και το N υποστύλωμα (στο R05 έμεναν δόντια 0,15)· παρειά καθιστικού 9,55
- R06: είσοδος κτιρίου Θ0.04 1,20×2,40 + W0.04 σταθερό 1,25 = κούφωμα 2,45 στο 9,70–12,15 (A-50-02· ο πεσσός 0,10 καταργείται) · Θ0.03 1,10 (A-50-02· η κάτοψη R01 γράφει 1,20 – ΝΑ ΔΙΕΥΚΡΙΝΙΣΤΕΙ) · ΝΑ υποστύλωμα 9,10 (R01: 9,15 – ΝΑ ΕΠΙΒΕΒΑΙΩΘΕΙ στον Σ3)
- R06: Υπν.1 ντουλάπες 5,1 m όπως R05 (Δ 1,50 × 0,65 ως την παρειά του Δ υποστυλώματος · N 1,95 · Α 1,65 στον T7-01), κρεβάτι 1,60 κεφαλάρι δυτικά · Υπν.2 6,60–9,375 × 0,805–4,45 + ντουλάπα 2,80 (4,45–5,05) · απορρίφθηκαν 06/11: WC στην εσοχή Υπν.1, δίπλα στο άνοιγμα, κάτω από το λουτρό
- R05: έλεγχος λευκών κουκίδων στις γωνίες (check_corners.py = 0/0) · R04: χωλ 0,90, κανένα κενό ντουλάπας / πάγκου από τοίχο, έπιπλα από το EPIPLA
- R03: T3 όπως B1 = CW 30 + 2 × 12,5 (5,5)· δίπλα σε υποστύλωμα ο σκελετός σε απόσταση 2 cm από το τούβλο ώστε η παρειά να είναι ΠΕΡΑΣΙΑ με το T9 (2,5) – κανένα δόντι · περιβάλλων χώρος από το A-10-GF αχνά, χωρίς κείμενα
- R01: ΚΑΜΙΑ πόρτα διαμερίσματος προς το lobby (T6-01 συμπαγής) · είσοδος ΙΣ1 = Θ0.03 από τη νότια βεράντα · Λουτρό: ντους 1,65×0,80 βόρεια, γυαλί 0,70, λεκάνη στον T7-01, πάγκος 0,50 ανατολικά
- Πόρτες μέσα στον χώρο, ισοπαχείς παραστάδες, ορθοστάτες UA 2 mm · T6 15 cm · T10 25 cm · T3 και στις δύο παραστάδες κάθε κουφώματος · W0.07 μέσα στο τοιχείο Κ2 (κενό 0,60×0,90 στον ξυλότυπο) · θερμοπρόσοψη 10 / 5 cm

ΕΡΓΟ	ΘΕΜΑ ΣΧΕΔΙΟΥ	ΒΑΣΗ	ΑΡ. ΣΧΕΔΙΟΥ
ΠΕΝΤΑΟΡΟΦΟ ΚΤΗΡΙΟ ΚΑΤΟΙΚΙΩΝ – ΑΡΓΥΡΟΥΠΟΛΗ Κωνσταντινουπόλεως 12 & Αγ. Βαρβάρας · Ο.Τ. 103-15 Εργοδότης: INTERKAT Α.Ε. · Κατασκευή: ARKAD Ι.Κ.Ε.	**ΚΑΤΟΨΗ ΤΟΙΧΟΠΟΙΙΩΝ – ΙΣΟΓΕΙΟΥ** Είδη τοιχοποιιών · διαστάσεις χάραξης · κουφώματα · εξώστες ΙΣΟΓΕΙΟ – ΙΣ1	Βάση: A-10-GF R01 (05/11/2026, Drive) · Σ3_ΕΦ · κανόνες B1 R20	**T-01** **Κλίμακα 1:60 · A3** 06/11/2026 · R06

T1 Εξωτερική οπτοπλινθοδομή 1:4

πάχος 25 cm

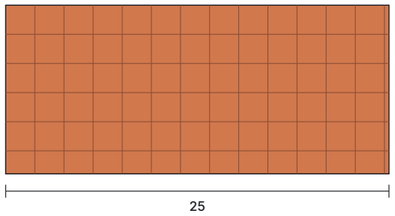

θερμομονωτικό τούβλο κάθετων οπών 25 cm · θερμοπρόσοψη 10 cm έξω · επένδυση T3 μέσα όπου σημειώνεται




Τοίχοι: T1-01, T1-02, T1-03, T1-04, T1-05, T1-06, T1-07, T1-08, T1-09, T1-10, T1-11, T1-12

Μήκος 15,10 m · επιφάνεια ≈ 45,3 m²

T5 Οπτοπλινθοδομή πυρήνα 1:4

πάχος 10 cm

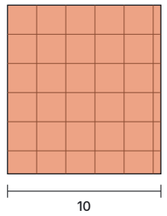

θερμομονωτικό τούβλο κάθετων οπών 10 cm · γύρω από τον πυρήνα (ανελκυστήρας – ηλεκτροστάσιο)




Τοίχοι: T5-01, T5-02


Μήκος 3,90 m · επιφάνεια ≈ 11,7 m²

T10 Μέτωπο ανελκυστήρα 1:4

πάχος 25 cm

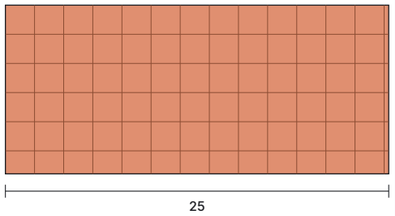

θερμομονωτικό τούβλο κάθετων οπών 25 cm · μέτωπο φρεατίου εκατέρωθεν της πόρτας 0,90 · ισοπαχές με τα τοιχεία 25 του φρεατίου (Σ5), περασιά και στις δύο παρειές, ώστε να κάθεται σωστά η κάσα της πόρτας ορόφου · θέση πόρτας προς επιβεβαίωση από τον προμηθευτή

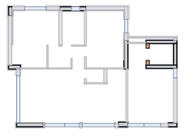


Τοίχοι: T10-01, T10-02

Μήκος 0,70 m · επιφάνεια ≈ 2,1 m²

T3 Επένδυση τοίχου 1:4

πάχος 5,5 cm

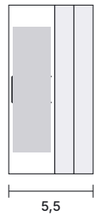

σκελετός 30 · 2 × γυψοσανίδα 12,5 · στις εσωτερικές παρειές των T1 – ΟΧΙ όπου πλακάκι ή ντουλάπα, ΟΧΙ στα έρκερ




Τοίχοι: T3-01, T3-02, T3-03, T3-04, T3-05, T3-06, T3-07, T3-08, T3-09, T3-10

Μήκος 8,98 m · επιφάνεια ≈ 26,9 m²

T9 Επένδυση υποστυλώματος 1:4

πάχος 2,5 cm

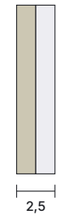

κόλλα + 1 × γυψοσανίδα 12,5 (ένα φύλλο) · στις παρειές υποστυλωμάτων μέσα στα διαμερίσματα – ΟΧΙ όπου πλακάκι ή ντουλάπα




Τοίχοι: T9-01, T9-02, T9-03


Μήκος 3,54 m · επιφάνεια ≈ 10,6 m²

T2 Χώρισμα γυψοσανίδας 1:4

πάχος 10 cm

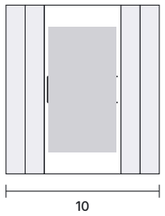

2 × γυψοσανίδα 12,5 · σκελετός CW 50 · 2 × γυψοσανίδα 12,5 · εσωτερικά χωρίσματα · ανθυγρή γυψοσανίδα στην πλευρά των λουτρών · ανοίγματα πορτών με ορθοστάτες UA 50 (2 mm)

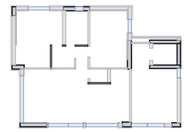


Τοίχοι: T2-01, T2-02, T2-03, T2-04


Μήκος 4,70 m · επιφάνεια ≈ 14,1 m²

T2N Χώρισμα γυψ. – πλευρά ντουλάπας 1:4

πάχος 8,75 cm

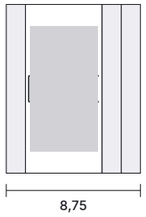

1 × γυψοσανίδα 12,5 (πλευρά ντουλάπας) · σκελετός CW 50 · 2 × γυψοσανίδα 12,5 · όπου η μία παρειά βλέπει σε ντουλάπα: ένα φύλλο αρκεί (κανόνας R15)

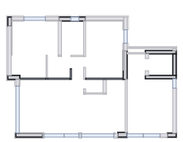


Τοίχοι: T2N-01, T2N-02, T2N-03, T2N-04


Μήκος 7,25 m · επιφάνεια ≈ 21,8 m²

T2A Χώρισμα γυψοσανίδας 15 1:4

πάχος 15 cm

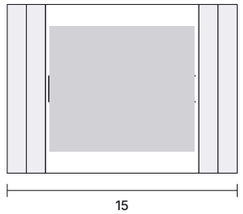

2 × γυψοσανίδα 12,5 · σκελετός CW 100 + πετροβάμβακας · 2 × γυψοσανίδα 12,5 · λουτρό γονέων / χωλ · υπνοδωμάτια · ανοίγματα πορτών με ορθοστάτες UA 100 (2 mm)

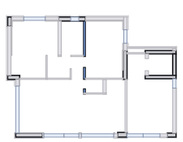


Τοίχοι: T2A-01, T2A-02, T2A-03


Μήκος 3,95 m · επιφάνεια ≈ 11,9 m²

T7 Τοίχος λεκάνης WC 1:4

πάχος 25 cm

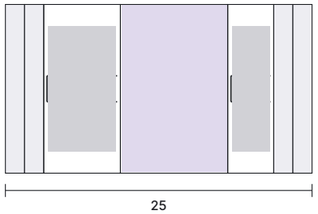

2 × γυψοσανίδα 12,5 · σκελετός CW 50 · κενό 12 cm (καζανάκι γυψοσανίδας στον σκελετό + κατακόρυφη στήλη Ø110, έξοδος Ø90) · σκελετός CW 30 · 2 × γυψοσανίδα 12,5 · ΟΛΟΙ οι τοίχοι λεκανών · ανθυγρή προς το λουτρό · στην πλευρά ντουλάπας 1 φύλλο · ανοίγματα πορτών με ορθοστάτες UA 50 (2 mm)

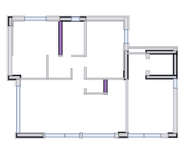


Τοίχοι: T7-01, T7-02


Μήκος 3,65 m · επιφάνεια ≈ 10,9 m²

T6 Τοίχος κλιμακοστασίου 1:4

πάχος 15 cm

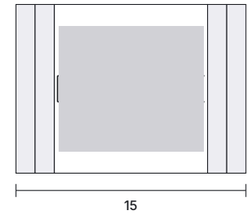

2 × γυψοσανίδα 12,5 πυράντοχη · σκελετός CW 100 + πετροβάμβακας · 2 × γυψοσανίδα 12,5 πυράντοχη · προς κοινόχρηστους χώρους · 15 cm · άνοιγμα πόρτας εισόδου (ασφαλείας) με ορθοστάτες UA 100 (2 mm) κατά Knauf

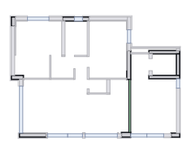


Τοίχοι: T6-01


Μήκος 3,95 m · επιφάνεια ≈ 11,8 m²

T8 Τοίχος shaft 1:4

πάχος 10 cm

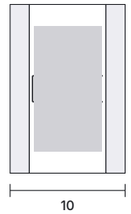

πλαίσιο + ανοιγόμενα φύλλα γυψοσανίδας · μέτωπο shaft ηλεκτρολογικών

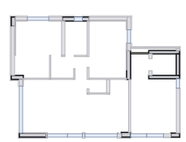

Τοίχοι: T8-01

Μήκος 1,35 m · επιφάνεια ≈ 4,1 m²

Επιφάνειες ενδεικτικές: μήκος × ύψος 3,00 m (τελικό δάπεδο – πλάκα) – οι τοίχοι ορίζονται μεταξύ ανοιγμάτων, χωρίς αφαίρεση κασών. T3 = επένδυση στην εσωτερική παρειά των T1 · T9 = περίμετρος υποστυλώματος × ύψος. R15: T2N = 1 φύλλο στην πλευρά ντουλάπας (T2N-01, T2N-02) · T7-01 1 φύλλο προς Υπν.1.

ΕΡΓΟ

ΠΕΝΤΑΟΡΟΦΟ ΚΤΗΡΙΟ ΚΑΤΟΙΚΙΩΝ – ΑΡΓΥΡΟΥΠΟΛΗ
Κωνσταντινουπόλεως 12 & Αγ. Βαρβάρας · Ο.Τ. 103-15
Εργοδότης: INTERKAT Α.Ε. · Κατασκευή: ARKAD Ι.Κ.Ε.

ΘΕΜΑ ΣΧΕΔΙΟΥ

ΕΙΔΗ ΤΟΙΧΟΠΟΙΙΩΝ – ΙΣΟΓΕΙΟΥ
Είδη τοιχοποιιών · ΙΣΟΓΕΙΟ – ΙΣ1
τομές 1:4 · μήκη – εμβαδά ανά είδος

ΒΑΣΗ

Βάση: κάτοψη τοιχοποιιών T-01 · κάτοψη A-10-GF

ΑΡ. ΣΧΕΔΙΟΥ

T-02
Κλίμακα 1:4 · A3
06/11/2026 · R06

ΠΡΟΜΕΤΡΗΣΗ ΤΟΙΧΟΠΟΙΙΩΝ – ΙΣΟΓΕΙΟ – ΙΣ1

τετραγωνικά ανά τυπολογία τοίχου · H = 3,00 m (τελικό δάπεδο – κάτω παρειά πλάκας) · μήκη στον άξονα, χωρίς αφαίρεση κουφωμάτων · R06

	Τύπος	Περιγραφή	Πάχος cm	Τοίχοι	Μήκος m	Επιφάνεια m²
ΤΟΥΒΛΑ						
	T1	Εξωτερική οπτοπλινθοδομή	25	12	15,10	**45,3**
	T5	Οπτοπλινθοδομή πυρήνα	10	2	3,90	**11,7**
	T10	Μέτωπο ανελκυστήρα	25	2	0,70	**2,1**
	Σύνολο τουβλα					**59,1 m²**
ΧΩΡΙΣΜΑΤΑ ΓΥΨΟΣΑΝΙΔΑΣ						
	T2	Χώρισμα γυψοσανίδας	10	4	4,70	**14,1**
	T2N	Χώρισμα γυψ. – πλευρά ντουλάπας	8,8	4	7,25	**21,8**
	T2A	Χώρισμα γυψοσανίδας 15	15	3	3,95	**11,9**
	T7	Τοίχος λεκάνης WC	25	2	3,65	**10,9**
	T6	Τοίχος κλιμακοστασίου	15	1	3,95	**11,8**
	T8	Τοίχος shaft	10	1	1,35	**4,1**
	Σύνολο χωρισματα γυψοσανιδας					**74,6 m²**
ΕΠΕΝΔΥΣΕΙΣ						
	T3	Επένδυση τοίχου	5,5	10	8,98	**26,9**
	T9	Επένδυση υποστυλώματος	2,5	3	3,54	**10,6**
	Σύνολο επενδυσεις					**37,5 m²**
	ΣΥΝΟΛΟ ΤΟΙΧΟΠΟΙΙΩΝ ΙΣ1					**171,2 m²**

ΘΕΡΜΟΠΡΟΣΟΨΗ (ETICS)

10 cm στις όψεις των διαμερισμάτων · 5 cm στο κλιμακοστάσιο / πυρήνα · ύψος 3,20 m (με τη μετώπη πλάκας) · καθαρά = όψη − κουφώματα + λαμπάδες/ανώφλια

Ζώνη	Μήκος όψης m	Μικτά m²	Κουφώματα m²	Λαμπάδες m²	Καθαρά m²
ETICS 10 cm – διαμερίσματα	29,40	94,1	−27,2	+5,9	**72,8**
ETICS 5 cm – κλιμακοστάσιο / πυρήνας	14,05	45,0	−6,8	+2,0	**40,2**
Σύνολο ETICS					**113,0 m²**

ΣΗΜΕΙΩΣΕΙΣ ΚΑΤΟΨΗΣ

• Θέσεις τοίχων και ανοιγμάτων κατά την κάτοψη ισογείου A-10-GF R01 (EDGE, μελέτη εφαρμογής, αναθεώρηση R01 05/11/2026, φάκελος PDF της μελέτης εφαρμογής στο Drive του έργου) με τους κανόνες του B1 R20 και τις αλλαγές R01–R06 του Γιάννη. Διαστάσεις στο τούβλο / μπετό και στις παρειές της γυψοσανίδας, χωρίς τη θερμοπρόσοψη. Υποστυλώματα / τοιχεία από τα μαύρα γεμίσματα του A-10-GF – ταυτίζονται με τον ξυλότυπο Σ3 (να επιβεβαιωθούν στον Σ3 πριν τη χάραξη· το R01 δείχνει το N υποστύλωμα στο 9,15–9,45 αντί 9,10–9,45 – εδώ 9,10 όπως B1).

• ΤΙ ΑΛΛΑΞΕ ΣΤΟ A-10-GF R01 (05/11/2026) σε σχέση με το R00 (23/07/2026): μόνο ετικέτες θυρών και μικρά στοιχεία – Θ0.03 γράφεται «1,20×2,40» (η γεωμετρία της κάτοψης και ο πίνακας A-50-02 λένε 1,10 → κρατήθηκε 1,10, ΝΑ ΔΙΕΥΚΡΙΝΙΣΤΕΙ), είσοδος κτιρίου Θ0.04 1,20 (ήταν 1,00) + W0.04 1,25 (ήταν 1,20), πύλες περίφραξης Θ0.02 / Θ0.04, γκαραζόπορτα Θ0.01 2,50×2,10, N υποστύλωμα 9,15, διακεκομμένες προβολές στο lobby και στη ΒΑ βεράντα. Οι τοίχοι του διαμερίσματος δεν άλλαξαν.

• Τ3 ΠΕΡΑΣΙΑ (R03, όπως B1): Τ3 = σκελετός CW 30 + 2 × γυψοσανίδα 12,5 (5,5 cm). Τα υποστυλώματα (30) προεξέχουν 5 cm από την εσωτερική παρειά του τούβλου (25) και παίρνουν κολλητή γυψοσανίδα Τ9 2,5 cm· όπου η Τ3 συνεχίζει δίπλα σε υποστύλωμα, ο σκελετός CW 30 στήνεται σε απόσταση 2 cm από το τούβλο ώστε η παρειά της γυψοσανίδας να είναι στο ίδιο επίπεδο με το Τ9: Τ3-06 (παρειά 1,125 = Τ9-01), Τ3-04/Τ3-05 (9,375 = Τ9-02), Τ3-08/09/10 (9,125 = Τ9-03). Αλλού η Τ3 κολλητά στο τούβλο: Β 0,805 · Δ καθιστικού 1,705. Όπου πλακάκι, ντουλάπα ή πάγκος: χωρίς Τ3 / Τ9 (γυμνό τούβλο / μπετό).

• ΜΕΓΑΛΟ ΣΑΛΟΝΙ (R06 – Γιάννης: «το σαλόνι δεν δουλεύει στο 3,5, θέλει 3,9 και πάνω σίγουρα», «πολύ μικρό καθιστικό έτσι, σκέψου κάτι άλλο, μην περιορίζεσαι, βρες τη βέλτιστη λύση»): ο βόρειος τοίχος του καθιστικού γυρίζει στο y 5,05–5,15 (όπως ο αρχιτέκτονας και το R04): T2N-01 (1,70–3,65, ντουλάπα Υπν.1) · T2-01 · T2N-03 (3,75–5,45, πλυντήριο + ντουλάπα χωλ) · T2N-04 (5,45–5,55) · άνοιγμα 0,90 (5,55–6,45) · T2A-02 / T2N-02 (6,45–9,40, ντουλάπα Υπν.2). Σαλόνι 1,705–6,45 × 5,15–9,125 = 4,75 × 3,975 ≈ 18,9 m² (μπροστά στο W0.01 3,50 και το W0.02), χωρίς κανέναν όγκο μέσα του· κουζίνα 6,45–9,55 × 3,975 με το WC στη ΒΑ γωνία της· σύνολο ≈ 29,3 m². Διαδρομή Θ0.03 (5,00–6,10) → άνοιγμα χωλ (5,55–6,45) ευθεία, με την πολυθρόνα 0,40 δυτικότερα. Απορρίφθηκαν 06/11: R05 (τοίχος στο 5,45–5,55, σαλόνι 3,575), WC στην εσοχή Υπν.1, WC δίπλα στο άνοιγμα με προεξοχή 1,10 στο σαλόνι, WC κάτω από το λουτρό με πόρτα Υπν.2 από το καθιστικό.

• WC ΣΤΗ ΒΑ ΓΩΝΙΑ ΤΗΣ ΖΩΝΗΣ ΚΑΘΙΣΤΙΚΟΥ-ΚΟΥΖΙΝΑΣ (R06, θέση αρχιτέκτονα – Γιάννης: «βάλε το WC στην κουζίνα, όχι στο δωμάτιο» / «το από πού θα μπαίνεις δεν με νοιάζει»): WC 6,60–7,90 × 5,15–6,15 (1,30 × 1,00 = 1,3 m²). Είναι η μόνη θέση που είναι στην κουζίνα, δεν κόβει το σαλόνι, δεν μπαίνει σε δωμάτιο και αφήνει την πόρτα του Υπν.2 στο χωλ. Πόρτα 0,70 γωνιακή στον δυτικό τοίχο (y 5,15–5,85), από το καθιστικό δίπλα στο άνοιγμα του χωλ, μεντεσές βόρεια 5,15, ανοίγει μέσα και διπλώνει στον βόρειο τοίχο (όπως A-10-GF)· παραστάδες ισοπαχείς 15/15 (T2A-02 βόρεια, T2A-03 0,40 νότια). Λεκάνη στον Τ7-02 ανατολικά (25, 7,90–8,15 × 5,15–6,25, άξονας y 5,55), νιπτήρας 0,50 × 0,35 στον νότιο τοίχο T2-04 (7,35–7,85 × 5,80–6,15, δίπλα στη λεκάνη, έξω από το τόξο της πόρτας). Δίπλα στον Τ7-02 η εσοχή 8,15–8,95 (0,80 – Γιάννης: «θέλω πιο πολύ χώρο στο ψυγείο») παίρνει το ΨΥΓΕΙΟ 0,80 × 0,70 κολλητά στον Τ7-02 και στη στήλη φούρνου – κανένα κενό. Όλοι οι τοίχοι του WC ανθυγρή γυψοσανίδα από μέσα.

• ΧΩΛ 2,70 × 0,90 (3,75–6,45 × 3,45–4,35, όπως R04 / αρχιτέκτονας): βόρεια πόρτες Υπν.1 (3,75–4,55) και λουτρού (4,80–5,50), ανατολικά πόρτα Υπν.2 (y 3,45–4,25), νότια εσοχή 0,70 (y 4,35–5,05): πλυντήριο 0,60 (3,75–4,35) + ντουλάπα 1,10 (4,35–5,45), T2N-04 επιστροφή 5,45–5,55, άνοιγμα προς καθιστικό 5,55–6,45 (0,90). Τοίχοι που βλέπουν σε ντουλάπα / πλυντήριο: 1 φύλλο (T2N-01…04).

• ΚΟΥΖΙΝΑ ΜΕ ΝΗΣΙΔΑ-ΤΡΑΠΕΖΑΡΙΑ (R06 – Γιάννης: «δούλεψε την κουζίνα με νησίδα-τραπεζαρία», «κενό νησίδα–κουζίνα τουλάχιστον 1,10, νησίδα 1,80 και κάτω»): ζώνη 6,45–9,55 × 5,15–9,125. Στη ΒΑ γωνία στήλη φούρνου 0,60 (8,95–9,55 × 5,15–5,75) και δίπλα της, στην εσοχή ανάμεσα στο WC και τον πάγκο, ψυγείο 0,80 × 0,70 (8,15–8,95) – κανένα κενό. Πάγκος 0,60 × 3,35 στον T6-01 (x 8,95–9,55, y 5,75–9,10): νεροχύτης 0,80 (6,30–7,10), πλυντήριο πιάτων 0,60 (7,10–7,70), πάγκος 0,50, εστίες 0,60 (8,20–8,80, απορροφητήρας στον T6-01), πάγκος 0,30 ως το N υποστύλωμα. ΝΗΣΙΔΑ-ΧΕΡΣΟΝΗΣΟΣ 0,90 × 1,80 (x 6,95–7,85, y 6,25–8,05) από τον νότιο τοίχο του WC προς τα νότια, παράλληλη στον πάγκο: διάδρομος εργασίας 1,10 (7,85–8,95), ανοιχτός προς νότο (1,075 ως τον τοίχο, μπροστά στο W0.03), 3 θέσεις δυτικά (βήμα 0,60, προεξοχή πάγκου 0,30–0,35 για τα γόνατα) = η νησίδα είναι και η τραπεζαρία. Ελεύθερη νησίδα (με διάδρομο και στις δύο άκρες) δεν χωράει μαζί με το WC στη ζώνη 3,10 × 3,975. Σαλόνι: καναπές 2,70 × 0,90 στον βόρειο τοίχο (1,80–4,50 × 5,25–6,15) απέναντι από την TV (έπιπλο TV του EPIPLA στον νότιο τοίχο), πολυθρόνα και τραπεζάκι του EPIPLA. Η τραπεζαρία + 6 καρέκλες του EPIPLA καταργείται· ύψος νησίδας / θέση νεροχύτη–εστιών τελικά από τον μελετητή κουζίνας. Πίσω από τον πάγκο χωρίς επένδυση (T6-01 γυψοσανίδα, N υποστύλωμα γυμνό)· η Τ3-10 μόνο στην παραστάδα του W0.03 (8,70–8,80).

• Τ6-01 ΣΤΟ 9,55–9,70 (R06 – Γιάννης: «δες καλύτερα τον τοίχο Τ6-01, τον έχεις βάλει σε λάθος θέση»): ο αρχιτέκτονας έχει τοίχο 30 στο 9,40–9,70· ο Τ6 15 cm (R01) είχε μπει στο 9,40–9,55 με σταθερή την παρειά του διαμερίσματος και άφηνε στο lobby δύο δόντια 0,15 (υποστύλωμα πυρήνα 9,70 στο 3,00–5,15, τοίχος 9,55, N υποστύλωμα 9,70 στο 9,10–9,45). Τώρα στο 9,55–9,70: η παρειά του lobby 9,70 είναι μία ευθεία από το φρεάτιο ως την είσοδο, και η παρειά του καθιστικού 9,55 είναι επίσης ευθεία (το υποστύλωμα πυρήνα τελειώνει στο 5,15 = γραμμή του βόρειου τοίχου, το N υποστύλωμα από 9,10 μέσα στον νότιο τοίχο). Το διαμέρισμα κερδίζει 0,15 (πάγκος κουζίνας 8,95–9,55).

• Υπν.1 (R06): κύριος χώρος 1,125–4,55 × 0,805–3,35 (3,425 × 2,545) + εσοχή 1,70–3,65 × 3,35–4,45 (≈ 10,9 m² καθαρά + ντουλάπες 3,1 m²). Ντουλάπες 0,60 χωνευτές, 5,1 m όπως R05: ΔΥΤΙΚΗ 1,05–1,70 × 3,35–4,85 (1,50, βάθος 0,65 από το γυμνό τούβλο ως την παρειά 1,70 του Δ υποστυλώματος – το μέτωπό της και η βόρεια παρειά του υποστυλώματος 4,85 είναι περασιά), ΝΟΤΙΑ 1,70–3,65 × 4,45–5,05 (1,95, ανάμεσα στο υποστύλωμα και τον T2-01), ΑΝΑΤΟΛΙΚΗ 3,95–4,55 × 0,805–2,45 (1,65 στον Τ7-01, 1 φύλλο πίσω της, τελειώνει 0,10 πριν το ανοιχτό φύλλο της πόρτας). Κρεβάτι 1,60 × 2,00 με κεφαλάρι στη δυτική επένδυση (στον βόρειο τοίχο είναι το W0.08 1,60 × 2,40), y 1,20–2,80, κομοδίνα 0,45 × 0,395 / 0,45 × 0,45, διάβαση προς την εσοχή 0,55. Πόρτα 0,80 στο 3,75–4,55, μεντεσές 4,55, διπλώνει στον Τ7-01. Η Τ3-06 ως 3,35 (πίσω από τη δυτική ντουλάπα γυμνό τούβλο).

• ΛΟΥΤΡΟ 1,65 × 2,55 (x 4,80–6,45 · y 0,80–3,35): Τ7-01 λεκάνης δυτικά (σταθερή η παρειά Υπν.1 4,55), T2A-01 ανατολικά 6,45–6,60 (A-10-GF), ντους 1,65×0,80 βόρεια (y 0,80–1,60) με γυάλινο διαχωριστικό 0,70 στο y 1,60 από τον Τ7-01, λεκάνη στον Τ7-01 (y 2,10), πάγκος 0,50 στον ανατολικό τοίχο (5,95–6,45 × 1,75–3,35), πόρτα 0,70 στο 4,80–5,50 (μεντεσές 5,50). W0.07 0,60×0,90 μέσα στο τοιχείο K2 (x 5,50–6,10): κενό στον ξυλότυπο από τώρα (ποδιά +1,50).

• Υπν.2 (6,60–9,375 × 0,805–4,45 ≈ 10,1 m²): ντουλάπα 6,60–9,40 × 4,45–5,05 (2,80), πόρτα 0,80 από το χωλ στο y 3,45–4,25 (T2A-01 / T2A-02, μεντεσές 4,25), W0.06 1,00×2,40 μπαλκονόπορτα προς τη ΒΑ βεράντα (9,80–11,45 × 0,45–2,70, +0,45). Τ9-02 στο υποστύλωμα πυρήνα 3,00–4,45 περασιά με την Τ3-05.


• ΚΑΘΙΣΤΙΚΟ: δυτικός τοίχος Τ1-07 1,40–1,65 + Τ3-07 ως 1,705 περασιά με το ΝΔ τοιχείο (1,40) και την ανατολική παρειά του Δ υποστυλώματος (1,70)· W0.01 3,50×2,40 στο 5,65–9,15· Τ9-03 στο ΝΔ τοιχείο (παρειά 9,125) περασιά με Τ3-08 / Τ3-09. Καναπές, πολυθρόνα (0,45 δυτικότερα), τραπεζάκι, έπιπλο TV από το EPIPLA.

• ΠΥΡΗΝΑΣ: Τ5-01 10 cm σε όλο το μήκος 9,70–13,35 (A-10-GF) με επιστροφή Τ5-02 στο φρεάτιο· shaft Η/Μ εκτός Σ.Δ. στο y 2,85–3,15 × 9,70–11,05 (βάθος 0,30 όπως B1 – ο αρχιτέκτονας δείχνει μέτωπο 25 στο 3,00–3,25). Μέτωπο ανελκυστήρα T10-01/T10-02 25 cm, πόρτα 0,90 στο y 3,60–4,50. Κύκλος περιστροφής ΑΜΕΑ R0,75 (1,50) στο 9,70–11,20. Σκάλα 16 ριχτιών όπως B1. ΕΙΣΟΔΟΣ ΚΤΙΡΙΟΥ (R06, A-50-02 06/11): ενιαίο κούφωμα αλουμινίου 2,45 στο 9,70–12,15 = πόρτα Θ0.04 1,20×2,40 (9,70–10,90, μεντεσές δυτικά, ανοίγει μέσα) + σταθερό W0.04 1,25×2,40 (10,90–12,15)· ο πεσσός τούβλου 0,10 του R01 καταργείται (παραστάδα = N υποστύλωμα 9,70). Καμία πόρτα διαμερίσματος προς το lobby.

• ΚΟΥΦΩΜΑΤΑ (A-50-02 06/11/2026 + A-10-GF R01): W0.08 1,60×2,40 (2,00–3,60) · W0.07 0,60×0,90 (ποδιά 1,50) · W0.06 1,00×2,40 (1,45–2,45) · W0.01 3,50×2,40 δίφυλλο επάλληλο (5,65–9,15) · W0.02 1,45 σταθερό (3,50–5,00 – ο πίνακας λέει 145, η κάτοψη 1,50) · Θ0.03 πόρτα ΙΣ1 1,10×2,40 (5,00–6,10 – ο πίνακας 110, η ετικέτα της κάτοψης R01 1,20: ΝΑ ΔΙΕΥΚΡΙΝΙΣΤΕΙ) · W0.03 2,40 = 1,50 σταθερό + 0,90 ανοιγοανακλινόμενο (6,30–8,70) · Θ0.04 1,20 + W0.04 1,25 · W0.05 0,70×1,35. Πεσσοί 0,10 (3,40–3,50), 0,20 (6,10–6,30), 0,30 (8,70–9,00) όπως ο αρχιτέκτονας – ΠΡΟΣ ΑΠΟΦΑΣΗ αν ο 0,10 ενσωματωθεί στο κούφωμα. Τ3 και στις δύο παραστάδες.

• ΘΕΡΜΟΠΡΟΣΟΨΗ: 10 cm στο διαμέρισμα, 5 cm στον πυρήνα / είσοδο κτιρίου (Τ5-01, φρεάτιο, Τ1-12, Τ1-11). ΥΨΟΣ ισογείου 3,00 (πλάκα οροφής +3,65 κατά Σ3) – επιφάνειες Τ-03 με Η = 3,00.

ΕΡΓΟ	ΘΕΜΑ ΣΧΕΔΙΟΥ	ΒΑΣΗ	ΑΡ. ΣΧΕΔΙΟΥ
ΠΕΝΤΑΟΡΟΦΟ ΚΤΗΡΙΟ ΚΑΤΟΙΚΙΩΝ – ΑΡΓΥΡΟΥΠΟΛΗ Κωνσταντινουπόλεως 12 & Αγ. Βαρβάρας · Ο.Τ. 103-15 Εργοδότης: INTERKAT Α.Ε. · Κατασκευή: ARKAD Ι.Κ.Ε.	**ΠΡΟΜΕΤΡΗΣΗ ΤΟΙΧΟΠΟΙΙΩΝ – ΙΣΟΓΕΙΟΥ** Τετραγωνικά ανά τυπολογία τοίχου · θερμοπρόσοψη 10 / 5 cm ΙΣΟΓΕΙΟ – ΙΣ1	Βάση: κάτοψη τοιχοποιιών Τ-01 · είδη Τ-02	**Τ-03** — · **A3** 06/11/2026 · R06

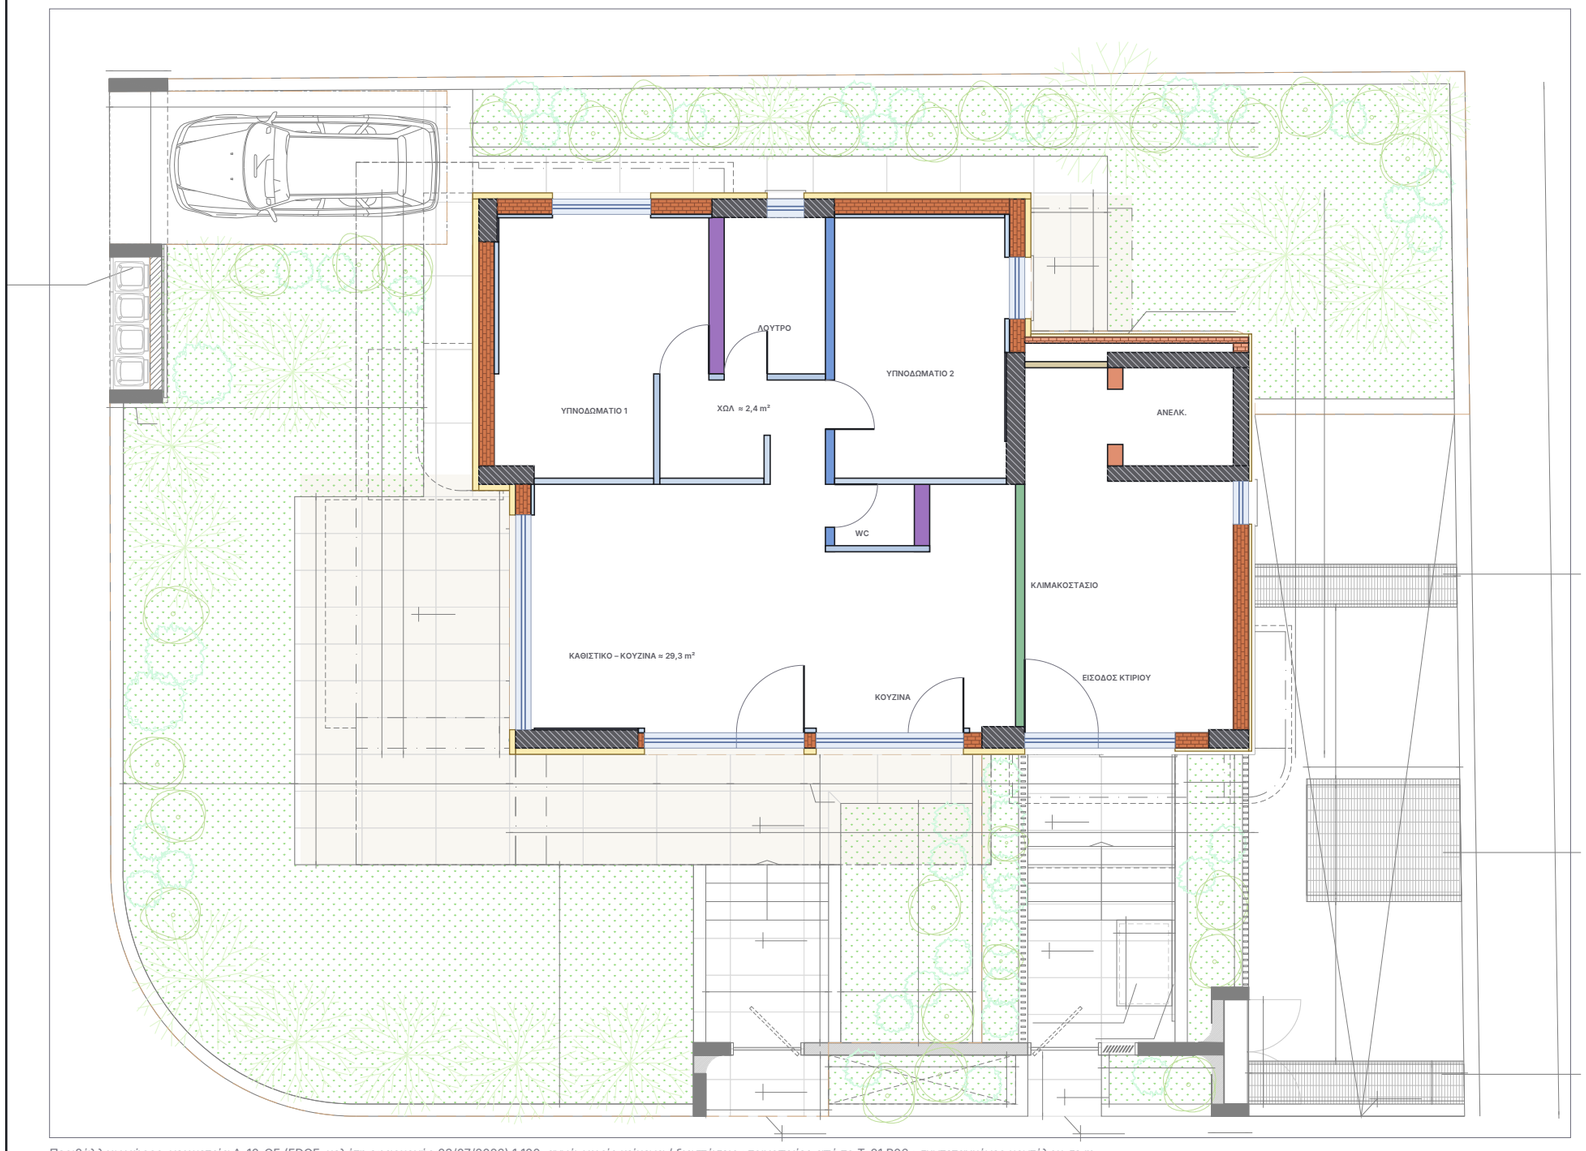

Περιβάλλων χώρος: γεωμετρία A-10-GF (EDGE, μελέτη εφαρμογής 23/07/2026) 1:100, αχνά, χωρίς κείμενα / διαστάσεις · τοιχοποιίες από το T-01 R06 · συντεταγμένες μοντέλου σε m

B

ΠΕΡΙΒΑΛΛΩΝ ΧΩΡΟΣ ΙΣΟΓΕΙΟΥ – όπως τον έχει ο αρχιτέκτονας (A-10-GF)

Το φύλλο δείχνει το οικόπεδο ολόκληρο με τον κήπο, τις βεράντες, τις εισόδους και τη ράμπα όπως τα έχει ο αρχιτέκτονας στο A-10-GF (μόνο η γεωμετρία, χωρίς τα κείμενά του), για να φαίνεται πώς δένουν οι τοιχοποιίες του ισογείου με τον περιβάλλοντα χώρο. Δεν είναι σχέδιο κατασκευής κήπου: για διαστάσεις, στάθμες και φυτεύσεις ισχύουν τα A-10-GF / A-14-GF και η μελέτη περιβάλλοντος χώρου.

ΚΗΠΟΣ ΙΣ1
Χώρος αποκλειστικής χρήσης ΙΣ1 κατοικίας 182,08 m² (σημεία 1…23 του A-10-GF): δυτικά και νότια του κτιρίου, βεράντα ισογείου δυτικά +0,40 (κλίση 1 %) και νότια +0,45 με σκαλιά 1–4 προς −0,30 · προβολές εξώστη / έρκερ με διακεκομμένη.

ΕΙΣΟΔΟΣ ΙΣ1
Από τη νότια περίφραξη: πύλη Θ 1,00/2,20 (x ≈ 5,2–6,2), σκαλιά −0,30 → +0,45, βεράντα, πόρτα Θ0.03 1,10×2,40 (5,00–6,10).

ΣΤΑΘΜΕΥΣΗ
Θ.Σ.Ι.1 13,75 m² στη ΒΔ γωνία του οικοπέδου (θέση στάθμευσης ισογείου), πλάτος 2,50 · μήκος 5,50.

ΦΥΤΕΜΕΝΟΙ ΧΩΡΟΙ
Φ.Χ.1 37,69 m² (βόρεια) · Φ.Χ.2 68,46 (νοτιοδυτικά) · Φ.Χ.3 8,39 · Φ.Χ.4 2,82 · Φ.Χ.5 3,76 · Φ.Χ.6 1,42 · Φ.Χ.7 2,44 m².

ΕΙΣΟΔΟΣ ΚΤΙΡΙΟΥ
Νότια: πύλη πεζών Θ 1,00/2,20 (x ≈ 9,85–10,85) στο −0,45, σκάλα 5 ριχτιών 2,40 (x 9,75–12,15) ως το πλατύσκαλο +0,45 (9,50–12,95 × 9,45–10,25), αναδιπλούμενη πλατφόρμα αναβατορίου ΑΜΕΑ 0,90×1,40 με οδηγό x 8,85–9,75, πόρτα αλουμινίου 1,00×2,40 + σταθερό W0.04 1,20 στο lobby (24,55 m²).

ΒΑ ΒΕΡΑΝΤΑ
Βεράντα ισογείου +0,45, 9,80–11,45 × 0,45–2,70, από την μπαλκονόπορτα W0.06 του Υπν.2 · ανατολικά της φυτεμένος χώρος.

ΟΧΗΜΑΤΑ / ΥΠΟΣΤΑΘΜΟΣ
Ράμπα Ι.Χ. κλίσης 16,12 % στη ΝΑ γωνία (είσοδος – έξοδος οχημάτων, −0,55), μετρητές ΔΕΔΔΗΕ, εσχάρες υποσταθμού: εξαερισμού Ι-Κ-Λ-Μ 3,40×0,60 = 2,04 m² (ανατολικά του lobby) και Ρ-Σ-Τ-Υ 3,52×0,60 = 2,11 m², καταπακτής Ν-Ξ-Ο-Π 2,80×1,80 = 5,02 m² (βλ. A-30-01).

ΕΡΓΟ	ΘΕΜΑ ΣΧΕΔΙΟΥ	ΒΑΣΗ	ΑΡ. ΣΧΕΔΙΟΥ
ΠΕΝΤΑΟΡΟΦΟ ΚΤΗΡΙΟ ΚΑΤΟΙΚΙΩΝ – ΑΡΓΥΡΟΥΠΟΛΗ Κωνσταντινουπόλεως 12 & Αγ. Βαρβάρας · Ο.Τ. 103-15 Εργοδότης: INTERKAT Α.Ε. · Κατασκευή: ARKAD Ι.Κ.Ε.	**ΠΕΡΙΒΑΛΛΩΝ ΧΩΡΟΣ – ΙΣΟΓΕΙΟ** Κήπος ΙΣ1 · βεράντες · είσοδοι · ράμπα κατά A-10-GF ΙΣΟΓΕΙΟ – ΙΣ1	Βάση: γεωμετρία περιβάλλοντος χώρου A-10-GF · τοιχοποιίες T-01	**T-04** **Κλίμακα 1:100 · A3** 06/11/2026 · R06