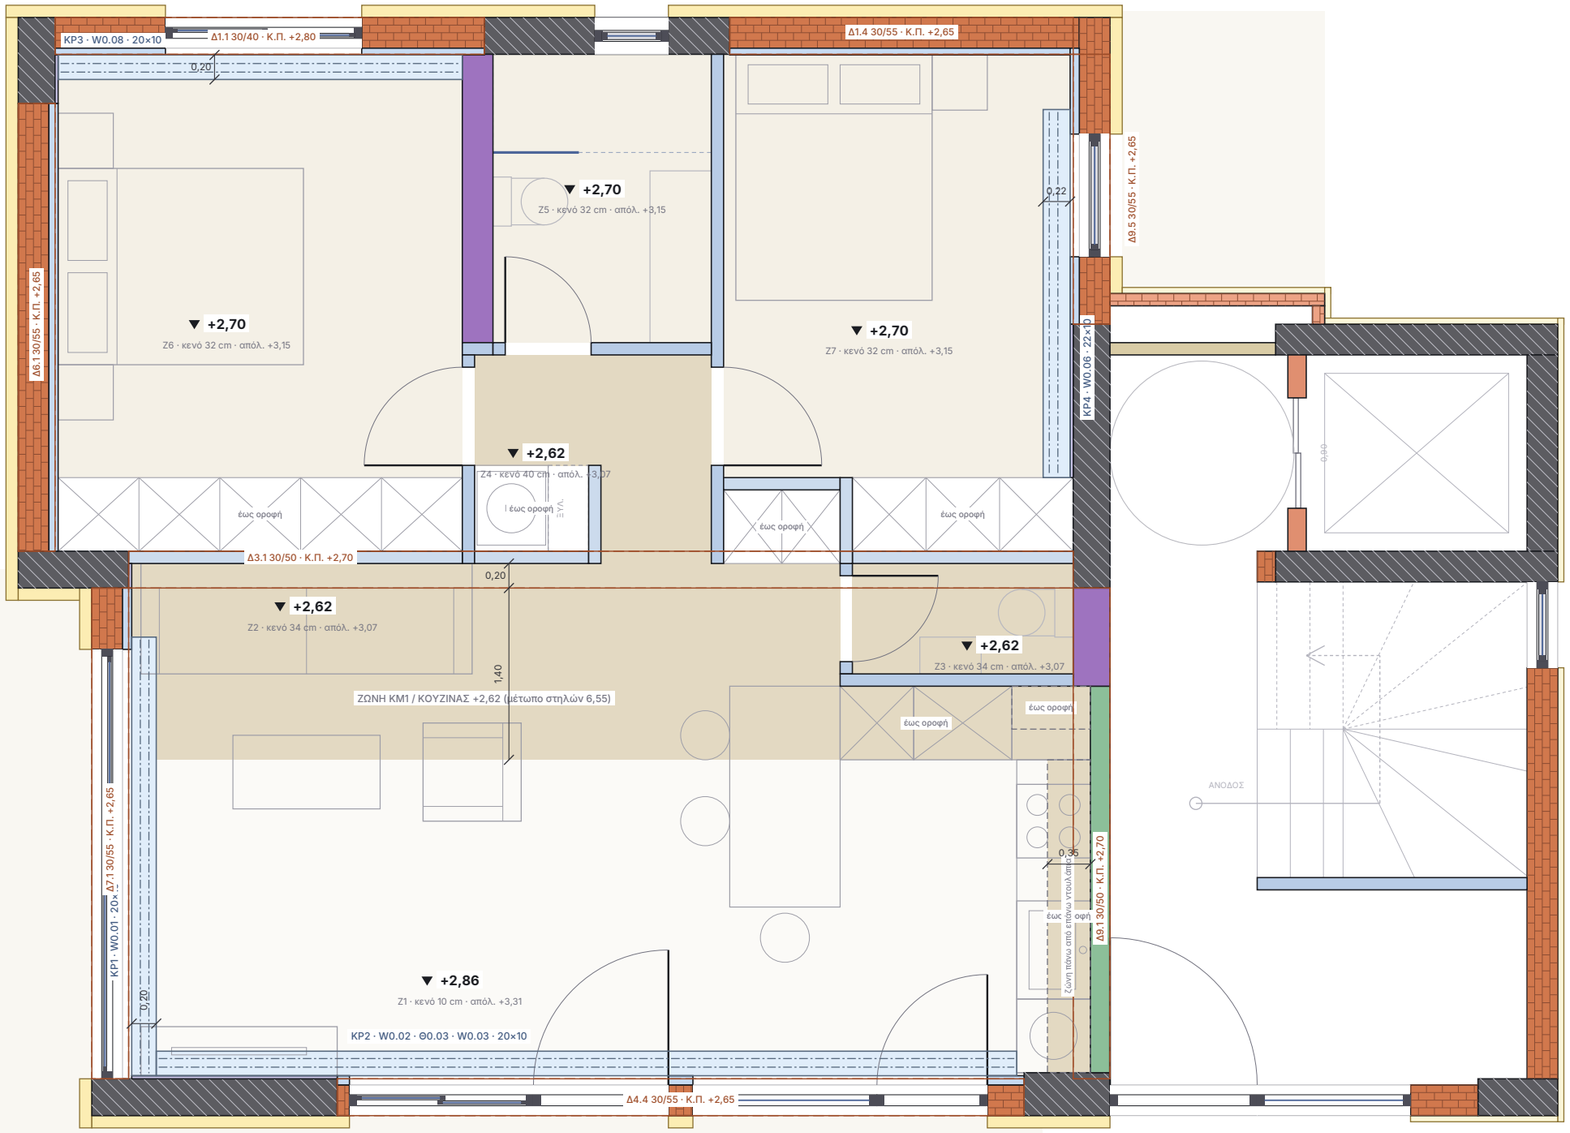


ΣΗΜΕΙΩΣΕΙΣ

Στάθμες από το τελικό δάπεδο του ισογείου – Τ.Δ. θεωρήθηκε +0,45 στο σύστημα του Σ3 (Α1): πάνω παρειά πλάκας +3,20 · κάτω παρειά Π3 h18 +3,02 · Π8 h24 +2,96 · δοκοί 50 +2,70 · 55 +2,65 · 40 +2,80. Σε κάθε στάθμη και η απόλυτη (Σ3).

Καθιστικό +2,86 (10 cm κάτω από την Π8) · ζώνη ΚΜ1 / κουζίνας +2,62 σε Γ (κρύβει Δ3.1 – που προεξέχει 0,20 στο καθιστικό – και Δ9.1) · χωλ / WC +2,62 · λουτρό / υπνοδωμάτια +2,70 περασιά με τη Δ3.1.

Αλλαγές στάθμης ΜΟΝΟ: γραμμή 6,55 (μέτωπο στηλών κουζίνας, ως τον Δ τοίχο) · γραμμή 9,19 (μέτωπο επάνω ντουλαπιών) · πόρτες.

Κουρτινόθηκες ΚΡ1–ΚΡ4: 20 × 10 cm (ΚΡ4 22 cm για τη μπαλκονόπορτα W0.06), δίπλα στις δοκούς όψης· η ΚΡ2 συνεχής σε όλο τον νότιο τοίχο (W0.02 · Θ0.03 · W0.03).


Πάνω από το Υπν.1: λουτρό γονέων Α΄ (Α2).

ΥΠΟΜΝΗΜΑ

- +2,86 καθιστικό = 10 cm κάτω από την Π8 h24 (spot σώμα ≤ 75 mm)
- +2,70 περασιά με δοκό 50: υπνοδωμάτια · λουτρό (κενό 32 cm)
- +2,62 ζώνη ΚΜ1 / κουζίνας · χωλ · WC (8 cm κάτω από τις δοκούς 50 – ψυκτικά)
- ΚΡ εσοχή κουρτίνας ανοιχτή ως την πλάκα · 2 οδηγοί
- δοκός (Σ3) · Κ.Π. = κάτω παρειά από Τ.Δ.

ΕΡΓΟ	ΘΕΜΑ ΣΧΕΔΙΟΥ	ΒΑΣΗ	ΑΡ. ΣΧΕΔΙΟΥ
ΠΕΝΤΑΟΡΟΦΟ ΚΤΗΡΙΟ ΚΑΤΟΙΚΙΩΝ – ΑΡΓΥΡΟΥΠΟΛΗ Κωνσταντινουπόλεως 12 & Αγ. Βαρβάρας · Ο.Τ. 103-15 Εργοδότης: INTERKAT Α.Ε. · Κατασκευή: ARKAD Ι.Κ.Ε.	**ΑΝΟΨΗ – ΣΤΑΘΜΕΣ · ΔΟΚΟΙ · ΚΟΥΡΤΙΝΕΣ** Στάθμες ψευδοροφής · δοκοί Σ3 · εσοχές κουρτινών ΙΣΟΓΕΙΟ – ΙΣ1 (Τ.Δ. θεωρήθηκε +0,45 στο σύστημα του Σ3)	Βάση: τοιχοποιίες ισογείου R13 · ξυλότυπος Σ3 (+3,65) · ανόψη Β1 R12	**ΑΝ-01** **Κλίμακα 1:50 · Α3** 07/11/2026 · R01

B

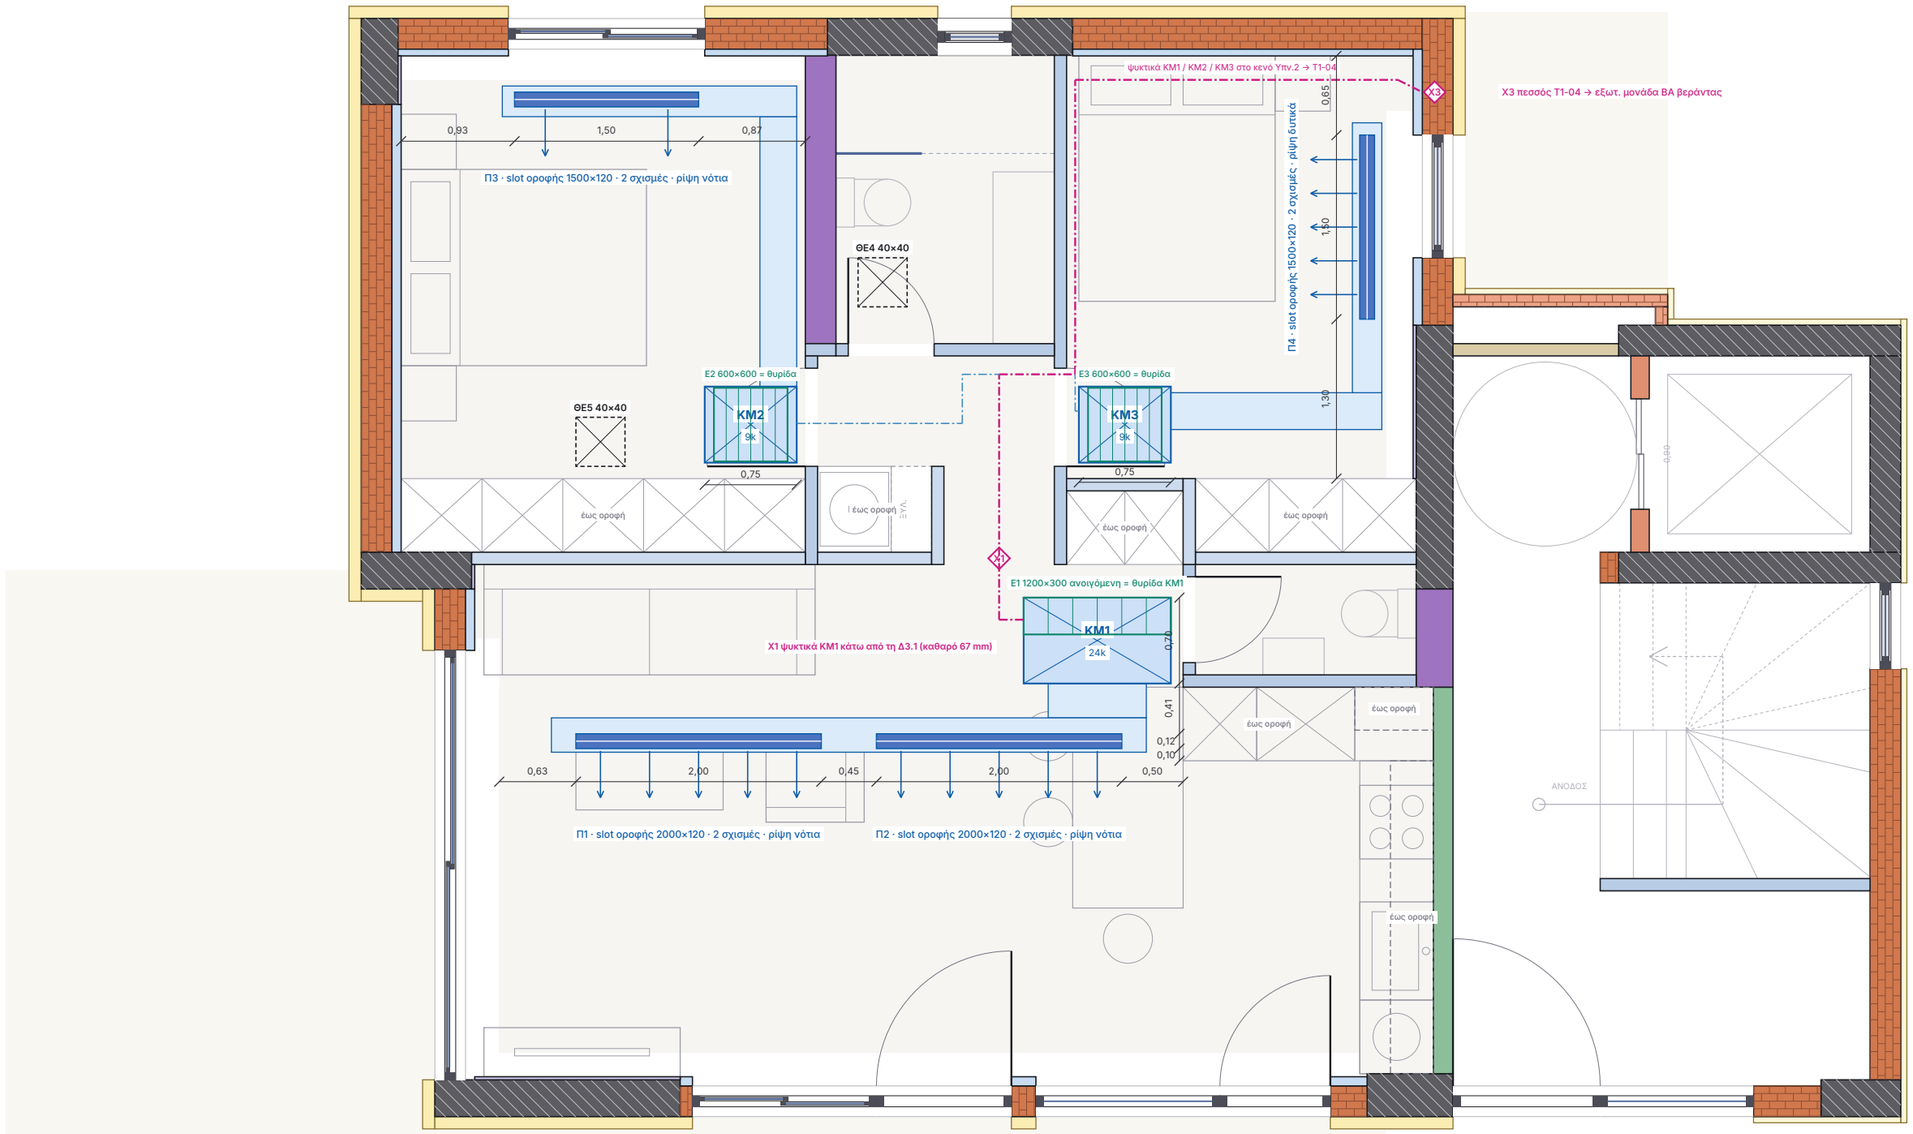

ΣΗΜΕΙΩΣΕΙΣ

Χώρος μονάδων (προδ. 1): ζώνη +2,62 κάτω από την Π18 +2,96 = 34 cm → ΚΜ1 245 + 10 + 40 = 295 → περιθώριο 45 mm · υπνοδωμάτια +2,70 κάτω από την Π3 +3,02 = 32 cm → ΚΜ2 / ΚΜ3 200 + 10 + 40 = 250 → περιθώριο 70 mm.

Προσαγωγή μόνο από γραμμικά slot οροφής: Π1 / Π2 στην ακμή της ζώνης (ρίψη νότια) · Π3 στο Υπν.1 πίσω από την ΚΡ3 (ρίψη νότια) · Π4 στο Υπν.2 δίπλα στην ΚΡ4 (ρίψη δυτικά).

Πρόσβαση: ανοιγόμενες επιστροφές με φίλτρο ακριβώς κάτω από τις μονάδες (Ε1 / Ε2 / Ε3)· οι ΚΜ2 / ΚΜ3 είναι στα υπνοδωμάτια γιατί το χωλ 0,90 δεν χωράει μονάδες + θυρίδες + ανιχνευτή.

Ψυκτικά ΚΜ1: από την ενιαία οροφή +2,62 του περάσματος χωλ – καθιστικού περνούν κάτω από τη Δ3.1 (καθαρό 2,70 – 2,62 – 12,5 = 67 mm → χωράει και μόνωση 13 mm) → κενό χωλ → μαζί με ΚΜ2 → Υπν.2 (κατά μήκος του Τ2-07 και του βόρειου τοίχου, πάνω από την ΚΜ3) → αυλάκι στον πεσσό Τ1-04 → εξωτερική μονάδα στη ΒΑ βεράντα. Καμία οπή σε δοκό.

Συμπυκνώματα με αντλία μαζί με τα ψυκτικά → σιφώνι βεράντας (επιβεβαίωση υδραυλικού).

ΥΠΟΜΝΗΜΑ

- ΚΜ καναλάτη μονάδα (slim: ΚΜ1 ≤ 245 mm · ΚΜ2/ΚΜ3 ≤ 200 mm)
- αεραγωγός / plenum προσαγωγής (μονωμένος, στο κενό)
- Π γραμμικό slot οροφής 2 σχισμών, ρυθμιζόμενη ρίψη
- στόμιο τοίχου (δεν υπάρχει στο ισόγειο)
- Ε στόμιο / κιβώτιο επιστροφής με φίλτρο
- ΘΕ θυρίδα επίσκεψης (αφανής, βαφόμενη)
- Χ κατέβασμα / έξοδος σωληνώσεων – καμία οπή σε σκυρόδεμα

ΕΡΓΟ	ΘΕΜΑ ΣΧΕΔΙΟΥ	ΒΑΣΗ	ΑΡ. ΣΧΕΔΙΟΥ
ΠΕΝΤΑΟΡΟΦΟ ΚΤΗΡΙΟ ΚΑΤΟΙΚΙΩΝ – ΑΡΓΥΡΟΥΠΟΛΗ Κωνσταντινουπόλεως 12 & Αγ. Βαρβάρας · Ο.Τ. 103-15 Εργοδότης: INTERKAT Α.Ε. · Κατασκευή: ARKAD Ι.Κ.Ε.	**ΑΝΟΨΗ – ΚΛΙΜΑΤΙΣΜΟΣ · ΘΥΡΙΔΕΣ** Καναλάτες μονάδες · slot · θυρίδες / επιστροφές · ψυκτικά ΙΣΟΓΕΙΟ – ΙΣ1 (Τ.Δ. θεωρήθηκε +0,45 στο σύστημα του Σ3)	Βάση: τοιχοποιίες ισογείου R13 · ξυλότυπος Σ3 (+3,65) · ανόψη Β1 R12	**ΑΝ-02** **Κλίμακα 1:50 · Α3** 07/11/2026 · R01



ΣΗΜΕΙΩΣΕΙΣ

Κατανομή: Υπν. 2 × 2 spots · λουτρό 3 (IP65 στο ντους) · WC 1 · χωλ 2 · είσοδος 1 · κουζίνα 2 στον άξονα του διαδρόμου νησίδα – πάγκος + LED4 κάτω από τα επάνω ντουλάπια. Σύνολο 17 spots + 2 παροχές + LED4.

Πυρανίχνευση (προδ. 4): καθιστικό, Υπν.1, Υπν.2, χωλ (άξονας 0,90 – στενός διάδρομος), κουζίνα θερμοδιαφορικός· ≥ 0,50 από τοίχους / φωτιστικά, ≥ 1,00 από slot προσαγωγής· λουτρό / WC χωρίς ανιχνευτή καπνού.

ΚΡΕΜ0 στο κέντρο του καθιστικού (ανάμεσα σε καναπέ και TV) · ΚΡΕΜ1 πάνω από τη νησίδα.

Οπή spot Ø 75–80 ανάμεσα στα προφίλ CD (όχι πάνω τους)· όπου πέφτει σε προφίλ, μετατόπιση του προφίλ – όχι του spot.

ΥΠΟΜΝΗΜΑ

- χωνευτό spot LED 7–9 W, 2700 K, CRI ≥ 90, UGR < 19, σώμα ≤ 75 mm
- χωνευτό spot IP44 (λουτρά)
- χωνευτό spot IP65 (πάνω από ντους)
- ΚΡΕΜ παροχή οροφής (κουτί + ενίσχυση ανάρτησης)
- ΑΚ ανιχνευτής καπνού (ΕΠ104 · EN 54-7)
- ΑΘ θερμοδιαφορικός ανιχνευτής (κουζίνα · EN 54-5)
- ακτίνα 0,50 m γύρω από ανιχνευτή – κανένας τοίχος / φωτιστικό μέσα
- LED4 κρυφό γραμμικό 3000 K κάτω από τα επάνω ντουλάπια κουζίνας

ΕΡΓΟ	ΘΕΜΑ ΣΧΕΔΙΟΥ	ΒΑΣΗ	ΑΡ. ΣΧΕΔΙΟΥ
ΠΕΝΤΑΟΡΟΦΟ ΚΤΗΡΙΟ ΚΑΤΟΙΚΙΩΝ – ΑΡΓΥΡΟΥΠΟΛΗ Κωνσταντινουπόλεως 12 & Αγ. Βαρβάρας · Ο.Τ. 103-15 Εργοδότης: INTERKAT Α.Ε. · Κατασκευή: ARKAD Ι.Κ.Ε.	**ΑΝΟΨΗ – ΦΩΤΙΣΜΟΣ · ΠΥΡΑΝΙΧΝΕΥΣΗ** Χωνευτά spots · παροχές · LED κουζίνας · ανιχνευτές ΙΣΟΓΕΙΟ – ΙΣ1 (Τ.Δ. θεωρήθηκε +0,45 στο σύστημα του Σ3)	Βάση: τοιχοποιίες ισογείου R13 · ξυλότυπος Σ3 (+3,65) · ανόψη Β1 R12	**ΑΝ-03** **Κλίμακα 1:50 · Α3** 07/11/2026 · R01

ΣΥΜΜΟΡΦΩΣΗ ΜΕ ΤΙΣ ΠΡΟΔΙΑΓΡΑΦΕΣ (ιδιοκτήτης 07/11/2026)

1 Κλιματισμός	Καναλάτη σε καθιστικό – κουζίνα (ΚΜ1 24k), Υπν.1 (ΚΜ2), Υπν.2 (ΚΜ3) · προσαγωγή ΜΟΝΟ από slot οροφής (Π1–Π4) · χώρος 34 / 32 cm (περιθώριο 45 / 70 mm) · θυρίδες = ανοιγόμενες επιστροφές Ε1 / Ε2 / Ε3 · ψυκτικά ΚΜ1 κάτω από τη Δ3.1 με 67 mm.
2 Κουρτίνες	ΚΡ1–ΚΡ4 σε όλα τα ανοίγματα καθιστικού / υπνοδωματίων, 20 (22) × 10 cm, ανοιχτές ως την πλάκα, δίπλα στις δοκούς όψης.
3 Φωτισμός	17 χωνευτά spots (υπνοδωμάτια, λουτρό, WC, χωλ, είσοδος, κουζίνα) + LED4 · καθιστικό με ΚΡΕΜ0 / ΚΡΕΜ1 (όπως Β1) · κανένα spot κάτω από μονάδα / αεραγωγό / σε θυρίδα / πάνω από ντουλάπι.
4 Πυρανίχνευση	ΑΚ1–ΑΚ4 καπνού + ΑΘ5 θερμοδιαφορικός κουζίνας · ≥ 0,50 / 0,50 / 1,00 (χωλ 0,90: στον άξονα).
5 Κατασκευή	Βασική 10 cm κάτω από την πλάκα στο καθιστικό · καταβίβαση για τις καναλάτες (ζώνη +2,62 / υπνοδωμάτια +2,70) · όλες οι δοκοί κρυμμένες ή περασιά · κανένα δόντι.
6 Γενική αρχή	3 στάθμες· η μόνη αλλαγή στον ενιαίο χώρο καθιστικού – κουζίνας είναι πάνω στα μέτωπα των στηλών / ντουλαπιών.

ΕΓΚΕΚΡΙΜΕΝΕΣ ΑΠΟΚΛΙΣΕΙΣ (ιδιοκτήτης 07/11/2026)

· Καθιστικό χωρίς spots – παροχές ΚΡΕΜ0 / ΚΡΕΜ1 (απόφαση R02 του Β1 – επιβεβαίωση για το ισόγειο, Α3).
· Μονάδες slim ≤ 245 mm (ΚΜ1) / ≤ 200 mm (ΚΜ2, ΚΜ3) ως παραδοχή μέχρι την επιλογή μοντέλου (όπως Β1).

ΙΣΟΓΕΙΟ R01 (07/11/2026)

· Πρώτη έκδοση ανόψης ισογείου πάνω στις τοιχοποιίες R13 (νησίδα) και τον Σ3 – με τη λογική του Β1 R12.
· Καθιστικό +2,86 (10 cm κάτω από την Π8 h24) με ζώνη +2,62 σε Γ: βόρεια 4,95–6,55 (κρύβει τη Δ3.1 που προεξέχει 0,20, ΚΜ1, slot Π1/Π2, στήλες κουζίνας – η γραμμή 6,55 είναι το μέτωπο των στηλών) και ανατολικά πάνω από τα επάνω ντουλάπια (κρύβει τη Δ9.1).
· Χωλ / WC +2,62 ενιαία με τη ζώνη (χωρίς σκαλοπάτι στο πέρασμα) · λουτρό / υπνοδωμάτια +2,70 περασιά με τη Δ3.1 (κενό 32 cm).
· ΚΜ2 / ΚΜ3 μέσα στα υπνοδωμάτια με slot οροφής (χωλ 0,90) · ψυκτικά ΚΜ1 κάτω από τη Δ3.1 με καθαρό 67 mm (χωράει μόνωση 13 mm) · έξοδος από τον πεσσό Τ1-04 στη ΒΑ βεράντα.

ΑΝΟΙΚΤΑ ΣΗΜΕΙΑ

· Α1 [ΑΠΟΦΑΣΗ] Τ.Δ. ισογείου στο σύστημα του Σ3: θεωρήθηκε +0,45 (Α-10-GF «ΙΣ1 +0,45») → πλάκα +3,20 από Τ.Δ., καθαρό ύψος καθιστικού 2,86 / υπνοδωματίων 2,70. Αν διαφέρει, αλλάζουν μόνο οι αριθμοί (οι αποστάσεις από την πλάκα μένουν) – επιβεβαίωση (τομή Α-30 ή στατικός).
· Α2 [ΣΥΝΤΟΝΙΣΜΟΣ] Το λουτρό γονέων του Α΄ είναι πάνω από το Υπν.1: η στήλη λεκάνης (x ≈ 2,75 · y ≈ 3,37) πέφτει μέσα στο δωμάτιο → εκτροπή στο κενό 32 cm ως τη ντουλάπα (y 4,25–4,85) και κατέβασμα μέσα σε αυτή· ΘΕ5 για καθαρισμό – οριστικά στις αποχετεύσεις.
· Α3 [ΑΠΟΦΑΣΗ] Καθιστικό χωρίς spots με παροχές ΚΡΕΜ0 / ΚΡΕΜ1 – όπως Β1 (R02): επιβεβαίωση ότι ισχύει και στο ισόγειο.
· Α4 [ΑΠΟΦΑΣΗ] Επάνω ντουλάπια κουζίνας στον Τ6-01 και στη γωνία ως τη ζώνη +2,62, με LED4 από κάτω – όπως Β1 («παντού ψηλά ντουλάπια»).
· Α5 [ΜΟΝΤΕΛΟ] ΚΜ1 24k / ΚΜ2 9k / ΚΜ3 9k ενδεικτικά (μελέτη ψύξης ισογείου) · slim ≤ 245 / ≤ 200 mm · ΚΜ2 / ΚΜ3 μέσα στα υπνοδωμάτια (το χωλ 0,90 δεν χωράει μονάδες + θυρίδες + ανιχνευτή) → αθόρυβες μονάδες.
· Α6 [ΣΤΑΤΙΚΟΣ] Δοκοί / πλάκες από το παράγωγο σχέδιο γεωμετρίας του Σ3 (εγκεκριμένο 02/2024)· το Σ3_ΕΦ (Κόγιας) να ελεγχθεί πριν τη σκυροδέτηση – κρίσιμα: Π8 h24, Δ3.1 30/50 στο 4,85–5,15, Δ9.1 30/50.

ΕΛΕΓΧΟΣ ΣΥΓΚΡΟΥΣΕΩΝ & ΣΤΑΘΜΩΝ – 56 έλεγχοι · ΟΚ 55 · ΟΡΙΑΚΟ 0 · ΕΓΚΕΚΡ. 1 · ΑΠΟΚΛΙΣΗ 0

Αυτόματος έλεγχος από το μοντέλο (code/anopseis/checks.py): στάθμες ↔ δοκοί · κενό μονάδων · θυρίδες · spots ↔ ζώνες / θυρίδες / μονάδες / αεραγωγοί / κουρτινόθηκες · ανιχνευτές ↔ τοίχοι / φωτιστικά / στόμια · κουρτινόθηκες ↔ κουφώματα / δοκοί.


ΚΩΔ.	ΚΑΤΑΣΤ.	ΣΤΟΙΧΕΙΟ	ΜΕΤΡΗΣΗ
ΣΤ01	ΟΚ	Z2 ΖΩΝΗ ΚΜ1 – ΚΟΥΖΙΝΑ ↔ Δ3.1 30/50 (Κ.Π. +2.70)	οροφή +2.62 · κρυμμένη 8 cm
ΣΤ02	ΟΚ	Z2 ΖΩΝΗ ΚΜ1 – ΚΟΥΖΙΝΑ ↔ Δ9.1 30/50 (Κ.Π. +2.70)	οροφή +2.62 · κρυμμένη 8 cm
ΣΤ03	ΟΚ	Z3 WC ↔ Δ3.1 30/50 (Κ.Π. +2.70)	οροφή +2.62 · κρυμμένη 8 cm
ΣΤ04	ΟΚ	Z4 ΧΩΛ ↔ Δ3.1 30/50 (Κ.Π. +2.70)	οροφή +2.62 · κρυμμένη 8 cm
ΚΛ-ΚΜ1	ΟΚ	ΚΜ1 24.000 Btu/h – καθιστικό – κουζίνα	κενό 340 mm · περιθώριο +45 mm
ΘΕ-ΚΜ1	ΟΚ	ΚΜ1 – πρόσβαση συντήρησης	Ε1
ΚΛ-ΚΜ2	ΟΚ	ΚΜ2 9.000 Btu/h – Υπνοδωμάτιο 1	κενό 320 mm · περιθώριο +70 mm
ΘΕ-ΚΜ2	ΟΚ	ΚΜ2 – πρόσβαση συντήρησης	Ε2
ΚΛ-ΚΜ3	ΟΚ	ΚΜ3 9.000 Btu/h – Υπνοδωμάτιο 2	κενό 320 mm · περιθώριο +70 mm
ΘΕ-ΚΜ3	ΟΚ	ΚΜ3 – πρόσβαση συντήρησης	Ε3
ΨΥ-ΚΜ1	ΟΚ	Όδευση ψυκτικών ΚΜ1 ζώνη → πέρασμα → χωλ → Υπν.2 → Τ1-04	ελάχιστο 280 mm
ΨΥ-ΚΜ2	ΟΚ	Όδευση ψυκτικών ΚΜ2 Υπν.1 → χωλ	ελάχιστο 280 mm
ΨΥ-ΔΟΚ	ΟΚ	Διέλευση ψυκτικών ΚΜ1 κάτω από τη Δ3.1 (x ≈ 6.00, πέρασμα χ…	καθαρό 67.5 mm · περιθώριο +25.6 mm
ΚΔ-ΚΜ1	ΟΚ	Καθιστικό – κουζίνα (ενιαίος χώρος)	ΚΜ1
ΚΔ-ΚΜ2	ΟΚ	Υπνοδωμάτιο 1	ΚΜ2
ΚΔ-ΚΜ3	ΟΚ	Υπνοδωμάτιο 2	ΚΜ3
ΣΤ-Π1	ΟΚ	Π1 slot οροφής 2000×120 · 2 σχισμές	μέσα
ΣΤ-Π2	ΟΚ	Π2 slot οροφής 2000×120 · 2 σχισμές	μέσα
ΣΤ-Π3	ΟΚ	Π3 slot οροφής 1500×120 · 2 σχισμές	μέσα
ΣΤ-Π4	ΟΚ	Π4 slot οροφής 1500×120 · 2 σχισμές	μέσα
SP-Υ1	ΟΚ	Υ1 spot (1.800 · 1.750) – ΥΠΝΟΔΩΜΑΤΙΟ 1	κενό 307 mm · άκρη 0.67
SP-Υ2	ΟΚ	Υ2 spot (3.200 · 1.750) – ΥΠΝΟΔΩΜΑΤΙΟ 1	κενό 307 mm · άκρη 0.74
SP-Υ3	ΟΚ	Υ3 spot (1.800 · 3.300) – ΥΠΝΟΔΩΜΑΤΙΟ 1	κενό 307 mm · άκρη 0.67
SP-Υ4	ΟΚ	Υ4 spot (3.200 · 3.300) – ΥΠΝΟΔΩΜΑΤΙΟ 1	κενό 307 mm · άκρη 0.95
SP-Υ5	ΟΚ	Υ5 spot (7.200 · 1.750) – ΥΠΝΟΔΩΜΑΤΙΟ 2	κενό 307 mm · άκρη 0.65
SP-Υ6	ΟΚ	Υ6 spot (8.600 · 1.750) – ΥΠΝΟΔΩΜΑΤΙΟ 2	κενό 307 mm · άκρη 0.55
SP-Υ7	ΟΚ	Υ7 spot (7.200 · 3.300) – ΥΠΝΟΔΩΜΑΤΙΟ 2	κενό 307 mm · άκρη 0.65
SP-Υ8	ΟΚ	Υ8 spot (8.600 · 3.300) – ΥΠΝΟΔΩΜΑΤΙΟ 2	κενό 307 mm · άκρη 0.55

ΚΩΔ.	ΚΑΤΑΣΤ.	ΣΤΟΙΧΕΙΟ	ΜΕΤΡΗΣΗ
SP-Λ1	ΟΚ	Λ1 spot IP65 (5.560 · 1.200) – ΛΟΥΤΡΟ	κενό 307 mm · άκρη 0.40
SP-Λ2	ΟΚ	Λ2 spot IP44 (5.450 · 2.150) – ΛΟΥΤΡΟ	κενό 307 mm · άκρη 0.78
SP-Λ3	ΟΚ	Λ3 spot IP44 (5.450 · 2.850) – ΛΟΥΤΡΟ	κενό 307 mm · άκρη 0.30
SP-Λ4	ΟΚ	Λ4 spot IP44 (8.400 · 5.300) – WC	κενό 327 mm · άκρη 0.35
SP-Χ1	ΟΚ	Χ1 spot (5.650 · 3.700) – ΧΩΛ	κενό 387 mm · άκρη 0.45
SP-Χ2	ΟΚ	Χ2 spot (6.000 · 4.600) – ΧΩΛ	κενό 387 mm · άκρη 0.35
SP-Ε1	ΟΚ	Ε1 spot (5.550 · 8.550) – ΚΑΘΙΣΤΙΚΟ – ΚΟΥΖΙΝΑ	κενό 88 mm · άκρη 0.38
SP-Μ1	ΟΚ	Μ1 spot (8.220 · 7.000) – ΚΑΘΙΣΤΙΚΟ – ΚΟΥΖΙΝΑ	κενό 88 mm · άκρη 0.45
SP-Μ2	ΟΚ	Μ2 spot (8.220 · 8.400) – ΚΑΘΙΣΤΙΚΟ – ΚΟΥΖΙΝΑ	κενό 88 mm · άκρη 0.53
SP-ΚΑΘ	ΕΓΚΕΚΡ.	Καθιστικό	παροχές ΚΡΕΜ0 / ΚΡΕΜ1 – όπως Β1 (απόφα…
ΠΥ-ΑΚ1	ΟΚ	ΑΚ1 καπνού (5.30 · 7.70) – καθιστικό – κουζίνα	τοίχος 1.15 · Ε1 0.89 · Π2 1.25
ΠΥ-ΑΚ2	ΟΚ	ΑΚ2 καπνού (2.50 · 2.52) – Υπνοδωμάτιο 1	τοίχος 1.37 · Υ1 1.04 · Π3 1.30
ΠΥ-ΑΚ3	ΟΚ	ΑΚ3 καπνού (7.90 · 2.52) – Υπνοδωμάτιο 2	τοίχος 1.35 · Υ6 1.04 · Π4 1.04
ΠΥ-ΑΚ4	ΟΚ	ΑΚ4 καπνού (5.05 · 3.70) – χωλ – άξονας διαδρόμου 0,90	τοίχος 0.45 (διάδρομος 0,90 – άξονας) · Χ1 …
ΠΥ-ΑΘ5	ΟΚ	ΑΘ5 θερμοδιαφορικός (8.22 · 7.70) – κουζίνα – θερμοδιαφορικός…	τοίχος 0.97 · Μ1 0.70 · Π2 1.75
ΠΥ-ΧΩΡ	ΟΚ	Κάλυψη χώρων	καθιστικό · κουζίνα (θερμικός) · Υπν.1 · Υπν…
ΘΕ-ΘΕ4	ΟΚ	ΘΕ4 40×40 – λουτρό: επίσκεψη αποχετεύσεων λουτρού Α΄	ελεύθερη
ΘΕ-ΘΕ5	ΟΚ	ΘΕ5 40×40 – Υπν.1: καθαριστήριο αποχέτευσης λουτρού γονέων …	ελεύθερη
ΚΡ-ΚΡ1	ΟΚ	ΚΡ1 W0.01 – καθιστικό – Δ · 20 × 10 cm · οδηγοί 7 / 14 cm	πλήρης · βάθος 10 cm
ΚΡ-ΚΡ2	ΟΚ	ΚΡ2 W0.02 · Θ0.03 · W0.03 – καθιστικό – Ν · 20 × 10 cm · οδηγοί 7…	πλήρης · βάθος 10 cm
ΚΡ-ΚΡ3	ΟΚ	ΚΡ3 W0.08 – Υπν.1 – Β · 20 × 10 cm · οδηγοί 7 / 14 cm	πλήρης · βάθος 32 cm
ΚΡ-ΚΡ4	ΟΚ	ΚΡ4 W0.06 – Υπν.2 – Α · 22 × 10 cm · οδηγοί 10 / 17 cm (μπαλκον…	πλήρης · βάθος 32 cm
ΚΡ-W0.07	ΟΚ	W0.07	δεν απαιτείται – λουτρό (στο τοιχείο Κ2)
ΚΡ-W0.05	ΟΚ	W0.05	δεν απαιτείται – κλιμακοστάσιο (εκτός διαμ…
ΣΘ-Ζ1	ΟΚ	Ζ1 +2,86 ↔ Ζ2 +2,62	ζώνη ΚΜ1 / κουζίνας· βόρεια στη γραμμή τ…
ΣΘ-Ζ4	ΟΚ	Ζ4 +2,62 ↔ Ζ5 / Ζ6 / Ζ7 +2,70	χωλ ↔ λουτρό / υπνοδωμάτια – μόνο σε πό…
ΣΘ-Ζ2	ΟΚ	Ζ2 +2,62 ↔ Ζ4 / Ζ3 +2,62	ίδια στάθμη – κανένα σκαλοπάτι στο πέρα…
ΣΘ-ΣΥΝ	ΟΚ	Στάθμες στο διαμέρισμα	+2.62 · +2.70 · +2.86 (καθιστικό +2,86 = 10…

B

ΕΡΓΟ **ΠΕΝΤΑΟΡΟΦΟ ΚΤΗΡΙΟ ΚΑΤΟΙΚΙΩΝ – ΑΡΓΥΡΟΥΠΟΛΗ** Κωνσταντινουπόλεως 12 & Αγ. Βαρβάρας · Ο.Τ. 103-15 Εργοδότης: INTERKAT Α.Ε. · Κατασκευή: ARKAD Ι.Κ.Ε.	ΘΕΜΑ ΣΧΕΔΙΟΥ **ΑΝΟΨΗ – ΕΛΕΓΧΟΣ ΠΡΟΔΙΑΓΡΑΦΩΝ** Συμμόρφωση · έλεγχος συγκρούσεων · αλλαγές R01 · ανοικτά σημεία ΙΣΟΓΕΙΟ – ΙΣ1 (Τ.Δ. θεωρήθηκε +0,45 στο σύστημα του Σ3)	ΒΑΣΗ Βάση: τοιχοποιίες ισογείου R13 · ξυλότυπος Σ3 (+3,65) · ανόψη Β1 R12	ΑΡ. ΣΧΕΔΙΟΥ **ΑΝ-04** — 07/11/2026 · R01

B

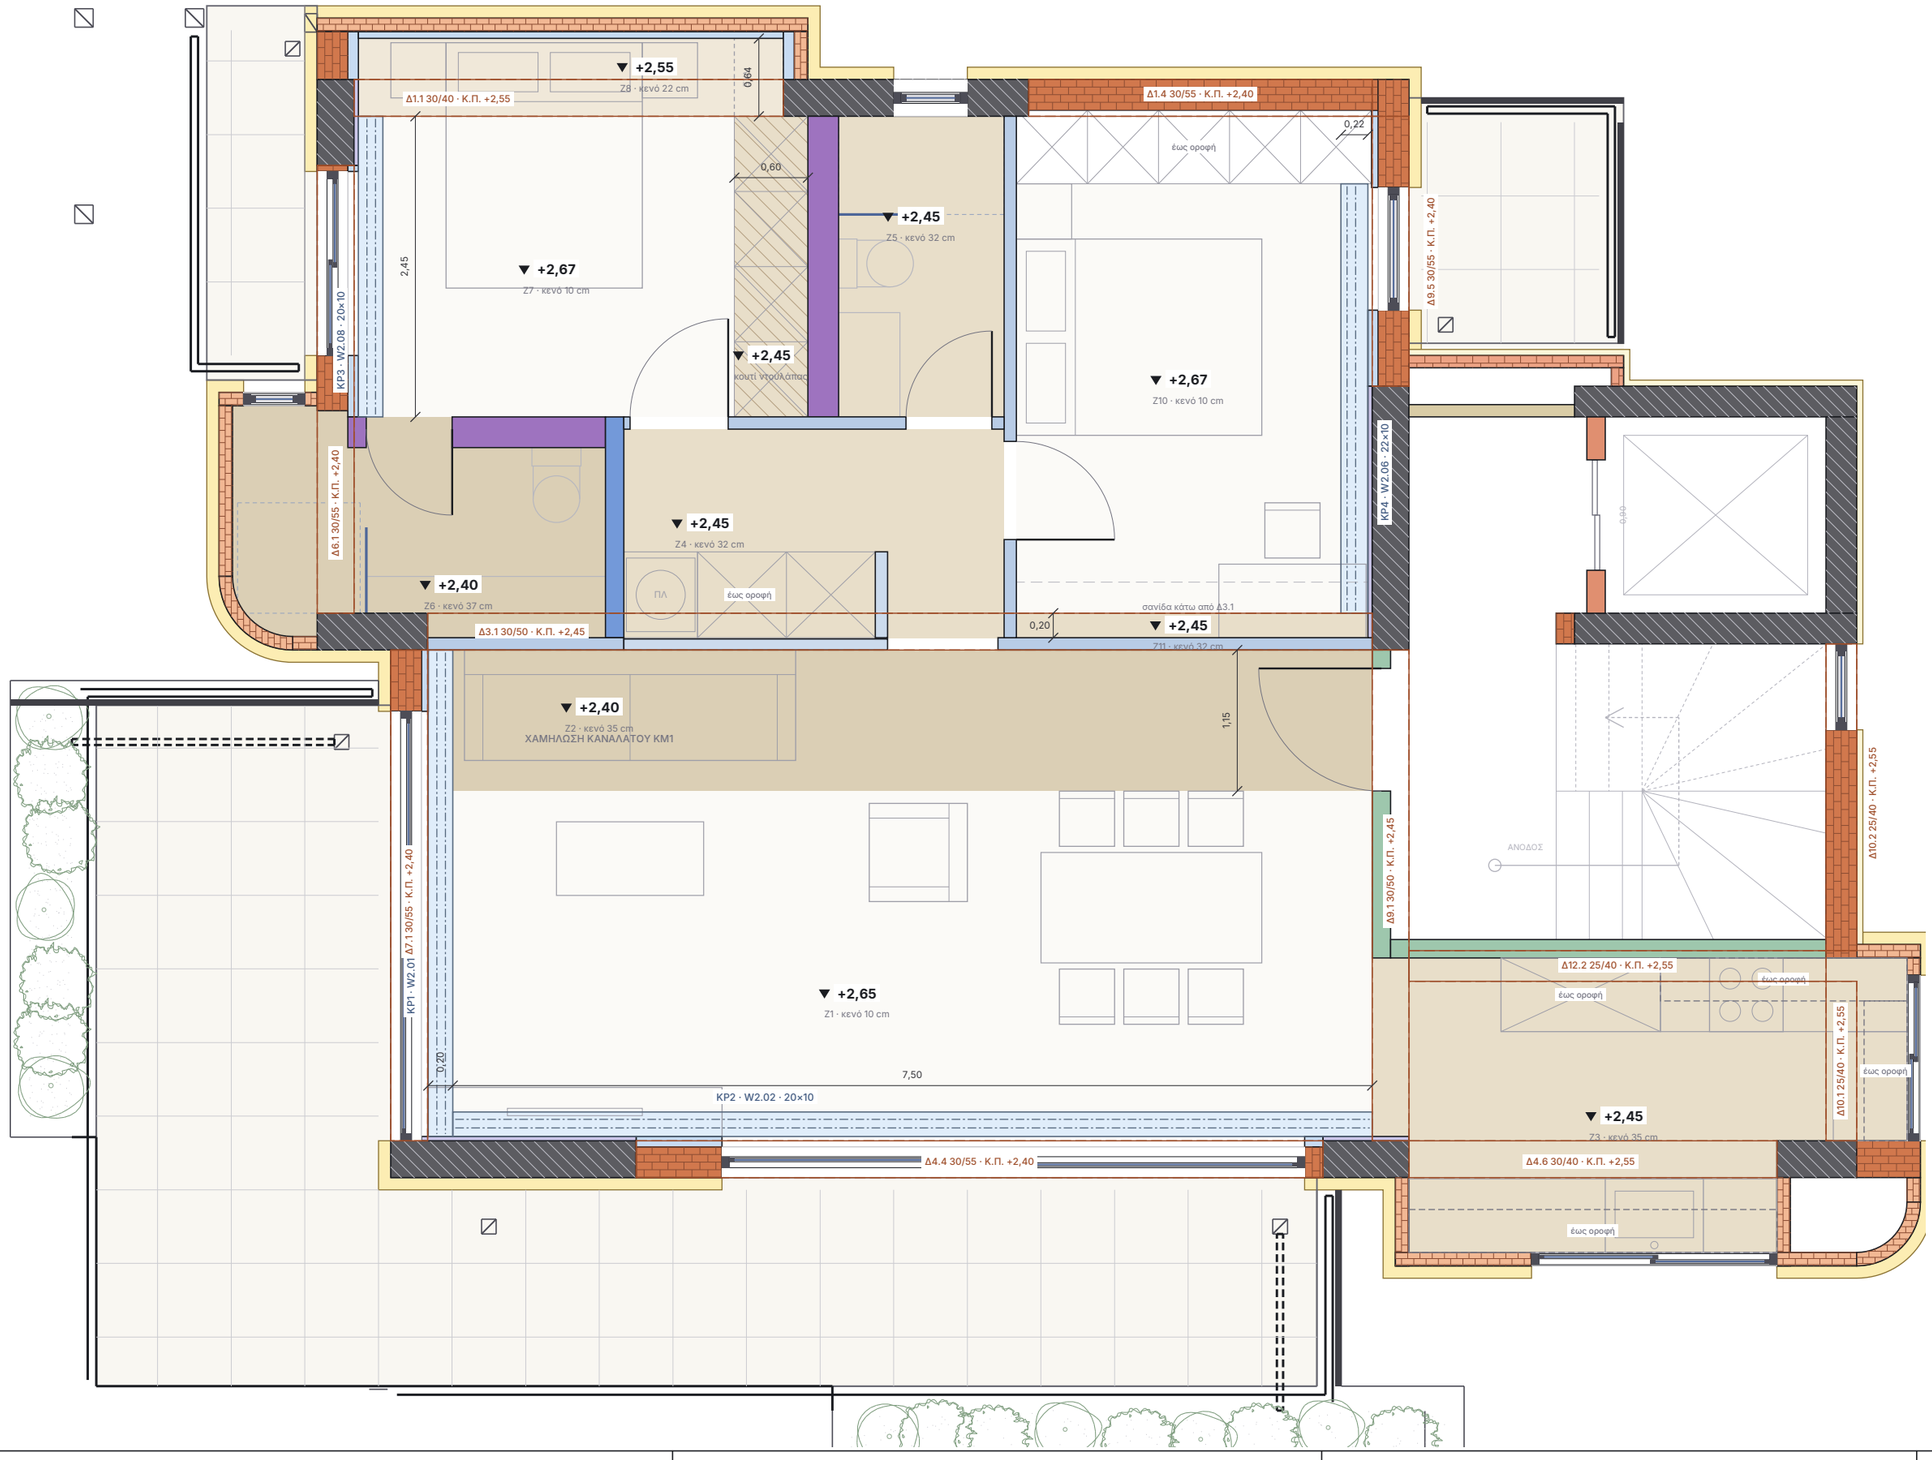

ΣΗΜΕΙΩΣΕΙΣ

Στάθμες από το τελικό δάπεδο του ορόφου (Β΄ +6,90). Πάνω παρειά πλάκας +2,95· κάτω παρειά Π3 h18 +2,77 · Π8 h20 +2,75 · Π10 h15 +2,80.

Κανόνας: πουθενά ψευδοροφή κάτω από κάτω παρειά δοκού· όπου «περασιά» η γυψοσανίδα στη δοκό προσθέτει ≈ 1,5 cm.

Αλλαγές στάθμης ΜΟΝΟ: χαμήλωση ΚΜ1 · γραμμή δοκού Δ9.1 (καθιστικό → κουζίνα) · γραμμή Δ1.1 (κεφαλάρι) · μετώπη ντουλάπας Υπν.1 (Π3) · σανίδα κάτω από Δ3.1 στο Υπν.2.


Κουρτινόθηκες: 20 × 10 cm (ΚΡ4 22 cm για το ανοιγοανακλινόμενο W2.06), σε όλο το μήκος του τοίχου, δίπλα (όχι κάτω) από τις δοκούς όψης.

R12: ΜΟΝΟ η χαμήλωση της ΚΜ1 −5 cm → +2,40 (κενό 35 cm): η Δ3.1 κρύβεται 5 cm και τα ψυκτικά της ΚΜ1 περνούν από κάτω της προς τη ντουλάπα του χωλ (ιδιοκτήτης 07/11). Το καθιστικό μένει +2,65. Στο άνοιγμα χωλ – καθιστικού: χωλ +2,45 (περασιά Δ3.1) / χαμήλωση +2,40.

ΥΠΟΜΝΗΜΑ

- +2,65 / +2,67 βασική = 10 cm κάτω από την πλάκα (spot σώμα ≤ 75 mm)
- +2,55 περασιά με δοκό 40 (κεφαλάρι Υπν.1)
- +2,45 περασιά με δοκό 50: χωλ · λουτρό · κουζίνα
- +2,40 χαμήλωση ΚΜ1 (5 cm κάτω από Δ3.1 – ψυκτικά) · λουτρό γονέων (περασιά Δ6.1)
- ΚΡ εσοχή κουρτίνας ανοιχτή ως την πλάκα · 2 οδηγοί
- δοκός (Σ5) · Κ.Π. = κάτω παρειά από Τ.Δ.

ΕΡΓΟ	ΘΕΜΑ ΣΧΕΔΙΟΥ	ΒΑΣΗ	ΑΡ. ΣΧΕΔΙΟΥ
ΠΕΝΤΑΟΡΟΦΟ ΚΤΗΡΙΟ ΚΑΤΟΙΚΙΩΝ – ΑΡΓΥΡΟΥΠΟΛΗ Κωνσταντινουπόλεως 12 & Αγ. Βαρβάρας · Ο.Τ. 103-15 Εργοδότης: INTERKAT Α.Ε. · Κατασκευή: ARKAD Ι.Κ.Ε.	**ΑΝΟΨΗ – ΣΤΑΘΜΕΣ · ΔΟΚΟΙ · ΚΟΥΡΤΙΝΕΣ** Στάθμες ψευδοροφής · δοκοί Σ5 · εσοχές κουρτινών Α΄ · Β΄ · Γ΄ ΟΡΟΦΟΣ – Β1 (τυπικός όροφος)	Βάση: τοιχοποιίες Β1 R25 · ξυλότυπος Σ5 (+9,85) · ανόψη R10	**ΑΝ-05** **Κλίμακα 1:50 · Α3** 07/11/2026 · R12

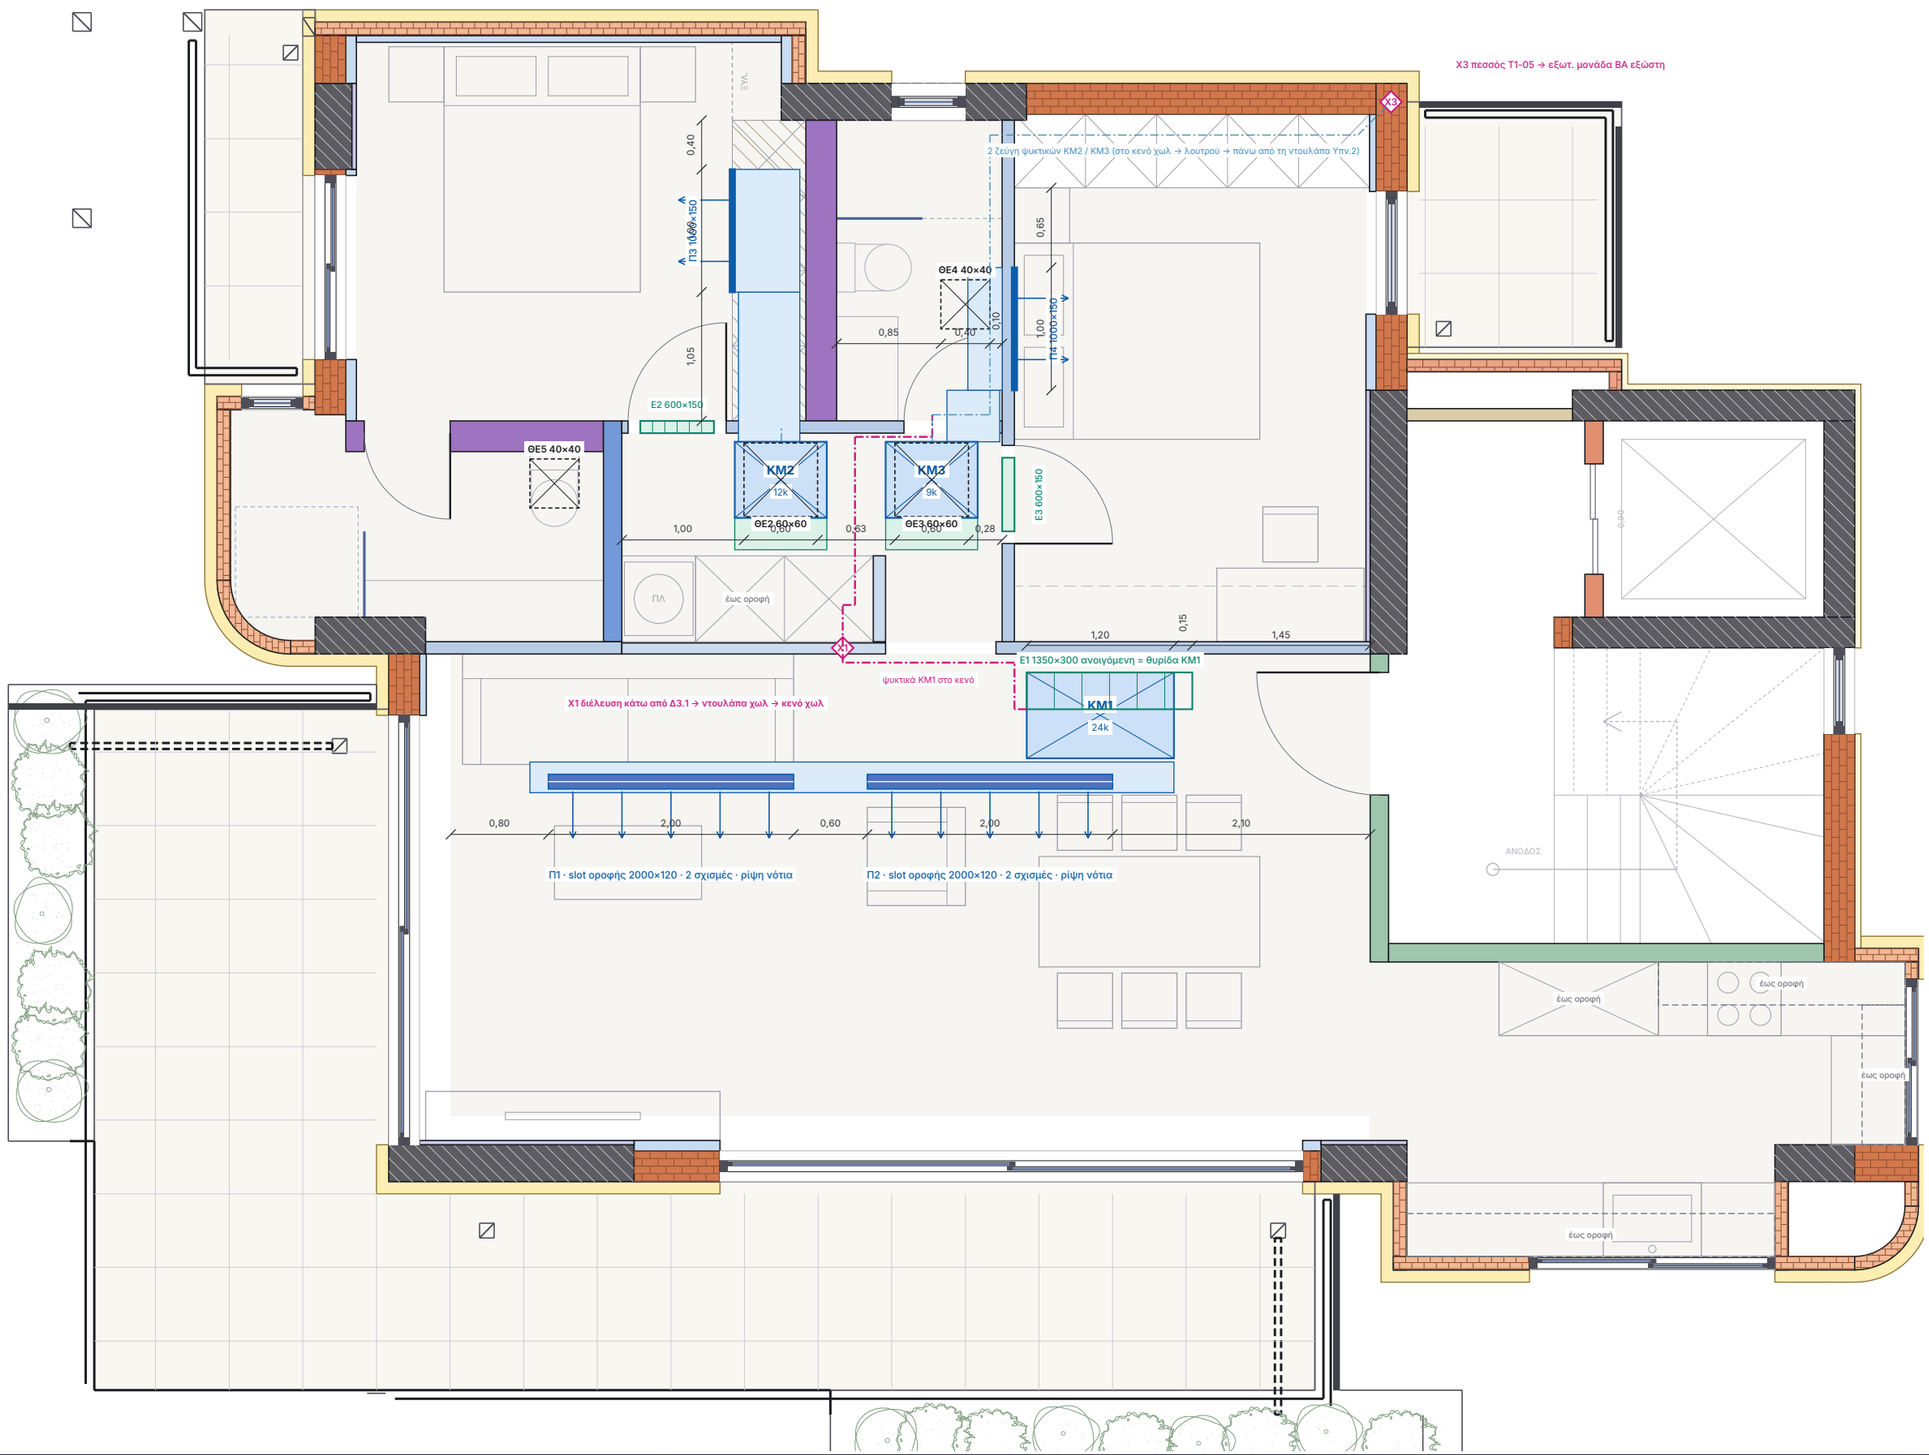

ΕΡΓΟ

ΠΕΝΤΑΟΡΟΦΟ ΚΤΗΡΙΟ ΚΑΤΟΙΚΙΩΝ – ΑΡΓΥΡΟΥΠΟΛΗ
Κωνσταντινουπόλεως 12 & Αγ. Βαρβάρας · Ο.Τ. 103-15
Εργοδότης: INTERKAT Α.Ε. · Κατασκευή: ARKAD Ι.Κ.Ε.

ΘΕΜΑ ΣΧΕΔΙΟΥ


ΑΝΟΨΗ – ΚΛΙΜΑΤΙΣΜΟΣ · ΘΥΡΙΔΕΣ
Καναλάτες μονάδες · αεραγωγοί · στόμια · θυρίδες επίσκεψης · ψυκτικά
Α΄ · Β΄ · Γ΄ ΟΡΟΦΟΣ – Β1 (τυπικός όροφος)

ΒΑΣΗ

Βάση: τοιχοποιίες Β1 R25 · ξυλότυπος Σ5 (+9,85) · ανόψη R10

ΑΡ. ΣΧΕΔΙΟΥ

ΑΝ-06
Κλίμακα 1:50 · Α3
07/11/2026 · R12

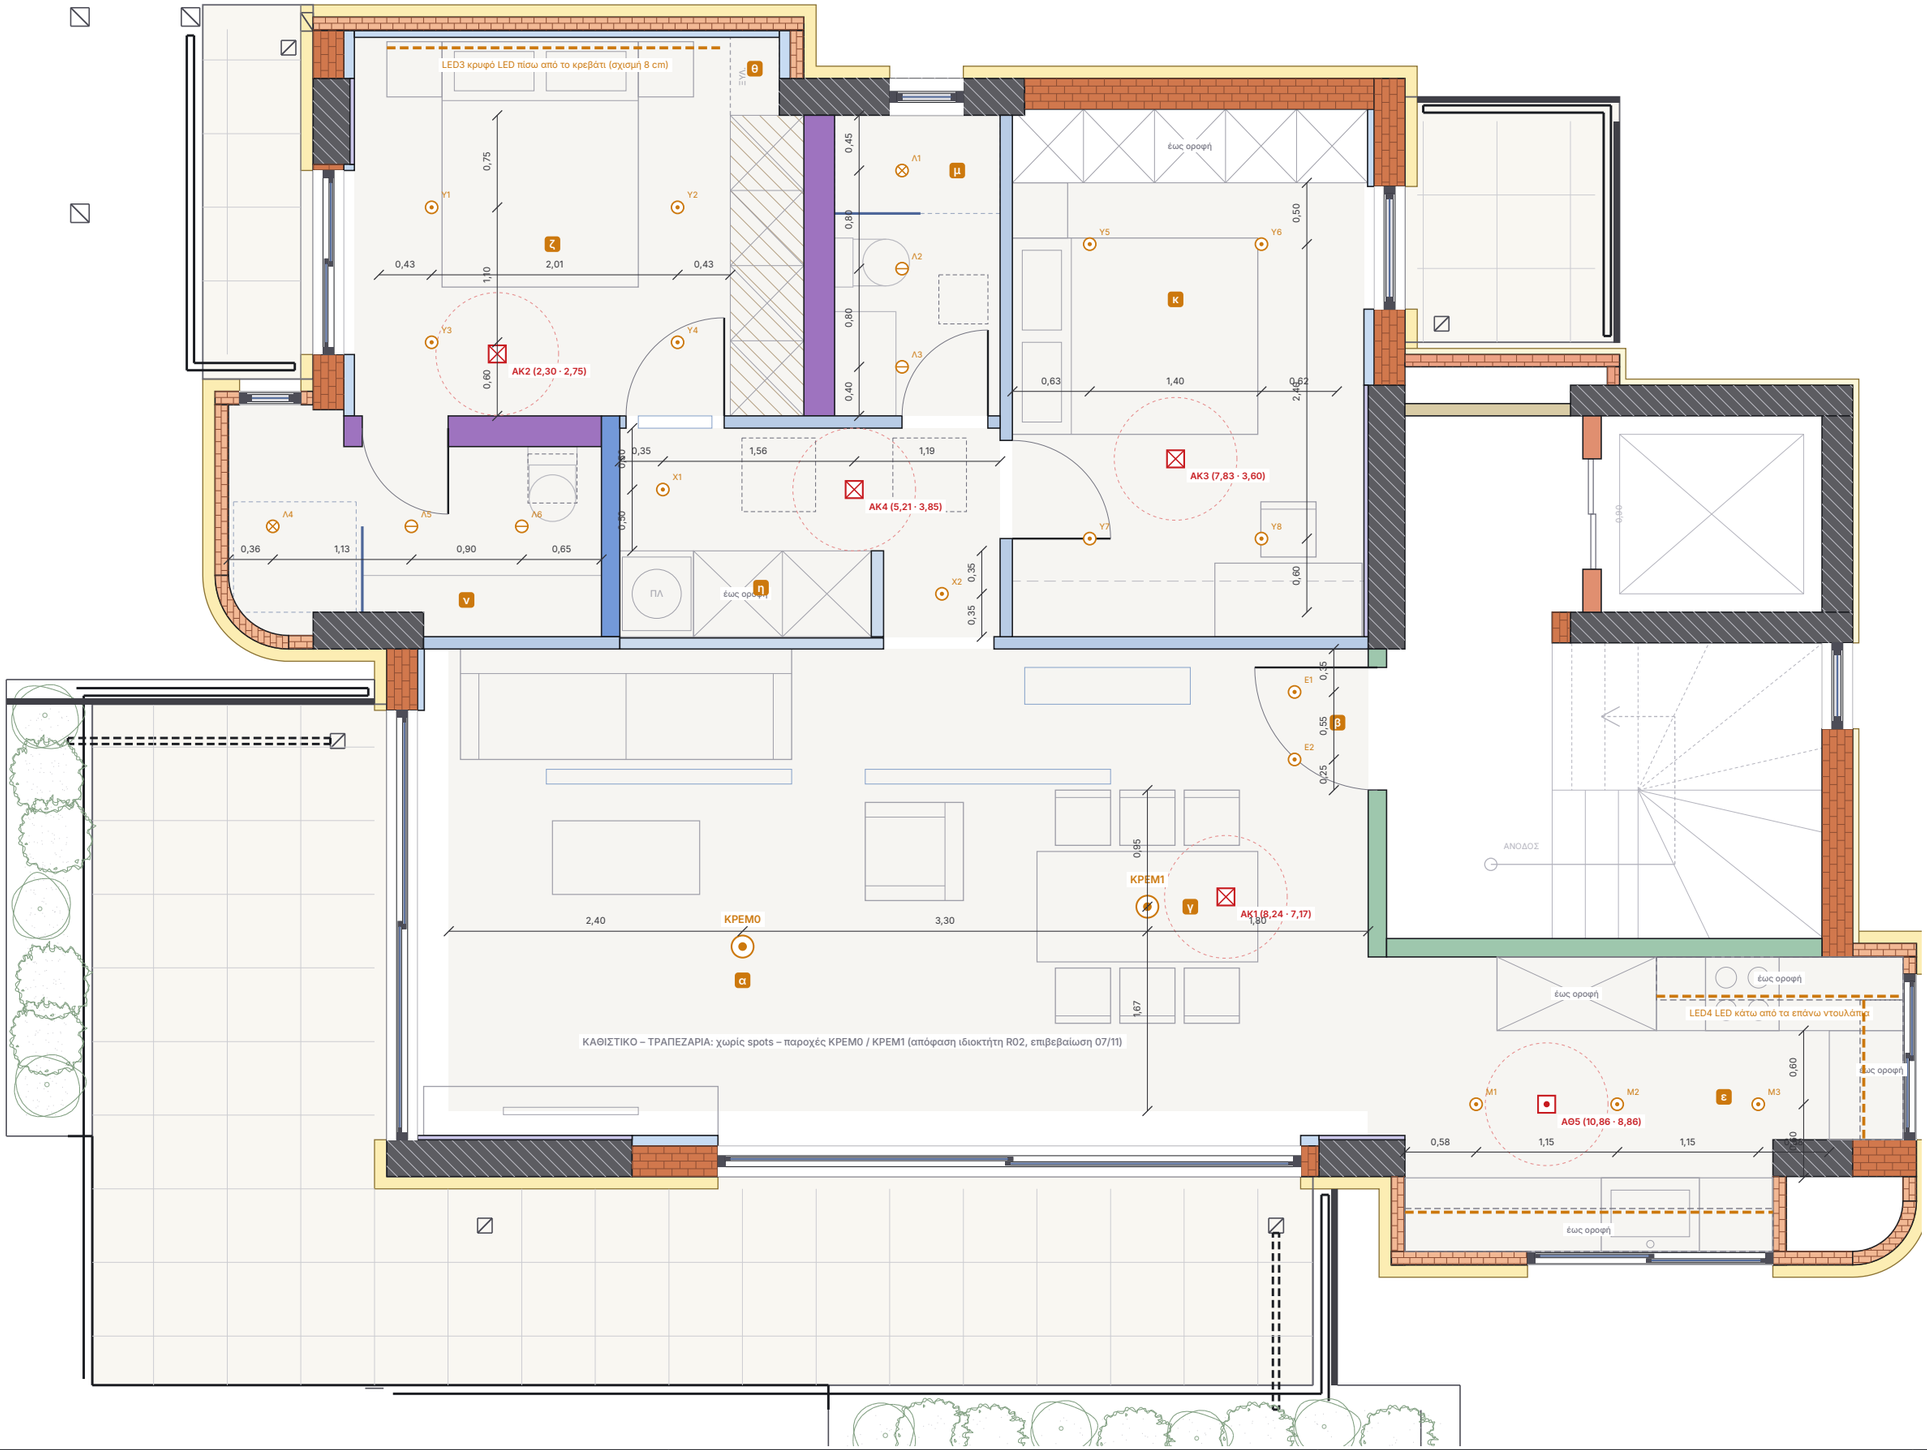

ΣΗΜΕΙΩΣΕΙΣ

Κατανομή: Υπν. 2 × 2 spots συμμετρικά στην ελεύθερη οροφή · λουτρά 3 (IP65 στο ντους) · κουζίνα 3 στον άξονα του διαδρόμου (γενικός) + LED κάτω από τα ντουλάπια (πάγκος) · χωλ / είσοδος στον άξονα της διαδρομής. Σύνολο 21 spots + 2 παροχές + LED3 + LED4.

Πυρανίχνευση (προδ. 4): σε κάθε κύριο χώρο και στο χωλ· ≥ 0,50 από τοίχους / δοκούς / φωτιστικά, ≥ 1,00 από στόμια προσαγωγής· λουτρά χωρίς ανιχνευτή καπνού (υδρατμοί).

R11 χωλ: AK4 στον άξονα του διαδρόμου 1,00 (0,50 από τους δύο τοίχους, ανάμεσα στις ΘΕ2 / ΘΕ3)· X1 στον άξονα, X2 στο κέντρο του περάσματος. Στο R10 ο AK4 ήταν 0,29 από την ακμή και ≈ 0,30 από spot.

R11: Y1–Y4 0,43 από KP3 / μέτωπο ντουλάπας 4,20 · KPEM1 στο κέντρο της τραπεζαρίας R23.

R12 κουζίνα (ιδιοκτήτης 07/11): επάνω ντουλάπια περασιά με την οροφή (διακεκομμένα) με LED4 από κάτω για τον πάγκο· τα spots M1–M3 είναι γενικός φωτισμός στον άξονα του διαδρόμου (y 8,86), 0,60 από τη στήλη / τους πάγκους, κανένα πάνω από ντουλάπι. AΘ5 ανάμεσα στα M1 / M2, 1,4 m από τις εστίες. Χωρίς Wi-Fi.

Οπή spot Ø 75–80 ανάμεσα στα προφίλ CD (όχι πάνω τους)· όπου πέφτει σε προφίλ, μετατόπιση του προφίλ – όχι του spot.

ΥΠΟΜΝΗΜΑ

- χωνευτό spot LED 7–9 W, 2700 K, CRI ≥ 90, UGR < 19, σώμα ≤ 75 mm
- χωνευτό spot IP44 (λουτρά)
- χωνευτό spot IP65 (πάνω από ντους)
- KPEM παροχή οροφής (κουτί + ενίσχυση ανάρτησης)
- AK ανιχνευτής καπνού (ΕΠ04 · EN 54-7)
- AΘ θερμοδιαφορικός ανιχνευτής (κουζίνα · EN 54-5)
- ακτίνα 0,50 m γύρω από ανιχνευτή – κανένας τοίχος / φωτιστικό μέσα
- LED κρυφό γραμμικό 3000 K – LED3 κεφαλάρι · LED4 κάτω από τα ντουλάπια κουζίνας

ΕΡΓΟ

ΠΕΝΤΑΟΡΟΦΟ ΚΤΗΡΙΟ ΚΑΤΟΙΚΙΩΝ – ΑΡΓΥΡΟΥΠΟΛΗ
Κωνσταντινουπόλεως 12 & Αγ. Βαρβάρας · Ο.Τ. 103-15
Εργοδότης: INTERKAT Α.Ε. · Κατασκευή: ARKAD Ι.Κ.Ε.

ΘΕΜΑ ΣΧΕΔΙΟΥ

ΑΝΟΨΗ – ΦΩΤΙΣΜΟΣ · ΠΥΡΑΝΙΧΝΕΥΣΗ
Χωνευτά spots · παροχές · κρυφό LED · ανιχνευτές
Α΄ · Β΄ · Γ΄ ΟΡΟΦΟΣ – Β1 (τυπικός όροφος)

ΒΑΣΗ

Βάση: τοιχοποιίες B1 R25 · ξυλότυπος Σ5 (+9,85) · ανόψη R10

ΑΡ. ΣΧΕΔΙΟΥ

AN-07
Κλίμακα 1:50 · A3
07/11/2026 · R12

ΣΥΜΜΟΡΦΩΣΗ ΜΕ ΤΙΣ ΠΡΟΔΙΑΓΡΑΦΕΣ (ιδιοκτήτης 07/11/2026)

1 Κλιματισμός — Καναλάτη σε καθιστικό (ΚΜ1 24k), Υπν.1 (ΚΜ2 12k), Υπν.2 (ΚΜ3 9k) · κουζίνα από την ΚΜ1 (ΕΓΚΕΚΡ.) · slot Π1/Π2 στο καθιστικό, γραμμικά Π3/Π4 στα υπνοδωμάτια (ΕΓΚΕΚΡ.) · χώρος 35 / 32 cm (ΚΜ1 περιθώριο 55 mm) · θυρίδες Ε1 / ΘΕ2 / ΘΕ3 · ψυκτικά ΚΜ1 κάτω από τη Δ3.1 (οριακό 3,6 mm).

2 Κουρτίνες — ΚΡ1–ΚΡ4 σε όλα τα ανοίγματα καθιστικού / υπνοδωματίων, 20 (22) × 10 cm, 2 οδηγοί, ανοιχτές ως την πλάκα, δίπλα στις δοκούς όψης.

3 Φωτισμός — 21 χωνευτά spots σε υπνοδωμάτια, λουτρά, χωλ, είσοδο, κουζίνα (γενικός) + LED κάτω από τα ντουλάπια κουζίνας (IP44/IP65 στα λουτρά) · καθιστικό με ΚΡΕΜ0/ΚΡΕΜ1 (ΕΓΚΕΚΡ.) · κανένα spot κάτω από μονάδα / αεραγωγό / σε θυρίδα / πάνω από ντουλάπι · κενό ≥ 88 mm πάνω από κάθε spot.

4 Πυρανίχνευση — ΑΚ1–ΑΚ4 καπνού + ΑΘ5 θερμοδιαφορικός κουζίνας · όλοι ≥ 0,50 από τοίχους / δοκούς / φωτιστικά και ≥ 1,00 από στόμια προσαγωγής.

5 Κατασκευή — Βασική 10 cm κάτω από την πλάκα · μεγαλύτερη καταβίβαση μόνο στις καναλάτες (+2,40 / +2,45) · περασιά με τις δοκούς · μία σανίδα κάτω από τη Δ3.1 στο Υπν.2 (εξαίρεση) · κανένα δόντι.

6 Γενική αρχή — 5 στάθμες σε όλο το διαμέρισμα, κάθε αλλαγή πάνω σε γραμμή δοκού ή μετώπη ντουλάπας.

ΕΓΚΕΚΡΙΜΕΝΕΣ ΑΠΟΚΛΙΣΕΙΣ (ιδιοκτήτης 07/11/2026)

- Καθιστικό – τραπεζαρία χωρίς spots (απόφαση R02· «η νέα προδιαγραφή δεν υπερισχύει»).
- Κουζίνα χωρίς δική της καναλάτη – καλύπτεται από την ΚΜ1 24k.
- Π3 / Π4 υπνοδωματίων: γραμμικά στόμια 1000×150 σε μετώπη / τοίχο, όχι slot.
- Μονάδες slim ≤ 245 mm (ΚΜ1) / ≤ 200 mm (ΚΜ2, ΚΜ3) ως παραδοχή μέχρι την επιλογή μοντέλου.

ΑΛΛΑΓΕΣ R11 → R12 (ιδιοκτήτης 07/11/2026)

- Χαμήλωση ΚΜ1 −5 cm: +2,45 → +2,40 (κενό 35 cm) – ΜΟΝΟ η χαμήλωση, το καθιστικό μένει +2,65 (ιδιοκτήτης 07/11). Η Δ3.1 (+2,45) κρύβεται πλέον 5 cm και τα ψυκτικά της ΚΜ1 περνούν από κάτω της: συνδέσεις δυτικά → βόρεια ακμή της χαμήλωσης → μέσα από τον Τ2Ν-01 στο επάνω μέρος της ντουλάπας χωλ (x ≈ 5,10) → κενό χωλ → μαζί με ΚΜ2 / ΚΜ3 ως τον πεσσό Τ1-05. Καταργείται το κατέβασμα στην είσοδο (ΝΤ4 / κανάλι). Η ΚΜ1 έχει τώρα περιθώριο 55 mm (ήταν 5).
- Χωρίς Wi-Fi access point (ιδιοκτήτης 07/11).
- Κουζίνα: επάνω ντουλάπια περασιά με την οροφή και LED από κάτω (ιδιοκτήτης 07/11) – ο πάγκος φωτίζεται από το LED4· τα spots της οροφής γίνονται γενικός φωτισμός: Μ1–Μ3 στον άξονα του διαδρόμου της κουζίνας (y 8,86, x 10,28 / 11,43 / 12,58)· ΑΘ5 ανάμεσα στα Μ1 / Μ2, 1,4 m από τις εστίες. Στο R11 το Μ1 έπεφτε στη στήλη ψυγείου (διάταξη Δ΄ R04 / αρχιτέκτονα) και το Μ6 πάνω στα ντουλάπια του έρκερ. Σύνολο 21 spots.

ΠΡΟΗΓΟΥΜΕΝΗ ΑΝΑΘΕΩΡΗΣΗ

- R11: βάση τοιχοποιίες B1 R25 · Π3 / αεραγωγός ΚΜ2 στη ντουλάπα 4,20–4,80 · ΘΕ4 έξω από το ντους · ΑΚ4 στον άξονα του διαδρόμου · χωλ 2 spots · ΚΡΕΜ1 στο κέντρο της τραπεζαρίας · ΚΡ4 από 1,35.

ΑΝΟΙΚΤΑ ΣΗΜΕΙΑ

- Α1 [ΚΑΤΑΣΚΕΥΗ] Διέλευση ψυκτικών ΚΜ1 κάτω από τη Δ3.1: καθαρό ύψος 2,45 − 2,40 − γυψοσανίδα 12,5 = 37,5 mm. Χωράει σωλήνας αερίου 5/8″ με μόνωση 9 mm (Ø ≈ 34) – με μόνωση 13 mm (Ø ≈ 42) ΟΧΙ. Στο σημείο διέλευσης χωρίς περιμετρικό UD, οι σωλήνες δίπλα-δίπλα (όχι ο ένας πάνω στον άλλο)· στη ντουλάπα χωλ επάνω καπάκι ≤ +2,40 στα νότια 0,25 (κάτω από τη δοκό). Αν ο ψυκτικός θέλει 13 mm: χαμήλωση στο +2,38.
- Α2 [ΜΟΝΤΕΛΟ] Μοντέλα καναλάτων: έλεγχος ύψους (≤ 245 / ≤ 200 mm) και θέσης ηλεκτρικού κουτιού / αντλίας της ΚΜ1 – αν δεν φτάνονται από την ανοιγόμενη Ε1 (300 mm), προστίθεται θυρίδα 40×40 στο ανατολικό άκρο της μονάδας.
- Α3 [ΣΤΑΤΙΚΟΣ] Διατομή Δ10.1 (χωρίς ετικέτα στον Σ5 – θεωρήθηκε 25/40). Δεν επηρεάζει τη στάθμη της κουζίνας (+2,45 ≤ 2,55).
- Α4 [ΕΠΙ ΤΟΠΟΥ] Μέτρηση πλακών / δοκών μετά το ξεκαλούπωμα κάθε ορόφου (Α΄ Σ4 · Β΄ Σ5 · Γ΄ Σ6) πριν τη χάραξη – η ανόψη θεωρεί ίδιους δοκούς στους τρεις τυπικούς ορόφους· οι Σ4 / Σ6 να ελεγχθούν.


ΕΛΕΓΧΟΣ ΣΥΓΚΡΟΥΣΕΩΝ & ΣΤΑΘΜΩΝ – 73 έλεγχοι · ΟΚ 68 · ΟΡΙΑΚΟ 1 · ΕΓΚΕΚΡ. 4 · ΑΠΟΚΛΙΣΗ 0

Αυτόματος έλεγχος από το μοντέλο (code/anopseis/checks.py): στάθμες ↔ δοκοί · κενό μονάδων · θυρίδες · spots ↔ ζώνες / θυρίδες / μονάδες / αεραγωγοί / κουρτινόθηκες · ανιχνευτές ↔ τοίχοι / φωτιστικά / στόμια · κουρτινόθηκες ↔ κουφώματα / δοκοί.

ΚΩΔ.	ΚΑΤΑΣΤ.	ΣΤΟΙΧΕΙΟ	ΜΕΤΡΗΣΗ
ΣΤ01	ΟΚ	Ζ3 ΚΟΥΖΙΝΑ ↔ Δ9.1 30/50 (Κ.Π. +2.45)	οροφή +2.45 · περασιά
ΣΤ02	ΟΚ	Ζ3 ΚΟΥΖΙΝΑ ↔ Δ4.6 30/40 (Κ.Π. +2.55)	οροφή +2.45 · κρυμμένη 10 cm
ΣΤ03	ΟΚ	Ζ3 ΚΟΥΖΙΝΑ ↔ Δ12.2 25/40 (Κ.Π. +2.55)	οροφή +2.45 · κρυμμένη 10 cm
ΣΤ04	ΟΚ	Ζ3 ΚΟΥΖΙΝΑ ↔ Δ10.1 25/40 (Κ.Π. +2.55)	οροφή +2.45 · κρυμμένη 10 cm
ΣΤ05	ΟΚ	Ζ4 ΧΩΛ ↔ Δ3.1 30/50 (Κ.Π. +2.45)	οροφή +2.45 · περασιά
ΣΤ06	ΟΚ	Ζ6 ΛΟΥΤΡΟ ΓΟΝΕΩΝ ↔ Δ6.1 30/55 (Κ.Π. +2.40)	οροφή +2.40 · περασιά
ΣΤ07	ΟΚ	Ζ6 ΛΟΥΤΡΟ ΓΟΝΕΩΝ ↔ Δ3.1 30/50 (Κ.Π. +2.45)	οροφή +2.40 · κρυμμένη 5 cm
ΣΤ08	ΟΚ	Ζ8 ΚΕΦΑΛΑΡΙ ΥΠΝ.1 (έρκερ) ↔ Δ1.1 30/40 (Κ.Π. +2.55)	οροφή +2.55 · περασιά
ΣΤ09	ΟΚ	Ζ11 ΣΑΝΙΔΑ ΚΑΤΩ ΑΠΟ Δ3.1 (Υπν.2) ↔ Δ3.1 30/50 (Κ.Π. +2.45)	οροφή +2.45 · περασιά
ΚΛ-ΚΜ1	ΟΚ	ΚΜ1 24.000 Btu/h – καθιστικό – τραπεζαρία – κουζίνα	κενό 350 mm · περιθώριο +55 mm
ΘΕ-ΚΜ1	ΟΚ	ΚΜ1 – πρόσβαση συντήρησης	Ε1
ΚΛ-ΚΜ2	ΟΚ	ΚΜ2 12.000 Btu/h – Υπνοδωμάτιο 1	κενό 320 mm · περιθώριο +70 mm
ΘΕ-ΚΜ2	ΟΚ	ΚΜ2 – πρόσβαση συντήρησης	ΘΕ2
ΚΛ-ΚΜ3	ΟΚ	ΚΜ3 9.000 Btu/h – Υπνοδωμάτιο 2	κενό 320 mm · περιθώριο +70 mm
ΘΕ-ΚΜ3	ΟΚ	ΚΜ3 – πρόσβαση συντήρησης	ΘΕ3
ΨΥ-ΚΜ1	ΟΚ	Όδευση ψυκτικών ΚΜ1 χαμήλωση → ντουλάπα χωλ → κενό χωλ…	ελάχιστο 280 mm
ΨΥ-ΔΟΚ	ΟΡΙΑΚΟ	Διέλευση ψυκτικών ΚΜ1 κάτω από τη Δ3.1 (x ≈ 5.10, Τ2Ν-01 → ντο…	καθαρό 37.5 mm · περιθώριο +3.6 mm
ΚΔ-ΚΜ1	ΟΚ	Καθιστικό – τραπεζαρία	ΚΜ1
ΚΔ-ΚΜ2	ΟΚ	Υπνοδωμάτιο 1	ΚΜ2
ΚΔ-ΚΜ3	ΟΚ	Υπνοδωμάτιο 2	ΚΜ3
ΚΔ-ΚΟΥΖ	ΕΓΚΕΚΡ.	Κουζίνα	από την ΚΜ1 (ανοιχτή στο καθιστικό)
ΣΤ-Π1	ΟΚ	Π1 slot οροφής 2000×120 · 2 σχισμές	μέσα
ΣΤ-Π2	ΟΚ	Π2 slot οροφής 2000×120 · 2 σχισμές	μέσα
ΣΤ-Π3	ΕΓΚΕΚΡ.	Π3 γραμμικό 1000×150 · μετώπη ντουλάπας +2,48…+2,63	γραμμικό στόμιο μετώπης / τοίχου
ΣΤ-Π4	ΕΓΚΕΚΡ.	Π4 γραμμικό 1000×150 · τοίχος +2,48…+2,63	γραμμικό στόμιο μετώπης / τοίχου
SP-Υ1	ΟΚ	Υ1 spot (1.765 · 1.550) – ΥΠΝΟΔΩΜΑΤΙΟ 1	κενό 88 mm · άκρη 0.63
SP-Υ2	ΟΚ	Υ2 spot (3.770 · 1.550) – ΥΠΝΟΔΩΜΑΤΙΟ 1	κενό 88 mm · άκρη 0.43
SP-Υ3	ΟΚ	Υ3 spot (1.765 · 2.650) – ΥΠΝΟΔΩΜΑΤΙΟ 1	κενό 88 mm · άκρη 0.60
SP-Υ4	ΟΚ	Υ4 spot (3.770 · 2.650) – ΥΠΝΟΔΩΜΑΤΙΟ 1	κενό 88 mm · άκρη 0.43
SP-Υ5	ΟΚ	Υ5 spot (7.130 · 1.850) – ΥΠΝΟΔΩΜΑΤΙΟ 2	κενό 88 mm · άκρη 0.50
SP-Υ6	ΟΚ	Υ6 spot (8.530 · 1.850) – ΥΠΝΟΔΩΜΑΤΙΟ 2	κενό 88 mm · άκρη 0.50
SP-Υ7	ΟΚ	Υ7 spot (7.130 · 4.250) – ΥΠΝΟΔΩΜΑΤΙΟ 2	κενό 88 mm · άκρη 0.60
SP-Υ8	ΟΚ	Υ8 spot (8.530 · 4.250) – ΥΠΝΟΔΩΜΑΤΙΟ 2	κενό 88 mm · άκρη 0.60
SP-Λ1	ΟΚ	Λ1 spot IP65 (5.600 · 1.250) – ΛΟΥΤΡΟ	κενό 307 mm · άκρη 0.45
SP-Λ2	ΟΚ	Λ2 spot IP44 (5.600 · 2.050) – ΛΟΥΤΡΟ	κενό 307 mm · άκρη 0.55
SP-Λ3	ΟΚ	Λ3 spot IP44 (5.600 · 2.850) – ΛΟΥΤΡΟ	κενό 307 mm · άκρη 0.40
SP-Λ4	ΟΚ	Λ4 spot IP65 (0.470 · 4.150) – ΛΟΥΤΡΟ ΓΟΝΕΩΝ	κενό 358 mm · άκρη 0.36
SP-Λ5	ΟΚ	Λ5 spot IP44 (1.600 · 4.150) – ΛΟΥΤΡΟ ΓΟΝΕΩΝ	κενό 358 mm · άκρη 0.70
SP-Λ6	ΟΚ	Λ6 spot IP44 (2.500 · 4.150) – ΛΟΥΤΡΟ ΓΟΝΕΩΝ	κενό 358 mm · άκρη 0.65
SP-Χ1	ΟΚ	Χ1 spot (3.650 · 3.850) – ΧΩΛ	κενό 307 mm · άκρη 0.35
SP-Χ2	ΟΚ	Χ2 spot (5.925 · 4.700) – ΧΩΛ	κενό 307 mm · άκρη 0.35
SP-Ε1	ΟΚ	Ε1 spot (8.800 · 5.500) – ΧΑΜΗΛΩΣΗ ΚΑΝΑΛΑΤΟΥ / ΕΙΣΟΔΟΣ	κενό 338 mm · άκρη 0.35
SP-Ε2	ΟΚ	Ε2 spot (8.800 · 6.050) – ΧΑΜΗΛΩΣΗ ΚΑΝΑΛΑΤΟΥ / ΕΙΣΟΔΟΣ	κενό 338 mm · άκρη 0.25
SP-Μ1	ΟΚ	Μ1 spot (10.280 · 8.860) – ΚΟΥΖΙΝΑ	κενό 337 mm · άκρη 0.63
SP-Μ2	ΟΚ	Μ2 spot (11.430 · 8.860) – ΚΟΥΖΙΝΑ	κενό 337 mm · άκρη 1.20
SP-Μ3	ΟΚ	Μ3 spot (12.580 · 8.860) – ΚΟΥΖΙΝΑ	κενό 337 mm · άκρη 0.31
SP-ΚΑΘ	ΕΓΚΕΚΡ.	Καθιστικό – τραπεζαρία	παροχές ΚΡΕΜ0 / ΚΡΕΜ1 (απόφαση R02)
ΠΥ-ΑΚ1	ΟΚ	ΑΚ1 καπνού (8.24 · 7.17) – καθιστικό – τραπεζαρία (R05: 0,55 από…	τοίχος 0.87 · ΚΡΕΜ1 0.64 · Π2 1.32
ΠΥ-ΑΚ2	ΟΚ	ΑΚ2 καπνού (2.30 · 2.75) – Υπνοδωμάτιο 1	τοίχος 0.50 · Υ3 0.54 · Π3 1.96
ΠΥ-ΑΚ3	ΟΚ	ΑΚ3 καπνού (7.83 · 3.60) – Υπνοδωμάτιο 2	τοίχος 1.25 · Υ8 0.96 · Π4 1.44
ΠΥ-ΑΚ4	ΟΚ	ΑΚ4 καπνού (5.21 · 3.85) – χωλ – άξονας διαδρόμου 1,00, ανάμεσ…	τοίχος 0.50 · Λ3 1.07 · Π4 1.53
ΠΥ-ΑΘ5	ΟΚ	ΑΘ5 θερμοδιαφορικός (10.86 · 8.86) – κουζίνα – θερμοδιαφορικό…	τοίχος 0.60 · Μ2 0.57 · Π2 4.41
ΠΥ-ΧΩΡ	ΟΚ	Κάλυψη χώρων	καθιστικό · Υπν.1 · Υπν.2 · χωλ · κουζίνα (θ…
ΘΕ-ΘΕ2	ΟΚ	ΘΕ2 60×60 – ΚΜ2 (φίλτρο, ηλεκτρικό κουτί, αντλία)	ελεύθερη
ΘΕ-ΘΕ3	ΟΚ	ΘΕ3 60×60 – ΚΜ3 (φίλτρο, ηλεκτρικό κουτί, αντλία)	ελεύθερη
ΘΕ-ΘΕ4	ΟΚ	ΘΕ4 40×40 – λουτρό: plenum / ρύθμιση Π4 · έξω από το ντους (R1…	ελεύθερη
ΘΕ-ΘΕ5	ΟΚ	ΘΕ5 40×40 – λουτρό γονέων: αποχέτευση άνω ορόφου (θέση κατ…	ελεύθερη
ΚΡ-ΚΡ1	ΟΚ	ΚΡ1 W2.01 – καθιστικό – Δ · 20 × 10 cm · οδηγοί 7 / 14 cm	πλήρης · βάθος 10 cm
ΚΡ-ΚΡ2	ΟΚ	ΚΡ2 W2.02 – καθιστικό – Ν · 20 × 10 cm · οδηγοί 7 / 14 cm	πλήρης · βάθος 10 cm
ΚΡ-ΚΡ3	ΟΚ	ΚΡ3 W2.08 – Υπν.1 – Δ · 20 × 10 cm · οδηγοί 7 / 14 cm	πλήρης · βάθος 10 cm
ΚΡ-ΚΡ4	ΟΚ	ΚΡ4 W2.06 – Υπν.2 – Α · 22 × 10 cm · οδηγοί 10 / 17 cm (ανοιγοα…	πλήρης · βάθος 10 cm
ΚΡ-W2.03	ΟΚ	W2.03	δεν απαιτείται – κουζίνα – πάνω από τον ν…
ΚΡ-W2.04	ΟΚ	W2.04	δεν απαιτείται – κουζίνα – έρκερ, πάνω από…
ΚΡ-W2.05	ΟΚ	W2.05	δεν απαιτείται – κλιμακοστάσιο (εκτός διαμ…
ΚΡ-W2.07	ΟΚ	W2.07	δεν απαιτείται – λουτρό (στο τοιχείο Κ2)
ΚΡ-W2.09	ΟΚ	W2.09	δεν απαιτείται – λουτρό γονέων (ντους)
ΣΘ-Ζ1	ΟΚ	Ζ1 +2,65 ↔ Ζ2 +2,40	χαμήλωση καναλάτου ΚΜ1 (προδ. 1/5)
ΣΘ-Ζ4	ΟΚ	Ζ4 +2,45 ↔ Ζ2 +2,40	στη γραμμή της Δ3.1 (άνοιγμα χωλ – καθιστι…
ΣΘ-Ζ1	ΟΚ	Ζ1 +2,65 ↔ Ζ3 +2,45	στη γραμμή της δοκού Δ9.1 (περασιά)
ΣΘ-Ζ7	ΟΚ	Ζ7 +2,67 ↔ Ζ8 +2,55	στη γραμμή της δοκού Δ1.1 (κεφαλάρι έρκε…
ΣΘ-Ζ7	ΟΚ	Ζ7 +2,67 ↔ Ζ9 +2,45	μετώπη ντουλάπας Υπν.1 με το στόμιο Π3
ΣΘ-Ζ10	ΟΚ	Ζ10 +2,67 ↔ Ζ11 +2,45	σανίδα κάτω από τη Δ3.1 (εξαίρεση προδ. …
ΣΘ-ΣΥΝ	ΟΚ	Στάθμες στο διαμέρισμα	+2.40 · +2.45 · +2.55 · +2.65 · +2.67 (χαμήλ…

B

ΕΡΓΟ	ΘΕΜΑ ΣΧΕΔΙΟΥ	ΒΑΣΗ	ΑΡ. ΣΧΕΔΙΟΥ
ΠΕΝΤΑΟΡΟΦΟ ΚΤΗΡΙΟ ΚΑΤΟΙΚΙΩΝ – ΑΡΓΥΡΟΥΠΟΛΗ Κωνσταντινουπόλεως 12 & Αγ. Βαρβάρας · Ο.Τ. 103-15 Εργοδότης: INTERKAT Α.Ε. · Κατασκευή: ARKAD Ι.Κ.Ε.	**ΑΝΟΨΗ – ΕΛΕΓΧΟΣ ΠΡΟΔΙΑΓΡΑΦΩΝ** Συμμόρφωση · έλεγχος συγκρούσεων · αλλαγές R12 · ανοικτά σημεία Α΄ · Β΄ · Γ΄ ΟΡΟΦΟΣ – Β1 (τυπικός όροφος)	Βάση: τοιχοποιίες B1 R25 · ξυλότυπος Σ5 (+9,85) · ανόψη R10	**ΑΝ-08** — 07/11/2026 · R12

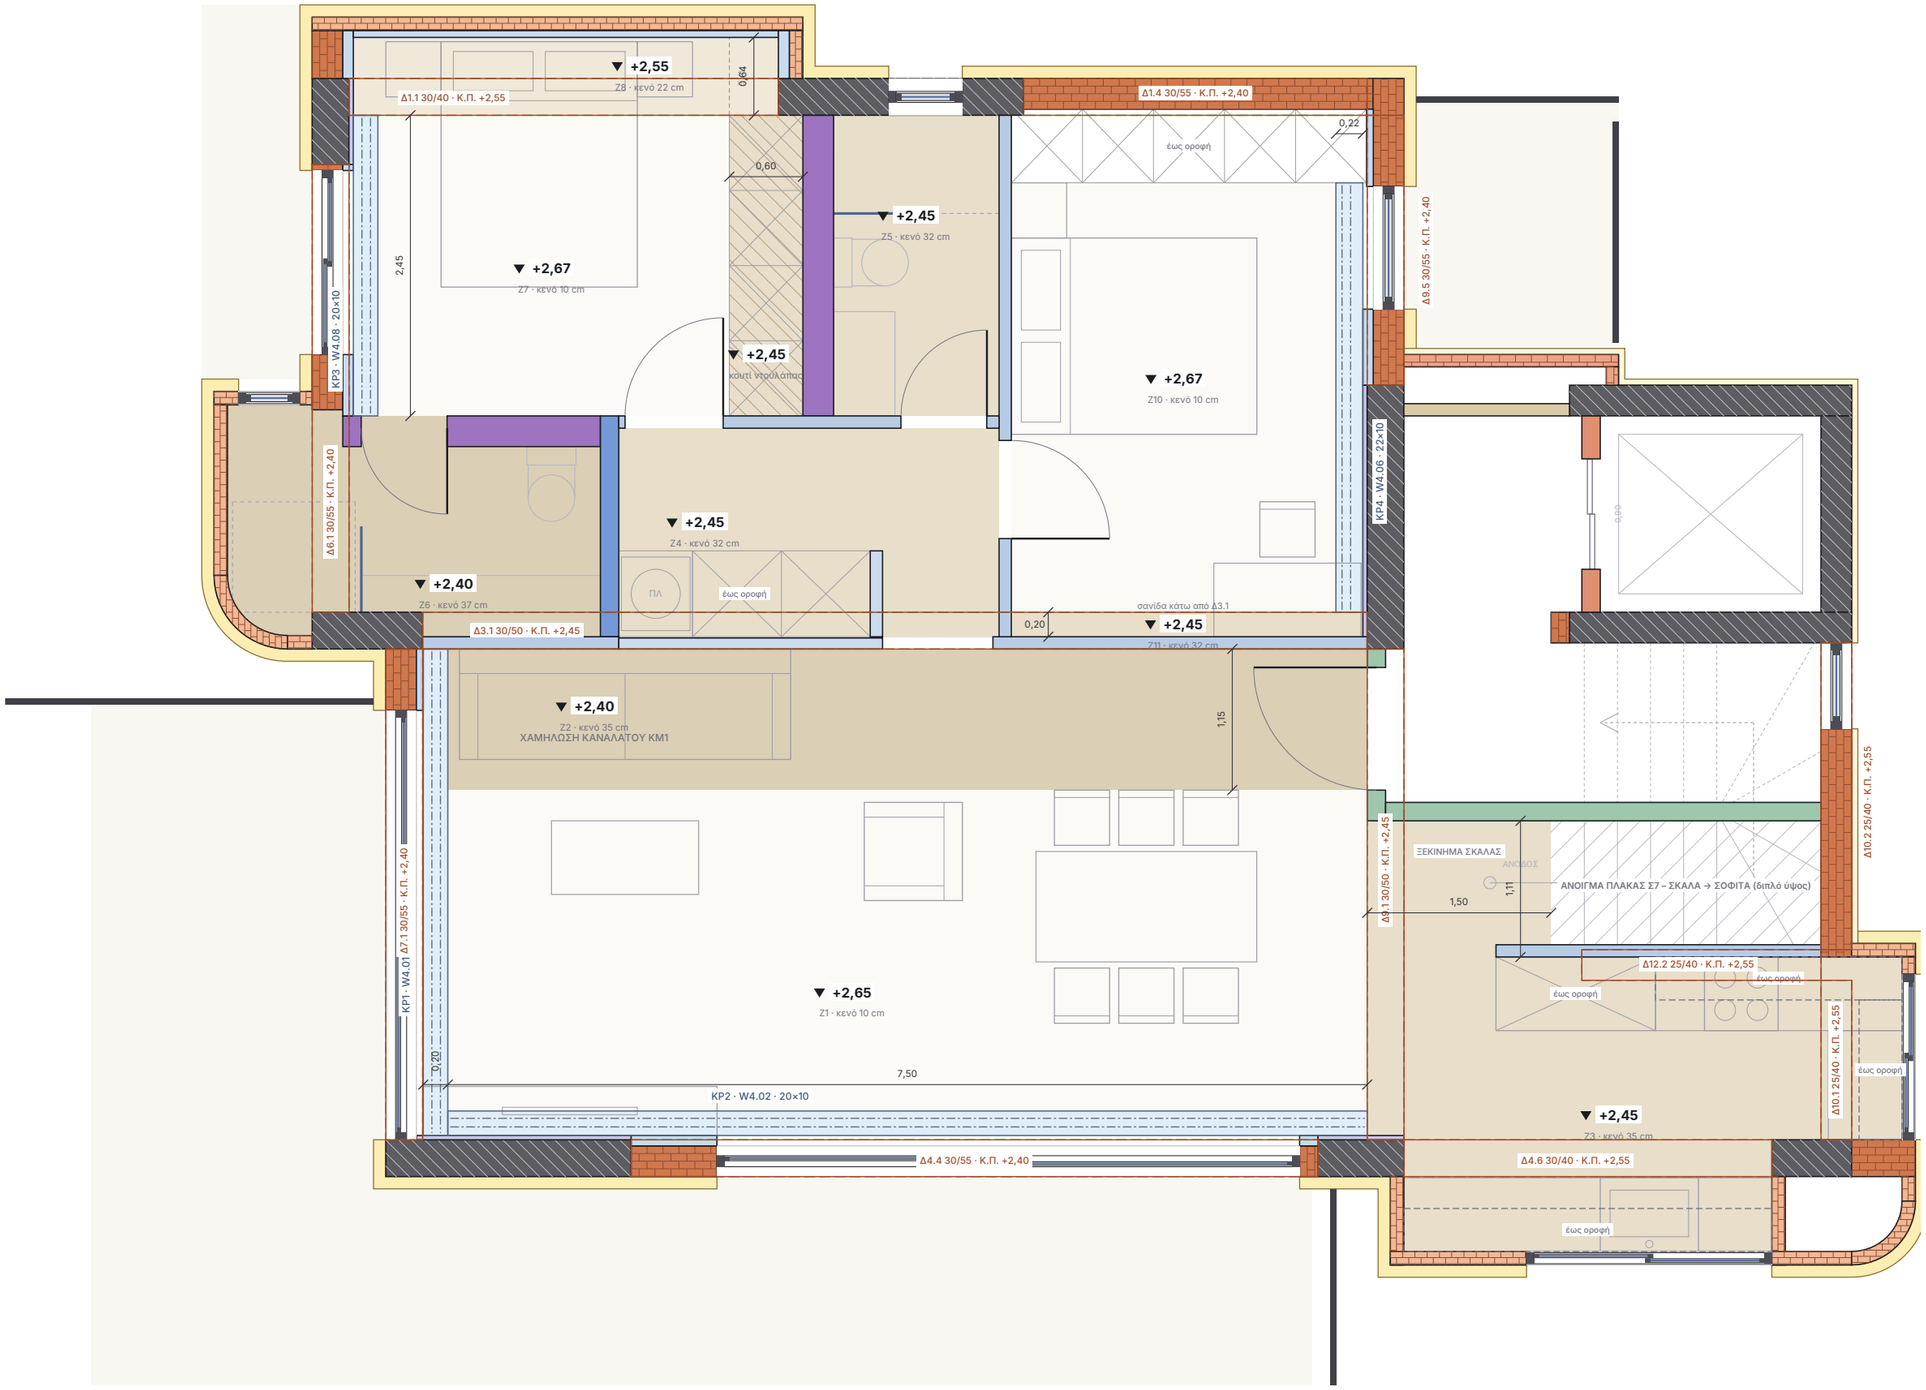

ΣΗΜΕΙΩΣΕΙΣ

Στάθμες από το τελικό δάπεδο του Δ΄ (+13,10). Πάνω παρειά πλάκας Σ7 +2,95 (+16,05)· κάτω παρειά Π3 h18 +2,77 · Π8 h20 +2,75 · Π10 h15 +2,80 (όπως Σ5 – Α4).

Ίδιο διαμέρισμα με το Β1: ίδιες στάθμες R12 (καθιστικό +2,65 · χαμήλωση ΚΜ1 +2,40 · κουζίνα / χωλ / λουτρό +2,45 · λουτρό γονέων +2,40 · υπνοδωμάτια +2,67).

Ξεκίνημα ιδιωτικής σκάλας 9,40–10,90: +2,45 ενιαίο με την κουζίνα, περασιά με τη Δ9.1. Στο 10,90 τελειώνει η ψευδοροφή στο άνοιγμα της πλάκας (γωνιόκρανο) – βλ. Α3.


Κουρτινόθηκες ΚΡ1–ΚΡ4: 20 × 10 cm (ΚΡ4 22), όπως Β1.

Πάνω από το Υπν.2: λουτρό / WC σοφίτας (Α5) · πάνω από καθιστικό / κουζίνα / Υπν.1: δώμα (Α6).

ΥΠΟΜΝΗΜΑ

- +2,65 / +2,67 βασική = 10 cm κάτω από την πλάκα (spot σώμα ≤ 75 mm)
- +2,55 περασιά με δοκό 40 (κεφαλάρι Υπν.1)
- +2,45 περασιά με δοκό 50: χωλ · λουτρό · κουζίνα · ξεκίνημα σκάλας
- +2,40 χαμήλωση ΚΜ1 (5 cm κάτω από Δ3.1 – ψυκτικά) · λουτρό γονέων (περασιά Δ6.1)
- ΚΡ εσοχή κουρτίνας ανοιχτή ως την πλάκα · 2 οδηγοί
- δοκός (Σ7) · Κ.Π. = κάτω παρειά από Τ.Δ.

ΕΡΓΟ	ΘΕΜΑ ΣΧΕΔΙΟΥ	ΒΑΣΗ	ΑΡ. ΣΧΕΔΙΟΥ
ΠΕΝΤΑΟΡΟΦΟ ΚΤΗΡΙΟ ΚΑΤΟΙΚΙΩΝ – ΑΡΓΥΡΟΥΠΟΛΗ Κωνσταντινουπόλεως 12 & Αγ. Βαρβάρας · Ο.Τ. 103-15 Εργοδότης: INTERKAT Α.Ε. · Κατασκευή: ARKAD Ι.Κ.Ε.	**ΑΝΟΨΗ – ΣΤΑΘΜΕΣ · ΔΟΚΟΙ · ΚΟΥΡΤΙΝΕΣ** Στάθμες ψευδοροφής · δοκοί Σ7 · εσοχές κουρτινών · ξεκίνημα σκάλας Δ΄ ΟΡΟΦΟΣ – Δ1 κάτω επίπεδο (μεζονέτα)	Βάση: τοιχοποιίες Δ΄ R04 · ξυλότυπος Σ7_ΕΦ (+16,05) · ανόψη Β1 R12	**ΑΝ-09** **Κλίμακα 1:50 · Α3** 07/11/2026 · R01

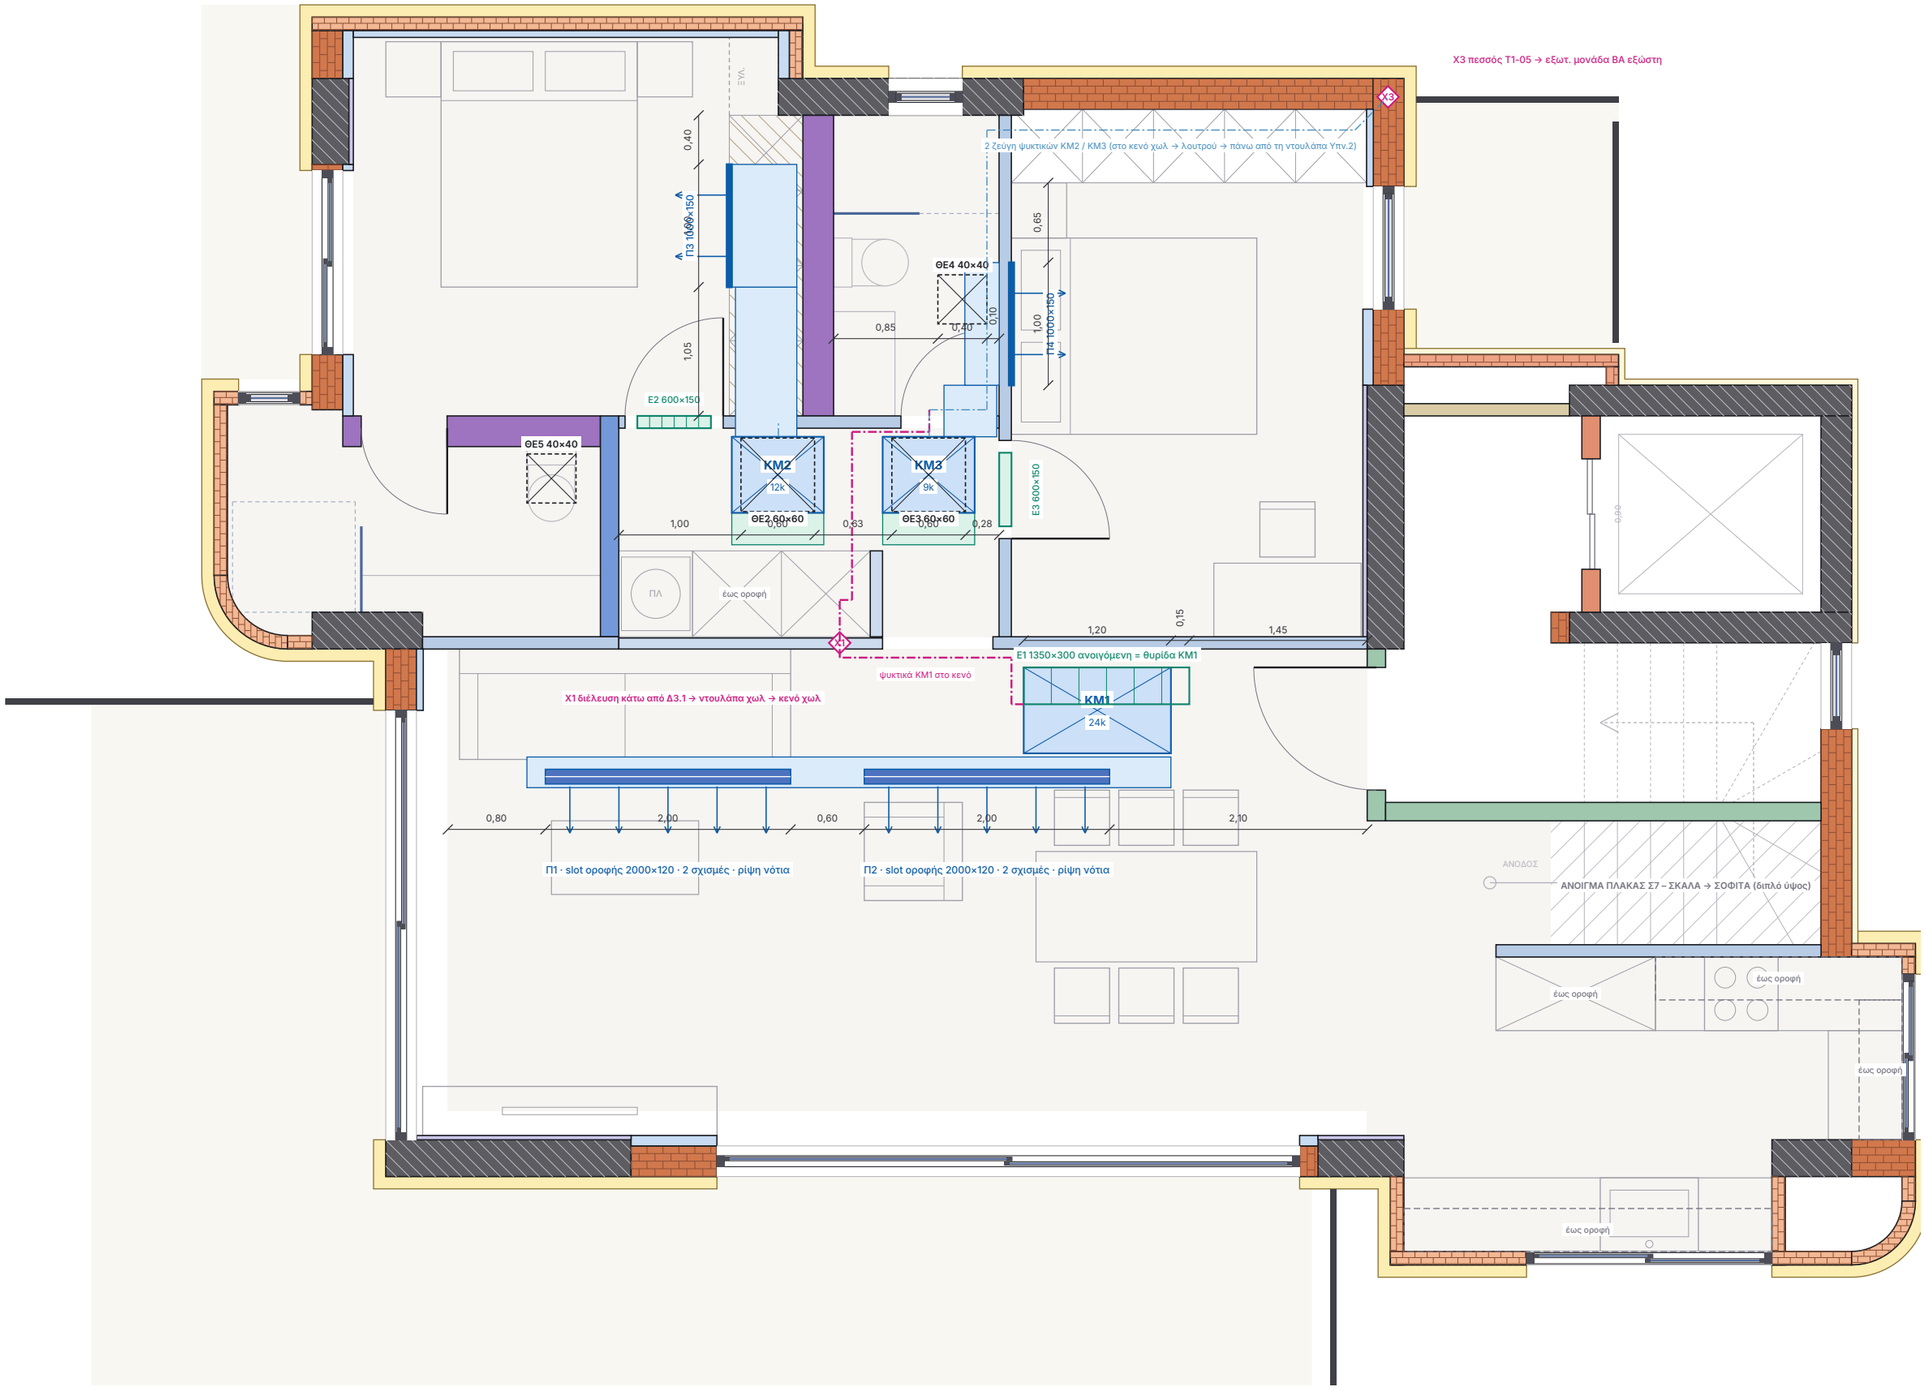

ΣΗΜΕΙΩΣΕΙΣ

Χώρος μονάδων (προδ. 1): χαμήλωση ΚΜ1 +2,40 κάτω από Π8 +2,75 = 35 cm (R12)· χωλ +2,45 κάτω από Π3 +2,77 = 32 cm.

ΚΜ1: μονάδα ≤ 245 mm + στηρίγματα 10 mm + σκελετός/γυψοσανίδα 40 mm = 295 ≤ 350 → περιθώριο 55 mm.

ΚΜ2 / ΚΜ3: 200 + 10 + 40 = 250 ≤ 320 → περιθώριο 70 mm (κλίση συμπυκνωμάτων / αντλία).

Πρόσβαση: ΚΜ1 από την ανοιγόμενη Ε1 · ΚΜ2 / ΚΜ3 από ΘΕ2 / ΘΕ3 60×60 ακριβώς κάτω από τις μονάδες.

Ψυκτικά ΚΜ1 (R12, ιδιοκτήτης: «μέσω οροφής και ντουλάπας χωλ»): συνδέσεις ΚΜ1 δυτικά → βόρεια ακμή της χαμήλωσης → Χ1: κάτω από τη Δ3.1 μέσα από τον Τ2Ν-01 στο επάνω μέρος της ντουλάπας χωλ (x ≈ 5,10) → άνοδος στο κενό του χωλ ανάμεσα στις ΚΜ2 / ΚΜ3 → μαζί με ΚΜ2 / ΚΜ3 → κενό λουτρού → πάνω από τη ντουλάπα Υπν.2 → πεσσός Τ1-05. Καμία οπή σε δοκό.


Χ1 – ΟΡΙΑΚΟ: καθαρό κάτω από τη Δ3.1 = 2,45 − 2,40 − 12,5 = 37,5 mm → σωλήνας αερίου 5/8" με μόνωση 9 mm (Ø ≈ 34) χωράει, με 13 mm όχι. Χωρίς UD στο σημείο, σωλήνες δίπλα-δίπλα· ντουλάπα χωλ με επάνω καπάκι ≤ +2,40 στα νότια 0,25.

Εξωτερική μονάδα στον ΒΑ εξώστη του Δ΄ (όπως Β1)· συμπυκνώματα με αντλία → σιφώνι / υδρορροή εξώστη (επιβεβαίωση υδραυλικού).

ΥΠΟΜΝΗΜΑ

- ΚΜ καναλάτη μονάδα (slim: ΚΜ1 ≤ 245 mm · ΚΜ2/ΚΜ3 ≤ 200 mm)
- αεραγωγός / plenum προσαγωγής (μονωμένος, στο κενό)
- Π1 / Π2 γραμμικό slot οροφής 2 σχισμών, ρυθμιζόμενη ρίψη
- Π3 / Π4 γραμμικό στόμιο 1000×150 σε μετώπη / τοίχο (εγκεκριμένο)
- Ε στόμιο / κιβώτιο επιστροφής με φίλτρο
- ΘΕ θυρίδα επίσκεψης (αφανής, βαφόμενη)
- Χ κατέβασμα / έξοδος σωληνώσεων – καμία οπή σε σκυρόδεμα

ΕΡΓΟ	ΘΕΜΑ ΣΧΕΔΙΟΥ	ΒΑΣΗ	ΑΡ. ΣΧΕΔΙΟΥ
ΠΕΝΤΑΟΡΟΦΟ ΚΤΗΡΙΟ ΚΑΤΟΙΚΙΩΝ – ΑΡΓΥΡΟΥΠΟΛΗ Κωνσταντινουπόλεως 12 & Αγ. Βαρβάρας · Ο.Τ. 103-15 Εργοδότης: INTERKAT Α.Ε. · Κατασκευή: ARKAD Ι.Κ.Ε.	**ΑΝΟΨΗ – ΚΛΙΜΑΤΙΣΜΟΣ · ΘΥΡΙΔΕΣ** Καναλάτες μονάδες · αεραγωγοί · στόμια · θυρίδες επίσκεψης · ψυκτικά Δ΄ ΟΡΟΦΟΣ – Δ1 κάτω επίπεδο (μεζονέτα)	Βάση: τοιχοποιίες Δ΄ R04 · ξυλότυπος Σ7_ΕΦ (+16,05) · ανόψη Β1 R12	**ΑΝ-10** **Κλίμακα 1:50 · Α3** 07/11/2026 · R01

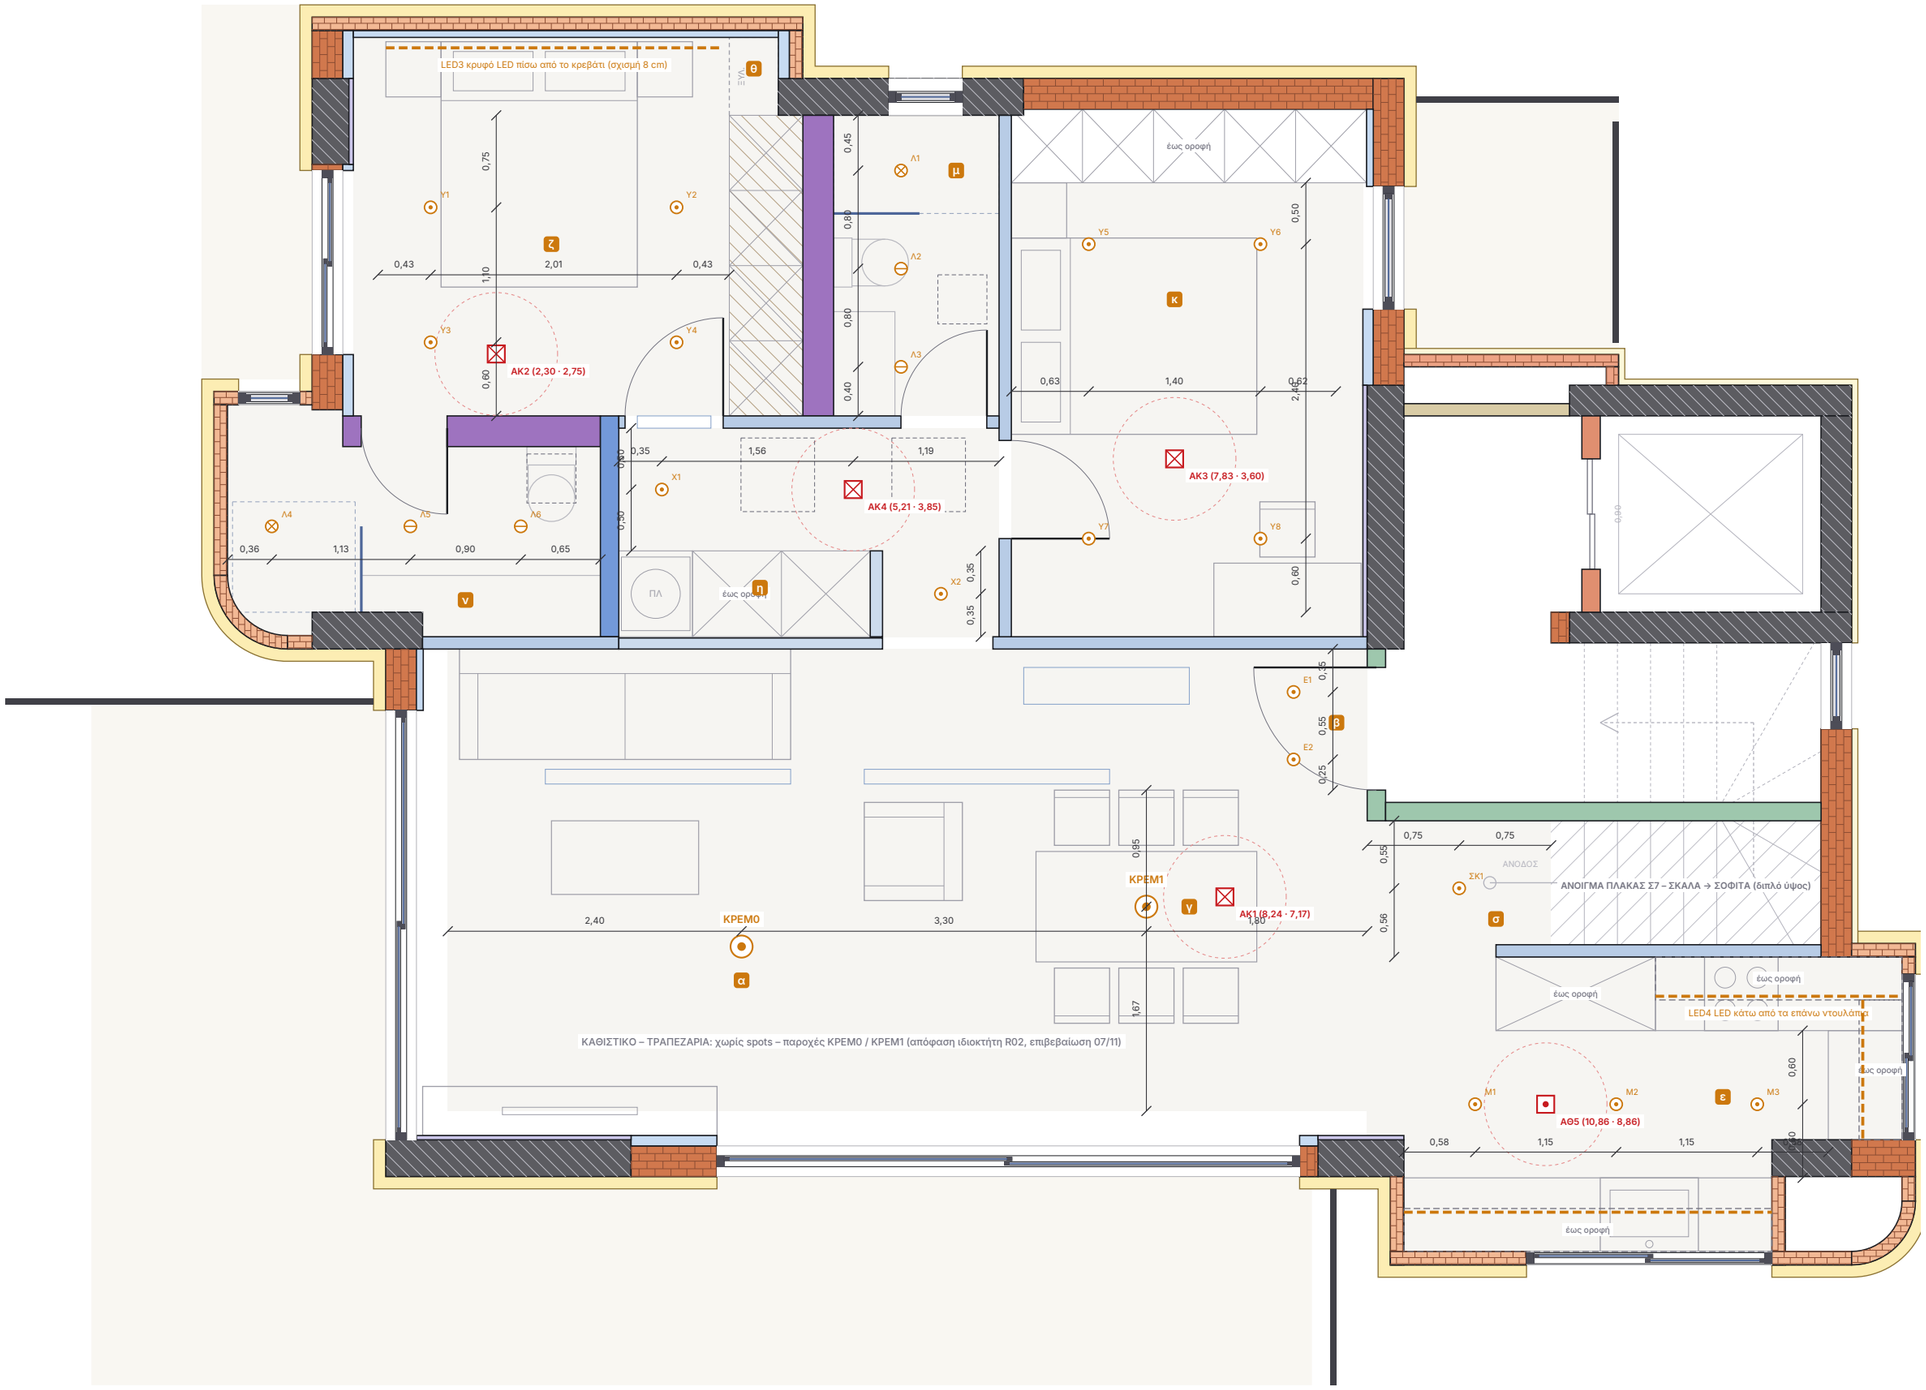

ΣΗΜΕΙΩΣΕΙΣ

Κατανομή όπως Β1 R12: Υπν. 2 × 2 spots · λουτρά 3 (IP65 στο ντους) · κουζίνα 3 γενικός + LED4 κάτω από τα ντουλάπια · χωλ / είσοδος · + ΣΚ1 στο ξεκίνημα της σκάλας. Σύνολο 22 spots + 2 παροχές + LED3 + LED4.

Σκάλα προς σοφίτα: φωτιστικά τοίχου / σκαλοπατιών (ηλεκτρολογικά) – ανιχνευτής καπνού στο πλατύσκαλο της σοφίτας (ανόψη σοφίτας).

Πυρανίχνευση (προδ. 4): σε κάθε κύριο χώρο και στο χωλ· ≥ 0,50 από τοίχους / δοκούς / φωτιστικά, ≥ 1,00 από στόμια προσαγωγής· λουτρά χωρίς ανιχνευτή καπνού.

Οπή spot Ø 75–80 ανάμεσα στα προφίλ CD (όχι πάνω τους)· όπου πέφτει σε προφίλ, μετατόπιση του προφίλ – όχι του spot.

ΥΠΟΜΝΗΜΑ

- χωνευτό spot LED 7–9 W, 2700 K, CRI ≥ 90, UGR < 19, σώμα ≤ 75 mm
- χωνευτό spot IP44 (λουτρά)
- χωνευτό spot IP65 (πάνω από ντους)
- ΚΡΕΜ παροχή οροφής (κουτί + ενίσχυση ανάρτησης)
- ΑΚ ανιχνευτής καπνού (ΕΠ04 · EN 54-7)
- ΑΘ θερμοδιαφορικός ανιχνευτής (κουζίνα · EN 54-5)
- ακτίνα 0,50 m γύρω από ανιχνευτή – κανένας τοίχος / φωτιστικό μέσα
- LED κρυφό γραμμικό 3000 K – LED3 κεφαλάρι · LED4 κάτω από τα ντουλάπια κουζίνας

ΕΡΓΟ	ΘΕΜΑ ΣΧΕΔΙΟΥ	ΒΑΣΗ	ΑΡ. ΣΧΕΔΙΟΥ
ΠΕΝΤΑΟΡΟΦΟ ΚΤΗΡΙΟ ΚΑΤΟΙΚΙΩΝ – ΑΡΓΥΡΟΥΠΟΛΗ Κωνσταντινουπόλεως 12 & Αγ. Βαρβάρας · Ο.Τ. 103-15 Εργοδότης: INTERKAT Α.Ε. · Κατασκευή: ARKAD Ι.Κ.Ε.	**ΑΝΟΨΗ – ΦΩΤΙΣΜΟΣ · ΠΥΡΑΝΙΧΝΕΥΣΗ** Χωνευτά spots · παροχές · κρυφό LED · ανιχνευτές Δ΄ ΟΡΟΦΟΣ – Δ1 κάτω επίπεδο (μεζονέτα)	Βάση: τοιχοποιίες Δ΄ R04 · ξυλότυπος Σ7_ΕΦ (+16,05) · ανόψη Β1 R12	**ΑΝ-11** **Κλίμακα 1:50 · Α3** 07/11/2026 · R01

B

ΣΥΜΜΟΡΦΩΣΗ ΜΕ ΤΙΣ ΠΡΟΔΙΑΓΡΑΦΕΣ (ιδιοκτήτης 07/11/2026)

1 Κλιματισμός Όπως Β1: ΚΜ1 24k καθιστικό / κουζίνα (ΕΓΚΕΚΡ.), ΚΜ2 12k Υπν.1, ΚΜ3 9k Υπν.2 · slot Π1/Π2 · γραμμικά Π3/Π4 (ΕΓΚΕΚΡ.) · χώρος 35 / 32 cm · θυρίδες Ε1 / ΘΕ2 / ΘΕ3 · ψυκτικά ΚΜ1 κάτω από τη Δ3.1 (οριακό 3,6 mm).

2 Κουρτίνες ΚΡ1–ΚΡ4 σε όλα τα ανοίγματα καθιστικού / υπνοδωματίων (W4.01, W4.02, W4.08, W4.06), 20 (22) × 10 cm, ανοιχτές ως την πλάκα.

3 Φωτισμός 22 χωνευτά spots (Β1 + ΣΚ1 σκάλας) + LED κάτω από τα ντουλάπια κουζίνας · καθιστικό με ΚΡΕΜ0/ΚΡΕΜ1 (ΕΓΚΕΚΡ.) · κανένα spot κάτω από μονάδα / αεραγωγό / σε θυρίδα / πάνω από ντουλάπι · κενό ≥ 88 mm.

4 Πυρανίχνευση ΑΚ1–ΑΚ4 καπνού + ΑΘ5 θερμοδιαφορικός κουζίνας · σκάλα: ανιχνευτής στο πλατύσκαλο σοφίτας.

5 Κατασκευή Όπως Β1 · το ξεκίνημα της σκάλας ενιαίο με την κουζίνα +2,45 (περασιά Δ9.1) · ακμή στο άνοιγμα της πλάκας με γωνιόκρανο.

6 Γενική αρχή 5 στάθμες, κάθε αλλαγή πάνω σε γραμμή δοκού ή μετώπη ντουλάπας – όπως Β1.

ΕΓΚΕΚΡΙΜΕΝΕΣ ΑΠΟΚΛΙΣΕΙΣ (ιδιοκτήτης 07/11/2026)

· Καθιστικό – τραπεζαρία χωρίς spots (απόφαση R02· «η νέα προδιαγραφή δεν υπερισχύει»).
· Κουζίνα χωρίς δική της καναλάτη – καλύπτεται από την ΚΜ1 24k.
· Π3 / Π4 υπνοδωματίων: γραμμικά στόμια 1000×150 σε μετώπη / τοίχο, όχι slot.
· Μονάδες slim ≤ 245 mm (ΚΜ1) / ≤ 200 mm (ΚΜ2, ΚΜ3) ως παραδοχή μέχρι την επιλογή μοντέλου.

ΔΙΑΦΟΡΕΣ ΑΠΟ ΤΟ Β1 R12 (Δ΄ R01 · 07/11/2026)

· Πρώτη έκδοση της ανόψης Δ΄ – ίδια με το Β1 R12 (ίδιο διαμέρισμα, ίδιες αποφάσεις ιδιοκτήτη 07/11: χαμήλωση ΚΜ1 +2,40 με τα ψυκτικά κάτω από τη Δ3.1 στη ντουλάπα χωλ · κουζίνα με επάνω ντουλάπια περασιά και LED4 · χωρίς Wi-Fi · καθιστικό χωρίς spots).
· Ξεκίνημα ιδιωτικής σκάλας 9,40–10,90 × 6,55–7,66 στη στάθμη της κουζίνας +2,45 (περασιά με τη Δ9.1 – η γραμμή της δοκού χωρίζει καθιστικό +2,65 και κουζίνα / σκάλα +2,45)· ανατολικά του 10,90 το άνοιγμα της πλάκας Σ7 (χωρίς ψευδοροφή, ακμή με γωνιόκρανο). Spot ΣΚ1 στο κέντρο του πλατύσκαλου.
· Δ12.2 του Σ7 από x 11,15 (στο Β1 από 9,70) – κρυμμένη πάνω από την κουζίνα +2,45.

ΑΝΟΙΚΤΑ ΣΗΜΕΙΑ

· Α1 [ΚΑΤΑΣΚΕΥΗ] Διέλευση ψυκτικών ΚΜ1 κάτω από τη Δ3.1 όπως Β1: καθαρό 37,5 mm → αερίου 5/8″ με μόνωση 9 mm χωράει, με 13 mm όχι (τότε χαμήλωση +2,38).
· Α2 [ΜΟΝΤΕΛΟ] Μοντέλα καναλάτων (≤ 245 / ≤ 200 mm) και θέση ηλεκτρικού κουτιού ΚΜ1 – όπως Β1.
· Α3 [ΣΤΑΤΙΚΟΣ] Δοκός / ακμή πλάκας Σ7 στο x 10,90–11,15 (κάτω από το Δ τοιχείο του κλιμακοστασίου της σοφίτας): η ψευδοροφή +2,45 του ξεκινήματος της σκάλας τελειώνει εκεί – η κάτω παρειά της δοκού πρέπει να είναι ≥ +2,45 (διατομή ≤ 50 cm).
· Α4 [ΣΤΑΤΙΚΟΣ] Δοκοί Σ7_ΕΦ στη ζώνη του διαμερίσματος: θεωρήθηκαν ίδιοι με τον Σ5 (ο έλεγχος της 07/11 έγινε μόνο στη ζώνη της σκάλας) – επιβεβαίωση πριν τη σκυροδέτηση του Σ7· και μέτρηση μετά το ξεκαλούπωμα.
· Α5 [ΑΠΟΦΑΣΗ] Λουτρό / WC σοφίτας πάνω από το Υπν.2 (και τη ντουλάπα του): η ανόψη κρατά το Υπν.2 +2,67 (κενό 10 cm) θεωρώντας ότι τα οριζόντια της αποχέτευσης μπαίνουν στην επίστρωση της σοφίτας (15 cm) και οι στήλες κατεβαίνουν μέσα στη ντουλάπα Υπν.2 (έως οροφή). Αν ο υδραυλικός τις φέρει από κάτω → χαμήλωση Υπν.2 στο +2,45 (κενό 32 cm, περασιά Δ3.1) – να αποφασιστεί στις αποχετεύσεις.
· Α6 [ΣΥΝΤΟΝΙΣΜΟΣ] Δώμα πάνω από καθιστικό / κουζίνα / Υπν.1: οι υδρορροές του δώματος κατεβαίνουν κατακόρυφα στις όψεις / εξώστες – καμία οριζόντια όδευση στο κενό 10 cm του καθιστικού. Κουτιά οροφής και σωληνώσεις ανιχνευτών μέσα στην ψευδοροφή (όχι στη μόνωση δώματος).

ΕΛΕΓΧΟΣ ΣΥΓΚΡΟΥΣΕΩΝ & ΣΤΑΘΜΩΝ – 74 έλεγχοι · ΟΚ 69 · ΟΡΙΑΚΟ 1 · ΕΓΚΕΚΡ. 4 · ΑΠΟΚΛΙΣΗ 0

Αυτόματος έλεγχος από το μοντέλο (code/anopseis/checks.py): στάθμες ↔ δοκοί · κενό μονάδων · θυρίδες · spots ↔ ζώνες / θυρίδες / μονάδες / αεραγωγοί / κουρτινόθηκες · ανιχνευτές ↔ τοίχοι / φωτιστικά / στόμια · κουρτινόθηκες ↔ κουφώματα / δοκοί.

ΚΩΔ.	ΚΑΤΑΣΤ.	ΣΤΟΙΧΕΙΟ	ΜΕΤΡΗΣΗ
ΣΤ01	ΟΚ	Ζ3 ΚΟΥΖΙΝΑ – ΞΕΚΙΝΗΜΑ ΣΚΑΛΑΣ ↔ Δ9.1 30/50 (Κ.Π. +2.45)	οροφή +2.45 · περασιά
ΣΤ02	ΟΚ	Ζ3 ΚΟΥΖΙΝΑ – ΞΕΚΙΝΗΜΑ ΣΚΑΛΑΣ ↔ Δ4.6 30/40 (Κ.Π. +2.55)	οροφή +2.45 · κρυμμένη 10 cm
ΣΤ03	ΟΚ	Ζ3 ΚΟΥΖΙΝΑ – ΞΕΚΙΝΗΜΑ ΣΚΑΛΑΣ ↔ Δ12.2 25/40 (Κ.Π. +2.55)	οροφή +2.45 · κρυμμένη 10 cm
ΣΤ04	ΟΚ	Ζ3 ΚΟΥΖΙΝΑ – ΞΕΚΙΝΗΜΑ ΣΚΑΛΑΣ ↔ Δ10.1 25/40 (Κ.Π. +2.55)	οροφή +2.45 · κρυμμένη 10 cm
ΣΤ05	ΟΚ	Ζ4 ΧΩΛ ↔ Δ3.1 30/50 (Κ.Π. +2.45)	οροφή +2.45 · περασιά
ΣΤ06	ΟΚ	Ζ6 ΛΟΥΤΡΟ ΓΟΝΕΩΝ ↔ Δ6.1 30/55 (Κ.Π. +2.40)	οροφή +2.40 · περασιά
ΣΤ07	ΟΚ	Ζ6 ΛΟΥΤΡΟ ΓΟΝΕΩΝ ↔ Δ3.1 30/50 (Κ.Π. +2.45)	οροφή +2.40 · κρυμμένη 5 cm
ΣΤ08	ΟΚ	Ζ8 ΚΕΦΑΛΑΡΙ ΥΠΝ.1 (έρκερ) ↔ Δ1.1 30/40 (Κ.Π. +2.55)	οροφή +2.55 · περασιά
ΣΤ09	ΟΚ	Ζ11 ΣΑΝΙΔΑ ΚΑΤΩ ΑΠΟ Δ3.1 (Υπν.2) ↔ Δ3.1 30/50 (Κ.Π. +2.45)	οροφή +2.45 · περασιά
ΚΛ-ΚΜ1	ΟΚ	ΚΜ1 24.000 Btu/h – καθιστικό – τραπεζαρία – κουζίνα	κενό 350 mm · περιθώριο +55 mm
ΘΕ-ΚΜ1	ΟΚ	ΚΜ1 – πρόσβαση συντήρησης	Ε1
ΚΛ-ΚΜ2	ΟΚ	ΚΜ2 12.000 Btu/h – Υπνοδωμάτιο 1	κενό 320 mm · περιθώριο +70 mm
ΘΕ-ΚΜ2	ΟΚ	ΚΜ2 – πρόσβαση συντήρησης	ΘΕ2
ΚΛ-ΚΜ3	ΟΚ	ΚΜ3 9.000 Btu/h – Υπνοδωμάτιο 2	κενό 320 mm · περιθώριο +70 mm
ΘΕ-ΚΜ3	ΟΚ	ΚΜ3 – πρόσβαση συντήρησης	ΘΕ3
ΨΥ-ΚΜ1	ΟΚ	Όδευση ψυκτικών ΚΜ1 χαμήλωση → ντουλάπα χωλ → κενό χωλ…	ελάχιστο 280 mm
ΨΥ-ΔΟΚ	ΟΡΙΑΚΟ	Διέλευση ψυκτικών ΚΜ1 κάτω από τη Δ3.1 (x ≈ 5.10, Τ2Ν-01 → ντο…	καθαρό 37.5 mm · περιθώριο +3.6 mm
ΚΔ-ΚΜ1	ΟΚ	Καθιστικό – τραπεζαρία	ΚΜ1
ΚΔ-ΚΜ2	ΟΚ	Υπνοδωμάτιο 1	ΚΜ2
ΚΔ-ΚΜ3	ΟΚ	Υπνοδωμάτιο 2	ΚΜ3
ΚΔ-ΚΟΥΖ	ΕΓΚΕΚΡ.	Κουζίνα	από την ΚΜ1 (ανοιχτή στο καθιστικό)
ΣΤ-Π1	ΟΚ	Π1 slot οροφής 2000×120 · 2 σχισμές	μέσα
ΣΤ-Π2	ΟΚ	Π2 slot οροφής 2000×120 · 2 σχισμές	μέσα
ΣΤ-Π3	ΕΓΚΕΚΡ.	Π3 γραμμικό 1000×150 · μετώπη ντουλάπας +2,48…+2,63	γραμμικό στόμιο μετώπης / τοίχου
ΣΤ-Π4	ΕΓΚΕΚΡ.	Π4 γραμμικό 1000×150 · τοίχος +2,48…+2,63	γραμμικό στόμιο μετώπης / τοίχου
SP-Υ1	ΟΚ	Υ1 spot (1.765 · 1.550) – ΥΠΝΟΔΩΜΑΤΙΟ 1	κενό 88 mm · άκρη 0.63
SP-Υ2	ΟΚ	Υ2 spot (3.770 · 1.550) – ΥΠΝΟΔΩΜΑΤΙΟ 1	κενό 88 mm · άκρη 0.43
SP-Υ3	ΟΚ	Υ3 spot (1.765 · 2.650) – ΥΠΝΟΔΩΜΑΤΙΟ 1	κενό 88 mm · άκρη 0.60
SP-Υ4	ΟΚ	Υ4 spot (3.770 · 2.650) – ΥΠΝΟΔΩΜΑΤΙΟ 1	κενό 88 mm · άκρη 0.43
SP-Υ5	ΟΚ	Υ5 spot (7.130 · 1.850) – ΥΠΝΟΔΩΜΑΤΙΟ 2	κενό 88 mm · άκρη 0.50
SP-Υ6	ΟΚ	Υ6 spot (8.530 · 1.850) – ΥΠΝΟΔΩΜΑΤΙΟ 2	κενό 88 mm · άκρη 0.50
SP-Υ7	ΟΚ	Υ7 spot (7.130 · 4.250) – ΥΠΝΟΔΩΜΑΤΙΟ 2	κενό 88 mm · άκρη 0.60
SP-Υ8	ΟΚ	Υ8 spot (8.530 · 4.250) – ΥΠΝΟΔΩΜΑΤΙΟ 2	κενό 88 mm · άκρη 0.60
SP-Λ1	ΟΚ	Λ1 spot IP65 (5.600 · 1.250) – ΛΟΥΤΡΟ	κενό 307 mm · άκρη 0.45
SP-Λ2	ΟΚ	Λ2 spot IP44 (5.600 · 2.050) – ΛΟΥΤΡΟ	κενό 307 mm · άκρη 0.55
SP-Λ3	ΟΚ	Λ3 spot IP44 (5.600 · 2.850) – ΛΟΥΤΡΟ	κενό 307 mm · άκρη 0.40
SP-Λ4	ΟΚ	Λ4 spot IP65 (0.470 · 4.150) – ΛΟΥΤΡΟ ΓΟΝΕΩΝ	κενό 358 mm · άκρη 0.36
SP-Λ5	ΟΚ	Λ5 spot IP44 (1.600 · 4.150) – ΛΟΥΤΡΟ ΓΟΝΕΩΝ	κενό 358 mm · άκρη 0.70
SP-Λ6	ΟΚ	Λ6 spot IP44 (2.500 · 4.150) – ΛΟΥΤΡΟ ΓΟΝΕΩΝ	κενό 358 mm · άκρη 0.65
SP-Χ1	ΟΚ	Χ1 spot (3.650 · 3.850) – ΧΩΛ	κενό 307 mm · άκρη 0.35
SP-Χ2	ΟΚ	Χ2 spot (5.925 · 4.700) – ΧΩΛ	κενό 307 mm · άκρη 0.35
SP-Ε1	ΟΚ	Ε1 spot (8.800 · 5.500) – ΧΑΜΗΛΩΣΗ ΚΑΝΑΛΑΤΟΥ / ΕΙΣΟΔΟΣ	κενό 338 mm · άκρη 0.35
SP-Ε2	ΟΚ	Ε2 spot (8.800 · 6.050) – ΧΑΜΗΛΩΣΗ ΚΑΝΑΛΑΤΟΥ / ΕΙΣΟΔΟΣ	κενό 338 mm · άκρη 0.25
SP-Μ1	ΟΚ	Μ1 spot (10.280 · 8.860) – ΚΟΥΖΙΝΑ – ΞΕΚΙΝΗΜΑ ΣΚΑΛΑΣ	κενό 337 mm · άκρη 0.63
SP-Μ2	ΟΚ	Μ2 spot (11.430 · 8.860) – ΚΟΥΖΙΝΑ – ΞΕΚΙΝΗΜΑ ΣΚΑΛΑΣ	κενό 337 mm · άκρη 1.20
SP-Μ3	ΟΚ	Μ3 spot (12.580 · 8.860) – ΚΟΥΖΙΝΑ – ΞΕΚΙΝΗΜΑ ΣΚΑΛΑΣ	κενό 337 mm · άκρη 0.31
SP-ΣΚ1	ΟΚ	ΣΚ1 spot (10.150 · 7.100) – ΚΟΥΖΙΝΑ – ΞΕΚΙΝΗΜΑ ΣΚΑΛΑΣ	κενό 337 mm · άκρη 0.55
SP-ΚΑΘ	ΕΓΚΕΚΡ.	Καθιστικό – τραπεζαρία	παροχές ΚΡΕΜ0 / ΚΡΕΜ1 (απόφαση R02)
ΠΥ-ΑΚ1	ΟΚ	ΑΚ1 καπνού (8.24 · 7.17) – καθιστικό – τραπεζαρία (R05: 0,55 από…	τοίχος 0.87 · ΚΡΕΜ1 0.64 · Π2 1.32
ΠΥ-ΑΚ2	ΟΚ	ΑΚ2 καπνού (2.30 · 2.75) – Υπνοδωμάτιο 1	τοίχος 0.50 · Υ3 0.54 · Π3 1.96
ΠΥ-ΑΚ3	ΟΚ	ΑΚ3 καπνού (7.83 · 3.60) – Υπνοδωμάτιο 2	τοίχος 1.25 · Υ8 0.96 · Π4 1.44
ΠΥ-ΑΚ4	ΟΚ	ΑΚ4 καπνού (5.21 · 3.85) – χωλ – άξονας διαδρόμου 1,00, ανάμεσ…	τοίχος 0.50 · Λ3 1.07 · Π4 1.53
ΠΥ-ΑΘ5	ΟΚ	ΑΘ5 θερμοδιαφορικός (10.86 · 8.86) – κουζίνα – θερμοδιαφορικό…	τοίχος 0.60 · Μ2 0.57 · Π2 4.41
ΠΥ-ΧΩΡ	ΟΚ	Κάλυψη χώρων	καθιστικό · Υπν.1 · Υπν.2 · χωλ · κουζίνα (θε…
ΘΕ-ΘΕ2	ΟΚ	ΘΕ2 60×60 – ΚΜ2 (φίλτρο, ηλεκτρικό κουτί, αντλία)	ελεύθερη
ΘΕ-ΘΕ3	ΟΚ	ΘΕ3 60×60 – ΚΜ3 (φίλτρο, ηλεκτρικό κουτί, αντλία)	ελεύθερη
ΘΕ-ΘΕ4	ΟΚ	ΘΕ4 40×40 – λουτρό: plenum / ρύθμιση Π4 · έξω από το ντους (R1…	ελεύθερη
ΘΕ-ΘΕ5	ΟΚ	ΘΕ5 40×40 – λουτρό γονέων: επίσκεψη κενού (από πάνω δώμα – …	ελεύθερη
ΚΡ-ΚΡ1	ΟΚ	ΚΡ1 W4.01 – καθιστικό – Δ · 20 × 10 cm · οδηγοί 7 / 14 cm	πλήρης · βάθος 10 cm
ΚΡ-ΚΡ2	ΟΚ	ΚΡ2 W4.02 – καθιστικό – Ν · 20 × 10 cm · οδηγοί 7 / 14 cm	πλήρης · βάθος 10 cm
ΚΡ-ΚΡ3	ΟΚ	ΚΡ3 W4.08 – Υπν.1 – Δ · 20 × 10 cm · οδηγοί 7 / 14 cm	πλήρης · βάθος 10 cm
ΚΡ-ΚΡ4	ΟΚ	ΚΡ4 W4.06 – Υπν.2 – Α · 22 × 10 cm · οδηγοί 10 / 17 cm (ανοιγοα…	πλήρης · βάθος 10 cm
ΚΡ-W4.03	ΟΚ	W4.03	δεν απαιτείται – κουζίνα – πάνω από τον ν…
ΚΡ-W4.04	ΟΚ	W4.04	δεν απαιτείται – κουζίνα – έρκερ, πάνω από…
ΚΡ-W4.05	ΟΚ	W4.05	δεν απαιτείται – κλιμακοστάσιο (εκτός διαμ…
ΚΡ-W4.07	ΟΚ	W4.07	δεν απαιτείται – λουτρό (στο τοιχείο Κ2)
ΚΡ-W4.09	ΟΚ	W4.09	δεν απαιτείται – λουτρό γονέων (ντους)
ΣΘ-Ζ1	ΟΚ	Ζ1 +2,65 ↔ Ζ2 +2,40	χαμήλωση καναλάτου ΚΜ1 (προδ. 1/5)
ΣΘ-Ζ4	ΟΚ	Ζ4 +2,45 ↔ Ζ2 +2,40	στη γραμμή της Δ3.1 (άνοιγμα χωλ – καθιστι…
ΣΘ-Ζ1	ΟΚ	Ζ1 +2,65 ↔ Ζ3 +2,45	στη γραμμή της δοκού Δ9.1 (περασιά) – καθ…
ΣΘ-Ζ7	ΟΚ	Ζ7 +2,67 ↔ Ζ8 +2,55	στη γραμμή της δοκού Δ1.1 (κεφαλάρι έρκε…
ΣΘ-Ζ7	ΟΚ	Ζ7 +2,67 ↔ Ζ9 +2,45	μετώπη ντουλάπας Υπν.1 με το στόμιο Π3
ΣΘ-Ζ10	ΟΚ	Ζ10 +2,67 ↔ Ζ11 +2,45	σανίδα κάτω από τη Δ3.1 (εξαίρεση προδ. …
ΣΘ-ΣΥΝ	ΟΚ	Στάθμες στο διαμέρισμα	+2.40 · +2.45 · +2.55 · +2.65 · +2.67 (χαμήλ…


ΕΡΓΟ
ΠΕΝΤΑΟΡΟΦΟ ΚΤΗΡΙΟ ΚΑΤΟΙΚΙΩΝ – ΑΡΓΥΡΟΥΠΟΛΗ
Κωνσταντινουπόλεως 12 & Αγ. Βαρβάρας · Ο.Τ. 103-15
Εργοδότης: INTERKAT Α.Ε. · Κατασκευή: ARKAD Ι.Κ.Ε.

ΘΕΜΑ ΣΧΕΔΙΟΥ
ΑΝΟΨΗ – ΕΛΕΓΧΟΣ ΠΡΟΔΙΑΓΡΑΦΩΝ
Συμμόρφωση · έλεγχος συγκρούσεων · αλλαγές R01 · ανοικτά σημεία
Δ΄ ΟΡΟΦΟΣ – Δ1 κάτω επίπεδο (μεζονέτα)

ΒΑΣΗ
Βάση: τοιχοποιίες Δ΄ R04 · ξυλότυπος Σ7_ΕΦ (+16,05) · ανόψη Β1 R12

ΑΡ. ΣΧΕΔΙΟΥ
ΑΝ-12
—
07/11/2026 · R01

B

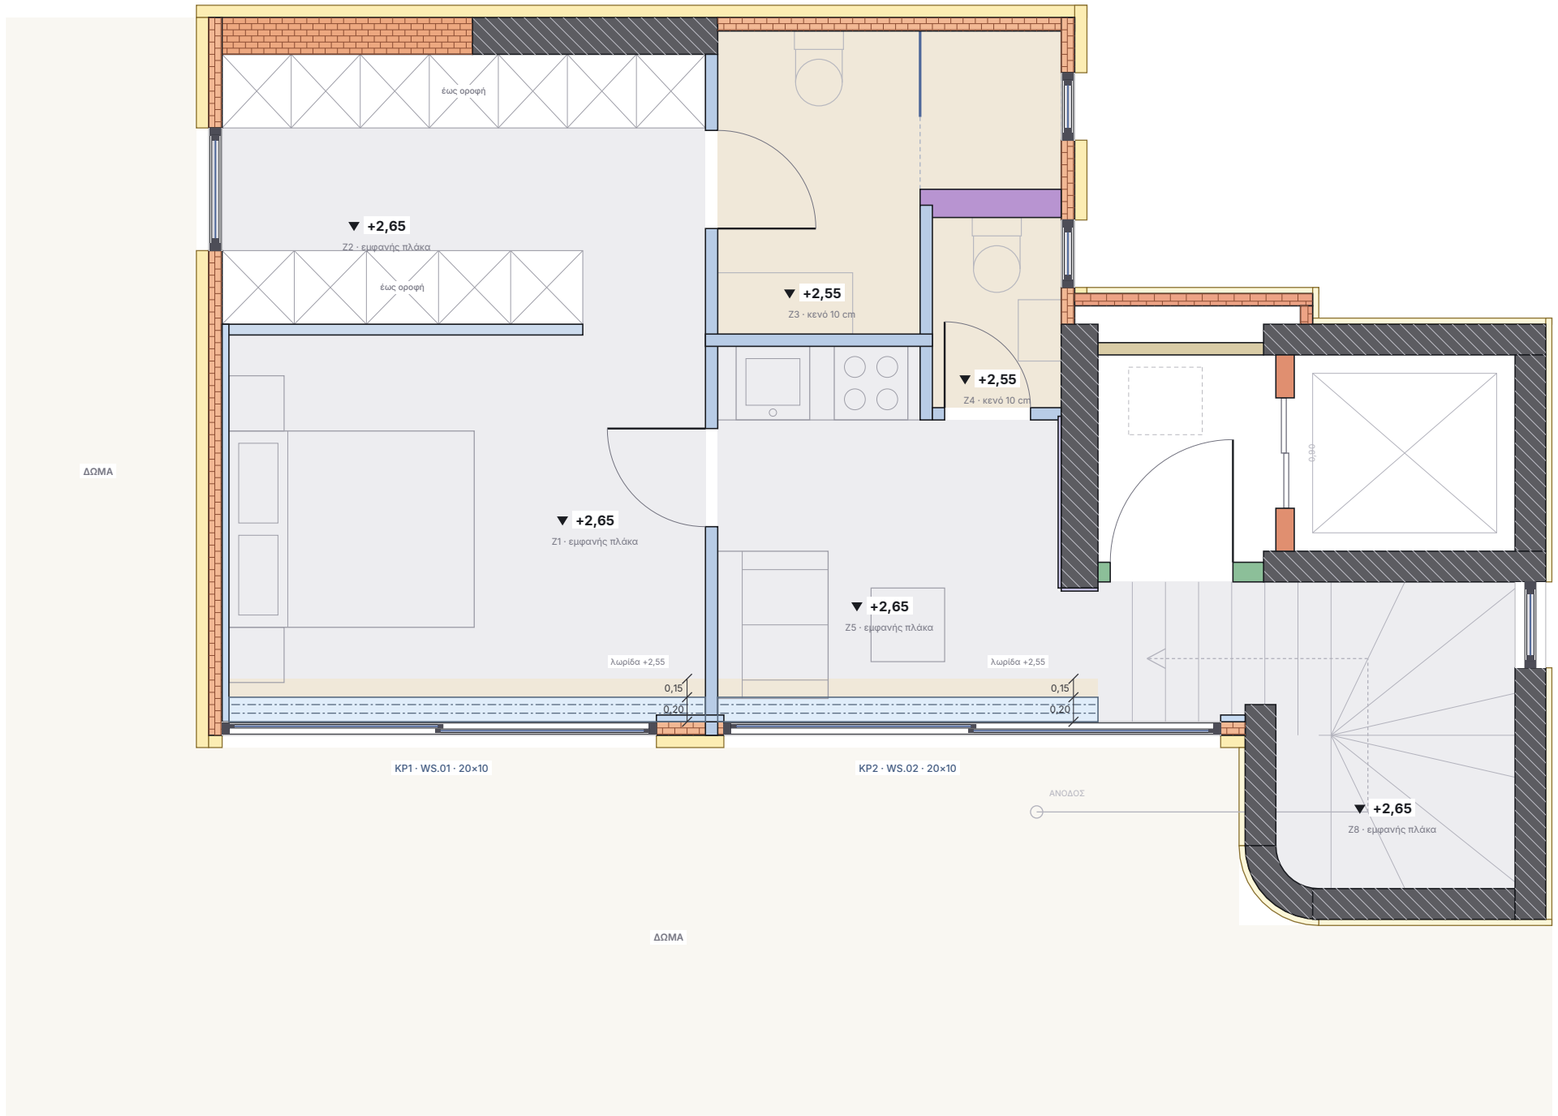

ΣΗΜΕΙΩΣΕΙΣ

Ιδιοκτήτης 07/11: «η στέγη έχει κλείσει – μην την κατεβάσεις γενικά, μόνο όπου ωραίο ή αναγκαίο». Η οροφή είναι η κάτω παρειά της πλάκας στέγης Σ8 (όλες οι δοκοί ανεστραμμένες → επίπεδη, κανένα δοκάρι μέσα): σπατουλαριστή / βαμμένη, +2,65 από το Τ.Δ. +16,20 (§1Β – Α1).

Καταβιβάσεις ΜΟΝΟ: (α) λωρίδα κουρτίνας 15 cm (+2,55, μετώπη 10) + εσοχή 20 × 10 ανοιχτή ως την πλάκα, κατά μήκος WS.01 / WS.02 – αναγκαίο για την προδιαγραφή 2 · (β) λουτρό / WC +2,55 ανθυγρή – χωνευτά IP65 / IP44 και κρυμμένα καλώδια (κλειστοί χώροι, χωρίς σπάσιμο).


Βεστιάριο / υπνοδωμάτιο / καθιστικό / σκάλα: χωρίς ψευδοροφή. Το κλιματιστικό είναι κρυφό στη ντουλάπα – καμία καταβίβαση γι' αυτό.

Σκάλα: εμφανής πλάκα πάνω από την ιδιωτική σκάλα (διπλό ύψος από τον Δ΄).

ΥΠΟΜΝΗΜΑ

- εμφανής πλάκα Σ8 +2,65 – χωρίς ψευδοροφή (κουτιά spot / ανιχνευτών στο σκυρόδεμα)
- +2,55 ψευδοροφή 10 cm: λουτρό / WC (ανθυγρή) · λωρίδες κουρτίνας
- ΚΡ εσοχή κουρτίνας 20 × 10 ανοιχτή ως την πλάκα · 2 οδηγοί

ΕΡΓΟ	ΘΕΜΑ ΣΧΕΔΙΟΥ	ΒΑΣΗ	ΑΡ. ΣΧΕΔΙΟΥ
ΠΕΝΤΑΟΡΟΦΟ ΚΤΗΡΙΟ ΚΑΤΟΙΚΙΩΝ – ΑΡΓΥΡΟΥΠΟΛΗ Κωνσταντινουπόλεως 12 & Αγ. Βαρβάρας · Ο.Τ. 103-15 Εργοδότης: INTERKAT Α.Ε. · Κατασκευή: ARKAD Ι.Κ.Ε.	**ΑΝΟΨΗ – ΣΤΑΘΜΕΣ · ΔΟΚΟΙ · ΚΟΥΡΤΙΝΕΣ** Εμφανής πλάκα Σ8 · τοπικές καταβιβάσεις · κουρτινόθηκες ΣΟΦΙΤΑ – Δ1 πάνω επίπεδο (μεζονέτα)	Βάση: τοιχοποιίες σοφίτας R04 · Σ8 (ανεστρ. δοκοί) · ύψος 2,65	**ΑΝ-13** **Κλίμακα 1:50 · Α3** 07/11/2026 · R01

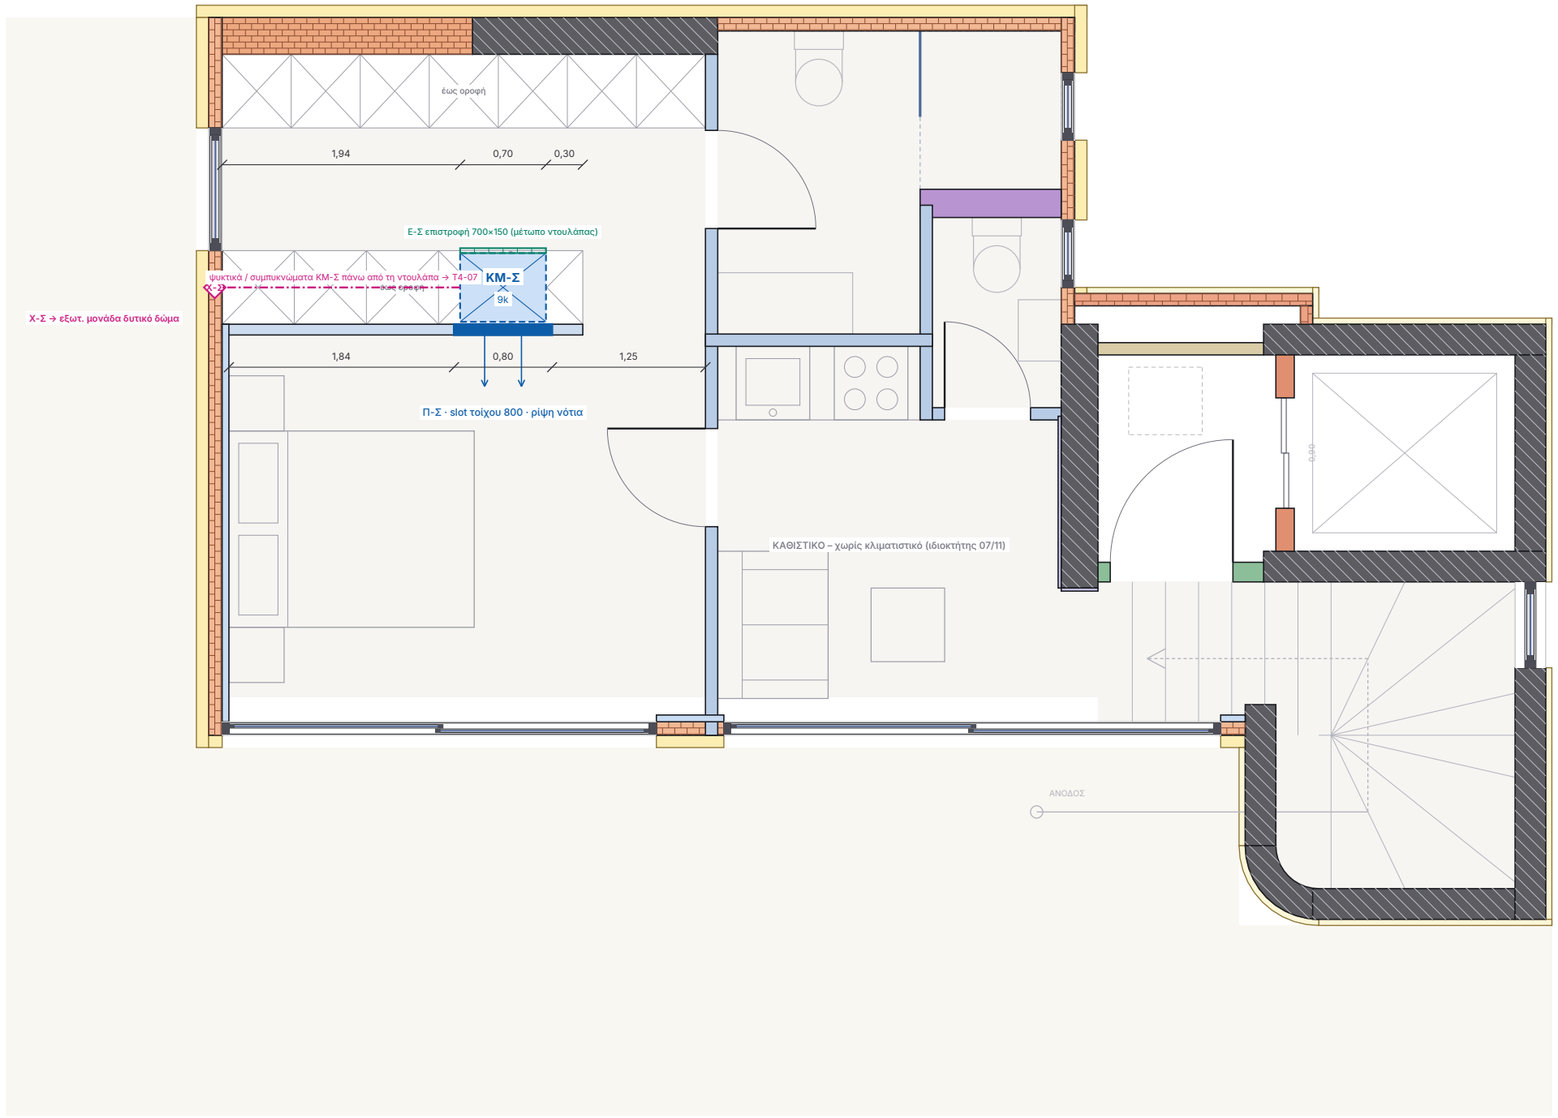

ΣΗΜΕΙΩΣΕΙΣ

Ιδιοκτήτης 07/11: «στη σοφίτα μόνο ένα κλιματιστικό στο δωμάτιο, μπορεί να είναι και κρυφό τοίχου».

ΚΜ-Σ 9.000 Btu/h slim καναλάτη (ύψος ≤ 200 · βάθος ≤ 550) οριζόντια πάνω από τη νότια ντουλάπα του βεστιαρίου στο 4,50–5,20: καπάκι ντουλάπας +2,30, μονάδα +2,31…+2,51, πλάκα +2,65 → περιθώριο 120 mm.

Προσαγωγή Π-Σ: γραμμικό slot 2 σχισμών 800 στον τοίχο Τ2Ν-01 (+2,40…+2,52), ρίψη νότια κατά μήκος της οροφής – όχι πάνω στο προσκέφαλο (κρεβάτι κεφαλάρι δυτικά).

Επιστροφή Ε-Σ: γρίλια με φίλτρο στο επάνω μέρος του μετώπου της ντουλάπας (βεστιάριο, ανοιχτό στο υπνοδωμάτιο από το πέρασμα 1,00). Συντήρηση από τα επάνω πορτάκια της ντουλάπας – καμία θυρίδα οροφής.

Ψυκτικά + συμπυκνώματα πάνω από τη ντουλάπα δυτικά (≈ 2 m) → Χ-Σ: μέσα από τον Τ4-07 ψηλά (+2,45) → εξωτερική μονάδα στο δυτικό δώμα · συμπυκνώματα με φυσική ροή → σιφώνι δώματος.

Καθιστικό – kitchenette: χωρίς κλιματιστικό (απόφαση ιδιοκτήτη).

ΥΠΟΜΝΗΜΑ

- ΚΜ-Σ κρυφή καναλάτη slim στη ντουλάπα (διακεκομμένο: μέσα σε έπιπλο)
- αεραγωγός / plenum προσαγωγής (μονωμένος, στο κενό)
- γραμμικό slot οροφής
- Π-Σ γραμμικό slot 2 σχισμών στον τοίχο Τ2Ν-01 (κρυφή μονάδα τοίχου)
- Ε στόμιο / κιβώτιο επιστροφής με φίλτρο
- ΘΕ θυρίδα επίσκεψης (αφανής, βαφόμενη)
- Χ κατέβασμα / έξοδος σωληνώσεων – καμία οπή σε σκυρόδεμα

ΕΡΓΟ

ΠΕΝΤΑΟΡΟΦΟ ΚΤΗΡΙΟ ΚΑΤΟΙΚΙΩΝ – ΑΡΓΥΡΟΥΠΟΛΗ
Κωνσταντινουπόλεως 12 & Αγ. Βαρβάρας · Ο.Τ. 103-15
Εργοδότης: INTERKAT Α.Ε. · Κατασκευή: ARKAD Ι.Κ.Ε.

ΘΕΜΑ ΣΧΕΔΙΟΥ


ΑΝΟΨΗ – ΚΛΙΜΑΤΙΣΜΟΣ · ΘΥΡΙΔΕΣ
Ένα κλιματιστικό – κρυφή μονάδα στη ντουλάπα βεστιαρίου · ψυκτικά ΣΟΦΙΤΑ – Δ1 πάνω επίπεδο (μεζονέτα)

ΒΑΣΗ

Βάση: τοιχοποιίες σοφίτας R04 · Σ8 (ανεστρ. δοκοί) · ύψος 2,65

ΑΡ. ΣΧΕΔΙΟΥ

ΑΝ-14
Κλίμακα 1:50 · Α3
07/11/2026 · R01

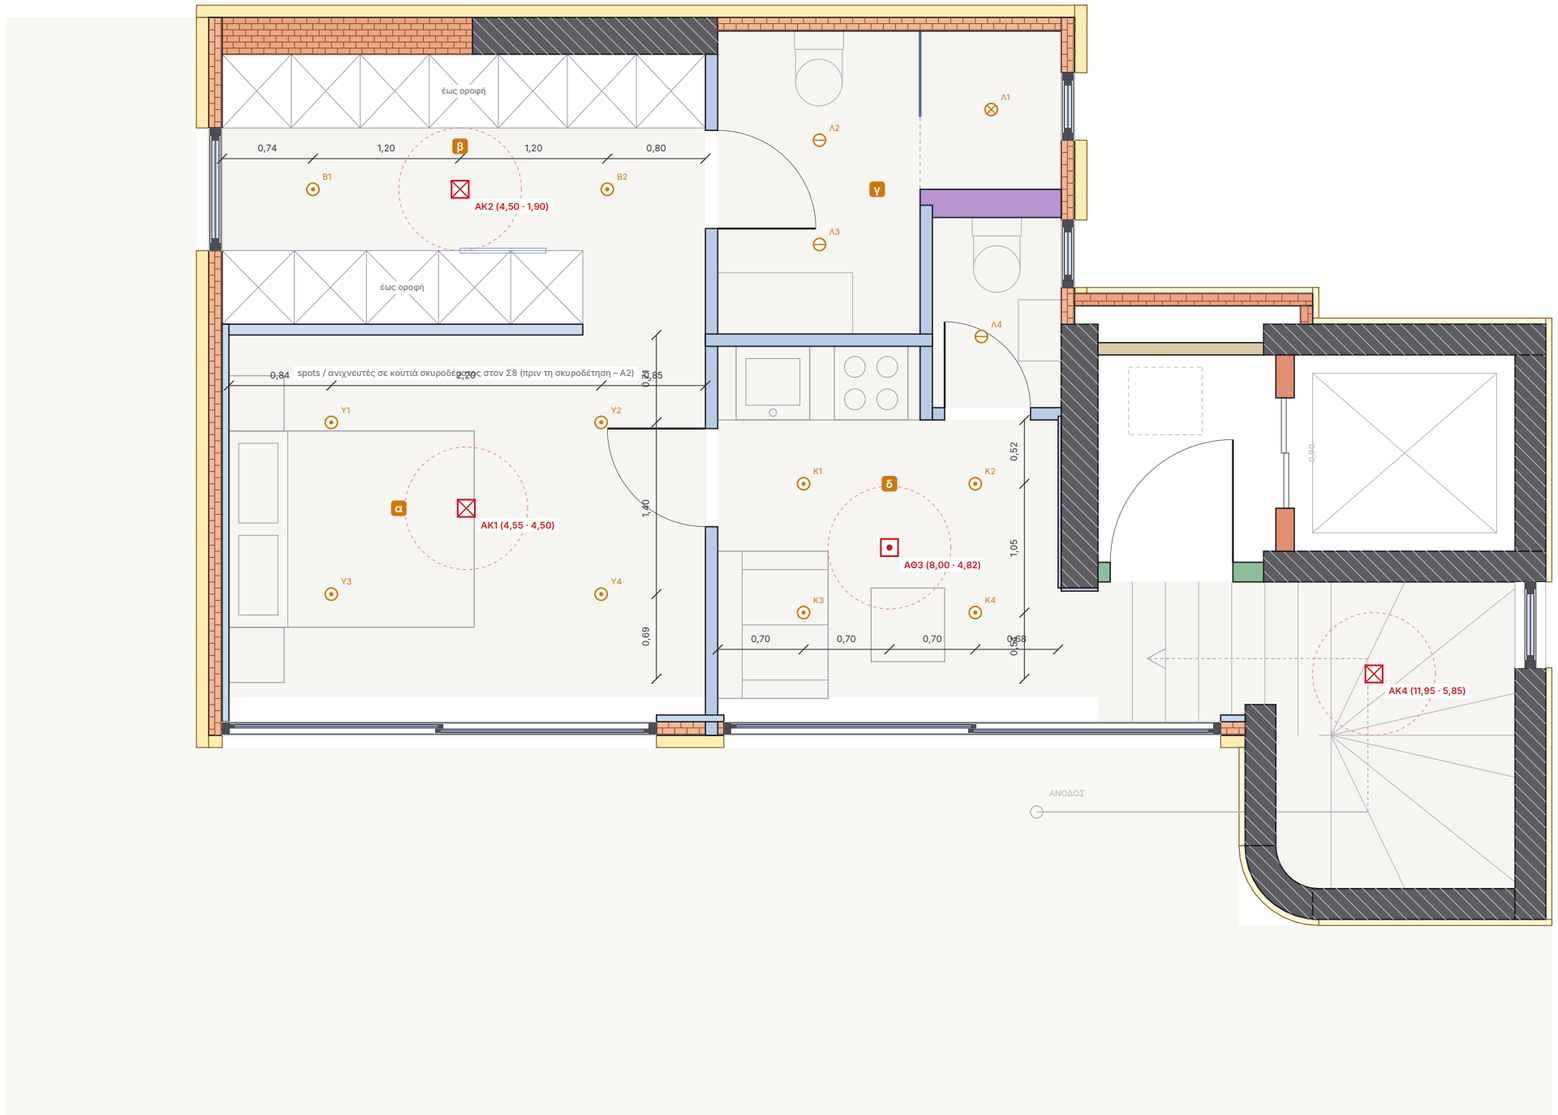

B

ΣΗΜΕΙΩΣΕΙΣ

Spots στην εμφανή πλάκα: κουτί χωνευτού φωτιστικού για σκυρόδεμα (Ø 80, βάθος ≤ 100) + σωλήνας, δεμένα στον ξυλότυπο Σ8 πριν τη σκυροδέτηση· το ίδιο για τα κουτιά των ανιχνευτών. Σπατουλάρισμα / βαφή μετά.

Κατανομή: υπνοδωμάτιο 2 × 2 · βεστιάριο 2 στον άξονα του διαδρόμου · λουτρό 3 (IP65 στο ντους) · WC 1 · καθιστικό – kitchenette 2 × 2 (η βόρεια σειρά 0,52 από τον πάγκο). Σύνολο 14 spots.

Πυρανίχνευση: καπνού σε υπνοδωμάτιο, βεστιάριο και κορυφή σκάλας · θερμοδιαφορικός στο καθιστικό (εστίες kitchenette σε 1,2 m)· ≥ 0,50 από τοίχους / φωτιστικά, ≥ 1,00 από την προσαγωγή.

Σκάλα: φωτιστικά τοίχου / σκαλοπατιών (ηλεκτρολογικά).

ΥΠΟΜΝΗΜΑ

- χωνευτό spot LED 7–9 W, 2700 K – σε κουτί σκυροδέματος (εμφανής πλάκα) ή στην ψευδοροφή
- χωνευτό spot IP44 (λουτρά)
- χωνευτό spot IP65 (πάνω από ντους)
- ΚΡΕΜ παροχή οροφής (κουτί + ενίσχυση ανάρτησης)
- ΑΚ ανιχνευτής καπνού (ΕΠ04 · EN 54-7)
- ΑΘ θερμοδιαφορικός ανιχνευτής (κουζίνα · EN 54-5)
- ακτίνα 0,50 m γύρω από ανιχνευτή – κανένας τοίχος / φωτιστικό μέσα
- LED κρυφό γραμμικό (δεν προβλέπεται στη σοφίτα)

ΕΡΓΟ	ΘΕΜΑ ΣΧΕΔΙΟΥ	ΒΑΣΗ	ΑΡ. ΣΧΕΔΙΟΥ
ΠΕΝΤΑΟΡΟΦΟ ΚΤΗΡΙΟ ΚΑΤΟΙΚΙΩΝ – ΑΡΓΥΡΟΥΠΟΛΗ Κωνσταντινουπόλεως 12 & Αγ. Βαρβάρας · Ο.Τ. 103-15 Εργοδότης: INTERKAT Α.Ε. · Κατασκευή: ARKAD Ι.Κ.Ε.	**ΑΝΟΨΗ – ΦΩΤΙΣΜΟΣ · ΠΥΡΑΝΙΧΝΕΥΣΗ** Spots σε κουτιά σκυροδέματος / IP στα λουτρά · ανιχνευτές ΣΟΦΙΤΑ – Δ1 πάνω επίπεδο (μεζονέτα)	Βάση: τοιχοποιίες σοφίτας R04 · Σ8 (ανεστρ. δοκοί) · ύψος 2,65	**ΑΝ-15** **Κλίμακα 1:50 · Α3** 07/11/2026 · R01

ΣΥΜΜΟΡΦΩΣΗ ΜΕ ΤΙΣ ΠΡΟΔΙΑΓΡΑΦΕΣ (ιδιοκτήτης 07/11/2026)

1 Κλιματισμός	Μία καναλάτη ΚΜ-Σ 9k στο υπνοδωμάτιο, κρυφή στη ντουλάπα βεστιαρίου (οδηγία ιδιοκτήτη) · προσαγωγή γραμμικό slot στον τοίχο · επιστροφή με φίλτρο · πρόσβαση από τα πορτάκια · καθιστικό χωρίς κλιματιστικό (ΕΓΚΕΚΡ.).
2 Κουρτίνες	ΚΡ1 (WS.01) / ΚΡ2 (WS.02 – καθιστικό) 20 × 10, ανοιχτές ως την πλάκα, με λωρίδα +2,55.
3 Φωτισμός	14 χωνευτά spots: σε κουτιά σκυροδέματος στην εμφανή πλάκα, IP65 / IP44 στη ψευδοροφή λουτρού / WC.
4 Πυρανίχνευση	ΑΚ1 υπνοδωμάτιο · ΑΚ2 βεστιάριο · ΑΘ3 καθιστικό – kitchenette · ΑΚ4 κορυφή σκάλας.
5 Κατασκευή	Χωρίς γενική καταβίβαση (ιδιοκτήτης) · τοπικά μόνο λουτρό / WC και λωρίδες κουρτίνας +2,55 · κανένα δοκάρι (Σ8 ανεστραμμένες).
6 Γενική αρχή	2 στάθμες: εμφανής πλάκα +2,65 / +2,55· οι λωρίδες κουρτίνας στη γραμμή της τζαμαρίας, τα λουτρά πίσω από πόρτα.

ΕΓΚΕΚΡΙΜΕΝΕΣ ΑΠΟΚΛΙΣΕΙΣ (ιδιοκτήτης 07/11/2026)

· Σοφίτα: μόνο ένα κλιματιστικό, στο δωμάτιο, κρυφό τοίχου (ιδιοκτήτης 07/11).

· Σοφίτα: χωρίς γενική καταβίβαση της οροφής – spots σε κουτιά σκυροδέματος στην πλάκα (ιδιοκτήτη 07/11).

ΣΟΦΙΤΑ R01 (07/11/2026)

· Πρώτη έκδοση ανόψης σοφίτας (ιδιοκτήτης 07/11: «μην την κατεβάσεις γενικά – μόνο όπου ωραίο ή αναγκαίο · ένα κλιματιστικό στο δωμάτιο, μπορεί κρυφό τοίχου»).

· Οροφή: εμφανής πλάκα Σ8 +2,65 σε υπνοδωμάτιο, βεστιάριο, καθιστικό, σκάλα. Καταβιβάσεις μόνο: λωρίδα κουρτίνας 15 + εσοχή 20 × 10 κατά μήκος των WS.01 / WS.02 (+2,55) · λουτρό / WC +2,55 (ανθυγρή – χωνευτά IP65 / IP44).

· Κλιματισμός: ΚΜ-Σ 9k slim κρυφή πάνω από τη νότια ντουλάπα του βεστιαρίου (καπάκι +2,30), προσαγωγή slot στον T2N-01 προς το υπνοδωμάτιο, επιστροφή από γρίλια στο μέτωπο της ντουλάπας, ψυκτικά από τον Τ4-07 στο δυτικό δώμα. Καθιστικό χωρίς κλιματιστικό.

· Φωτισμός: 14 spots (κουτιά σκυροδέματος στην πλάκα / IP στα λουτρά) · πυρανίχνευση: υπνοδωμάτιο, βεστιάριο, καθιστικό (θερμοδιαφορικός), κορυφή σκάλας.

ΑΝΟΙΚΤΑ ΣΗΜΕΙΑ

· Α1 [ΣΤΑΤΙΚΟΣ] Ύψος σοφίτας: θεωρήθηκε 2,65 (§1Β) με επίπεδη κάτω παρειά Σ8 (ανεστραμμένες δοκοί). Ο Σ8 γράφει στάθμες στέγης +18,49 / +18,70 … +19,72 (κεκλιμένη) – να επιβεβαιωθεί ότι η κάτω παρειά είναι οριζόντια· αν είναι κεκλιμένη, οι θέσεις μένουν, αλλάζουν μόνο οι στάθμες.

· Α2 [ΚΑΤΑΣΚΕΥΗ] ΠΡΙΝ τη σκυροδέτηση του Σ8: κουτιά χωνευτών spots για σκυρόδεμα (Ø 80, βάθος ≤ 100) + κουτιά ανιχνευτών + σωληνώσεις μέσα στην πλάκα στις θέσεις του φύλλου φωτισμού. Μετά τη σκυροδέτηση μόνο επιφανειακά κανάλια.

· Α3 [ΑΠΟΦΑΣΗ] Καθιστικό σοφίτας με 4 spots (δεύτερος χώρος με kitchenette) – ή όπως τα καθιστικά των ορόφων (χωρίς spots, μία παροχή ΚΡΕΜ στο κέντρο).

· Α4 [ΑΠΟΦΑΣΗ] Κουρτινόθηκες ως λωρίδα ψευδοροφής 0,35 (+2,55) κατά μήκος WS.01 / WS.02 (πρόταση – καθαρή εσοχή όπως στους ορόφους) ή επιφανειακή ράγα στην πλάκα χωρίς καμία ψευδοροφή.

· Α5 [ΜΟΝΤΕΛΟ] ΚΜ-Σ: slim καναλάτη ύψος ≤ 200, βάθος ≤ 550 (χωρά στη ντουλάπα 0,60), μικρή στατική πίεση· η νότια ντουλάπα του βεστιαρίου στο 4,50–5,20 με καπάκι +2,30 και επάνω πορτάκια (πρόσβαση).

· Α6 [ΣΥΝΤΟΝΙΣΜΟΣ] Εξωτερική μονάδα ΚΜ-Σ στο δυτικό δώμα (Χ-Σ μέσα από τον Τ4-07 ψηλά)· συμπυκνώματα με φυσική ροή → σιφώνι δώματος.

· Α7 [ΣΥΝΤΟΝΙΣΜΟΣ] Αποχετεύσεις λουτρού / WC σοφίτας στην επίστρωση της σοφίτας (15 cm) – όχι στην οροφή του Δ΄ (βλ. Δ΄ Α5).

ΕΛΕΓΧΟΣ ΣΥΓΚΡΟΥΣΕΩΝ & ΣΤΑΘΜΩΝ – 41 έλεγχοι · ΟΚ 39 · ΟΡΙΑΚΟ 0 · ΕΓΚΕΚΡ. 2 · ΑΠΟΚΛΙΣΗ 0

Αυτόματος έλεγχος από το μοντέλο (code/anopseis/checks.py): στάθμες ↔ δοκοί · κενό μονάδων · θυρίδες · spots ↔ ζώνες / θυρίδες / μονάδες / αεραγωγοί / κουρτινόθηκες · ανιχνευτές ↔ τοίχοι / φωτιστικά / στόμια · κουρτινόθηκες ↔ κουφώματα / δοκοί.

ΚΩΔ.	ΚΑΤΑΣΤ.	ΣΤΟΙΧΕΙΟ	ΜΕΤΡΗΣΗ
ΣΤ-Ζ1	ΟΚ	Ζ1 ΥΠΝΟΔΩΜΑΤΙΟ – εμφανής πλάκα +2,65	Σ8: όλες οι δοκοί ανεστραμμένες – επίπεδη…
ΣΤ-Ζ2	ΟΚ	Ζ2 ΒΕΣΤΙΑΡΙΟ – εμφανής πλάκα +2,65	Σ8: όλες οι δοκοί ανεστραμμένες – επίπεδη…
ΣΤ-Ζ5	ΟΚ	Ζ5 ΚΑΘΙΣΤΙΚΟ – KITCHENETTE – εμφανής πλάκα +2,65	Σ8: όλες οι δοκοί ανεστραμμένες – επίπεδη…
ΣΤ-Ζ8	ΟΚ	Ζ8 ΚΛΙΜΑΚΟΣΤΑΣΙΟ Δ1 – εμφανής πλάκα +2,65	Σ8: όλες οι δοκοί ανεστραμμένες – επίπεδη…
ΚΛ-ΚΜ-Σ	ΟΚ	ΚΜ-Σ 9.000 Btu/h – Υπνοδωμάτιο σοφίτας (κρυφή)	πάνω από τη ντουλάπα βεστιαρίου (καπάκι…
ΘΕ-ΚΜ-Σ	ΟΚ	ΚΜ-Σ – πρόσβαση συντήρησης	επάνω πορτάκια της ντουλάπας βεστιαρίο…
ΚΔ-ΥΠΝ	ΟΚ	Υπνοδωμάτιο σοφίτας	ΚΜ-Σ κρυφή (ντουλάπα βεστιαρίου / slot στ…
ΚΔ-ΒΕΣΤ	ΟΚ	Βεστιάριο	από την ΚΜ-Σ (επιστροφή από το βεστιάρι…
ΚΔ-ΚΑΘ	ΕΓΚΕΚΡ.	Καθιστικό – kitchenette σοφίτας	χωρίς κλιματιστικό – ιδιοκτήτης 07/11: «μό…
ΣΤ-Π-Σ	ΟΚ	Π-Σ γραμμικό slot 2 σχισμών 800 στον τοίχο Τ2N-01 (+2,40…+2,5…	γραμμικό slot στον τοίχο – κρυφή μονάδα τ…
SP-Υ1	ΟΚ	Υ1 spot (3.450 · 3.800) – ΥΠΝΟΔΩΜΑΤΙΟ	κουτί σκυροδέματος στον ξυλότυπο · άκρη …
SP-Υ2	ΟΚ	Υ2 spot (5.650 · 3.800) – ΥΠΝΟΔΩΜΑΤΙΟ	κουτί σκυροδέματος στον ξυλότυπο · άκρη …
SP-Υ3	ΟΚ	Υ3 spot (3.450 · 5.200) – ΥΠΝΟΔΩΜΑΤΙΟ	κουτί σκυροδέματος στον ξυλότυπο · άκρη …
SP-Υ4	ΟΚ	Υ4 spot (5.650 · 5.200) – ΥΠΝΟΔΩΜΑΤΙΟ	κουτί σκυροδέματος στον ξυλότυπο · άκρη …
SP-Β1	ΟΚ	Β1 spot (3.300 · 1.900) – ΒΕΣΤΙΑΡΙΟ	κουτί σκυροδέματος στον ξυλότυπο · άκρη …
SP-Β2	ΟΚ	Β2 spot (5.700 · 1.900) – ΒΕΣΤΙΑΡΙΟ	κουτί σκυροδέματος στον ξυλότυπο · άκρη …
SP-Λ1	ΟΚ	Λ1 spot IP65 (8.830 · 1.250) – ΛΟΥΤΡΟ	κενό 88 mm · άκρη 0.57
SP-Λ2	ΟΚ	Λ2 spot IP44 (7.430 · 1.500) – ΛΟΥΤΡΟ	κενό 88 mm · άκρη 0.83
SP-Λ3	ΟΚ	Λ3 spot IP44 (7.430 · 2.350) – ΛΟΥΤΡΟ	κενό 88 mm · άκρη 0.73
SP-Λ4	ΟΚ	Λ4 spot IP44 (8.750 · 3.100) – WC	κενό 88 mm · άκρη 0.40
SP-Κ1	ΟΚ	Κ1 spot (7.300 · 4.300) – ΚΑΘΙΣΤΙΚΟ – KITCHENETTE	κουτί σκυροδέματος στον ξυλότυπο · άκρη …
SP-Κ2	ΟΚ	Κ2 spot (8.700 · 4.300) – ΚΑΘΙΣΤΙΚΟ – KITCHENETTE	κουτί σκυροδέματος στον ξυλότυπο · άκρη …
SP-Κ3	ΟΚ	Κ3 spot (7.300 · 5.350) – ΚΑΘΙΣΤΙΚΟ – KITCHENETTE	κουτί σκυροδέματος στον ξυλότυπο · άκρη …
SP-Κ4	ΟΚ	Κ4 spot (8.700 · 5.350) – ΚΑΘΙΣΤΙΚΟ – KITCHENETTE	κουτί σκυροδέματος στον ξυλότυπο · άκρη …
SP-ΟΡΟ	ΕΓΚΕΚΡ.	Εμφανής πλάκα Σ8	κουτιά σκυροδέματος εγκιβωτισμένα στον …
ΠΥ-ΑΚ1	ΟΚ	ΑΚ1 καπνού (4.55 · 4.50) – υπνοδωμάτιο	τοίχος 1.39 · Υ1 1.30 · Π-Σ 1.41
ΠΥ-ΑΚ2	ΟΚ	ΑΚ2 καπνού (4.50 · 1.90) – βεστιάριο – άξονας διαδρόμου 1,00	τοίχος 0.50 (διάδρομος 1,00 – άξονας) · Β1 1…
ΠΥ-ΑΘ3	ΟΚ	ΑΘ3 θερμοδιαφορικός (8.00 · 4.82) – καθιστικό – kitchenette (θερ…	τοίχος 1.07 · Κ2 0.87 · Π-Σ 3.25
ΠΥ-ΑΚ4	ΟΚ	ΑΚ4 καπνού (11.95 · 5.85) – κορυφή ιδιωτικής σκάλας (καλύπτει κ…	τοίχος 0.75 · Κ4 3.29 · Π-Σ 7.25
ΠΥ-ΧΩΡ	ΟΚ	Κάλυψη χώρων	υπνοδωμάτιο · βεστιάριο · καθιστικό (θερμι…
ΚΡ-ΚΡ1	ΟΚ	ΚΡ1 WS.01 – υπνοδωμάτιο – Ν · 20 × 10 cm · οδηγοί 7 / 14 cm	πλήρης · βάθος 10 cm
ΚΡ-ΚΡ2	ΟΚ	ΚΡ2 WS.02 – καθιστικό – Ν · 20 × 10 cm · οδηγοί 7 / 14 cm	πλήρης · βάθος 10 cm
ΚΡ-WS.06	ΟΚ	WS.06	δεν απαιτείται – βεστιάριο – ανάμεσα σε ντ…
ΚΡ-WS.02-Α	ΟΚ	WS.02-Α	δεν απαιτείται – ανατολικό 1,00 της τζαμα…
ΚΡ-WS.03	ΟΚ	WS.03	δεν απαιτείται – κλιμακοστάσιο (εκτός διαμ…
ΚΡ-WS.04	ΟΚ	WS.04	δεν απαιτείται – WC (ποδιά 1,50)
ΚΡ-WS.05	ΟΚ	WS.05	δεν απαιτείται – ντους (ποδιά 1,50)
ΣΘ-Ζ1	ΟΚ	Ζ1 εμφανής ↔ Ζ6 +2,55	λωρίδα κουρτινόθηκης ΚΡ1 κατά μήκος του…
ΣΘ-Ζ5	ΟΚ	Ζ5 εμφανής ↔ Ζ7 +2,55	λωρίδα κουρτινόθηκης ΚΡ2 κατά μήκος του…
ΣΘ-Ζ3	ΟΚ	Ζ3 / Ζ4 +2,55	λουτρό / WC – κλειστοί χώροι με πόρτα · α…
ΣΘ-ΣΥΝ	ΟΚ	Στάθμες στο διαμέρισμα	+2.55 · +2.65 (εμφανής πλάκα +2,65 · λωρι…

B