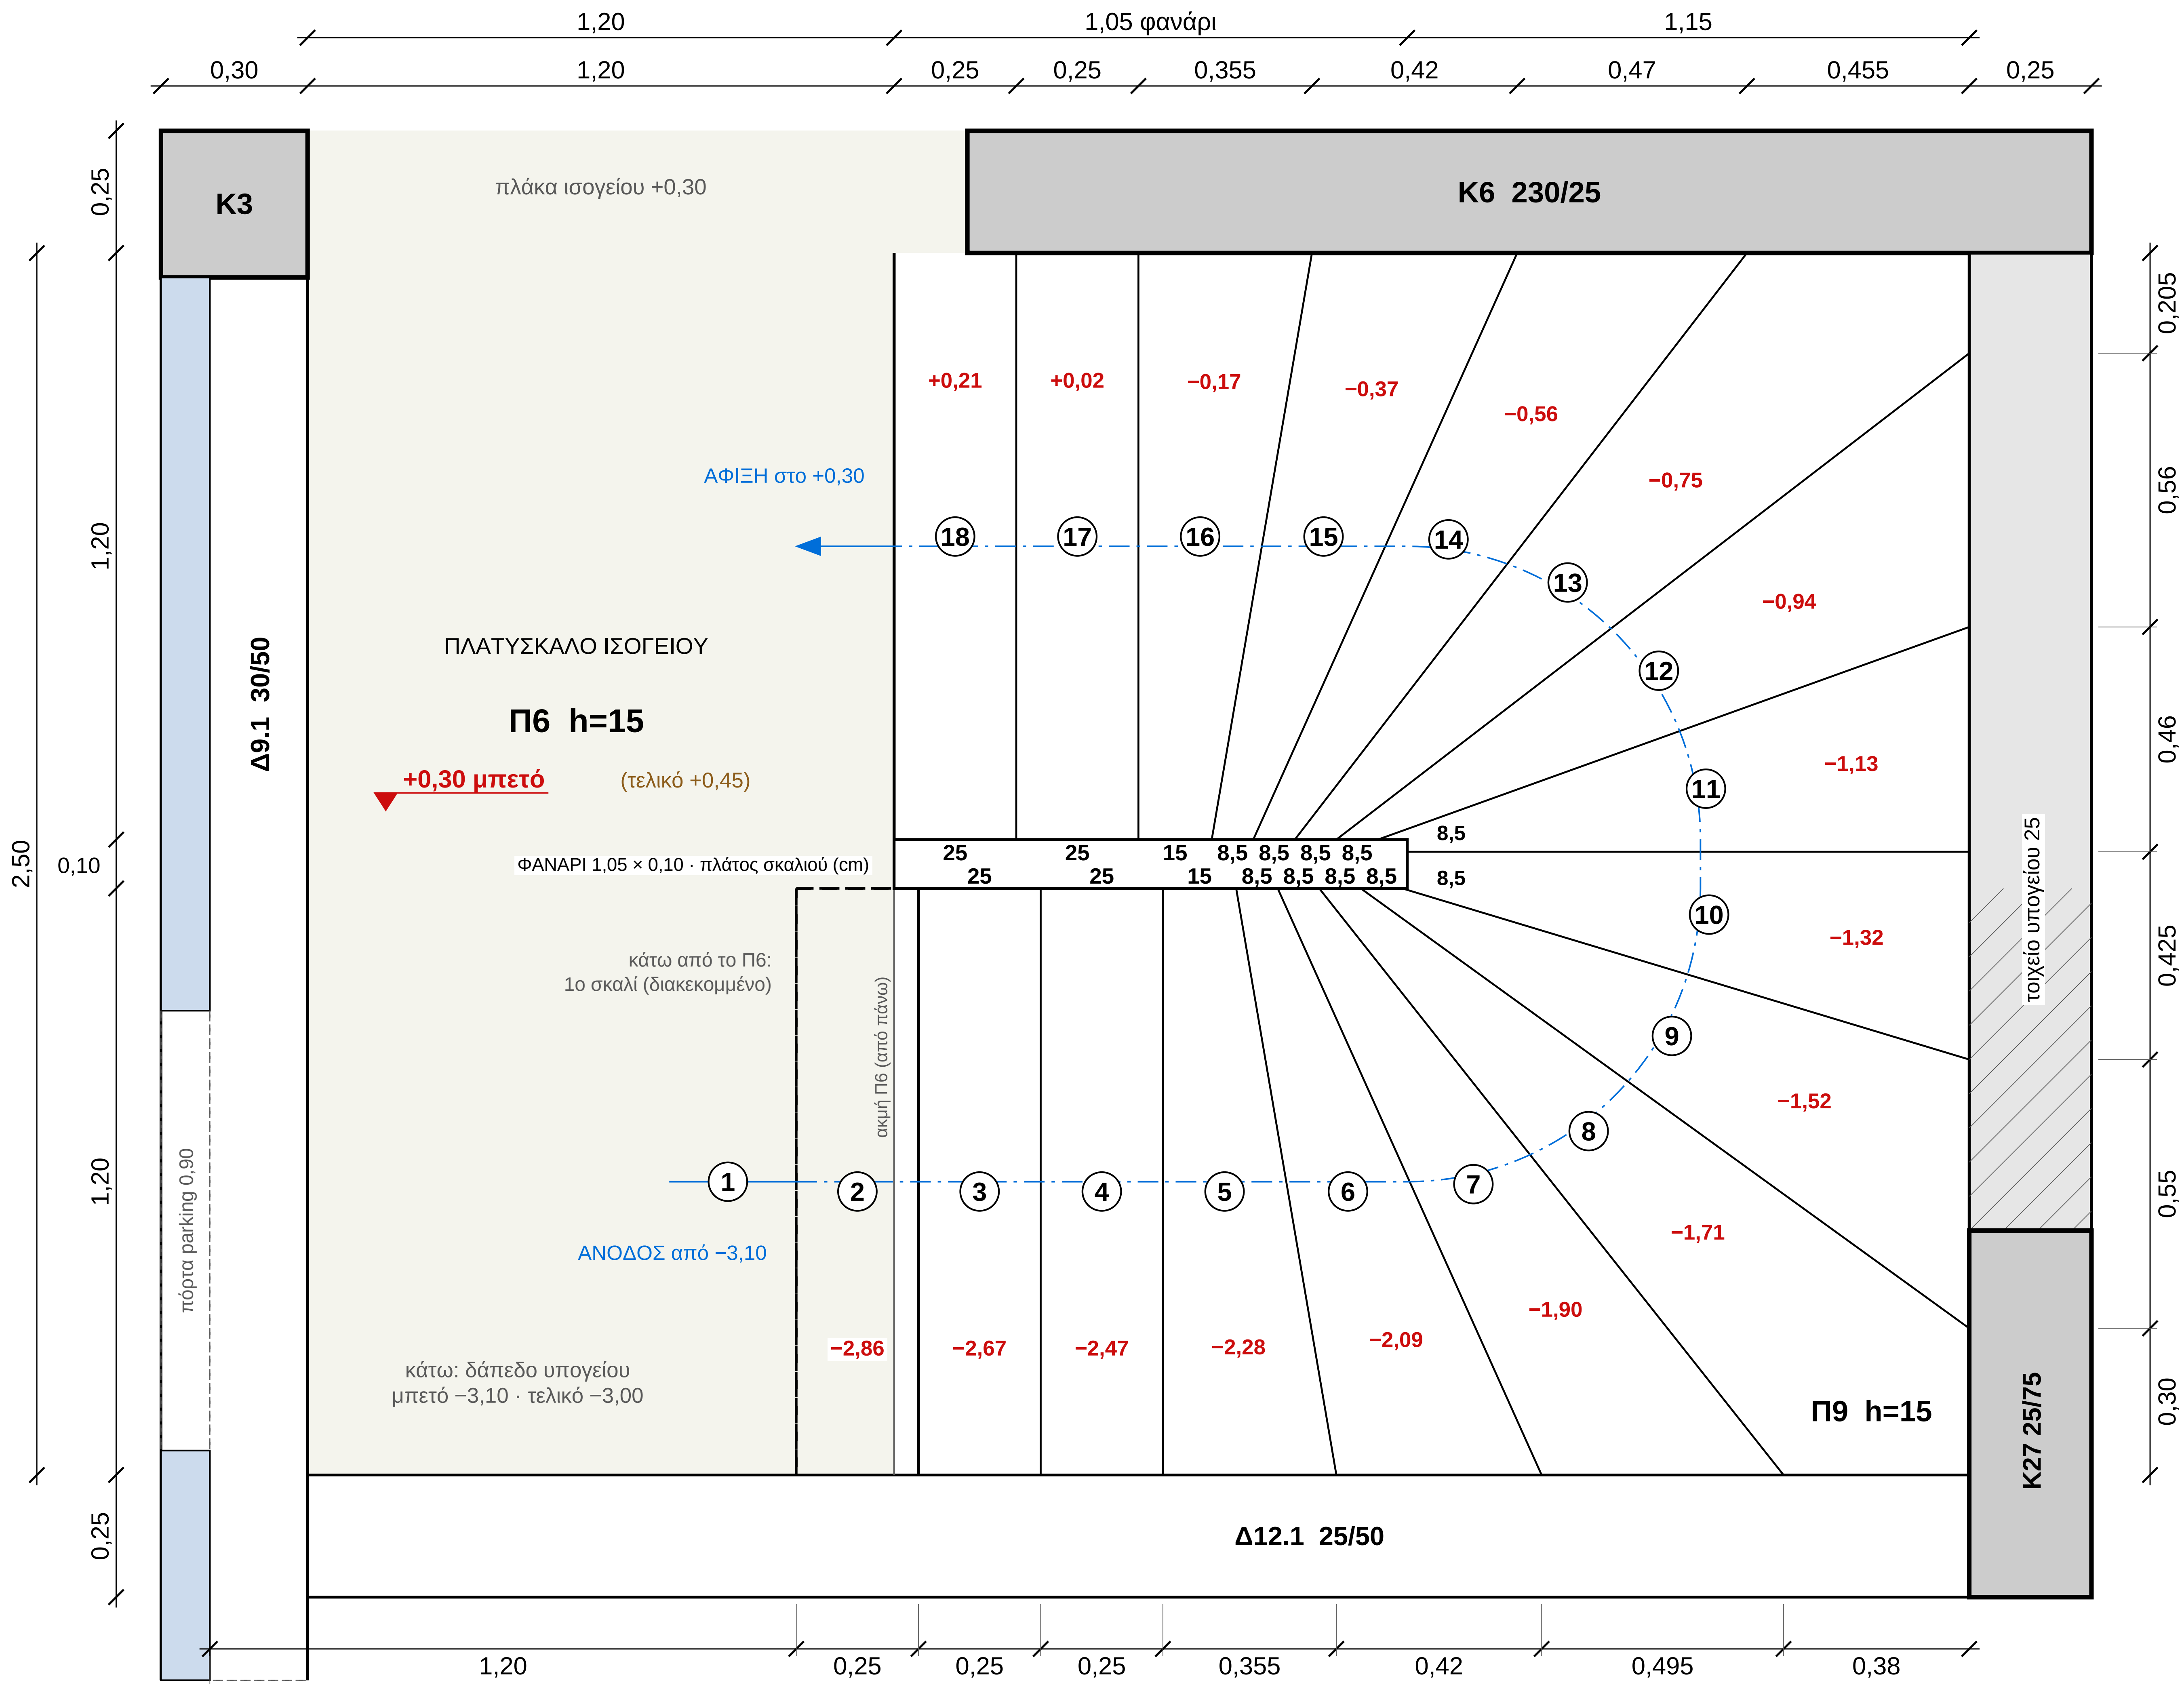

Σ2α

ΣΚΑΛΑ ΥΠΟΓΕΙΟΥ → ΙΣΟΓΕΙΟΥ

ΚΑΤΟΨΗ ΞΥΛΟΤΥΠΟΥ

ΚΛΙΜΑΚΑ

1:12,5

A3 – εκτύπωση 100 %

0 20 40 cm

ΑΛΛΑΓΗ: 18 ΡΙΧΤΙΑ
αντί 16 της μελέτης (21,6 cm)
ένα σκαλί ακόμη στο υπόγειο,
κάτω από το πλατύσκαλο Π6
φανάρι 1,05 (μελέτη 1,00)
ΜΕ ΕΓΚΡΙΣΗ ΜΕΛΕΤΗΤΩΝ

ΠΛΑΤΥΣΚΑΛΟ ΥΠΟΓΕΙΟΥ
1,20 m από τον τοίχο της
πόρτας ως το 1ο σκαλί

ΑΡΙΘΜΗΣΗ 1–18
ο αριθμός είναι ΠΡΙΝ από το
ρίχτι του · 18 ρίχτια =
17 πατήματα + πλατύσκαλο

ΜΕΣΑ ΣΤΟ ΦΑΝΑΡΙ
πλάτος κάθε σκαλιού
στο φανάρι, σε cm

ΚΟΚΚΙΝΟ
στάθμη ΜΠΕΤΟΥ πατήματος
(τελικό − επένδυση 5 cm *)

ΜΠΛΕ
γραμμή ανάβασης, 60 cm από
το φανάρι: πάτημα 25 cm
σε όλα τα σκαλοπάτια

ΡΙΧΤΙΑ
18 × 19,17 cm (τελικό)
μπετό: 1ο 24,2 · 2ο–17ο 19,17
18ο 9,2 cm

ΣΤΑΘΜΕΣ
μπετό −3,10 → +0,30
τελικό −3,00 → +0,45
πλάκες Π6 / Π9 h = 15

ΔΙΑΣΤΑΣΕΙΣ
σε m, από παρειές μπετού
κλάδος 1,20 · φανάρι 1,05×0,10

* επένδυση βαθμίδας 5 cm:
παραδοχή – να επιβεβαιωθεί

ΚΩΝΣΤΑΝΤΙΝΟΥΠΟΛΕΩΣ 12
& ΑΓ. ΒΑΡΒΑΡΑΣ
ΑΡΓΥΡΟΥΠΟΛΗ

Βάση: Σ2_ΕΦ · A-10-B · A-30-AA
R04 · 14/11/2026