
B

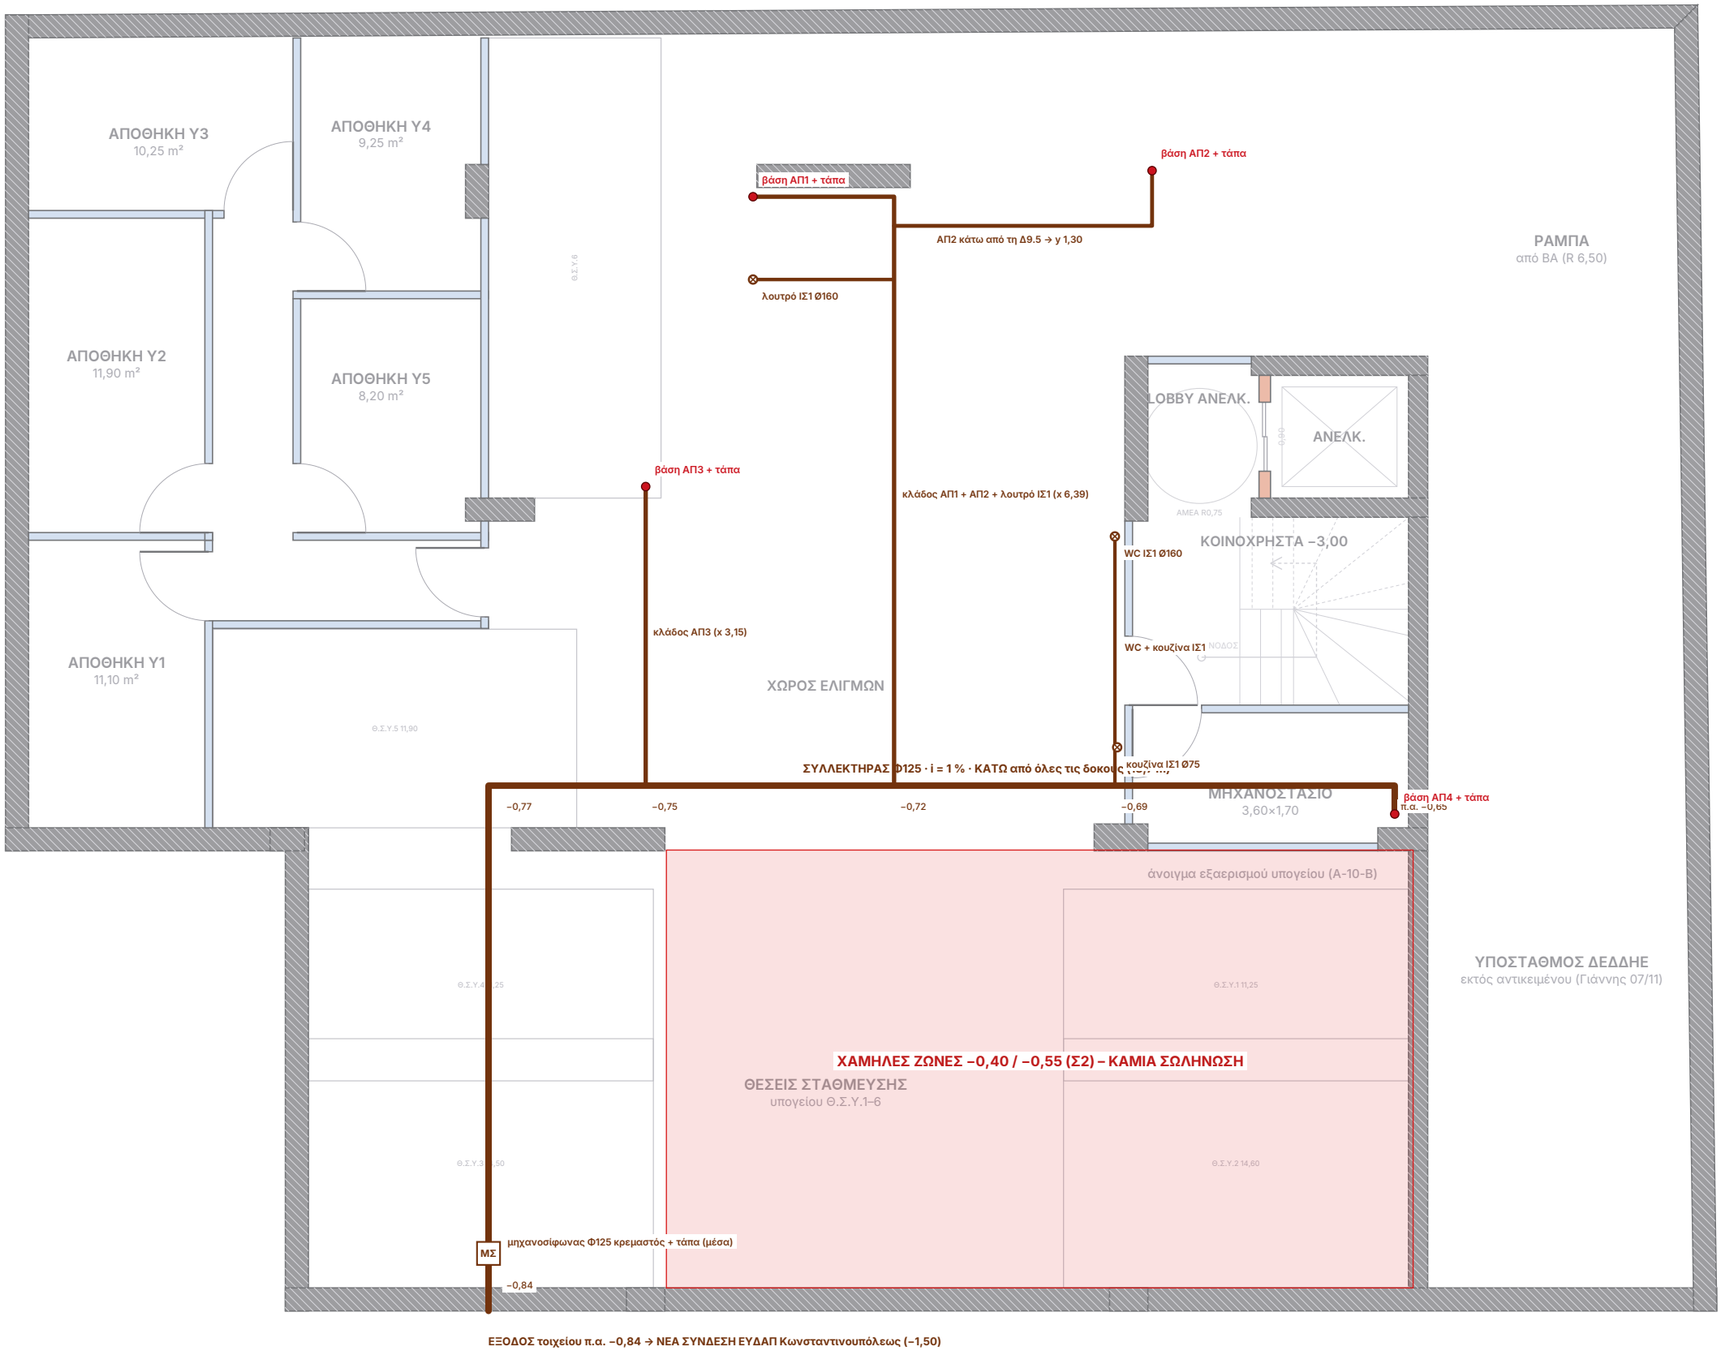


ΥΠΟΜΝΗΜΑ

- Στήλη λυμάτων ΑΠ (Φ100 / ΑΠ4 Φ75) · αερισμός συνεχίζει
- Θέση R12 όπου μετακινήθηκε (διακεκομμένη)
- Λεκάνη → στήλη Φ90 / Φ100
- Ποτισόφωνο / σιφώνι → στήλη Φ50–Φ75
- Ντους / πλυντήριο Φ50 · νιπτήρας Φ40 · νεροχύτης Φ50
- Ποτισόφωνο ΠΣ (σιφώνι δαπέδου)
- Υδρορροή ΥΔ Φ75 μέσα στη θερμοπρόσοψη (αναμονή Ø125)
- Σιφώνι ομβρίων εξώστη · διακεκ. = πλευρική έξοδος
- Δοκός (Σ4/Σ5) – καμία οπή
- Συλλεκτήρας Φ125 / κλάδοι – κρεμαστοί κάτω από δοκούς

ΣΗΜΕΙΩΣΕΙΣ ΥΠΟΓΕΙΟΥ – R14

1. Διαδρομή και στάθμες όπως R12: κεφαλή ΑΠ4 −0,65 → έξοδος ΝΔ −0,84, i = 1 %, 18,7 m, κάτω από όλες τις δοκούς Σ2 – καμία διάτρηση.
2. Αλλαγές λόγω νέων τοιχοποιιών: βάση ΑΠ1 4,55 / 0,92 (από 4,83), ΑΠ3 3,15 / 4,70 (από 3,95), ΑΠ2 9,755 / 0,58, ΑΠ4 κουτί 12,92 / 8,97.
3. Πτώσεις ισογείου στις νέες θέσεις: λουτρό 4,55 / 2,00 · WC 9,27 / 5,35 · νεροχύτης 9,30 / 8,10.
4. Χαμηλές ζώνες −0,40 / −0,55: τίποτα. Ο υποσταθμός ΔΕΔΔΗΕ δεν αγγίζεται.
5. ΑΝΟΙΚΤΑ: βάθος ΕΥΔΑΠ −1,50 · καθαρό ύψος 2,16 πάνω από Θ.Σ.Υ. 3/4 (< 2,20).

ΕΡΓΟ	ΘΕΜΑ ΣΧΕΔΙΟΥ	ΒΑΣΗ	ΑΡ. ΣΧΕΔΙΟΥ
ΠΕΝΤΑΟΡΟΦΟ ΚΤΗΡΙΟ ΚΑΤΟΙΚΙΩΝ – ΑΡΓΥΡΟΥΠΟΛΗ Κωνσταντινουπόλεως 12 & Αγ. Βαρβάρας · Ο.Τ. 103-15 Εργοδότης: INTERKAT Α.Ε. · Κατασκευή: ARKAD Ι.Κ.Ε.	**ΟΡΟΦΗ ΥΠΟΓΕΙΟΥ – ΣΥΛΛΕΚΤΗΡΑΣ** Λύση R12 στις νέες τοιχοποιίες · λύματα · αερισμοί · όμβρια ΥΠΟΓΕΙΟ – συλλεκτήρας κάτω από τις δοκούς · έξοδος −0,84	R12 ΑΠ-02 · Σ2 εφαρμογής · τοιχοποιίες υπογείου R05	**ΑΠ-01** **Κλίμακα 1:80 · Α3** 10/11/2026 · R14

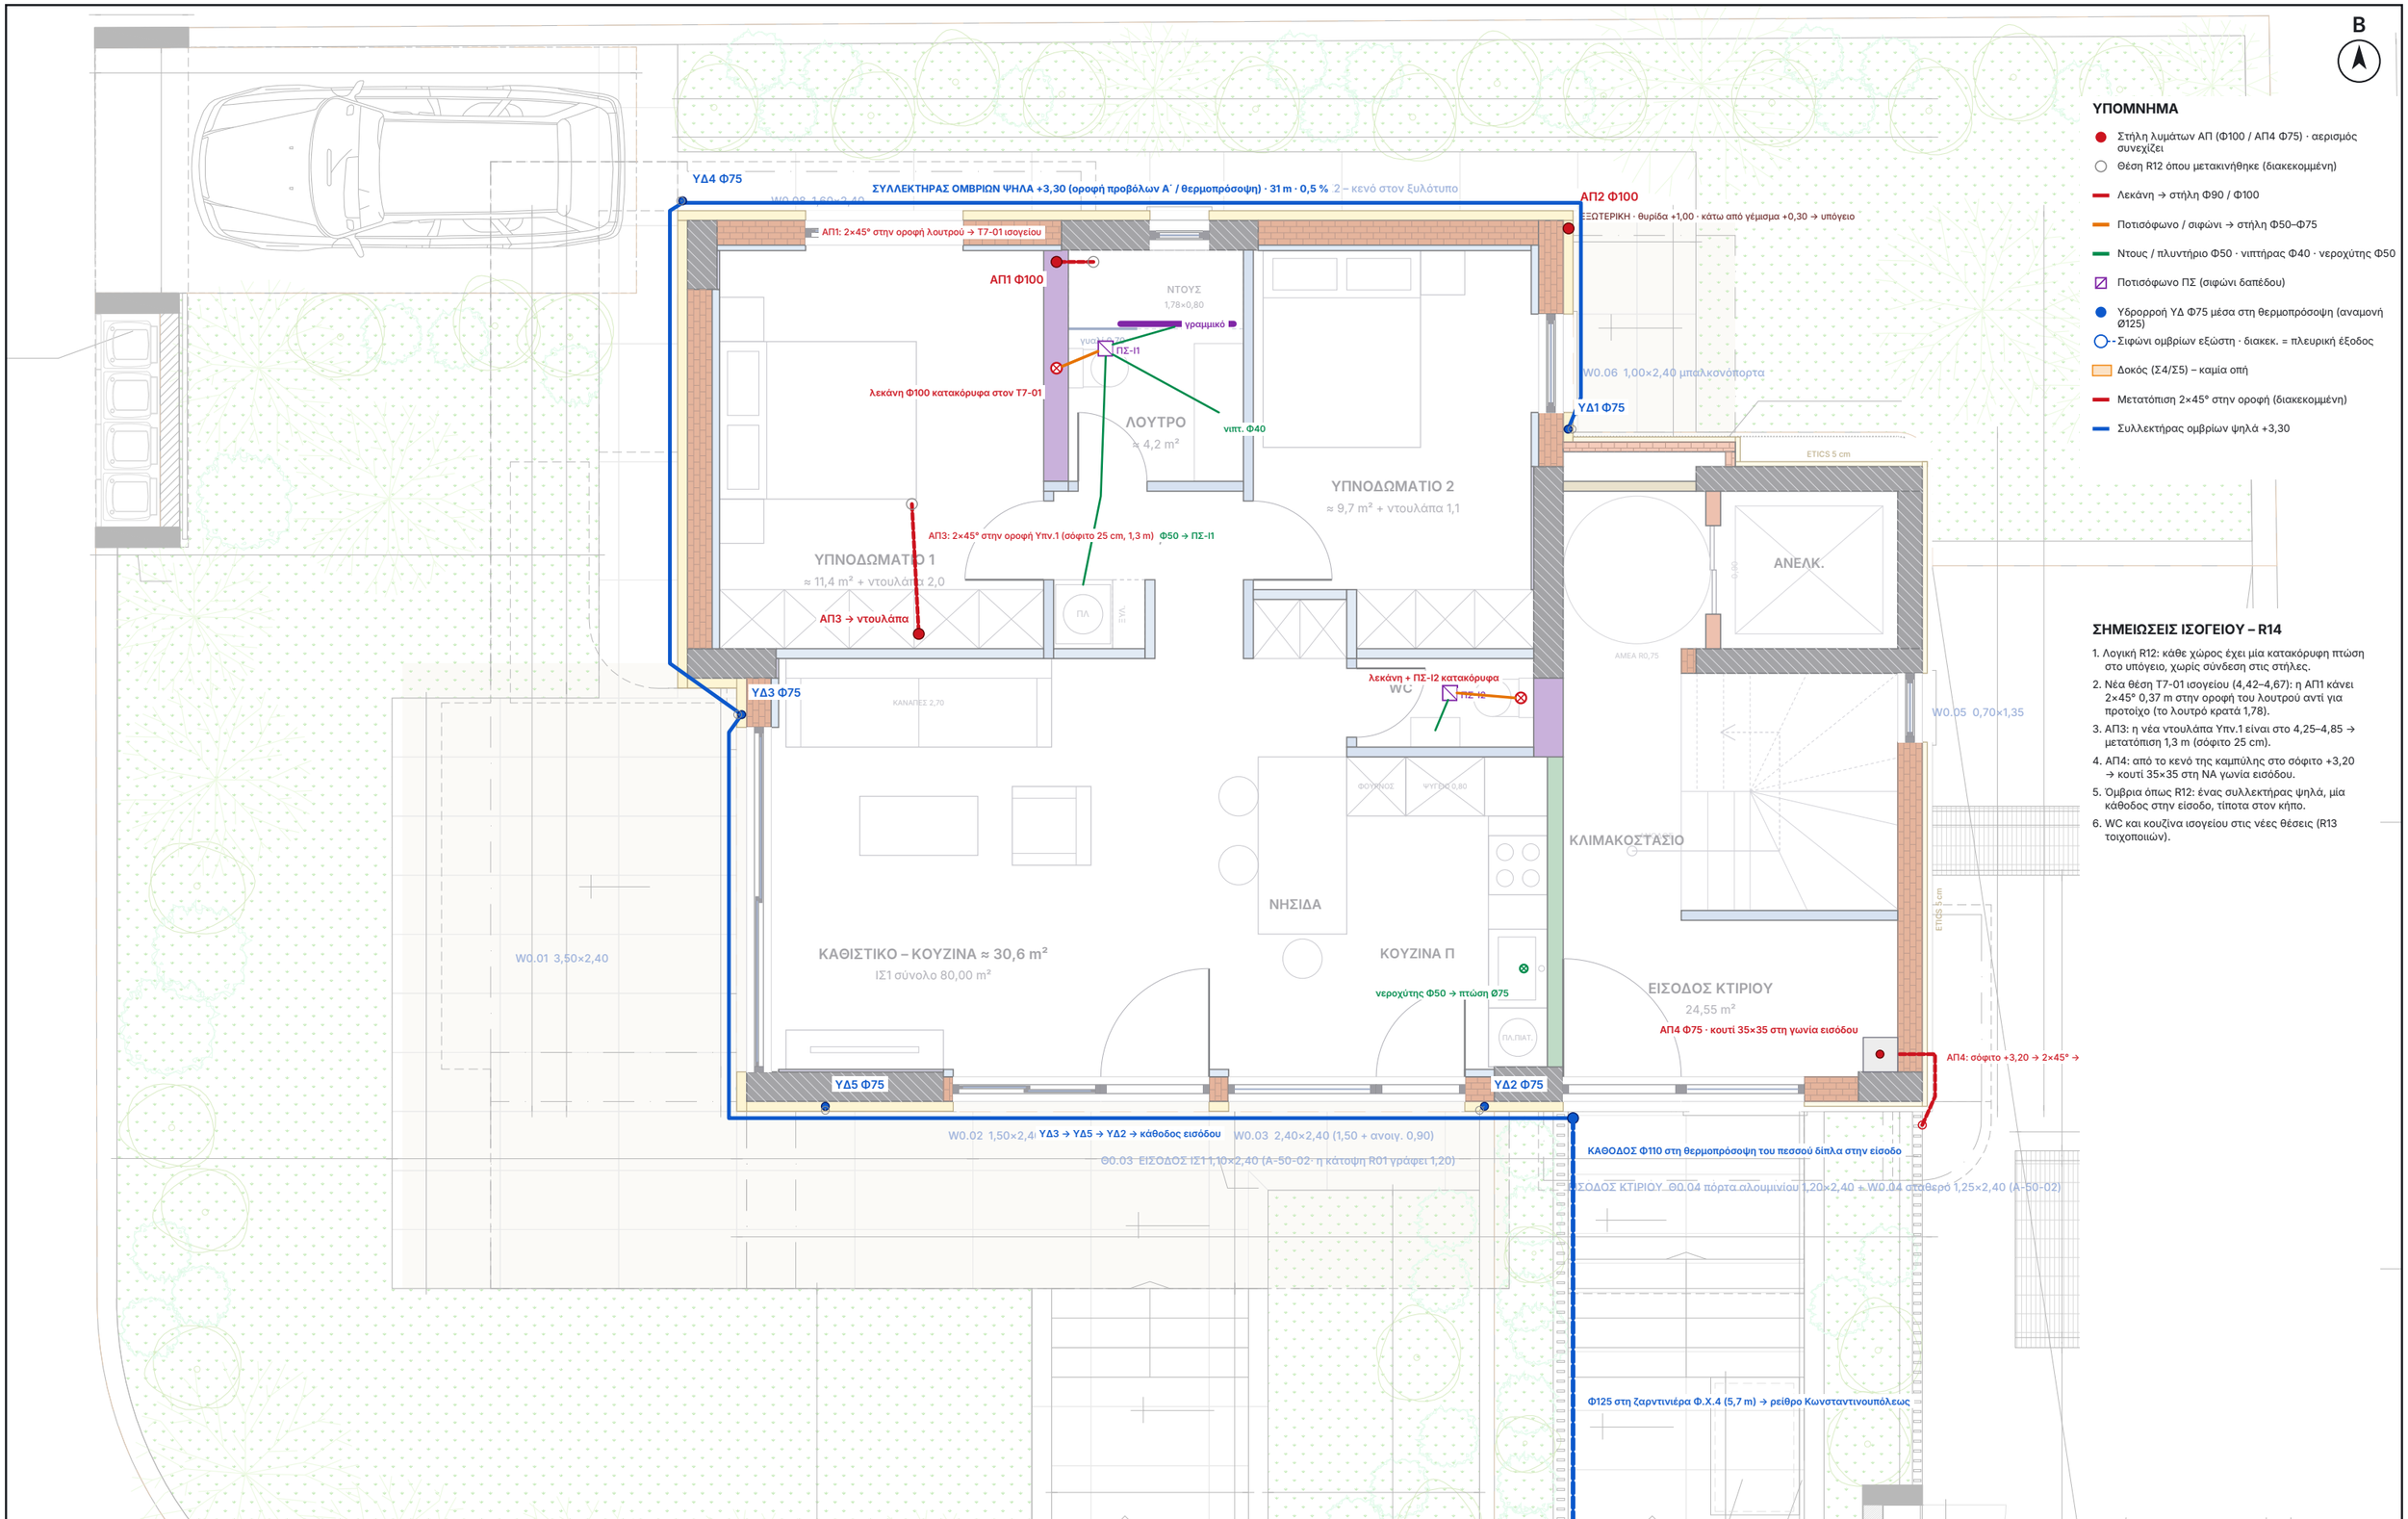

ΕΡΓΟ

ΠΕΝΤΑΟΡΟΦΟ ΚΤΗΡΙΟ ΚΑΤΟΙΚΙΩΝ – ΑΡΓΥΡΟΥΠΟΛΗ
Κωνσταντινουπόλεως 12 & Αγ. Βαρβάρας · Ο.Τ. 103-15
Εργοδότης: INTERKAT Α.Ε. · Κατασκευή: ARKAD Ι.Κ.Ε.

ΘΕΜΑ ΣΧΕΔΙΟΥ


ΙΣΟΓΕΙΟ – ΑΠΟΧΕΤΕΥΣΗ & ΟΜΒΡΙΑ
Λύση R12 στις νέες τοιχοποιίες · λύματα · αερισμοί · όμβρια
ΙΣΟΓΕΙΟ – πτώσεις · μετατοπίσεις στηλών · όμβρια ψηλά

ΒΑΣΗ

R12 ΑΠ-04 · τοιχοποιίες ισογείου R13

ΑΡ. ΣΧΕΔΙΟΥ

ΑΠ-02
Κλίμακα 1:60 · Α3
10/11/2026 · R14

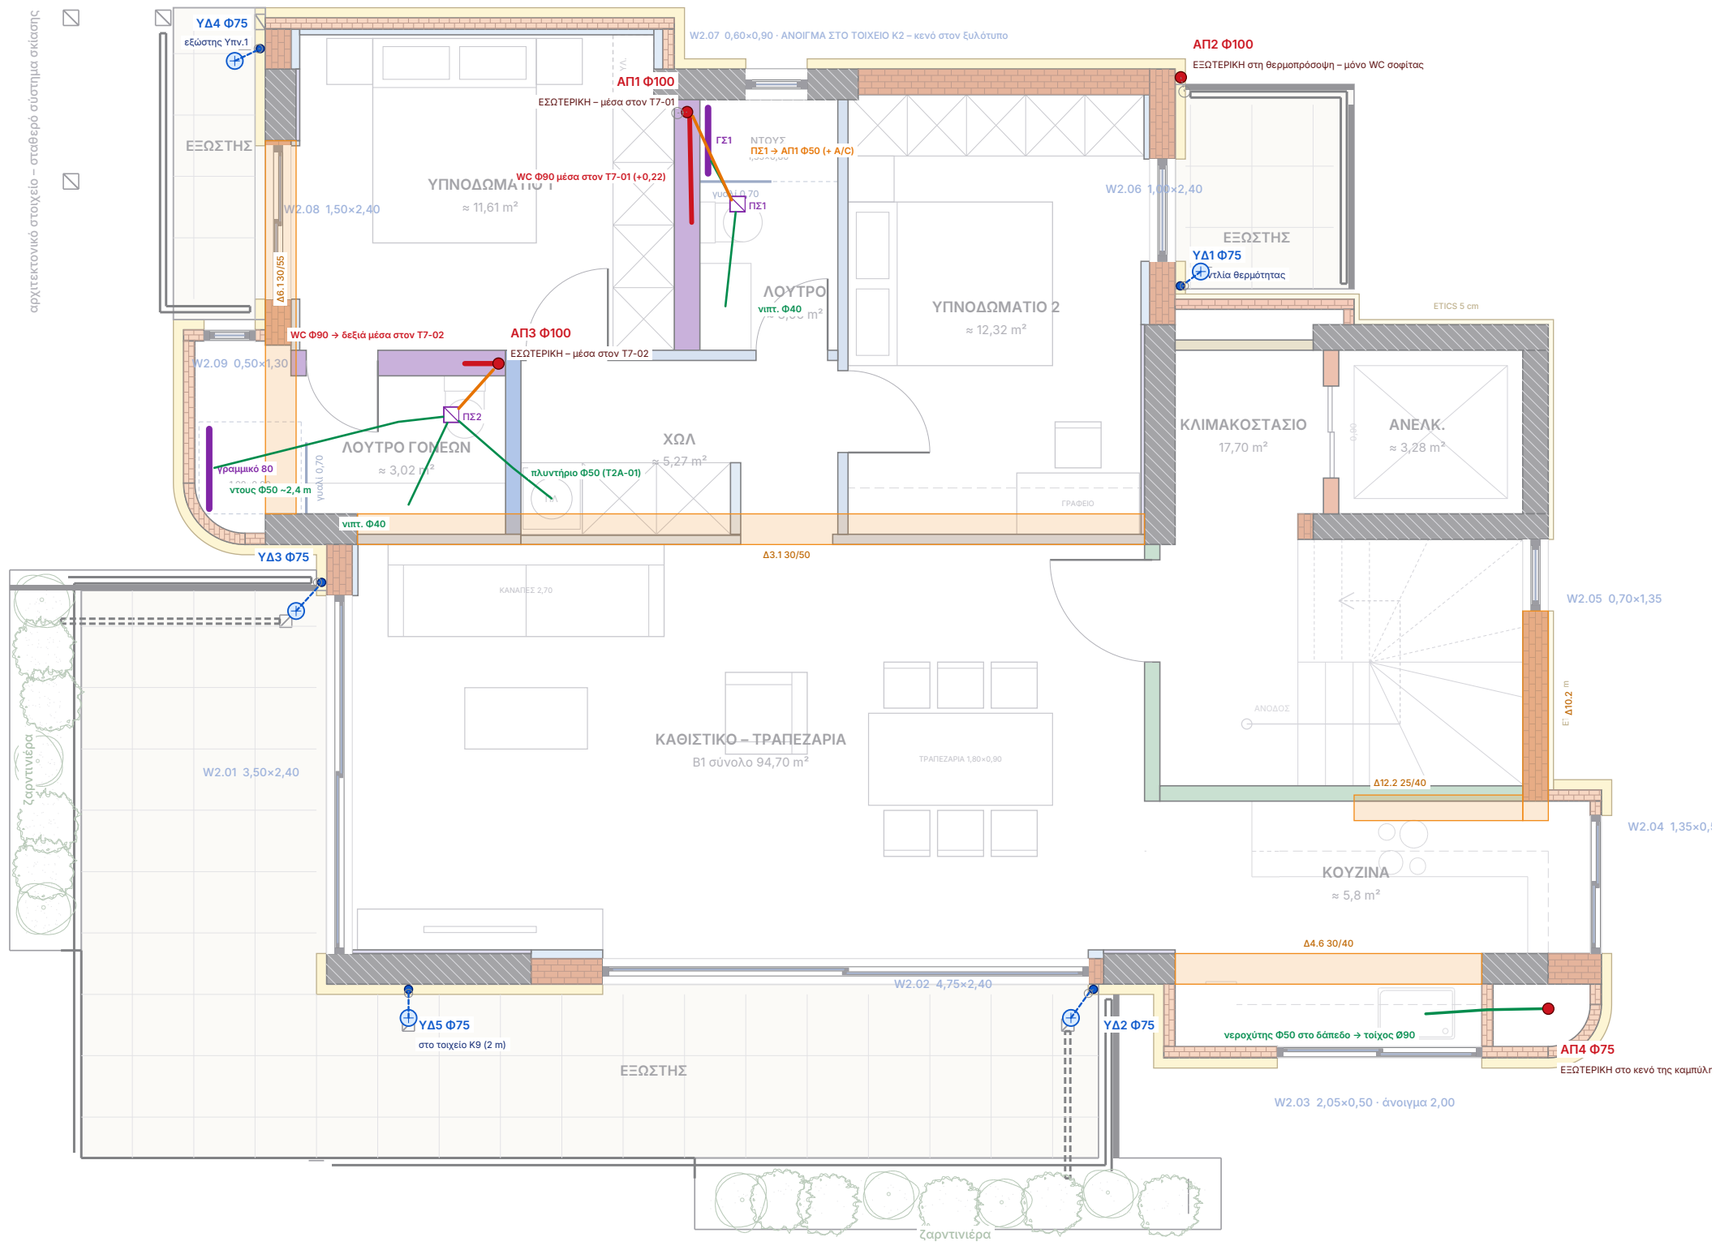


ΥΠΟΜΝΗΜΑ

- Στήλη λυμάτων ΑΠ (Φ100 / ΑΠ4 Φ75) · αερισμός συνεχίζει
- Θέση R12 όπου μετακινήθηκε (διακεκομμένη)
- Λεκάνη → στήλη Φ90 / Φ100
- Ποτισόφωνο / σιφώνι → στήλη Φ50–Φ75
- Ντους / πλυντήριο Φ50 · νιπτήρας Φ40 · νεροχύτης Φ50
- Ποτισόφωνο ΠΣ (σιφώνι δαπέδου)
- Υδρορροή ΥΔ Φ75 μέσα στη θερμοπρόσοψη (αναμονή Φ125)
- Σιφώνι ομβρίων εξώστη · διακεκ. = πλευρική έξοδος
- Δοκός (Σ4/Σ5) – καμία οπή
- Γραμμικό σιφώνι ντους

ΣΗΜΕΙΩΣΕΙΣ – R14

1. Λύση R12 στις νέες τοιχοποιίες: ΑΠ1 μέσα στον Τ7-01 (4,925 / 0,92), ΑΠ3 μέσα στον Τ7-02 (3,08 / 3,38).
2. ΑΠ2 κατέβηκε στο y 0,58: στο 0,72 έπεφτε πάνω στο στηθαίο του εξώστη Υπν.2.
3. ΥΔ3 στο x 1,35 (μέσα στη θερμοπρόσοψη του Τ1-12, έξω από το τοιχείο). Οι άλλες υδρορροές μένουν.
4. Λεκάνες κρεμαστές, Φ90 μέσα στους τοίχους λεκάνης (+0,22). Ποτισόφωνα δίπλα στις λεκάνες.
5. Πλυντήριο: νέα θέση στο χωλ → ΠΣ2 μέσα από τον Τ2Α-01.
6. ΑΠ4 Φ75 εξωτερική στο κενό της καμπύλης (12,81–13,76 × 9,45–10,06) – καμία οπή πλάκας.

ΕΡΓΟ	ΘΕΜΑ ΣΧΕΔΙΟΥ	ΒΑΣΗ	ΑΡ. ΣΧΕΔΙΟΥ
ΠΕΝΤΑΟΡΟΦΟ ΚΤΗΡΙΟ ΚΑΤΟΙΚΙΩΝ – ΑΡΓΥΡΟΥΠΟΛΗ Κωνσταντινουπόλεως 12 & Αγ. Βαρβάρας · Ο.Τ. 103-15 Εργοδότης: INTERKAT Α.Ε. · Κατασκευή: ARKAD Ι.Κ.Ε.	**Α΄·Β΄·Γ΄ ΟΡΟΦΟΣ – ΣΤΗΛΕΣ & ΣΥΝΔΕΣΕΙΣ** Λύση R12 στις νέες τοιχοποιίες · λύματα · αερισμοί · όμβρια Α΄ · Β΄ · Γ΄ ΟΡΟΦΟΣ – τυπικός (Β1)	R12 ΑΠ-05/06/07 · τοιχοποιίες τυπικού R25	**ΑΠ-03** **Κλίμακα 1:60 · Α3** 10/11/2026 · R14

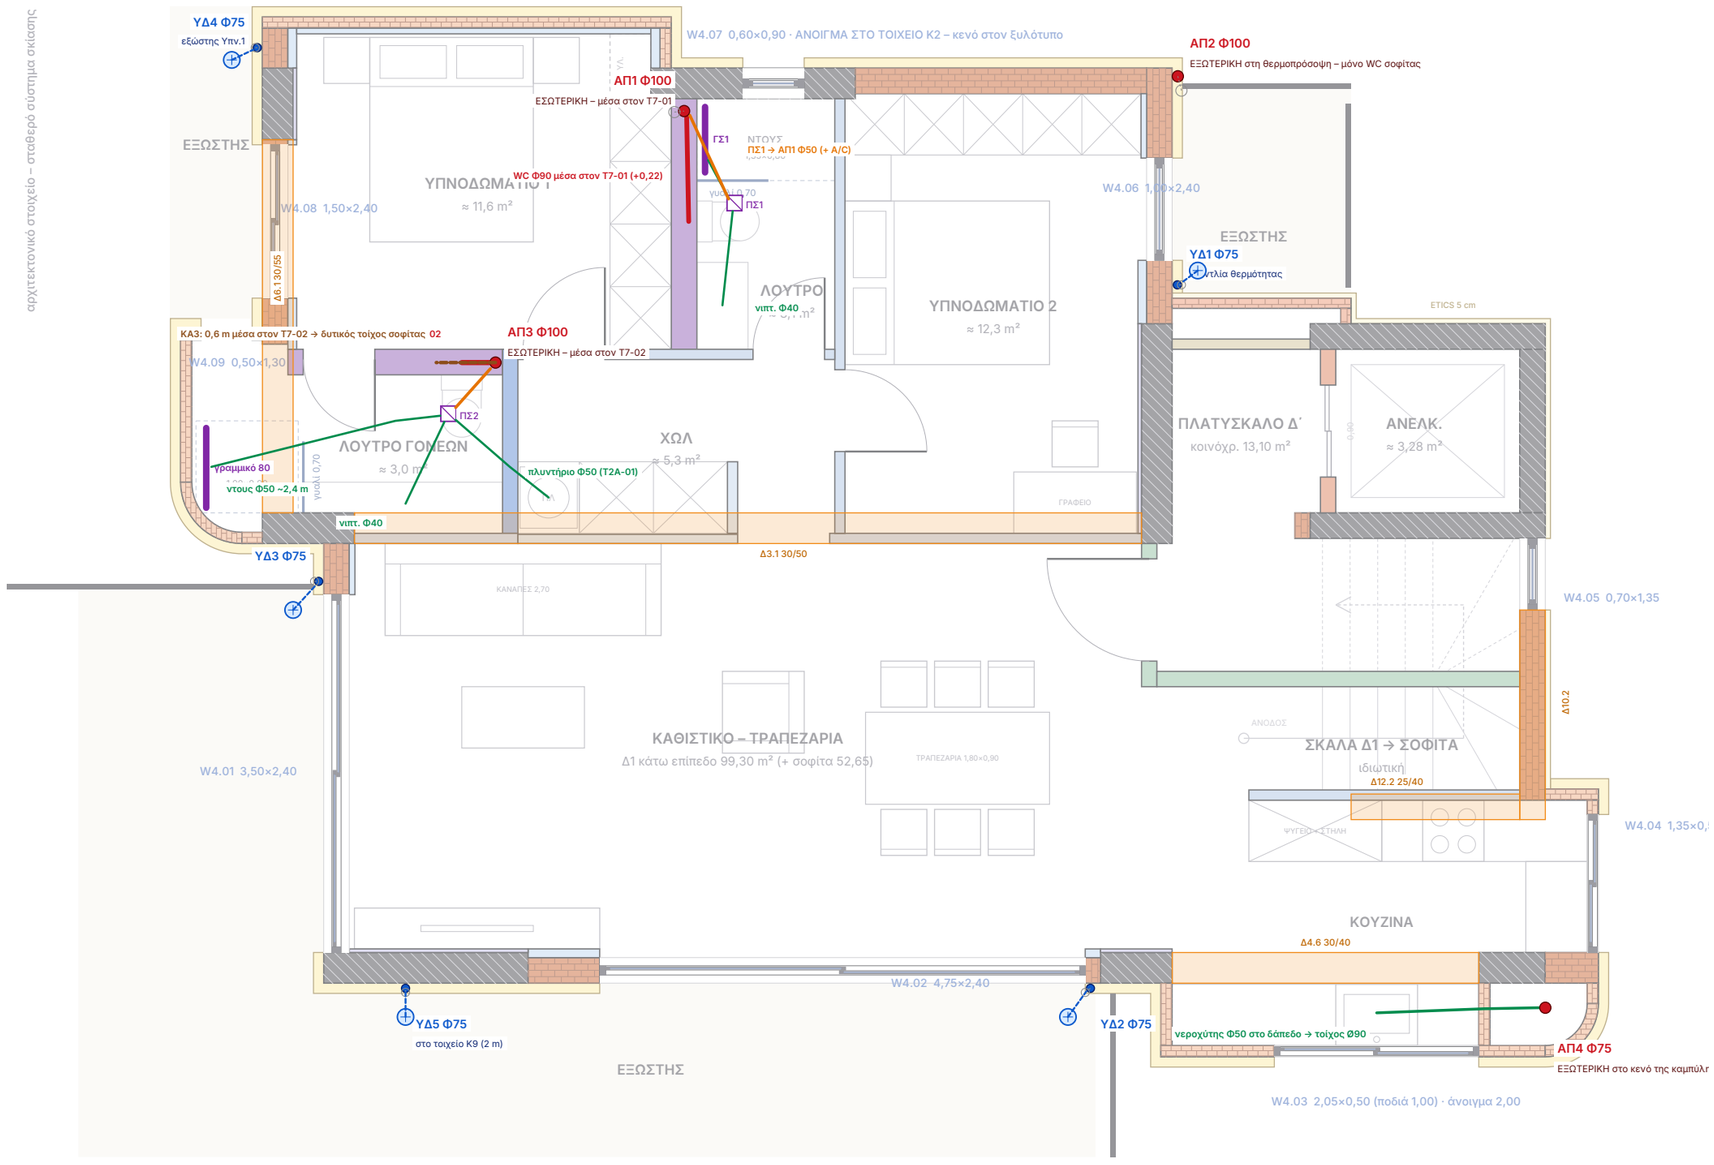


ΥΠΟΜΝΗΜΑ

- Στήλη λυμάτων ΑΠ (Φ100 / ΑΠ4 Φ75) · αερισμός συνεχίζει
- Θέση R12 όπου μετακινήθηκε (διακεκομμένη)
- Λεκάνη → στήλη Φ90 / Φ100
- Ποτισόφωνο / σιφώνι → στήλη Φ50–Φ75
- Ντους / πλυντήριο Φ50 · νιπτήρας Φ40 · νεροχύτης Φ50
- Ποτισόφωνο ΠΣ (σιφώνι δαπέδου)
- Υδρορροή ΥΔ Φ75 μέσα στη θερμοπρόσοψη (αναμονή Φ125)
- Σιφώνι ομβρίων εξώστη · διακεκ. = πλευρική έξοδος
- Δοκός (Σ4/Σ5) – καμία οπή
- Γραμμικό σιφώνι ντους

ΣΗΜΕΙΩΣΕΙΣ – R14

1. Λύση R12 στις νέες τοιχοποιίες: ΑΠ1 μέσα στον Τ7-01 (4,925 / 0,92), ΑΠ3 μέσα στον Τ7-02 (3,08 / 3,38).
2. ΑΠ2 κατέβηκε στο y 0,58: στο 0,72 έπεφτε πάνω στο στηθαίο του εξώστη Υπν.2.
3. ΥΔ3 στο x 1,35 (μέσα στη θερμοπρόσοψη του Τ1-12, έξω από το τοιχείο). Οι άλλες υδρορροές μένουν.
4. Λεκάνες κρεμαστές, Φ90 μέσα στους τοίχους λεκάνης (+0,22). Ποτισόφωνα δίπλα στις λεκάνες.
5. Πλυντήριο: νέα θέση στο χωλ → ΠΣ2 μέσα από τον Τ2Α-01.
6. ΑΠ4 Φ75 εξωτερική στο κενό της καμπύλης (12,81–13,76 × 9,45–10,06) – καμία οπή πλάκας.

ΕΡΓΟ	ΘΕΜΑ ΣΧΕΔΙΟΥ	ΒΑΣΗ	ΑΡ. ΣΧΕΔΙΟΥ
ΠΕΝΤΑΟΡΟΦΟ ΚΤΗΡΙΟ ΚΑΤΟΙΚΙΩΝ – ΑΡΓΥΡΟΥΠΟΛΗ Κωνσταντινουπόλεως 12 & Αγ. Βαρβάρας · Ο.Τ. 103-15 Εργοδότης: INTERKAT Α.Ε. · Κατασκευή: ARKAD Ι.Κ.Ε.	**Δ΄ ΟΡΟΦΟΣ – ΣΤΗΛΕΣ & ΣΥΝΔΕΣΕΙΣ** Λύση R12 στις νέες τοιχοποιίες · λύματα · αερισμοί · όμβρια Δ΄ ΟΡΟΦΟΣ – Δ1 κάτω επίπεδο	R12 ΑΠ-05 · τοιχοποιίες Δ΄ R04	**ΑΠ-04** **Κλίμακα 1:60 · Α3** 10/11/2026 · R14

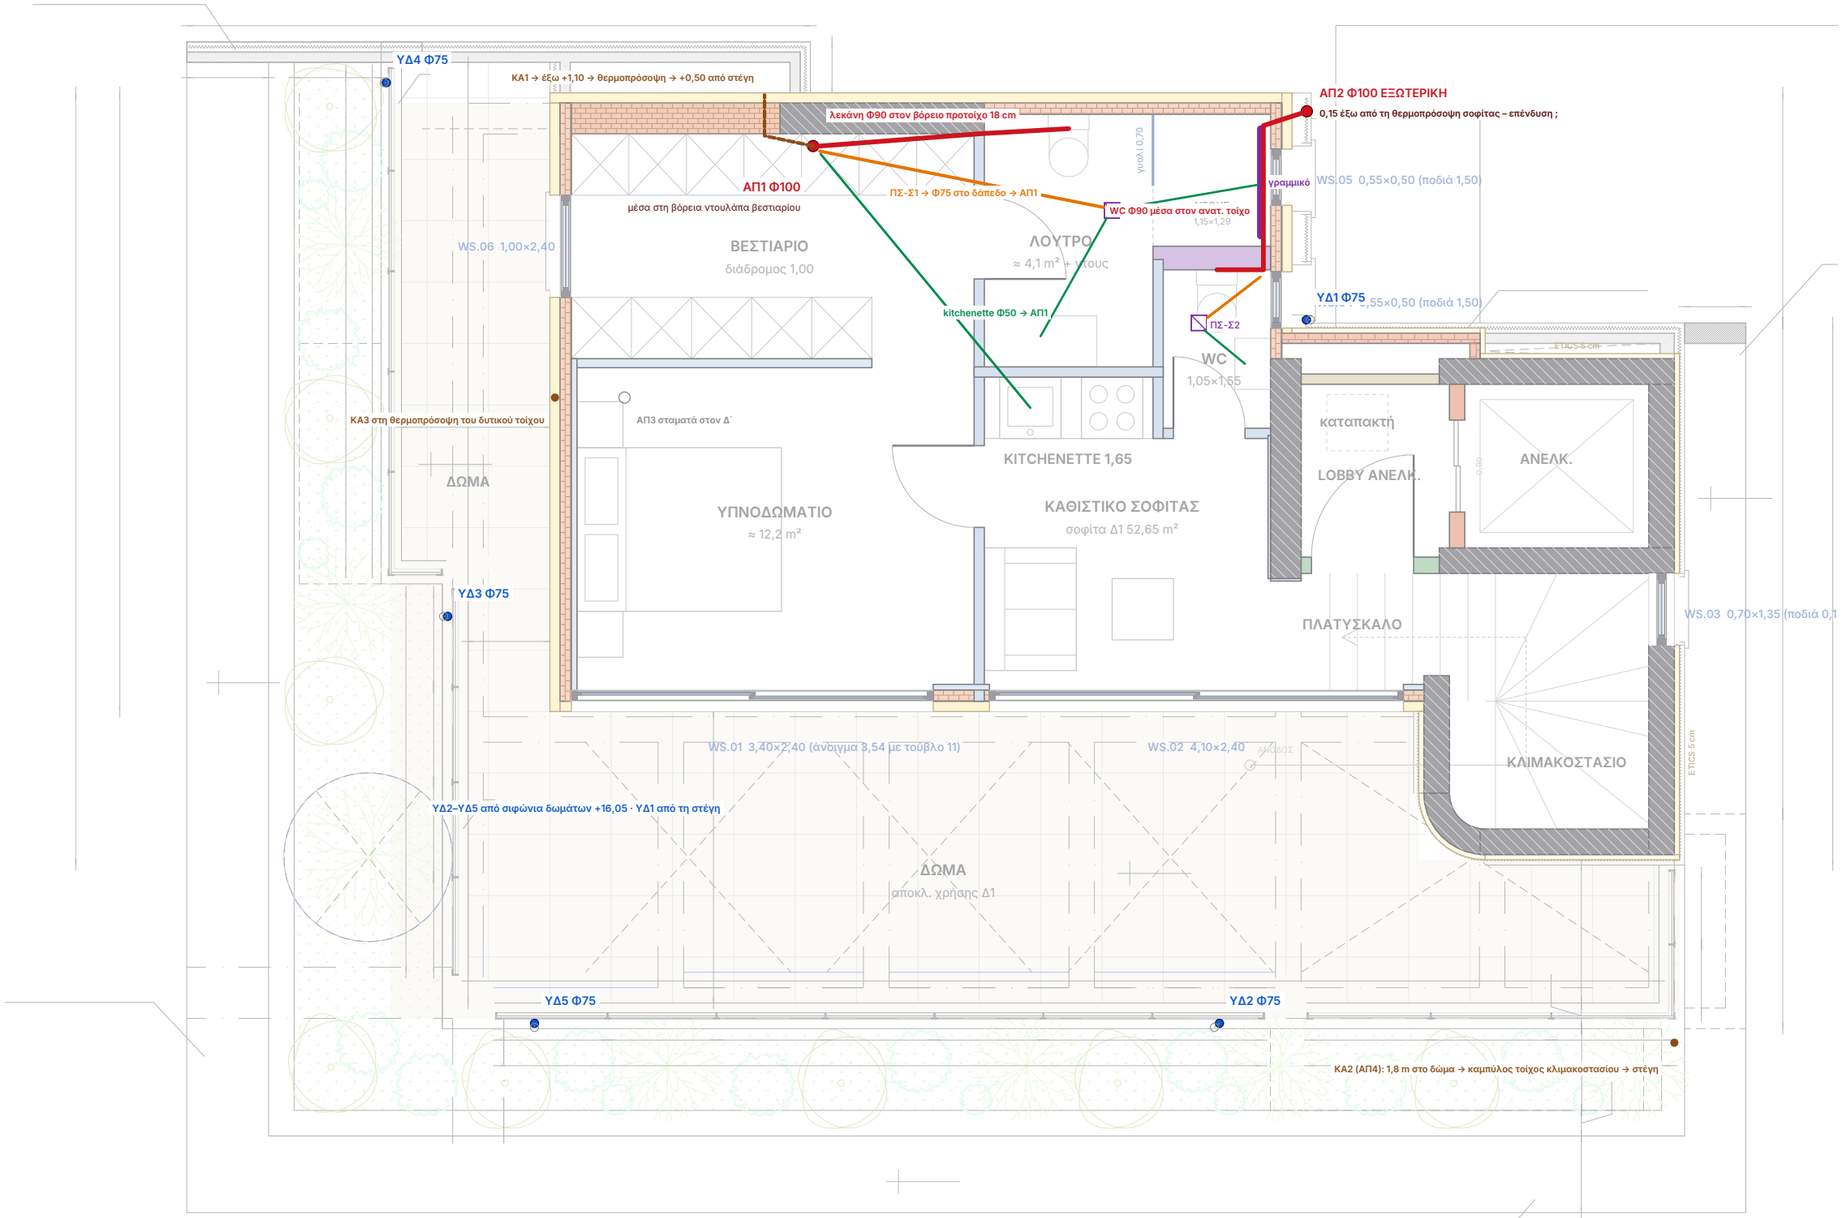

B

ΥΠΟΜΝΗΜΑ

- Στήλη λυμάτων ΑΠ (Φ100 / ΑΠ4 Φ75) · αερισμός συνεχίζει
- Θέση R12 όπου μετακινήθηκε (διακεκομμένη)
- Λεκάνη → στήλη Φ90 / Φ100
- Ποτισόφωνο / σιφώνι → στήλη Φ50–Φ75
- Ντους / πλυντήριο Φ50 · νιπτήρας Φ40 · νεροχύτης Φ50
- Ποτισόφωνο ΠΣ (σιφώνι δαπέδου)
- Υδρορροή ΥΔ Φ75 μέσα στη θερμοπρόσοψη (αναμονή Φ125)
- Σιφώνι ομβρίων εξώστη · διακεκ. = πλευρική έξοδος
- Δοκός (Σ4/Σ5) – καμία οπή
- Αερισμός ΚΑ – βγαίνει έξω, ανεβαίνει στη θερμοπρόσοψη
- Γραμμικό σιφώνι ντους

ΣΗΜΕΙΩΣΕΙΣ ΣΟΦΙΤΑΣ – R14

1. Λουτρό + kitchenette → ΑΠ1 στη βόρεια ντουλάπα, WC → ΑΠ2 εξωτερική, όπως R12 ΑΠ-08.
2. Νέα σοφίτα R04: λουτρό ανατολικά του Κ2 → λεκάνη 2,5 m από την ΑΠ1 με Φ90 σε προτοίχο.
3. Η γωνία της σοφίτας είναι 0,19 m δυτικότερα από των ορόφων → η ΑΠ2 μένει 0,15 έξω από τη θερμοπρόσοψη.
4. Όλοι οι αερισμοί έξω (ΚΑ1, ΑΠ2, ΚΑ2, ΚΑ3) – κανένας σε οροφή.

ΕΡΓΟ	ΘΕΜΑ ΣΧΕΔΙΟΥ	ΒΑΣΗ	ΑΡ. ΣΧΕΔΙΟΥ
ΠΕΝΤΑΟΡΟΦΟ ΚΤΗΡΙΟ ΚΑΤΟΙΚΙΩΝ – ΑΡΓΥΡΟΥΠΟΛΗ Κωνσταντινουπόλεως 12 & Αγ. Βαρβάρας · Ο.Τ. 103-15 Εργοδότης: INTERKAT Α.Ε. · Κατασκευή: ARKAD Ι.Κ.Ε.	**ΣΟΦΙΤΑ – ΑΠΟΧΕΤΕΥΣΗ & ΑΕΡΙΣΜΟΙ** Λύση R12 στις νέες τοιχοποιίες · λύματα · αερισμοί · όμβρια ΣΟΦΙΤΑ – Δ1 πάνω επίπεδο	R12 ΑΠ-08 · τοιχοποιίες σοφίτας R04	**ΑΠ-05** **Κλίμακα 1:60 · A3** 10/11/2026 · R14

ΑΛΛΑΓΕΣ R12 → R14 (μόνο λόγω νέων τοιχοποιιών)

Στοιχείο	R12	R14	Λόγος
ΑΠ1	4,83 / 0,93 στη ντουλάπα ΝΤ1	4,925 / 0,92 μέσα στον Τ7-01	λουτρό +10 cm (R18): ο Τ7-01 πήγε στο 4,80–5,05
ΑΠ1 ισόγειο	προτοίχος λουτρού ΙΣ1 (λουτρό 1,70 → 1,50)	2×45° στην οροφή λουτρού → Τ7-01 ισογείου 4,55	ο Τ7-01 ισογείου είναι στο 4,42–4,67
ΑΠ3	3,08 / 3,38 μέσα στον Τ7-02	ίδια	ο Τ7-02 τελειώνει στο 3,15 – χωράει
ΑΠ3 ισόγειο	2×45° → ντουλάπα 3,15 / 3,95	2×45° → ντουλάπα 3,15 / 4,70	νέα ντουλάπα Υπν.1 ισογείου 4,25–4,85
ΑΠ2	9,79 / 0,72	9,755 / 0,58	στο 0,72 έπεφτε στο στηθαίο εξώστη Υπν.2 (9,80–11,45 × 0,65–0,85)
ΑΠ4	13,35 / 9,69 κενό καμπύλης	ίδια · κουτί ισογείου 12,92 / 8,97	το κενό υπάρχει στο R25· γωνία εισόδου νέου ισογείου
ΥΔ3	1,31 / 5,52	1,35 / 5,52	μέσα στη θερμοπρόσοψη του Τ1-12, έξω από το τοιχείο εξώστη
ΥΔ1 · ΥΔ2 · ΥΔ4 · ΥΔ5	θερμοπρόσοψη	ίδιες (±5 cm)	επιβεβαιώθηκαν στις νέες παρειές
Πτώσεις ισογείου	4,86/2,00 · 7,82/5,28 · 9,17/7,92	4,55/2,00 · 9,27/5,35 · 9,30/8,10	νέο λουτρό, WC και κουζίνα ισογείου R13
Πλυντήριο	ΠΣ2 λουτρού γονέων	ίδιο – από τη νέα θέση στο χωλ μέσα από τον Τ2Α-01	πλυντήριο στο 3,30–3,90
Σοφίτα	λουτρό → ΑΠ1 · WC → ΑΠ2	ίδια – Φ90 2,5 m στον βόρειο προτοίχο	νέα σοφίτα R04: λουτρό ανατολικά του Κ2

ΠΡΟΤΑΣΕΙΣ ΒΕΛΤΙΩΣΗΣ – απάντησε με τον αριθμό (π.χ. «1 ΟΚ, 3 όχι»)

Νο	Θέμα	Πρόταση	Ερώτηση
1	ΑΠ3 στο ισόγειο	Αντί για σόφιτο 1,3 m στο Υπν.1, κουτί 20×20 στη θέση 3,08 / 3,38 μέσα στη γωνία ντουλάπας–τοίχου ισογείου.	Σόφιτο ή κουτί;
2	ΑΠ2 στη σοφίτα	Η σοφίτα συνδέεται στην ΑΠ1 με μόλο WC Φ32 και καταργείται η ΑΠ2. Αλλιώς επένδυση της ΑΠ2 στο δώμα.	Κρατάμε την ΑΠ2;
3	Ντους γονέων	Το ΠΣ2 πάει δίπλα στο γυαλί (1,25 / 4,30): ντους Φ50 0,9 m αντί 2,4 m, και ΠΣ2 → ΑΠ3 Φ75 μέσα στον Τ7-02.	ΟΚ;
4	Κλίση ομβρίων +3,30	31 m με 0,5 % είναι οριακό για φύλλα. Πρόταση 1 % (πτώση 0,31 m) ή δεύτερη κάθοδος στη ΒΔ γωνία.	Ποιο;
5	Ύψος υπογείου	Ο συλλεκτήρας δίνει 2,16 πάνω από Θ.Σ.Υ. 3/4. Πρόταση: ο νότιος κλάδος κολλητά στο δυτικό τοιχείο (x −1,10).	ΟΚ;
6	Ηχομόνωση στηλών	ΑΠ1 και ΑΠ3 περνούν δίπλα σε υπνοδωμάτια: ηχομονωτικός σωλήνας τύπου PP 3 στρώσεων αντί U-PVC.	ΟΚ;
7	Υδρορροές στη θερμοπρόσοψη	Φ75 σε ETICS 10 cm αφήνει 2,5 cm μόνωση: τοπικά ETICS 12 cm ή υδρορροή Φ63.	Ποιο;
8	ΑΠ4 κουζίνες	Φ75 επαρκεί για 4 κουζίνες. Πρόταση Φ90 για λίπη, ίδια θέση στο κενό της καμπύλης.	Φ75 ή Φ90;