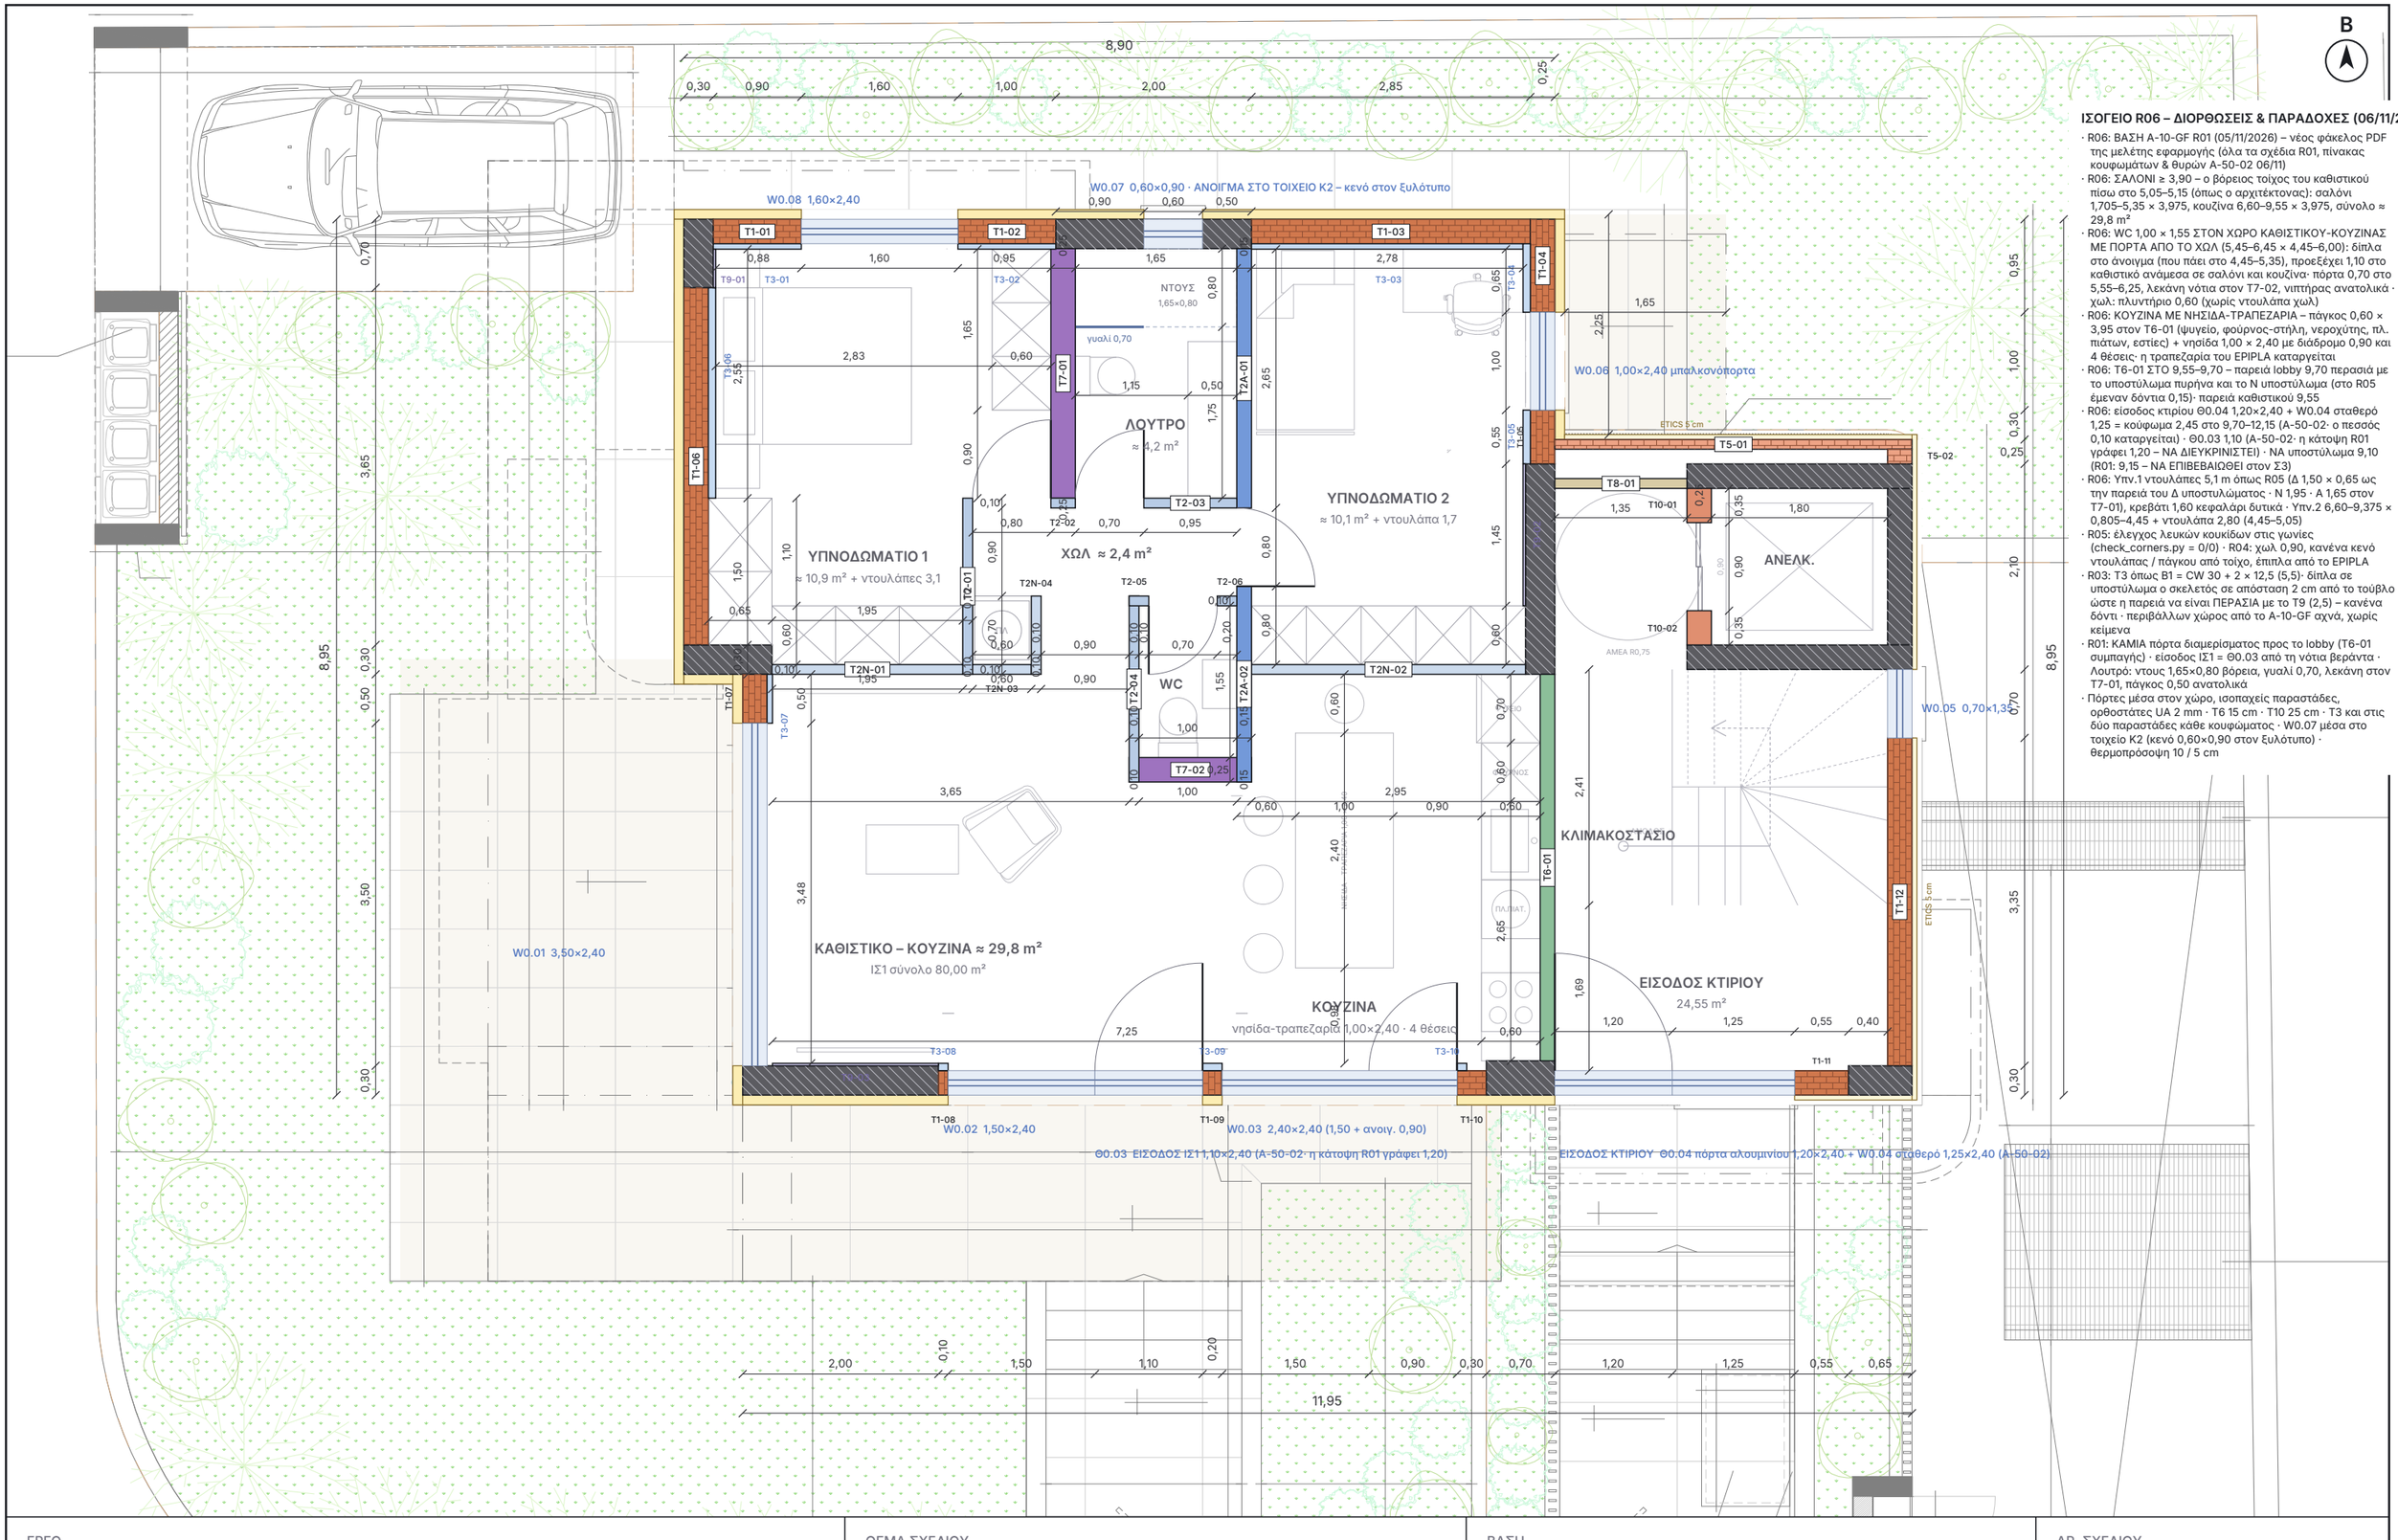


ΙΣΟΓΕΙΟ R06 – ΔΙΟΡΘΩΣΕΙΣ & ΠΑΡΑΔΟΧΕΣ (06/11/2026)


- R06: ΒΑΣΗ A-10-GF R01 (05/11/2026) – νέος φάκελος PDF της μελέτης εφαρμογής (όλα τα σχέδια R01, πίνακας κουφωμάτων & θυρών A-50-02 06/11)
- R06: ΣΑΛΟΝΙ ≥ 3,90 – ο βόρειος τοίχος του καθιστικού πίσω στο 5,05–5,15 (όπως ο αρχιτέκτονας): σαλόνι 1,705–5,35 × 3,975, κουζίνα 6,60–9,55 × 3,975, σύνολο ≈ 29,8 m²
- R06: WC 1,00 × 1,55 ΣΤΟΝ ΧΩΡΟ ΚΑΘΙΣΤΙΚΟΥ-ΚΟΥΖΙΝΑΣ ΜΕ ΠΟΡΤΑ ΑΠΟ ΤΟ ΧΩΛ (5,45–6,45 × 4,45–6,00): δίπλα στο άνοιγμα (που πάει στα 4,45–5,35), προεξέχει 1,10 στο καθιστικό ανάμεσα σε σαλόνι και κουζίνα· πόρτα 0,70 στο 5,55–6,25, λεκάνη νότια στον T7-02, νιπτήρας ανατολικά · χωλ: πλυντήριο 0,60 (χωρίς ντουλάπα χωλ)
- R06: ΚΟΥΖΙΝΑ ΜΕ ΝΗΣΙΔΑ-ΤΡΑΠΕΖΑΡΙΑ – πάγκος 0,60 × 3,95 στον T6-01 (ψυγείο, φούρνος-στήλη, νεροχύτης, πλ. πιάτων, εστίες) + νησίδα 1,00 × 2,40 με διάδρομο 0,90 και 4 θέσεις· η τραπεζαρία του EPIPLA καταργείται
- R06: T6-01 ΣΤΟ 9,55–9,70 – παρειά lobby 9,70 περασιά με το υποστύλωμα πυρήνα και το Ν υποστύλωμα (στο R05 έμεναν δόντια 0,15)· παρειά καθιστικού 9,55
- R06: είσοδος κτιρίου Θ0.04 1,20×2,40 + W0.04 σταθερό 1,25 = κούφωμα 2,45 στο 9,70–12,15 (A-50-02· ο πεσσός 0,10 καταργείται) · Θ0.03 1,10 (A-50-02· η κάτοψη R01 γράφει 1,20 – ΝΑ ΔΙΕΥΚΡΙΝΙΣΤΕΙ) · ΝΑ υποστύλωμα 9,10 (R01: 9,15 – ΝΑ ΕΠΙΒΕΒΑΙΩΘΕΙ στον Σ3)
- R06: Υπν.1 ντουλάπες 5,1 m όπως R05 (Δ 1,50 × 0,65 ως την παρειά του Δ υποστυλώματος · Ν 1,95 · Α 1,65 στον T7-01), κρεβάτι 1,60 κεφαλάρι δυτικά · Υπν.2 6,60–9,375 × 0,805–4,45 + ντουλάπα 2,80 (4,45–5,05)
- R05: έλεγχος λευκών κουκίδων στις γωνίες (check_corners.py = 0/0) · R04: χωλ 0,90, κανένα κενό ντουλάπας / πάγκου από τοίχο, έπιπλα από το EPIPLA
- R03: T3 όπως B1 = CW 30 + 2 × 12,5 (5,5)· δίπλα σε υποστύλωμα ο σκελετός σε απόσταση 2 cm από το τούβλο ώστε η παρειά να είναι ΠΕΡΑΣΙΑ με το Τ9 (2,5) – κανένα δόντι · περιβάλλων χώρος από το A-10-GF αχνά, χωρίς κείμενα
- R01: ΚΑΜΙΑ πόρτα διαμερίσματος προς το lobby (T6-01 συμπαγής) · είσοδος ΙΣ1 = Θ0.03 από τη νότια βεράντα · Λουτρό: ντους 1,65×0,80 βόρεια, γυαλί 0,70, λεκάνη στον T7-01, πάγκος 0,50 ανατολικά
- Πόρτες μέσα στον χώρο, ισοπαχείς παραστάδες, ορθοστάτες UA 2 mm · T6 15 cm · T10 25 cm · T3 και στις δύο παραστάδες κάθε κουφώματος · W0.07 μέσα στο τοιχείο Κ2 (κενό 0,60×0,90 στον ξυλότυπο) · θερμοπρόσοψη 10 / 5 cm

ΕΡΓΟ	ΘΕΜΑ ΣΧΕΔΙΟΥ	ΒΑΣΗ	ΑΡ. ΣΧΕΔΙΟΥ
ΠΕΝΤΑΟΡΟΦΟ ΚΤΗΡΙΟ ΚΑΤΟΙΚΙΩΝ – ΑΡΓΥΡΟΥΠΟΛΗ Κωνσταντινουπόλεως 12 & Αγ. Βαρβάρας · Ο.Τ. 103-15 Εργοδότης: INTERKAT Α.Ε. · Κατασκευή: ARKAD Ι.Κ.Ε.	**ΚΑΤΟΨΗ ΤΟΙΧΟΠΟΙΙΩΝ – ΙΣΟΓΕΙΟΥ** Είδη τοιχοποιιών · διαστάσεις χάραξης · κουφώματα · εξώστες ΙΣΟΓΕΙΟ – ΙΣ1	Βάση: A-10-GF R01 (05/11/2026, Drive) · Σ3_ΕΦ · κανόνες B1 R20	**T-01** **Κλίμακα 1:60 · A3** 06/11/2026 · R06


T1 Εξωτερική οπτοπλινθοδομή

1:4

πάχος 25 cm

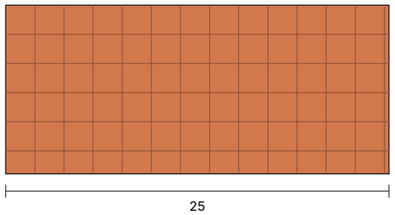

θερμομονωτικό τούβλο κάθετων οπών 25 cm · θερμοπρόσοψη 10 cm έξω · επένδυση T3 μέσα όπου σημειώνεται

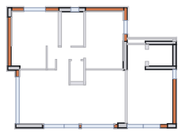


Τοίχοι: T1-01, T1-02, T1-03, T1-04, T1-05, T1-06, T1-07, T1-08, T1-09, T1-10, T1-11, T1-12

Μήκος 15,10 m · επιφάνεια ≈ 45,3 m²


T5 Οπτοπλινθοδομή πυρήνα

1:4

πάχος 10 cm

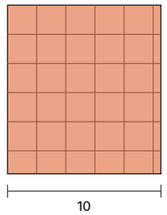

θερμομονωτικό τούβλο κάθετων οπών 10 cm · γύρω από τον πυρήνα (ανελκυστήρας – ηλεκτροστάσιο)

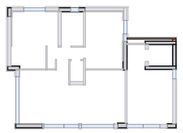


Τοίχοι: T5-01, T5-02

Μήκος 3,90 m · επιφάνεια ≈ 11,7 m²


T10 Μέτωπο ανελκυστήρα

1:4

πάχος 25 cm

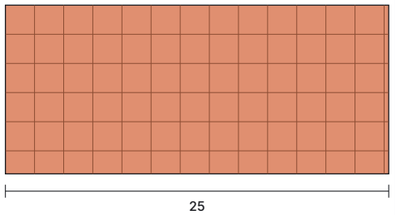

θερμομονωτικό τούβλο κάθετων οπών 25 cm · μέτωπο φρεατίου εκατέρωθεν της πόρτας 0,90 · ισοπαχές με τα τοιχεία 25 του φρεατίου (Σ5), περασιά και στις δύο παρειές, ώστε να κάθεται σωστά η κάσα της πόρτας ορόφου · θέση πόρτας προς επιβεβαίωση από τον προμηθευτή

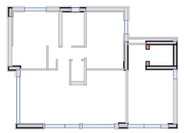


Τοίχοι: T10-01, T10-02

Μήκος 0,70 m · επιφάνεια ≈ 2,1 m²


T3 Επένδυση τοίχου

1:4

πάχος 5,5 cm

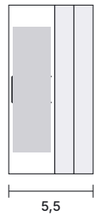

σκελετός 30 · 2 × γυψοσανίδα 12,5 · στις εσωτερικές παρειές των T1 – ΟΧΙ όπου πλακάκι ή ντουλάπα, ΟΧΙ στα έρκερ

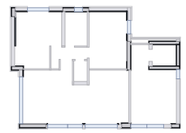

Τοίχοι: T3-01, T3-02, T3-03, T3-04, T3-05, T3-06, T3-07, T3-08, T3-09, T3-10

Μήκος 8,98 m · επιφάνεια ≈ 26,9 m²


T9 Επένδυση υποστυλώματος

1:4

πάχος 2,5 cm



κόλλα + 1 × γυψοσανίδα 12,5 (ένα φύλλο) · στις παρειές υποστυλωμάτων μέσα στα διαμερίσματα – ΟΧΙ όπου πλακάκι ή ντουλάπα

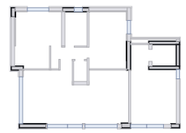


Τοίχοι: T9-01, T9-02, T9-03

Μήκος 3,54 m · επιφάνεια ≈ 10,6 m²


T2 Χώρισμα γυψοσανίδας

1:4

πάχος 10 cm

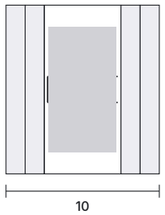

2 × γυψοσανίδα 12,5 · σκελετός CW 50 · 2 × γυψοσανίδα 12,5 · εσωτερικά χωρίσματα · ανθυγρή γυψοσανίδα στην πλευρά των λουτρών · ανοίγματα πορτών με ορθοστάτες UA 50 (2 mm)

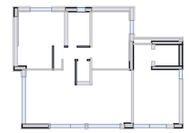


Τοίχοι: T2-01, T2-02, T2-03, T2-04, T2-05, T2-06

Μήκος 5,30 m · επιφάνεια ≈ 15,9 m²


T2N Χώρισμα γυψ. – πλευρά ντουλάπας

1:4

πάχος 8,75 cm

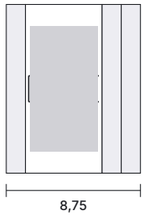

1 × γυψοσανίδα 12,5 (πλευρά ντουλάπας) · σκελετός CW 50 · 2 × γυψοσανίδα 12,5 · όπου η μία παρειά βλέπει σε ντουλάπα: ένα φύλλο αρκεί (κανόνας R15)

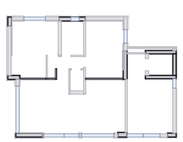


Τοίχοι: T2N-01, T2N-02, T2N-03, T2N-04

Μήκος 6,15 m · επιφάνεια ≈ 18,5 m²


T2A Χώρισμα γυψοσανίδας 15

1:4

πάχος 15 cm

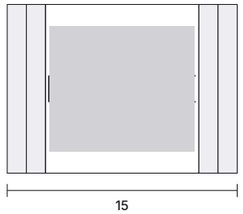

2 × γυψοσανίδα 12,5 · σκελετός CW 100 + πετροβάμβακας · 2 × γυψοσανίδα 12,5 · λουτρό γονέων / χωλ · υπνοδωμάτια · ανοίγματα πορτών με ορθοστάτες UA 100 (2 mm)

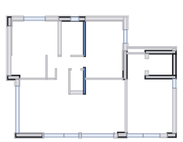


Τοίχοι: T2A-01, T2A-02

Μήκος 4,65 m · επιφάνεια ≈ 14,0 m²

T7 Τοίχος λεκάνης WC

1:4

πάχος 25 cm

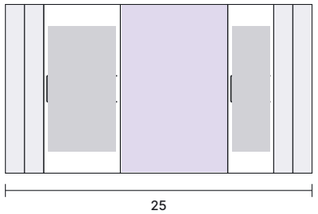

2 × γυψοσανίδα 12,5 · σκελετός CW 50 · κενό 12 cm (καζανάκι γυψοσανίδας στον σκελετό + κατακόρυφη στήλη Ø110, έξοδος Ø90) · σκελετός CW 30 · 2 × γυψοσανίδα 12,5 · ΟΛΟΙ οι τοίχοι λεκανών · ανθυγρή προς το λουτρό · στην πλευρά ντουλάπας 1 φύλλο · ανοίγματα πορτών με ορθοστάτες UA 50 (2 mm)




Τοίχοι: T7-01, T7-02

Μήκος 3,80 m · επιφάνεια ≈ 11,4 m²


T6 Τοίχος κλιμακοστασίου

1:4

πάχος 15 cm

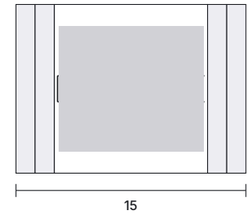

2 × γυψοσανίδα 12,5 πυράντοχη · σκελετός CW 100 + πετροβάμβακας · 2 × γυψοσανίδα 12,5 πυράντοχη · προς κοινόχρηστους χώρους · 15 cm · άνοιγμα πόρτας εισόδου (ασφαλείας) με ορθοστάτες UA 100 (2 mm) κατά Knauf

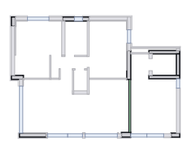


Τοίχοι: T6-01

Μήκος 3,95 m · επιφάνεια ≈ 11,8 m²


T8 Τοίχος shaft

1:4

πάχος 10 cm

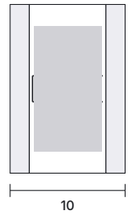

πλαίσιο + ανοιγόμενα φύλλα γυψοσανίδας · μέτωπο shaft ηλεκτρολογικών

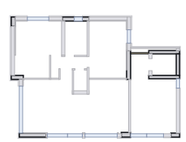

Τοίχοι: T8-01

Μήκος 1,35 m · επιφάνεια ≈ 4,1 m²

Επιφάνειες ενδεικτικές: μήκος × ύψος 3,00 m (τελικό δάπεδο – πλάκα) – οι τοίχοι ορίζονται μεταξύ ανοιγμάτων, χωρίς αφαίρεση κασών. T3 = επένδυση στην εσωτερική παρειά των T1 · T9 = περίμετρος υποστυλώματος × ύψος. R15: T2N = 1 φύλλο στην πλευρά ντουλάπας (T2N-01, T2N-02) · T7-01 1 φύλλο προς Υπν.1.

ΕΡΓΟ

ΠΕΝΤΑΟΡΟΦΟ ΚΤΗΡΙΟ ΚΑΤΟΙΚΙΩΝ – ΑΡΓΥΡΟΥΠΟΛΗ
Κωνσταντινουπόλεως 12 & Αγ. Βαρβάρας · Ο.Τ. 103-15
Εργοδότης: INTERKAT Α.Ε. · Κατασκευή: ARKAD Ι.Κ.Ε.

ΘΕΜΑ ΣΧΕΔΙΟΥ

ΕΙΔΗ ΤΟΙΧΟΠΟΙΙΩΝ – ΙΣΟΓΕΙΟΥ
Είδη τοιχοποιιών · ΙΣΟΓΕΙΟ – ΙΣ1
τομές 1:4 · μήκη – εμβαδά ανά είδος

ΒΑΣΗ

Βάση: κάτοψη τοιχοποιιών T-01 · κάτοψη A-10-GF

ΑΡ. ΣΧΕΔΙΟΥ

T-02
Κλίμακα 1:4 · A3
06/11/2026 · R06

ΠΡΟΜΕΤΡΗΣΗ ΤΟΙΧΟΠΟΙΙΩΝ – ΙΣΟΓΕΙΟ – ΙΣ1

τετραγωνικά ανά τυπολογία τοίχου · H = 3,00 m (τελικό δάπεδο – κάτω παρειά πλάκας) · μήκη στον άξονα, χωρίς αφαίρεση κουφωμάτων · R06

	Τύπος	Περιγραφή	Πάχος cm	Τοίχοι	Μήκος m	Επιφάνεια m²
ΤΟΥΒΛΑ						
	T1	Εξωτερική οπτοπλινθοδομή	25	12	15,10	**45,3**
	T5	Οπτοπλινθοδομή πυρήνα	10	2	3,90	**11,7**
	T10	Μέτωπο ανελκυστήρα	25	2	0,70	**2,1**
	Σύνολο τουβλα					**59,1 m²**
ΧΩΡΙΣΜΑΤΑ ΓΥΨΟΣΑΝΙΔΑΣ						
	T2	Χώρισμα γυψοσανίδας	10	6	5,30	**15,9**
	T2N	Χώρισμα γυψ. – πλευρά ντουλάπας	8,8	4	6,15	**18,5**
	T2A	Χώρισμα γυψοσανίδας 15	15	2	4,65	**14,0**
	T7	Τοίχος λεκάνης WC	25	2	3,80	**11,4**
	T6	Τοίχος κλιμακοστασίου	15	1	3,95	**11,8**
	T8	Τοίχος shaft	10	1	1,35	**4,1**
	Σύνολο χωρισματα γυψοσανιδας					**75,6 m²**
ΕΠΕΝΔΥΣΕΙΣ						
	T3	Επένδυση τοίχου	5,5	10	8,98	**26,9**
	T9	Επένδυση υποστυλώματος	2,5	3	3,54	**10,6**
	Σύνολο επενδυσεις					**37,5 m²**
	ΣΥΝΟΛΟ ΤΟΙΧΟΠΟΙΙΩΝ ΙΣ1					**172,2 m²**

ΘΕΡΜΟΠΡΟΣΟΨΗ (ETICS)

10 cm στις όψεις των διαμερισμάτων · 5 cm στο κλιμακοστάσιο / πυρήνα · ύψος 3,20 m (με τη μετώπη πλάκας) · καθαρά = όψη − κουφώματα + λαμπάδες/ανώφλια

Ζώνη	Μήκος όψης m	Μικτά m²	Κουφώματα m²	Λαμπάδες m²	Καθαρά m²
ETICS 10 cm – διαμερίσματα	29,40	94,1	−27,2	+5,9	**72,8**
ETICS 5 cm – κλιμακοστάσιο / πυρήνας	14,05	45,0	−6,8	+2,0	**40,2**
Σύνολο ETICS					**113,0 m²**

ΣΗΜΕΙΩΣΕΙΣ ΚΑΤΟΨΗΣ

• Θέσεις τοίχων και ανοιγμάτων κατά την κάτοψη ισογείου A-10-GF R01 (EDGE, μελέτη εφαρμογής, αναθεώρηση R01 05/11/2026, φάκελος PDF της μελέτης εφαρμογής στο Drive του έργου) με τους κανόνες του B1 R20 και τις αλλαγές R01–R06 του Γιάννη. Διαστάσεις στο τούβλο / μπετό και στις παρειές της γυψοσανίδας, χωρίς τη θερμοπρόσοψη. Υποστυλώματα / τοιχεία από τα μαύρα γεμίσματα του A-10-GF – ταυτίζονται με τον ξυλότυπο Σ3 (να επιβεβαιωθούν στον Σ3 πριν τη χάραξη· το R01 δείχνει το N υποστύλωμα στο 9,15–9,45 αντί 9,10–9,45 – εδώ 9,10 όπως B1).

• ΤΙ ΑΛΛΑΞΕ ΣΤΟ A-10-GF R01 (05/11/2026) σε σχέση με το R00 (23/07/2026): μόνο ετικέτες θυρών και μικρά στοιχεία – Θ0.03 γράφεται «1,20×2,40» (η γεωμετρία της κάτοψης και ο πίνακας A-50-02 λένε 1,10 → κρατήθηκε 1,10, ΝΑ ΔΙΕΥΚΡΙΝΙΣΤΕΙ), είσοδος κτιρίου Θ0.04 1,20 (ήταν 1,00) + W0.04 1,25 (ήταν 1,20), πύλες περίφραξης Θ0.02 / Θ0.04, γκαραζόπορτα Θ0.01 2,50×2,10, N υποστύλωμα 9,15, διακεκομμένες προβολές στο lobby και στη ΒΑ βεράντα. Οι τοίχοι του διαμερίσματος δεν άλλαξαν.

• Τ3 ΠΕΡΑΣΙΑ (R03, όπως B1): Τ3 = σκελετός CW 30 + 2 × γυψοσανίδα 12,5 (5,5 cm). Τα υποστυλώματα (30) προεξέχουν 5 cm από την εσωτερική παρειά του τούβλου (25) και παίρνουν κολλητή γυψοσανίδα Τ9 2,5 cm· όπου η Τ3 συνεχίζει δίπλα σε υποστύλωμα, ο σκελετός CW 30 στήνεται σε απόσταση 2 cm από το τούβλο ώστε η παρειά της γυψοσανίδας να είναι στο ίδιο επίπεδο με το Τ9: Τ3-06 (παρειά 1,125 = Τ9-01), Τ3-04/Τ3-05 (9,375 = Τ9-02), Τ3-08/09/10 (9,125 = Τ9-03). Αλλού η Τ3 κολλητά στο τούβλο: Β 0,805 · Δ καθιστικού 1,705. Όπου πλακάκι, ντουλάπα ή πάγκος: χωρίς Τ3 / Τ9 (γυμνό τούβλο / μπετό).

• ΣΑΛΟΝΙ ≥ 3,90 (R06 – Γιάννης: «το σαλόνι δεν δουλεύει στο 3,5, θέλει 3,9 και πάνω σίγουρα»): ο βόρειος τοίχος του καθιστικού γυρίζει στο y 5,05–5,15 (όπως ο αρχιτέκτονας και το R04): T2N-01 (1,70–3,65, ντουλάπα Υπν.1) · T2-01 · T2N-03 (3,75–4,35, πλυντήριο) · T2N-04 (4,35–4,45) · άνοιγμα 0,90 (4,45–5,35) · WC (5,35–6,60, προεξέχει ως 6,25) · T2N-02 (6,60–9,40, ντουλάπα Υπν.2). Σαλόνι 1,705–5,35 × 5,15–9,125 (3,65 × 3,975 ≈ 14,5 m²) και κουζίνα 6,60–9,55 × 5,15–9,125 (2,95 × 3,975) με βάθος 3,975 και τα δύο· μόνο η λωρίδα 5,35–6,60 (η διαδρομή από την πόρτα Θ0.03) έχει τον όγκο του WC. Σύνολο ≈ 29,8 m². Το R05 (τοίχος στο 5,45–5,55, σαλόνι 3,575, WC στο χωλ) απορρίφθηκε.

• WC ΣΤΟΝ ΧΩΡΟ ΚΑΘΙΣΤΙΚΟΥ-ΚΟΥΖΙΝΑΣ ΜΕ ΠΟΡΤΑ ΑΠΟ ΤΟ ΧΩΛ (R06 – Γιάννης: «βάλε το WC στην κουζίνα, όχι στο δωμάτιο· μπορείς να μπαίνεις από το χωλ, οκ, αλλά ναι, είναι στο καθιστικό-κουζίνα χώρο»): WC 5,45–6,45 × 4,45–6,00 (1,00 × 1,55 ≈ 1,55 m²) δίπλα στο άνοιγμα χωλ–καθιστικό, που μετακινείται από 5,55–6,45 στο 4,45–5,35 (0,90, απέναντι από την πόρτα του Υπν.1). Πόρτα 0,70 στον νότιο τοίχο του χωλ (5,55–6,25, παραστάδες Τ2-05 / Τ2-06 0,20 / 0,20, μεντεσές δυτικά 5,55, ανοίγει μέσα και διπλώνει στον Τ2-04). Λεκάνη στον Τ7-02 νότια (25, 5,35–6,60 × 6,00–6,25, άξονας x 5,85), νιπτήρας 0,50 × 0,35 στον Τ2A-02 ανατολικά (y 5,00–5,50). Τοίχοι: Τ2-04 δυτικά (5,35–5,45 × 4,35–6,25 = ανατολική παραστάδα του ανοίγματος), Τ2-05 / Τ2-06 βόρεια, Τ2A-02 ανατολικά (15, ως 6,25), Τ7-02 νότια. Ο όγκος του WC (5,35–6,60 × 5,15–6,25) προεξέχει 1,10 στο καθιστικό, μπροστά του περνάει η διαδρομή Θ0.03 → άνοιγμα (x 4,45–5,35). Στο χωλ μένει μόνο το πλυντήριο 0,60 × 0,70 (3,75–4,35) – η ντουλάπα χωλ 1,10 χάνεται. Όλοι οι τοίχοι του WC ανθυγρή γυψοσανίδα από μέσα.

• ΧΩΛ 2,70 × 0,90 (y 3,45–4,35, όπως R04): βόρεια πόρτες Υπν.1 (3,75–4,55) και λουτρού (4,80–5,50), ανατολικά πόρτα Υπν.2 (y 3,45–4,25), νότια: εσοχή πλυντηρίου 0,60 × 0,70 (3,75–4,35 × 4,35–5,05), T2N-04 (4,35–4,45), άνοιγμα προς καθιστικό 4,45–5,35 (0,90), T2-04 (5,35–5,45), πόρτα WC 5,55–6,25, T2A-02. Τοίχοι που βλέπουν σε ντουλάπα / πλυντήριο: 1 φύλλο (T2N-01…04).

• ΚΟΥΖΙΝΑ ΜΕ ΝΗΣΙΔΑ-ΤΡΑΠΕΖΑΡΙΑ (R06 – Γιάννης: «δούλεψε την κουζίνα με νησίδα-τραπεζαρία»): πάγκος 0,60 × 3,95 στον Τ6-01 (x 8,95–9,55, y 5,15–9,10) όπως ο αρχιτέκτονας, από βορρά: ψυγείο 0,70 × 0,65 (5,15–5,85, στη γωνία), στήλη φούρνου 0,60 (5,85–6,45), νεροχύτης 0,80 (6,45–7,25), πλυντήριο πιάτων 0,60 (7,25–7,85), πάγκος 0,35, εστίες 0,60 (8,20–8,80, απορροφητήρας στον Τ6-01), πάγκος 0,30 ως το N υποστύλωμα. ΝΗΣΙΔΑ 1,00 × 2,40 (x 7,05–8,05, y 5,75–8,15) παράλληλη στον πάγκο: διάδρομος εργασίας 0,90 (8,05–8,95), είσοδος στον διάδρομο από νότια (0,975 ως τον τοίχο), 4 θέσεις (3 δυτικά με προεξοχή πάγκου 0,35–0,40 για τα γόνατα, νότια από τον T7-02 του WC + 1 στο βόρειο άκρο, το κενό 0,60 ως τον τοίχο δεν είναι διάδρομος) = η νησίδα είναι και η τραπεζαρία. Η τραπεζαρία με τις 6 καρέκλες του EPIPLA καταργείται· ύψος νησίδας / θέση νεροχύτη–εστιών τελικά από τον μελετητή κουζίνας. Πίσω από τον πάγκο χωρίς επένδυση (Τ6-01 γυψοσανίδα, N υποστύλωμα γυμνό)· η Τ3-10 μόνο στην παραστάδα του W0.03 (8,70–8,80).

• Τ6-01 ΣΤΟ 9,55–9,70 (R06 – Γιάννης: «δες καλύτερα τον τοίχο Τ6-01, τον έχεις βάλει σε λάθος θέση»): ο αρχιτέκτονας έχει τοίχο 30 στο 9,40–9,70· ο Τ6 15 cm (R01) είχε μπει στο 9,40–9,55 με σταθερή την παρειά του διαμερίσματος και άφηνε στο lobby δύο δόντια 0,15 (υποστύλωμα πυρήνα 9,70 στο 3,00–5,15, τοίχος 9,55, N υποστύλωμα 9,70 στο 9,10–9,45). Τώρα στο 9,55–9,70: η παρειά του lobby 9,70 είναι μία ευθεία από το φρεάτιο ως την είσοδο, και η παρειά του καθιστικού 9,55 είναι επίσης ευθεία (το υποστύλωμα πυρήνα τελειώνει στο 5,15 = γραμμή του βόρειου τοίχου, το N υποστύλωμα από 9,10 μέσα στον νότιο τοίχο). Το διαμέρισμα κερδίζει 0,15 (πάγκος κουζίνας 8,95–9,55).

• Υπν.1 (R06): κύριος χώρος 1,125–4,55 × 0,805–3,35 (3,425 × 2,545) + εσοχή 1,70–3,65 × 3,35–4,45 (≈ 10,9 m² καθαρά + ντουλάπες 3,1 m²). Ντουλάπες 0,60 χωνευτές, 5,1 m όπως R05: ΔΥΤΙΚΗ 1,05–1,70 × 3,35–4,85 (1,50, βάθος 0,65 από το γυμνό τούβλο ως την παρειά 1,70 του Δ υποστυλώματος – το μέτωπό της και η βόρεια παρειά του υποστυλώματος 4,85 είναι περασιά), ΝΟΤΙΑ 1,70–3,65 × 4,45–5,05 (1,95, ανάμεσα στο υποστύλωμα και τον Τ2-01), ΑΝΑΤΟΛΙΚΗ 3,95–4,55 × 0,805–2,45 (1,65 στον Τ7-01, 1 φύλλο πίσω της, τελειώνει 0,10 πριν το ανοιχτό φύλλο της πόρτας). Κρεβάτι 1,60 × 2,00 με κεφαλάρι στη δυτική επένδυση (στον βόρειο τοίχο είναι το W0.08 1,60 × 2,40), y 1,20–2,80, κομοδίνα 0,45 × 0,395 / 0,45 × 0,45, διάβαση προς την εσοχή 0,55. Πόρτα 0,80 στο 3,75–4,55, μεντεσές 4,55, διπλώνει στον Τ7-01. Η Τ3-06 ως 3,35 (πίσω από τη δυτική ντουλάπα γυμνό τούβλο).

• ΛΟΥΤΡΟ 1,65 × 2,55 (x 4,80–6,45 · y 0,80–3,35): Τ7-01 λεκάνης δυτικά (σταθερή η παρειά Υπν.1 4,55), Τ2A-01 ανατολικά 6,45–6,60 (A-10-GF), ντους 1,65×0,80 βόρεια (y 0,80–1,60) με γυάλινο διαχωριστικό 0,70 στο y 1,60 από τον Τ7-01, λεκάνη στον Τ7-01 (y 2,10), πάγκος 0,50 στον ανατολικό τοίχο (5,95–6,45 × 1,75–3,35), πόρτα 0,70 στο 4,80–5,50 (μεντεσές 5,50). W0.07 0,60×0,90 μέσα στο τοιχείο K2 (x 5,50–6,10): κενό στον ξυλότυπο από τώρα (ποδιά +1,50).

• Υπν.2 (6,60–9,375 × 0,805–4,45 ≈ 10,1 m²): ντουλάπα 6,60–9,40 × 4,45–5,05 (2,80), πόρτα 0,80 από το χωλ στο y 3,45–4,25 (Τ2A-01 / Τ2A-02, μεντεσές 4,25), W0.06 1,00×2,40 μπαλκονόπορτα προς τη ΒΑ βεράντα (9,80–11,45 × 0,45–2,70, +0,45). Τ9-02 στο υποστύλωμα πυρήνα 3,00–4,45 περασιά με την Τ3-05.

• ΚΑΘΙΣΤΙΚΟ: δυτικός τοίχος Τ1-07 1,40–1,65 + Τ3-07 ως 1,705 περασιά με το ΝΔ τοιχείο (1,40) και την ανατολική παρειά του Δ υποστυλώματος (1,70)· W0.01 3,50×2,40 στο 5,65–9,15· Τ9-03 στο ΝΔ τοιχείο (παρειά 9,125) περασιά με Τ3-08 / Τ3-09. Καναπές, πολυθρόνα (0,45 δυτικότερα), τραπεζάκι, έπιπλο TV από το EPIPLA.

• ΠΥΡΗΝΑΣ: Τ5-01 10 cm σε όλο το μήκος 9,70–13,35 (A-10-GF) με επιστροφή Τ5-02 στο φρεάτιο· shaft Η/Μ εκτός Σ.Δ. στο y 2,85–3,15 × 9,70–11,05 (βάθος 0,30 όπως B1 – ο αρχιτέκτονας δείχνει μέτωπο 25 στο 3,00–3,25). Μέτωπο ανελκυστήρα Τ10-01/Τ10-02 25 cm, πόρτα 0,90 στο y 3,60–4,50. Κύκλος περιστροφής AMEA R0,75 (1,50) στο 9,70–11,20. Σκάλα 16 ριχτιών όπως B1. ΕΙΣΟΔΟΣ ΚΤΙΡΙΟΥ (R06, A-50-02 06/11): ενιαίο κούφωμα αλουμινίου 2,45 στο 9,70–12,15 = πόρτα Θ0.04 1,20×2,40 (9,70–10,90, μεντεσές δυτικά, ανοίγει μέσα) + σταθερό W0.04 1,25×2,40 (10,90–12,15)· ο πεσσός τούβλου 0,10 του R01 καταργείται (παραστάδα = N υποστύλωμα 9,70). Καμία πόρτα διαμερίσματος προς το lobby.

• ΚΟΥΦΩΜΑΤΑ (A-50-02 06/11/2026 + A-10-GF R01): W0.08 1,60×2,40 (2,00–3,60) · W0.07 0,60×0,90 (ποδιά 1,50) · W0.06 1,00×2,40 (1,45–2,45) · W0.01 3,50×2,40 δίφυλλο επάλληλο (5,65–9,15) · W0.02 1,45 σταθερό (3,50–5,00 – ο πίνακας λέει 145, η κάτοψη 1,50) · Θ0.03 πόρτα ΙΣ1 1,10×2,40 (5,00–6,10 – ο πίνακας 110, η ετικέτα της κάτοψης R01 1,20: ΝΑ ΔΙΕΥΚΡΙΝΙΣΤΕΙ) · W0.03 2,40 = 1,50 σταθερό + 0,90 ανοιγοανακλινόμενο (6,30–8,70) · Θ0.04 1,20 + W0.04 1,25 · W0.05 0,70×1,35. Πεσσοί 0,10 (3,40–3,50), 0,20 (6,10–6,30), 0,30 (8,70–9,00) όπως ο αρχιτέκτονας – ΠΡΟΣ ΑΠΟΦΑΣΗ αν ο 0,10 ενσωματωθεί στο κούφωμα. Τ3 και στις δύο παραστάδες.

• ΠΕΡΙΒΑΛΛΩΝ ΧΩΡΟΣ: κήπος αποκλειστικής χρήσης ΙΣ1 182,08 m², Θ.Σ.Ι.1, φυτεύσεις, βεράντες (+0,40 δυτικά, +0,45 νότια, ΒΑ), σκαλιά, πλατφόρμα AMEA, ράμπα, περίφραξη – αχνά από το A-10-GF R01, χωρίς κείμενα· δεν είναι σχέδιο κατασκευής του κήπου (ισχύουν A-10-GF / A-14-GF). Όλο το οικόπεδο στο Τ-04 (1:100).

• ΘΕΡΜΟΠΡΟΣΟΨΗ: 10 cm στο διαμέρισμα, 5 cm στον πυρήνα / είσοδο κτιρίου (Τ5-01, φρεάτιο, Τ1-12, Τ1-11). ΥΨΟΣ ισογείου 3,00 (πλάκα οροφής +3,65 κατά Σ3) – επιφάνειες Τ-03 με H = 3,00.

ΕΡΓΟ

ΠΕΝΤΑΟΡΟΦΟ ΚΤΗΡΙΟ ΚΑΤΟΙΚΙΩΝ – ΑΡΓΥΡΟΥΠΟΛΗ
Κωνσταντινουπόλεως 12 & Αγ. Βαρβάρας · Ο.Τ. 103-15
Εργοδότης: INTERKAT Α.Ε. · Κατασκευή: ARKAD Ι.Κ.Ε.

ΘΕΜΑ ΣΧΕΔΙΟΥ


ΠΡΟΜΕΤΡΗΣΗ ΤΟΙΧΟΠΟΙΙΩΝ – ΙΣΟΓΕΙΟΥ
Τετραγωνικά ανά τυπολογία τοίχου · θερμοπρόσοψη 10 / 5 cm
ΙΣΟΓΕΙΟ – ΙΣ1

ΒΑΣΗ

Βάση: κάτοψη τοιχοποιιών Τ-01 · είδη Τ-02

ΑΡ. ΣΧΕΔΙΟΥ

Τ-03
— · A3
06/11/2026 · R06

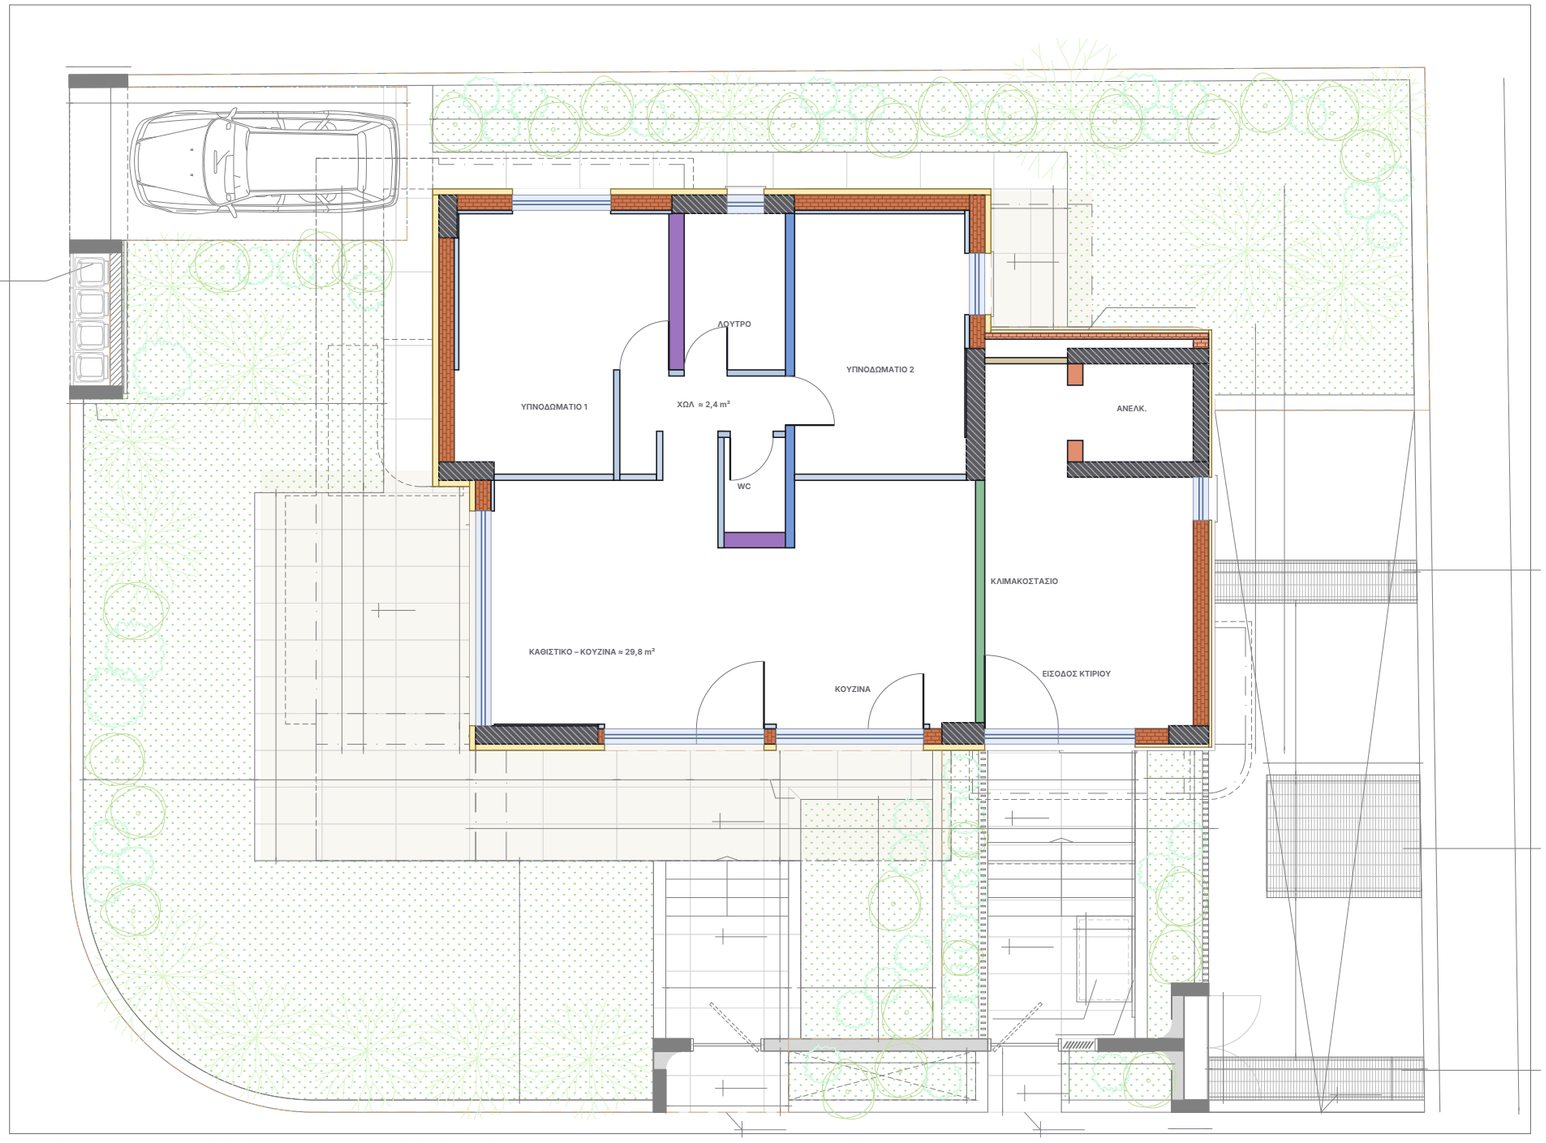

Περιβάλλων χώρος: γεωμετρία A-10-GF (EDGE, μελέτη εφαρμογής 23/07/2026) 1:100, αχνά, χωρίς κείμενα / διαστάσεις · τοιχοποιίες από το T-01 R06 · συντεταγμένες μοντέλου σε m

B

ΠΕΡΙΒΑΛΛΩΝ ΧΩΡΟΣ ΙΣΟΓΕΙΟΥ – όπως τον έχει ο αρχιτέκτονας (A-10-GF)

Το φύλλο δείχνει το οικόπεδο ολόκληρο με τον κήπο, τις βεράντες, τις εισόδους και τη ράμπα όπως τα έχει ο αρχιτέκτονας στο A-10-GF (μόνο η γεωμετρία, χωρίς τα κείμενά του), για να φαίνεται πώς δένουν οι τοιχοποιίες του ισογείου με τον περιβάλλοντα χώρο. Δεν είναι σχέδιο κατασκευής κήπου: για διαστάσεις, στάθμες και φυτεύσεις ισχύουν τα A-10-GF / A-14-GF και η μελέτη περιβάλλοντος χώρου.

ΚΗΠΟΣ ΙΣ1
Χώρος αποκλειστικής χρήσης ΙΣ1 κατοικίας 182,08 m² (σημεία 1…23 του A-10-GF): δυτικά και νότια του κτιρίου, βεράντα ισογείου δυτικά +0,40 (κλίση 1 %) και νότια +0,45 με σκαλιά 1–4 προς −0,30 · προβολές εξώστη / έρκερ με διακεκομμένη.

ΕΙΣΟΔΟΣ ΙΣ1
Από τη νότια περίφραξη: πύλη Θ 1,00/2,20 (x ≈ 5,2–6,2), σκαλιά −0,30 → +0,45, βεράντα, πόρτα Θ0.03 1,10×2,40 (5,00–6,10).

ΣΤΑΘΜΕΥΣΗ
Θ.Σ.Ι.1 13,75 m² στη ΒΔ γωνία του οικοπέδου (θέση στάθμευσης ισογείου), πλάτος 2,50 · μήκος 5,50.

ΦΥΤΕΜΕΝΟΙ ΧΩΡΟΙ
Φ.Χ.1 37,69 m² (βόρεια) · Φ.Χ.2 68,46 (νοτιοδυτικά) · Φ.Χ.3 8,39 · Φ.Χ.4 2,82 · Φ.Χ.5 3,76 · Φ.Χ.6 1,42 · Φ.Χ.7 2,44 m².

ΕΙΣΟΔΟΣ ΚΤΙΡΙΟΥ
Νότια: πύλη πεζών Θ 1,00/2,20 (x ≈ 9,85–10,85) στο −0,45, σκάλα 5 ριχτιών 2,40 (x 9,75–12,15) ως το πλατύσκαλο +0,45 (9,50–12,95 × 9,45–10,25), αναδιπλούμενη πλατφόρμα αναβατορίου ΑΜΕΑ 0,90×1,40 με οδηγό x 8,85–9,75, πόρτα αλουμινίου 1,00×2,40 + σταθερό W0.04 1,20 στο lobby (24,55 m²).

ΒΑ ΒΕΡΑΝΤΑ
Βεράντα ισογείου +0,45, 9,80–11,45 × 0,45–2,70, από την μπαλκονόπορτα W0.06 του Υπν.2 · ανατολικά της φυτεμένος χώρος.

ΟΧΗΜΑΤΑ / ΥΠΟΣΤΑΘΜΟΣ
Ράμπα Ι.Χ. κλίσης 16,12 % στη ΝΑ γωνία (είσοδος – έξοδος οχημάτων, −0,55), μετρητές ΔΕΔΔΗΕ, εσχάρες υποσταθμού: εξαερισμού Ι-Κ-Λ-Μ 3,40×0,60 = 2,04 m² (ανατολικά του lobby) και Ρ-Σ-Τ-Υ 3,52×0,60 = 2,11 m², καταπακτής Ν-Ξ-Ο-Π 2,80×1,80 = 5,02 m² (βλ. A-30-01).

ΕΡΓΟ	ΘΕΜΑ ΣΧΕΔΙΟΥ	ΒΑΣΗ	ΑΡ. ΣΧΕΔΙΟΥ
ΠΕΝΤΑΟΡΟΦΟ ΚΤΗΡΙΟ ΚΑΤΟΙΚΙΩΝ – ΑΡΓΥΡΟΥΠΟΛΗ Κωνσταντινουπόλεως 12 & Αγ. Βαρβάρας · Ο.Τ. 103-15 Εργοδότης: INTERKAT Α.Ε. · Κατασκευή: ARKAD Ι.Κ.Ε.	**ΠΕΡΙΒΑΛΛΩΝ ΧΩΡΟΣ – ΙΣΟΓΕΙΟ** Κήπος ΙΣ1 · βεράντες · είσοδοι · ράμπα κατά A-10-GF ΙΣΟΓΕΙΟ – ΙΣ1	Βάση: γεωμετρία περιβάλλοντος χώρου A-10-GF · τοιχοποιίες T-01	**T-04** **Κλίμακα 1:100 · A3** 06/11/2026 · R06