B


ΙΣΟΓΕΙΟ R05 – ΔΙΟΡΘΩΣΕΙΣ & ΠΑΡΑΔΟΧΕΣ (05/11/2026)

- R05: ΤΟ WC ΦΕΥΓΕΙ ΑΠΟ ΤΟ ΚΑΘΙΣΤΙΚΟ → νότια πλευρά του χωλ, 1,55 × 1,00 (3,75–5,30 × 4,45–5,45), πόρτα 0,70 γωνιακή από το χωλ, λεκάνη στον T7-02 (= παραστάδα του ανοίγματος)· ντουλάπα πλυντηρίου / χωλ καταργείται, πλυντήριο στην κουζίνα
- R05: ΚΟΥΖΙΝΑ ΣΕ Γ στη ΒΑ γωνία (βόρειο σκέλος 2,35 + γωνία + ανατολικό 2,95 ≈ 5,9 m): φούρνος-στήλη, πλυντήριο, νεροχύτης, πλ. πιάτων, εστίες, ψυγείο 0,70 δίπλα στο W0.03 – καμία εσοχή, κανένα κενό
- R05: βόρειος τοίχος καθιστικού ΣΕ ΜΙΑ ΕΥΘΕΙΑ στο 5,45–5,55 (T2N-01 · T2-05 WC · άνοιγμα 0,90 · T2N-02)· Υπν.1 / Υπν.2 +0,40 νότια, ντουλάπες 0,60 στο 4,85–5,45
- R05: Υπν.1 ντουλάπες 5,1 m: N 1,95 + Δ 1,50 (0,65, ως την παρειά 1,70 του Δ υποστυλώματος – περασιά με το μέτωπο 4,85) + Α 1,65 στον T7-01· κρεβάτι 1,60 κεφαλάρι δυτικά, 0,10 βορειότερα (διάβαση προς την εσοχή 0,55)
- R05: λευκές κουκίδες στις γωνίες = ακάλυπτα τετραγωνάκια 10×10 / 5×5 όπου δύο τοίχοι τελείωναν ο ένας στην παρειά του άλλου – διορθώθηκαν (έλεγχος check_corners.py)
- R04: χωλ 0,90 (τοίχος λουτρού / πόρτας Υπν.1 στο 3,35–3,45, λουτρό 2,55) · κανένα κενό ντουλάπας / πάγκου από τοίχο · έπιπλα από το EPIPLA του αρχιτέκτονα (το WC 2,00 του R04 απορρίφθηκε)
- R03: T3 όπως B1 = CW 30 + 2 × 12,5 (5,5)· δίπλα σε υποστύλωμα ο σκελετός σε απόσταση 2 cm από το τούβλο ώστε η παρειά να είναι ΠΕΡΑΣΙΑ με το T9 (2,5) – κανένα δόντι
- R03: κήπος / βεράντες / φυτεύσεις / είσοδοι / ράμπα από τη γεωμετρία του A-10-GF, αχνά, χωρίς κείμενα και διαστάσεις · δάπεδα βεραντών μπεζ όπως B1 · όλο το οικόπεδο στο T-04 1:100
- R01: ΕΙΣΟΔΟΣ ΚΤΙΡΙΟΥ = πόρτα αλουμινίου 1,00×2,40 στον νότιο τοίχο του lobby (9,80–10,80, μεντεσές δυτικά, ανοίγει μέσα) + σταθερό W0.04 1,20 (10,95–12,15), ενιαίο κούφωμα · ΚΑΜΙΑ πόρτα διαμερίσματος προς το lobby · είσοδος ΙΣ1 = Θ0.03 1,10 από τη νότια βεράντα
- Λουτρό: ντους 1,65×0,80 βόρεια, γυαλί 0,70 · λεκάνη στον T7-01 · πάγκος 0,50 ανατολικά · WC: λεκάνη στον T7-02, νιπτήρας 0,50 × 0,35 νότια
- Πόρτες μέσα στον χώρο, ισοπαχείς παραστάδες, ορθοστάτες UA 2 mm · T6 15 cm · T10 25 cm · T3 και στις δύο παραστάδες κάθε κουφώματος · W0.07 μέσα στο τοιχείο K2 (κενό 0,60×0,90 στον ξυλότυπο) · θερμοπρόσοψη 10 / 5 cm


ΕΡΓΟ **ΠΕΝΤΑΟΡΟΦΟ ΚΤΗΡΙΟ ΚΑΤΟΙΚΙΩΝ – ΑΡΓΥΡΟΥΠΟΛΗ** Κωνσταντινουπόλεως 12 & Αγ. Βαρβάρας · Ο.Τ. 103-15 Εργοδότης: INTERKAT Α.Ε. · Κατασκευή: ARKAD Ι.Κ.Ε.	ΘΕΜΑ ΣΧΕΔΙΟΥ **ΚΑΤΟΨΗ ΤΟΙΧΟΠΟΙΙΩΝ – ΙΣΟΓΕΙΟΥ** Είδη τοιχοποιιών · διαστάσεις χάραξης · κουφώματα · εξώστες ΙΣΟΓΕΙΟ – ΙΣ1	ΒΑΣΗ Βάση: A-10-GF (μελ. εφαρμογής, Drive) · ξυλότυπος Σ3_ΕΦ · κανόνες B1 R20	ΑΡ. ΣΧΕΔΙΟΥ **T-01** **Κλίμακα 1:60 · A3** 05/11/2026 · R05

T1 Εξωτερική οπτοπλινθοδομή 1:4

πάχος 25 cm

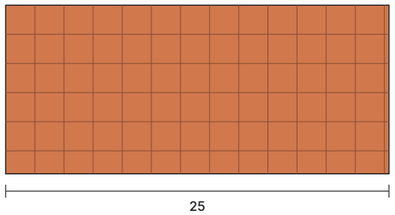

θερμομονωτικό τούβλο κάθετων οπών 25 cm · θερμοπρόσοψη 10 cm έξω · επένδυση T3 μέσα όπου σημειώνεται

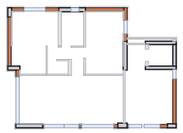


Τοίχοι: T1-01, T1-02, T1-03, T1-04, T1-05, T1-06, T1-07, T1-08, T1-09, T1-10, T1-11, T1-12, T1-13


Μήκος 15,35 m · επιφάνεια ≈ 46,0 m²

T5 Οπτοπλινθοδομή πυρήνα 1:4

πάχος 10 cm

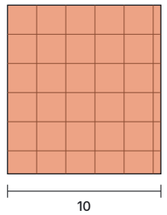

θερμομονωτικό τούβλο κάθετων οπών 10 cm · γύρω από τον πυρήνα (ανελκυστήρας – ηλεκτροστάσιο)

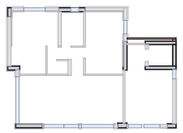


Τοίχοι: T5-01, T5-02


Μήκος 3,90 m · επιφάνεια ≈ 11,7 m²

T10 Μέτωπο ανελκυστήρα 1:4

πάχος 25 cm

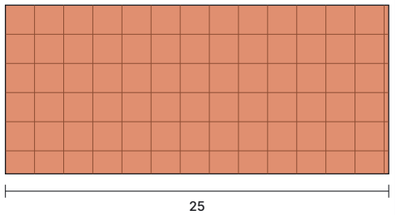

θερμομονωτικό τούβλο κάθετων οπών 25 cm · μέτωπο φρεατίου εκατέρωθεν της πόρτας 0,90 · ισοπαχές με τα τοιχεία 25 του φρεατίου (Σ5), περασιά και στις δύο παρειές, ώστε να κάθεται σωστά η κάσα της πόρτας ορόφου · θέση πόρτας προς επιβεβαίωση από τον προμηθευτή

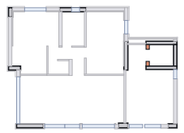


Τοίχοι: T10-01, T10-02


Μήκος 0,70 m · επιφάνεια ≈ 2,1 m²

T3 Επένδυση τοίχου 1:4

πάχος 5,5 cm

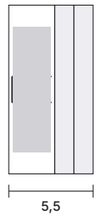

σκελετός 30 · 2 × γυψοσανίδα 12,5 · στις εσωτερικές παρειές των T1 – ΟΧΙ όπου πλακάκι ή ντουλάπα, ΟΧΙ στα έρκερ

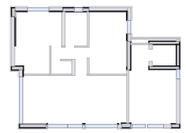


Τοίχοι: T3-01, T3-02, T3-03, T3-04, T3-05, T3-06, T3-07, T3-08, T3-09, T3-10


Μήκος 8,98 m · επιφάνεια ≈ 26,9 m²

T9 Επένδυση υποστυλώματος 1:4

πάχος 2,5 cm

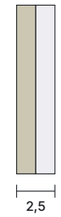

κόλλα + 1 × γυψοσανίδα 12,5 (ένα φύλλο) · στις παρειές υποστυλωμάτων μέσα στα διαμερίσματα – ΟΧΙ όπου πλακάκι ή ντουλάπα

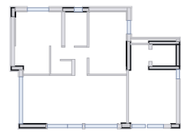


Τοίχοι: T9-01, T9-02, T9-03


Μήκος 3,94 m · επιφάνεια ≈ 11,8 m²

T2 Χώρισμα γυψοσανίδας 1:4

πάχος 10 cm

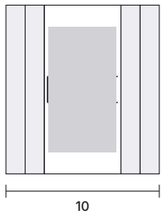

2 × γυψοσανίδα 12,5 · σκελετός CW 50 · 2 × γυψοσανίδα 12,5 · εσωτερικά χωρίσματα · ανθυγρή γυψοσανίδα στην πλευρά των λουτρών · ανοίγματα πορτών με ορθοστάτες UA 50 (2 mm)

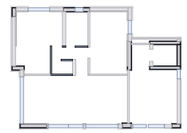


Τοίχοι: T2-01, T2-02, T2-03, T2-04, T2-05


Μήκος 5,80 m · επιφάνεια ≈ 17,4 m²

T2N Χώρισμα γυψ. – πλευρά ντουλάπας 1:4

πάχος 8,75 cm

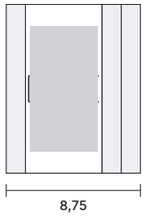

1 × γυψοσανίδα 12,5 (πλευρά ντουλάπας) · σκελετός CW 50 · 2 × γυψοσανίδα 12,5 · όπου η μία παρειά βλέπει σε ντουλάπα: ένα φύλλο αρκεί (κανόνας R15)

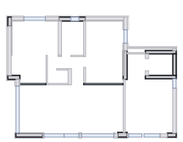


Τοίχοι: T2N-01, T2N-02


Μήκος 4,90 m · επιφάνεια ≈ 14,7 m²

T2A Χώρισμα γυψοσανίδας 15 1:4

πάχος 15 cm

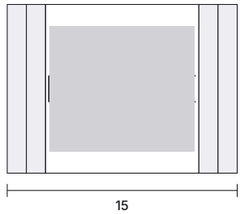

2 × γυψοσανίδα 12,5 · σκελετός CW 100 + πετροβάμβακας · 2 × γυψοσανίδα 12,5 · λουτρό γονέων / χωλ · υπνοδωμάτια · ανοίγματα πορτών με ορθοστάτες UA 100 (2 mm)

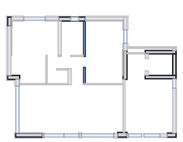


Τοίχοι: T2A-01, T2A-02


Μήκος 3,85 m · επιφάνεια ≈ 11,6 m²

T7 Τοίχος λεκάνης WC 1:4

πάχος 25 cm

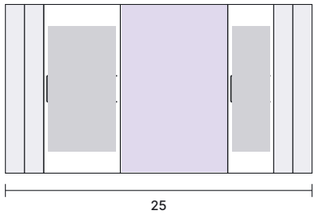

2 × γυψοσανίδα 12,5 · σκελετός CW 50 · κενό 12 cm (καζανάκι γυψοσανίδας στον σκελετό + κατακόρυφη στήλη Ø110, έξοδος Ø90) · σκελετός CW 30 · 2 × γυψοσανίδα 12,5 · ΟΛΟΙ οι τοίχοι λεκανών · ανθυγρή προς το λουτρό · στην πλευρά ντουλάπας 1 φύλλο · ανοίγματα πορτών με ορθοστάτες UA 50 (2 mm)

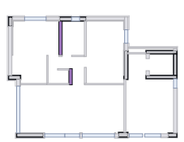


Τοίχοι: T7-01, T7-02


Μήκος 3,75 m · επιφάνεια ≈ 11,2 m²

T6 Τοίχος κλιμακοστασίου 1:4

πάχος 15 cm

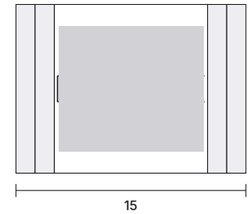

2 × γυψοσανίδα 12,5 πυράντοχη · σκελετός CW 100 + πετροβάμβακας · 2 × γυψοσανίδα 12,5 πυράντοχη · προς κοινόχρηστους χώρους · 15 cm · άνοιγμα πόρτας εισόδου (ασφαλείας) με ορθοστάτες UA 100 (2 mm) κατά Knauf

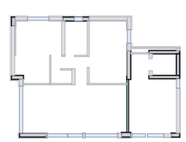


Τοίχοι: T6-01


Μήκος 3,95 m · επιφάνεια ≈ 11,8 m²

T8 Τοίχος shaft 1:4

πάχος 10 cm

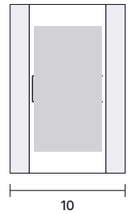

πλαίσιο + ανοιγόμενα φύλλα γυψοσανίδας · μέτωπο shaft ηλεκτρολογικών

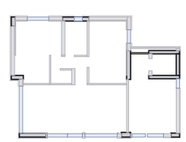

Τοίχοι: T8-01

Μήκος 1,35 m · επιφάνεια ≈ 4,1 m²

Επιφάνειες ενδεικτικές: μήκος × ύψος 3,00 m (τελικό δάπεδο – πλάκα) – οι τοίχοι ορίζονται μεταξύ ανοιγμάτων, χωρίς αφαίρεση κασών. T3 = επένδυση στην εσωτερική παρειά των T1 · T9 = περίμετρος υποστυλώματος × ύψος. R15: T2N = 1 φύλλο στην πλευρά ντουλάπας (T2N-01, T2N-02) · T7-01 1 φύλλο προς Υπν.1.

ΕΡΓΟ

ΠΕΝΤΑΟΡΟΦΟ ΚΤΗΡΙΟ ΚΑΤΟΙΚΙΩΝ – ΑΡΓΥΡΟΥΠΟΛΗ
Κωνσταντινουπόλεως 12 & Αγ. Βαρβάρας · Ο.Τ. 103-15
Εργοδότης: INTERKAT Α.Ε. · Κατασκευή: ARKAD Ι.Κ.Ε.

ΘΕΜΑ ΣΧΕΔΙΟΥ

ΕΙΔΗ ΤΟΙΧΟΠΟΙΙΩΝ – ΙΣΟΓΕΙΟΥ
Είδη τοιχοποιιών · ΙΣΟΓΕΙΟ – ΙΣ1
τομές 1:4 · μήκη – εμβαδά ανά είδος

ΒΑΣΗ

Βάση: κάτοψη τοιχοποιιών T-01 · κάτοψη A-10-GF

ΑΡ. ΣΧΕΔΙΟΥ

T-02
Κλίμακα 1:4 · A3
05/11/2026 · R05

ΠΡΟΜΕΤΡΗΣΗ ΤΟΙΧΟΠΟΙΙΩΝ – ΙΣΟΓΕΙΟ – ΙΣ1

τετραγωνικά ανά τυπολογία τοίχου · H = 3,00 m (τελικό δάπεδο – κάτω παρειά πλάκας) · μήκη στον άξονα, χωρίς αφαίρεση κουφωμάτων · R05

	Τύπος	Περιγραφή	Πάχος cm	Τοίχοι	Μήκος m	Επιφάνεια m²
ΤΟΥΒΛΑ						
	T1	Εξωτερική οπτοπλινθοδομή	25	13	15,35	**46,0**
	T5	Οπτοπλινθοδομή πυρήνα	10	2	3,90	**11,7**
	T10	Μέτωπο ανελκυστήρα	25	2	0,70	**2,1**
	Σύνολο τουβλα					**59,9 m²**
ΧΩΡΙΣΜΑΤΑ ΓΥΨΟΣΑΝΙΔΑΣ						
	T2	Χώρισμα γυψοσανίδας	10	5	5,80	**17,4**
	T2N	Χώρισμα γυψ. – πλευρά ντουλάπας	8,8	2	4,90	**14,7**
	T2A	Χώρισμα γυψοσανίδας 15	15	2	3,85	**11,6**
	T7	Τοίχος λεκάνης WC	25	2	3,75	**11,2**
	T6	Τοίχος κλιμακοστασίου	15	1	3,95	**11,8**
	T8	Τοίχος shaft	10	1	1,35	**4,1**
	Σύνολο χωρισματα γυψοσανιδας					**70,8 m²**
ΕΠΕΝΔΥΣΕΙΣ						
	T3	Επένδυση τοίχου	5,5	10	8,98	**26,9**
	T9	Επένδυση υποστυλώματος	2,5	3	3,94	**11,8**
	Σύνολο επενδυσεις					**38,7 m²**
	ΣΥΝΟΛΟ ΤΟΙΧΟΠΟΙΙΩΝ ΙΣ1					**169,4 m²**

ΘΕΡΜΟΠΡΟΣΟΨΗ (ETICS)

10 cm στις όψεις των διαμερισμάτων · 5 cm στο κλιμακοστάσιο / πυρήνα · ύψος 3,20 m (με τη μετώπη πλάκας) · καθαρά = όψη − κουφώματα + λαμπάδες/ανώφλια

Ζώνη	Μήκος όψης m	Μικτά m²	Κουφώματα m²	Λαμπάδες m²	Καθαρά m²
ETICS 10 cm – διαμερίσματα	29,40	94,1	−27,2	+5,9	**72,8**
ETICS 5 cm – κλιμακοστάσιο / πυρήνας	13,90	44,5	−6,2	+2,0	**40,2**
Σύνολο ETICS					**113,1 m²**

ΣΗΜΕΙΩΣΕΙΣ ΚΑΤΟΨΗΣ

• Θέσεις τοίχων και ανοιγμάτων κατά την κάτοψη ισογείου A-10-GF (EDGE 23/07/2026, μελέτη εφαρμογής, Drive του έργου) με τους κανόνες του B1 R20 και τις αλλαγές R01–R05 του Γιάννη. Διαστάσεις στο τούβλο / μπετό και στις παρειές της γυψοσανίδας, χωρίς τη θερμοπρόσοψη. Υποστυλώματα / τοιχεία από τα μαύρα γεμίσματα του A-10-GF – ταυτίζονται με τον ξυλότυπο Σ3 (να επιβεβαιωθούν στον Σ3 πριν τη χάραξη).

• Τ3 ΠΕΡΑΣΙΑ (R03, όπως B1): T3 = σκελετός CW 30 + 2 × γυψοσανίδα 12,5 (5,5 cm). Τα υποστυλώματα (30) προεξέχουν 5 cm από την εσωτερική παρειά του τούβλου (25) και παίρνουν κολλητή γυψοσανίδα T9 2,5 cm· όπου η T3 συνεχίζει δίπλα σε υποστύλωμα, ο σκελετός CW 30 στήνεται σε απόσταση 2 cm από το τούβλο ώστε η παρειά της γυψοσανίδας να είναι στο ίδιο επίπεδο με το T9: T3-06 (παρειά 1,125 = T9-01), T3-04/T3-05 (9,375 = T9-02), T3-08/09/10 (9,125 = T9-03). Αλλού η T3 κολλητά στο τούβλο: B 0,805 · Δ καθιστικού 1,705. Όπου πλακάκι, ντουλάπα ή πάγκος: χωρίς T3 / T9 (γυμνό τούβλο / μπετό).

• WC ΣΤΟ ΧΩΛ (R05 – Γιάννης: «μικρό WC και καλύτερη κουζίνα, όχι μεγαλύτερο WC»): το WC του αρχιτέκτονα (1,55 × 0,95 μέσα στο καθιστικό, με κενό 0,45–0,60 ως τον πάγκο) φεύγει από το καθιστικό και μπαίνει στη νότια πλευρά του χωλ, στη θέση της εσοχής πλυντηρίου: 3,75–5,30 × 4,45–5,45 (1,55 × 1,00 = 1,55 m²). Πόρτα 0,70 γωνιακή στο 3,75–4,45 (μεντεσές 3,75, ανοίγει μέσα, διπλώνει στον T2-01 – ισοπαχείς παραστάδες 10 / 10), λεκάνη στον T7-02 (25, 5,30–5,55 × 4,35–5,55 – ο ίδιος τοίχος είναι η δυτική παραστάδα του ανοίγματος χωλ–καθιστικό), νιπτήρας 0,50 × 0,35 στον νότιο τοίχο (4,55–5,05), λεκάνη άξονας 4,85. Τοίχοι: T2-04 βόρεια (4,45–5,30), T2-05 νότια (3,65–5,30 × 5,45–5,55), T2-01 δυτικά. Η ντουλάπα πλυντηρίου 0,70 και η ντουλάπα χωλ καταργούνται – το πλυντήριο πάει στην κουζίνα (βόρειο σκέλος, δίπλα στη στήλη φούρνου).

• ΚΟΥΖΙΝΑ ΣΕ Γ (R05): χωρίς WC στη ΒΑ γωνία, ο πάγκος 0,60 γυρίζει σε Γ: βόρειο σκέλος στον T2N-02 από την παραστάδα του ανοίγματος (6,45) ως τη γωνία (8,80) = 2,35 + γωνία 0,60 + ανατολικό σκέλος στον T6-01 από 6,15 ως το N υποστύλωμα (9,10) = 2,95 → ≈ 5,9 m μετώπου (ο αρχιτέκτονας: ευθύγραμμος 3,40 + ψυγείο στην εσοχή). Διάταξη: στήλη φούρνου 0,60 στην παραστάδα (6,45–7,05), πλυντήριο 0,60 (7,05–7,65), πάγκος 1,15 + γωνία, νεροχύτης 0,80 (y 6,15–6,95), πλυντήριο πιάτων 0,60, εστίες 0,60 (7,55–8,15, απορροφητήρας στον T6-01), πάγκος 0,25, ψυγείο 0,70 × 0,65 (8,40–9,10) δίπλα στην παραστάδα του W0.03. Ο T2N-02 πίσω από το βόρειο σκέλος: 2 φύλλα προς την κουζίνα + ενίσχυση (OSB) για τα κρεμαστά ντουλάπια. Πίσω από τους πάγκους χωρίς επένδυση (T6-01 γυψοσανίδα, N υποστύλωμα γυμνό)· η T3-10 μόνο στην παραστάδα του W0.03 (8,70–8,80). Η τραπεζαρία (EPIPLA) μετακινήθηκε 0,48 δυτικά / 0,55 νότια ώστε οι καρέκλες να απέχουν ≥ 1,00 από τους πάγκους.

• ΒΟΡΕΙΟΣ ΤΟΙΧΟΣ ΚΑΘΙΣΤΙΚΟΥ ΣΕ ΜΙΑ ΕΥΘΕΙΑ (R05): T2N-01 (1,70–3,65, ντουλάπα Υπν.1) · T2-05 (3,65–5,30, WC) · T7-02 (5,30–5,55) · άνοιγμα 0,90 (5,55–6,45) · T2A-02 / T2N-02 (6,45–9,40, ντουλάπα Υπν.2) – όλοι στο y 5,45–5,55, κανένα δόντι. Ο T2A-02 ως 5,45. Το καθιστικό–τραπεζαρία–κουζίνα γίνεται καθαρό ορθογώνιο 7,70 × 3,575 (1,70–9,40 × 5,55–9,125 ≈ 27,5 m²) χωρίς τον όγκο του WC. Ο καναπές (EPIPLA) ακολουθεί τον τοίχο (+0,40 νότια).

• ΑΠΟΘΗΚΕΣ → ΝΤΟΥΛΑΠΕΣ (Γιάννης 05/11): η αποθήκη του Υπν.1 (1,10–3,55 × 3,80–5,00) και η αποθήκη του Υπν.2 (6,60–9,40 × 3,00–5,00) καταργούνται· τα δωμάτια μεγαλώνουν ως το y 4,85 (R05: +0,40 από το R04) και παίρνουν ντουλάπα 0,60 χωνευτή στο y 4,85–5,45. Οι εσωτερικοί τοίχοι τους (y 3,65–3,80 και y 2,85–3,00) δεν κτίζονται.

• Υπν.1 (R05 – «μεγαλύτερη ντουλάπα και σωστή διάταξη»): κύριος χώρος 1,125–4,55 × 0,805–3,35 (3,425 × 2,545) + εσοχή 1,70–3,65 × 3,35–4,85 (≈ 11,7 m² καθαρά). Ντουλάπες 0,60 χωνευτές, 5,1 m συνολικά: ΝΟΤΙΑ 1,70–3,65 × 4,85–5,45 (1,95, ανάμεσα στο Δ υποστύλωμα και τον T2-01), ΔΥΤΙΚΗ 1,05–1,70 × 3,35–4,85 (1,50, βάθος 0,65 από το γυμνό τούβλο ως την παρειά 1,70 του υποστυλώματος – το μέτωπό της και η βόρεια παρειά του υποστυλώματος 4,85 είναι περασιά, κανένα κενό / ξυλουργικό), ΑΝΑΤΟΛΙΚΗ 3,95–4,55 × 0,805–2,45 (1,65 στον T7-01, 1 φύλλο πίσω της, τελειώνει 0,10 πριν το ανοιχτό φύλλο της πόρτας). Κρεβάτι 1,60 × 2,00 με κεφαλάρι στη δυτική επένδυση (όπως ο αρχιτέκτονας – στον βόρειο τοίχο είναι το W0.08 1,60 × 2,40), 0,10 βορειότερα από το EPIPLA (y 1,20–2,80): κομοδίνα 0,45 × 0,395 βόρεια και 0,45 × 0,45 νότια, διάβαση προς την εσοχή 0,55 (διαγώνιο 0,75 ανάμεσα στο κρεβάτι και τον T2-01). Πόρτα 0,80 στο 3,75–4,55, μεντεσές 4,55, διπλώνει στον T7-01. Η T3-06 ως 3,35 (πίσω από τη δυτική ντουλάπα γυμνό τούβλο).

• ΧΩΛ 2,70 × 0,90 (y 3,45–4,35): βόρεια πόρτες Υπν.1 (3,75–4,55) και λουτρού (4,80–5,50), νότια πόρτα WC (3,75–4,45) και T7-02, ανατολικά πόρτα Υπν.2 (y 3,45–4,25), άνοιγμα προς καθιστικό 5,55–6,45 (0,90, μήκος 1,20 ανάμεσα στον T7-02 και τον T2A-02). Τοίχοι που βλέπουν σε ντουλάπα: 1 φύλλο (T2N-01, T2N-02).

• ΛΟΥΤΡΟ 1,65 × 2,55 (x 4,80–6,45 · y 0,80–3,35): T7-01 λεκάνης δυτικά (σταθερή η παρειά Υπν.1 4,55), T2A-01 ανατολικά 6,45–6,60 (A-10-GF), ντους 1,65×0,80 βόρεια (y 0,80–1,60) με γυάλινο διαχωριστικό 0,70 στο y 1,60 από τον T7-01, λεκάνη στον T7-01 (y 2,10), πάγκος 0,50 στον ανατολικό τοίχο (5,95–6,45 × 1,75–3,35), πόρτα 0,70 στο 4,80–5,50 (μεντεσές 5,50). W0.07 0,60×0,90 μέσα στο τοιχείο K2 (x 5,50–6,10): κενό στον ξυλότυπο από τώρα (ποδιά +1,50).

• Υπν.2 (6,60–9,375 × 0,805–4,85 ≈ 11,2 m²): ντουλάπα 6,60–9,40 × 4,85–5,45 (2,80), πόρτα 0,80 από το χωλ στο y 3,45–4,25 (T2A-01 / T2A-02, μεντεσές 4,25), W0.06 1,00×2,40 μπαλκονόπορτα προς τη ΒΑ βεράντα (9,80–11,45 × 0,45–2,70, +0,45). T9-02 στο υποστύλωμα πυρήνα 3,00–4,85 περασιά με την T3-05.

• ΛΕΥΚΕΣ ΚΟΥΚΙΔΕΣ ΣΤΙΣ ΓΩΝΙΕΣ (ερώτηση Γιάννη, R05): ήταν ακάλυπτα τετραγωνάκια του μοντέλου εκεί που δύο λεπτοί τοίχοι γωνίαζαν και ο καθένας τελείωνε στην παρειά του άλλου (π.χ. T2N-01 / T2N-03 στο 5,45–5,55 × 5,05–5,15, T3-02 / T7-01 / K2 στο 4,55–4,60 × 0,75–0,80). Διορθώθηκαν: ο ένας τοίχος περνάει ως την εξωτερική γωνία (T7-02 ως 4,35 / 5,55, T2-05 ως 3,65, T3-02 ως 4,60, T2A-01/02 ως 3,45 / 5,45). Έλεγχος κάθε έκδοσης με code/toixopoiies/check_corners.py (raster 1 cm).

• ΚΑΘΙΣΤΙΚΟ: δυτικός τοίχος T1-07 1,40–1,65 + T3-07 ως 1,705 (ο αρχιτέκτονας 1,40–1,70) περασιά με το ΝΔ τοιχείο (1,40) και την ανατολική παρειά του Δ υποστυλώματος (1,70). W0.01 3,50×2,40 στο 5,65–9,15. Νότιος τοίχος: T9-03 στο ΝΔ τοιχείο (παρειά 9,125) περασιά με T3-08 / T3-09.

• ΠΥΡΗΝΑΣ: T5-01 10 cm σε όλο το μήκος 9,70–13,35 (A-10-GF) με επιστροφή T5-02 στο φρεάτιο· shaft H/M εκτός Σ.Δ. στο y 2,85–3,15 × 9,70–11,05 (βάθος 0,30 όπως B1 – ο αρχιτέκτονας δείχνει μέτωπο 25 στο 3,00–3,25). Μέτωπο ανελκυστήρα T10-01/T10-02 25 cm, πόρτα 0,90 στο y 3,60–4,50. Κύκλος περιστροφής ΑΜΕΑ R0,75 (1,50) στο 9,70–11,20. Σκάλα 16 ριχτιών όπως B1. ΕΙΣΟΔΟΣ ΚΤΙΡΙΟΥ: ενιαίο κούφωμα αλουμινίου 2,35 = πόρτα 1,00×2,40 (9,80–10,80) + κολωνάκι 0,15 + σταθερό W0.04 1,20 (10,95–12,15)· καμία πόρτα διαμερίσματος προς το lobby (T6-01 συμπαγής, κουζίνα πίσω του).


• ΚΟΥΦΩΜΑΤΑ (πίνακας κουφωμάτων A-10-GF): W0.08 1,60×2,40 (2,00–3,60) · W0.07 0,60×0,90 · W0.06 1,00×2,40 (1,45–2,45) · W0.01 3,50×2,40 (5,65–9,15) · W0.02 1,50 (3,50–5,00) · Θ0.03 πόρτα 1,10 (5,00–6,10) · W0.03 2,40 = 1,50 + ανοιγόμενο 0,90 (6,30–8,70) · είσοδος 1,00 + W0.04 1,20 · W0.05 0,70×1,35. Πεσσοί 0,10 (3,40–3,50 και 9,70–9,80), 0,20 (6,10–6,30), 0,30 (8,70–9,00) όπως ο αρχιτέκτονας – ΠΡΟΣ ΑΠΟΦΑΣΗ αν οι 0,10 ενσωματωθούν στα κουφώματα. Τ3 και στις δύο παραστάδες.

• ΠΕΡΙΒΑΛΛΩΝ ΧΩΡΟΣ: κήπος αποκλειστικής χρήσης ΙΣ1 182,08 m², θέση στάθμευσης Θ.Σ.Ι.1, φυτεμένοι χώροι, βεράντες (+0,40 δυτικά, +0,45 νότια, ΒΑ), σκαλιά, πλατφόρμα ΑΜΕΑ, ράμπα Ι.Χ., περίφραξη – αχνά, από τη γεωμετρία του A-10-GF (χωρίς κείμενα / διαστάσεις). Δεν είναι σχέδιο κατασκευής του κήπου· ισχύουν A-10-GF / A-14-GF. Πλήρες οικόπεδο στο T-04 (1:100).

• ΕΠΙΠΛΑ: από το layer EPIPLA του A-10-GF (κρεβάτι Υπν.2, καναπές, πολυθρόνα, τραπεζάκι, τραπέζι + καρέκλες, έπιπλο TV), αχνά όπως στο B1· καναπές και τραπεζαρία μετατοπισμένα όσο μετακινήθηκαν οι τοίχοι / οι πάγκοι. Κρεβάτι Υπν.1 και κουζίνα από το μοντέλο (νέες θέσεις). Στο λουτρό / WC μόνο πάγκος, λεκάνη, γυαλί (κανόνας B1)· ντουλάπες δικές μας.

• ΘΕΡΜΟΠΡΟΣΟΨΗ: 10 cm στο διαμέρισμα (B, Δ, N όψεις και A του Υπν.2), 5 cm στον πυρήνα / είσοδο κτιρίου (T5-01, φρεάτιο, T1-13, πεσσοί νότιου τοίχου lobby). ΥΨΟΣ ισογείου 3,00 (πλάκα οροφής +3,65 κατά Σ3) – οι επιφάνειες του T-03 με H = 3,00.

ΕΡΓΟ	ΘΕΜΑ ΣΧΕΔΙΟΥ	ΒΑΣΗ	ΑΡ. ΣΧΕΔΙΟΥ
ΠΕΝΤΑΟΡΟΦΟ ΚΤΗΡΙΟ ΚΑΤΟΙΚΙΩΝ – ΑΡΓΥΡΟΥΠΟΛΗ Κωνσταντινουπόλεως 12 & Αγ. Βαρβάρας · Ο.Τ. 103-15 Εργοδότης: INTERKAT Α.Ε. · Κατασκευή: ARKAD Ι.Κ.Ε.	**ΠΡΟΜΕΤΡΗΣΗ ΤΟΙΧΟΠΟΙΙΩΝ – ΙΣΟΓΕΙΟΥ** Τετραγωνικά ανά τυπολογία τοίχου · θερμοπρόσοψη 10 / 5 cm ΙΣΟΓΕΙΟ – ΙΣ1	Βάση: κάτοψη τοιχοποιιών T-01 · είδη T-02	**T-03** — · A3 05/11/2026 · R05

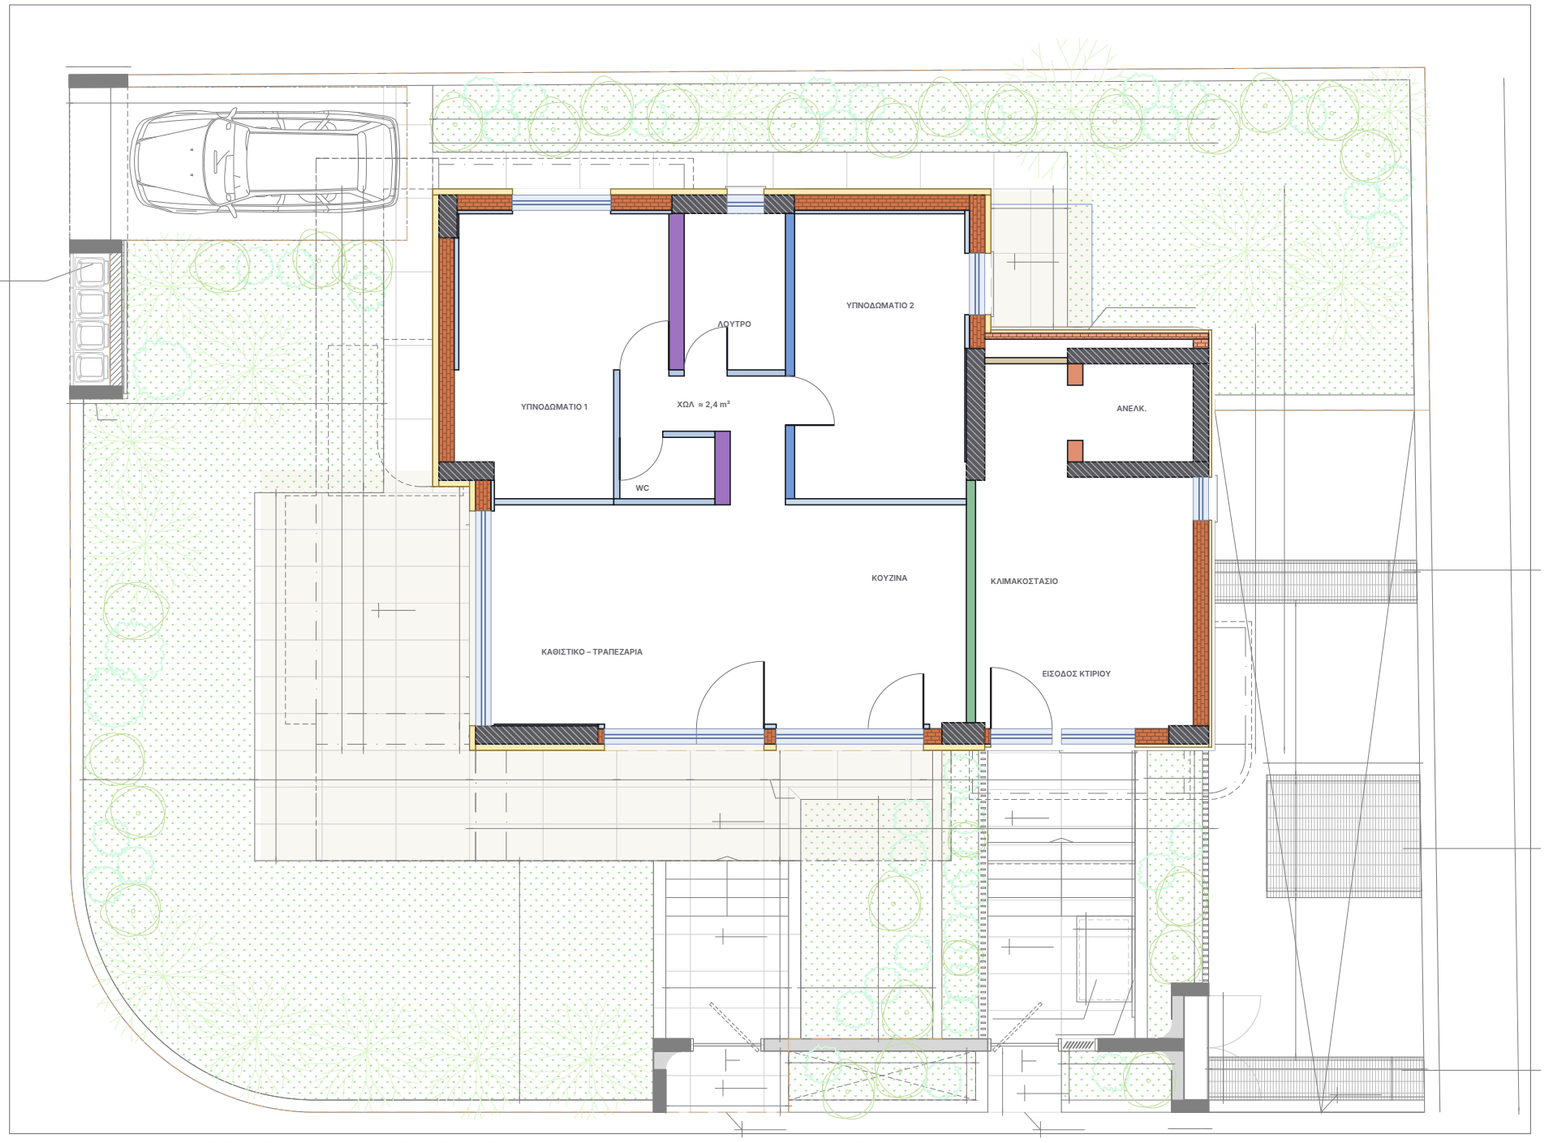

Περιβάλλων χώρος: γεωμετρία A-10-GF (EDGE, μελέτη εφαρμογής 23/07/2026) 1:100, αχνά, χωρίς κείμενα / διαστάσεις · τοιχοποιίες από το T-01 R05 · συντεταγμένες μοντέλου σε m

B

ΠΕΡΙΒΑΛΛΩΝ ΧΩΡΟΣ ΙΣΟΓΕΙΟΥ – όπως τον έχει ο αρχιτέκτονας (A-10-GF)

Το φύλλο δείχνει το οικόπεδο ολόκληρο με τον κήπο, τις βεράντες, τις εισόδους και τη ράμπα όπως τα έχει ο αρχιτέκτονας στο A-10-GF (μόνο η γεωμετρία, χωρίς τα κείμενά του), για να φαίνεται πώς δένουν οι τοιχοποιίες του ισογείου με τον περιβάλλοντα χώρο. Δεν είναι σχέδιο κατασκευής κήπου: για διαστάσεις, στάθμες και φυτεύσεις ισχύουν τα A-10-GF / A-14-GF και η μελέτη περιβάλλοντος χώρου.

ΚΗΠΟΣ ΙΣ1
Χώρος αποκλειστικής χρήσης ΙΣ1 κατοικίας 182,08 m² (σημεία 1…23 του A-10-GF): δυτικά και νότια του κτιρίου, βεράντα ισογείου δυτικά +0,40 (κλίση 1 %) και νότια +0,45 με σκαλιά 1–4 προς −0,30 · προβολές εξώστη / έρκερ με διακεκομμένη.

ΕΙΣΟΔΟΣ ΙΣ1
Από τη νότια περίφραξη: πύλη Θ 1,00/2,20 (x ≈ 5,2–6,2), σκαλιά −0,30 → +0,45, βεράντα, πόρτα Θ0.03 1,10×2,40 (5,00–6,10).

ΣΤΑΘΜΕΥΣΗ
Θ.Σ.Ι.1 13,75 m² στη ΒΔ γωνία του οικοπέδου (θέση στάθμευσης ισογείου), πλάτος 2,50 · μήκος 5,50.

ΦΥΤΕΜΕΝΟΙ ΧΩΡΟΙ
Φ.Χ.1 37,69 m² (βόρεια) · Φ.Χ.2 68,46 (νοτιοδυτικά) · Φ.Χ.3 8,39 · Φ.Χ.4 2,82 · Φ.Χ.5 3,76 · Φ.Χ.6 1,42 · Φ.Χ.7 2,44 m².

ΕΙΣΟΔΟΣ ΚΤΙΡΙΟΥ
Νότια: πύλη πεζών Θ 1,00/2,20 (x ≈ 9,85–10,85) στο −0,45, σκάλα 5 ριχτιών 2,40 (x 9,75–12,15) ως το πλατύσκαλο +0,45 (9,50–12,95 × 9,45–10,25), αναδιπλούμενη πλατφόρμα αναβατορίου ΑΜΕΑ 0,90×1,40 με οδηγό x 8,85–9,75, πόρτα αλουμινίου 1,00×2,40 + σταθερό W0.04 1,20 στο lobby (24,55 m²).

ΒΑ ΒΕΡΑΝΤΑ
Βεράντα ισογείου +0,45, 9,80–11,45 × 0,45–2,70, από την μπαλκονόπορτα W0.06 του Υπν.2 · ανατολικά της φυτεμένος χώρος.

ΟΧΗΜΑΤΑ / ΥΠΟΣΤΑΘΜΟΣ
Ράμπα Ι.Χ. κλίσης 16,12 % στη ΝΑ γωνία (είσοδος – έξοδος οχημάτων, −0,55), μετρητές ΔΕΔΔΗΕ, εσχάρες υποσταθμού: εξαερισμού Ι-Κ-Λ-Μ 3,40×0,60 = 2,04 m² (ανατολικά του lobby) και Ρ-Σ-Τ-Υ 3,52×0,60 = 2,11 m², καταπακτής Ν-Ξ-Ο-Π 2,80×1,80 = 5,02 m² (βλ. A-30-01).

ΕΡΓΟ	ΘΕΜΑ ΣΧΕΔΙΟΥ	ΒΑΣΗ	ΑΡ. ΣΧΕΔΙΟΥ
ΠΕΝΤΑΟΡΟΦΟ ΚΤΗΡΙΟ ΚΑΤΟΙΚΙΩΝ – ΑΡΓΥΡΟΥΠΟΛΗ Κωνσταντινουπόλεως 12 & Αγ. Βαρβάρας · Ο.Τ. 103-15 Εργοδότης: INTERKAT Α.Ε. · Κατασκευή: ARKAD Ι.Κ.Ε.	**ΠΕΡΙΒΑΛΛΩΝ ΧΩΡΟΣ – ΙΣΟΓΕΙΟ** Κήπος ΙΣ1 · βεράντες · είσοδοι · ράμπα κατά A-10-GF ΙΣΟΓΕΙΟ – ΙΣ1	Βάση: γεωμετρία περιβάλλοντος χώρου A-10-GF · τοιχοποιίες T-01	**T-04** **Κλίμακα 1:100 · A3** 05/11/2026 · R05