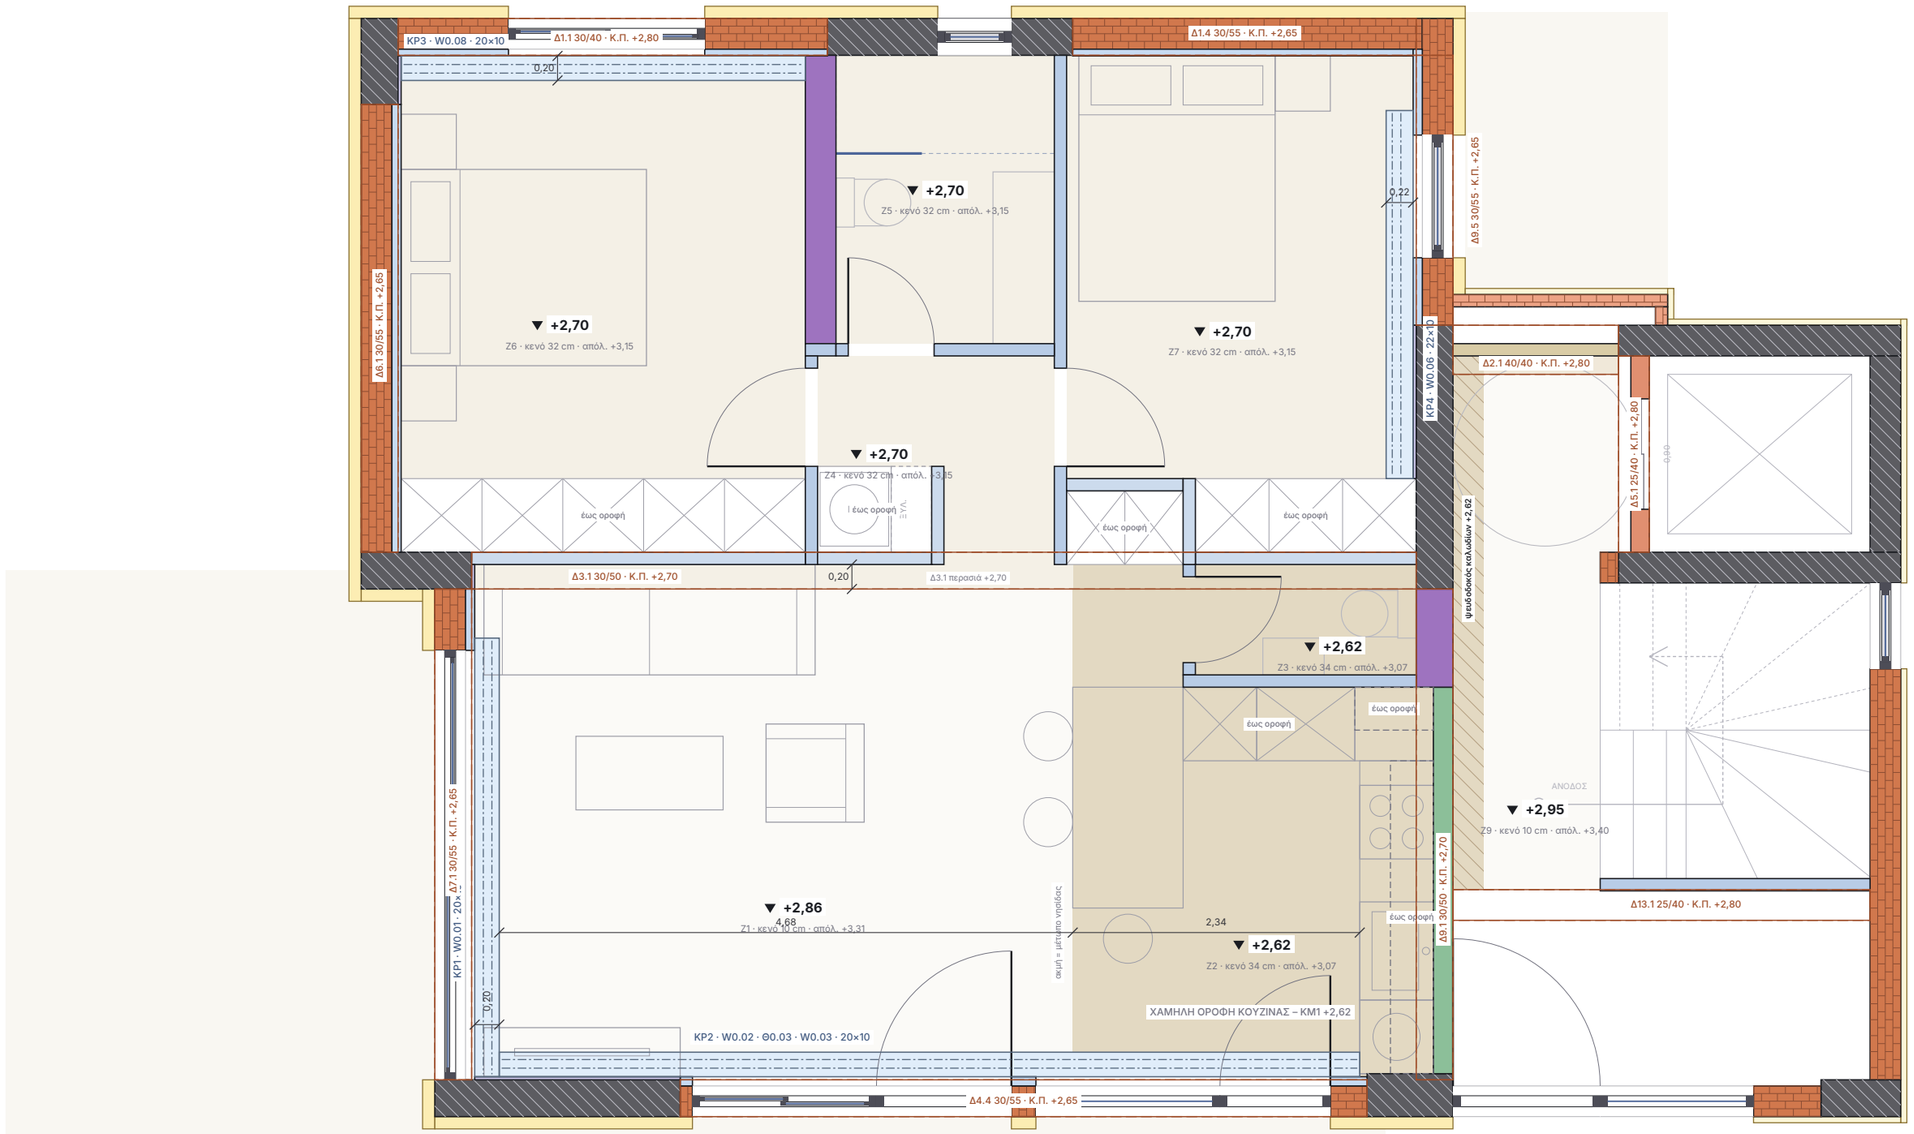


ΣΗΜΕΙΩΣΕΙΣ

Στάθμες από το τελικό δάπεδο του ισογείου – Τ.Δ. θεωρήθηκε +0,45 στο σύστημα του Σ3 (Α1): πάνω παρειά πλάκας +3,20 · κάτω παρειά Π3 h18 +3,02 · Π8 h24 +2,96 · δοκοί 50 +2,70 · 55 +2,65 · 40 +2,80. Σε κάθε στάθμη και η απόλυτη (Σ3).

R02 (ιδιοκτήτης 07/11: «του σαλονιού τη χαμηλή οροφή κάτω από την κουζίνα και το μηχάνημα εκεί»): χαμηλή οροφή +2,62 ΜΟΝΟ πάνω από την κουζίνα (νησίδα, στήλες, πάγκος, προθάλαμος WC), ακμή στο μέτωπο της νησίδας x 6,60 σε όλο το βάθος. Το καθιστικό ελεύθερο +2,86.

R03 (ιδιοκτήτης 09/11: «τα χωλ δεν χρειάζεται να κατέβουν»): χωλ +2,70 = λουτρό / υπνοδωμάτια, περασιά με τη Δ3.1. Η Δ3.1 προεξέχει 0,20 στο καθιστικό (4,95–5,15) → γυψοσανίδα περασιά +2,70: στο πέρασμα από το χωλ μία μόνο αλλαγή (+2,70 → +2,86) στη νότια παρειά της δοκού.

Κουρτινόθηκες ΚΡ1–ΚΡ4: 20 × 10 cm (ΚΡ4 22 cm για τη μπαλκονόπορτα W0.06)· η ΚΡ2 συνεχής σε όλο τον νότιο τοίχο (W0.02 · Θ0.03 · W0.03).


Πάνω από το Υπν.1: λουτρό γονέων Α΄ (Α2).

R04 – ΚΛΙΜΑΚΟΣΤΑΣΙΟ (ιδιοκτήτης 09/11: «καμιά δεκαριά πόντους για φωτισμό – ένα δοκάρι για τα καλώδια»): Ζ9 lobby + πλατύσκαλο +2,95 (10 cm κάτω από την πλάκα h15) · Ζ10 ψευδοδοκός καλωδίων +2,62 στη γραμμή Κ3 · Ζ11 Δ2.1 περασιά +2,80· ακμές στο χείλος της σκάλας και στη Δ13.1 – η είσοδος κτιρίου κατά αρχιτέκτονα.

ΥΠΟΜΝΗΜΑ

- +2,86 καθιστικό = 10 cm κάτω από την Π8 h24 (spot σώμα ≤ 75 mm)
- +2,70 περασιά με δοκό 50: υπνοδωμάτια · λουτρό · χωλ · Δ3.1 στο καθιστικό (κενό 32 cm)
- +2,62 χαμηλή οροφή κουζίνας (ΚΜ1) · WC (8 cm κάτω από τις δοκούς 50)
- ΚΡ εσοχή κουρτίνας ανοιχτή ως την πλάκα · 2 οδηγοί
- δοκός (Σ3) · Κ.Π. = κάτω παρειά από Τ.Δ.

ΕΡΓΟ	ΘΕΜΑ ΣΧΕΔΙΟΥ	ΒΑΣΗ	ΑΡ. ΣΧΕΔΙΟΥ
ΠΕΝΤΑΟΡΟΦΟ ΚΤΗΡΙΟ ΚΑΤΟΙΚΙΩΝ – ΑΡΓΥΡΟΥΠΟΛΗ Κωνσταντινουπόλεως 12 & Αγ. Βαρβάρας · Ο.Τ. 103-15 Εργοδότης: INTERKAT Α.Ε. · Κατασκευή: ARKAD Ι.Κ.Ε.	**ΑΝΟΨΗ – ΣΤΑΘΜΕΣ · ΔΟΚΟΙ · ΚΟΥΡΤΙΝΕΣ** Στάθμες ψευδοροφής · χαμηλή οροφή κουζίνας · δοκοί Σ3 · κουρτίνες ΙΣΟΓΕΙΟ – ΙΣ1 (Τ.Δ. θεωρήθηκε +0,45 στο σύστημα του Σ3)	Βάση: τοιχοποιίες ισογείου R13 · ξυλότυπος Σ3_ΕΦ (+3,65) · ανόψη Β1 R16	**ΑΝ-01** **Κλίμακα 1:50 · Α3** 09/11/2026 · R05

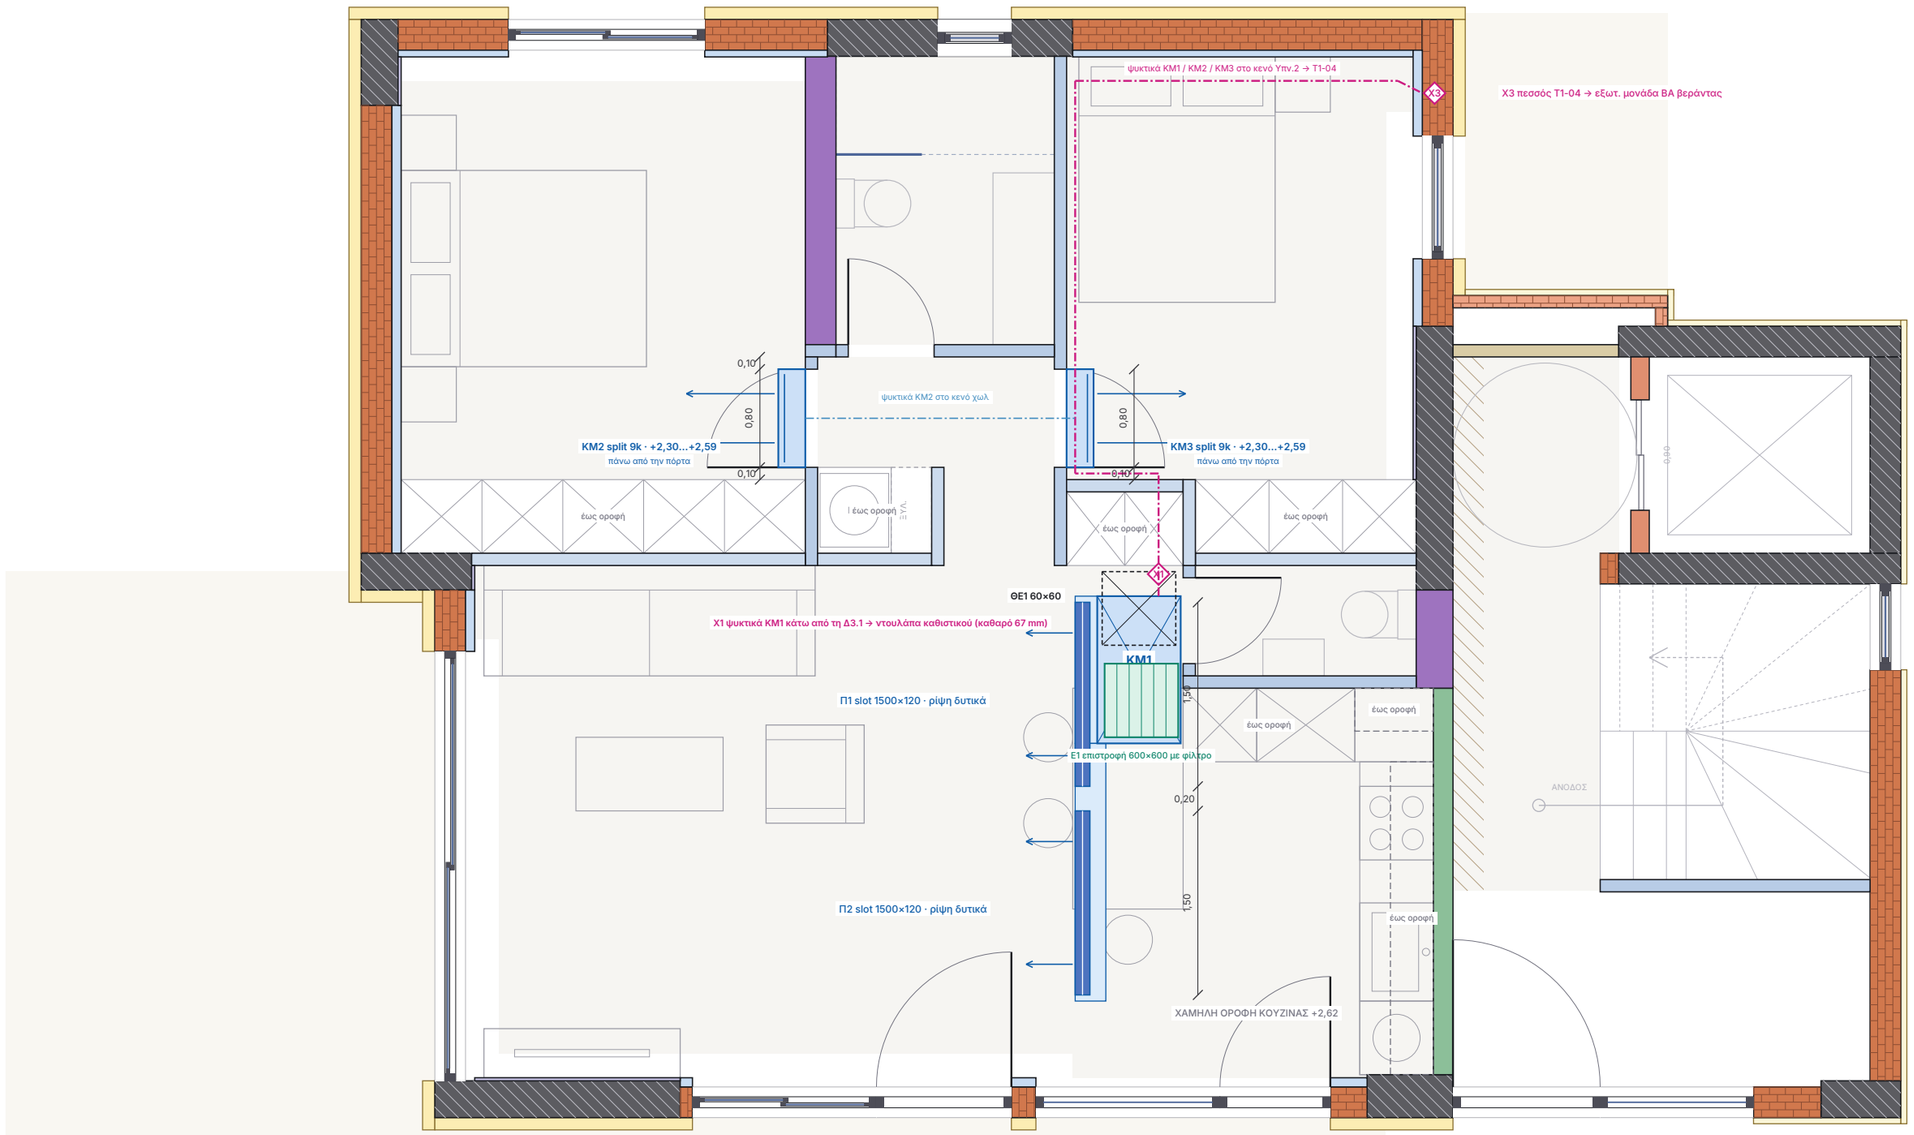

ΣΗΜΕΙΩΣΕΙΣ

R02 – ΚΜ1 ΣΤΗ ΧΑΜΗΛΗ ΟΡΟΦΗ ΤΗΣ ΚΟΥΖΙΝΑΣ (ιδιοκτήτης 07/11): ζώνη +2,62 κάτω από την Π8 +2,96 = 34 cm → ΚΜ1 245 + 10 + 40 = 295 → περιθώριο 45 mm. Η μονάδα πάνω από τον προθάλαμο WC / το βόρειο άκρο της νησίδας (όχι πάνω από εστίες ή στήλες)· Ε1 600×600 επιστροφή με φίλτρο.

R03 – θυρίδες (ιδιοκτήτης 09/11: «μόνο στο καναλάτο μία τετράγωνη από τη μεριά των ηλεκτρικών»): μόνο ΘΕ1 60×60 στο βόρειο άκρο της ΚΜ1 (συνδέσεις / ηλεκτρικό κουτί) – καμία θυρίδα σε λουτρό / Υπν.1 (ΘΕ4 / ΘΕ5 καταργήθηκαν).

Προσαγωγή: κιβώτιο-plenum στο δυτικό πλάι της μονάδας + κανάλι 250×200 κατά μήκος της ακμής → Π1 / Π2 slot 1,50 στην ακμή x 6,60 με ρίψη ΔΥΤΙΚΑ σε όλο το καθιστικό (4,7 m)· ρυθμίστε τις σχισμές οριζόντια (Coanda) ώστε ο αέρας να μην πέφτει στις θέσεις της νησίδας.

Ψυκτικά ΚΜ1: βόρεια κάτω από τη Δ3.1 μέσα από το επάνω μέρος της ντουλάπας καθιστικού (καθαρό 2,70 − 2,62 − 12,5 = 67 mm → χωράει και μόνωση 13 mm) → Τ2Ν-05 → κενό Υπν.2 → Τ1-04 → εξωτερική μονάδα στη ΒΑ βεράντα. Καμία οπή σε δοκό.

R02 – ΥΠΝΟΔΩΜΑΤΙΑ ΜΕ SPLIT (ιδιοκτήτης: «στα δωμάτια δεν θα βάζουμε καναλάτο, θα βάζουμε split σε ένα σημείο που θα βρεις»): ΚΜ2 / ΚΜ3 9k ψηλά ΠΑΝΩ ΑΠΟ ΤΗΝ ΠΟΡΤΑ κάθε δωματίου (τοίχος χωλ, +2,30…+2,59 – 11 cm από την οροφή +2,70, 5 cm πάνω από την κάσα 2,25).

Γιατί εκεί: ο αέρας ρίχνεται κατά μήκος του δωματίου ΔΙΠΛΑ από το κρεβάτι (Υπν.1 κεφαλάρι δυτικά → ρίψη δυτικά 0,42 νότια του κρεβατιού · Υπν.2 κεφαλάρι βόρεια → ρίψη ανατολικά 0,95 νότια από τα πόδια) – όχι στο πρόσωπο· τα ψυκτικά μπαίνουν κατευθείαν στο κενό χωλ / Υπν.2 όπου ήδη περνά η ΚΜ1· τα συμπυκνώματα κατεβαίνουν με φυσική ροή μέσα στον γυψότοιχο στη στήλη Τ7-01 / στο σιφώνι του λουτρού.

Στήριξη split σε γυψότοιχο: ενίσχυση (OSB 18 ή UA) στο υπέρθυρο.

ΥΠΟΜΝΗΜΑ

- KM1 καναλάτη μονάδα (slim ≤ 245 mm)
- KM2 / KM3 split τοίχου (σώμα στον τοίχο, βέλη = ρίψη)
- αεραγωγός / plenum προσαγωγής (μονωμένος, στο κενό)
- Π1 / Π2 γραμμικό slot οροφής 2 σχισμών στην ακμή της χαμήλωσης κουζίνας
- Ε στόμιο / κιβώτιο επιστροφής με φίλτρο
- ΘΕ θυρίδα επίσκεψης τετράγωνη – ΜΟΝΟ στην καναλάτη, στην πλευρά του ηλεκτρικού κουτιού (ιδιοκτήτης 09/11)
- Χ κατέβασμα / έξοδος σωληνώσεων – καμία οπή σε σκυρόδεμα

ΕΡΓΟ	ΘΕΜΑ ΣΧΕΔΙΟΥ	ΒΑΣΗ	ΑΡ. ΣΧΕΔΙΟΥ
ΠΕΝΤΑΟΡΟΦΟ ΚΤΗΡΙΟ ΚΑΤΟΙΚΙΩΝ – ΑΡΓΥΡΟΥΠΟΛΗ Κωνσταντινουπόλεως 12 & Αγ. Βαρβάρας · Ο.Τ. 103-15 Εργοδότης: INTERKAT Α.Ε. · Κατασκευή: ARKAD Ι.Κ.Ε.	**ΑΝΟΨΗ – ΚΛΙΜΑΤΙΣΜΟΣ · ΘΥΡΙΔΕΣ** Καναλάτη ΚΜ1 στη χαμηλή οροφή κουζίνας · split υπνοδωματίων · ψυκτικά ΙΣΟΓΕΙΟ – ΙΣ1 (Τ.Δ. θεωρήθηκε +0,45 στο σύστημα του Σ3)	Βάση: τοιχοποιίες ισογείου R13 · ξυλότυπος Σ3_ΕΦ (+3,65) · ανόψη Β1 R16	**ΑΝ-02** **Κλίμακα 1:50 · Α3** 09/11/2026 · R05



ΕΡΓΟ	ΘΕΜΑ ΣΧΕΔΙΟΥ	ΒΑΣΗ	ΑΡ. ΣΧΕΔΙΟΥ
ΠΕΝΤΑΟΡΟΦΟ ΚΤΗΡΙΟ ΚΑΤΟΙΚΙΩΝ – ΑΡΓΥΡΟΥΠΟΛΗ Κωνσταντινουπόλεως 12 & Αγ. Βαρβάρας · Ο.Τ. 103-15 Εργοδότης: INTERKAT Α.Ε. · Κατασκευή: ARKAD Ι.Κ.Ε.	**ΑΝΟΨΗ – ΦΩΤΙΣΜΟΣ · ΠΥΡΑΝΙΧΝΕΥΣΗ** Χωνευτά spots · κρεμαστά · LED κουζίνας · ανιχνευτές ΙΣΟΓΕΙΟ – ΙΣ1 (Τ.Δ. θεωρήθηκε +0,45 στο σύστημα του Σ3)	Βάση: τοιχοποιίες ισογείου R13 · ξυλότυπος Σ3_ΕΦ (+3,65) · ανόψη Β1 R16	**ΑΝ-03** **Κλίμακα 1:50 · A3** 09/11/2026 · R05

ΣΥΜΜΟΡΦΩΣΗ ΜΕ ΤΙΣ ΠΡΟΔΙΑΓΡΑΦΕΣ (ιδιοκτήτης 07/11/2026)

1 Κλιματισμός — Καναλάτη ΚΜ1 24k στη χαμηλή οροφή της κουζίνας (ιδιοκτήτης 07/11) με slot Π1 / Π2 στην ακμή → καθιστικό · split τοίχου ΚΜ2 / ΚΜ3 στα υπνοδωμάτια πάνω από πόρτες 2,20 (ιδιοκτήτης – ΕΓΚΕΚΡ.) · χώρος 34 cm (περιθώριο 45 mm) · μία θυρίδα ΘΕ1 60×60 · ψυκτικά ΚΜ1 κάτω από τη Δ3.1 με 67 mm.

2 Κουρτίνες — ΚΡ1–ΚΡ4 σε όλα τα ανοίγματα καθιστικού / υπνοδωματίων, 20 (22) × 10 cm, ανοιχτές ως την πλάκα, δίπλα στις δοκούς όψης.

3 Φωτισμός — 22 χωνευτά spots (υπνοδωμάτια, λουτρό, WC, χωλ, κουζίνα, καθιστικό ΚΘ1–ΚΘ7) + LED4 · ΚΡΕΜ0 στο κέντρο του τραπεζιού σαλονιού · ΚΡΕΜ1 στο κέντρο της νησίδας · κανένα spot κάτω από μονάδα / αεραγωγό / σε θυρίδα / πάνω από ντουλάπι.

4 Πυρανίχνευση — ΑΚ1–ΑΚ4 καπνού + ΑΘ5 θερμοδιαφορικός κουζίνας · ≥ 0,50 / 0,50 / 1,00 (χωλ 0,90: στον άξονα).

5 Κατασκευή — Βασική 10 cm κάτω από την πλάκα στο καθιστικό · καταβίβαση μόνο για την καναλάτη (κουζίνα / WC +2,62) · χωλ / υπνοδωμάτια / λουτρό / Δ3.1 +2,70 περασιά με τις δοκούς (R03) · κανένα δόντι.

6 Γενική αρχή — 3 στάθμες· στον ενιαίο χώρο καθιστικού – κουζίνας μία ευθεία στο μέτωπο της νησίδας και η γραμμή της Δ3.1.

ΕΓΚΕΚΡΙΜΕΝΑ / ΑΠΟΦΑΣΕΙΣ ΙΔΙΟΚΤΗΤΗ (07 – 09/11/2026)

· Πόρτες δωματίων 2,20 παντού · θυρίδες μόνο στην καναλάτη, μία τετράγωνη στην πλευρά των ηλεκτρικών · χωλ όχι χαμηλωμένο (R03, 09/11).

· Ψευδοροφή στο κλιμακοστάσιο για τα καλώδια από το shaft στο διαμέρισμα (R04, 09/11).

· Χαμηλή οροφή του σαλονιού πάνω από την κουζίνα, με το μηχάνημα εκεί (R02).

· Υπνοδωμάτια με split τοίχου αντί καναλάτου (R02).

· Μονάδα ΚΜ1 slim ≤ 245 mm ως παραδοχή μέχρι την επιλογή μοντέλου (όπως Β1).

ΑΛΛΑΓΕΣ R03 → R05 – ΚΛΙΜΑΚΟΣΤΑΣΙΟ (ιδιοκτήτης 09/11/2026)

· Κλιμακοστάσιο (ιδιοκτήτης 09/11: «οροφή – από το shaft να φεύγουν καλώδια μέσα στο διαμέρισμα» και «καμιά δεκαριά πόντους για να μπει φωτισμός – μήπως φτιάξουμε κάποιο δοκάρι από το οποίο θα μπαίνουν μέσα»): lobby + πλατύσκαλο +2,95 = 10 cm κάτω από την πλάκα h15 (spots ΚΛ1 / ΚΛ2, ΑΚ6) · η Δ2.1 40/40 περασιά +2,80 · ακμή στη Δ13.1 προς την είσοδο κτιρίου.

· ΨΕΥΔΟΔΟΚΟΣ ΚΑΛΩΔΙΩΝ +2,62 (κουτί γυψοσανίδας 0,25 × 33 cm) στη γραμμή Κ3 (9,70–9,95) από το μέτωπο του shaft ως τη Δ13.1: τα καλώδια βγαίνουν από το shaft μέσα του (κάτω από τη Δ2.1, 167 mm) και στο y 6,40 περνούν μέσα από τον Τ6-01 κάτω από τη Δ9.1 (67,5 mm) στο κενό της χαμηλής οροφής κουζίνας (ίδια στάθμη +2,62). Το ΙΣ1 δεν έχει πόρτα στο lobby.

ΠΡΟΗΓΟΥΜΕΝΗ ΑΝΑΘΕΩΡΗΣΗ

· R04 (09/11): οροφή κλιμακοστασίου ενιαία +2,62 – ιδιοκτήτης: «δε θέλω τόσο κατέβασμα».

· R03 (09/11): χωλ +2,70 και Δ3.1 περασιά · μία θυρίδα ΘΕ1 60×60 · πόρτες 2,20 · R02: χαμηλή οροφή + ΚΜ1 πάνω από την κουζίνα, split υπνοδωματίων.

ΑΝΟΙΚΤΑ ΣΗΜΕΙΑ

· Α1 [ΑΠΟΦΑΣΗ] Τ.Δ. ισογείου στο σύστημα του Σ3: θεωρήθηκε +0,45 (Α-10-GF «ΙΣ1 +0,45») → πλάκα +3,20 από Τ.Δ., καθαρό ύψος καθιστικού 2,86 / υπνοδωματίων 2,70 / κουζίνας 2,62. Αν διαφέρει, αλλάζουν μόνο οι αριθμοί – επιβεβαίωση (τομή Α-30 ή στατικός).

· Α2 [ΣΥΝΤΟΝΙΣΜΟΣ] Το λουτρό γονέων του Α΄ είναι πάνω από το Υπν.1: η στήλη λεκάνης (x ≈ 2,75 · y ≈ 3,37) πέφτει μέσα στο δωμάτιο → εκτροπή στο κενό 32 cm ως τη ντουλάπα (y 4,25–4,85) και κατέβασμα μέσα σε αυτή· καθαριστήριο μέσα στη ντουλάπα (καμία θυρίδα οροφής – ιδιοκτήτης 09/11) – οριστικά στις αποχετεύσεις.

· Α3 [ΑΠΟΦΑΣΗ] Spots καθιστικού ΚΘ1–ΚΘ7 = πρόταση (κύκλωμα λ με dimmer) – μπορούν να αφαιρεθούν χωρίς άλλη αλλαγή.

· Α4 [ΑΠΟΦΑΣΗ] Επάνω ντουλάπια κουζίνας στον Τ6-01 και στη γωνία ως την οροφή +2,62, με LED4 από κάτω – όπως Β1.

· Α6 [ΜΟΝΤΕΛΟ] ΚΜ1 24k slim ≤ 245 mm · ηλεκτρικό κουτί στην πλευρά των συνδέσεων (βόρεια) → ΘΕ1 εκεί, αλλιώς καθρεφτίζεται · split ≤ 290 × 800 mm · μελέτη ψύξης ισογείου.

· Α8 [ΗΛΕΚΤΡΟΛΟΓΙΚΑ] Καλώδια shaft → ΙΣ1 μέσα από τον Τ6-01 (πυράντοχος, διπλός σκελετός) κάτω από τη Δ9.1: πυροφραγή στη διέλευση· θέση πίνακα κατά τα ηλεκτρολογικά. Πλάκα lobby χωρίς ετικέτα στον Σ3 – θεωρήθηκε h15 όπως η Ε.Ζ. 25/15.


· Α7 [ΣΤΑΤΙΚΟΣ] Δοκοί / πλάκες από το παράγωγο σχέδιο γεωμετρίας του Σ3 (εγκεκριμένο 02/2024)· το Σ3_ΕΦ (Κόγιας) να ελεγχθεί πριν τη σκυροδέτηση – κρίσιμα: Π8 h24, Δ3.1 30/50 στο 4,85–5,15, Δ9.1 30/50.

ΕΛΕΓΧΟΣ ΣΥΓΚΡΟΥΣΕΩΝ & ΣΤΑΘΜΩΝ – 76 έλεγχοι · ΟΚ 73 · ΟΡΙΑΚΟ 0 · ΕΓΚΕΚΡ. 3 · ΑΠΟΚΛΙΣΗ 0

Αυτόματος έλεγχος από το μοντέλο (code/anopseis/checks.py): στάθμες ↔ δοκοί · κενό μονάδων · θυρίδες · spots ↔ ζώνες / θυρίδες / μονάδες / αεραγωγοί / κουρτινόθηκες · ανιχνευτές ↔ τοίχοι / φωτιστικά / στόμια · κουρτινόθηκες ↔ κουφώματα / δοκοί.

ΚΩΔ.	ΚΑΤΑΣΤ.	ΣΤΟΙΧΕΙΟ	ΜΕΤΡΗΣΗ
ΣΤ01	ΟΚ	Z2 ΚΟΥΖΙΝΑ – ΧΑΜΗΛΗ ΟΡΟΦΗ ΚΜ1 ↔ Δ3.1 30/50 (Κ.Π. +2.70)	οροφή +2.62 · κρυμμένη 8 cm
ΣΤ02	ΟΚ	Z2 ΚΟΥΖΙΝΑ – ΧΑΜΗΛΗ ΟΡΟΦΗ ΚΜ1 ↔ Δ9.1 30/50 (Κ.Π. +2.70)	οροφή +2.62 · κρυμμένη 8 cm
ΣΤ03	ΟΚ	Z3 WC ↔ Δ3.1 30/50 (Κ.Π. +2.70)	οροφή +2.62 · κρυμμένη 8 cm
ΣΤ04	ΟΚ	Z4 ΧΩΛ ↔ Δ3.1 30/50 (Κ.Π. +2.70)	οροφή +2.70 · περασιά
ΣΤ05	ΟΚ	Z10 ΨΕΥΔΟΔΟΚΟΣ ΚΑΛΩΔΙΩΝ (κλιμακοστάσιο) ↔ Δ2.1 40/40 (Κ…	οροφή +2.62 · κρυμμένη 18 cm
ΣΤ06	ΟΚ	Z11 ΣΑΝΙΔΑ ΚΑΤΩ ΑΠΟ Δ2.1 (lobby) ↔ Δ2.1 40/40 (Κ.Π. +2.80)	οροφή +2.80 · περασιά
ΣΤ07	ΟΚ	Z8 Δ3.1 ΣΤΟ ΚΑΘΙΣΤΙΚΟ (περασιά) ↔ Δ3.1 30/50 (Κ.Π. +2.70)	οροφή +2.70 · περασιά
ΚΛ-ΚΜ1	ΟΚ	ΚΜ1 24.000 Btu/h – καθιστικό – κουζίνα	κενό 340 mm · περιθώριο +45 mm
ΘΕ-ΚΜ1	ΟΚ	ΚΜ1 – πρόσβαση συντήρησης	ΘΕ1
ΚΛ-ΚΜ2	ΟΚ	ΚΜ2 split τοίχου 9.000 Btu/h – Υπνοδωμάτιο 1 (πάνω από την πό…	οροφή +2,70 · μονάδα +2,30…+2,59 · πάνω…
ΚΡ-ΚΜ2	ΟΚ	ΚΜ2 – ρίψη δυτικά, νότια του κρεβατιού	ο άξονας της ρίψης περνά 0,42 νότια του κ…
ΨΣ-ΚΜ2	ΟΚ	ΚΜ2 – ψυκτικά / συμπυκνώματα	ψυκτικά από πίσω στο κενό χωλ (+2,62) → …
ΚΛ-ΚΜ3	ΟΚ	ΚΜ3 split τοίχου 9.000 Btu/h – Υπνοδωμάτιο 2 (πάνω από την πό…	οροφή +2,70 · μονάδα +2,30…+2,59 · πάνω…
ΚΡ-ΚΜ3	ΟΚ	ΚΜ3 – ρίψη ανταλικά, νότια από τα πόδια του κρεβατιού	κεφαλάρι βόρεια (6,65–8,25 × 0,805–2,805…
ΨΣ-ΚΜ3	ΟΚ	ΚΜ3 – ψυκτικά / συμπυκνώματα	ψυκτικά από πίσω κατευθείαν στο κενό Υπν…
ΚΑΛ-ΟΔ	ΟΚ	Όδευση καλωδίων shaft → οροφή κλιμακοστασίου → κουζίνα ΙΣ1	ελάχιστο 300 mm
ΨΥ-ΚΜ1	ΟΚ	Όδευση ψυκτικών ΚΜ1 κουζίνα → ντουλάπα καθιστικού → Υπν.2…	ελάχιστο 280 mm
ΨΥ-ΚΜ2	ΟΚ	Όδευση ψυκτικών split ΚΜ2 Υπν.1 → κενό χωλ → Υπν.2	ελάχιστο 280 mm
ΨΥ-ΔΟΚ	ΟΚ	Διέλευση ψυκτικών ΚΜ1 κάτω από τη Δ3.1 (x ≈ 7.30, ντουλάπα κ…	καθαρό 67.5 mm · περιθώριο +25.6 mm
ΚΑΛ-Δ2.1	ΟΚ	Διέλευση καλωδίων shaft κάτω από τη Δ2.1 (ψευδοδοκός x 9,70…	καθαρό 167.5 mm · περιθώριο +135.5 mm
ΚΑΛ-Δ9.1	ΟΚ	Διέλευση καλωδίων shaft κάτω από τη Δ9.1 (ψευδοδοκός y ≈ 6,40…	καθαρό 67.5 mm · περιθώριο +35.5 mm
ΚΔ-ΚΜ1	ΟΚ	Καθιστικό – κουζίνα (ενιαίος χώρος)	ΚΜ1 καναλάτη στη χαμηλή οροφή της κουζ…
ΚΔ-ΚΜ2	ΕΓΚΕΚΡ.	Υπνοδωμάτιο 1	ΚΜ2 split τοίχου (ιδιοκτήτης 07/11: «στα δ…
ΚΔ-ΚΜ3	ΕΓΚΕΚΡ.	Υπνοδωμάτιο 2	ΚΜ3 split τοίχου (ιδιοκτήτης 07/11: «στα δ…
ΣΤ-Π1	ΟΚ	Π1 slot οροφής 1500×120 · 2 σχισμές	μέσα
ΣΤ-Π2	ΟΚ	Π2 slot οροφής 1500×120 · 2 σχισμές	μέσα
SP-Y1	ΟΚ	Υ1 spot (1.800 · 1.750) – ΥΠΝΟΔΩΜΑΤΙΟ 1	κενό 307 mm · άκρη 0.67
SP-Y2	ΟΚ	Υ2 spot (3.200 · 1.750) – ΥΠΝΟΔΩΜΑΤΙΟ 1	κενό 307 mm · άκρη 0.74
SP-Y3	ΟΚ	Υ3 spot (1.800 · 3.300) – ΥΠΝΟΔΩΜΑΤΙΟ 1	κενό 307 mm · άκρη 0.67
SP-Y4	ΟΚ	Υ4 spot (3.200 · 3.300) – ΥΠΝΟΔΩΜΑΤΙΟ 1	κενό 307 mm · άκρη 0.95
SP-Y5	ΟΚ	Υ5 spot (7.200 · 1.750) – ΥΠΝΟΔΩΜΑΤΙΟ 2	κενό 307 mm · άκρη 0.65
SP-Y6	ΟΚ	Υ6 spot (8.600 · 1.750) – ΥΠΝΟΔΩΜΑΤΙΟ 2	κενό 307 mm · άκρη 0.55
SP-Y7	ΟΚ	Υ7 spot (7.200 · 3.300) – ΥΠΝΟΔΩΜΑΤΙΟ 2	κενό 307 mm · άκρη 0.65
SP-Y8	ΟΚ	Υ8 spot (8.600 · 3.300) – ΥΠΝΟΔΩΜΑΤΙΟ 2	κενό 307 mm · άκρη 0.55
SP-Λ1	ΟΚ	Λ1 spot IP65 (5.560 · 1.200) – ΛΟΥΤΡΟ	κενό 307 mm · άκρη 0.40
SP-Λ2	ΟΚ	Λ2 spot IP44 (5.450 · 2.150) – ΛΟΥΤΡΟ	κενό 307 mm · άκρη 0.78
SP-Λ3	ΟΚ	Λ3 spot IP44 (5.450 · 2.850) – ΛΟΥΤΡΟ	κενό 307 mm · άκρη 0.30
SP-Λ4	ΟΚ	Λ4 spot IP44 (8.400 · 5.300) – WC	κενό 327 mm · άκρη 0.35
SP-X1	ΟΚ	X1 spot (4.900 · 3.700) – ΧΩΛ	κενό 307 mm · άκρη 0.38
SP-X2	ΟΚ	X2 spot (6.000 · 4.600) – ΧΩΛ	κενό 307 mm · άκρη 0.35
SP-M1	ΟΚ	M1 spot (8.220 · 7.000) – ΚΟΥΖΙΝΑ – ΧΑΜΗΛΗ ΟΡΟΦΗ ΚΜ1	κενό 327 mm · άκρη 1.05
SP-M2	ΟΚ	M2 spot (8.220 · 8.400) – ΚΟΥΖΙΝΑ – ΧΑΜΗΛΗ ΟΡΟΦΗ ΚΜ1	κενό 327 mm · άκρη 0.72
SP-ΚΘ1	ΟΚ	ΚΘ1 spot (2.450 · 6.000) – ΚΑΘΙΣΤΙΚΟ	κενό 88 mm · άκρη 0.53
SP-ΚΘ2	ΟΚ	ΚΘ2 spot (2.450 · 7.200) – ΚΑΘΙΣΤΙΚΟ	κενό 88 mm · άκρη 0.53
SP-ΚΘ3	ΟΚ	ΚΘ3 spot (2.450 · 8.400) – ΚΑΘΙΣΤΙΚΟ	κενό 88 mm · άκρη 0.53
SP-ΚΘ4	ΟΚ	ΚΘ4 spot (3.650 · 8.400) – ΚΑΘΙΣΤΙΚΟ	κενό 88 mm · άκρη 0.53
SP-ΚΘ5	ΟΚ	ΚΘ5 spot (4.850 · 8.400) – ΚΑΘΙΣΤΙΚΟ	κενό 88 mm · άκρη 0.53
SP-ΚΘ6	ΟΚ	ΚΘ6 spot (6.050 · 8.400) – ΚΑΘΙΣΤΙΚΟ	κενό 88 mm · άκρη 0.53
SP-ΚΘ7	ΟΚ	ΚΘ7 spot (7.250 · 8.400) – ΚΟΥΖΙΝΑ – ΧΑΜΗΛΗ ΟΡΟΦΗ ΚΜ1	κενό 327 mm · άκρη 0.65
SP-ΚΛ1	ΟΚ	ΚΛ1 spot (10.500 · 3.850) – ΚΛΙΜΑΚΟΣΤΑΣΙΟ – LOBBY (κοινόχρη…	κενό 87 mm · άκρη 0.45
SP-ΚΛ2	ΟΚ	ΚΛ2 spot (10.425 · 6.400) – ΚΛΙΜΑΚΟΣΤΑΣΙΟ – LOBBY (κοινόχρη…	κενό 87 mm · άκρη 0.47
SP-ΚΑΘ	ΟΚ	Καθιστικό	ΚΘ1–ΚΘ7 περιμετρικά (κύκλωμα λ, dimmer)…
ΚΜΣ-ΚΡΕΜ0	ΟΚ	ΚΡΕΜ0 κρεμαστό – τραπέζι σαλονιού	κέντρο (3.15 · 6.65) · Π1 3.47
ΚΜΣ-ΚΡΕΜ1	ΟΚ	ΚΡΕΜ1 κρεμαστό – νησίδα	κέντρο (7.05 · 6.85) · κανένα στόμιο δεν ρί…
ΠΥ-ΑΚ1	ΟΚ	ΑΚ1 καπνού (5.30 · 7.70) – καθιστικό	τοίχος 1.30 · ΚΘ5 0.83 · Π2 1.32
ΠΥ-ΑΚ2	ΟΚ	ΑΚ2 καπνού (2.50 · 2.52) – Υπνοδωμάτιο 1	τοίχος 1.37 · Υ1 1.04 · ΚΜ2 1.89
ΠΥ-ΑΚ3	ΟΚ	ΑΚ3 καπνού (7.90 · 2.52) – Υπνοδωμάτιο 2	τοίχος 1.35 · Υ6 1.04 · ΚΜ3 1.40
ΠΥ-ΑΚ4	ΟΚ	ΑΚ4 καπνού (5.45 · 3.70) – χωλ – άξονας διαδρόμου 0,90 (≥ 1,00…	τοίχος 0.45 (διάδρομος 0,90 – άξονας) · Χ1…
ΠΥ-ΑΘ5	ΟΚ	ΑΘ5 θερμοδιαφορικός (8.22 · 7.70) – κουζίνα – θερμοδιαφορικός…	τοίχος 0.97 · Μ1 0.70 · Π2 1.48
ΠΥ-ΑΚ6	ΟΚ	ΑΚ6 καπνού (10.45 · 4.50) – κλιμακοστάσιο – lobby ανελκυστήρα …	τοίχος 0.50 · ΚΛ1 0.65 · ΚΜ3 3.70
ΠΥ-ΧΩΡ	ΟΚ	Κάλυψη χώρων	καθιστικό · κουζίνα (θερμικός) · Υπν.1 · Υπν…
ΘΕ-ΘΕ1	ΟΚ	ΘΕ1 60×60 – ΚΜ1: στο βόρειο άκρο – πλευρά συνδέσεων / ηλεκτρ…	ελεύθερη
ΘΕ-ΚΑΝ	ΕΓΚΕΚΡ.	Θυρίδες επίσκεψης – κανόνας ιδιοκτήτη 09/11	μόνο ΘΕ1 60×60 στην ΚΜ1 (πλευρά ηλεκτρ…
ΚΡ-ΚΡ1	ΟΚ	ΚΡ1 W0.01 – καθιστικό – Δ · 20 × 10 cm · οδηγοί 7 / 14 cm	πλήρης · βάθος 10 cm
ΚΡ-ΚΡ2	ΟΚ	ΚΡ2 W0.02 · Θ0.03 · W0.03 – καθιστικό – Ν · 20 × 10 cm · οδηγοί 7…	πλήρης · βάθος 10 cm
ΚΡ-ΚΡ3	ΟΚ	ΚΡ3 W0.08 – Υπν.1 – Β · 20 × 10 cm · οδηγοί 7 / 14 cm	πλήρης · βάθος 32 cm
ΚΡ-ΚΡ4	ΟΚ	ΚΡ4 W0.06 – Υπν.2 – Α · 22 × 10 cm · οδηγοί 10 / 17 cm (μπαλκον…	πλήρης · βάθος 32 cm
ΚΡ-W0.07	ΟΚ	W0.07	δεν απαιτείται – λουτρό (στο τοιχείο Κ2)
ΚΡ-W0.05	ΟΚ	W0.05	δεν απαιτείται – κλιμακοστάσιο (εκτός διαμ…
ΣΘ-Ζ1	ΟΚ	Ζ1 +2,86 ↔ Ζ2 +2,62	χαμηλή οροφή κουζίνας / ΚΜ1 – μία ευθεία…
ΣΘ-Ζ1	ΟΚ	Ζ1 +2,86 ↔ Ζ8 +2,70	νότια παρειά της Δ3.1 (5,15) – η δοκός με γυ…
ΣΘ-Ζ8	ΟΚ	Ζ8 +2,70 ↔ Ζ2 +2,62	η Δ3.1 «μπαίνει» στη χαμηλή οροφή της κο…
ΣΘ-Ζ4	ΟΚ	Ζ4 / Ζ5 / Ζ6 / Ζ7 / Ζ8 +2,70	ίδια στάθμη – χωλ, λουτρό, υπνοδωμάτια, Δ…
ΣΘ-Ζ10	ΟΚ	Ζ10 +2,62 ↔ Ζ9 +2,95	κλιμακοστάσιο (R04): ψευδοδοκός καλωδίω…
ΣΘ-Ζ11	ΟΚ	Ζ11 +2,80 ↔ Ζ9 +2,95	γραμμή της Δ2.1 (περασιά) στο μέτωπο του…
ΣΘ-ΣΥΝ	ΟΚ	Στάθμες στο διαμέρισμα	+2.62 · +2.70 · +2.80 · +2.86 · +2.95 (καθιστ…

B

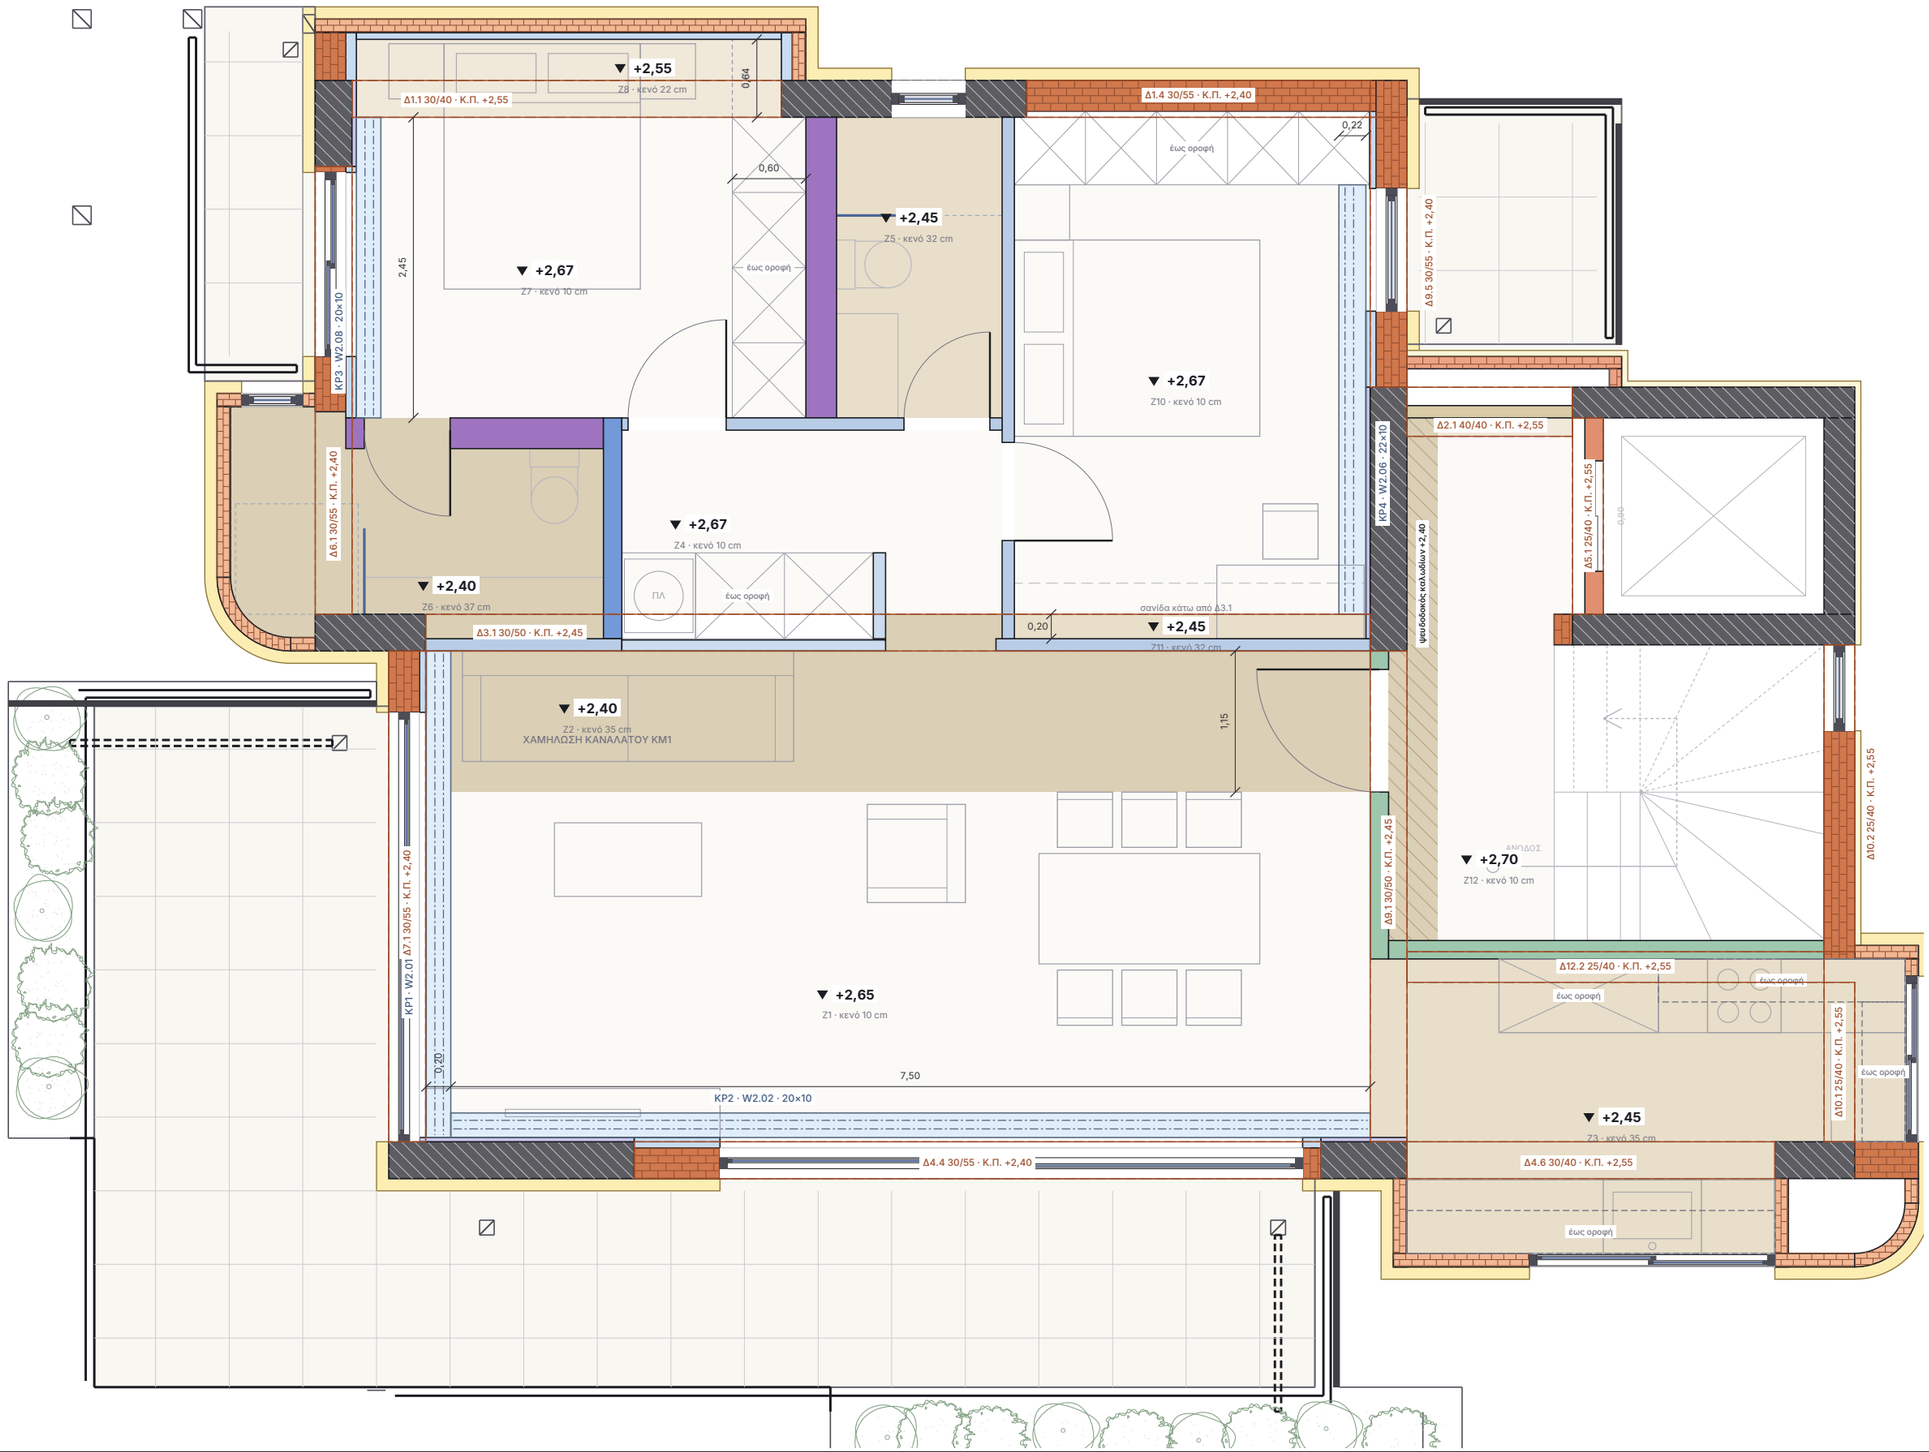

ΣΗΜΕΙΩΣΕΙΣ

Στάθμες από το τελικό δάπεδο του ορόφου (Β΄ +6,90). Πάνω παρειά πλάκας +2,95· κάτω παρειά Π3 h18 +2,77 · Π8 h20 +2,75 · Π10 h15 +2,80.

Κανόνας: πουθενά ψευδοροφή κάτω από κάτω παρειά δοκού· όπου «περασιά» η γυψοσανίδα στη δοκό προσθέτει ≈ 1,5 cm.

Αλλαγές στάθμης ΜΟΝΟ: χαμήλωση ΚΜ1 · γραμμή δοκού Δ9.1 (καθιστικό → κουζίνα) · γραμμή Δ1.1 (κεφαλάρι) · σανίδα κάτω από Δ3.1 στο Υπν.2 · πόρτα λουτρού. R13: χωρίς κουτί ντουλάπας Υπν.1.

Κουρτινόθηκες: 20 × 10 cm (ΚΡ4 22 cm για το ανοιγοανακλινόμενο W2.06), σε όλο το μήκος του τοίχου, δίπλα (όχι κάτω) από τις δοκούς όψης.

R15 – ΚΛΙΜΑΚΟΣΤΑΣΙΟ (ιδιοκτήτης 09/11: «καμιά δεκαριά πόντους για να μπει φωτισμός · ένα δοκάρι από το οποίο θα μπαίνουν τα καλώδια»): Z12 lobby + πλατύσκαλο +2,70 = 10 cm κάτω από την πλάκα h15 · Z13 ψευδοδοκός καλωδίων +2,40 στη γραμμή Κ3 / Δ9.1 (0,25 στο lobby, 0,40 στο πλατύσκαλο – κρύβει και την προεξοχή της Δ9.1) · Z14 Δ2.1 περασιά +2,55. Πάνω από τα σκέλη της σκάλας καμία ψευδοροφή.

R12: ΜΟΝΟ η χαμήλωση της ΚΜ1 –5 cm → +2,40 (κενό 35 cm): η Δ3.1 κρύβεται 5 cm και τα ψυκτικά της ΚΜ1 περνούν από κάτω της προς τη ντουλάπα του χωλ (ιδιοκτήτης 07/11). Το καθιστικό μένει +2,65.


R14 (ιδιοκτήτης 09/11: «τα χωλ δεν χρειάζεται να κατέβουν στο 2,45»): χωλ +2,67 = υπνοδωμάτια (κενό 10 cm: ψυκτικά δίπλα-δίπλα + spots). Στο άνοιγμα προς το καθιστικό η χαμήλωση +2,40 μπαίνει κάτω από τη Δ3.1 ως τη βόρεια παρειά της (4,85) – μία αλλαγή στη γραμμή της δοκού. Ντουλάπα χωλ: μέτωπο ως +2,67, πίσω 0,20 κάτω από τη δοκό καπάκι ≤ +2,40.

ΥΠΟΜΝΗΜΑ

- +2,65 / +2,67 βασική = 10 cm κάτω από την πλάκα (spot σώμα ≤ 75 mm) · υπνοδωμάτια + χωλ (R14)
- +2,55 περασιά με δοκό 40 (κεφαλάρι Υπν.1)
- +2,45 περασιά με δοκό 50: λουτρό · κουζίνα
- +2,40 χαμήλωση ΚΜ1 (5 cm κάτω από Δ3.1 – ψυκτικά) · λουτρό γονέων (περασιά Δ6.1)
- ΚΡ εσοχή κουρτίνας ανοιχτή ως την πλάκα · 2 οδηγοί
- δοκός (Σ5) · Κ.Π. = κάτω παρειά από Τ.Δ.

ΕΡΓΟ	ΘΕΜΑ ΣΧΕΔΙΟΥ	ΒΑΣΗ	ΑΡ. ΣΧΕΔΙΟΥ
ΠΕΝΤΑΟΡΟΦΟ ΚΤΗΡΙΟ ΚΑΤΟΙΚΙΩΝ – ΑΡΓΥΡΟΥΠΟΛΗ Κωνσταντινουπόλεως 12 & Αγ. Βαρβάρας · Ο.Τ. 103-15 Εργοδότης: INTERKAT Α.Ε. · Κατασκευή: ARKAD Ι.Κ.Ε.	**ΑΝΟΨΗ – ΣΤΑΘΜΕΣ · ΔΟΚΟΙ · ΚΟΥΡΤΙΝΕΣ** Στάθμες ψευδοροφής · δοκοί Σ5 · εσοχές κουρτινών Α΄ · Β΄ · Γ΄ ΟΡΟΦΟΣ – Β1 (τυπικός όροφος)	Βάση: τοιχοποιίες Β1 R25 · ξυλότυπος Σ5 (+9,85) · ανόψη R10	**ΑΝ-05** **Κλίμακα 1:50 · Α3** 09/11/2026 · R16

B

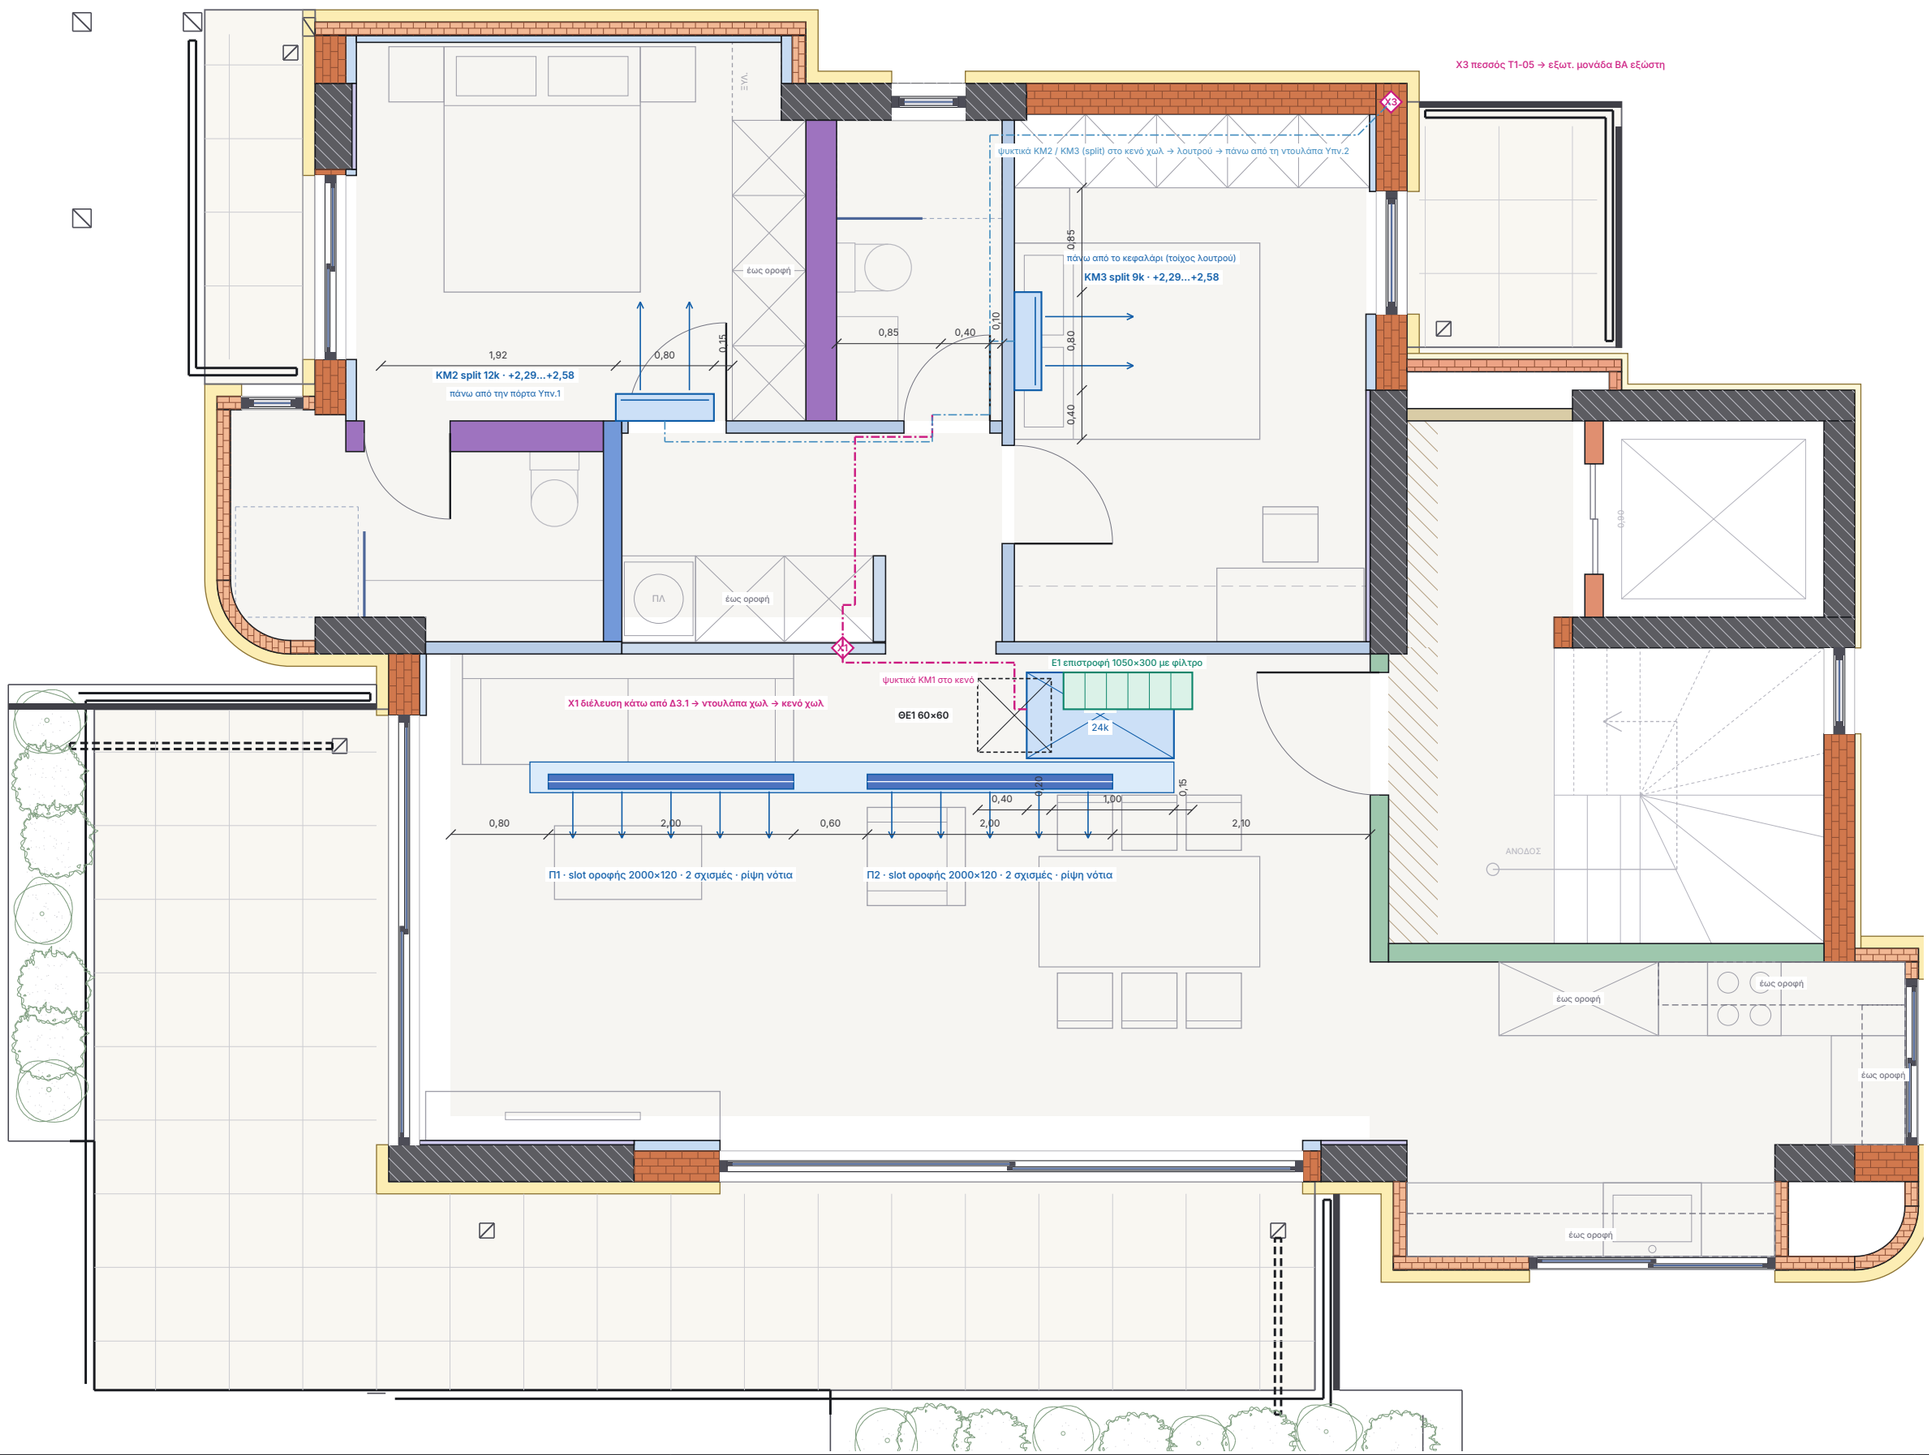

ΣΗΜΕΙΩΣΕΙΣ

Χώρος ΚΜ1 (προδ. 1): χαμήλωση +2,40 κάτω από Π8 +2,75 = 35 cm → 245 + 10 + 40 = 295 → περιθώριο 55 mm. Θυρίδα ΘΕ1 60×60 στο δυτικό άκρο (πλευρά συνδέσεων / ηλεκτρικού κουτιού – ιδιοκτήτης 09/11: «μόνο στο καναλάτο μία τετράγωνη»)· Ε1 επιστροφή με φίλτρο.

R14: θυρίδες ΜΟΝΟ στην καναλάτη – καμία θυρίδα στα λουτρά (ΘΕ4 / ΘΕ5 καταργήθηκαν). Χωλ +2,67: τα ψυκτικά ΚΜ1 / ΚΜ2 στο κενό 10 cm δίπλα-δίπλα.

R13 – ΥΠΝΟΔΩΜΑΤΙΑ ΜΕ SPLIT (ιδιοκτήτης 07/11: «στα δωμάτια δεν θα βάζουμε καναλάτο, θα βάζουμε split σε ένα σημείο που θα βρεις»). Κανόνας θέσης: ψηλά σε εσωτερικό τοίχο, ρίψη κατά μήκος του δωματίου που δεν πέφτει στο προσκέφαλο, ψυκτικά κατευθείαν στο κενό χωλ / λουτρού.

ΚΜ2 12k Υπν.1: ΠΑΝΩ ΑΠΟ ΤΗΝ ΠΟΡΤΑ (3,25–4,05 · +2,29…+2,58, 9 cm από την οροφή +2,67, 4 cm πάνω από την κάσα 2,25). Το κεφαλάρι είναι στο έρκερ (εξωτερικός τοίχος, LED3, Δ1.1 – χωρίς κενό για ψυκτικά) → ο αέρας ρίχνεται βόρεια δίπλα από την ανατολική πλευρά του κρεβατιού.

ΚΜ3 9k Υπν.2: ΠΑΝΩ ΑΠΟ ΤΟ ΚΕΦΑΛΑΡΙ στον τοίχο λουτρού Τ2-02 (2,20–3,00 · +2,29…+2,58), ρίψη ανατολικά προς τα πόδια και το W2.06.

Ψυκτικά split: από πίσω από τη μονάδα μέσα στον γυψότοιχο / υπέρθυρο ως το κενό χωλ (+2,45) / λουτρού → μαζί με την ΚΜ1 → πάνω από τη ντουλάπα Υπν.2 → πεσσός Τ1-05 → εξωτερική μονάδα ΒΑ εξώστη. Συμπυκνώματα με φυσική ροή μέσα στον γυψότοιχο στα σιφώνια των λουτρών (ΚΜ2 → Τ2Α-01 / λουτρό γονέων · ΚΜ3 → Τ2-02 / λουτρό) – χωρίς αντλία.

Ψυκτικά ΚΜ1 (R12, ιδιοκτήτης: «μέσω οροφής και ντουλάπας χωλ»): Χ1 κάτω από τη Δ3.1 μέσα από τον Τ2Ν-01 στη ντουλάπα χωλ (x ≈ 5,10) → κενό χωλ → λουτρό → Τ1-05. ΟΡΙΑΚΟ: καθαρό 37,5 mm → αερίου 5/8″ με μόνωση 9 mm χωράει, 13 mm όχι. Καμία οπή σε δοκό.

Στήριξη split σε γυψότοιχο: ενίσχυση (OSB 18 ή UA) πίσω από τη βάση της μονάδας / στο υπέρθυρο.

ΥΠΟΜΝΗΜΑ

- ΚΜ1 καναλάτη μονάδα (slim ≤ 245 mm)
- ΚΜ2 / ΚΜ3 split τοίχου (σώμα στον τοίχο, βέλη = ρίψη)
- αεραγωγός / plenum προσαγωγής (μονωμένος, στο κενό)
- Π1 / Π2 γραμμικό slot οροφής 2 σχισμών, ρυθμιζόμενη ρίψη
- Ε στόμιο / κιβώτιο επιστροφής με φίλτρο
- ΘΕ θυρίδα επίσκεψης τετράγωνη – ΜΟΝΟ στην καναλάτη, στην πλευρά του ηλεκτρικού κουτιού (ιδιοκτήτης 09/11)
- Χ κατέβασμα / έξοδος σωληνώσεων – καμία οπή σε σκυρόδεμα

ΕΡΓΟ

ΠΕΝΤΑΟΡΟΦΟ ΚΤΗΡΙΟ ΚΑΤΟΙΚΙΩΝ – ΑΡΓΥΡΟΥΠΟΛΗ
Κωνσταντινουπόλεως 12 & Αγ. Βαρβάρας · Ο.Τ. 103-15
Εργοδότης: INTERKAT Α.Ε. · Κατασκευή: ARKAD Ι.Κ.Ε.

ΘΕΜΑ ΣΧΕΔΙΟΥ

ΑΝΟΨΗ – ΚΛΙΜΑΤΙΣΜΟΣ · ΘΥΡΙΔΕΣ
Καναλάτη ΚΜ1 · split υπνοδωματίων · slot · μία θυρίδα 60×60 · ψυκτικά
Α΄ · Β΄ · Γ΄ ΟΡΟΦΟΣ – Β1 (τυπικός όροφος)

ΒΑΣΗ

Βάση: τοιχοποιίες Β1 R25 · ξυλότυπος Σ5 (+9,85) · ανόψη R10

ΑΡ. ΣΧΕΔΙΟΥ

ΑΝ-06
Κλίμακα 1:50 · Α3
09/11/2026 · R16



ΣΗΜΕΙΩΣΕΙΣ

Κατανομή: Υπν. 2 × 2 spots · λουτρά 3 (IP65 στο ντους) · κουζίνα 3 στον άξονα του διαδρόμου + LED κάτω από τα ντουλάπια · χωλ / είσοδος στον άξονα της διαδρομής · καθιστικό ΚΘ1–ΚΘ7. Σύνολο 28 spots + 2 κρεμαστά + LED3 + LED4.

R13 καθιστικό (ιδιοκτήτης: «το κρεμαστό του σαλονιού σε λάθος θέση – σκέψου μήπως βάλουμε και σποτ»): ΚΡΕΜ0 στο ΚΕΝΤΡΟ του τραπεζιού σαλονιού (3,35 · 6,85 – ήταν 4,30 · 7,575, ανάμεσα σε τραπεζάκι και TV), 0,60 από το slot Π1· ΚΡΕΜ1 στο κέντρο της τραπεζαρίας.

Spots καθιστικού ΚΘ1–ΚΘ7 (πρόταση, κύκλωμα λ με dimmer): περιμετρικά στις δύο τζαμαρίες, 0,55 από τις κουρτινόθηκες ΚΡ1 / ΚΡ2, ανά 1,20 – φωτίζουν κουρτίνες και τοίχο TV χωρίς θάμβωση στον καναπέ· το κέντρο μένει στο κρεμαστό.

Πυρανίχνευση (προδ. 4): σε κάθε κύριο χώρο και στο χωλ· ≥ 0,50 από τοίχους / δοκούς / φωτιστικά, ≥ 1,00 από στόμια προσαγωγής και split· λουτρά χωρίς ανιχνευτή καπνού (υδρατμοί). R13: ΑΚ2 (2,70 · 2,00) · ΑΚ3 (7,83 · 3,85).

Κουζίνα (R12): επάνω ντουλάπια περασιά με την οροφή με LED4 από κάτω για τον πάγκο· Μ1–Μ3 γενικός φωτισμός στον άξονα (y 8,86)· ΑΘ5 1,4 m από τις εστίες.

Οπή spot Ø 75–80 ανάμεσα στα προφίλ CD (όχι πάνω τους)· όπου πέφτει σε προφίλ, μετατόπιση του προφίλ – όχι του spot.

R15 – ΚΑΛΩΔΙΑ ΑΠΟ ΤΟ SHAFT (ιδιοκτήτης 09/11): έξοδος από το επάνω μέρος του μετώπου-ντουλάπας Τ8-01 ΜΕΣΑ στον ψευδοδοκό (κάτω από τη Δ2.1, καθαρό 137 mm) → κατά μήκος του Κ3 → πάνω από την πόρτα εισόδου μέσα από τον Τ6Α κάτω από τη Δ9.1 (καθαρό 37,5 mm → σωλήνες ≤ Ø 32 σε μία στρώση, πλάτος ≤ 0,90, πυροφραγή στη διέλευση) → χαμήλωση ΚΜ1 (κενό 35 cm) → πίνακας. Κλιμακοστάσιο: ΚΛ1 / ΚΛ2 κοινοχρήστων (αισθητήρας) + ΑΚ6.

ΥΠΟΜΝΗΜΑ

- χωνευτό spot LED 7–9 W, 2700 K, CRI ≥ 90, UGR < 19, σώμα ≤ 75 mm
- χωνευτό spot IP44 (λουτρά)
- χωνευτό spot IP65 (πάνω από ντους)
- split τοίχου (για συντονισμό – βλ. φύλλο κλιματισμού)
- ΚΡΕΜ παροχή οροφής (κουτί + ενίσχυση ανάρτησης)
- καλώδια από το shaft Η/Μ (■ έξοδος πάνω από το μέτωπο-ντουλάπα Τ8-01) → ψευδοροφή κλιμακοστασίου → διαμέρισμα
- ΑΚ ανιχνευτής καπνού (ΕΠ04 · EN 54-7)
- ΑΘ θερμοδιαφορικός ανιχνευτής (κουζίνα · EN 54-5)
- ακτίνα 0,50 m γύρω από ανιχνευτή – κανένας τοίχος / φωτιστικό μέσα
- LED κρυφό γραμμικό 3000 K – LED3 κεφαλάρι · LED4 κάτω από τα ντουλάπια κουζίνας

ΕΡΓΟ

ΠΕΝΤΑΟΡΟΦΟ ΚΤΗΡΙΟ ΚΑΤΟΙΚΙΩΝ – ΑΡΓΥΡΟΥΠΟΛΗ
Κωνσταντινουπόλεως 12 & Αγ. Βαρβάρας · Ο.Τ. 103-15
Εργοδότης: INTERKAT Α.Ε. · Κατασκευή: ARKAD Ι.Κ.Ε.

ΘΕΜΑ ΣΧΕΔΙΟΥ

ΑΝΟΨΗ – ΦΩΤΙΣΜΟΣ · ΠΥΡΑΝΙΧΝΕΥΣΗ
Χωνευτά spots · παροχές · κρυφό LED · ανιχνευτές
Α΄ · Β΄ · Γ΄ ΟΡΟΦΟΣ – Β1 (τυπικός όροφος)

ΒΑΣΗ

Βάση: τοιχοποιίες Β1 R25 · ξυλότυπος Σ5 (+9,85) · ανόψη R10

ΑΡ. ΣΧΕΔΙΟΥ

AN-07
Κλίμακα 1:50 · A3
09/11/2026 · R16

ΣΥΜΜΟΡΦΩΣΗ ΜΕ ΤΙΣ ΠΡΟΔΙΑΓΡΑΦΕΣ (ιδιοκτήτης 07/11/2026)

1 Κλιματισμός	Καναλάτη ΚΜ1 24k στο καθιστικό / κουζίνα (κουζίνα από την ΚΜ1 – ΕΓΚΕΚΡ.) με slot Π1/Π2 · υπνοδωμάτια με split τοίχου ΚΜ2 / ΚΜ3 πάνω από πόρτα 2,20 / κεφαλάρι (ιδιοκτήτης – ΕΓΚΕΚΡ.) · χώρος 35 cm (περιθώριο 55 mm) · μία θυρίδα ΘΕ1 60×60 (ιδιοκτήτης 09/11) · ψυκτικά ΚΜ1 κάτω από τη Δ3.1 (οριακό 3,6 mm).
2 Κουρτίνες	ΚΡ1–ΚΡ4 σε όλα τα ανοίγματα καθιστικού / υπνοδωματίων, 20 (22) × 10 cm, 2 οδηγοί, ανοιχτές ως την πλάκα, δίπλα στις δοκούς όψης.
3 Φωτισμός	28 χωνευτά spots σε όλους τους χώρους (καθιστικό ΚΘ1–ΚΘ7 περιμετρικά – R13) + ΚΡΕΜ0 στο κέντρο του τραπεζιού σαλονιού + ΚΡΕΜ1 τραπεζαρίας + LED3 / LED4 · IP44/IP65 στα λουτρά · κανένα spot κάτω από μονάδα / αεραγωγό / σε θυρίδα / πάνω από ντουλάπι.
4 Πυρανίχνευση	ΑΚ1–ΑΚ4 καπνού + ΑΘ5 θερμοδιαφορικός κουζίνας · όλοι ≥ 0,50 από τοίχους / δοκούς / φωτιστικά και ≥ 1,00 από στόμια / split.
5 Κατασκευή	Βασική 10 cm κάτω από την πλάκα (καθιστικό, υπνοδωμάτια, χωλ – R14) · μεγαλύτερη καταβύθιση μόνο στην καναλάτη ΚΜ1 (+2,40) · λουτρό / κουζίνα περασιά με τις δοκούς (+2,45) · μία σανίδα κάτω από τη Δ3.1 στο Υπν.2 (εξαίρεση) · κανένα δόντι.
6 Γενική αρχή	5 στάθμες, κάθε αλλαγή πάνω σε γραμμή δοκού ή σε πόρτα· υπνοδωμάτια και χωλ ενιαία +2,67 (R14)· κλιμακοστάσιο +2,40 + ψευδοδοκός καλωδίων +2,40 στη γραμμή Κ3 / Δ9.1 (R15).

ΕΓΚΕΚΡΙΜΕΝΑ / ΑΠΟΦΑΣΕΙΣ ΙΔΙΟΚΤΗΤΗ (07 – 09/11/2026)

- Πόρτες δωματίων 2,20 παντού · θυρίδες μόνο στην καναλάτη, μία τετράγωνη στην πλευρά των ηλεκτρικών · χωλ όχι στο 2,45 (R14, 09/11).
- Ψευδοροφή στο κλιμακοστάσιο για τα καλώδια από το shaft στο διαμέρισμα (R15, 09/11).
- Υπνοδωμάτια με split τοίχου αντί καναλάτου (R13: «στα δωμάτια δεν θα βάζουμε καναλάτο, θα βάζουμε split»).
- Κουζίνα χωρίς δική της καναλάτη – καλύπτεται από την ΚΜ1 24k.
- Μονάδα ΚΜ1 slim ≤ 245 mm ως παραδοχή μέχρι την επιλογή μοντέλου.
- Η απόφαση R02 «καθιστικό χωρίς spots» αναθεωρείται (R13: «σκέψου μήπως βάλουμε και σποτ») – τα ΚΘ1–ΚΘ7 είναι πρόταση (Α6).

ΑΛΛΑΓΕΣ R14 → R16 – ΚΛΙΜΑΚΟΣΤΑΣΙΟ (ιδιοκτήτης 09/11/2026)

- Κλιμακοστάσιο (ιδιοκτήτης 09/11: «να βάλουμε μια οροφή – από το shaft να φεύγουν καλώδια μέσα στο διαμέρισμα» και «δε θέλω τόσο κατέβασμα, καμιά δεκαριά πόντους για να μπει και φωτισμός – μήπως φτιάξουμε κάποιο δοκάρι από το οποίο θα μπαίνουν μέσα»): lobby ανελκυστήρα + πλατύσκαλο +2,70 = 10 cm κάτω από την πλάκα h15 (spots ΚΛ1 / ΚΛ2) · η Δ2.1 40/40 περασιά +2,55.
- ΨΕΥΔΟΔΟΚΟΣ ΚΑΛΩΔΙΩΝ +2,40 (κουτί γυψοσανίδας) στη γραμμή Κ3 / Δ9.1: 0,25 στο lobby (9,70–9,95), 0,40 στο πλατύσκαλο (9,55–9,95, κρύβει την προεξοχή της Δ9.1), από το μέτωπο του shaft ως τον ντίτο τοίχο – μία ευθεία x 9,95. Τα καλώδια βγαίνουν από το shaft μέσα του (κάτω από τη Δ2.1, 137 mm) και μπαίνουν στο διαμέρισμα πάνω από την πόρτα εισόδου κάτω από τη Δ9.1 (37,5 mm – σωλήνες ≤ Ø 32 σε μία στρώση).
- Ανιχνευτής ΑΚ6 στο lobby ανελκυστήρα.

ΠΡΟΗΓΟΥΜΕΝΗ ΑΝΑΘΕΩΡΗΣΗ

- R15 (09/11): οροφή κλιμακοστασίου ενιαία +2,40 με τα καλώδια στο κενό – ιδιοκτήτης: «δε θέλω τόσο κατέβασμα».
- R14 (09/11): χωλ +2,67 · μία θυρίδα ΘΕ1 60×60 στην ΚΜ1 · πόρτες 2,20 · R13: split στα υπνοδωμάτια · ΚΡΕΜ0 στο τραπέζι σαλονιού · ΚΘ1–ΚΘ7.

ΑΝΟΙΚΤΑ ΣΗΜΕΙΑ


- Α1 [ΚΑΤΑΣΚΕΥΗ] Διέλευση ψυκτικών ΚΜ1 κάτω από τη Δ3.1: καθαρό ύψος 2,45 – 2,40 – γυψοσανίδα 12,5 = 37,5 mm. Χωράει σωλήνας αερίου 5/8″ με μόνωση 9 mm (Ø ≈ 34) – με μόνωση 13 mm (Ø ≈ 42) OXI. Στο σημείο διέλευσης χωρίς περιμετρικό UD, οι σωλήνες δίπλα-δίπλα (όχι ο ένας πάνω στον άλλο)· στη ντουλάπα χωλ επάνω καπάκι ≤ +2,40 στα νότια 0,25 (κάτω από τη δοκό). Αν ο ψυκτικός θέλει 13 mm: χαμήλωση στο +2,38.
- Α2 [ΜΟΝΤΕΛΟ] ΚΜ1: ύψος ≤ 245 mm · ηλεκτρικό κουτί στην πλευρά των συνδέσεων (δυτικά) → ΘΕ1 60×60 εκεί· αν το μοντέλο το έχει ανατολικά, η ΘΕ1 καθρεφτίζεται στο ανατολικό άκρο (ίδιο μέγεθος). Split ΚΜ2 / ΚΜ3: ύψος ≤ 290, πλάτος ≤ 800 mm.
- Α6 [ΑΠΟΦΑΣΗ] Spots καθιστικού ΚΘ1–ΚΘ7 = πρόταση (η απόφαση R02 ήταν «χωρίς spots»)· σε δικό τους κύκλωμα λ με dimmer – μπορούν να αφαιρεθούν χωρίς άλλη αλλαγή.
- Α3 [ΣΤΑΤΙΚΟΣ] Διατομή Δ10.1 (χωρίς ετικέτα στον Σ5 – θεωρήθηκε 25/40). Δεν επηρεάζει τη στάθμη της κουζίνας (+2,45 ≤ 2,55).
- Α7 [ΣΤΑΤΙΚΟΣ] Πλάκα πάνω από το lobby ανελκυστήρα χωρίς ετικέτα στον Σ5 (ανάμεσα στη Δ2.1 και την Ε.Ζ. 25/15) – θεωρήθηκε h15 όπως η Ε.Ζ. 25/15 και το lobby του Σ7· αν είναι h20 η οροφή του lobby πάει +2,65 (spots).
- Α8 [ΗΛΕΚΤΡΟΛΟΓΙΚΑ] Καλώδια πάνω από την πόρτα εισόδου κάτω από τη Δ9.1: καθαρό 37,5 mm → σωλήνες ≤ Ø 32 δίπλα-δίπλα σε μία στρώση (πλάτος ≤ 0,90)· πυροφραγή στη διέλευση του Τ6Α (πυράντοχος τοίχος κλιμακοστασίου)· θέση πίνακα διαμερίσματος κατά τα ηλεκτρολογικά.
- Α4 [ΕΠΙ ΤΟΠΟΥ] Μέτρηση πλακών / δοκών μετά το ξεκαλούπωμα κάθε ορόφου (Α΄ Σ4 · Β΄ Σ5 · Γ΄ Σ6) πριν τη χάραξη – η ανόψη θεωρεί ίδιους δοκούς στους τρεις τυπικούς ορόφους· οι Σ4 / Σ6 να ελεγχθούν.

ΕΛΕΓΧΟΣ ΣΥΓΚΡΟΥΣΕΩΝ & ΣΤΑΘΜΩΝ – 92 έλεγχοι · ΟΚ 86 · ΟΡΙΑΚΟ 2 · ΕΓΚΕΚΡ. 4 · ΑΠΟΚΛΙΣΗ 0

Αυτόματος έλεγχος από το μοντέλο (code/anopseis/checks.py): στάθμες ↔ δοκοί · κενό μονάδων · θυρίδες · spots ↔ ζώνες / θυρίδες / μονάδες / αεραγωγοί / κουρτινόθηκες · ανιχνευτές ↔ τοίχοι / φωτιστικά / στόμια · κουρτινόθηκες ↔ κουφώματα / δοκοί.

ΚΩΔ.	ΚΑΤΑΣΤ.	ΣΤΟΙΧΕΙΟ	ΜΕΤΡΗΣΗ
ΣΤ01	ΟΚ	Ζ2 ΧΑΜΗΛΩΣΗ ΚΑΝΑΛΑΤΟΥ / ΕΙΣΟΔΟΣ ↔ Δ3.1 30/50 (Κ.Π. +2.4…	οροφή +2.40 · κρυμμένη 5 cm
ΣΤ02	ΟΚ	Ζ3 ΚΟΥΖΙΝΑ ↔ Δ9.1 30/50 (Κ.Π. +2.45)	οροφή +2.45 · περασιά
ΣΤ03	ΟΚ	Ζ3 ΚΟΥΖΙΝΑ ↔ Δ4.6 30/40 (Κ.Π. +2.55)	οροφή +2.45 · κρυμμένη 10 cm
ΣΤ04	ΟΚ	Ζ3 ΚΟΥΖΙΝΑ ↔ Δ12.2 25/40 (Κ.Π. +2.55)	οροφή +2.45 · κρυμμένη 10 cm
ΣΤ05	ΟΚ	Ζ3 ΚΟΥΖΙΝΑ ↔ Δ10.1 25/40 (Κ.Π. +2.55)	οροφή +2.45 · κρυμμένη 10 cm
ΣΤ06	ΟΚ	Ζ6 ΛΟΥΤΡΟ ΓΟΝΕΩΝ ↔ Δ6.1 30/55 (Κ.Π. +2.40)	οροφή +2.40 · περασιά
ΣΤ07	ΟΚ	Ζ6 ΛΟΥΤΡΟ ΓΟΝΕΩΝ ↔ Δ3.1 30/50 (Κ.Π. +2.45)	οροφή +2.40 · κρυμμένη 5 cm
ΣΤ08	ΟΚ	Ζ8 ΚΕΦΑΛΑΡΙ ΥΠΝ.1 (έρκερ) ↔ Δ1.1 30/40 (Κ.Π. +2.55)	οροφή +2.55 · περασιά
ΣΤ09	ΟΚ	Ζ11 ΣΑΝΙΔΑ ΚΑΤΩ ΑΠΟ Δ3.1 (Υπν.2) ↔ Δ3.1 30/50 (Κ.Π. +2.45)	οροφή +2.45 · περασιά
ΣΤ10	ΟΚ	Ζ13 ΨΕΥΔΟΔΟΚΟΣ ΚΑΛΩΔΙΩΝ (κλιμακοστάσιο) ↔ Δ9.1 30/50 (Κ…	οροφή +2.40 · κρυμμένη 5 cm
ΣΤ11	ΟΚ	Ζ13 ΨΕΥΔΟΔΟΚΟΣ ΚΑΛΩΔΙΩΝ (κλιμακοστάσιο) ↔ Δ2.1 40/40 (Κ…	οροφή +2.40 · κρυμμένη 15 cm
ΣΤ12	ΟΚ	Ζ14 ΣΑΝΙΔΑ ΚΑΤΩ ΑΠΟ Δ2.1 (lobby) ↔ Δ2.1 40/40 (Κ.Π. +2.55)	οροφή +2.55 · περασιά
ΚΛ-ΚΜ1	ΟΚ	ΚΜ1 24.000 Btu/h – καθιστικό – τραπεζαρία – κουζίνα	κενό 350 mm · περιθώριο +55 mm
ΘΕ-ΚΜ1	ΟΚ	ΚΜ1 – πρόσβαση συντήρησης	ΘΕ1
ΚΛ-ΚΜ2	ΟΚ	ΚΜ2 split τοίχου 12.000 Btu/h – Υπνοδωμάτιο 1 (πάνω από την πό…	οροφή +2,67 · μονάδα +2,29…+2,58 · πάν…
ΚΡ-ΚΜ2	ΟΚ	ΚΜ2 – ρίψη βόρεια κατά μήκος της ανατολικής πλευράς του κρε…	το κεφαλάρι είναι στο έρκερ (εξωτ. τοίχος …
ΨΣ-ΚΜ2	ΟΚ	ΚΜ2 – ψυκτικά / συμπυκνώματα	ψυκτικά από πίσω μέσα στο υπέρθυρο στο κ…
ΚΛ-ΚΜ3	ΟΚ	ΚΜ3 split τοίχου 9.000 Btu/h – Υπνοδωμάτιο 2 (πάνω από το κεφ…	οροφή +2,67 · μονάδα +2,29…+2,58 · πάνω…
ΚΡ-ΚΜ3	ΟΚ	ΚΜ3 – ρίψη ανατολικά κατά μήκος του κρεβατιού	πάνω από το κεφαλάρι – ο αέρας πέφτει π…
ΨΣ-ΚΜ3	ΟΚ	ΚΜ3 – ψυκτικά / συμπυκνώματα	ψυκτικά από πίσω στο κενό λουτρού → πάν…
ΚΑΛ-ΟΔ	ΟΚ	Όδευση καλωδίων shaft → οροφή κλιμακοστασίου → είσοδος δια…	ελάχιστο 310 mm
ΨΥ-ΚΜ1	ΟΚ	Όδευση ψυκτικών ΚΜ1 χαμήλωση → ντουλάπα χωλ → κενό χωλ…	ελάχιστο 60 mm
ΨΥ-ΚΜ2	ΟΚ	Όδευση ψυκτικών split ΚΜ2 / ΚΜ3 κενό χωλ → λουτρό → Τ1-05	ελάχιστο 60 mm
ΨΥ-ΔΟΚ	ΟΡΙΑΚΟ	Διέλευση ψυκτικών ΚΜ1 κάτω από τη Δ3.1 (x ≈ 5.10, Τ2Ν-01 → ντο…	καθαρό 37.5 mm · περιθώριο +3.6 mm
ΚΑΛ-Δ2.1	ΟΚ	Διέλευση καλωδίων shaft κάτω από τη Δ2.1 (ψευδοδοκός x 9,70…	καθαρό 137.5 mm · περιθώριο +105.5 mm
ΚΑΛ-Δ9.1	ΟΡΙΑΚΟ	Διέλευση καλωδίων shaft κάτω από τη Δ9.1 (ψευδοδοκός y ≈ 5,8…	καθαρό 37.5 mm · περιθώριο +5.5 mm
ΚΔ-ΚΜ1	ΟΚ	Καθιστικό – τραπεζαρία	ΚΜ1 καναλάτη
ΚΔ-ΚΜ2	ΕΓΚΕΚΡ.	Υπνοδωμάτιο 1	ΚΜ2 split τοίχου (ιδιοκτήτης 07/11: «στα δ…
ΚΔ-ΚΜ3	ΕΓΚΕΚΡ.	Υπνοδωμάτιο 2	ΚΜ3 split τοίχου (ιδιοκτήτης 07/11: «στα δ…
ΚΔ-ΚΟΥΖ	ΕΓΚΕΚΡ.	Κουζίνα	από την ΚΜ1 (ανοιχτή στο καθιστικό)
ΣΤ-Π1	ΟΚ	Π1 slot οροφής 2000×120 · 2 σχισμές	μέσα
ΣΤ-Π2	ΟΚ	Π2 slot οροφής 2000×120 · 2 σχισμές	μέσα
SP-Υ1	ΟΚ	Υ1 spot (1.765 · 1.550) – ΥΠΝΟΔΩΜΑΤΙΟ 1	κενό 88 mm · άκρη 0.63
SP-Υ2	ΟΚ	Υ2 spot (3.770 · 1.550) – ΥΠΝΟΔΩΜΑΤΙΟ 1	κενό 88 mm · άκρη 0.75
SP-Υ3	ΟΚ	Υ3 spot (1.765 · 2.650) – ΥΠΝΟΔΩΜΑΤΙΟ 1	κενό 88 mm · άκρη 0.60
SP-Υ4	ΟΚ	Υ4 spot (3.770 · 2.650) – ΥΠΝΟΔΩΜΑΤΙΟ 1	κενό 88 mm · άκρη 0.60
SP-Υ5	ΟΚ	Υ5 spot (7.130 · 1.850) – ΥΠΝΟΔΩΜΑΤΙΟ 2	κενό 88 mm · άκρη 0.50
SP-Υ6	ΟΚ	Υ6 spot (8.530 · 1.850) – ΥΠΝΟΔΩΜΑΤΙΟ 2	κενό 88 mm · άκρη 0.50
SP-Υ7	ΟΚ	Υ7 spot (7.130 · 4.250) – ΥΠΝΟΔΩΜΑΤΙΟ 2	κενό 88 mm · άκρη 0.60
SP-Υ8	ΟΚ	Υ8 spot (8.530 · 4.250) – ΥΠΝΟΔΩΜΑΤΙΟ 2	κενό 88 mm · άκρη 0.60
SP-Λ1	ΟΚ	Λ1 spot IP65 (5.600 · 1.250) – ΛΟΥΤΡΟ	κενό 307 mm · άκρη 0.45
SP-Λ2	ΟΚ	Λ2 spot IP44 (5.600 · 2.050) – ΛΟΥΤΡΟ	κενό 307 mm · άκρη 0.55
SP-Λ3	ΟΚ	Λ3 spot IP44 (5.600 · 2.850) – ΛΟΥΤΡΟ	κενό 307 mm · άκρη 0.40
SP-Λ4	ΟΚ	Λ4 spot IP65 (0.470 · 4.150) – ΛΟΥΤΡΟ ΓΟΝΕΩΝ	κενό 358 mm · άκρη 0.36
SP-Λ5	ΟΚ	Λ5 spot IP44 (1.600 · 4.150) – ΛΟΥΤΡΟ ΓΟΝΕΩΝ	κενό 358 mm · άκρη 0.70
SP-Λ6	ΟΚ	Λ6 spot IP44 (2.500 · 4.150) – ΛΟΥΤΡΟ ΓΟΝΕΩΝ	κενό 358 mm · άκρη 0.65
SP-Χ1	ΟΚ	Χ1 spot (3.650 · 3.850) – ΧΩΛ	κενό 88 mm · άκρη 0.35
SP-Χ2	ΟΚ	Χ2 spot (5.925 · 4.700) – ΧΩΛ	κενό 88 mm · άκρη 0.15
SP-Ε1	ΟΚ	Ε1 spot (8.800 · 5.500) – ΧΑΜΗΛΩΣΗ ΚΑΝΑΛΑΤΟΥ / ΕΙΣΟΔΟΣ	κενό 338 mm · άκρη 0.35
SP-Ε2	ΟΚ	Ε2 spot (8.800 · 6.050) – ΧΑΜΗΛΩΣΗ ΚΑΝΑΛΑΤΟΥ / ΕΙΣΟΔΟΣ	κενό 338 mm · άκρη 0.25
SP-Μ1	ΟΚ	Μ1 spot (10.280 · 8.860) – ΚΟΥΖΙΝΑ	κενό 337 mm · άκρη 0.63
SP-Μ2	ΟΚ	Μ2 spot (11.430 · 8.860) – ΚΟΥΖΙΝΑ	κενό 337 mm · άκρη 1.20
SP-Μ3	ΟΚ	Μ3 spot (12.580 · 8.860) – ΚΟΥΖΙΝΑ	κενό 337 mm · άκρη 0.31
SP-ΚΘ1	ΟΚ	ΚΘ1 spot (2.450 · 7.200) – ΚΑΘΙΣΤΙΚΟ – ΤΡΑΠΕΖΑΡΙΑ	κενό 88 mm · άκρη 0.55
SP-ΚΘ2	ΟΚ	ΚΘ2 spot (2.450 · 8.360) – ΚΑΘΙΣΤΙΚΟ – ΤΡΑΠΕΖΑΡΙΑ	κενό 88 mm · άκρη 0.55
SP-ΚΘ3	ΟΚ	ΚΘ3 spot (3.650 · 8.360) – ΚΑΘΙΣΤΙΚΟ – ΤΡΑΠΕΖΑΡΙΑ	κενό 88 mm · άκρη 0.55
SP-ΚΘ4	ΟΚ	ΚΘ4 spot (4.850 · 8.360) – ΚΑΘΙΣΤΙΚΟ – ΤΡΑΠΕΖΑΡΙΑ	κενό 88 mm · άκρη 0.55
SP-ΚΘ5	ΟΚ	ΚΘ5 spot (6.050 · 8.360) – ΚΑΘΙΣΤΙΚΟ – ΤΡΑΠΕΖΑΡΙΑ	κενό 88 mm · άκρη 0.55
SP-ΚΘ6	ΟΚ	ΚΘ6 spot (7.250 · 8.360) – ΚΑΘΙΣΤΙΚΟ – ΤΡΑΠΕΖΑΡΙΑ	κενό 88 mm · άκρη 0.55
SP-ΚΘ7	ΟΚ	ΚΘ7 spot (8.450 · 8.360) – ΚΑΘΙΣΤΙΚΟ – ΤΡΑΠΕΖΑΡΙΑ	κενό 88 mm · άκρη 0.55
SP-ΚΛ1	ΟΚ	ΚΛ1 spot (10.500 · 3.850) – ΚΛΙΜΑΚΟΣΤΑΣΙΟ – LOBBY (κοινόχρη…	κενό 87 mm · άκρη 0.45
SP-ΚΛ2	ΟΚ	ΚΛ2 spot (10.425 · 6.400) – ΚΛΙΜΑΚΟΣΤΑΣΙΟ – LOBBY (κοινόχρη…	κενό 87 mm · άκρη 0.47
SP-ΚΑΘ	ΟΚ	Καθιστικό – τραπεζαρία	ΚΘ1–ΚΘ7 περιμετρικά (κύκλωμα λ, dimmer)…
ΚΜΣ-ΚΡΕΜ0	ΟΚ	ΚΡΕΜ0 κρεμαστό – τραπέζι σαλονιού	κέντρο (3.35 · 6.85) · Π1 0.60
ΚΜΣ-ΚΡΕΜ1	ΟΚ	ΚΡΕΜ1 κρεμαστό – τραπεζαρία	κέντρο (7.60 · 7.25) · Π2 1.04
ΠΥ-ΑΚ1	ΟΚ	ΑΚ1 καπνού (8.24 · 7.17) – καθιστικό – τραπεζαρία (R05: 0,55 από…	τοίχος 0.87 · ΚΡΕΜ1 0.64 · Π2 1.32
ΠΥ-ΑΚ2	ΟΚ	ΑΚ2 καπνού (2.70 · 2.00) – Υπνοδωμάτιο 1 (R13: ≥ 1,00 από το spli…	τοίχος 1.20 · Υ1 1.04 · ΚΜ2 1.17
ΠΥ-ΑΚ3	ΟΚ	ΑΚ3 καπνού (7.83 · 3.85) – Υπνοδωμάτιο 2 (R13: εκτός ρίψης ΚΜ…	τοίχος 1.00 · Υ8 0.81 · ΚΜ3 1.40
ΠΥ-ΑΚ4	ΟΚ	ΑΚ4 καπνού (5.21 · 3.85) – χωλ – άξονας διαδρόμου 1,00	τοίχος 0.50 · Λ3 1.07 · ΚΜ2 1.31
ΠΥ-ΑΘ5	ΟΚ	ΑΘ5 θερμοδιαφορικός (10.86 · 8.86) – κουζίνα – θερμοδιαφορικό…	τοίχος 0.60 · Μ2 0.57 · Π2 4.41
ΠΥ-ΑΚ6	ΟΚ	ΑΚ6 καπνού (10.45 · 4.50) – κλιμακοστάσιο – lobby ανελκυστήρα …	τοίχος 0.50 · ΚΛ1 0.65 · Π2 3.55
ΠΥ-ΧΩΡ	ΟΚ	Κάλυψη χώρων	καθιστικό · Υπν.1 · Υπν.2 · χωλ · κουζίνα (Θ…
ΘΕ-ΘΕ1	ΟΚ	ΘΕ1 60×60 – ΚΜ1: στο δυτικό άκρο – πλευρά συνδέσεων / ηλεκτρ…	ελεύθερη
ΘΕ-ΚΑΝ	ΕΓΚΕΚΡ.	Θυρίδες επίσκεψης – κανόνας ιδιοκτήτη 09/11	μόνο ΘΕ1 60×60 στην ΚΜ1 (πλευρά ηλεκτρ…
ΚΡ-ΚΡ1	ΟΚ	ΚΡ1 W2.01 – καθιστικό – Δ · 20 × 10 cm · οδηγοί 7 / 14 cm	πλήρης · βάθος 10 cm
ΚΡ-ΚΡ2	ΟΚ	ΚΡ2 W2.02 – καθιστικό – Ν · 20 × 10 cm · οδηγοί 7 / 14 cm	πλήρης · βάθος 10 cm
ΚΡ-ΚΡ3	ΟΚ	ΚΡ3 W2.08 – Υπν.1 – Δ · 20 × 10 cm · οδηγοί 7 / 14 cm	πλήρης · βάθος 10 cm
ΚΡ-ΚΡ4	ΟΚ	ΚΡ4 W2.06 – Υπν.2 – Α · 22 × 10 cm · οδηγοί 10 / 17 cm (ανοιγοα…	πλήρης · βάθος 10 cm
ΚΡ-W2.03	ΟΚ	W2.03	δεν απαιτείται – κουζίνα – πάνω από τον ν…
ΚΡ-W2.04	ΟΚ	W2.04	δεν απαιτείται – κουζίνα – έρκερ, πάνω από…
ΚΡ-W2.05	ΟΚ	W2.05	δεν απαιτείται – κλιμακοστάσιο (εκτός διαμ…
ΚΡ-W2.07	ΟΚ	W2.07	δεν απαιτείται – λουτρό (στο τοιχείο Κ2)
ΚΡ-W2.09	ΟΚ	W2.09	δεν απαιτείται – λουτρό γονέων (ντους)
ΣΘ-Ζ1	ΟΚ	Ζ1 +2,65 ↔ Ζ2 +2,40	χαμήλωση καναλάτου ΚΜ1 (προδ. 1/5)
ΣΘ-Ζ4	ΟΚ	Ζ4 +2,67 ↔ Ζ2 +2,40	στη βόρεια παρειά της Δ3.1 (άνοιγμα χωλ –…
ΣΘ-Ζ4	ΟΚ	Ζ4 +2,67 ↔ Ζ5 +2,45	χωλ ↔ λουτρό – μόνο στην πόρτα (αποχέ…
ΣΘ-Ζ1	ΟΚ	Ζ1 +2,65 ↔ Ζ3 +2,45	στη γραμμή της δοκού Δ9.1 (περασιά)
ΣΘ-Ζ7	ΟΚ	Ζ7 +2,67 ↔ Ζ8 +2,55	στη γραμμή της δοκού Δ1.1 (κεφαλάρι έρκε…
ΣΘ-Ζ10	ΟΚ	Ζ10 +2,67 ↔ Ζ11 +2,45	σανίδα κάτω από τη Δ3.1 (εξαίρεση προδ. …
ΣΘ-Ζ13	ΟΚ	Ζ13 +2,40 ↔ Ζ12 +2,70	κλιμακοστάσιο (R15): ψευδοδοκός καλωδίω…
ΣΘ-Ζ14	ΟΚ	Ζ14 +2,55 ↔ Ζ12 +2,70	γραμμή της Δ2.1 (περασιά) στο μέτωπο του…
ΣΘ-ΣΥΝ	ΟΚ	Στάθμες στο διαμέρισμα	+2.40 · +2.45 · +2.55 · +2.65 · +2.67 · +2.70…

B

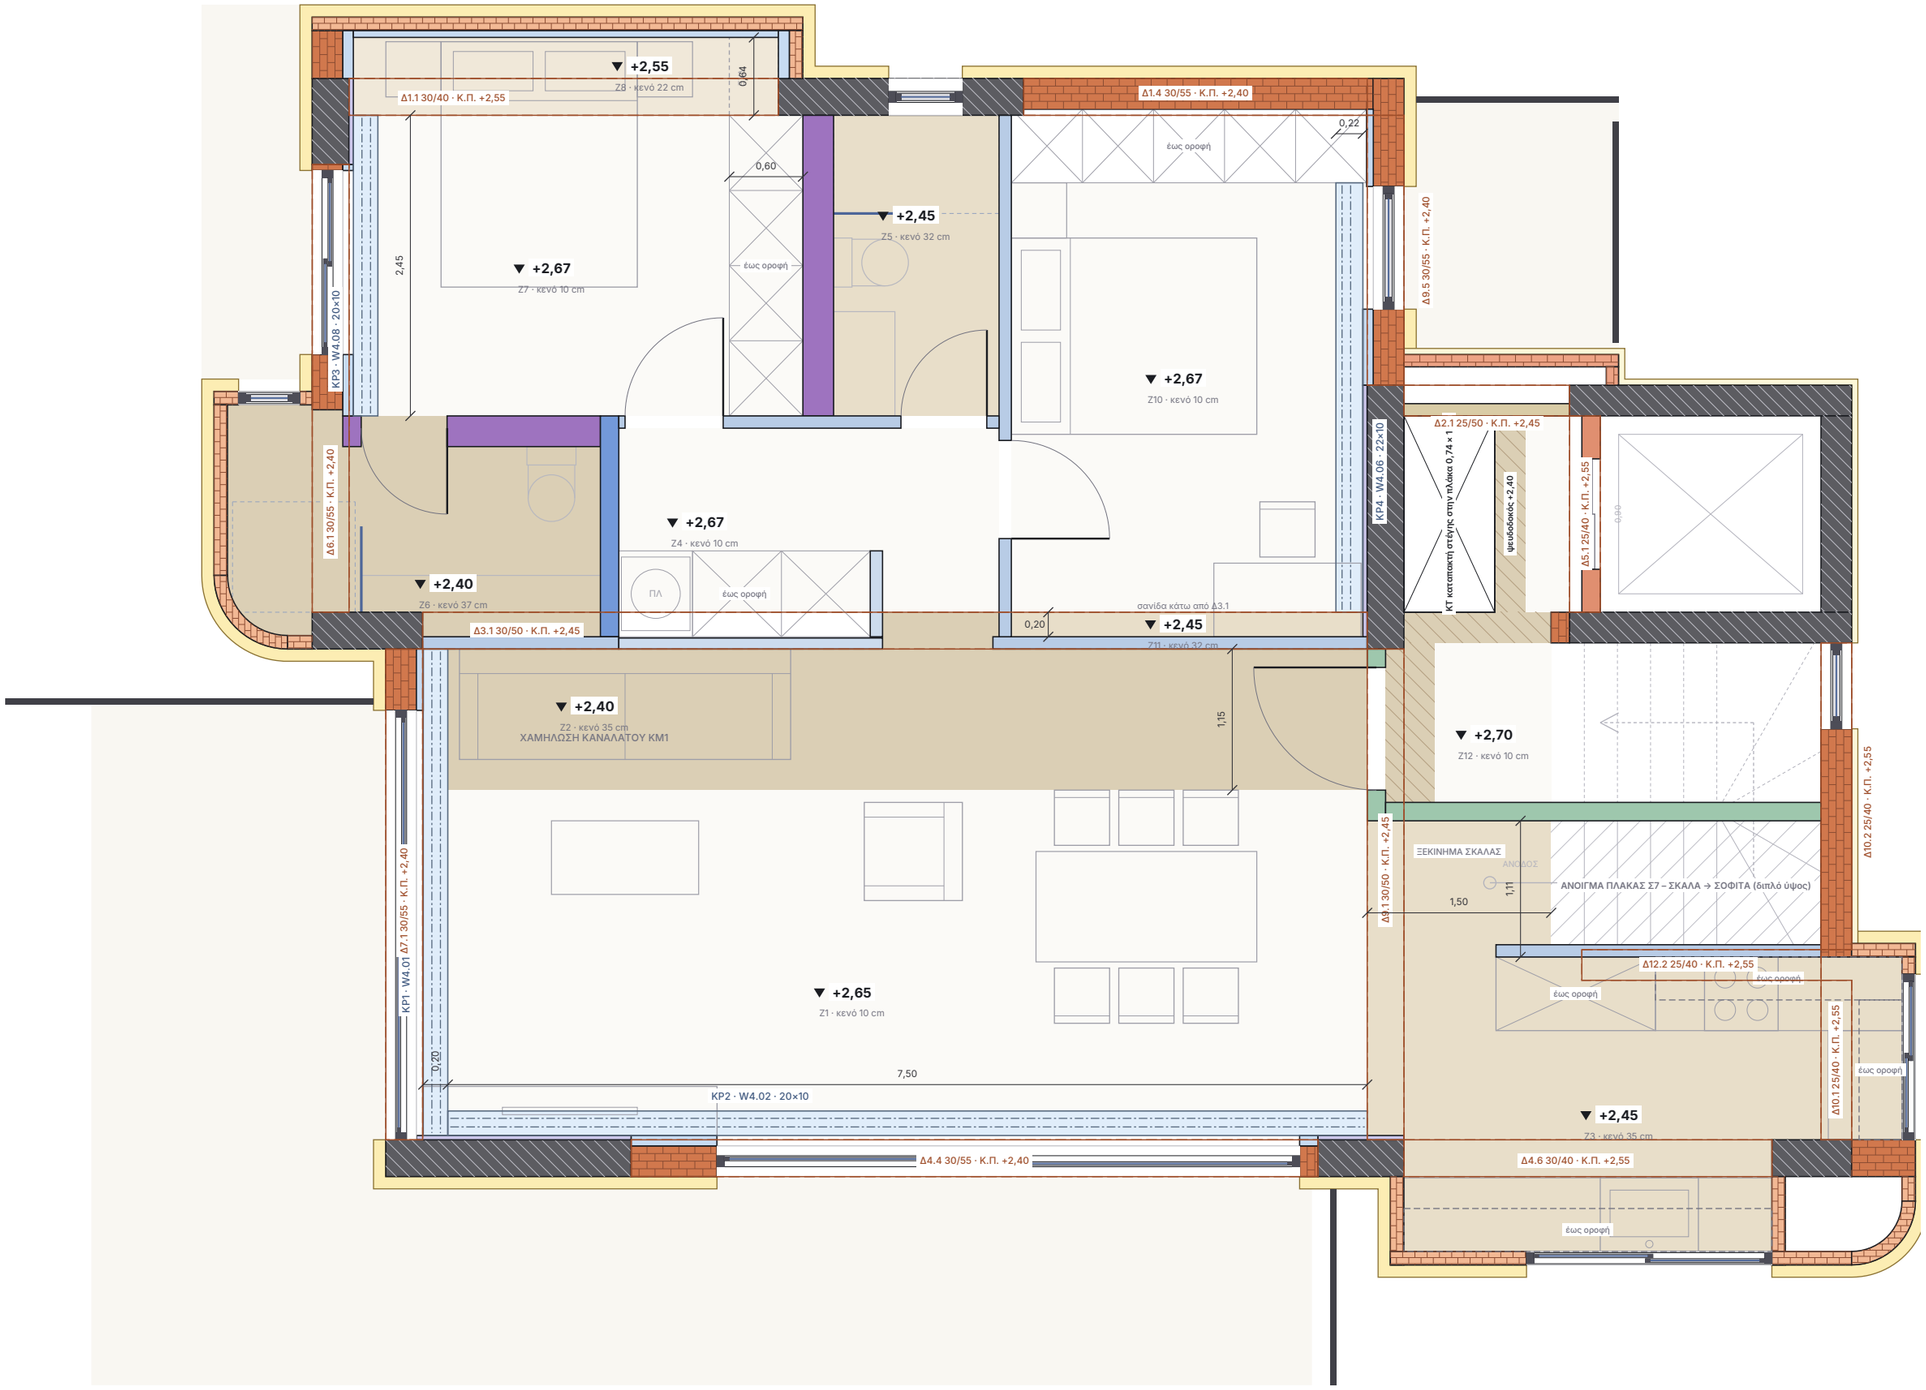

ΣΗΜΕΙΩΣΕΙΣ

Στάθμες από το τελικό δάπεδο του Δ΄ (+13,10). Πάνω παρειά πλάκας Σ7 +2,95 (+16,05)· κάτω παρειά Π3 h18 +2,77 · Π8 h20 +2,75 · Π10 h15 +2,80 (όπως Σ5 – Α4).

Ίδιο διαμέρισμα με το Β1: ίδιες στάθμες R14 (καθιστικό +2,65 · χαμήλωση ΚΜ1 +2,40 · κουζίνα / λουτρό +2,45 · λουτρό γονέων +2,40 · υπνοδωμάτια + χωλ +2,67).

Ξεκίνημα ιδιωτικής σκάλας 9,40–10,90: +2,45 ενιαίο με την κουζίνα, περασιά με τη Δ9.1. Στο 10,90 τελειώνει η ψευδοροφή στο άνοιγμα της πλάκας (γωνιόκρανο) – βλ. Α3.


Κουρτινόθηκες ΚΡ1–ΚΡ4: 20 × 10 cm (ΚΡ4 22), όπως Β1.

Πάνω από το Υπν.2: λουτρό / WC σοφίτας (Α5) · πάνω από καθιστικό / κουζίνα / Υπν.1: δώμα (Α6).

ΥΠΟΜΝΗΜΑ

- +2,65 / +2,67 βασική = 10 cm κάτω από την πλάκα (spot σώμα ≤ 75 mm) · υπνοδωμάτια + χωλ (R14)
- +2,55 περασιά με δοκό 40 (κεφαλάρι Υπν.1)
- +2,45 περασιά με δοκό 50: χωλ · λουτρό · κουζίνα · ξεκίνημα σκάλας
- +2,40 χαμήλωση ΚΜ1 (5 cm κάτω από Δ3.1 – ψυκτικά) · λουτρό γονέων (περασιά Δ6.1)
- ΚΡ εσοχή κουρτίνας ανοιχτή ως την πλάκα · 2 οδηγοί
- δοκός (Σ7) · Κ.Π. = κάτω παρειά από Τ.Δ.

ΕΡΓΟ	ΘΕΜΑ ΣΧΕΔΙΟΥ	ΒΑΣΗ	ΑΡ. ΣΧΕΔΙΟΥ
ΠΕΝΤΑΟΡΟΦΟ ΚΤΗΡΙΟ ΚΑΤΟΙΚΙΩΝ – ΑΡΓΥΡΟΥΠΟΛΗ Κωνσταντινουπόλεως 12 & Αγ. Βαρβάρας · Ο.Τ. 103-15 Εργοδότης: INTERKAT Α.Ε. · Κατασκευή: ARKAD Ι.Κ.Ε.	**ΑΝΟΨΗ – ΣΤΑΘΜΕΣ · ΔΟΚΟΙ · ΚΟΥΡΤΙΝΕΣ** Στάθμες ψευδοροφής · δοκοί Σ7 · εσοχές κουρτινών · ξεκίνημα σκάλας Δ΄ ΟΡΟΦΟΣ – Δ1 κάτω επίπεδο (μεζονέτα)	Βάση: τοιχοποιίες Δ΄ R04 · ξυλότυπος Σ7_ΕΦ (+16,05) · ανόψη Β1 R16	**ΑΝ-09** **Κλίμακα 1:50 · Α3** 09/11/2026 · R05

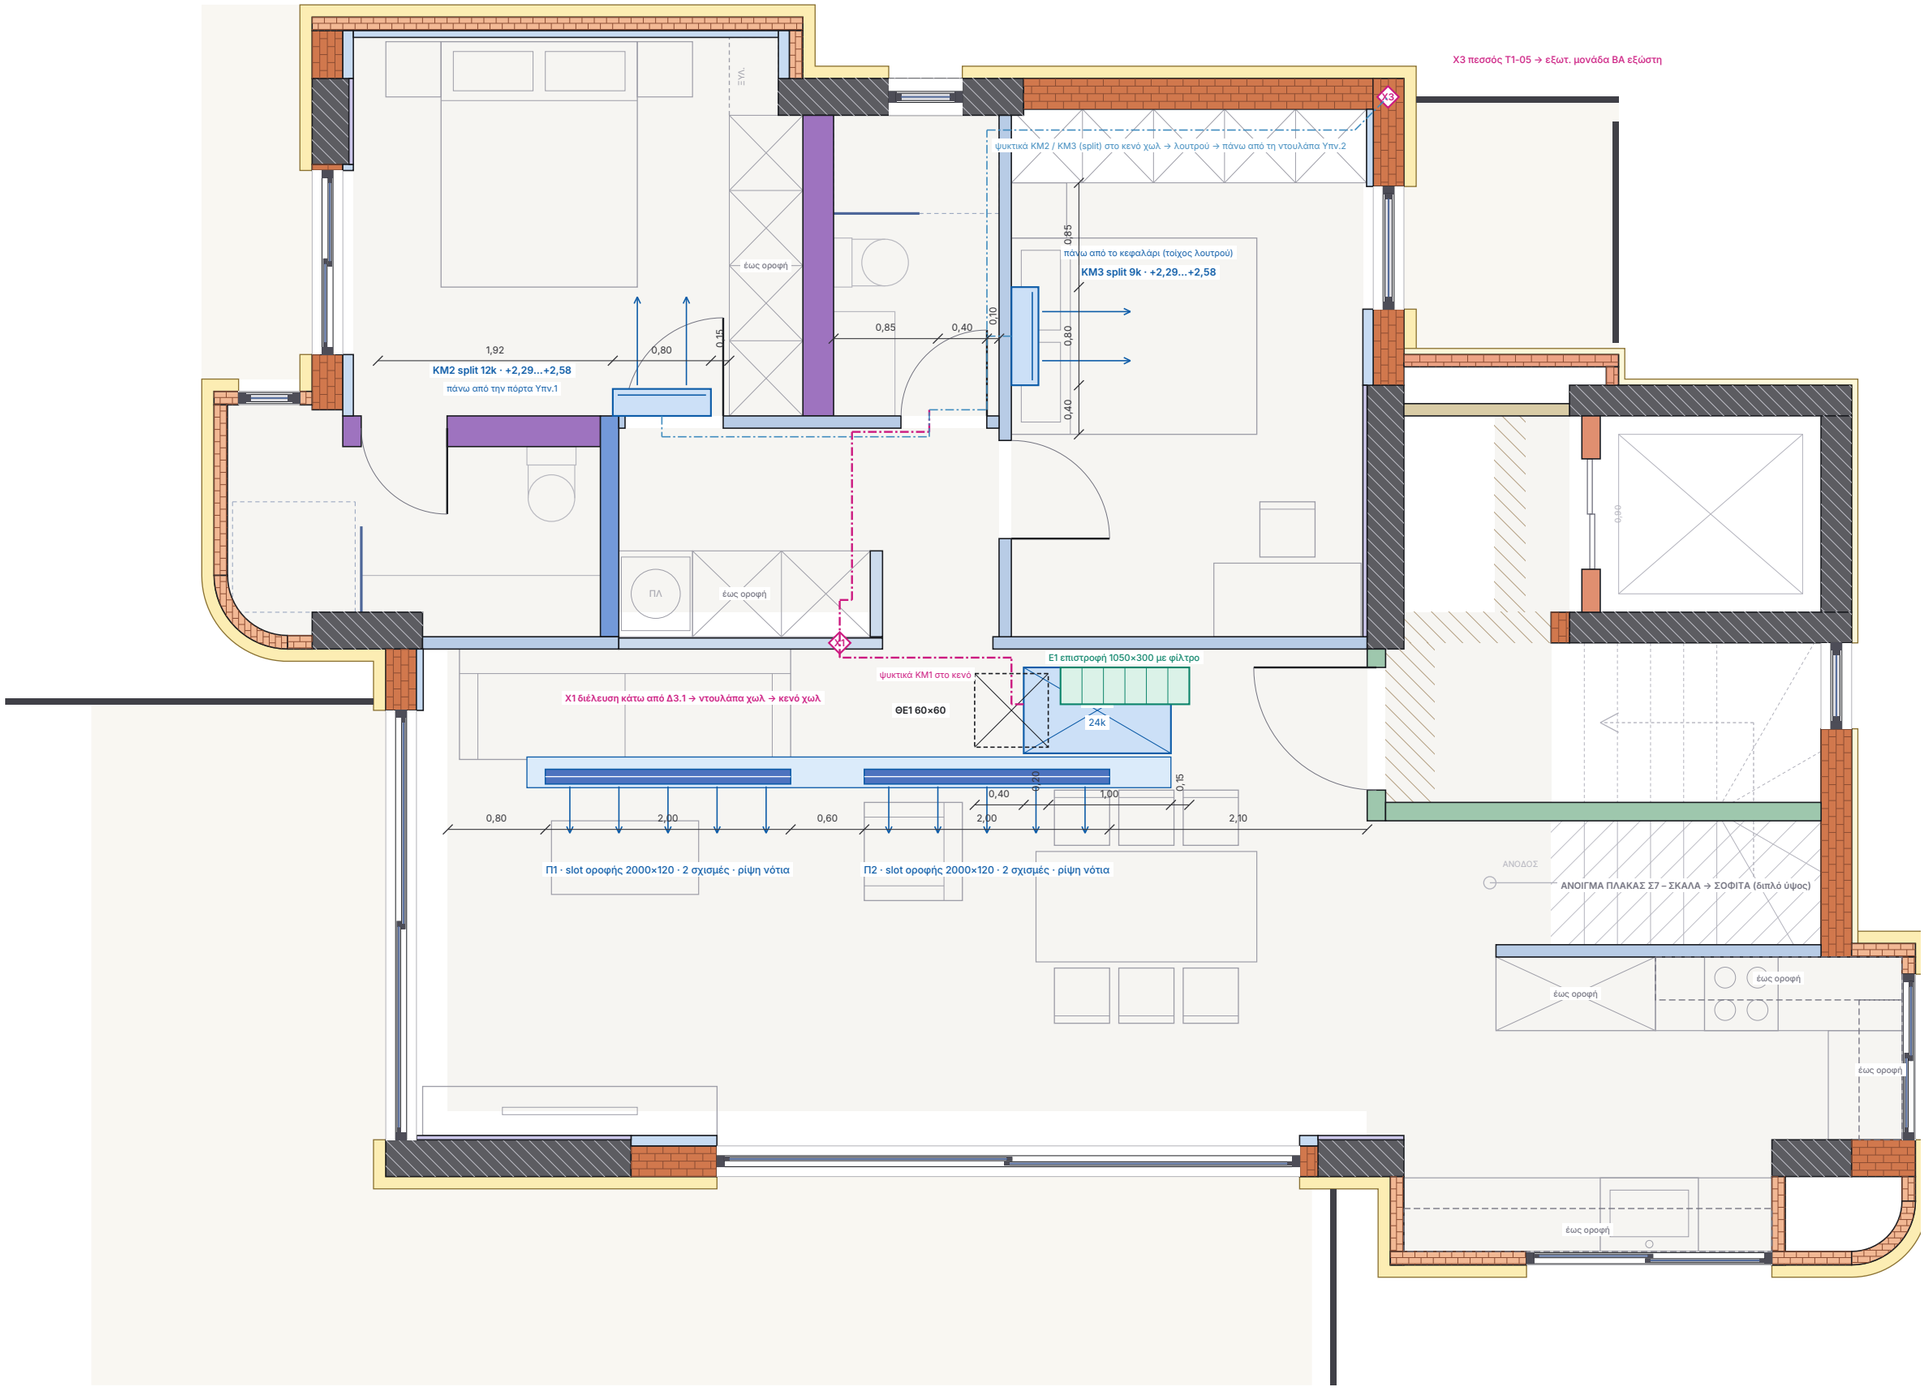

ΣΗΜΕΙΩΣΕΙΣ

Χώρος ΚΜ1 (προδ. 1): χαμήλωση +2,40 κάτω από Π8 +2,75 = 35 cm → 245 + 10 + 40 = 295 → περιθώριο 55 mm. Θυρίδα ΘΕ1 60×60 στο δυτικό άκρο (πλευρά συνδέσεων / ηλεκτρικού κουτιού – ιδιοκτήτης 09/11: «μόνο στο καναλάτο μία τετράγωνη»)· Ε1 επιστροφή με φίλτρο.

R14: θυρίδες ΜΟΝΟ στην καναλάτη – καμία θυρίδα στα λουτρά (ΘΕ4 / ΘΕ5 καταργήθηκαν). Χωλ +2,67: τα ψυκτικά ΚΜ1 / ΚΜ2 στο κενό 10 cm δίπλα-δίπλα.

R13 – ΥΠΝΟΔΩΜΑΤΙΑ ΜΕ SPLIT (ιδιοκτήτης 07/11: «στα δωμάτια δεν θα βάζουμε καναλάτο, θα βάζουμε split σε ένα σημείο που θα βρεις»). Κανόνας θέσης: ψηλά σε εσωτερικό τοίχο, ρίψη κατά μήκος του δωματίου που δεν πέφτει στο προσκέφαλο, ψυκτικά κατευθείαν στο κενό χωλ / λουτρού.

ΚΜ2 12k Υπν.1: ΠΑΝΩ ΑΠΟ ΤΗΝ ΠΟΡΤΑ (3,25–4,05 · +2,29…+2,58, 9 cm από την οροφή +2,67, 4 cm πάνω από την κάσα 2,25). Το κεφαλάρι είναι στο έρκερ (εξωτερικός τοίχος, LED3, Δ1.1 – χωρίς κενό για ψυκτικά) → ο αέρας ρίχνεται βόρεια δίπλα από την ανατολική πλευρά του κρεβατιού.

ΚΜ3 9k Υπν.2: ΠΑΝΩ ΑΠΟ ΤΟ ΚΕΦΑΛΑΡΙ στον τοίχο λουτρού Τ2-02 (2,20–3,00 · +2,29…+2,58), ρίψη ανατολικά προς τα πόδια και το W2.06.

Ψυκτικά split: από πίσω από τη μονάδα μέσα στον γυψότοιχο / υπέρθυρο ως το κενό χωλ (+2,45) / λουτρού → μαζί με την ΚΜ1 → πάνω από τη ντουλάπα Υπν.2 → πεσσός Τ1-05 → εξωτερική μονάδα ΒΑ εξώστη. Συμπυκνώματα με φυσική ροή μέσα στον γυψότοιχο στα σιφώνια των λουτρών (ΚΜ2 → Τ2Α-01 / λουτρό γονέων · ΚΜ3 → Τ2-02 / λουτρό) – χωρίς αντλία.

Ψυκτικά ΚΜ1 (R12, ιδιοκτήτης: «μέσω οροφής και ντουλάπας χωλ»): Χ1 κάτω από τη Δ3.1 μέσα από τον Τ2Ν-01 στη ντουλάπα χωλ (x ≈ 5,10) → κενό χωλ → λουτρό → Τ1-05. ΟΡΙΑΚΟ: καθαρό 37,5 mm → αερίου 5/8″ με μόνωση 9 mm χωράει, 13 mm όχι. Καμία οπή σε δοκό.


Στήριξη split σε γυψότοιχο: ενίσχυση (OSB 18 ή UA) πίσω από τη βάση της μονάδας / στο υπέρθυρο.

Εξωτερική μονάδα στον ΒΑ εξώστη του Δ΄ (όπως Β1)· συμπυκνώματα με αντλία → σιφώνι / υδρορροή εξώστη (επιβεβαίωση υδραυλικού).

ΥΠΟΜΝΗΜΑ

- ΚΜ1 καναλάτη μονάδα (slim ≤ 245 mm)
- ΚΜ2 / ΚΜ3 split τοίχου (σώμα στον τοίχο, βέλη = ρίψη)
- αεραγωγός / plenum προσαγωγής (μονωμένος, στο κενό)
- Π1 / Π2 γραμμικό slot οροφής 2 σχισμών, ρυθμιζόμενη ρίψη
- Ε στόμιο / κιβώτιο επιστροφής με φίλτρο
- ΘΕ θυρίδα επίσκεψης τετράγωνη – ΜΟΝΟ στην καναλάτη, στην πλευρά του ηλεκτρικού κουτιού (ιδιοκτήτης 09/11)
- Χ κατέβασμα / έξοδος σωληνώσεων – καμία οπή σε σκυρόδεμα

ΕΡΓΟ	ΘΕΜΑ ΣΧΕΔΙΟΥ	ΒΑΣΗ	ΑΡ. ΣΧΕΔΙΟΥ
ΠΕΝΤΑΟΡΟΦΟ ΚΤΗΡΙΟ ΚΑΤΟΙΚΙΩΝ – ΑΡΓΥΡΟΥΠΟΛΗ Κωνσταντινουπόλεως 12 & Αγ. Βαρβάρας · Ο.Τ. 103-15 Εργοδότης: INTERKAT Α.Ε. · Κατασκευή: ARKAD Ι.Κ.Ε.	**ΑΝΟΨΗ – ΚΛΙΜΑΤΙΣΜΟΣ · ΘΥΡΙΔΕΣ** Καναλάτη ΚΜ1 · split υπνοδωματίων · slot · μία θυρίδα 60×60 · ψυκτικά Δ΄ ΟΡΟΦΟΣ – Δ1 κάτω επίπεδο (μεζονέτα)	Βάση: τοιχοποιίες Δ΄ R04 · ξυλότυπος Σ7_ΕΦ (+16,05) · ανόψη Β1 R16	**ΑΝ-10** **Κλίμακα 1:50 · Α3** 09/11/2026 · R05

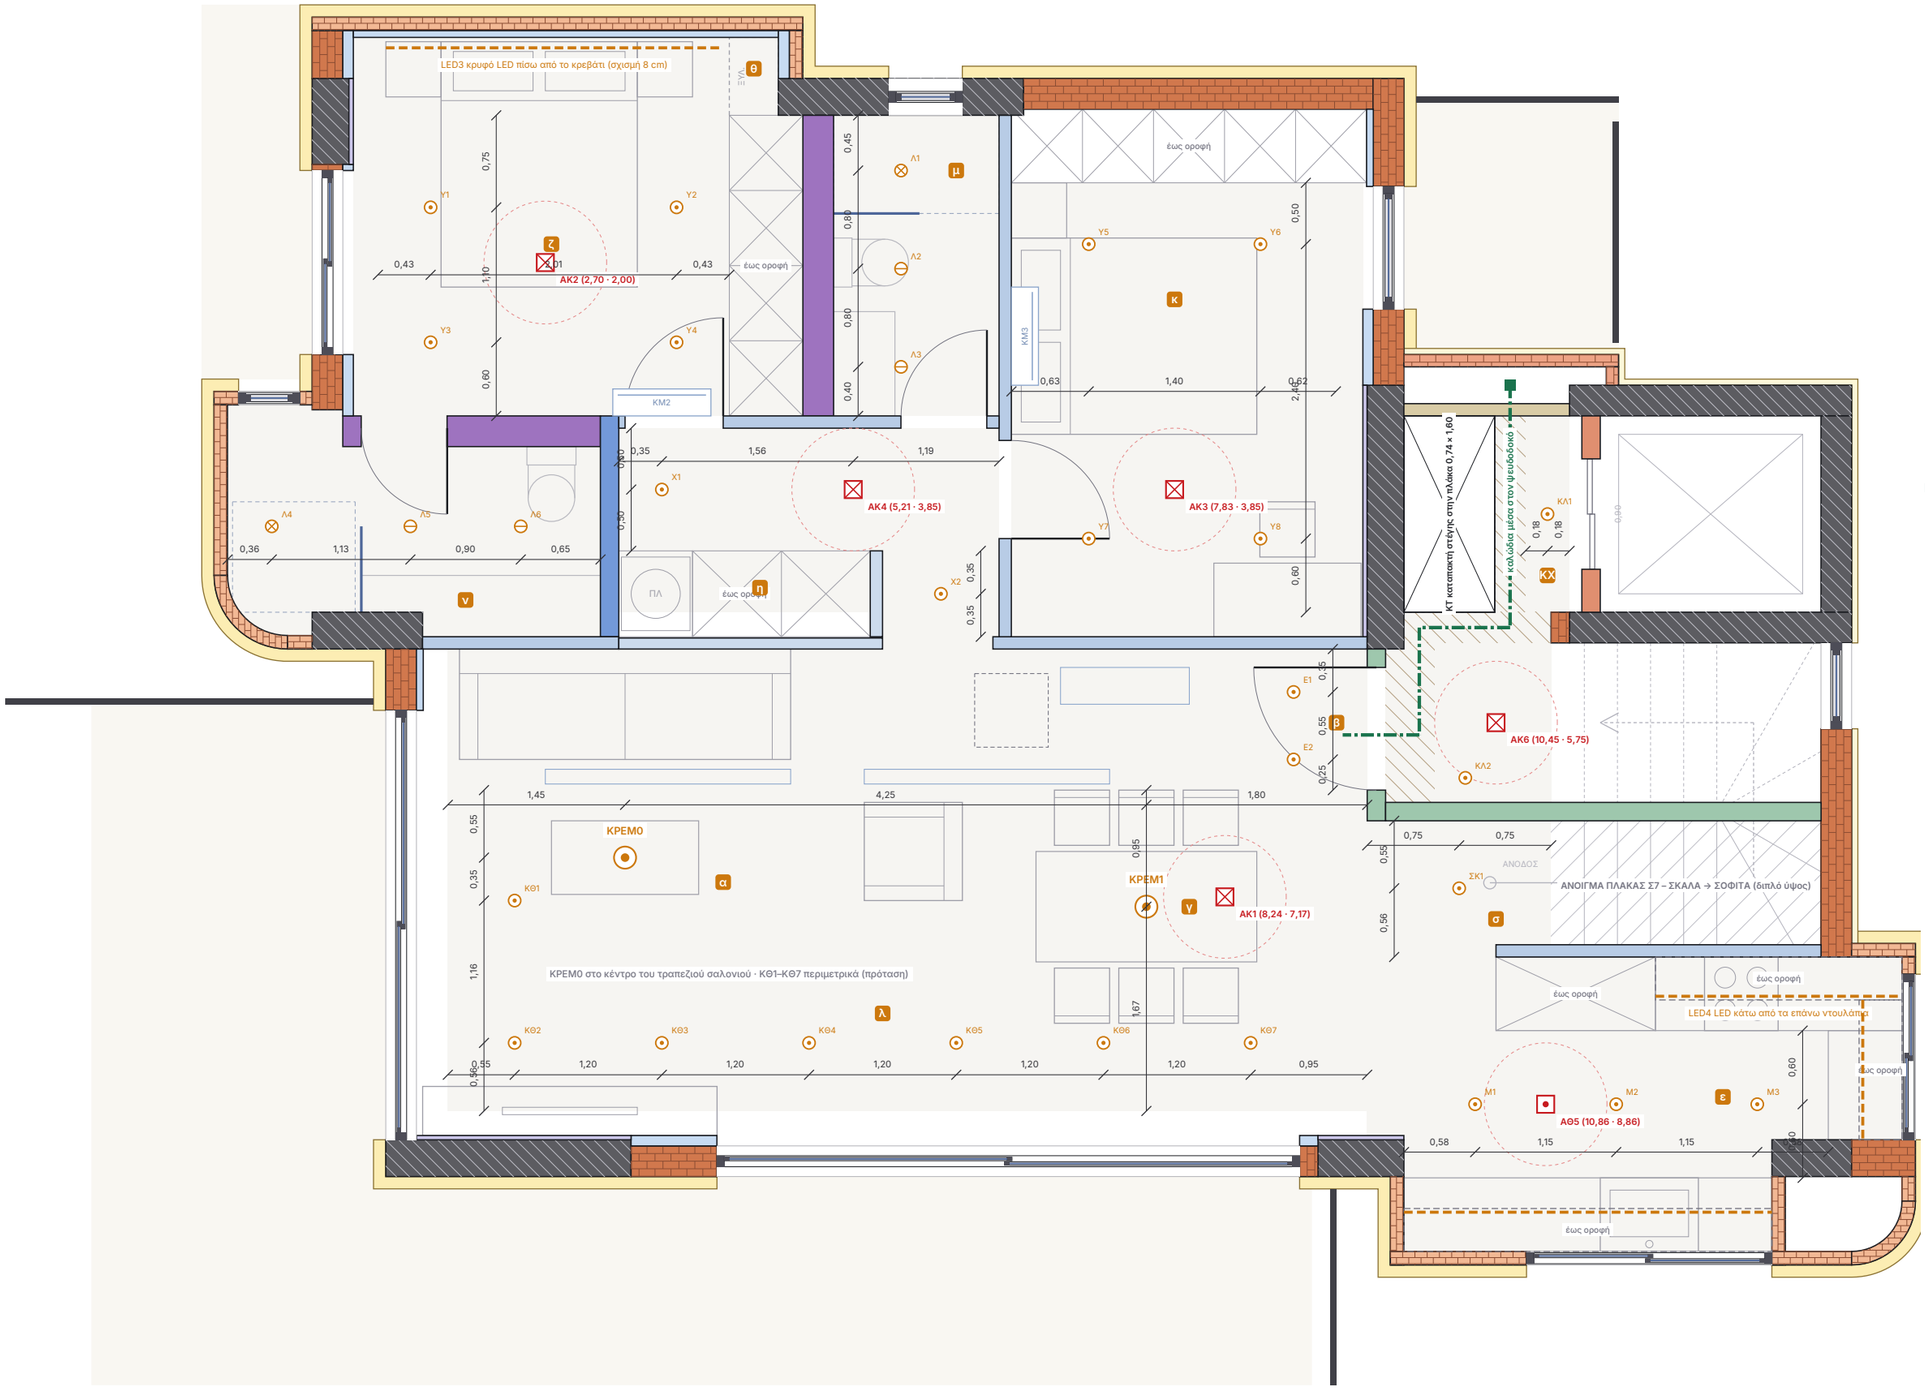

ΣΗΜΕΙΩΣΕΙΣ

Κατανομή όπως Β1 R13: Υπν. 2 × 2 spots · λουτρά 3 (IP65 στο ντους) · κουζίνα 3 γενικός + LED4 κάτω από τα ντουλάπια · χωλ / είσοδος · καθιστικό ΚΘ1–ΚΘ7 περιμετρικά + ΚΡΕΜ0 στο κέντρο του τραπεζιού σαλονιού · + ΣΚ1 στο ξεκίνημα της σκάλας. Σύνολο 29 spots + 2 κρεμαστά + LED3 + LED4.

Σκάλα προς σοφίτα: φωτιστικά τοίχου / σκαλοπατιών (ηλεκτρολογικά) – ανιχνευτής καπνού στο πλατύσκαλο της σοφίτας (ανόψη σοφίτας).

Πυρανίχνευση (προδ. 4): σε κάθε κύριο χώρο και στο χωλ· ≥ 0,50 από τοίχους / δοκούς / φωτιστικά, ≥ 1,00 από στόμια προσαγωγής / split· λουτρά χωρίς ανιχνευτή καπνού.

Οπή spot Ø 75–80 ανάμεσα στα προφίλ CD (όχι πάνω τους)· όπου πέφτει σε προφίλ, μετατόπιση του προφίλ – όχι του spot.

R04 – ΚΑΛΩΔΙΑ ΑΠΟ ΤΟ SHAFT μέσα στον ψευδοδοκό +2,40: έξοδος στο Τ8-01 (x 10,44–10,69) κάτω από τη Δ2.1 25/50 → ανατολικά και νότια της καταπακτής → γραμμή Δ9.1 → πάνω από την πόρτα εισόδου → χαμήλωση ΚΜ1. Καθαρό 37,5 mm και στις δύο δοκούς → σωλήνες ≤ Ø 32 σε μία στρώση, πυροφραγή στον Τ6Α.

ΥΠΟΜΝΗΜΑ

- χωνευτό spot LED 7–9 W, 2700 K, CRI ≥ 90, UGR < 19, σώμα ≤ 75 mm
- χωνευτό spot IP44 (λουτρά)
- χωνευτό spot IP65 (πάνω από ντους)
- split τοίχου (για συντονισμό – βλ. φύλλο κλιματισμού)
- ΚΡΕΜ παροχή οροφής (κουτί + ενίσχυση ανάρτησης)
- καλώδια από το shaft Η/Μ (■ έξοδος πάνω από το μέτωπο-ντουλάπα Τ8-01) → ψευδοροφή κλιμακοστασίου → διαμέρισμα
- καταπακτή πρόσβασης στη στέγη στο επίπεδο της ψευδοροφής (αρχιτέκτονας)
- ΑΚ ανιχνευτής καπνού (ΕΠ104 · EN 54-7)
- ΑΘ θερμοδιαφορικός ανιχνευτής (κουζίνα · EN 54-5)
- ακτίνα 0,50 m γύρω από ανιχνευτή – κανένας τοίχος / φωτιστικό μέσα
- LED κρυφό γραμμικό 3000 K – LED3 κεφαλάρι · LED4 κάτω από τα ντουλάπια κουζίνας

ΕΡΓΟ

ΠΕΝΤΑΟΡΟΦΟ ΚΤΗΡΙΟ ΚΑΤΟΙΚΙΩΝ – ΑΡΓΥΡΟΥΠΟΛΗ
Κωνσταντινουπόλεως 12 & Αγ. Βαρβάρας · Ο.Τ. 103-15
Εργοδότης: INTERKAT Α.Ε. · Κατασκευή: ARKAD Ι.Κ.Ε.

ΘΕΜΑ ΣΧΕΔΙΟΥ

ΑΝΟΨΗ – ΦΩΤΙΣΜΟΣ · ΠΥΡΑΝΙΧΝΕΥΣΗ
Χωνευτά spots · παροχές · κρυφό LED · ανιχνευτές
Δ΄ ΟΡΟΦΟΣ – Δ1 κάτω επίπεδο (μεζονέτα)

ΒΑΣΗ

Βάση: τοιχοποιίες Δ΄ R04 · ξυλότυπος Σ7_ΕΦ (+16,05) · ανόψη Β1 R16

ΑΡ. ΣΧΕΔΙΟΥ

ΑΝ-11
Κλίμακα 1:50 · Α3
09/11/2026 · R05

ΣΥΜΜΟΡΦΩΣΗ ΜΕ ΤΙΣ ΠΡΟΔΙΑΓΡΑΦΕΣ (ιδιοκτήτης 07/11/2026)

1 Κλιματισμός Όπως Β1 R14: καναλάτη ΚΜ1 24k καθιστικό / κουζίνα (ΕΓΚΕΚΡ.) με slot Π1/Π2 · split τοίχου ΚΜ2 / ΚΜ3 στα υπνοδωμάτια (ΕΓΚΕΚΡ.) · χώρος 35 cm · μία θυρίδα ΘΕ1 60×60 · ψυκτικά ΚΜ1 κάτω από τη Δ3.1 (οριακό 3,6 mm).

2 Κουρτίνες ΚΡ1–ΚΡ4 σε όλα τα ανοίγματα καθιστικού / υπνοδωματίων (W4.01, W4.02, W4.08, W4.06), 20 (22) × 10 cm, ανοιχτές ως την πλάκα.

3 Φωτισμός 29 χωνευτά spots (Β1 R13 + ΣΚ1 σκάλας) + ΚΡΕΜ0 / ΚΡΕΜ1 + LED3 / LED4 · κανένα spot κάτω από μονάδα / αεραγωγό / σε θυρίδα / πάνω από ντουλάπι · κενό ≥ 88 mm.

4 Πυρανίχνευση ΑΚ1–ΑΚ4 καπνού + ΑΘ5 θερμοδιαφορικός κουζίνας · σκάλα: ανιχνευτής στο πλατύσκαλο σοφίτας.

5 Κατασκευή Όπως Β1 · το ξεκίνημα της σκάλας ενιαίο με την κουζίνα +2,45 (περασιά Δ9.1) · ακμή στο άνοιγμα της πλάκας με γωνιόκρανο.

6 Γενική αρχή 5 στάθμες, κάθε αλλαγή πάνω σε γραμμή δοκού ή σε πόρτα – όπως Β1· υπνοδωμάτια και χωλ ενιαία +2,67.

ΕΓΚΕΚΡΙΜΕΝΑ / ΑΠΟΦΑΣΕΙΣ ΙΔΙΟΚΤΗΤΗ (07 – 09/11/2026)

· Πόρτες δωματίων 2,20 παντού · θυρίδες μόνο στην καναλάτη, μία τετράγωνη στην πλευρά των ηλεκτρικών · χωλ όχι στο 2,45 (R14, 09/11).

· Ψευδοροφή στο κλιμακοστάσιο για τα καλώδια από το shaft στο διαμέρισμα (R15, 09/11).

· Υπνοδωμάτια με split τοίχου αντί καναλάτου (R13: «στα δωμάτια δεν θα βάζουμε καναλάτο, θα βάζουμε split»).

· Κουζίνα χωρίς δική της καναλάτη – καλύπτεται από την ΚΜ1 24k.

· Μονάδα ΚΜ1 slim ≤ 245 mm ως παραδοχή μέχρι την επιλογή μοντέλου.

· Η απόφαση R02 «καθιστικό χωρίς spots» αναθεωρείται (R13: «σκέψου μήπως βάλουμε και spot») – τα ΚΘ1–ΚΘ7 είναι πρόταση (Α6).

ΑΛΛΑΓΕΣ R03 → R05 – ΚΛΙΜΑΚΟΣΤΑΣΙΟ · ΔΙΑΦΟΡΕΣ ΑΠΟ ΤΟ Β1 R16 (09/11/2026)

· R05 = Β1 R16 (ιδιοκτήτης 09/11: οροφή κλιμακοστασίου «καμιά δεκαριά πόντους για να μπει φωτισμός» + «ένα δοκάρι από το οποίο θα μπαίνουν τα καλώδια»): lobby + κοινόχρηστο πλατύσκαλο +2,70 = 10 cm κάτω από την πλάκα h15 · ψευδοδοκός καλωδίων +2,40.

· Διαφορά από το Β1: στο lobby του Δ΄ είναι το άνοιγμα της καταπακτής στέγης (Σ7 9,70–10,44 × 3,25–4,85, Α-10-4F) – μένει στην πλάκα όπως ο αρχιτέκτονας και ο ψευδοδοκός το πλαισιώνει ανατολικά και νότια, μετά συνεχίζει στη γραμμή Δ9.1 στο πλατύσκαλο. Καλώδια κάτω από τη Δ2.1 25/50 και τη Δ9.1 με 37,5 mm (σωλήνες ≤ Ø 32 σε μία στρώση).

ΠΡΟΗΓΟΥΜΕΝΗ ΑΝΑΘΕΩΡΗΣΗ

· R04: οροφή κλιμακοστασίου ενιαία +2,40, καταπακτή στην ψευδοροφή – ιδιοκτήτης: «δε θέλω τόσο κατέβασμα».

· R03 = Β1 R14 (χωλ +2,67 · ΘΕ1 · πόρτες 2,20) · R02 = Β1 R13 · R01 = Β1 R12 + ξεκίνημα σκάλας.

ΑΝΟΙΚΤΑ ΣΗΜΕΙΑ

· Α1 [ΚΑΤΑΣΚΕΥΗ] Διέλευση ψυκτικών ΚΜ1 κάτω από τη Δ3.1 όπως Β1: καθαρό 37,5 mm → αερίου 5/8″ με μόνωση 9 mm χωράει, με 13 mm όχι (τότε χαμήλωση +2,38).

· Α2 [ΜΟΝΤΕΛΟ] ΚΜ1 ≤ 245 mm · ΘΕ1 60×60 στην πλευρά του ηλεκτρικού κουτιού (καθρεφτίζεται αν το μοντέλο το έχει ανατολικά) · split ΚΜ2 / ΚΜ3 ≤ 290 × 800 mm – όπως Β1.

· Α7 [ΑΠΟΦΑΣΗ] Όπως Β1 Α6: spots καθιστικού ΚΘ1–ΚΘ7 = πρόταση (κύκλωμα λ – αφαιρούνται χωρίς άλλη αλλαγή).

· Α8 [ΚΑΤΑΣΚΕΥΗ] Καταπακτή στέγης στο lobby (Α-10-4F, άνοιγμα Σ7 0,74 × 1,60) στην πλάκα όπως ο αρχιτέκτονας· η οροφή +2,70 και ο ψευδοδοκός +2,40 την πλαισιώνουν (επένδυση των παρειών ως την πλάκα).

· Α9 [ΗΛΕΚΤΡΟΛΟΓΙΚΑ] Καλώδια shaft → διαμέρισμα: Δ2.1 25/50 και Δ9.1 με καθαρό 37,5 mm → σωλήνες ≤ Ø 32 σε μία στρώση· πυροφραγή στον Τ6Α.

· Α3 [ΣΤΑΤΙΚΟΣ] Δοκός / ακμή πλάκας Σ7 στο x 10,90–11,15 (κάτω από το Δ τοιχείο του κλιμακοστασίου της σοφίτας): η ψευδοροφή +2,45 του ξεκινήματος της σκάλας τελειώνει εκεί – η κάτω παρειά της δοκού πρέπει να είναι ≥ +2,45 (διατομή ≤ 50 cm).

· Α4 [ΣΤΑΤΙΚΟΣ] Δοκοί Σ7_ΕΦ στη ζώνη του διαμερίσματος: θεωρήθηκαν ίδιοι με τον Σ5 (ο έλεγχος της 07/11 έγινε μόνο στη ζώνη της σκάλας) – επιβεβαίωση πριν τη σκυροδέτηση του Σ7· και μέτρηση μετά το ξεκαλούπωμα.

· Α5 [ΑΠΟΦΑΣΗ] Λουτρό / WC σοφίτας πάνω από το Υπν.2 (και τη ντουλάπα του): η ανόψη κρατά το Υπν.2 +2,67 (κενό 10 cm) θεωρώντας ότι τα οριζόντια της αποχέτευσης μπαίνουν στην επίστρωση της σοφίτας (15 cm) και οι στήλες κατεβαίνουν μέσα στη ντουλάπα Υπν.2 (έως οροφή). Αν ο υδραυλικός τις φέρει από κάτω → χαμήλωση Υπν.2 στο +2,45 (κενό 32 cm, περασιά Δ3.1) – να αποφασιστεί στις αποχετεύσεις.

· Α6 [ΣΥΝΤΟΝΙΣΜΟΣ] Δώμα πάνω από καθιστικό / κουζίνα / Υπν.1: οι υδρορροές του δώματος κατεβαίνουν κατακόρυφα στις όψεις / εξώστες – καμία οριζόντια όδευση στο κενό 10 cm του καθιστικού. Κουτιά οροφής και σωληνώσεις ανιχνευτών μέσα στην ψευδοροφή (όχι στη μόνωση δώματος).


ΕΛΕΓΧΟΣ ΣΥΓΚΡΟΥΣΕΩΝ & ΣΤΑΘΜΩΝ – 92 έλεγχοι · ΟΚ 85 · ΟΡΙΑΚΟ 3 · ΕΓΚΕΚΡ. 4 · ΑΠΟΚΛΙΣΗ 0

Αυτόματος έλεγχος από το μοντέλο (code/anopseis/checks.py): στάθμες ↔ δοκοί · κενό μονάδων · θυρίδες · spots ↔ ζώνες / θυρίδες / μονάδες / αεραγωγοί / κουρτινόθηκες · ανιχνευτές ↔ τοίχοι / φωτιστικά / στόμια · κουρτινόθηκες ↔ κουφώματα / δοκοί.

ΚΩΔ.	ΚΑΤΑΣΤ.	ΣΤΟΙΧΕΙΟ	ΜΕΤΡΗΣΗ
ΣΤ01	ΟΚ	Z2 ΧΑΜΗΛΩΣΗ ΚΑΝΑΛΑΤΟΥ / ΕΙΣΟΔΟΣ ↔ Δ3.1 30/50 (Κ.Π. +2.4…	οροφή +2.40 · κρυμμένη 5 cm
ΣΤ02	ΟΚ	Z3 ΚΟΥΖΙΝΑ – ΞΕΚΙΝΗΜΑ ΣΚΑΛΑΣ ↔ Δ9.1 30/50 (Κ.Π. +2.45)	οροφή +2.45 · περασιά
ΣΤ03	ΟΚ	Z3 ΚΟΥΖΙΝΑ – ΞΕΚΙΝΗΜΑ ΣΚΑΛΑΣ ↔ Δ4.6 30/40 (Κ.Π. +2.55)	οροφή +2.45 · κρυμμένη 10 cm
ΣΤ04	ΟΚ	Z3 ΚΟΥΖΙΝΑ – ΞΕΚΙΝΗΜΑ ΣΚΑΛΑΣ ↔ Δ12.2 25/40 (Κ.Π. +2.55)	οροφή +2.45 · κρυμμένη 10 cm
ΣΤ05	ΟΚ	Z3 ΚΟΥΖΙΝΑ – ΞΕΚΙΝΗΜΑ ΣΚΑΛΑΣ ↔ Δ10.1 25/40 (Κ.Π. +2.55)	οροφή +2.45 · κρυμμένη 10 cm
ΣΤ06	ΟΚ	Z6 ΛΟΥΤΡΟ ΓΟΝΕΩΝ ↔ Δ6.1 30/55 (Κ.Π. +2.40)	οροφή +2.40 · περασιά
ΣΤ07	ΟΚ	Z6 ΛΟΥΤΡΟ ΓΟΝΕΩΝ ↔ Δ3.1 30/50 (Κ.Π. +2.45)	οροφή +2.40 · κρυμμένη 5 cm
ΣΤ08	ΟΚ	Z8 ΚΕΦΑΛΑΡΙ ΥΠΝ.1 (έρκερ) ↔ Δ1.1 30/40 (Κ.Π. +2.55)	οροφή +2.55 · περασιά
ΣΤ09	ΟΚ	Z11 ΣΑΝΙΔΑ ΚΑΤΩ ΑΠΟ Δ3.1 (Υπν.2) ↔ Δ3.1 30/50 (Κ.Π. +2.45)	οροφή +2.45 · περασιά
ΣΤ10	ΟΚ	Z13 ΨΕΥΔΟΔΟΚΟΣ ΚΑΛΩΔΙΩΝ (κλιμακοστάσιο) ↔ Δ9.1 30/50 (Κ…	οροφή +2.40 · κρυμμένη 5 cm
ΚΛ-ΚΜ1	ΟΚ	ΚΜ1 24.000 Btu/h – καθιστικό – τραπεζαρία – κουζίνα	κενό 350 mm · περιθώριο +55 mm
ΘΕ-ΚΜ1	ΟΚ	ΚΜ1 – πρόσβαση συντήρησης	ΘΕ1
ΚΛ-ΚΜ2	ΟΚ	ΚΜ2 split τοίχου 12.000 Btu/h – Υπνοδωμάτιο 1 (πάνω από την πό…	οροφή +2,67 · μονάδα +2,29…+2,58 · πάν…
ΚΡ-ΚΜ2	ΟΚ	ΚΜ2 – ρίψη βόρεια κατά μήκος της ανατολικής πλευράς του κρε…	το κεφαλάρι είναι στο έρκερ (εξωτ. τοίχος …
ΨΣ-ΚΜ2	ΟΚ	ΚΜ2 – ψυκτικά / συμπυκνώματα	ψυκτικά από πίσω μέσα στο υπέρθυρο στο κ…
ΚΛ-ΚΜ3	ΟΚ	ΚΜ3 split τοίχου 9.000 Btu/h – Υπνοδωμάτιο 2 (πάνω από το κεφ…	οροφή +2,67 · μονάδα +2,29…+2,58 · πάνω…
ΚΡ-ΚΜ3	ΟΚ	ΚΜ3 – ρίψη ανατολικά κατά μήκος του κρεβατιού	πάνω από το κεφαλάρι – ο αέρας πέφτει π…
ΨΣ-ΚΜ3	ΟΚ	ΚΜ3 – ψυκτικά / συμπυκνώματα	ψυκτικά από πίσω στο κενό λουτρού → πάν…
ΚΑΛ-ΟΔ	ΟΚ	Όδευση καλωδίων shaft → οροφή κλιμακοστασίου → είσοδος δια…	ελάχιστο 310 mm
ΨΥ-ΚΜ1	ΟΚ	Όδευση ψυκτικών ΚΜ1 χαμήλωση → ντουλάπα χωλ → κενό χωλ…	ελάχιστο 60 mm
ΨΥ-ΚΜ2	ΟΚ	Όδευση ψυκτικών split ΚΜ2 / ΚΜ3 κενό χωλ → λουτρό → Τ1-05	ελάχιστο 60 mm
ΨΥ-ΔΟΚ	ΟΡΙΑΚΟ	Διέλευση ψυκτικών ΚΜ1 κάτω από τη Δ3.1 (x ≈ 5.10, T2N-01 → ντο…	καθαρό 37.5 mm · περιθώριο +3.6 mm
ΚΑΛ-Δ2.1	ΟΡΙΑΚΟ	Διέλευση καλωδίων shaft κάτω από τη Δ2.1 (ψευδοδοκός x 10,44–…	καθαρό 37.5 mm · περιθώριο +5.5 mm
ΚΑΛ-Δ9.1	ΟΡΙΑΚΟ	Διέλευση καλωδίων shaft κάτω από τη Δ9.1 (ψευδοδοκός y ≈ 5,8…	καθαρό 37.5 mm · περιθώριο +5.5 mm
ΚΔ-ΚΜ1	ΟΚ	Καθιστικό – τραπεζαρία	ΚΜ1 καναλάτη
ΚΔ-ΚΜ2	ΕΓΚΕΚΡ.	Υπνοδωμάτιο 1	ΚΜ2 split τοίχου (ιδιοκτήτης 07/11: «στα δ…
ΚΔ-ΚΜ3	ΕΓΚΕΚΡ.	Υπνοδωμάτιο 2	ΚΜ3 split τοίχου (ιδιοκτήτης 07/11: «στα δ…
ΚΔ-ΚΟΥΖ	ΕΓΚΕΚΡ.	Κουζίνα	από την ΚΜ1 (ανοιχτή στο καθιστικό)
ΣΤ-Π1	ΟΚ	Π1 slot οροφής 2000×120 · 2 σχισμές	μέσα
ΣΤ-Π2	ΟΚ	Π2 slot οροφής 2000×120 · 2 σχισμές	μέσα
SP-Y1	ΟΚ	Y1 spot (1.765 · 1.550) – ΥΠΝΟΔΩΜΑΤΙΟ 1	κενό 88 mm · άκρη 0.63
SP-Y2	ΟΚ	Y2 spot (3.770 · 1.550) – ΥΠΝΟΔΩΜΑΤΙΟ 1	κενό 88 mm · άκρη 0.75
SP-Y3	ΟΚ	Y3 spot (1.765 · 2.650) – ΥΠΝΟΔΩΜΑΤΙΟ 1	κενό 88 mm · άκρη 0.60
SP-Y4	ΟΚ	Y4 spot (3.770 · 2.650) – ΥΠΝΟΔΩΜΑΤΙΟ 1	κενό 88 mm · άκρη 0.60
SP-Y5	ΟΚ	Y5 spot (7.130 · 1.850) – ΥΠΝΟΔΩΜΑΤΙΟ 2	κενό 88 mm · άκρη 0.50
SP-Y6	ΟΚ	Y6 spot (8.530 · 1.850) – ΥΠΝΟΔΩΜΑΤΙΟ 2	κενό 88 mm · άκρη 0.50
SP-Y7	ΟΚ	Y7 spot (7.130 · 4.250) – ΥΠΝΟΔΩΜΑΤΙΟ 2	κενό 88 mm · άκρη 0.60
SP-Y8	ΟΚ	Y8 spot (8.530 · 4.250) – ΥΠΝΟΔΩΜΑΤΙΟ 2	κενό 88 mm · άκρη 0.60
SP-Λ1	ΟΚ	Λ1 spot IP65 (5.600 · 1.250) – ΛΟΥΤΡΟ	κενό 307 mm · άκρη 0.45
SP-Λ2	ΟΚ	Λ2 spot IP44 (5.600 · 2.050) – ΛΟΥΤΡΟ	κενό 307 mm · άκρη 0.55
SP-Λ3	ΟΚ	Λ3 spot IP44 (5.600 · 2.850) – ΛΟΥΤΡΟ	κενό 307 mm · άκρη 0.40
SP-Λ4	ΟΚ	Λ4 spot IP65 (0.470 · 4.150) – ΛΟΥΤΡΟ ΓΟΝΕΩΝ	κενό 358 mm · άκρη 0.36
SP-Λ5	ΟΚ	Λ5 spot IP44 (1.600 · 4.150) – ΛΟΥΤΡΟ ΓΟΝΕΩΝ	κενό 358 mm · άκρη 0.70
SP-Λ6	ΟΚ	Λ6 spot IP44 (2.500 · 4.150) – ΛΟΥΤΡΟ ΓΟΝΕΩΝ	κενό 358 mm · άκρη 0.65
SP-X1	ΟΚ	X1 spot (3.650 · 3.850) – ΧΩΛ	κενό 88 mm · άκρη 0.35
SP-X2	ΟΚ	X2 spot (5.925 · 4.700) – ΧΩΛ	κενό 88 mm · άκρη 0.15

ΚΩΔ.	ΚΑΤΑΣΤ.	ΣΤΟΙΧΕΙΟ	ΜΕΤΡΗΣΗ
SP-E1	ΟΚ	E1 spot (8.800 · 5.500) – ΧΑΜΗΛΩΣΗ ΚΑΝΑΛΑΤΟΥ / ΕΙΣΟΔΟΣ	κενό 338 mm · άκρη 0.35
SP-E2	ΟΚ	E2 spot (8.800 · 6.050) – ΧΑΜΗΛΩΣΗ ΚΑΝΑΛΑΤΟΥ / ΕΙΣΟΔΟΣ	κενό 338 mm · άκρη 0.25
SP-M1	ΟΚ	M1 spot (10.280 · 8.860) – ΚΟΥΖΙΝΑ – ΞΕΚΙΝΗΜΑ ΣΚΑΛΑΣ	κενό 337 mm · άκρη 0.63
SP-M2	ΟΚ	M2 spot (11.430 · 8.860) – ΚΟΥΖΙΝΑ – ΞΕΚΙΝΗΜΑ ΣΚΑΛΑΣ	κενό 337 mm · άκρη 1.20
SP-M3	ΟΚ	M3 spot (12.580 · 8.860) – ΚΟΥΖΙΝΑ – ΞΕΚΙΝΗΜΑ ΣΚΑΛΑΣ	κενό 337 mm · άκρη 0.31
SP-ΚΘ1	ΟΚ	ΚΘ1 spot (2.450 · 7.200) – ΚΑΘΙΣΤΙΚΟ – ΤΡΑΠΕΖΑΡΙΑ	κενό 88 mm · άκρη 0.55
SP-ΚΘ2	ΟΚ	ΚΘ2 spot (2.450 · 8.360) – ΚΑΘΙΣΤΙΚΟ – ΤΡΑΠΕΖΑΡΙΑ	κενό 88 mm · άκρη 0.55
SP-ΚΘ3	ΟΚ	ΚΘ3 spot (3.650 · 8.360) – ΚΑΘΙΣΤΙΚΟ – ΤΡΑΠΕΖΑΡΙΑ	κενό 88 mm · άκρη 0.55
SP-ΚΘ4	ΟΚ	ΚΘ4 spot (4.850 · 8.360) – ΚΑΘΙΣΤΙΚΟ – ΤΡΑΠΕΖΑΡΙΑ	κενό 88 mm · άκρη 0.55
SP-ΚΘ5	ΟΚ	ΚΘ5 spot (6.050 · 8.360) – ΚΑΘΙΣΤΙΚΟ – ΤΡΑΠΕΖΑΡΙΑ	κενό 88 mm · άκρη 0.55
SP-ΚΘ6	ΟΚ	ΚΘ6 spot (7.250 · 8.360) – ΚΑΘΙΣΤΙΚΟ – ΤΡΑΠΕΖΑΡΙΑ	κενό 88 mm · άκρη 0.55
SP-ΚΘ7	ΟΚ	ΚΘ7 spot (8.450 · 8.360) – ΚΑΘΙΣΤΙΚΟ – ΤΡΑΠΕΖΑΡΙΑ	κενό 88 mm · άκρη 0.55
SP-ΚΛ1	ΟΚ	ΚΛ1 spot (10.870 · 4.050) – ΚΛΙΜΑΚΟΣΤΑΣΙΟ – LOBBY (κοινόχρη…	κενό 87 mm · άκρη 0.18
SP-ΚΛ2	ΟΚ	ΚΛ2 spot (10.200 · 6.200) – ΚΛΙΜΑΚΟΣΤΑΣΙΟ – LOBBY (κοινόχρη…	κενό 87 mm · άκρη 0.20
SP-ΣΚ1	ΟΚ	ΣΚ1 spot (10.150 · 7.100) – ΚΟΥΖΙΝΑ – ΞΕΚΙΝΗΜΑ ΣΚΑΛΑΣ	κενό 337 mm · άκρη 0.55
SP-ΚΑΘ	ΟΚ	Καθιστικό – τραπεζαρία	ΚΘ1–ΚΘ7 περιμετρικά (κύκλωμα λ, dimmer)…
ΚΜΣ-ΚΡΕΜ0	ΟΚ	ΚΡΕΜ0 κρεμαστό – τραπέζι σαλονιού	κέντρο (3.35 · 6.85) · Π1 0.60
ΚΜΣ-ΚΡΕΜ1	ΟΚ	ΚΡΕΜ1 κρεμαστό – τραπεζαρία	κέντρο (7.60 · 7.25) · Π2 1.04
ΠΥ-ΑΚ1	ΟΚ	ΑΚ1 καπνού (8.24 · 7.17) – καθιστικό – τραπεζαρία (R05: 0,55 από…	τοίχος 0.87 · ΚΡΕΜ1 0.64 · Π2 1.32
ΠΥ-ΑΚ2	ΟΚ	ΑΚ2 καπνού (2.70 · 2.00) – Υπνοδωμάτιο 1 (R13: ≥ 1,00 από το spli…	τοίχος 1.20 · Υ1 1.04 · ΚΜ2 1.17
ΠΥ-ΑΚ3	ΟΚ	ΑΚ3 καπνού (7.83 · 3.85) – Υπνοδωμάτιο 2 (R13: εκτός ρίψης ΚΜ…	τοίχος 1.00 · Υ8 0.81 · ΚΜ3 1.40
ΠΥ-ΑΚ4	ΟΚ	ΑΚ4 καπνού (5.21 · 3.85) – χωλ – άξονας διαδρόμου 1,00	τοίχος 0.50 · Λ3 1.07 · ΚΜ2 1.31
ΠΥ-ΑΘ5	ΟΚ	ΑΘ5 θερμοδιαφορικός (10.86 · 8.86) – κουζίνα – θερμοδιαφορικό…	τοίχος 0.60 · Μ2 0.57 · Π2 4.41
ΠΥ-ΑΚ6	ΟΚ	ΑΚ6 καπνού (10.45 · 5.75) – κλιμακοστάσιο – πλατύσκαλο (κοινό…	τοίχος 0.50 · ΚΛ2 0.51 · Π2 3.17
ΠΥ-ΧΩΡ	ΟΚ	Κάλυψη χώρων	καθιστικό · Υπν.1 · Υπν.2 · χωλ · κουζίνα (θε…
ΘΕ-ΘΕ1	ΟΚ	ΘΕ1 60×60 – ΚΜ1: στο δυτικό άκρο – πλευρά συνδέσεων / ηλεκτρ…	ελεύθερη
ΘΕ-ΚΤ	ΟΚ	ΚΤ – καταπακτή πρόσβασης στη στέγη στην πλάκα (αρχιτέκτονα…	άνοιγμα 0,74 × 1,60
ΘΕ-ΚΑΝ	ΕΓΚΕΚΡ.	Θυρίδες επίσκεψης – κανόνας ιδιοκτήτη 09/11	μόνο ΘΕ1 60×60 στην ΚΜ1 (πλευρά ηλεκτρ…
ΚΡ-ΚΡ1	ΟΚ	ΚΡ1 W4.01 – καθιστικό – Δ · 20 × 10 cm · οδηγοί 7 / 14 cm	πλήρης · βάθος 10 cm
ΚΡ-ΚΡ2	ΟΚ	ΚΡ2 W4.02 – καθιστικό – Ν · 20 × 10 cm · οδηγοί 7 / 14 cm	πλήρης · βάθος 10 cm
ΚΡ-ΚΡ3	ΟΚ	ΚΡ3 W4.08 – Υπν.1 – Δ · 20 × 10 cm · οδηγοί 7 / 14 cm	πλήρης · βάθος 10 cm
ΚΡ-ΚΡ4	ΟΚ	ΚΡ4 W4.06 – Υπν.2 – Α · 22 × 10 cm · οδηγοί 10 / 17 cm (ανοιγοα…	πλήρης · βάθος 10 cm
KP-W4.03	ΟΚ	W4.03	δεν απαιτείται – κουζίνα – πάνω από τον v…
KP-W4.04	ΟΚ	W4.04	δεν απαιτείται – κουζίνα – έρκερ, πάνω από…
KP-W4.05	ΟΚ	W4.05	δεν απαιτείται – κλιμακοστάσιο (εκτός διαμ…
KP-W4.07	ΟΚ	W4.07	δεν απαιτείται – λουτρό (στο τοιχείο Κ2)
KP-W4.09	ΟΚ	W4.09	δεν απαιτείται – λουτρό γονέων (ντους)
ΣΘ-Ζ1	ΟΚ	Ζ1 +2,65 ↔ Ζ2 +2,40	χαμήλωση καναλάτου ΚΜ1 (προδ. 1/5)
ΣΘ-Ζ4	ΟΚ	Ζ4 +2,67 ↔ Ζ2 +2,40	στη βόρεια παρειά της Δ3.1 (άνοιγμα χωλ –…
ΣΘ-Ζ1	ΟΚ	Ζ1 +2,65 ↔ Ζ3 +2,45	στη γραμμή της δοκού Δ9.1 (περασιά) – καθ…
ΣΘ-Ζ1	ΟΚ	Ζ1 +2,65 ↔ Ζ3 +2,45	στη γραμμή της δοκού Δ9.1 (περασιά)
ΣΘ-Ζ7	ΟΚ	Ζ7 +2,67 ↔ Ζ8 +2,55	στη γραμμή της δοκού Δ1.1 (κεφαλάρι έρκε…
ΣΘ-Ζ10	ΟΚ	Ζ10 +2,67 ↔ Ζ11 +2,45	σανίδα κάτω από τη Δ3.1 (εξαίρεση προδ. …
ΣΘ-Ζ13	ΟΚ	Ζ13 +2,40 ↔ Ζ12 +2,70	κλιμακοστάσιο (R15): ψευδοδοκός καλωδίω…
ΣΘ-Ζ14	ΟΚ	Ζ14 +2,55 ↔ Ζ12 +2,70	γραμμή της Δ2.1 (περασιά) στο μέτωπο του…
ΣΘ-ΣΥΝ	ΟΚ	Στάθμες στο διαμέρισμα	+2.40 · +2.45 · +2.55 · +2.65 · +2.67 · +2.70…

B

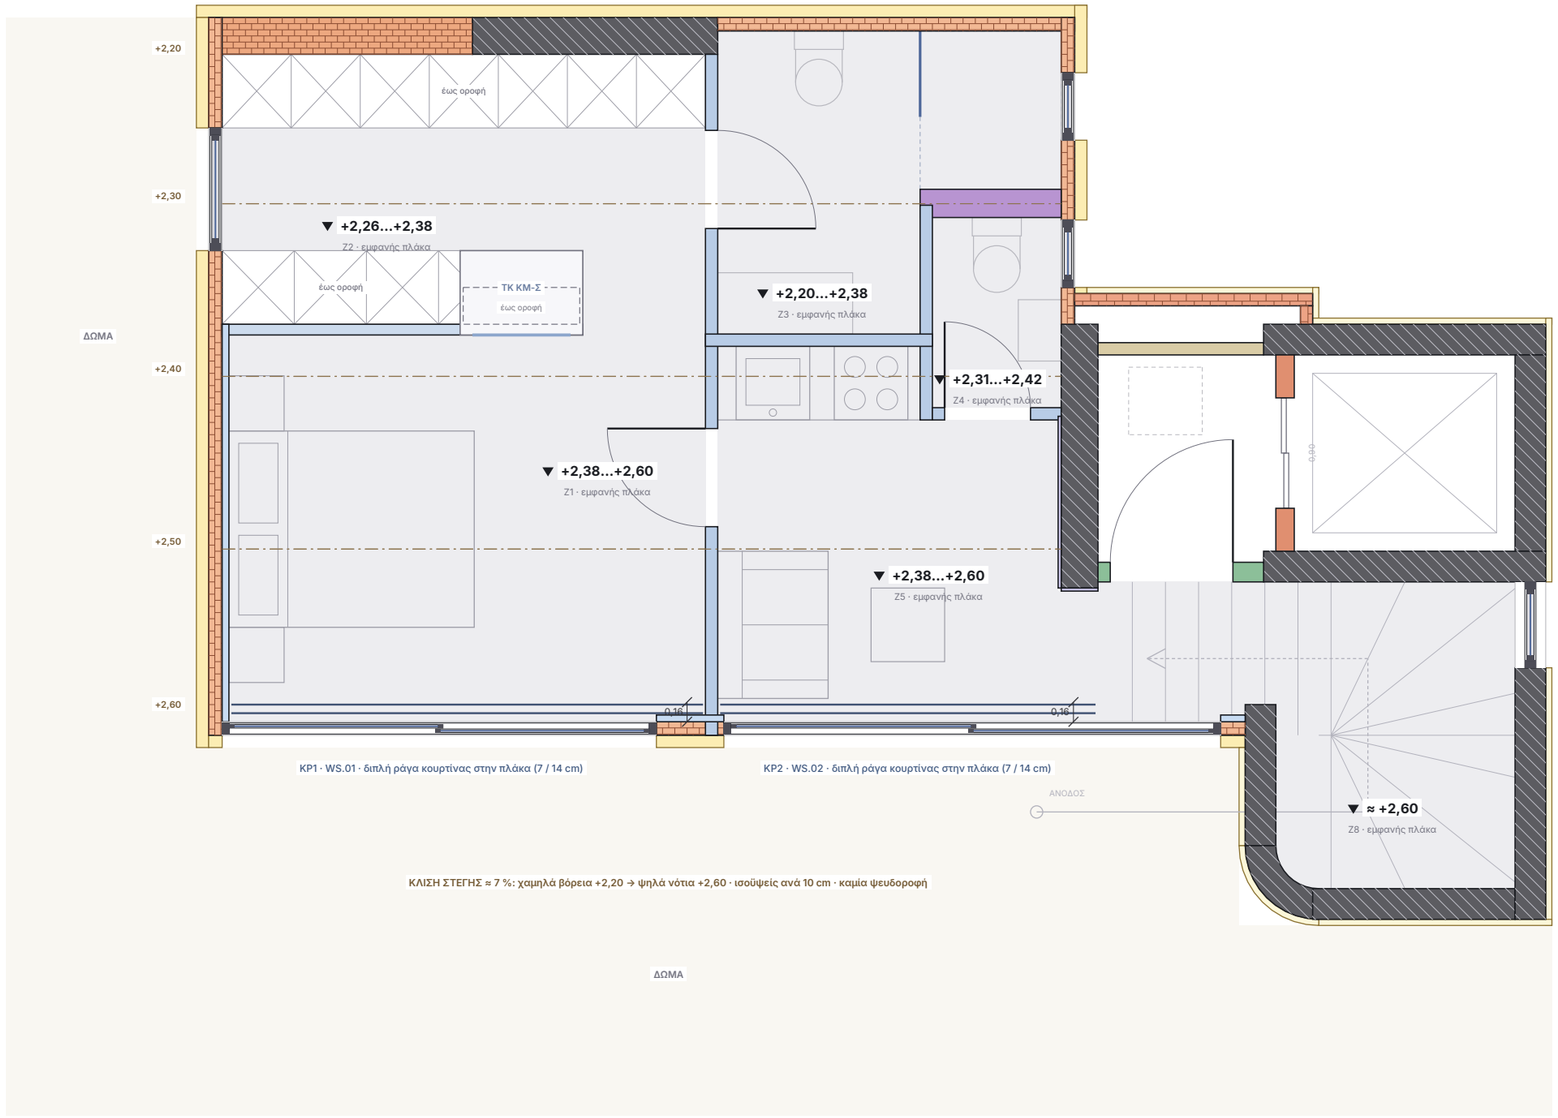

ΣΗΜΕΙΩΣΕΙΣ

Ιδιοκτήτης 07/11: «η οροφή της σοφίτας είναι με κλίση – αρχίζει περίπου από 2,2 και τελειώνει 2,6 · μην την κατεβάσεις γενικά». Η οροφή είναι η κάτω παρειά της κεκλιμένης πλάκας στέγης Σ8 (ανεστραμμένες δοκοί – κανένα δοκάρι μέσα): +2,20 στον βόρειο τοίχο, +2,60 στις νότιες τζαμαρίες, κλίση ≈ 7 % (4°). Οι διακεκομμένες είναι ισοϋψείς ανά 10 cm.

Σ8: κάτω παρειά +18,49 (Δ1.5) → +18,90 (Δ3.2) = 2,29 → 2,70 από το Τ.Δ. +16,20· η ανόψη κρατά τα δυσμενέστερα 2,20 / 2,60 (Α1).

Ύψη ανά χώρο: βεστιάριο 2,26–2,38 · λουτρό 2,20–2,38 · WC 2,31–2,42 · υπνοδωμάτιο / καθιστικό 2,38–2,60.

R03 – ΚΑΜΙΑ ψευδοροφή (ιδιοκτήτης 09/11: «δεν χρειάζονται γυψοσανίδες για κουρτίνες»): διπλή ράγα κουρτίνας KP1 / KP2 βιδωμένη στην πλάκα 7 / 14 cm από το τζάμι, από τοίχο σε τοίχο – παράλληλη στην τζαμαρία, άρα οριζόντια (+2,59).

Πόρτες 2,20 (ιδιοκτήτης 09/11): κάσα +2,25 – λουτρό ΟΡΙΑΚΟ (πλάκα +2,26 στο βόρειο άκρο, Α2) · υπνοδωμάτιο +2,43 · WC +2,42.


ΥΠΟΜΝΗΜΑ


- εμφανής κεκλιμένη πλάκα Σ8 +2,20 → +2,60 – χωρίς ψευδοροφή (ισοϋψείς ανά 10 cm)
- KP διπλή ράγα κουρτίνας στην πλάκα (7 / 14 cm από το τζάμι)

ΕΡΓΟ	ΘΕΜΑ ΣΧΕΔΙΟΥ	ΒΑΣΗ	ΑΡ. ΣΧΕΔΙΟΥ
ΠΕΝΤΑΟΡΟΦΟ ΚΤΗΡΙΟ ΚΑΤΟΙΚΙΩΝ – ΑΡΓΥΡΟΥΠΟΛΗ Κωνσταντινουπόλεως 12 & Αγ. Βαρβάρας · Ο.Τ. 103-15 Εργοδότης: INTERKAT Α.Ε. · Κατασκευή: ARKAD Ι.Κ.Ε.	**ΑΝΟΨΗ – ΣΤΑΘΜΕΣ · ΔΟΚΟΙ · ΚΟΥΡΤΙΝΕΣ** Εμφανής κεκλιμένη πλάκα Σ8 · ισοϋψείς · ράγες κουρτίνας στην πλάκα ΣΟΦΙΤΑ – Δ1 πάνω επίπεδο (μεζονέτα)	Βάση: τοιχοποιίες σοφίτας R04 · Σ8 (κεκλιμένη, ανεστρ. δοκοί)	**ΑΝ-13** **Κλίμακα 1:50 · A3** 09/11/2026 · R03

ΟΨΗ ΤΟΙΧΟΥ ΤΚ – ΚΜ-Σ

από το υπνοδωμάτιο · 1:25 · παρειά T2N-01
x 4,50–5,50 · κενό 0,30

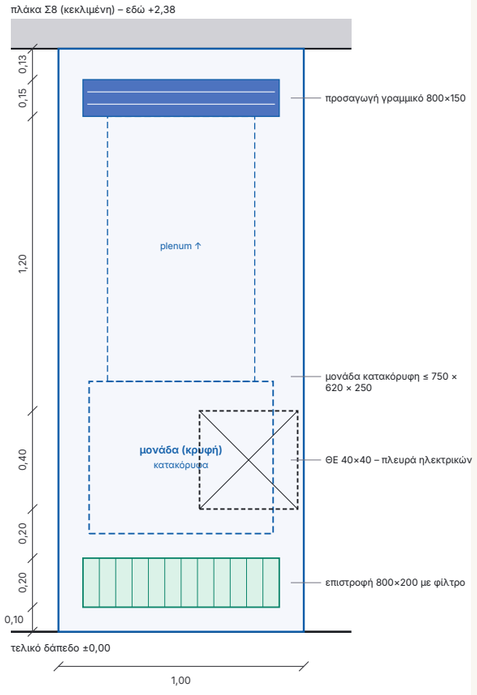

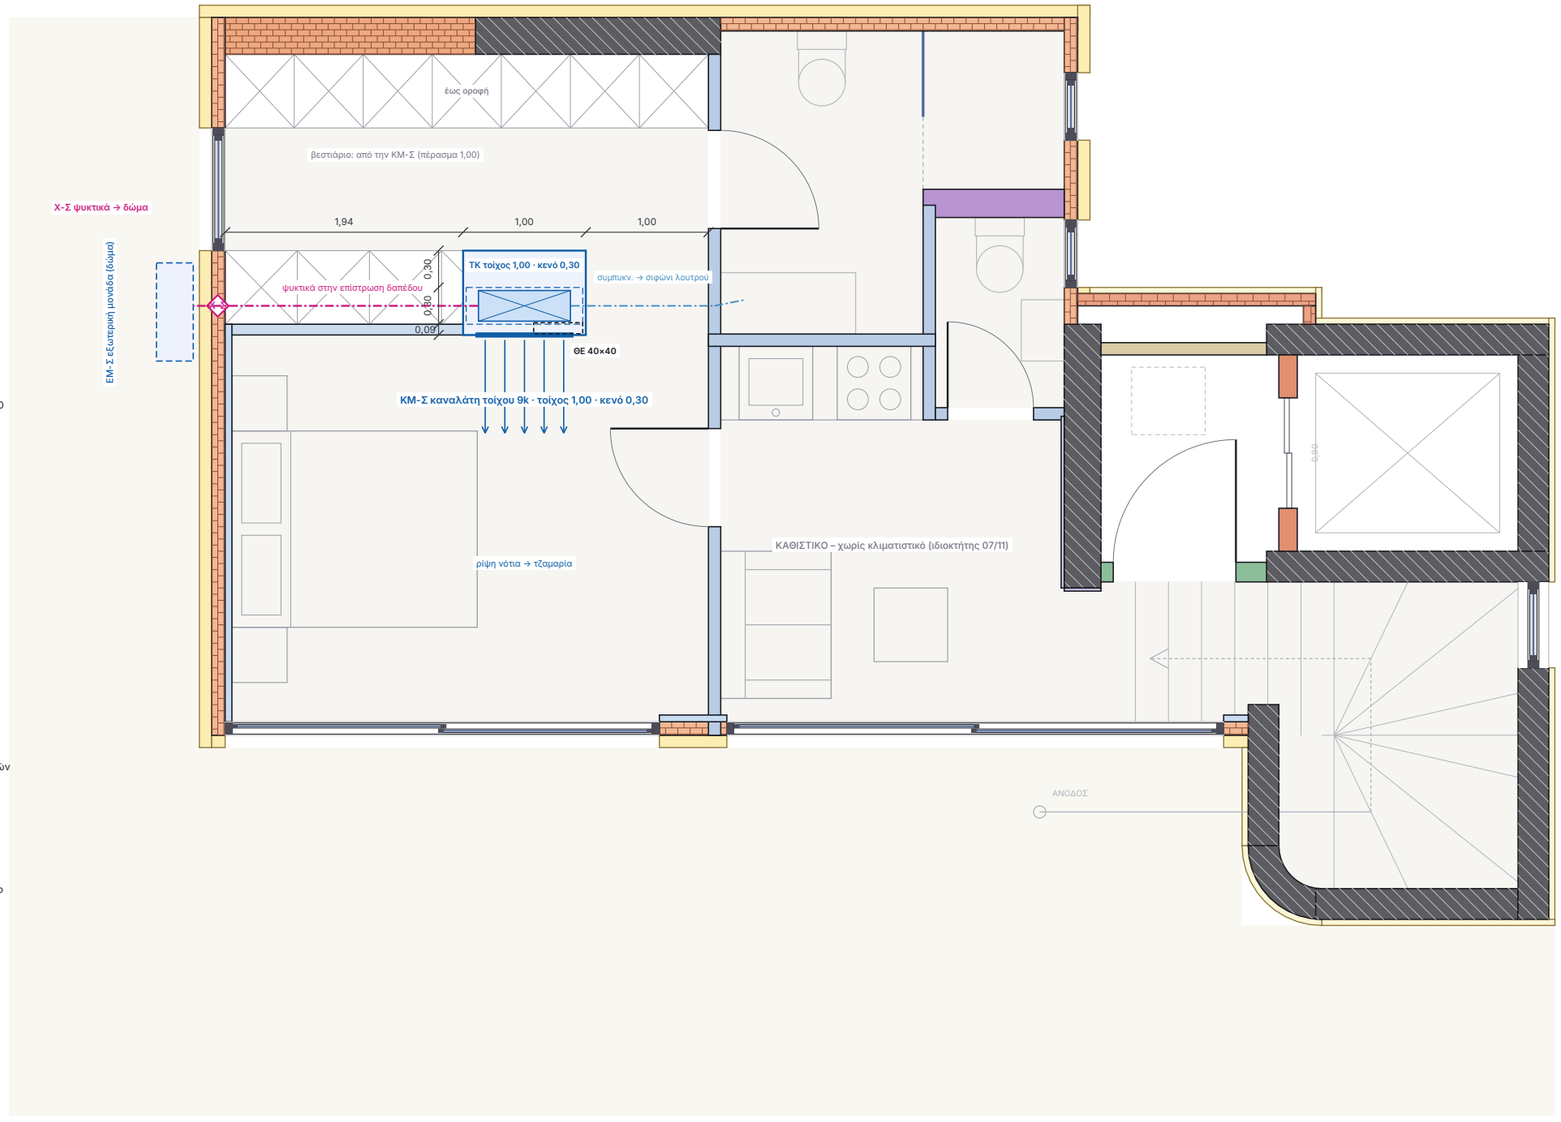

B

ΣΗΜΕΙΩΣΕΙΣ

Ιδιοκτήτης 09/11: «το κλιματιστικό στη σοφίτα δεν θα είναι split, θα είναι καναλάτο αλλά όχι οροφής, τοίχου – πρέπει να δημιουργήσουμε κάπου τοίχο πλάτους 1 m και να έχει κενό 30 cm».

ΘΕΣΗ: Βόρειος τοίχος του υπνοδωματίου (T2N-01) στο 4,50–5,50 = το ανατολικό 1,00 της νότιας ντουλάπας του βεστιαρίου. Η παρειά του υπνοδωματίου μένει επίπεδη με τα στόμια χωνευτά· η ντουλάπα μένει 0,60 στα 1,94 m· από το βεστιάριο μέτωπο 1,00 στη γραμμή των ντουλαπών.

ΓΙΑΤΙ ΕΚΕΙ: η ρίψη πάει νότια, κάθετα στο κρεβάτι, πάνω από τα πόδια του προς την τζαμαρία (το μεγάλο φορτίο) – όχι στο προσκέφαλο. Απορρίφθηκαν: κουτί μέσα στο δωμάτιο (στενεύει στο 0,45 το πέρασμα στο κομοδίνο) · κεφαλάρι (επιστροφή πίσω από το κρεβάτι) · ανατολικός τοίχος (ρίψη προς το προσκέφαλο).

Τοίχος ΤΚ: κενό 0,30 πίσω από την παρειά του υπνοδωματίου (2,70–3,00), μονάδα κατακόρυφα χαμηλά (A4), επιστροφή 800×200 με φίλτρο +0,10…+0,30, προσαγωγή 800×150 +2,10…+2,25 (οροφή εκεί +2,38), θυρίδα 40×40 +0,50…+0,90 στο ανατολικό άκρο (πλευρά ηλεκτρικών). Μπροστά προς το βεστιάριο ντουλάπι / ράφι 0,30. Ενίσχυση (OSB 18) για τη στήριξη της μονάδας.


Ψυκτικά στην επίστρωση δαπέδου δυτικά κάτω από τη ντουλάπα → έξοδος χαμηλά στον T4-07 (Χ-Σ) → εξωτερική μονάδα στο δυτικό δώμα. Συμπυκνώματα με ροή στην επίστρωση ανατολικά → σιφώνι λουτρού. Καμία σωλήνωση στην πλάκα ή σε ψευδοροφή.

Θυρίδες (ιδιοκτήτης 09/11: «μόνο στο καναλάτο, μία τετράγωνη από τη μεριά των ηλεκτρικών»): μόνο η 40×40 της ΚΜ-Σ.

ΥΠΟΜΝΗΜΑ

- ΚΜ-Σ καναλάτη τοίχου μέσα σε τοίχο 1,00 με κενό 0,30 (βέλη = ρίψη από το στόμιο προσαγωγής)
- ΘΕ θυρίδα επίσκεψης τετράγωνη – ΜΟΝΟ στην καναλάτη, στην πλευρά του ηλεκτρικού κουτιού (ιδιοκτήτης 09/11)
- εξωτερική μονάδα
- Χ κατέβασμα / έξοδος σωληνώσεων – καμία οπή σε σκυρόδεμα

ΕΡΓΟ	ΘΕΜΑ ΣΧΕΔΙΟΥ	ΒΑΣΗ	ΑΡ. ΣΧΕΔΙΟΥ
ΠΕΝΤΑΟΡΟΦΟ ΚΤΗΡΙΟ ΚΑΤΟΙΚΙΩΝ – ΑΡΓΥΡΟΥΠΟΛΗ Κωνσταντινουπόλεως 12 & Αγ. Βαρβάρας · Ο.Τ. 103-15 Εργοδότης: INTERKAT Α.Ε. · Κατασκευή: ARKAD Ι.Κ.Ε.	**ΑΝΟΨΗ – ΚΛΙΜΑΤΙΣΜΟΣ · ΘΥΡΙΔΕΣ** Καναλάτη τοίχου στο υπνοδωμάτιο (τοίχος 1,00 · κενό 0,30) · ψυκτικά στο δώμα ΣΟΦΙΤΑ – Δ1 πάνω επίπεδο (μεζονέτα)	Βάση: τοιχοποιίες σοφίτας R04 · Σ8 (κεκλιμένη, ανεστρ. δοκοί)	**ΑΝ-14** **Κλίμακα 1:50 · A3** 09/11/2026 · R03

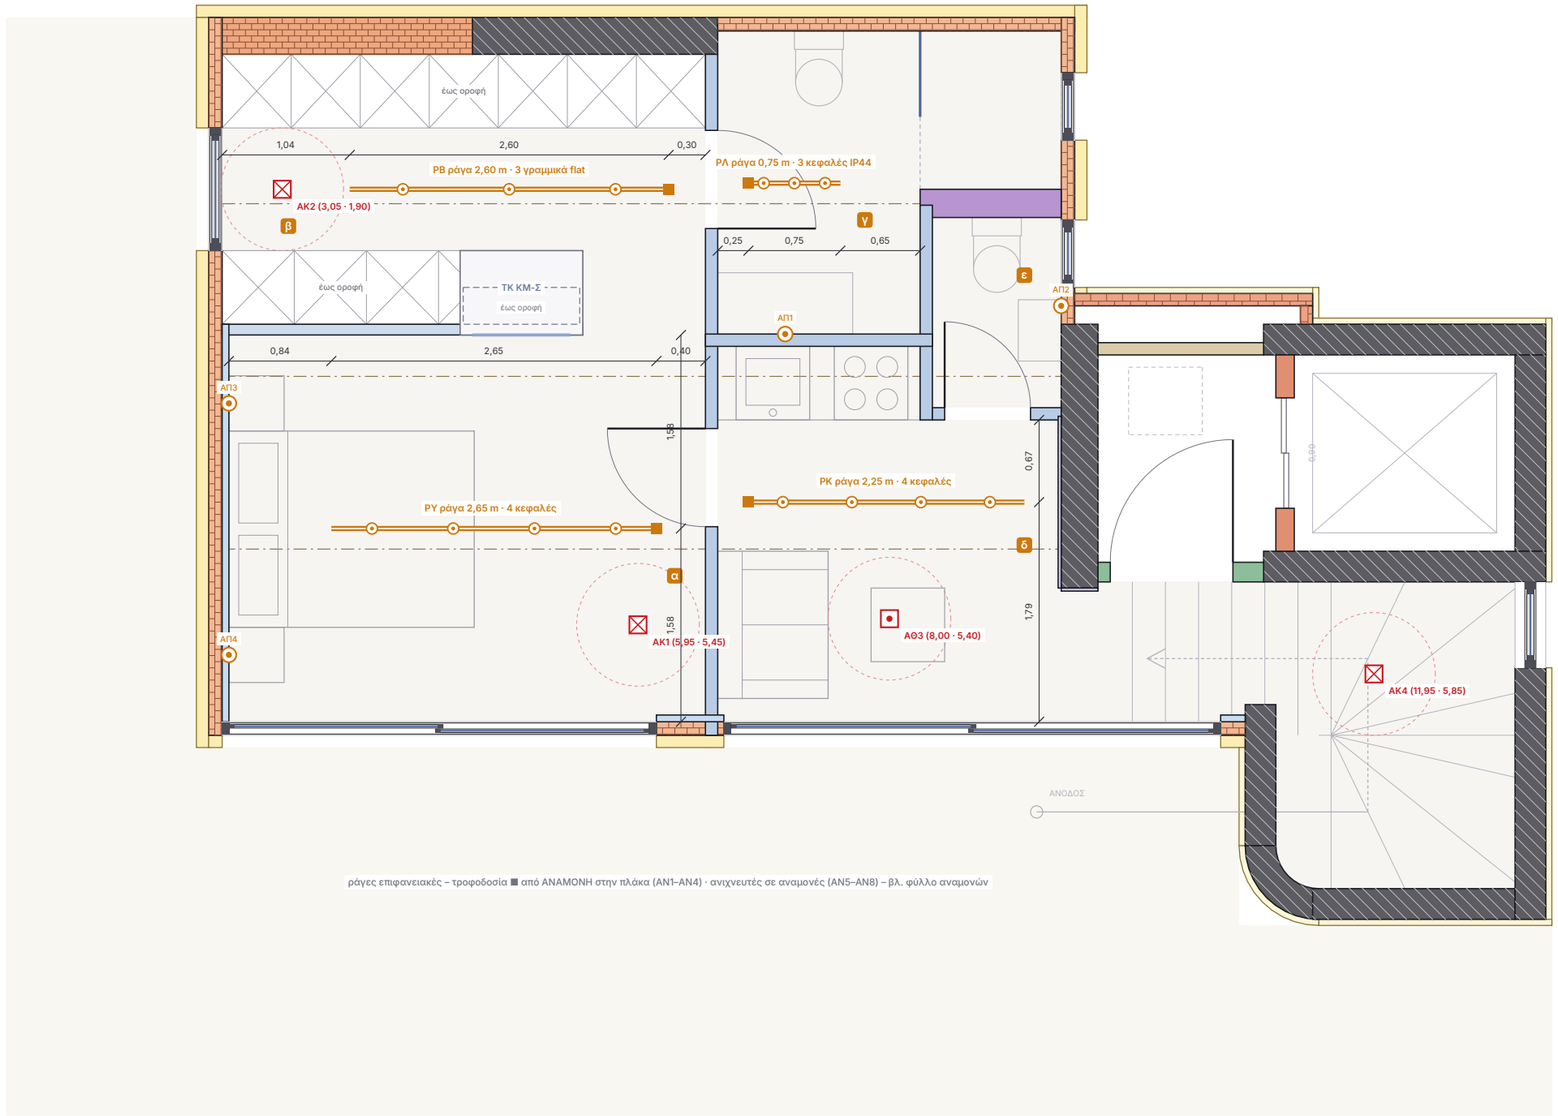

ΣΗΜΕΙΩΣΕΙΣ

Ιδιοκτήτης 09/11: «θα αφήσω αναμονές καλωδίων στην πλάκα της σοφίτας, οπότε θα παίρνουν από την οροφή · δεν χρειάζονται δύο ράγες εκεί που είναι το κρεβάτι και δύο στο κουζινάκι · στο μπάνιο βάλε κι εκεί ράγα, στο WC απλίκα».

Ράγες επιφανειακές στην εμφανή πλάκα, ΟΛΕΣ Α–Δ: παράλληλες στις ισοϋψείς, άρα οριζόντιες. Τροφοδοσία ■ από αναμονή στην πλάκα (ΑΝ1–ΑΝ4).

Υπνοδωμάτιο: ΡΥ 2,65 m στον άξονα του δωματίου = άξονας του κρεβατιού (y 4,665, οροφή +2,49), από 0,84 μετά το κεφαλάρι ως 0,40 από τον ανατολικό τοίχο – οι κεφαλές στρέφονται σε κρεβάτι, ντουλάπα, κουρτίνα· απλίκες ΑΠ3 / ΑΠ4 στα κομοδίνα.

Βεστιάριο: ΡΒ 2,60 m στον άξονα του διαδρόμου με γραμμικά flat (οροφή +2,29). Καθιστικό: ΡΚ 2,25 m, 0,67 μπροστά από τον πάγκο (+2,47) – κεφαλές προς πάγκο και καναπέ.

Λουτρό: ΡΛ 0,75 m (+2,29) ≥ 0,65 από το ντους (εκτός ζωνών 0–2), κεφαλές IP44 προς νιπτήρα, λεκάνη, ντους · ΑΠ1 καθρέπτης IP44. WC: ΑΠ2 IP44.

Πυρανίχνευση σε αναμονές: κλίση 4° < 20° → οροφή επίπεδη (CEN/TS 54-14)· ≥ 0,50 από τοίχους / ράγες, ≥ 1,00 από το στόμιο της ΚΜ-Σ και εκτός της ρίψης.

ΥΠΟΜΝΗΜΑ

- ράγα φωτισμού επιφανειακή, λευκή, με κεφαλές spot (■ = τροφοδοσία από αναμονή στην πλάκα)
- απλίκα τοίχου IP44 (λουτρό / WC) ή απλή (κομοδίνα)
- ΤΚ τοίχος καναλάτης – στόμιο προσαγωγής (για συντονισμό – βλ. φύλλο κλιματισμού)
- ΑΚ ανιχνευτής καπνού (ΕΠ04 · EN 54-7)
- ΑΘ θερμοδιαφορικός ανιχνευτής (κουζίνα · EN 54-5)
- ακτίνα 0,50 m γύρω από ανιχνευτή – κανένας τοίχος / φωτιστικό μέσα

ΕΡΓΟ	ΘΕΜΑ ΣΧΕΔΙΟΥ	ΒΑΣΗ	ΑΡ. ΣΧΕΔΙΟΥ
ΠΕΝΤΑΟΡΟΦΟ ΚΤΗΡΙΟ ΚΑΤΟΙΚΙΩΝ – ΑΡΓΥΡΟΥΠΟΛΗ Κωνσταντινουπόλεως 12 & Αγ. Βαρβάρας · Ο.Τ. 103-15 Εργοδότης: INTERKAT Α.Ε. · Κατασκευή: ARKAD Ι.Κ.Ε.	**ΑΝΟΨΗ – ΦΩΤΙΣΜΟΣ · ΠΥΡΑΝΙΧΝΕΥΣΗ** Ράγες σε αναμονές της πλάκας · απλίκες · ανιχνευτές ΣΟΦΙΤΑ – Δ1 πάνω επίπεδο (μεζονέτα)	Βάση: τοιχοποιίες σοφίτας R04 · Σ8 (κεκλιμένη, ανεστρ. δοκοί)	**ΑΝ-15** **Κλίμακα 1:50 · Α3** 09/11/2026 · R03

ΣΥΜΜΟΡΦΩΣΗ ΜΕ ΤΙΣ ΠΡΟΔΙΑΓΡΑΦΕΣ (ιδιοκτήτης 07/11/2026)

1 Κλιματισμός	Μία καναλάτη ΤΟΙΧΟΥ ΚΜ-Σ στο υπνοδωμάτιο (ιδιοκτήτης 09/11: «καναλάτο όχι οροφής – τοίχος 1 m με κενό 30 cm») με γραμμικό στόμιο ψηλά, ρίψη νότια μακριά από το προσκέφαλο · μία θυρίδα 40×40 · καθιστικό χωρίς κλιματιστικό (ΕΓΚΕΚΡ.).
2 Κουρτίνες	ΚΡ1 (WS.01) / ΚΡ2 (WS.02) διπλή ράγα στην πλάκα, οριζόντια, χωρίς γυψοσανίδα (ιδιοκτήτης 09/11 – ΕΓΚΕΚΡ.).
3 Φωτισμός	Χωρίς χωνευτά spots (ιδιοκτήτης) → 4 ράγες οριζόντιες σε αναμονές της πλάκας (ΡΥ · ΡΒ · ΡΛ · ΡΚ) + 4 απλίκες · λουτρό εκτός ζωνών ντους.
4 Πυρανίχνευση	ΑΚ1 υπνοδωμάτιο · ΑΚ2 βεστιάριο · ΑΘ3 καθιστικό – kitchenette · ΑΚ4 κορυφή σκάλας – όλοι σε αναμονές της πλάκας.
5 Κατασκευή	Χωρίς καμία ψευδοροφή (ιδιοκτήτης) · κανένα δοκάρι (Σ8 ανεστραμμένες) · 8 αναμονές ΑΝ1–ΑΝ8 με διαστάσεις από το σκυρόδεμα · πόρτες 2,20 κάτω από την κεκλιμένη πλάκα (λουτρό οριακό – Α2).
6 Γενική αρχή	Μία οροφή: η κεκλιμένη πλάκα, καθαρή· οι ράγες ακολουθούν τις ισοϋψείς· κανένα κανάλι / σωλήνας ορατός.

ΕΓΚΕΚΡΙΜΕΝΑ / ΑΠΟΦΑΣΕΙΣ ΙΔΙΟΚΤΗΤΗ (07 – 09/11/2026)

· Σοφίτα: μόνο ένα κλιματιστικό, στο υπνοδωμάτιο – καναλάτη ΤΟΙΧΟΥ σε τοίχο 1,00 με κενό 0,30 (ιδιοκτήτης 09/11).

· Σοφίτα: χωρίς καμία ψευδοροφή – χωρίς χωνευτά spots (ράγες σε αναμονές της πλάκας) και χωρίς γυψοσανίδες για κουρτίνες (ιδιοκτήτης 07 / 09/11).

· Πόρτες 2,20 παντού · θυρίδες μόνο στις καναλάτες, μία τετράγωνη στην πλευρά των ηλεκτρικών (ιδιοκτήτης 09/11).

ΑΛΛΑΓΕΣ R02 → R03 (ιδιοκτήτης 09/11/2026)

· Αναμονές στην πλάκα (ιδιοκτήτης 09/11: «θα αφήσω αναμονές καλωδίων στην πλάκα της σοφίτας – πρέπει να βγάλουμε ακριβή θέση»): 8 αναμονές ΑΝ1–ΑΝ8 (4 ράγες + 4 ανιχνευτές) με διαστάσεις από τις γωνίες Κ2 / Κ3 / Κ6 – νέο φύλλο αναμονών. Οι ράγες δεν τροφοδοτούνται πια από τοίχο / υπέρθυρο.

· Ράγες (ιδιοκτήτης: «δεν χρειάζονται δύο ράγες εκεί που είναι το κρεβάτι και δύο στο κουζινάκι · στο μπάνιο βάλε κι εκεί ράγα, στο WC απλίκα»): ΡΥ μία στον άξονα του υπνοδωματίου / κρεβατιού · ΡΚ μία στο καθιστικό 0,67 μπροστά από τον πάγκο · ΝΕΑ ΡΛ στο λουτρό εκτός ζωνών ντους · ΡΒ βεστιάριο 2,60. Απλίκες: καθρέπτης λουτρού, WC, 2 κομοδίνα (καταργήθηκαν η απλίκα ντους και η γενική του λουτρού).

· Κουρτίνες (ιδιοκτήτης: «δεν χρειάζονται γυψοσανίδες για κουρτίνες»): καταργήθηκαν οι λωρίδες +2,48 και οι εσοχές – διπλή ράγα κουρτίνας κατευθείαν στην πλάκα, οριζόντια· η σοφίτα χωρίς καμία ψευδοροφή.

· Κλιματισμός (ιδιοκτήτης: «όχι split – καναλάτο, όχι οροφής, τοίχου – τοίχος πλάτους 1 m με κενό 30 cm»): ΚΜ-Σ καναλάτη τοίχου στον βόρειο τοίχο του υπνοδωματίου, στο ανατολικό 1,00 της νότιας ντουλάπας βεστιαρίου (4,50–5,50)· προσαγωγή 800×150 ψηλά με ρίψη νότια, επιστροφή χαμηλά, θυρίδα 40×40 στην πλευρά των ηλεκτρικών· ψυκτικά στην επίστρωση → δώμα · συμπυκνώματα → σιφώνι λουτρού. Το split καταργήθηκε.

· Πόρτες 2,20 (ιδιοκτήτης: «ως 2,20 παντού»): κάσα +2,25 κάτω από την κεκλιμένη πλάκα – η πόρτα λουτρού (πλάκα +2,26 στο βόρειο άκρο) ΟΡΙΑΚΗ με τα 2,20 του ιδιοκτήτη, άνετη με τα 2,29 του Σ8 (Α2).

ΠΡΟΗΓΟΥΜΕΝΗ ΑΝΑΘΕΩΡΗΣΗ

· R02: κεκλιμένη εμφανής πλάκα · 5 ράγες με τροφοδοσία από τοίχο · 6 απλίκες · split ΚΜ-Σ πάνω από το κεφαλάρι · λωρίδες κουρτίνας +2,48.

ΑΝΟΙΚΤΑ ΣΗΜΕΙΑ

· Α1 [ΕΠΙ ΤΟΠΟΥ] Κλίση στέγης: ο Σ8 δίνει κάτω παρειά +18,49 (Δ1.5, βόρεια) → +18,90 (Δ3.2, νότια) = 2,29 → 2,70 από το Τ.Δ. +16,20· ο ιδιοκτήτης ≈ 2,20 → 2,60. Η ανόψη κρατά τα δυσμενέστερα (2,20 / 2,60) – μέτρηση μετά το ξεκαλούπωμα και επιβεβαίωση του τελικού δαπέδου.

· Α2 [ΕΠΙ ΤΟΠΟΥ] Πόρτα λουτρού 2,20: κάσα +2,25, πλάκα +2,26 στο βόρειο άκρο (2,20 ιδιοκτήτη) – χωράει χωρίς πρέκι, η κάσα βιδώνεται στον οδηγό UW της πλάκας. Με τα 2,29 του Σ8 περιθώριο 10 cm. Αν η μέτρηση δώσει < 2,26: πόρτα 2,15 στο λουτρό.

· Α3 [ΜΟΝΤΕΛΟ] Ράγες: επιφανειακό σύστημα λευκό (μονοφασικό 230 V ή μαγνητικό 48 V με τροφοδοτικό στο κουτί της αναμονής) με κεφαλές 7–10 W 2700 K · ΡΒ γραμμικά flat · ΡΛ κεφαλές IP44.

· Α4 [ΜΟΝΤΕΛΟ] ΚΜ-Σ: καναλάτη slim σε κατακόρυφη τοποθέτηση (ή κρυφού δαπέδου) ≤ 750 πλάτος × 250 βάθος – επιβεβαίωση με το μοντέλο πριν κτιστεί ο τοίχος· ισχύς 9k ή 12k κατά τη μελέτη ψύξης (νότια τζαμαρία 3,5 m κάτω από στέγη) · εξωτερική μονάδα στο δυτικό δώμα (Σύσταση ΟΙ).

· Α5 [ΣΥΝΤΟΝΙΣΜΟΣ] Ο τοίχος κλιματιστικού ΤΚ (1,00 × 0,30 κενό) και η νότια ντουλάπα 1,94 να περαστούν στις τοιχοποιίες σοφίτας (R05) μετά την έγκριση της θέσης.

· Α6 [ΣΥΝΤΟΝΙΣΜΟΣ] Αποχετεύσεις λουτρού / WC, ψυκτικά και συμπυκνώματα ΚΜ-Σ στην επίστρωση της σοφίτας (15 cm) – όχι στην οροφή του Δ΄.


· Α7 [ΚΑΤΑΣΚΕΥΗ] Αναμονές: κουτί οροφής για σκυρόδεμα Ø 80 στον ξυλότυπο + εύκαμπτος σωλήνας Ø 20 βαρέως τύπου με οδηγό, μέσα στην πλάκα ως τη θέση καθόδου (μέσα στη γραμμή του μελλοντικού τοίχου γυψοσανίδας, ±2 cm)· φωτογράφιση με μέτρο πριν τη σκυροδέτηση.

· Α8 [ΕΠΙ ΤΟΠΟΥ] Πλάκα πάνω από την ιδιωτική σκάλα (ανατολικά της Δ9.5): κλίση / στάθμη δεν φαίνεται στον Σ8 – μέτρηση.

ΕΛΕΓΧΟΣ ΣΥΓΚΡΟΥΣΕΩΝ & ΣΤΑΘΜΩΝ – 49 έλεγχοι · ΟΚ 43 · ΟΡΙΑΚΟ 1 · ΕΓΚΕΚΡ. 5 · ΑΠΟΚΛΙΣΗ 0

Αυτόματος έλεγχος από το μοντέλο (code/anopseis/checks.py): στάθμες ↔ δοκοί · κενό μονάδων · θυρίδες · spots ↔ ζώνες / θυρίδες / μονάδες / αεραγωγοί / κουρτινόθηκες · ανιχνευτές ↔ τοίχοι / φωτιστικά / στόμια · κουρτινόθηκες ↔ κουφώματα / δοκοί.

ΚΩΔ.	ΚΑΤΑΣΤ.	ΣΤΟΙΧΕΙΟ	ΜΕΤΡΗΣΗ
ΣΤ-Ζ1	ΟΚ	Ζ1 ΥΠΝΟΔΩΜΑΤΙΟ – εμφανής πλάκα +2,38…+2,60	Σ8 κεκλιμένη (ανεστραμμένες δοκοί): +2,2…
ΣΤ-Ζ2	ΟΚ	Ζ2 ΒΕΣΤΙΑΡΙΟ – εμφανής πλάκα +2,26…+2,38	Σ8 κεκλιμένη (ανεστραμμένες δοκοί): +2,2…
ΣΤ-Ζ3	ΟΚ	Ζ3 ΛΟΥΤΡΟ – εμφανής πλάκα +2,20…+2,38	Σ8 κεκλιμένη (ανεστραμμένες δοκοί): +2,2…
ΣΤ-Ζ4	ΟΚ	Ζ4 WC – εμφανής πλάκα +2,31…+2,42	Σ8 κεκλιμένη (ανεστραμμένες δοκοί): +2,2…
ΣΤ-Ζ5	ΟΚ	Ζ5 ΚΑΘΙΣΤΙΚΟ – KITCHENETTE – εμφανής πλάκα +2,38…+2,60	Σ8 κεκλιμένη (ανεστραμμένες δοκοί): +2,2…
ΣΤ-Ζ8	ΟΚ	Ζ8 ΚΛΙΜΑΚΟΣΤΑΣΙΟ Δ1 – εμφανής πλάκα ≈ +2,60	πλάκα Σ8 πάνω από την ιδιωτική σκάλα (δ…
ΚΛ-ΚΜ-Σ	ΟΚ	ΚΜ-Σ καναλάτη τοίχου 9.000 Btu/h – Υπνοδωμάτιο σοφίτας (τοί…	τοίχος 1,00 · κενό 0,30
ΣΤ-ΚΜ-Σ	ΟΚ	ΚΜ-Σ προσαγωγή γραμμικό 800×150 ψηλά στην παρειά	οροφή στον τοίχο +2,38 · στόμιο +2,10…+2…
ΚΡ-ΚΜ-Σ	ΟΚ	ΚΜ-Σ – ρίψη νότια, κάθετα στο κρεβάτι, προς την τζαμαρία	ρίψη νότια στη ζώνη x 4,60–5,40 (πόδια του…
ΘΕ-ΚΜ-Σ	ΟΚ	ΚΜ-Σ – θυρίδα 40×40 τετράγωνη στην παρειά	40×40 στο ανατολικό άκρο (πλευρά ηλεκτρ…
ΨΣ-ΚΜ-Σ	ΟΚ	ΚΜ-Σ – ψυκτικά / συμπυκνώματα	ψυκτικά κάτω στην επίστρωση δαπέδου → δ…
ΚΔ-ΥΠΝ	ΟΚ	Υπνοδωμάτιο σοφίτας	ΚΜ-Σ καναλάτη ΤΟΙΧΟΥ (ιδιοκτήτης 09/11: …
ΚΔ-ΒΕΣΤ	ΟΚ	Βεστιάριο	από την ΚΜ-Σ (ανοιχτό στο υπνοδωμάτιο …
ΚΔ-ΚΑΘ	ΕΓΚΕΚΡ.	Καθιστικό – kitchenette σοφίτας	χωρίς κλιματιστικό – ιδιοκτήτης 07/11: «μό…
SP-ΟΡΟ	ΕΓΚΕΚΡ.	Εμφανής κεκλιμένη πλάκα Σ8	δεν γίνονται (ιδιοκτήτης 07/11) → ράγες σε …
ΡΓ-ΡΥ	ΟΚ	ΡΥ ράγα – υπνοδωμάτιο – άξονας δωματίου / κρεβατιού (μία ράγ…	μήκος 2.65 · οροφή +2,49 · κεφαλές ≈ +2,…
ΡΓ-ΡΒ	ΟΚ	ΡΒ ράγα – βεστιάριο – άξονας διαδρόμου (γραμμικά flat)	μήκος 2.60 · οροφή +2,29 · κεφαλές ≈ +2,2…
ΡΓ-ΡΛ	ΟΚ	ΡΛ ράγα – λουτρό – εκτός ζωνών ντους (≥ 0,60)	μήκος 0.75 · οροφή +2,29 · κεφαλές ≈ +2,1…
ΡΓ-ΡΚ	ΟΚ	ΡΚ ράγα – καθιστικό – kitchenette (μία ράγα)	μήκος 2.25 · οροφή +2,47 · κεφαλές ≈ +2,3…
ΑΠ-ΑΠ1	ΟΚ	ΑΠ1 απλίκα IP44 – λουτρό – πάνω από τον καθρέπτη	τοίχος 0.00
ΑΠ-ΑΠ2	ΟΚ	ΑΠ2 απλίκα IP44 – WC – πάνω από τον νιπτήρα	τοίχος 0.00
ΑΠ-ΑΠ3	ΟΚ	ΑΠ3 απλίκα τοίχου – κομοδίνο Β	τοίχος 0.00
ΑΠ-ΑΠ4	ΟΚ	ΑΠ4 απλίκα τοίχου – κομοδίνο Ν	τοίχος 0.00
ΠΥ-ΑΚ1	ΟΚ	ΑΚ1 καπνού (5.95 · 5.45) – υπνοδωμάτιο (εκτός της ρίψης της ΚΜ-…	τοίχος 0.55 · ΡΥ 0.79 · ΚΜ-Σ 2.43
ΠΥ-ΑΚ2	ΟΚ	ΑΚ2 καπνού (3.05 · 1.90) – βεστιάριο – άξονας διαδρόμου 1,00	τοίχος 0.50 (διάδρομος 1,00 – άξονας) · ΡΒ …
ΠΥ-ΑΘ3	ΟΚ	ΑΘ3 θερμοδιαφορικός (8.00 · 5.40) – καθιστικό – kitchenette (θε…	τοίχος 1.40 · ΡΚ 0.95 · ΚΜ-Σ 3.48
ΠΥ-ΑΚ4	ΟΚ	ΑΚ4 καπνού (11.95 · 5.85) – κορυφή ιδιωτικής σκάλας (καλύπτει κ…	τοίχος 0.75 · ΡΚ 3.18 · ΚΜ-Σ 7.11
ΠΥ-ΧΩΡ	ΟΚ	Κάλυψη χώρων	υπνοδωμάτιο · βεστιάριο · καθιστικό (θερμι…
ΘΕ-ΚΑΝ	ΕΓΚΕΚΡ.	Θυρίδες επίσκεψης – κανόνας ιδιοκτήτη 09/11	μόνο η θυρίδα 40×40 της ΚΜ-Σ στην παρει…
ΚΡ-ΚΡ1	ΕΓΚΕΚΡ.	ΚΡ1 WS.01 – υπνοδωμάτιο – Ν · ράγα διπλή στην πλάκα · οδηγοί 7…	πλήρης 3.88 m · οροφή +2,59 σταθερή
ΚΡ-ΚΡ2	ΕΓΚΕΚΡ.	ΚΡ2 WS.02 – καθιστικό – Ν · ράγα διπλή στην πλάκα · οδηγοί 7 / 1…	πλήρης 3.10 m · οροφή +2,59 σταθερή
ΚΡ-WS.06	ΟΚ	WS.06	δεν απαιτείται – βεστιάριο – ανάμεσα σε ντ…
ΚΡ-WS.02-Α	ΟΚ	WS.02-A	δεν απαιτείται – ανατολικό 1,00 της τζαμα…
ΚΡ-WS.03	ΟΚ	WS.03	δεν απαιτείται – κλιμακοστάσιο (εκτός διαμ…
ΚΡ-WS.04	ΟΚ	WS.04	δεν απαιτείται – WC (ποδιά 1,50)
ΚΡ-WS.05	ΟΚ	WS.05	δεν απαιτείται – ντους (ποδιά 1,50)
ΠΡ-ΛΟΥ	ΟΡΙΑΚΟ	Πόρτα λουτρού 2,20 – κάσα +2,25	πλάκα +2,26 (Σ8 +2,35) · περιθώριο 8 mm (…
ΠΡ-ΥΠΝ	ΟΚ	Πόρτα υπνοδωματίου 2,20 – κάσα +2,25	πλάκα +2,43 (Σ8 +2,53) · περιθώριο 180 m…
ΠΡ-WC	ΟΚ	Πόρτα WC 2,20 – κάσα +2,25	πλάκα +2,42 (Σ8 +2,52) · περιθώριο 172 m…
ΑΝ-ΑΝ1	ΟΚ	ΑΝ1 ράγα ΡΥ υπνοδωματίου (6.10 · 4.67)	πλάκα +2,49 · ΝΑ γωνία Κ2: 0,50 Δ · 3,87 Ν
ΑΝ-ΑΝ2	ΟΚ	ΑΝ2 ράγα ΡΒ βεστιαρίου (6.20 · 1.90)	πλάκα +2,29 · ΝΑ γωνία Κ2: 0,40 Δ · 1,10 Ν
ΑΝ-ΑΝ3	ΟΚ	ΑΝ3 ράγα ΡΛ λουτρού (6.85 · 1.85)	πλάκα +2,29 · ΝΑ γωνία Κ2: 0,25 Α · 1,05 Ν
ΑΝ-ΑΝ4	ΟΚ	ΑΝ4 ράγα ΡΚ καθιστικού (6.85 · 4.45)	πλάκα +2,47 · ΝΑ γωνία Κ2: 0,25 Α · 3,65 Ν
ΑΝ-ΑΝ5	ΟΚ	ΑΝ5 ανιχνευτής ΑΚ1 (5.95 · 5.45)	πλάκα +2,54 · ΝΑ γωνία Κ2: 0,65 Δ · 4,65 Ν
ΑΝ-ΑΝ6	ΟΚ	ΑΝ6 ανιχνευτής ΑΚ2 (3.05 · 1.90)	πλάκα +2,29 · ΝΔ γωνία Κ2: 1,55 Δ · 1,10 Ν
ΑΝ-ΑΝ7	ΟΚ	ΑΝ7 ανιχνευτής ΑΘ3 (8.00 · 5.40)	πλάκα +2,54 · ΒΔ γωνία Κ3: 1,40 Δ · 2,40 Ν
ΑΝ-ΑΝ8	ΟΚ	ΑΝ8 ανιχνευτής ΑΚ4 (σκάλα) (11.95 · 5.85)	πλάκα +2,57 · ΝΔ γωνία τοιχείου Κ6: 0,90 …
ΣΘ-Μία	ΟΚ	Μία οροφή	R03: χωρίς λωρίδες κουρτίνας (ιδιοκτήτης)…
ΣΘ-ΣΥΝ	ΟΚ	Στάθμες στο διαμέρισμα	+2.60 (εμφανής κεκλιμένη πλάκα +2,20 →…

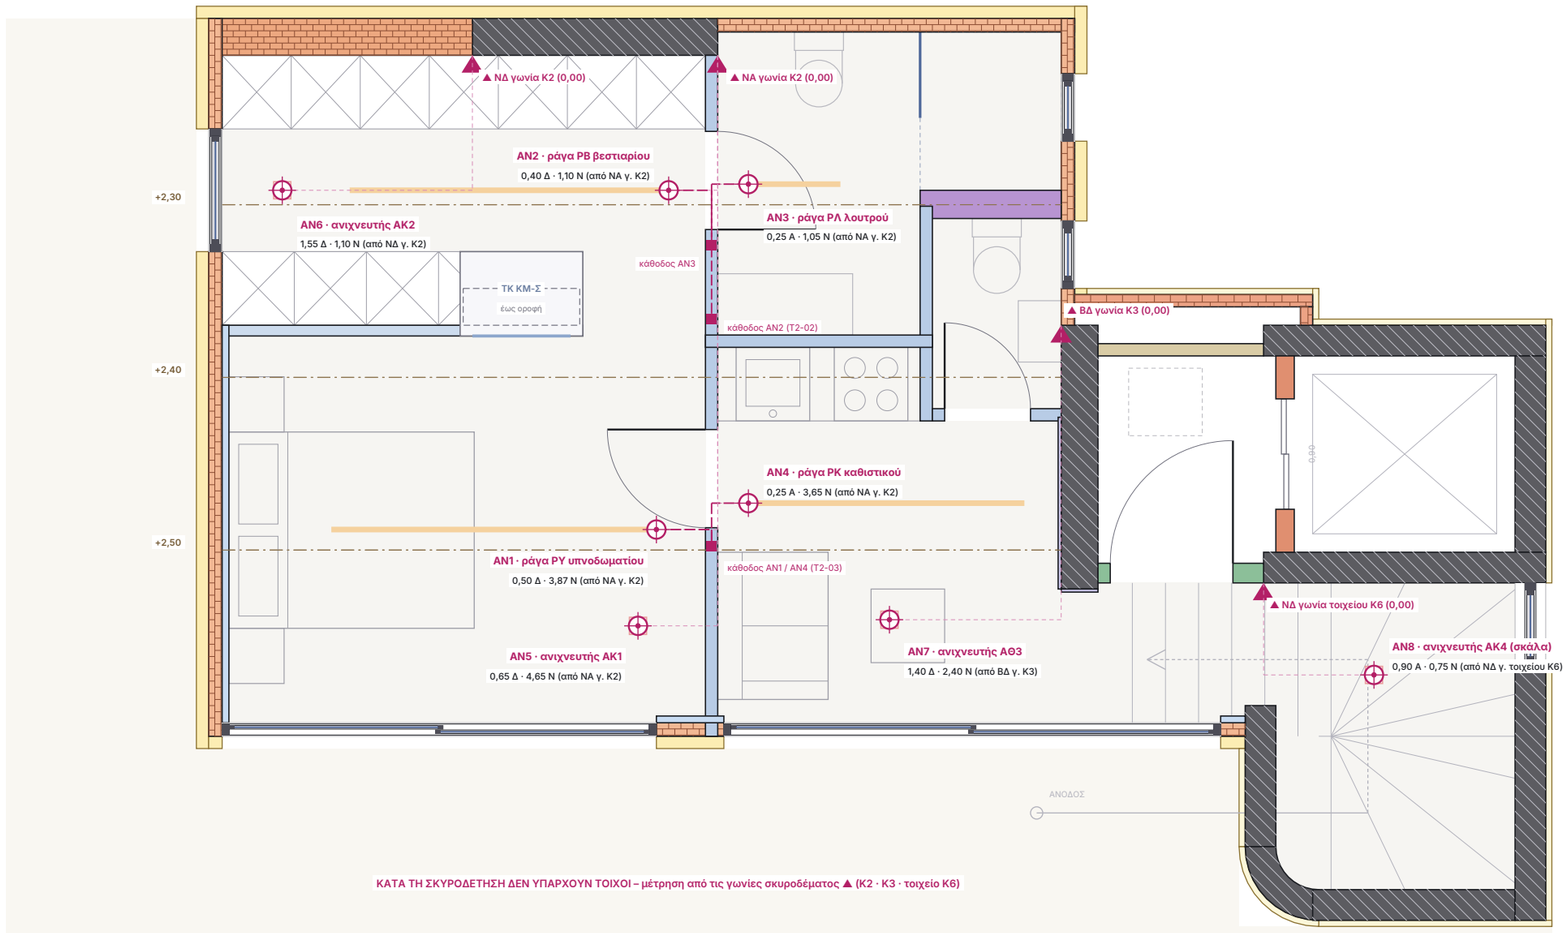

ΠΙΝΑΚΑΣ ΑΝΑΜΟΝΩΝ – κουτί οροφής για σκυρόδεμα Ø 80 στον ξυλότυπο + σωλήνας Ø 20 με οδηγό μέσα στην πλάκα

ΚΩΔ.	ΤΡΟΦΟΔΟΤΕΙ	x · y μοντέλου	ΣΤΟ ΚΑΛΟΥΠΙ – από γωνία σκυροδέματος	ΜΕΤΑ ΤΟΥΣ ΤΟΙΧΟΥΣ – από τελικές παρειές	ΚΑΤΩ ΠΑΡΕΙΑ ΠΛΑΚΑΣ	ΚΑΘΟΔΟΣ ΣΩΛΗΝΑ (πρόταση – κατά τα ηλεκτρολογικά)
ΑΝ1	ράγα ΡΥ υποδωματίου	6,10 · 4,67	ΝΑ γωνία Κ2: 0,50 Δ · 3,87 Ν	Υποδωματιο: 3,48 από Δ · 1,58 από Β παρειά	+2,49 (Σ8 +2,59)	(6,55 · 4,80) Τ2-03 (πλευρά κλειδαριάς πόρτας Υπν.) – διακόπτες υποδωματίου / καθιστικού
ΑΝ2	ράγα ΡΒ βεστιαρίου	6,20 · 1,90	ΝΑ γωνία Κ2: 0,40 Δ · 1,10 Ν	Βεστιαριο: 3,64 από Δ · 0,50 από Β παρειά	+2,29 (Σ8 +2,38)	(6,55 · 2,95) Τ2-02 – διακόπτης βεστιαρίου στο πέρασμα
ΑΝ3	ράγα ΡΛ λουτρού	6,85 · 1,85	ΝΑ γωνία Κ2: 0,25 Α · 1,05 Ν	Λουτρο: 0,25 από Δ · 1,24 από Β παρειά	+2,29 (Σ8 +2,38)	(6,55 · 2,35) Τ2-02 – διακόπτης λουτρού έξω από την πόρτα
ΑΝ4	ράγα ΡΚ καθιστικού	6,85 · 4,45	ΝΑ γωνία Κ2: 0,25 Α · 3,65 Ν	Καθιστικο: 0,25 από Δ · 0,67 από Β παρειά	+2,47 (Σ8 +2,57)	(6,55 · 4,80) Τ2-03 (πλευρά κλειδαριάς πόρτας Υπν.) – διακόπτες υποδωματίου / καθιστικού
ΑΝ5	ανιχνευτής ΑΚ1	5,95 · 5,45	ΝΑ γωνία Κ2: 0,65 Δ · 4,65 Ν	Υποδωματιο: 3,33 από Δ · 2,36 από Β παρειά	+2,54 (Σ8 +2,64)	διασύνδεση ανιχνευτών μέσα στην πλάκα – κάθοδος κατά τη μελέτη πυρανίχνευσης (ΕΠ04)
ΑΝ6	ανιχνευτής ΑΚ2	3,05 · 1,90	ΝΔ γωνία Κ2: 1,55 Δ · 1,10 Ν	Βεστιαριο: 0,49 από Δ · 0,50 από Β παρειά	+2,29 (Σ8 +2,38)	διασύνδεση ανιχνευτών μέσα στην πλάκα – κάθοδος κατά τη μελέτη πυρανίχνευσης (ΕΠ04)
ΑΝ7	ανιχνευτής ΑΘ3	8,00 · 5,40	ΒΔ γωνία Κ3: 1,40 Δ · 2,40 Ν	Καθιστικο: 1,40 από Δ · 1,62 από Β παρειά	+2,54 (Σ8 +2,64)	διασύνδεση ανιχνευτών μέσα στην πλάκα – κάθοδος κατά τη μελέτη πυρανίχνευσης (ΕΠ04)
ΑΝ8	ανιχνευτής ΑΚ4 (σκάλα)	11,95 · 5,85	ΝΔ γωνία τοιχείου Κ6: 0,90 Α · 0,75 Ν	Κλιμακοστασιο δ1: 2,25 από Δ · 0,75 από Β παρειά	+2,57 (Σ8 +2,67)	διασύνδεση ανιχνευτών μέσα στην πλάκα – κάθοδος κατά τη μελέτη πυρανίχνευσης (ΕΠ04)

ΕΡΓΟ

ΠΕΝΤΑΟΡΟΦΟ ΚΤΗΡΙΟ ΚΑΤΟΙΚΙΩΝ – ΑΡΓΥΡΟΥΠΟΛΗ
Κωνσταντινουπόλεως 12 & Αγ. Βαρβάρας · Ο.Τ. 103-15
Εργοδότης: INTERKAT Α.Ε. · Κατασκευή: ARKAD Ι.Κ.Ε.

ΘΕΜΑ ΣΧΕΔΙΟΥ

ΑΝΑΜΟΝΕΣ ΚΑΛΩΔΙΩΝ ΣΤΗΝ ΠΛΑΚΑ ΣΤΕΓΗΣ Σ8
Θέσεις αναμονών ΑΝ1–ΑΝ8 (ράγες · ανιχνευτές) πριν τη σκυροδέτηση – μέτρηση από το σκυρόδεμα
ΣΟΦΙΤΑ – Δ1 πάνω επίπεδο (μεζονέτα)

ΒΑΣΗ

Βάση: τοιχοποιίες σοφίτας R04 · Σ8 (κεκλιμένη, ανεστρ. δοκοί)

ΑΡ. ΣΧΕΔΙΟΥ

ΑΝ-17
Κλίμακα 1:50 · Α3
09/11/2026 · R03