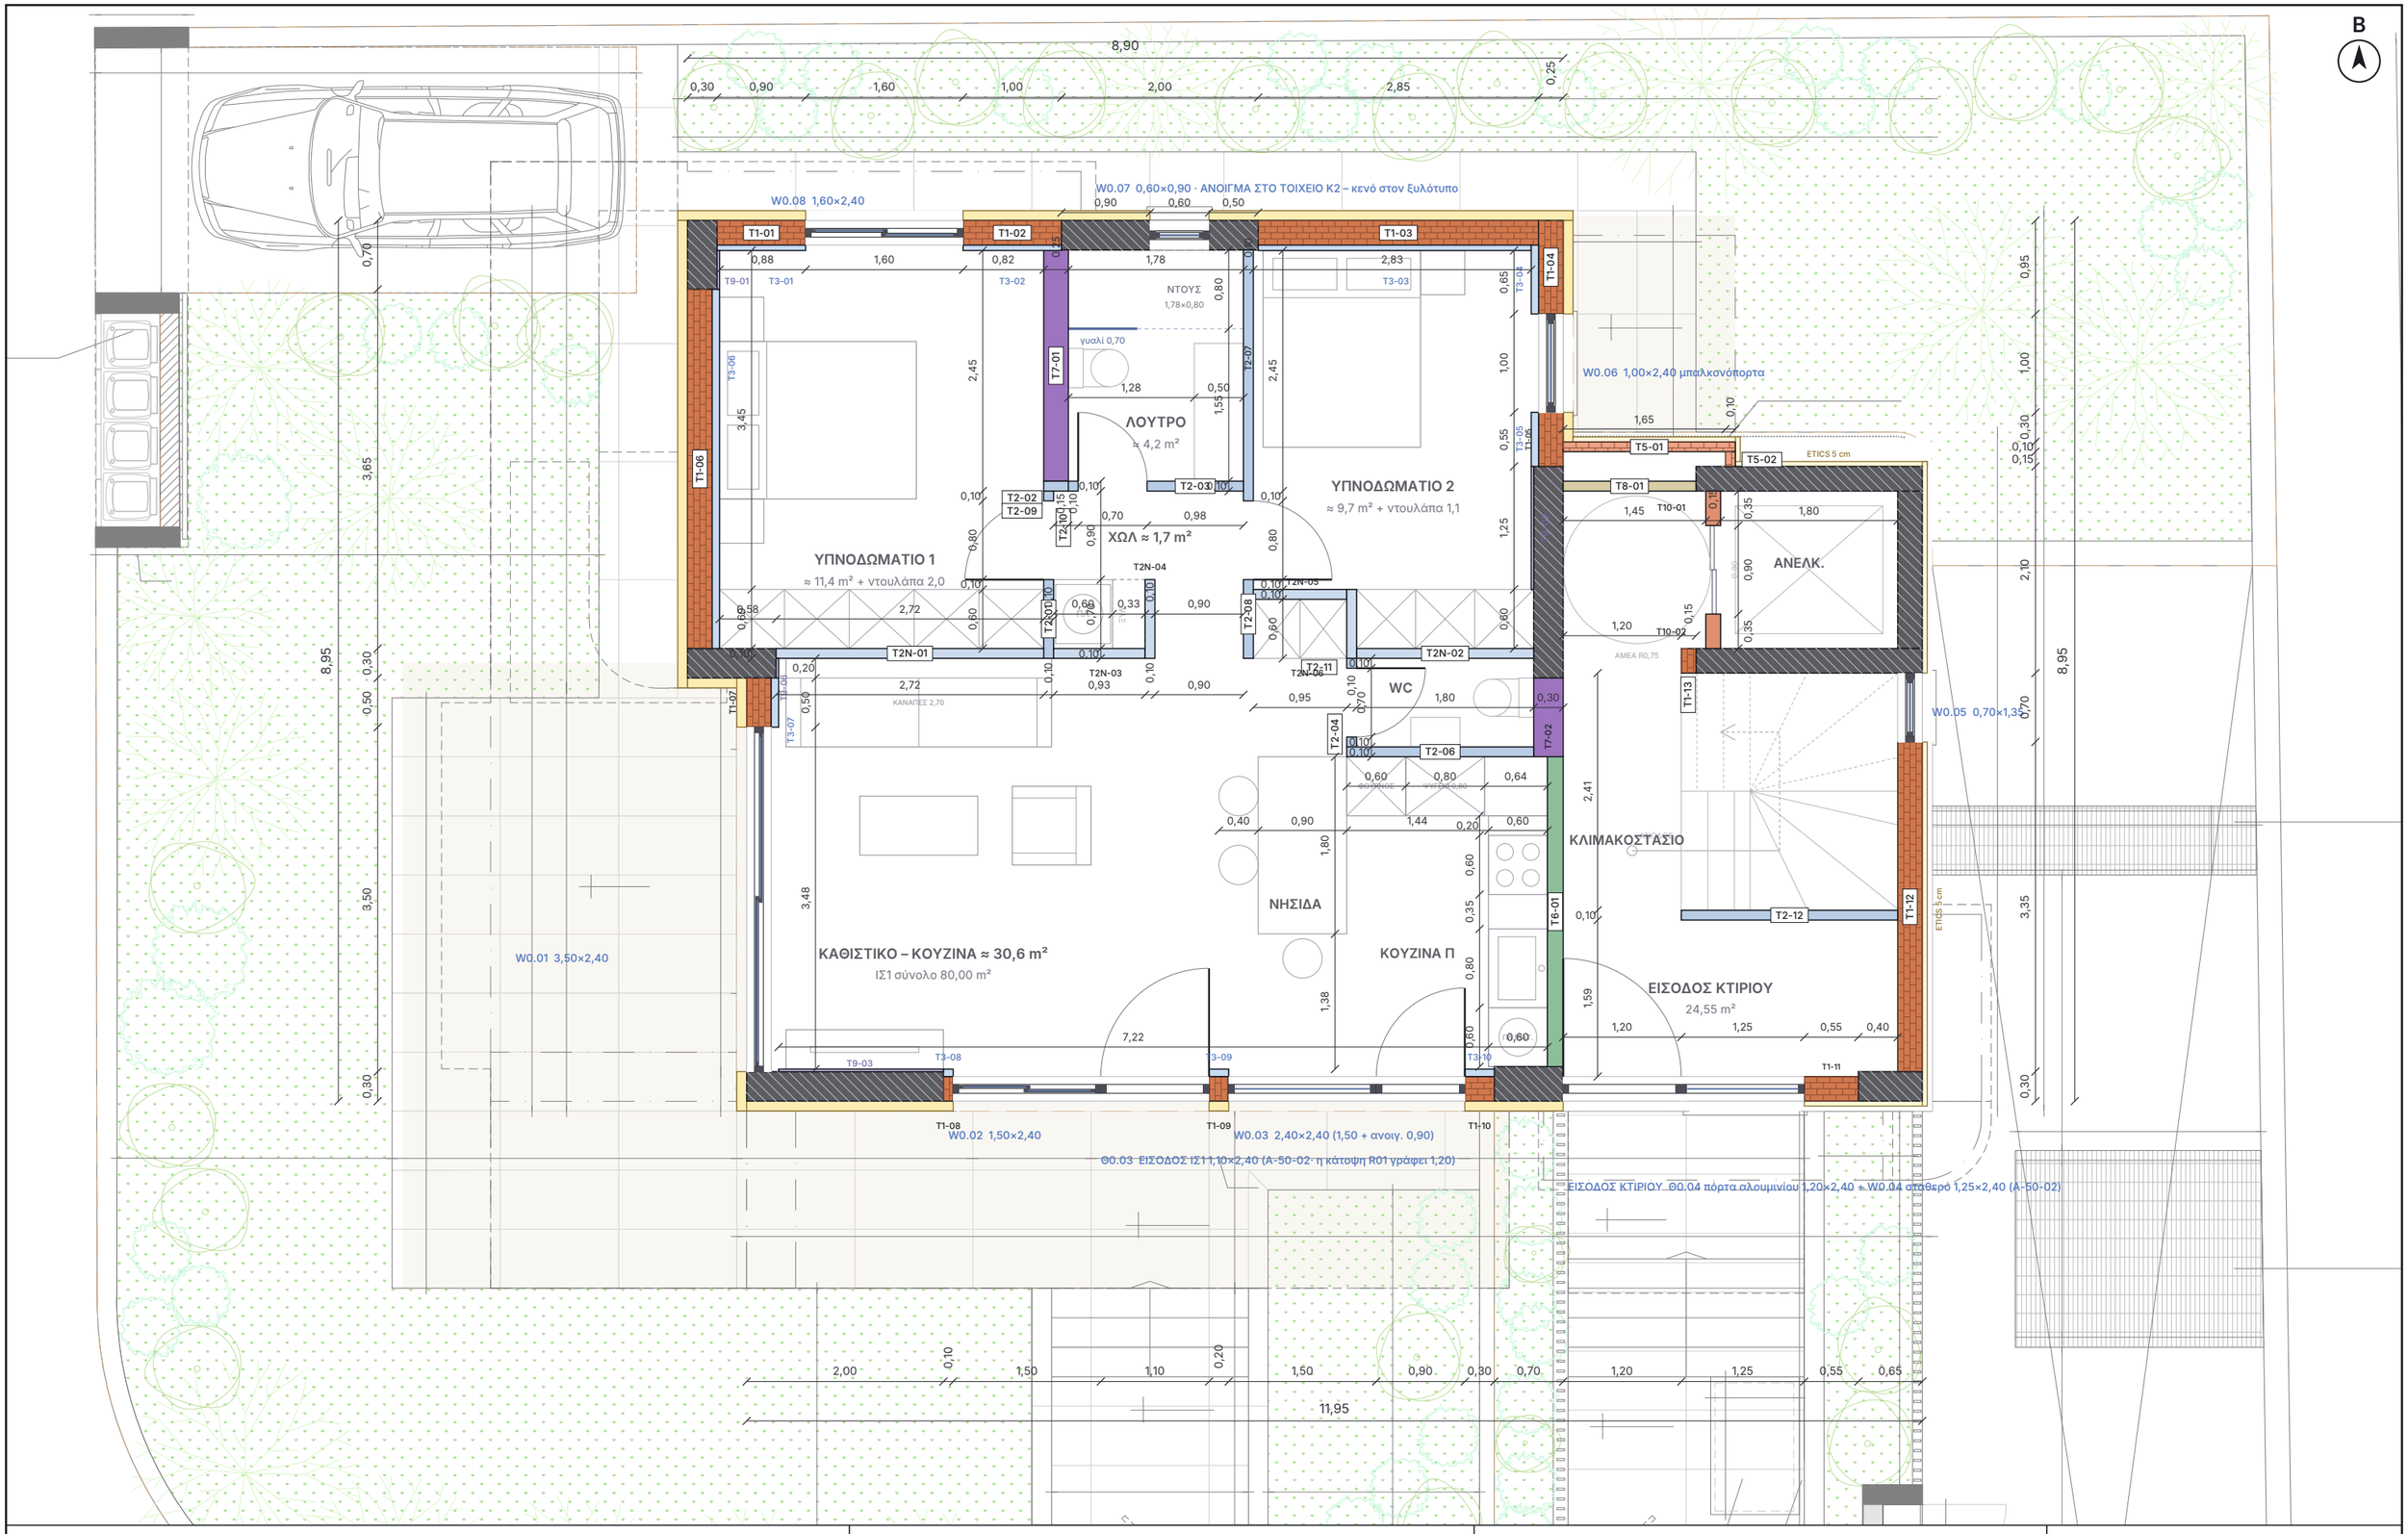


ΕΡΓΟ

ΠΕΝΤΑΟΡΟΦΟ ΚΤΗΡΙΟ ΚΑΤΟΙΚΙΩΝ – ΑΡΓΥΡΟΥΠΟΛΗ
Κωνσταντινουπόλεως 12 & Αγ. Βαρβάρας · Ο.Τ. 103-15
Εργοδότης: INTERKAT Α.Ε. · Κατασκευή: ARKAD Ι.Κ.Ε.

ΘΕΜΑ ΣΧΕΔΙΟΥ

ΚΑΤΟΨΗ ΤΟΙΧΟΠΟΙΙΩΝ – ΙΣΟΓΕΙΟΥ

Είδη τοιχοποιιών · διαστάσεις χάραξης · κουφώματα · εξώστες
ΙΣΟΓΕΙΟ – ΙΣ1

ΒΑΣΗ

Βάση: A-10-GF R01 (05/11/2026, Drive) · Σ3_ΕΦ · κανόνες B1 R20


ΑΡ. ΣΧΕΔΙΟΥ

T-01


Κλίμακα 1:60 · A3
07/11/2026 · R13


B
8,90
0,30
3,50
0,20
1,80
2,85
0,25
αρχιτεκτονικό στοιχείο – σταθερό σύστημα σκίασης
9,45
3,05
0,11
1,39
0,60
4,00
0,30
ΕΞΩΣΤΗΣ
T4-01
T4-02
T4-03
T4-04
T4-05
T4-06
T4-11
T4-12
B

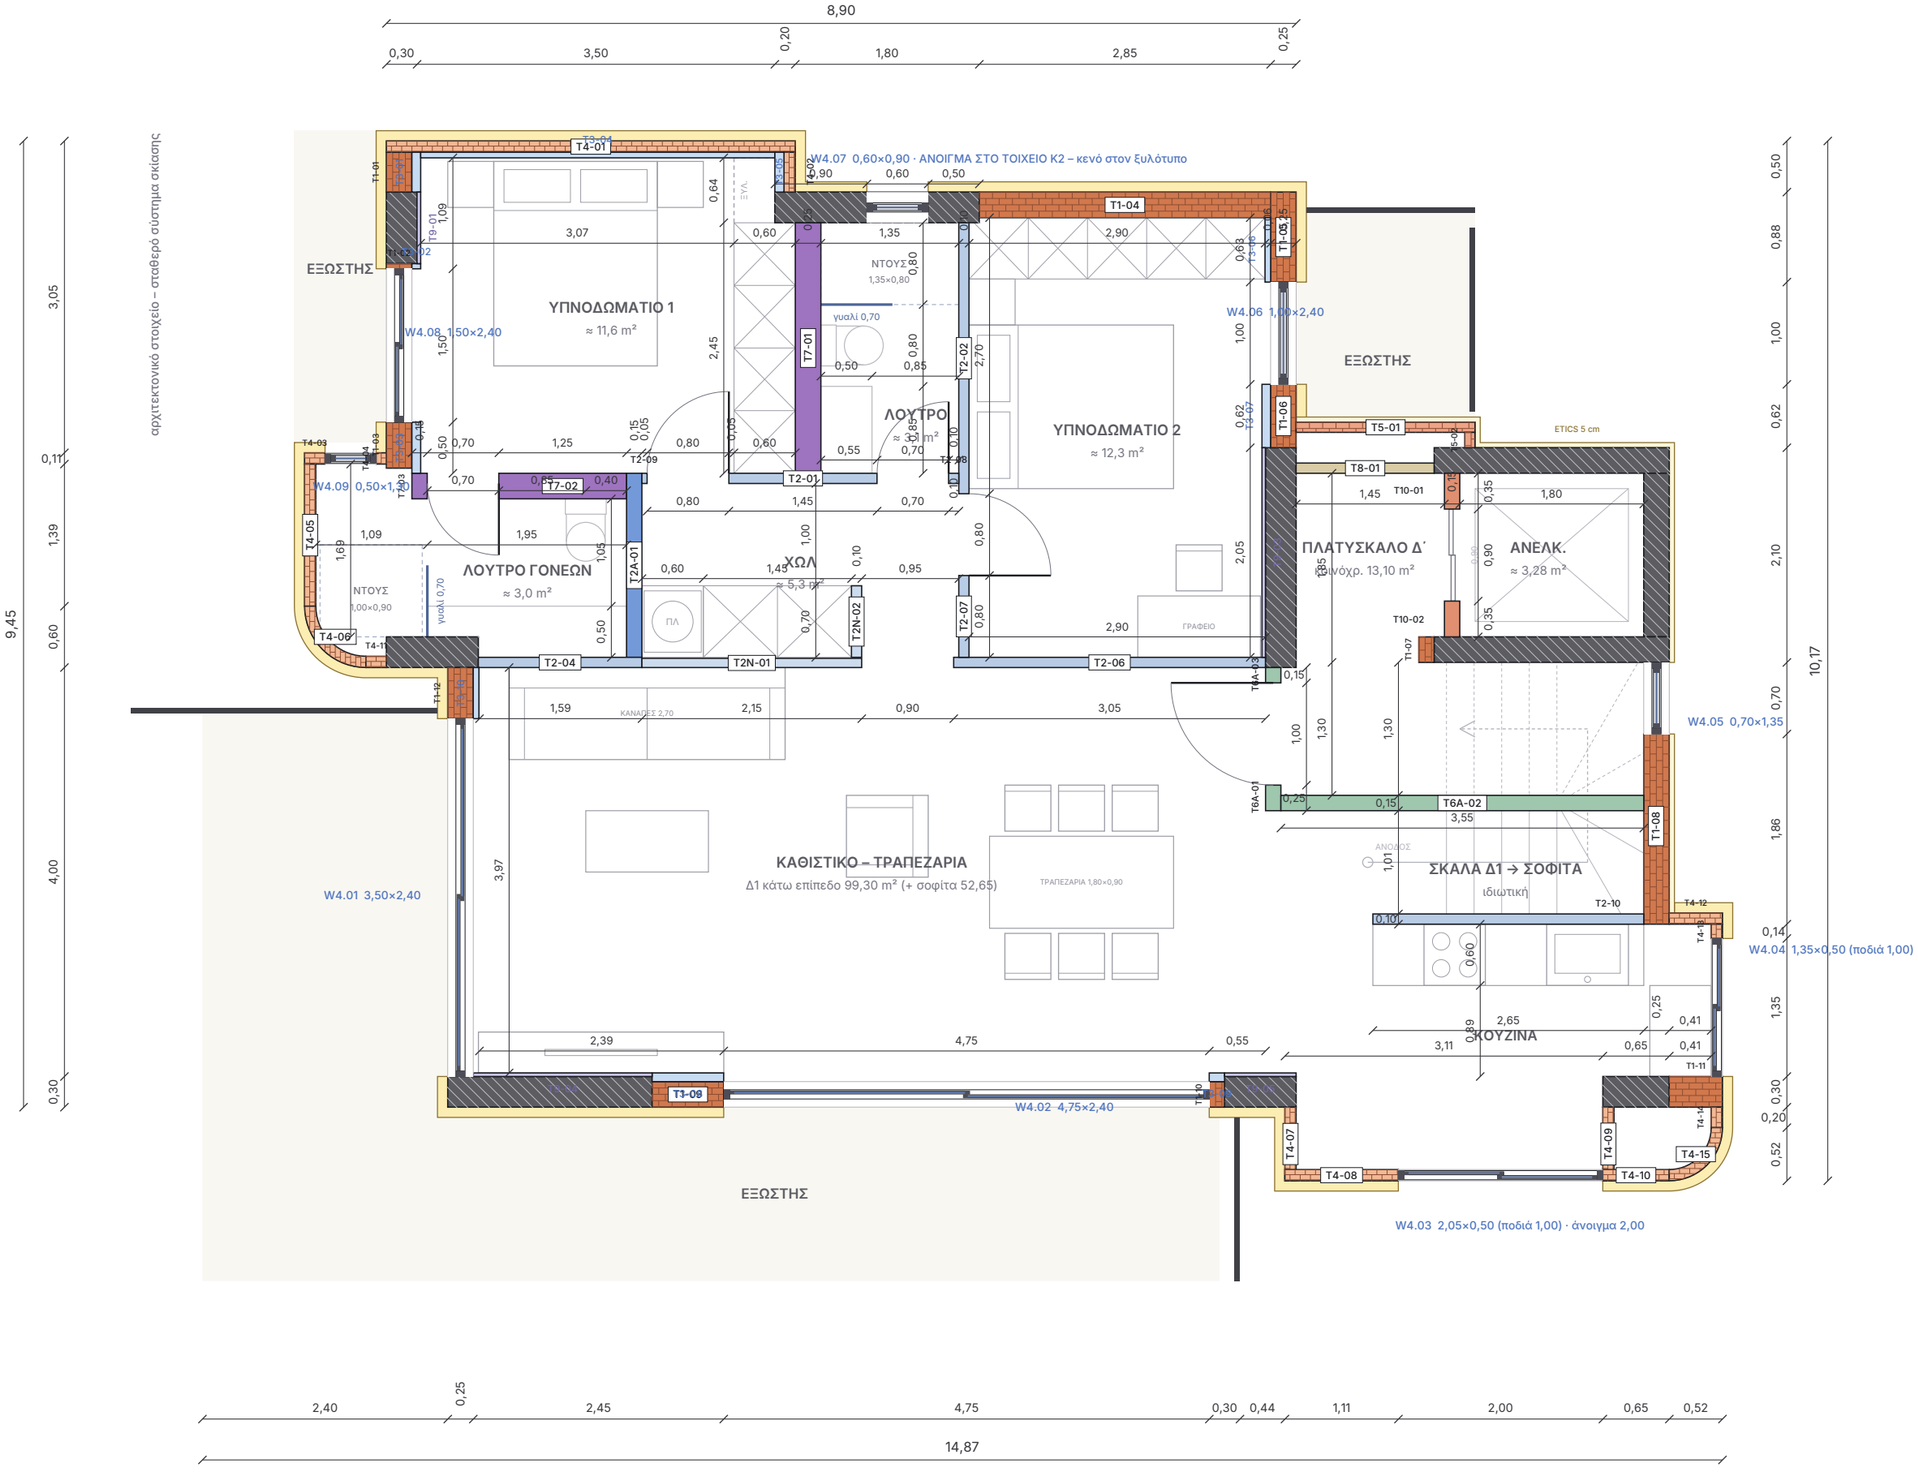

ΕΡΓΟ	ΘΕΜΑ ΣΧΕΔΙΟΥ	ΒΑΣΗ	ΑΡ. ΣΧΕΔΙΟΥ
ΠΕΝΤΑΟΡΟΦΟ ΚΤΗΡΙΟ ΚΑΤΟΙΚΙΩΝ – ΑΡΓΥΡΟΥΠΟΛΗ Κωνσταντινουπόλεως 12 & Αγ. Βαρβάρας · Ο.Τ. 103-15 Εργοδότης: INTERKAT Α.Ε. · Κατασκευή: ARKAD Ι.Κ.Ε.	**ΚΑΤΟΨΗ ΤΟΙΧΟΠΟΙΙΩΝ – Δ΄ ΟΡΟΦΟΥ** Είδη τοιχοποιιών · διαστάσεις χάραξης · κουφώματα · εξώστες Δ΄ ΟΡΟΦΟΣ – Δ1 (κάτω επίπεδο μεζονέτας)	Βάση: A-10-4F R01 (05/11/2026, Drive) · κανόνες B1 R24 / ΙΣ R13 / σοφίτας R03	**Τ-03** **Κλίμακα 1:60 · Α3** 07/11/2026 · R02

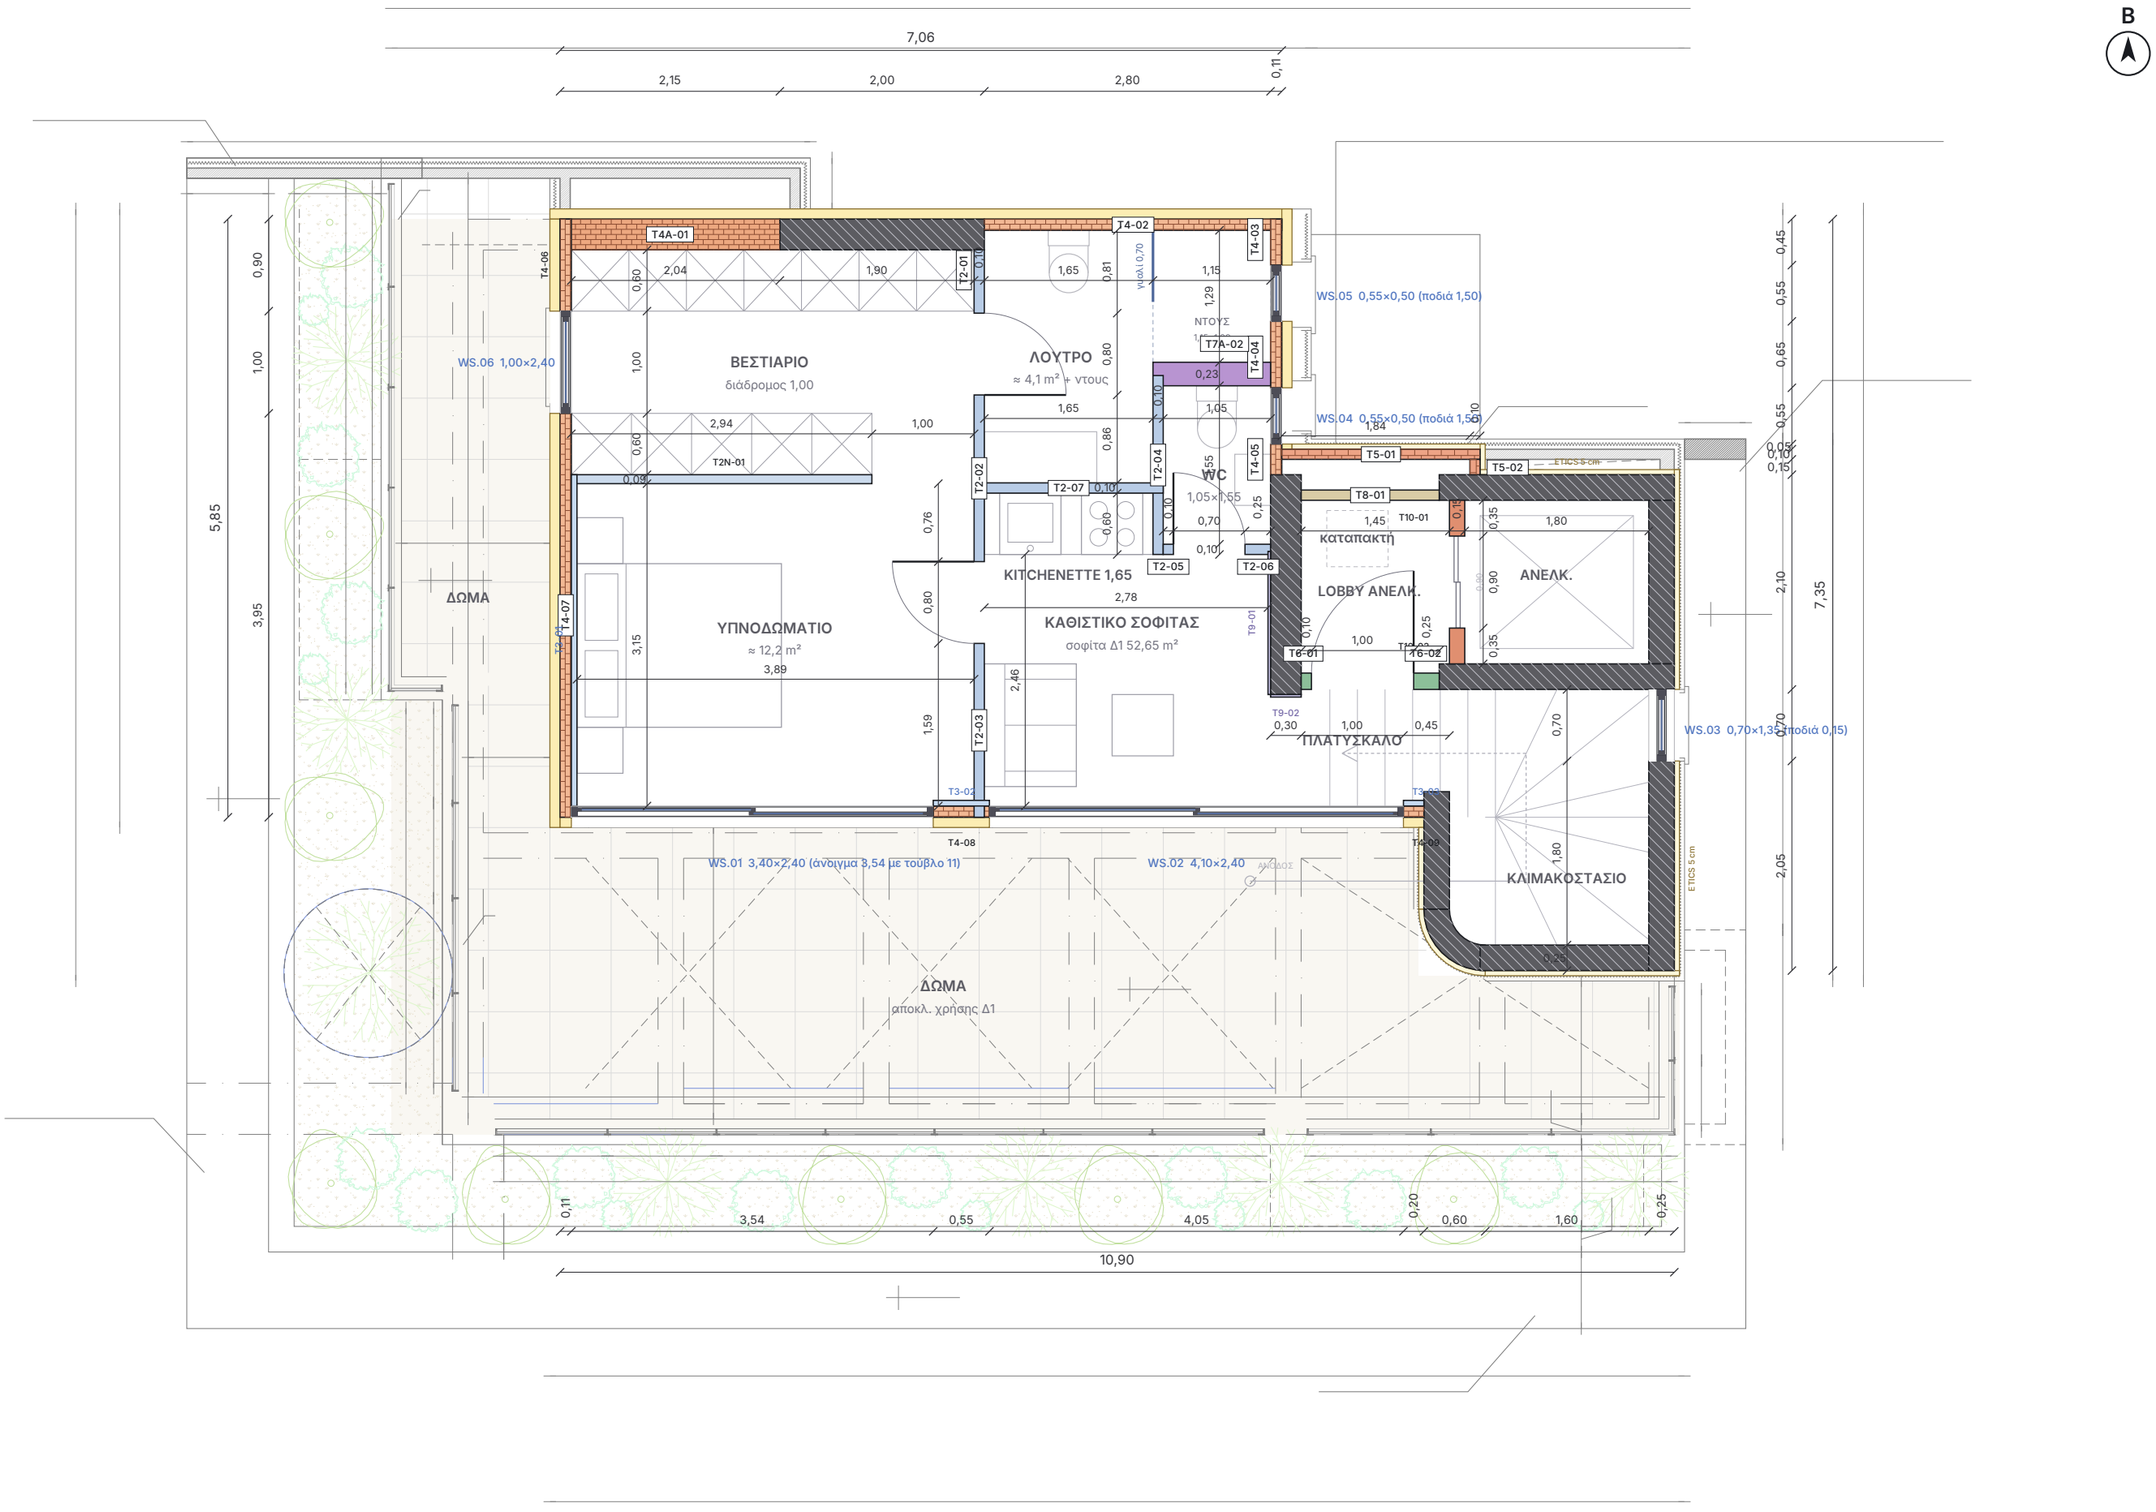


ΕΡΓΟ	ΘΕΜΑ ΣΧΕΔΙΟΥ	ΒΑΣΗ	ΑΡ. ΣΧΕΔΙΟΥ
ΠΕΝΤΑΟΡΟΦΟ ΚΤΗΡΙΟ ΚΑΤΟΙΚΙΩΝ – ΑΡΓΥΡΟΥΠΟΛΗ Κωνσταντινουπόλεως 12 & Αγ. Βαρβάρας · Ο.Τ. 103-15 Εργοδότης: INTERKAT Α.Ε. · Κατασκευή: ARKAD Ι.Κ.Ε.	**ΚΑΤΟΨΗ ΤΟΙΧΟΠΟΙΙΩΝ – ΣΟΦΙΤΑΣ** Είδη τοιχοποιιών · διαστάσεις χάραξης · κουφώματα · εξώστες ΣΟΦΙΤΑ – Δ1 (μεζονέτα)	Βάση: A-10-S R01 (05/11/2026, Drive) · Σ7_ΕΦ · κανόνες Β1 R20 / ΙΣ R11	**Τ-04** **Κλίμακα 1:60 · Α3** 07/11/2026 · R04

T1 Εξωτερική οπτοπλινθοδομή

1:4

πάχος 25 cm

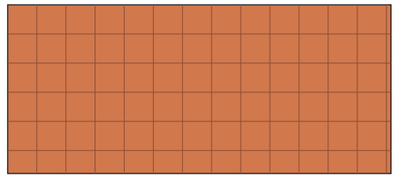


θερμομονωτικό τούβλο κάθετων οπών 25 cm · θερμοπρόσοψη 10 cm έξω · επένδυση Τ3 μέσα όπου σημειώνεται

ΙΣ1	15,35 m · 46,0 m²
Β1	9,52 m · 27,6 m²
Δ1 Δ΄	9,52 m · 27,6 m²
Σύνολο τεύχους	**34,39 m · 101,3 m²**

T4 Απλή οπτοπλινθοδομή 11

1:4

πάχος 11 cm

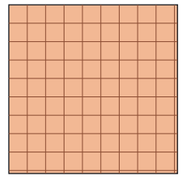


απλό τούβλο 6οπο 9 × 12 × 19 δρομικό ≈ 11 cm · σταθερή η εξωτερική παρειά · θερμοπρόσοψη 10 cm έξω · έρκερ Β1 · περίμετρος σοφίτας (Γιάννης 07/11)

Β1	11,94 m · 34,6 m²
Δ1 Δ΄	11,94 m · 34,6 m²
Δ1 σοφίτα	9,91 m · 26,3 m²
Σύνολο τεύχους	**33,78 m · 95,5 m²**

T4A Απλή οπτοπλινθοδομή 30

1:4

πάχος 30 cm

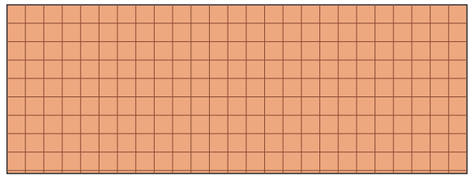


απλό τούβλο 6οπο 9 × 12 × 19 υπερμπατικό (1½ τούβλο) ≈ 30 cm · σταθερή η εξωτερική παρειά · θερμοπρόσοψη 10 cm έξω · εσωτερική παρειά περασιά με το τοιχείο Κ2 (0,80) ώστε η ντουλάπα του βεστιαρίου της σοφίτας να είναι ενιαία 0,60 χωρίς δόντι (Γιάννης 07/11, σοφίτα R03)

Δ1 σοφίτα	2,15 m · 5,7 m²
Σύνολο τεύχους	**2,15 m · 5,7 m²**

T5 Οπτοπλινθοδομή πυρήνα

1:4

πάχος 10 cm

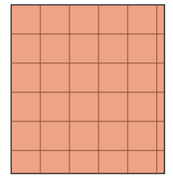


θερμομονωτικό τούβλο κάθετων οπών 10 cm · γύρω από τον πυρήνα (ανελκυστήρας – ηλεκτροστάσιο)

ΙΣ1	1,90 m · 5,7 m²
Β1	1,90 m · 5,5 m²
Δ1 Δ΄	1,90 m · 5,5 m²
Δ1 σοφίτα	2,09 m · 5,5 m²
Σύνολο τεύχους	**7,79 m · 22,3 m²**

T10 Μέτωπο ανελκυστήρα

1:4

πάχος 15 cm

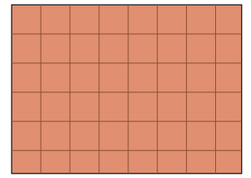


θερμομονωτικό τούβλο κάθετων οπών 15 cm · μέτωπο φρεατίου εκατέρωθεν της πόρτας 0,90 · στην ΕΣΩΤΕΡΙΚΗ παρειά της δοκού μετώπου του φρεατίου (Δ5.1 25/40 στον Σ3, x 11,05–11,30) → x 11,15–11,30, σε όλους τους ορόφους (R21 / ισόγειο R09, Γιάννης 07/11) · θέση πόρτας προς επιβεβαίωση από τον προμηθευτή

ΙΣ1	0,70 m · 2,1 m²
Β1	0,70 m · 2,0 m²
Δ1 Δ΄	0,70 m · 2,0 m²
Δ1 σοφίτα	0,70 m · 1,9 m²
Σύνολο τεύχους	**2,80 m · 8,0 m²**

T3 Επένδυση τοίχου

1:4

πάχος 5,5 cm

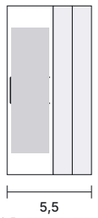

σκελετός 30 · 2 × γυψοσανίδα 12,5 · στις εσωτερικές παρειές των Τ1 – ΟΧΙ όπου πλακάκι ή ντουλάπα, ΟΧΙ στα έρκερ

ΙΣ1	10,68 m · 32,0 m²
Β1	7,43 m · 21,5 m²
Δ1 Δ΄	7,43 m · 21,5 m²
Δ1 σοφίτα	3,99 m · 10,6 m²
Σύνολο τεύχους	**29,53 m · 85,7 m²**

T9 Επένδυση υποστυλώματος

1:4

πάχος 2,5 cm




κόλλα + 1 × γυψοσανίδα 12,5 (ένα φύλλο) · στις παρειές υποστυλωμάτων μέσα στα διαμερίσματα – ΟΧΙ όπου πλακάκι ή ντουλάπα

ΙΣ1	3,52 m · 10,6 m²
Β1	5,20 m · 15,1 m²
Δ1 Δ΄	5,20 m · 15,1 m²
Δ1 σοφίτα	1,70 m · 4,5 m²
Σύνολο τεύχους	**15,62 m · 45,2 m²**

T2 Χώρισμα γυψοσανίδας

1:4

πάχος 10 cm

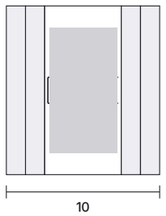


2 × γυψοσανίδα 12,5 · σκελετός CW 50 · 2 × γυψοσανίδα 12,5 · εσωτερικά χωρίσματα · ανθυγρή γυψοσανίδα στην πλευρά των λουτρών · ανοίγματα πορτών με ορθοστάτες UA 50 (2 mm)

ΙΣ1	9,88 m · 29,6 m²
Β1	9,75 m · 28,3 m²
Δ1 Δ΄	12,40 m · 36,0 m²
Δ1 σοφίτα	7,90 m · 20,9 m²
Σύνολο τεύχους	**39,93 m · 114,8 m²**

T2N Χώρισμα γυψ. – πλευρά ντουλάπας

1:4

πάχος 8,75 cm

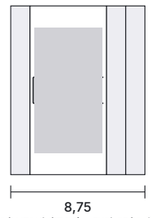


1 × γυψοσανίδα 12,5 (πλευρά ντουλάπας) · σκελετός CW 50 · 2 × γυψοσανίδα 12,5 · όπου η μία παρειά βλέπει σε ντουλάπα: ένα φύλλο αρκεί (κανόνας R15)

ΙΣ1	7,90 m · 23,7 m²
Β1	2,85 m · 8,3 m²
Δ1 Δ΄	2,85 m · 8,3 m²
Δ1 σοφίτα	2,94 m · 7,8 m²
Σύνολο τεύχους	**16,54 m · 48,0 m²**

T2A Χώρισμα γυψοσανίδας 15

1:4

πάχος 15 cm

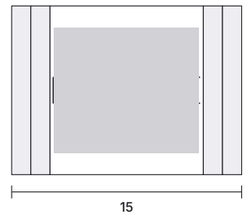


2 × γυψοσανίδα 12,5 · σκελετός CW 100 + πετροβάμβακας · 2 × γυψοσανίδα 12,5 · λουτρό γονέων / χωλ · υπνοδωμάτια · ανοίγματα πορτών με ορθοστάτες UA 100 (2 mm)

Β1	1,80 m · 5,2 m²
Δ1 Δ΄	1,80 m · 5,2 m²
Σύνολο τεύχους	**3,60 m · 10,4 m²**

T7 Τοίχος λεκάνης WC

1:4

πάχος 25 cm

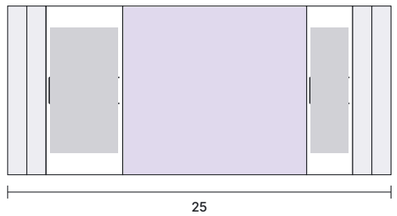


2 × γυψοσανίδα 12,5 · σκελετός CW 50 · κενό 12 cm (καζανάκι γυψοσανίδας στον σκελετό + κατακόρυφη στήλη Ø110, έξοδος Ø90) · σκελετός CW 30 · 2 × γυψοσανίδα 12,5 · ΟΛΟΙ οι τοίχοι λεκανών · ανθυγρή προς το λουτρό · στην πλευρά ντουλάπας 1 φύλλο · ανοίγματα πορτών με ορθοστάτες UA 50 (2 mm)

ΙΣ1	3,15 m · 9,4 m²
Β1	3,95 m · 11,5 m²
Δ1 Δ΄	3,95 m · 11,5 m²
Σύνολο τεύχους	**11,05 m · 32,4 m²**

T7A Τοίχος λεκάνης 23 – κενό 10

1:4

πάχος 23 cm

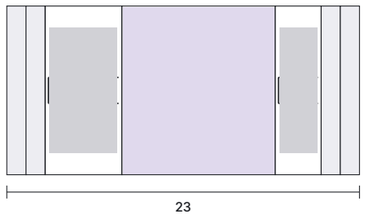


2 × γυψοσανίδα 12,5 · σκελετός CW 50 (καζανάκι γυψοσανίδας) · κενό 10 cm · σκελετός CW 30 · 2 × γυψοσανίδα 12,5 = 23 cm · όπως ο Τ7 με κενό 10 αντί 12 (σοφίτα: χωρίς κατακόρυφη στήλη από πάνω) · ανθυγρή προς λουτρό / WC · ανοίγματα με UA 50

Δ1 σοφίτα	1,15 m · 3,0 m²
Σύνολο τεύχους	**1,15 m · 3,0 m²**

T6 Τοίχος κλιμακοστασίου – διπλός σκελετός

1:4

πάχος 16 cm

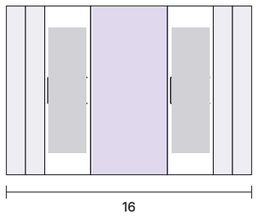


2 × γυψοσανίδα 12,5 πυράντοχη · σκελετός CW 30 · κενό 5 cm · σκελετός CW 30 · 2 × γυψοσανίδα 12,5 πυράντοχη = 16 cm · ισόγειο: Τ6-01 προς το lobby (R09, Γιάννης) · χωρίς πόρτα

ΙΣ1	3,15 m · 9,4 m²
Δ1 σοφίτα	0,41 m · 1,1 m²
Σύνολο τεύχους	**3,56 m · 10,5 m²**

T6A Τοίχος κλιμακοστασίου 15

1:4

πάχος 15 cm

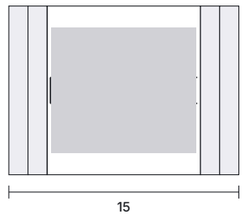


2 × γυψοσανίδα 12,5 πυράντοχη · σκελετός CW 100 + πετροβάμβακας · 2 × γυψοσανίδα 12,5 πυράντοχη = 15 cm · Β1: διαμέρισμα προς κλιμακοστάσιο (Τ6Α-01 / Τ6Α-03 με την πόρτα εισόδου – ορθοστάτες UA 100 + ψευτόκασα) και μέτωπο σκάλας Τ6Α-02 · (ως R21 ονομαζόταν Τ6)

Β1	5,06 m · 14,7 m²
Δ1 Δ΄	3,95 m · 11,5 m²
Σύνολο τεύχους	**9,01 m · 26,1 m²**

T8 Τοίχος shaft

1:4

πάχος 10 cm

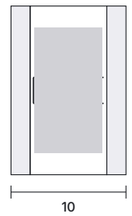

πλαίσιο + ανοιγόμενα φύλλα γυψοσανίδας · μέτωπο shaft ηλεκτρολογικών

ΙΣ1	1,35 m · 4,1 m²
Β1	1,35 m · 3,9 m²
Δ1 Δ΄	1,35 m · 3,9 m²
Δ1 σοφίτα	1,35 m · 3,6 m²
Σύνολο τεύχους	**5,40 m · 15,5 m²**

Επιφάνειες ενδεικτικές: μήκος × ύψος ορόφου (ισόγειο 3,00 · όροφοι 2,90 · σοφίτα 2,65) – οι τοίχοι ορίζονται μεταξύ ανοιγμάτων, χωρίς αφαίρεση κασών. Τ3 = επένδυση στην εσωτερική παρειά των Τ1 · Τ9 = περίμετρος υποστυλώματος × ύψος. Το Β1 μετράται μία φορά (τυπικός όροφος Α΄/Β΄/Γ΄ – ×3 για όλο το κτήριο).

ΕΡΓΟ

ΠΕΝΤΑΟΡΟΦΟ ΚΤΗΡΙΟ ΚΑΤΟΙΚΙΩΝ – ΑΡΓΥΡΟΥΠΟΛΗ
Κωνσταντινουπόλεως 12 & Αγ. Βαρβάρας · Ο.Τ. 103-15
Εργοδότης: INTERKAT Α.Ε. · Κατασκευή: ARKAD Ι.Κ.Ε.

ΘΕΜΑ ΣΧΕΔΙΟΥ

ΕΙΔΗ ΤΟΙΧΟΠΟΙΙΩΝ – ΟΛΟΙ ΟΙ ΟΡΟΦΟΙ
Είδη τοιχοποιιών · ΙΣ1 · Β1 · Δ1 Δ΄ · Δ1 ΣΟΦΊΤΑ
τομές 1:4 · μήκη – εμβαδά ανά είδος και όροφο

ΒΑΣΗ

Βάση: κατόψεις Τ-01…Τ-04

ΑΡ. ΣΧΕΔΙΟΥ

Τ-05
Κλίμακα 1:4 · Α3
07/11/2026 · ΙΣ R13 · Β1 R25 · Δ R02 · ΣΟΦ R04

ΠΡΟΜΕΤΡΗΣΗ ΤΟΙΧΟΠΟΙΙΩΝ – ΤΕΤΡΑΓΩΝΙΚΑ ΑΝΑ ΤΥΠΟΛΟΓΙΑ ΚΑΙ ΑΝΑ ΟΡΟΦΟ

ΙΣΟΓΕΙΟ – ΙΣ1 · R13

H = 3,00 m · μήκη στον άξονα, χωρίς αφαίρεση κουφωμάτων

	Τύπος	Περιγραφή	Πάχος cm	Τοίχοι	Μήκος m	m²
ΤΟΥΒΛΑ						
	T1	Εξωτερική οπτοπλ…	25	13	15,35	46,0
	T5	Οπτοπλινθοδομή…	10	2	1,90	5,7
	T10	Μέτωπο ανελκυστ…	15	2	0,70	2,1
	Σύνολο τουβλα					**53,9 m²**
ΧΩΡΙΣΜΑΤΑ ΓΥΨΟΣΑΝΙΔΑΣ						
	T2	Χώρισμα γυψοσα…	10	11	9,88	29,6
	T2N	Χώρισμα γυψ. – π…	8,8	6	7,90	23,7
	T7	Τοίχος λεκάνης…	25	2	3,15	9,4
	T6	Τοίχος κλιμακοστ…	16	1	3,15	9,4
	T8	Τοίχος shaft	10	1	1,35	4,1
	Σύνολο χωρισματα γυψοσανιδας					**76,3 m²**
ΕΠΕΝΔΥΣΕΙΣ						
	T3	Επένδυση τοίχου	5,5	10	10,68	32,0
	T9	Επένδυση υποστυ…	2,5	4	3,52	10,6
	Σύνολο επενδυσεις					**42,6 m²**
	ΣΥΝΟΛΟ ΤΟΙΧΟΠΟΙΙΩΝ ΙΣ1					**172,7 m²**

ΘΕΡΜΟΠΡΟΣΟΨΗ (ETICS) – ΙΣΟΓΕΙΟΥ

10 cm διαμέρισμα · 5 cm πυρήνας · ύψος 3,20 m (με μετώπη πλάκας)

Ζώνη	Μήκος m	Μικτά m²	Κουφώματα	Λαμπάδες	Καθαρά m²
ETICS 10 cm – διαμέρισμα	29,40	94,1	−27,2	+5,9	72,8
ETICS 5 cm – πυρήνας	14,15	45,3	−6,8	+2,0	40,5
Σύνολο ETICS ΙΣ1					113,3 m²

Α΄ · Β΄ · Γ΄ ΟΡΟΦΟΣ – Β1 (τυπικός όροφος) · R25

H = 2,90 m · μήκη στον άξονα, χωρίς αφαίρεση κουφωμάτων

	Τύπος	Περιγραφή	Πάχος cm	Τοίχοι	Μήκος m	m²
ΤΟΥΒΛΑ						
	T1	Εξωτερική οπτοπλ…	25	12	9,52	27,6
	T4	Απλή οπτοπλινθο…	11	15	11,94	34,6
	T5	Οπτοπλινθοδομή…	10	2	1,90	5,5
	T10	Μέτωπο ανελκυστ…	15	2	0,70	2,0
	Σύνολο τουβλα					**69,8 m²**
ΧΩΡΙΣΜΑΤΑ ΓΥΨΟΣΑΝΙΔΑΣ						
	T2	Χώρισμα γυψοσα…	10	7	9,75	28,3
	T2N	Χώρισμα γυψ. – π…	8,8	2	2,85	8,3
	T2A	Χώρισμα γυψοσα…	15	1	1,80	5,2
	T7	Τοίχος λεκάνης…	25	3	3,95	11,5
	T6A	Τοίχος κλιμακοστ…	15	3	5,06	14,7
	T8	Τοίχος shaft	10	1	1,35	3,9
	Σύνολο χωρισματα γυψοσανιδας					**71,8 m²**
ΕΠΕΝΔΥΣΕΙΣ						
	T3	Επένδυση τοίχου	5,5	10	7,43	21,5
	T9	Επένδυση υποστυ…	2,5	4	5,20	15,1
	Σύνολο επενδυσεις					**36,6 m²**
	ΣΥΝΟΛΟ ΤΟΙΧΟΠΟΙΙΩΝ Β1					**178,2 m²**

ΘΕΡΜΟΠΡΟΣΟΨΗ (ETICS) – Α΄·Β΄·Γ΄ ΟΡΟΦΟΥ

10 cm διαμέρισμα · 5 cm πυρήνας · ύψος 3,10 m (με μετώπη πλάκας)

Ζώνη	Μήκος m	Μικτά m²	Κουφώματα	Λαμπάδες	Καθαρά m²
ETICS 10 cm – διαμέρισμα	39,56	122,6	−28,7	+6,2	100,1
ETICS 5 cm – πυρήνας	8,50	26,4	−0,9	+0,5	25,9
Σύνολο ETICS Β1					126,0 m²

Δ΄ ΟΡΟΦΟΣ – Δ1 (κάτω επίπεδο μεζονέτας) · R02

H = 2,90 m · μήκη στον άξονα, χωρίς αφαίρεση κουφωμάτων

	Τύπος	Περιγραφή	Πάχος cm	Τοίχοι	Μήκος m	m²
ΤΟΥΒΛΑ						
	T1	Εξωτερική οπτοπλ…	25	12	9,52	27,6
	T4	Απλή οπτοπλινθο…	11	15	11,94	34,6
	T5	Οπτοπλινθοδομή…	10	2	1,90	5,5
	T10	Μέτωπο ανελκυστ…	15	2	0,70	2,0
	Σύνολο τουβλα					**69,8 m²**
ΧΩΡΙΣΜΑΤΑ ΓΥΨΟΣΑΝΙΔΑΣ						
	T2	Χώρισμα γυψοσα…	10	8	12,40	36,0
	T2N	Χώρισμα γυψ. – π…	8,8	2	2,85	8,3
	T2A	Χώρισμα γυψοσα…	15	1	1,80	5,2
	T7	Τοίχος λεκάνης…	25	3	3,95	11,5
	T6A	Τοίχος κλιμακοστ…	15	3	3,95	11,5
	T8	Τοίχος shaft	10	1	1,35	3,9
	Σύνολο χωρισματα γυψοσανιδας					**76,3 m²**
ΕΠΕΝΔΥΣΕΙΣ						
	T3	Επένδυση τοίχου	5,5	10	7,43	21,5
	T9	Επένδυση υποστυ…	2,5	4	5,20	15,1
	Σύνολο επενδυσεις					**36,6 m²**
	ΣΥΝΟΛΟ ΤΟΙΧΟΠΟΙΙΩΝ Δ1 Δ΄					**182,7 m²**

ΘΕΡΜΟΠΡΟΣΟΨΗ (ETICS) – Δ΄ ΟΡΟΦΟΥ

10 cm διαμέρισμα · 5 cm πυρήνας · ύψος 3,10 m (με μετώπη πλάκας)

Ζώνη	Μήκος m	Μικτά m²	Κουφώματα	Λαμπάδες	Καθαρά m²
ETICS 10 cm – διαμέρισμα	39,56	122,6	−28,7	+6,2	100,1
ETICS 5 cm – πυρήνας	8,50	26,4	−0,9	+0,5	25,9
Σύνολο ETICS Δ1 Δ΄					126,0 m²

ΣΟΦΙΤΑ – Δ1 (μεζονέτα) · R04

H = 2,65 m · μήκη στον άξονα, χωρίς αφαίρεση κουφωμάτων

	Τύπος	Περιγραφή	Πάχος cm	Τοίχοι	Μήκος m	m²
ΤΟΥΒΛΑ						
	T4	Απλή οπτοπλινθο…	11	8	9,91	26,3
	T4A	Απλή οπτοπλινθο…	30	1	2,15	5,7
	T5	Οπτοπλινθοδομή…	10	2	2,09	5,5
	T10	Μέτωπο ανελκυστ…	15	2	0,70	1,9
	Σύνολο τουβλα					**39,4 m²**
ΧΩΡΙΣΜΑΤΑ ΓΥΨΟΣΑΝΙΔΑΣ						
	T2	Χώρισμα γυψοσα…	10	7	7,90	20,9
	T2N	Χώρισμα γυψ. – π…	8,8	1	2,94	7,8
	T7A	Τοίχος λεκάνης 2…	23	1	1,15	3,0
	T6	Τοίχος κλιμακοστ…	16	2	0,41	1,1
	T8	Τοίχος shaft	10	1	1,35	3,6
	Σύνολο χωρισματα γυψοσανιδας					**36,4 m²**
ΕΠΕΝΔΥΣΕΙΣ						
	T3	Επένδυση τοίχου	5,5	3	3,99	10,6
	T9	Επένδυση υποστυ…	2,5	2	1,70	4,5
	Σύνολο επενδυσεις					**15,1 m²**
	ΣΥΝΟΛΟ ΤΟΙΧΟΠΟΙΙΩΝ Δ1 σοφίτα					**90,9 m²**

ΘΕΡΜΟΠΡΟΣΟΨΗ (ETICS) – ΣΟΦΙΤΑΣ

10 cm διαμέρισμα · 5 cm πυρήνας · ύψος 2,85 m (με μετώπη πλάκας)

Ζώνη	Μήκος m	Μικτά m²	Κουφώματα	Λαμπάδες	Καθαρά m²
ETICS 10 cm – διαμέρισμα	24,01	68,4	−21,2	+3,9	51,2
ETICS 5 cm – πυρήνας	12,77	36,4	−0,9	+0,5	35,9
Σύνολο ETICS Δ1 σοφίτα					87,1 m²

ΣΥΝΟΛΑ ΤΕΥΧΟΥΣ ΙΣ1: τοιχοποιίες 172,7 m² · ETICS 113,3 m² Β1: τοιχοποιίες 178,2 m² · ETICS 126,0 m² Δ1 Δ΄: τοιχοποιίες 182,7 m² · ETICS 126,0 m² Δ1 σοφίτα: τοιχοποιίες 90,9 m² · ETICS 87,1 m²

ΟΛΟΙ ΟΙ ΟΡΟΦΟΙ ΤΟΥ ΤΕΥΧΟΥΣ: τοιχοποιίες 624,4 m² · ETICS 452,4 m²

ΕΡΓΟ

ΠΕΝΤΑΟΡΟΦΟ ΚΤΗΡΙΟ ΚΑΤΟΙΚΙΩΝ – ΑΡΓΥΡΟΥΠΟΛΗ
Κωνσταντινουπόλεως 12 & Αγ. Βαρβάρας · Ο.Τ. 103-15
Εργοδότης: INTERKAT Α.Ε. · Κατασκευή: ARKAD Ι.Κ.Ε.

ΘΕΜΑ ΣΧΕΔΙΟΥ

ΠΡΟΜΕΤΡΗΣΗ – ΙΣ1 · Β1 · Δ1 Δ΄ · Δ1 ΣΟΦΊΤΑ
Τετραγωνικά ανά τυπολογία τοίχου, χωριστά ανά όροφο
θερμοπρόσοψη 10 / 5 cm

ΒΑΣΗ

Βάση: κατόψεις Τ-01…Τ-04 · είδη Τ-05

ΑΡ. ΣΧΕΔΙΟΥ

Τ-06
— · Α3
07/11/2026 · ΙΣ R13 · Β1 R25 · Δ R02 · ΣΟΦ R04