ΚΩΝΣΤΑΝΤΙΝΟΥΠΟΛΕΟΣ 12 & ΑΓ. ΒΑΡΒΑΡΑΣ, ΑΡΓΥΡΟΥΠΟΛΗ – ARKAD I.K.E.
Ξυλότυπος εργαταξίου – χωρίς οπλισμούς

ΞΥΛΟΤΥΠΟΣ ΟΡΟΦΗΣ ΥΠΟΓΕΙΟΥ

Σ2

ΣΤΑΘΜΗ ΑΝΩ ΠΛΑΚΑΣ
±0,00 / +0,30
ΚΛΙΜΑΚΑ 1:50 A2 · 100 %
0 — 1 m

K1 30/70 υποστύλωμα / τοιχείο (cm)
Δ1.1 30/40 δοκός: πλάτος / ύψος (το ύψος μαζί με την πλάκα)
L=3.50 καθαρό μήκος δοκού, παρειά με παρειά
Π3 h=15 πλάκα – πάχος (cm)
+0,30 στάθμη άνω μπετού (m)
μπλε τομές επί τόπου / φυτευτά και οι στάθμες τους
γέμισμα έως τη στάθμη +0,30 (πλάκα ±0,00)
ΜΠΑΖΩΜΑ («φελιζόλη» του μελετητή) κάτω από πλάκα οπή πλάκας 20 × 20 (αποχέτευση / υδρορροή)

Διαστάσεις σε m, από γωνία / παρειά κολόνας σε γωνία κολόνας. Οι αλυσίδες παρειών μετρήθηκαν από τη γεωμετρία του σχεδίου, οι υπόλοιπες είναι του μελετητή.


ΟΠΕΣ ΠΛΑΚΑΣ – ΚΟΥΤΙ 20 × 20
Θέση σε cm ως την ΑΚΜΗ του κουτιού, από παρειές σκυροδέματος.

- **H1** **ΑΠ1 Φ100** δυτ. ακμή 15 δυτ. της Δ παρ. K2 · 5 νότια της N παρ. K2
- **H2** **ΑΠ3 Φ100** δυτ. ακμή 15 δυτ. της Δ παρ. K2 · 1,85 m νότια της N παρ. K2
- **H3** **WC + κουζίνα ΙΣ1 Φ100** κολλητά στη Δ παρ. Δ9.1 · 50 νότια της N παρ. K3
- **H4** **ΑΠ4 Φ75** ανατ. ακμή στην ευθεία της Δ παρ. K7 · κολλητά στη Β παρ. δοκού K8–K7
- **H5** **ΑΠ2 Φ100** 10 ανατ. της Α παρ. Δ9.5 · 2,35 m βόρ. της Β παρ. K3
- **X1** Έξοδος συλλεκτήρα Φ125: χτύπιο Ø200 στο ΝΟΤΙΟ ΤΟΙΧΕΙΟ του υπογείου (όχι στην πλάκα) · άξονας 50 cm ανατ. της εσωτ. παρειάς του δυτικού τοιχείου · άντυγα −0,86

Τεύχος αποχετεύσεων R19, φύλλο ΑΠ-11. Καμία οπή σε δοκό, καμία αναμονή σε στηθαίο.


ΣΗΜΕΙΩΣΕΙΣ
· Β και Α πλευρά λοξές (όριο οικοπέδου): ισχύουν οι διαστάσεις του μελετητή κατά μήκος τους.

Βάση: Σ2_ΕΦ.pdf – ξυλότυπος οροφής υπογείου, Γ. Κόγιας (Drive 19/10/2026).
Οπλισμοί ΜΟΝΟ από το σχέδιο του μελετητή.
Έκδοση R03 – 10/11/2026

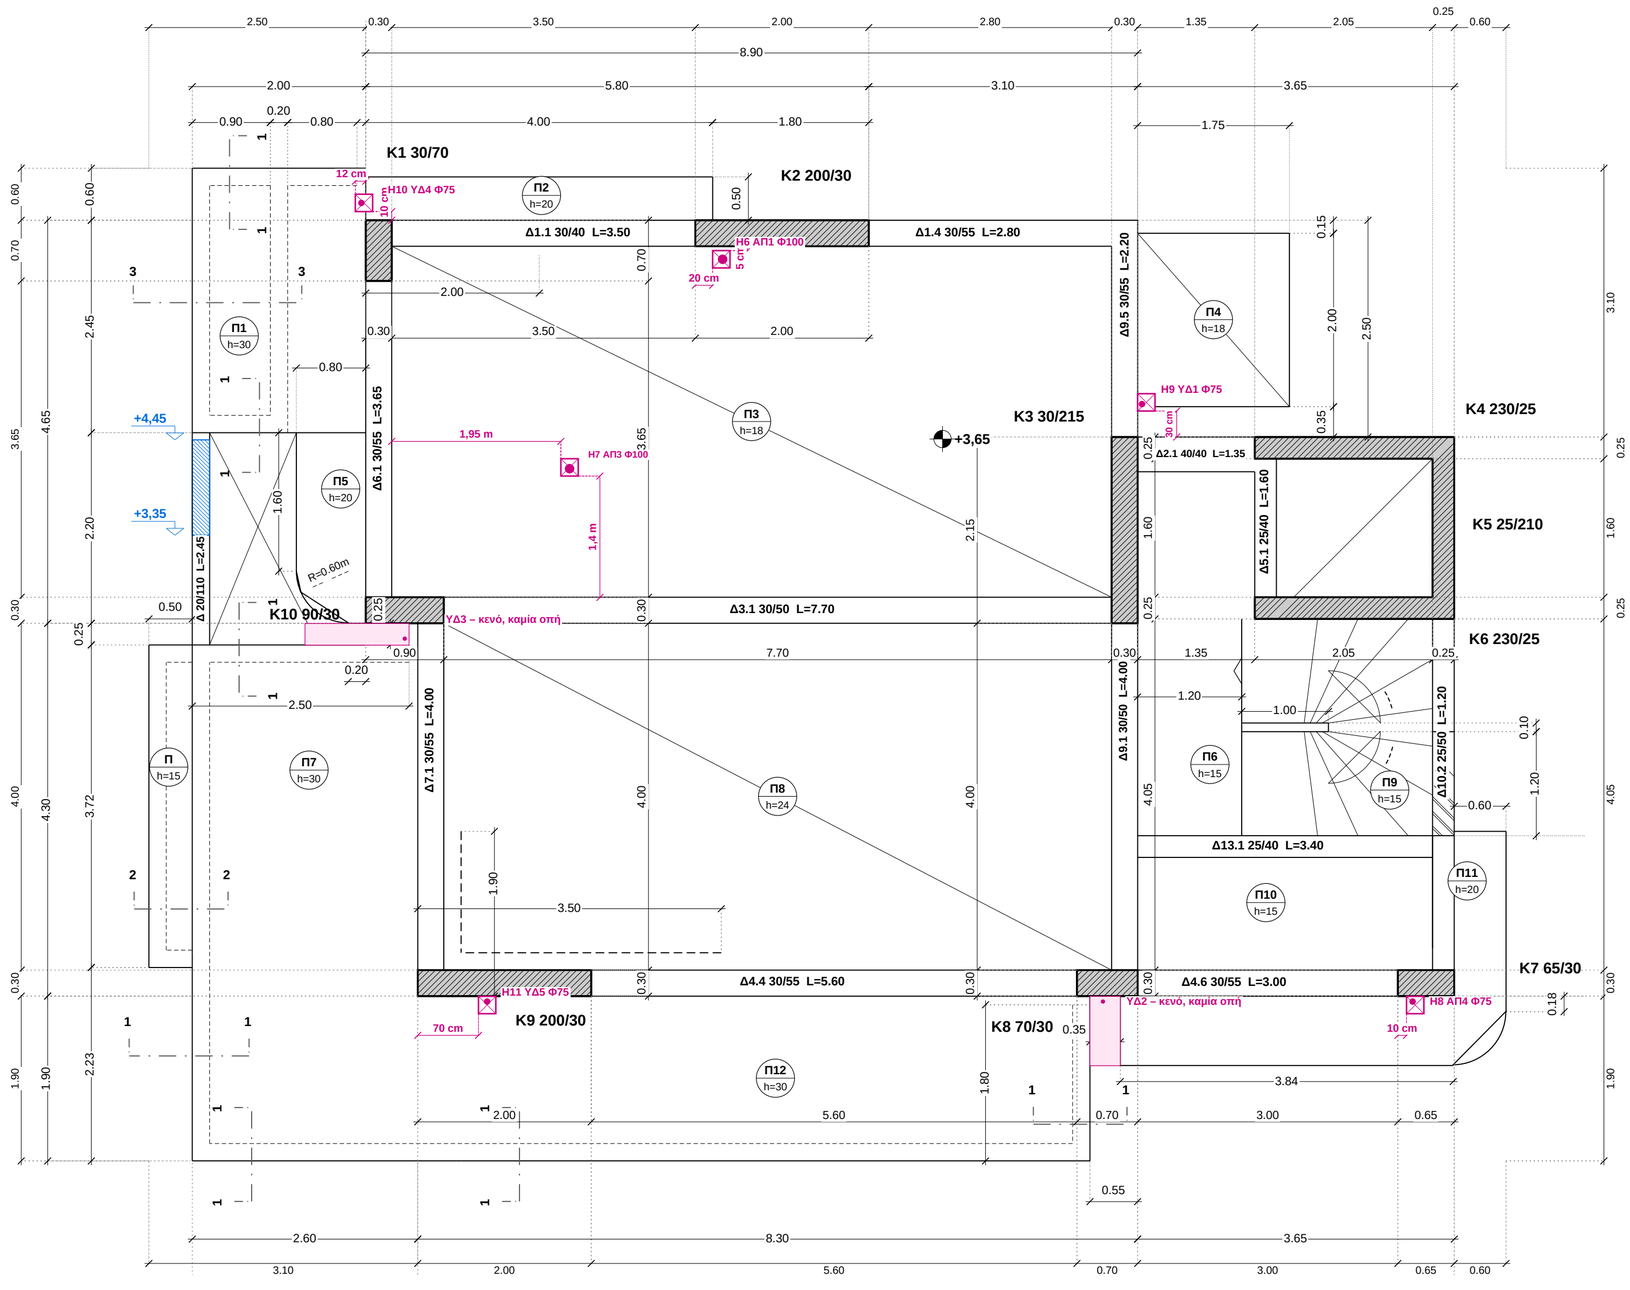


ΤΟΜΕΣ ΜΕΤΩΠΩΝ
(σκαρίφημα χωρίς κλίμακα)


ΤΟΜΗ 1-1

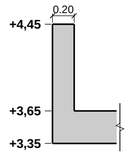

ΤΟΜΗ 2-2

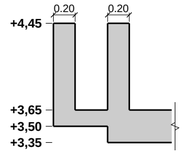

ΤΟΜΗ 3-3

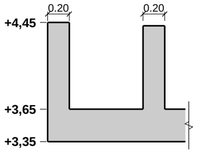

ΚΩΝΣΤΑΝΤΙΝΟΥΠΟΛΕΩΣ 12 & ΑΓ. ΒΑΡΒΑΡΑΣ, ΑΡΓΥΡΟΥΠΟΛΗ – ARKAD Ι.Κ.Ε.
Ξυλότυπος εργοταξίου – χωρίς οπλισμούς

ΞΥΛΟΤΥΠΟΣ ΟΡΟΦΗΣ ΙΣΟΓΕΙΟΥ — Σ3

ΣΤΑΘΜΗ ΑΝΩ ΠΛΑΚΑΣ
+3,65
ΚΛΙΜΑΚΑ 1:50 — A2 · 100 %

0 1 2 m

K1 30/70	υποστύλωμα / τοιχείο (cm)
Δ1.1 30/40	δοκός: πλάτος / ύψος (το ύψος μαζί με την πλάκα)
L=3.50	καθαρό μήκος δοκού, παρειά με παρειά
Π3 h=15	πλάκα – πάχος (cm)
+0,30	στάθμη άνω μπετού (m)
μπλε	τομές επί τόπου / φυτευτά και οι στάθμες τους
☒	οπή πλάκας 20 × 20 (αποχέτευση / υδρορροή)

Διαστάσεις σε m, από γωνία / παρειά κολόνας σε γωνία κολόνας. Οι αλυσίδες παρειών μετρήθηκαν από τη γεωμετρία του σχεδίου, οι υπόλοιπες είναι του μελετητή.

ΠΑΤΟΙ ΚΑΛΟΥΠΙΩΝ	στάθμη
Πλάκα h=15	**+3,50**
Πλάκα h=18	**+3,47**
Πλάκα h=20	**+3,45**
Πλάκα h=24	**+3,41**
Πλάκα h=30	**+3,35**
Δοκός ύψους 40	**+3,25**
Δοκός ύψους 50	**+3,15**
Δοκός ύψους 55	**+3,10**

Υπολογισμένα (στάθμη – ύψος)· όχι για ανεστραμμένες δοκούς / φυτευτά.

ΟΠΕΣ ΠΛΑΚΑΣ – ΚΟΥΤΙ 20 × 20
Θέση σε cm ως την ΑΚΜΗ του κουτιού, από παρειές σκυροδέματος.

H6 **ΑΠ1 Φ100**
20 ανατ. της Δ παρ. K2 · 5 νότια της N παρ. K2

H7 **ΑΠ3 Φ100**
1,95 m ανατ. της A παρ. Δ6.1 · 1,4 m βόρ. της B παρ. Δ3.1

H8 **ΑΠ4 Φ75**
10 ανατ. της Δ παρ. K7 · κολλητά στη N παρ. K7

H9 **ΥΔ1 Φ75**
κολλητά στη A παρ. Δ9.5 · 30 βόρ. της B παρ. K3

H10 **ΥΔ4 Φ75**
δυτ. ακμή 12 δυτ. της Δ παρ. K1 · 10 βόρ. της B παρ. K1

H11 **ΥΔ5 Φ75**
70 ανατ. της Δ παρ. K9 · κολλητά στη N παρ. K9

ΥΔ2 κενό 35 cm νότια της K8 – ΚΑΜΙΑ οπή

ΥΔ3 κενό 25 cm δυτικά της K10 – ΚΑΜΙΑ οπή

Τεύχος αποχετεύσεων R19, φύλλο ΑΠ-12.
Καμία οπή σε δοκό, καμία αναμονή σε στηθαίο.

ΣΗΜΕΙΩΣΕΙΣ


· Πρόβολοι: υποδοχή σιφωνιού και υδρορροή ΠΡΙΝ το μπετό, να μην κοπεί οπλισμός (μελετητής).

· Διαγραμμισμένο τοιχείο δίπλα στη σκάλα (0,60): έως το ύψος της σκάλας (μελετητής).

· Φυτευτά K23–K25 και τοιχεία εισόδου: φύλλο Σ3α.

Βάση: Σ3_ΕΦ.pdf – ξυλότυπος οροφής ισογείου, Γ. Κόγιας (Drive 19/10/2026).
Οπλισμοί ΜΟΝΟ από το σχέδιο του μελετητή.

Έκδοση R03 – 10/11/2026

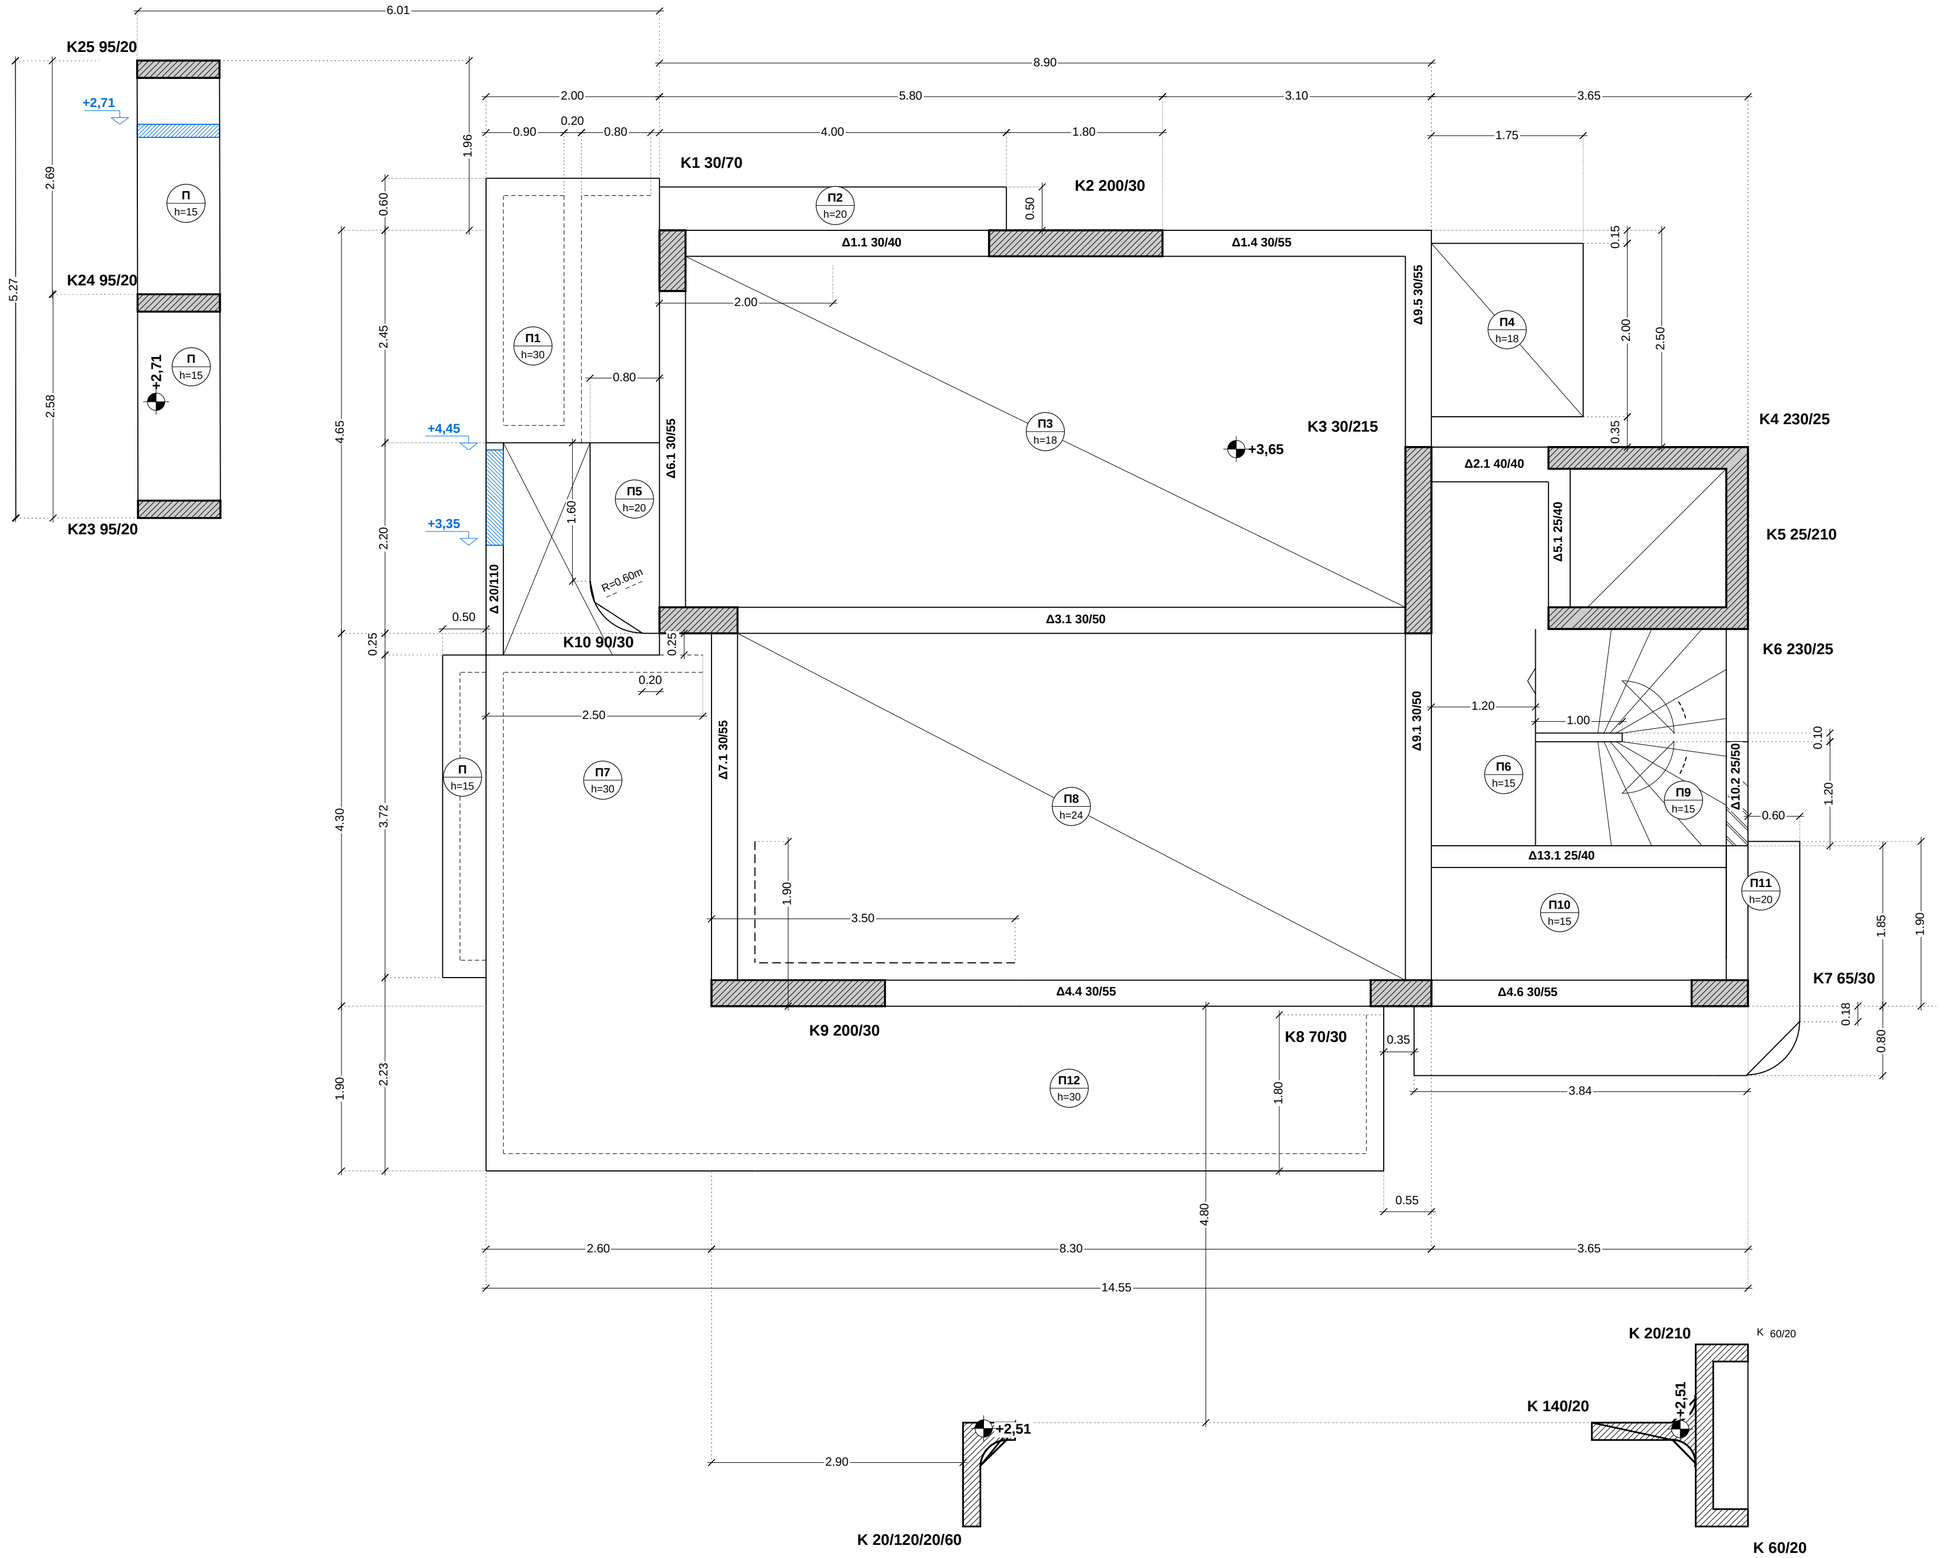

ΚΩΝΣΤΑΝΤΙΝΟΥΠΟΛΕΩΣ 12 & ΑΓ. ΒΑΡΒΑΡΑΣ, ΑΡΓΥΡΟΥΠΟΛΗ – ARKAD Ι.Κ.Ε.
Ξυλότυπος εργοταξίου – χωρίς οπλισμούς

ΟΡΟΦΗ ΙΣΟΓΕΙΟΥ – ΓΕΝΙΚΗ ΔΙΑΤΑΞΗ ΜΕ ΤΑ ΦΥΤΕΥΤΑ **Σ3α**

ΣΤΑΘΜΗ ΑΝΩ ΠΛΑΚΑΣ
+3,65
ΚΛΙΜΑΚΑ 1:50 A2 · 100 %
0 1 2 m

K1 30/70	υποστύλωμα / τοιχείο (cm)
Δ1.1 30/40	δοκός: πλάτος / ύψος (το ύψος μαζί με την πλάκα)
L=3.50	καθαρό μήκος δοκού, παρειά με παρειά
Π3 h=15	πλάκα – πάχος (cm)
+0,30	στάθμη άνω μπετού (m)
μπλε	τομές επί τόπου / φυτευτά και οι στάθμες τους


Διαστάσεις σε m, από γωνία / παρειά κολόνας σε γωνία κολόνας.

ΣΗΜΕΙΩΣΕΙΣ

· Γενική κάτοψη με τα φυτευτά: K23–K25 (δυτικά), τοιχεία εισόδου (νότια). Μεγαλύτερη κλίμακα: Σ3.


Βάση: Σ3_ΕΦ.pdf – ξυλότυπος οροφής ισογείου, Γ. Κόγιας (Drive 19/10/2026).
Οπλισμοί ΜΟΝΟ από το σχέδιο του μελετητή.

Έκδοση R03 – 10/11/2026

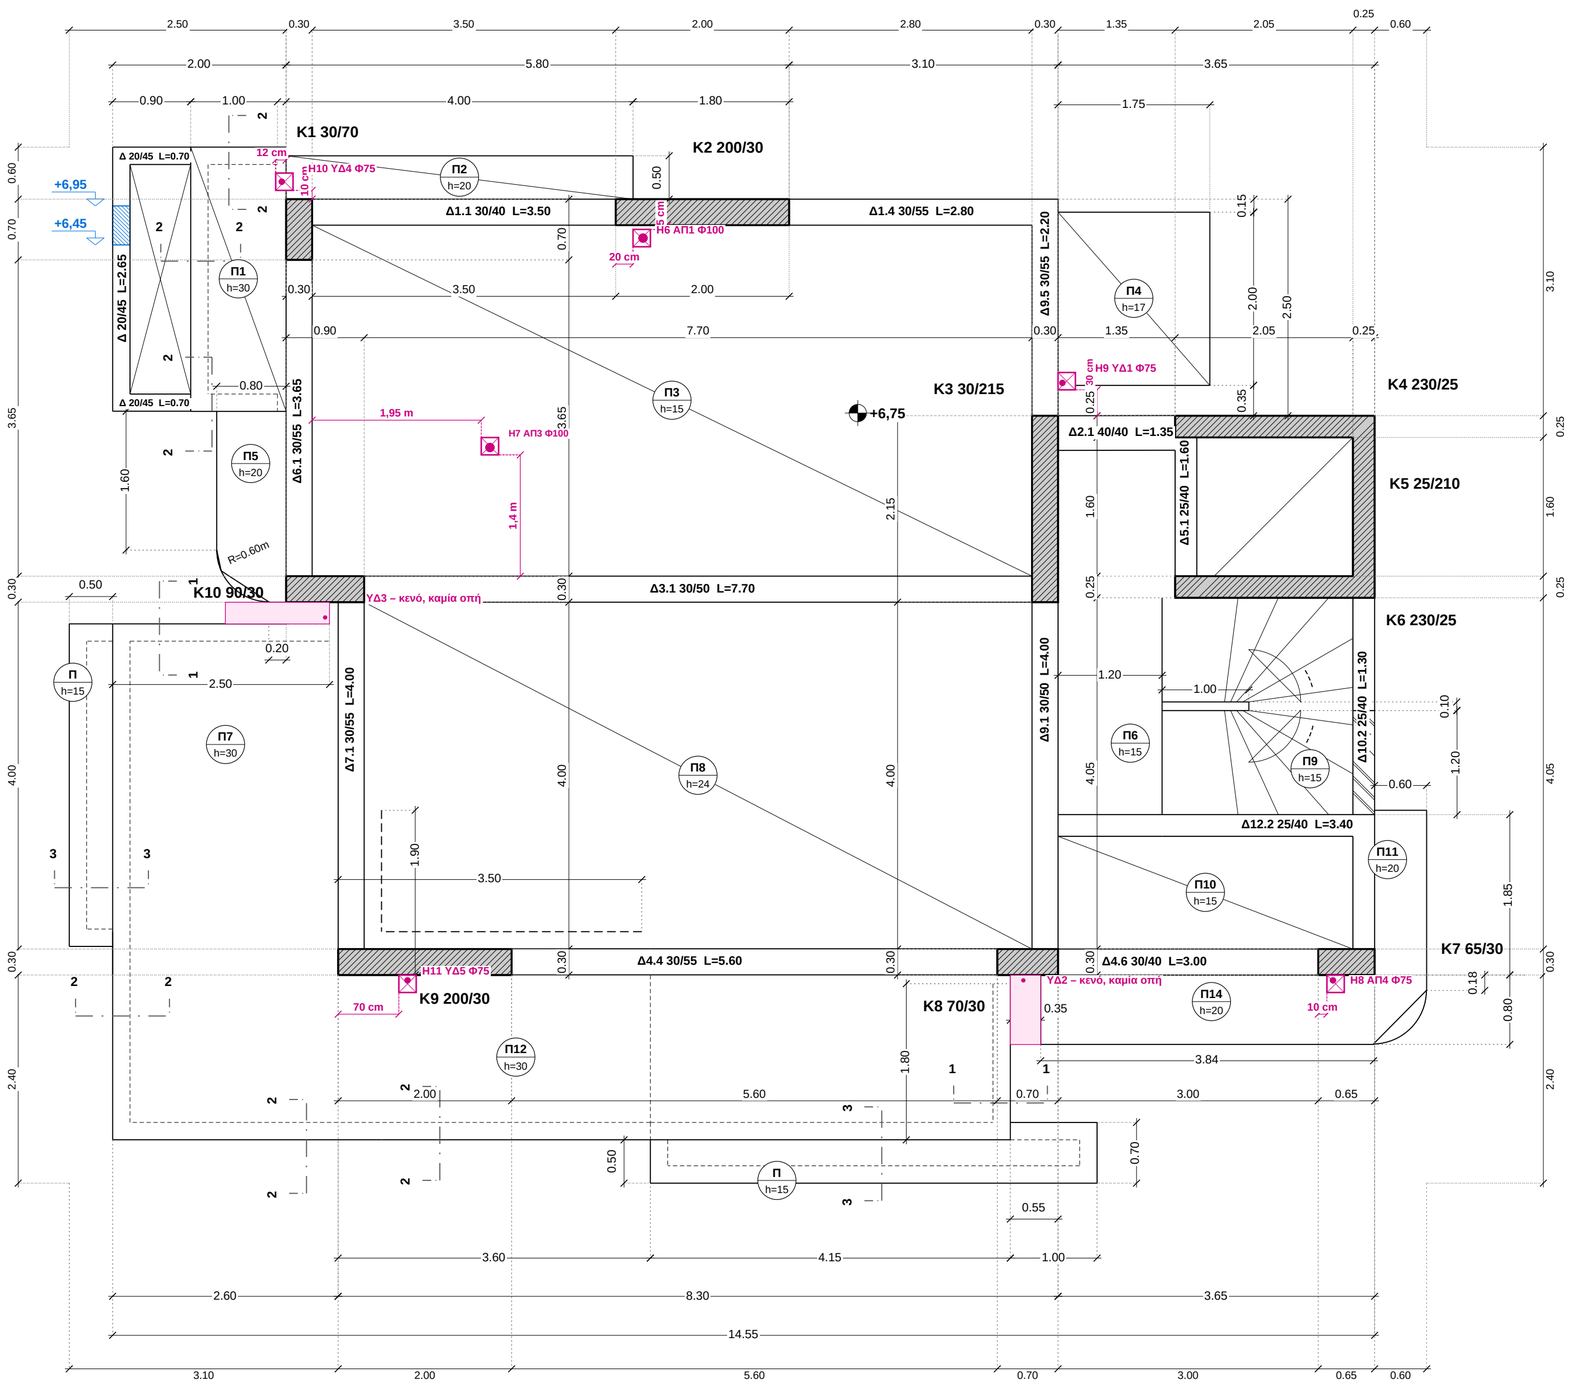


ΤΟΜΕΣ ΜΕΤΩΠΩΝ
(σκαρίφημα χωρίς κλίμακα)


ΤΟΜΗ 1-1

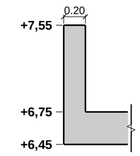

ΤΟΜΗ 2-2

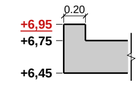

ΤΟΜΗ 3-3

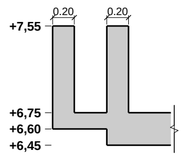

ΚΩΝΣΤΑΝΤΙΝΟΥΠΟΛΕΩΣ 12 & ΑΓ. ΒΑΡΒΑΡΑΣ, ΑΡΓΥΡΟΥΠΟΛΗ – ARKAD Ι.Κ.Ε.
Ξυλότυπος εργοταξίου – χωρίς οπλισμούς

ΞΥΛΟΤΥΠΟΣ ΟΡΟΦΗΣ Α΄ ΟΡΟΦΟΥ — Σ4

ΣΤΑΘΜΗ ΑΝΩ ΠΛΑΚΑΣ
+6,75
ΚΛΙΜΑΚΑ 1:50
A2 · 100 %
0 1 2 m

K1 30/70	υποστύλωμα / τοιχείο (cm)
Δ1.1 30/40	δοκός: πλάτος / ύψος (το ύψος μαζί με την πλάκα)
L=3.50	καθαρό μήκος δοκού, παρειά με παρειά
Π3 h=15	πλάκα – πάχος (cm)
+0,30	στάθμη άνω μπετού (m)
μπλε	τομές επί τόπου / φυτευτά και οι στάθμες τους
☒	οπή πλάκας 20 × 20 (αποχέτευση / υδρορροή)

Διαστάσεις σε m, από γωνία / παρειά κολόνας σε γωνία κολόνας. Οι αλυσίδες παρειών μετρήθηκαν από τη γεωμετρία του σχεδίου, οι υπόλοιπες είναι του μελετητή.

ΠΑΤΟΙ ΚΑΛΟΥΠΙΩΝ	στάθμη	ύψος*
Πλάκα h=15	**+6,60**	**2,95**
Πλάκα h=17	**+6,58**	**2,93**
Πλάκα h=20	**+6,55**	**2,90**
Πλάκα h=24	**+6,51**	**2,86**
Πλάκα h=30	**+6,45**	**2,80**
Δοκός ύψους 40	**+6,35**	**2,70**
Δοκός ύψους 50	**+6,25**	**2,60**
Δοκός ύψους 55	**+6,20**	**2,55**

* από την πλάκα του κάτω ορόφου (+3,65). Υπολογισμένα (στάθμη – ύψος)· όχι για ανεστραμμένες δοκούς / φυτευτά.

ΟΠΕΣ ΠΛΑΚΑΣ – ΚΟΥΤΙ 20 × 20
Θέση σε cm ως την ΑΚΜΗ του κουτιού, από παρειές σκυροδέματος.


H6 **ΑΠ1 Φ100** — 20 ανατ. της Δ παρ. K2 · 5 νότια της Ν παρ. K2
H7 **ΑΠ3 Φ100** — 1,95 m ανατ. της Α παρ. Δ6.1 · 1,4 m βόρ. της Β παρ. Δ3.1
H8 **ΑΠ4 Φ75** — 10 ανατ. της Δ παρ. K7 · κολλητά στη Ν παρ. K7
H9 **ΥΔ1 Φ75** — κολλητά στη Α παρ. Δ9.5 · 30 βόρ. της Β παρ. K3
H10 **ΥΔ4 Φ75** — δυτ. ακμή 12 δυτ. της Δ παρ. K1 · 10 βόρ. της Β παρ. K1
H11 **ΥΔ5 Φ75** — 70 ανατ. της Δ παρ. K9 · κολλητά στη Ν παρ. K9
ΥΔ2 κενό 35 cm νότια της K8 – ΚΑΜΙΑ οπή
ΥΔ3 κενό 25 cm δυτικά της K10 – ΚΑΜΙΑ οπή
Τεύχος αποχετεύσεων R19, φύλλο ΑΠ-13.
Καμία οπή σε δοκό, καμία αναμονή σε στηθαίο.

ΣΗΜΕΙΩΣΕΙΣ

· ΤΟΜΗ 2-2: μετόπη +6,45 έως +6,95 (ύψος 0,50 όπως Σ5) – αλλαγή 10/11/2026· ο μελετητής είχε +6,90. Να ενημερωθεί ο στατικός.
· Πρόβολοι: υποδοχή σιφωνιού και υδρορροή ΠΡΙΝ το μπετό, να μην κοπεί οπλισμός (μελετητής).
· Διαγραμμισμένο τοιχείο δίπλα στη σκάλα (0,60): έως το ύψος της σκάλας (μελετητής).

Βάση: Σ4_ΕΦ.pdf – ξυλότυπος οροφής Α΄ ορόφου, Γ. Κόγιας (Drive 19/10/2026).
Οπλισμοί ΜΟΝΟ από το σχέδιο του μελετητή.


Έκδοση R03 – 10/11/2026

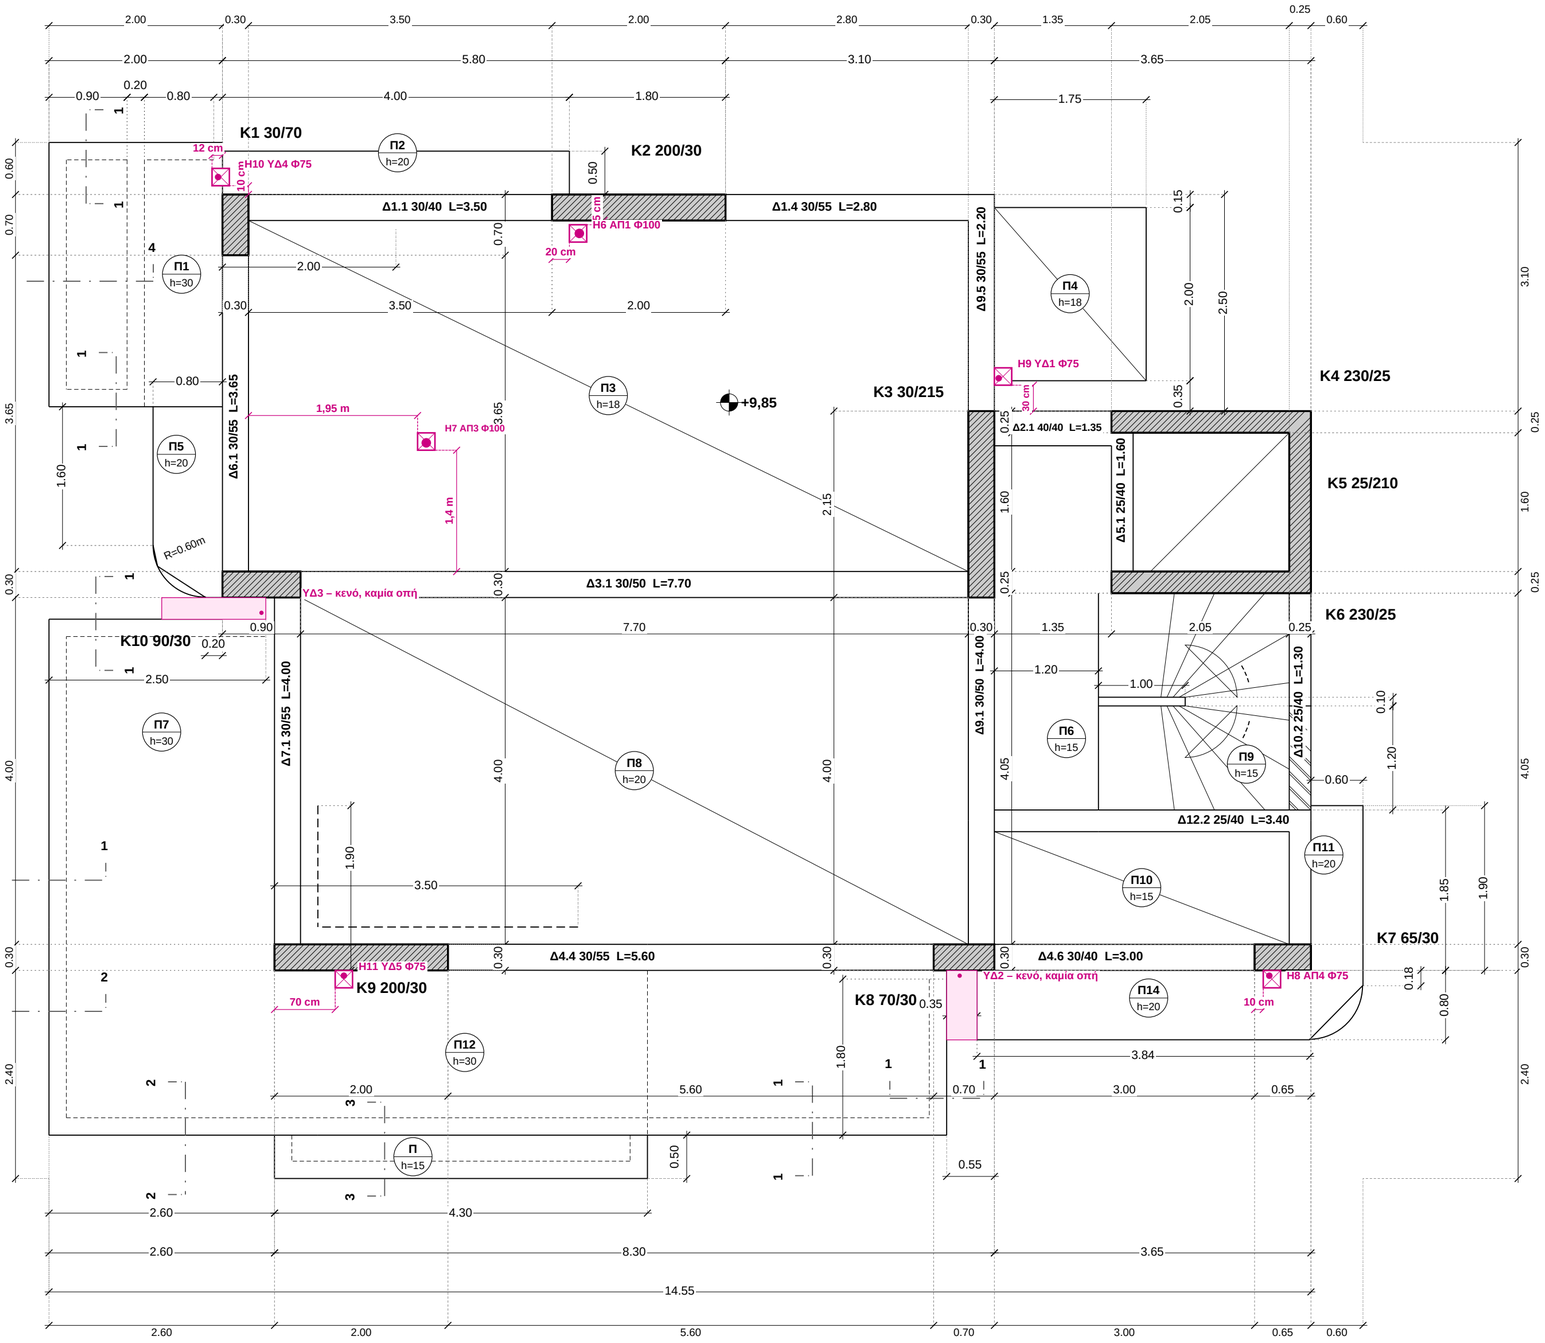


ΤΟΜΕΣ ΜΕΤΩΠΩΝ

(σκαρίφημα χωρίς κλίμακα)


ΤΟΜΗ 1-1

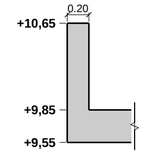


ΤΟΜΗ 2-2

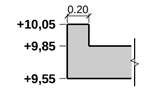

ΤΟΜΗ 3-3

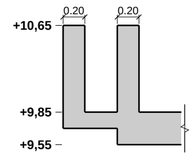

ΤΟΜΗ 4-4

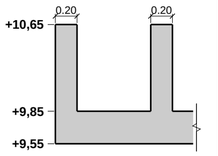

ΚΩΝΣΤΑΝΤΙΝΟΥΠΟΛΕΩΣ 12 & ΑΓ. ΒΑΡΒΑΡΑΣ, ΑΡΓΥΡΟΥΠΟΛΗ – ARKAD Ι.Κ.Ε.
Ξυλότυπος εργοταξίου – χωρίς οπλισμούς

ΞΥΛΟΤΥΠΟΣ ΟΡΟΦΗΣ Β΄ ΟΡΟΦΟΥ — Σ5

ΣΤΑΘΜΗ ΑΝΩ ΠΛΑΚΑΣ
+9,85
ΚΛΙΜΑΚΑ 1:50 — A2 · 100 %

0 1 2 m

K1 30/70	υποστύλωμα / τοιχείο (cm)
Δ1.1 30/40	δοκός: πλάτος / ύψος (το ύψος μαζί με την πλάκα)
L=3.50	καθαρό μήκος δοκού, παρειά με παρειά
Π3 h=15	πλάκα – πάχος (cm)
+0,30	στάθμη άνω μπετού (m)
μπλε	τομές επί τόπου / φυτευτά και οι στάθμες τους
☒	οπή πλάκας 20 × 20 (αποχέτευση / υδρορροή)

Διαστάσεις σε m, από γωνία / παρειά κολόνας σε γωνία κολόνας. Οι αλυσίδες παρειών μετρήθηκαν από τη γεωμετρία του σχεδίου, οι υπόλοιπες είναι του μελετητή.

ΠΑΤΟΙ ΚΑΛΟΥΠΙΩΝ	στάθμη	ύψος*
Πλάκα h=15	**+9,70**	**2,95**
Πλάκα h=18	**+9,67**	**2,92**
Πλάκα h=20	**+9,65**	**2,90**
Πλάκα h=30	**+9,55**	**2,80**
Δοκός ύψους 40	**+9,45**	**2,70**
Δοκός ύψους 50	**+9,35**	**2,60**
Δοκός ύψους 55	**+9,30**	**2,55**

* από την πλάκα του κάτω ορόφου (+6,75). Υπολογισμένα (στάθμη − ύψος)· όχι για ανεστραμμένες δοκούς / φυτευτά.

ΟΠΕΣ ΠΛΑΚΑΣ – ΚΟΥΤΙ 20 × 20
Θέση σε cm ως την ΑΚΜΗ του κουτιού, από παρειές σκυροδέματος.

- **Η6** **ΑΠ1 Φ100** — 20 ανατ. της Δ παρ. Κ2 · 5 νότια της Ν παρ. Κ2
- **Η7** **ΑΠ3 Φ100** — 1,95 m ανατ. της Α παρ. Δ6.1 · 1,4 m βόρ. της Β παρ. Δ3.1
- **Η8** **ΑΠ4 Φ75** — 10 ανατ. της Δ παρ. Κ7 · κολλητά στη Ν παρ. Κ7
- **Η9** **ΥΔ1 Φ75** — κολλητά στη Α παρ. Δ9.5 · 30 βόρ. της Β παρ. Κ3
- **Η10** **ΥΔ4 Φ75** — δυτ. ακμή 12 δυτ. της Δ παρ. Κ1 · 10 βόρ. της Β παρ. Κ1
- **Η11** **ΥΔ5 Φ75** — 70 ανατ. της Δ παρ. Κ9 · κολλητά στη Ν παρ. Κ9
- **ΥΔ2** κενό 35 cm νότια της Κ8 – ΚΑΜΙΑ οπή
- **ΥΔ3** κενό 25 cm δυτικά της Κ10 – ΚΑΜΙΑ οπή


Τεύχος αποχετεύσεων R19, φύλλο ΑΠ-14.
Καμία οπή σε δοκό, καμία αναμονή σε στηθαίο.

ΣΗΜΕΙΩΣΕΙΣ

· Πρόβολοι: υποδοχή σιφωνιού και υδρορροή ΠΡΙΝ το μπετό, να μην κοπεί οπλισμός (μελετητής).
· Διαγραμμισμένο τοιχείο δίπλα στη σκάλα (0,60): έως το ύψος της σκάλας (μελετητής).


Βάση: Σ5_ΕΦ.pdf – ξυλότυπος οροφής Β΄ ορόφου, Γ. Κόγιας (Drive 19/10/2026).
Οπλισμοί ΜΟΝΟ από το σχέδιο του μελετητή.

Έκδοση R03 – 10/11/2026

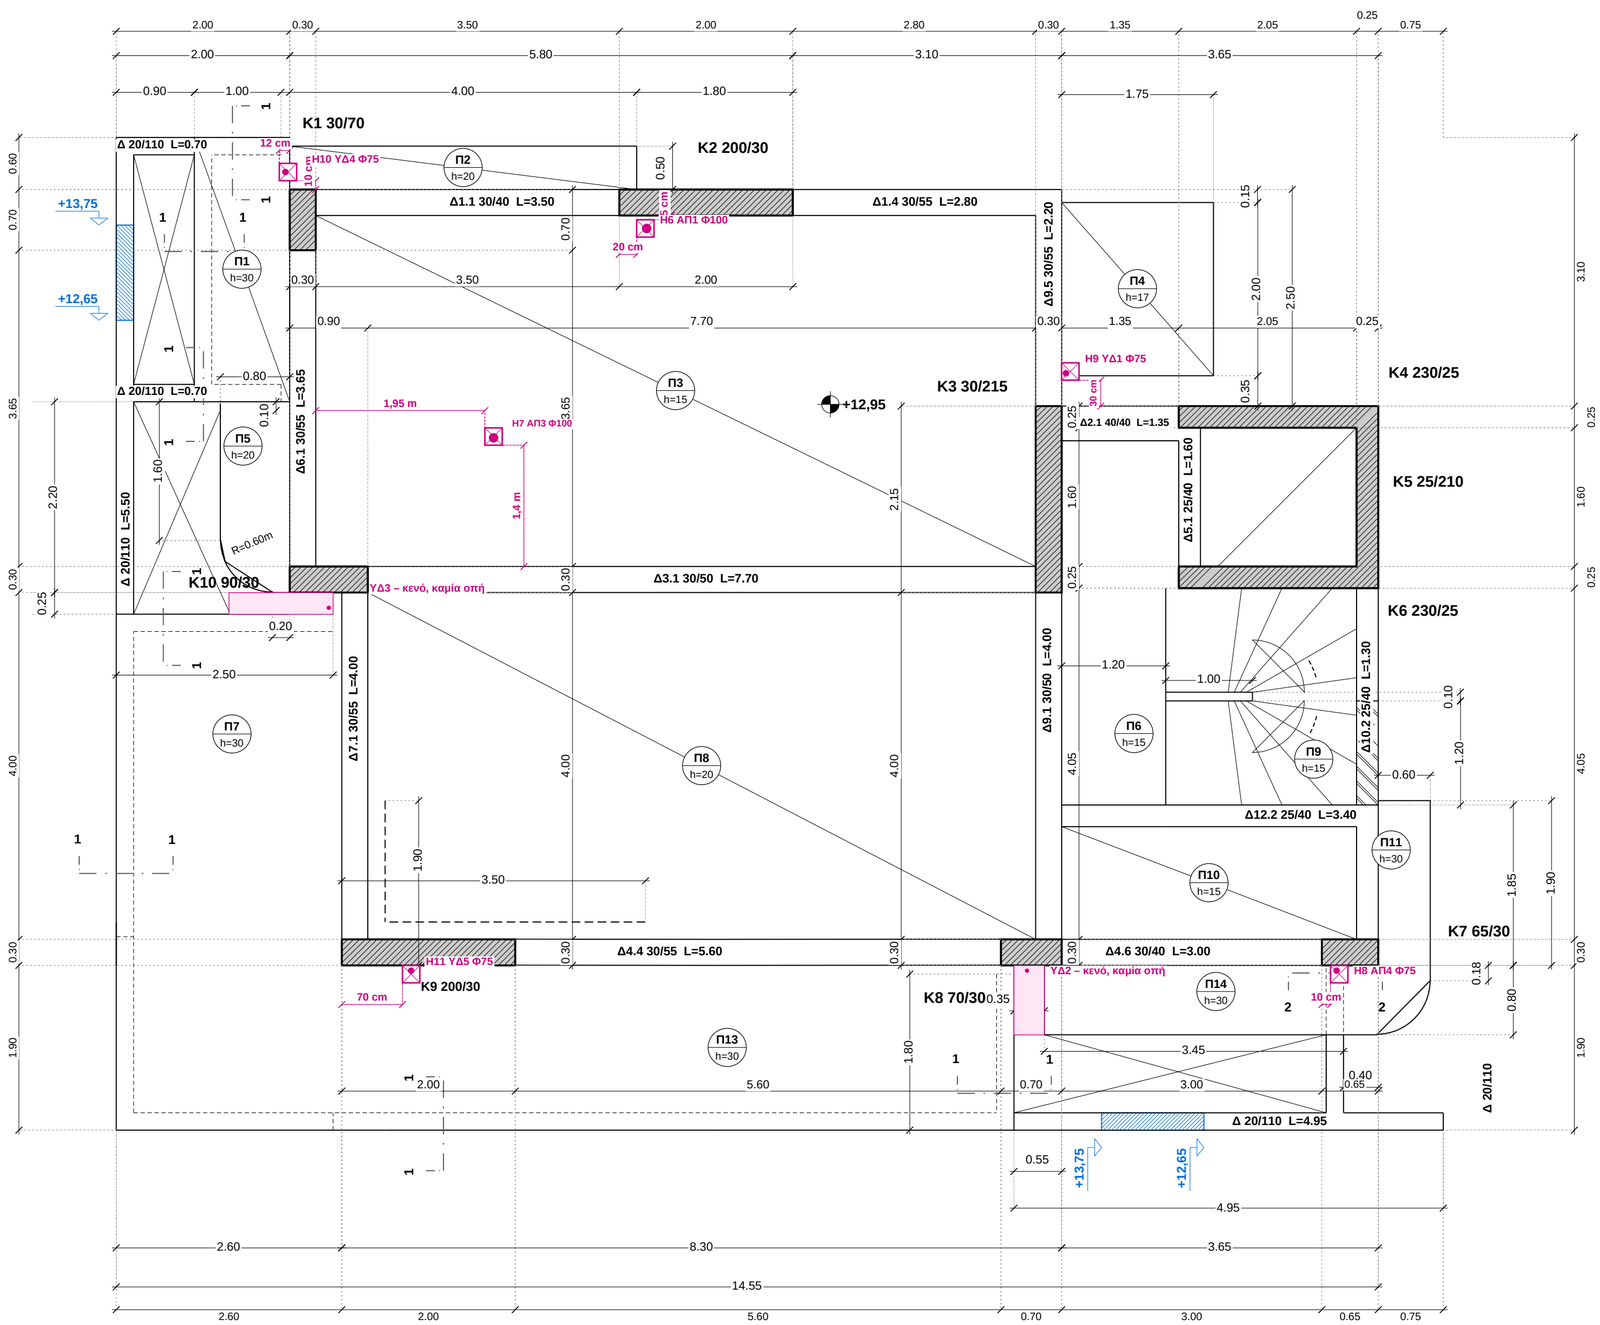


ΤΟΜΕΣ ΜΕΤΩΠΩΝ
(σκαρίφημα χωρίς κλίμακα)

ΤΟΜΗ 1-1

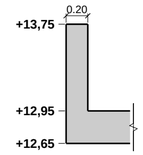

ΤΟΜΗ 2-2

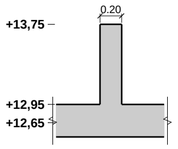

ΚΩΝΣΤΑΝΤΙΝΟΥΠΟΛΕΩΣ 12 & ΑΓ. ΒΑΡΒΑΡΑΣ, ΑΡΓΥΡΟΥΠΟΛΗ – ARKAD Ι.Κ.Ε.
Ξυλότυπος εργοταξίου – χωρίς οπλισμούς

ΞΥΛΟΤΥΠΟΣ ΟΡΟΦΗΣ Γ΄ ΟΡΟΦΟΥ — Σ6

ΣΤΑΘΜΗ ΑΝΩ ΠΛΑΚΑΣ
+12,95
ΚΛΙΜΑΚΑ 1:50 — A2 · 100 %

0 1 2 m

K1 30/70	υποστύλωμα / τοιχείο (cm)
Δ1.1 30/40	δοκός: πλάτος / ύψος (το ύψος μαζί με την πλάκα)
L=3.50	καθαρό μήκος δοκού, παρειά με παρειά
Π3 h=15	πλάκα – πάχος (cm)
+0,30	στάθμη άνω μπετού (m)
μπλε	τομές επί τόπου / φυτευτά και οι στάθμες τους
☒	οπή πλάκας 20 × 20 (αποχέτευση / υδρορροή)

Διαστάσεις σε m, από γωνία / παρειά κολόνας σε γωνία κολόνας. Οι αλυσίδες παρειών μετρήθηκαν από τη γεωμετρία του σχεδίου, οι υπόλοιπες είναι του μελετητή.

ΠΑΤΟΙ ΚΑΛΟΥΠΙΩΝ	στάθμη	ύψος*
Πλάκα h=15	**+12,80**	**2,95**
Πλάκα h=17	**+12,78**	**2,93**
Πλάκα h=20	**+12,75**	**2,90**
Πλάκα h=30	**+12,65**	**2,80**
Δοκός ύψους 40	**+12,55**	**2,70**
Δοκός ύψους 50	**+12,45**	**2,60**
Δοκός ύψους 55	**+12,40**	**2,55**

* από την πλάκα του κάτω ορόφου (+9,85). Υπολογισμένα (στάθμη − ύψος)· όχι για ανεστραμμένες δοκούς / φυτευτά.

ΟΠΕΣ ΠΛΑΚΑΣ – ΚΟΥΤΙ 20 × 20
Θέση σε cm ως την ΑΚΜΗ του κουτιού, από παρειές σκυροδέματος.

H6 **ΑΠ1 Φ100**
20 ανατ. της Δ παρ. Κ2 · 5 νότια της Ν παρ. Κ2

H7 **ΑΠ3 Φ100**
1,95 m ανατ. της Α παρ. Δ6.1 · 1,4 m βόρ. της Β παρ. Δ3.1

H8 **ΑΠ4 Φ75**
10 ανατ. της Δ παρ. Κ7 · κολλητά στη Ν παρ. Κ7

H9 **ΥΔ1 Φ75**
κολλητά στη Α παρ. Δ9.5 · 30 βόρ. της Β παρ. Κ3

H10 **ΥΔ4 Φ75**
δυτ. ακμή 12 δυτ. της Δ παρ. Κ1 · 10 βόρ. της Β παρ. Κ1

H11 **ΥΔ5 Φ75**
70 ανατ. της Δ παρ. Κ9 · κολλητά στη Ν παρ. Κ9

ΥΔ2 κενό 35 cm νότια της Κ8 – ΚΑΜΙΑ οπή

ΥΔ3 κενό 25 cm δυτικά της Κ10 – ΚΑΜΙΑ οπή

Τεύχος αποχετεύσεων R19, φύλλο ΑΠ-15.
Καμία οπή σε δοκό, καμία αναμονή σε στηθαίο.


ΣΗΜΕΙΩΣΕΙΣ

· Πρόβολοι: υποδοχή σιφωνιού και υδρορροή ΠΡΙΝ το μπετό, να μην κοπεί οπλισμός (μελετητής).

· Διαγραμμισμένο τοιχείο δίπλα στη σκάλα (0,60): έως το ύψος της σκάλας (μελετητής).

Βάση: Σ6_ΕΦ.pdf – ξυλότυπος οροφής Γ΄ ορόφου, Γ. Κόγιας (Drive 19/10/2026).
Οπλισμοί ΜΟΝΟ από το σχέδιο του μελετητή.

Έκδοση R03 – 10/11/2026

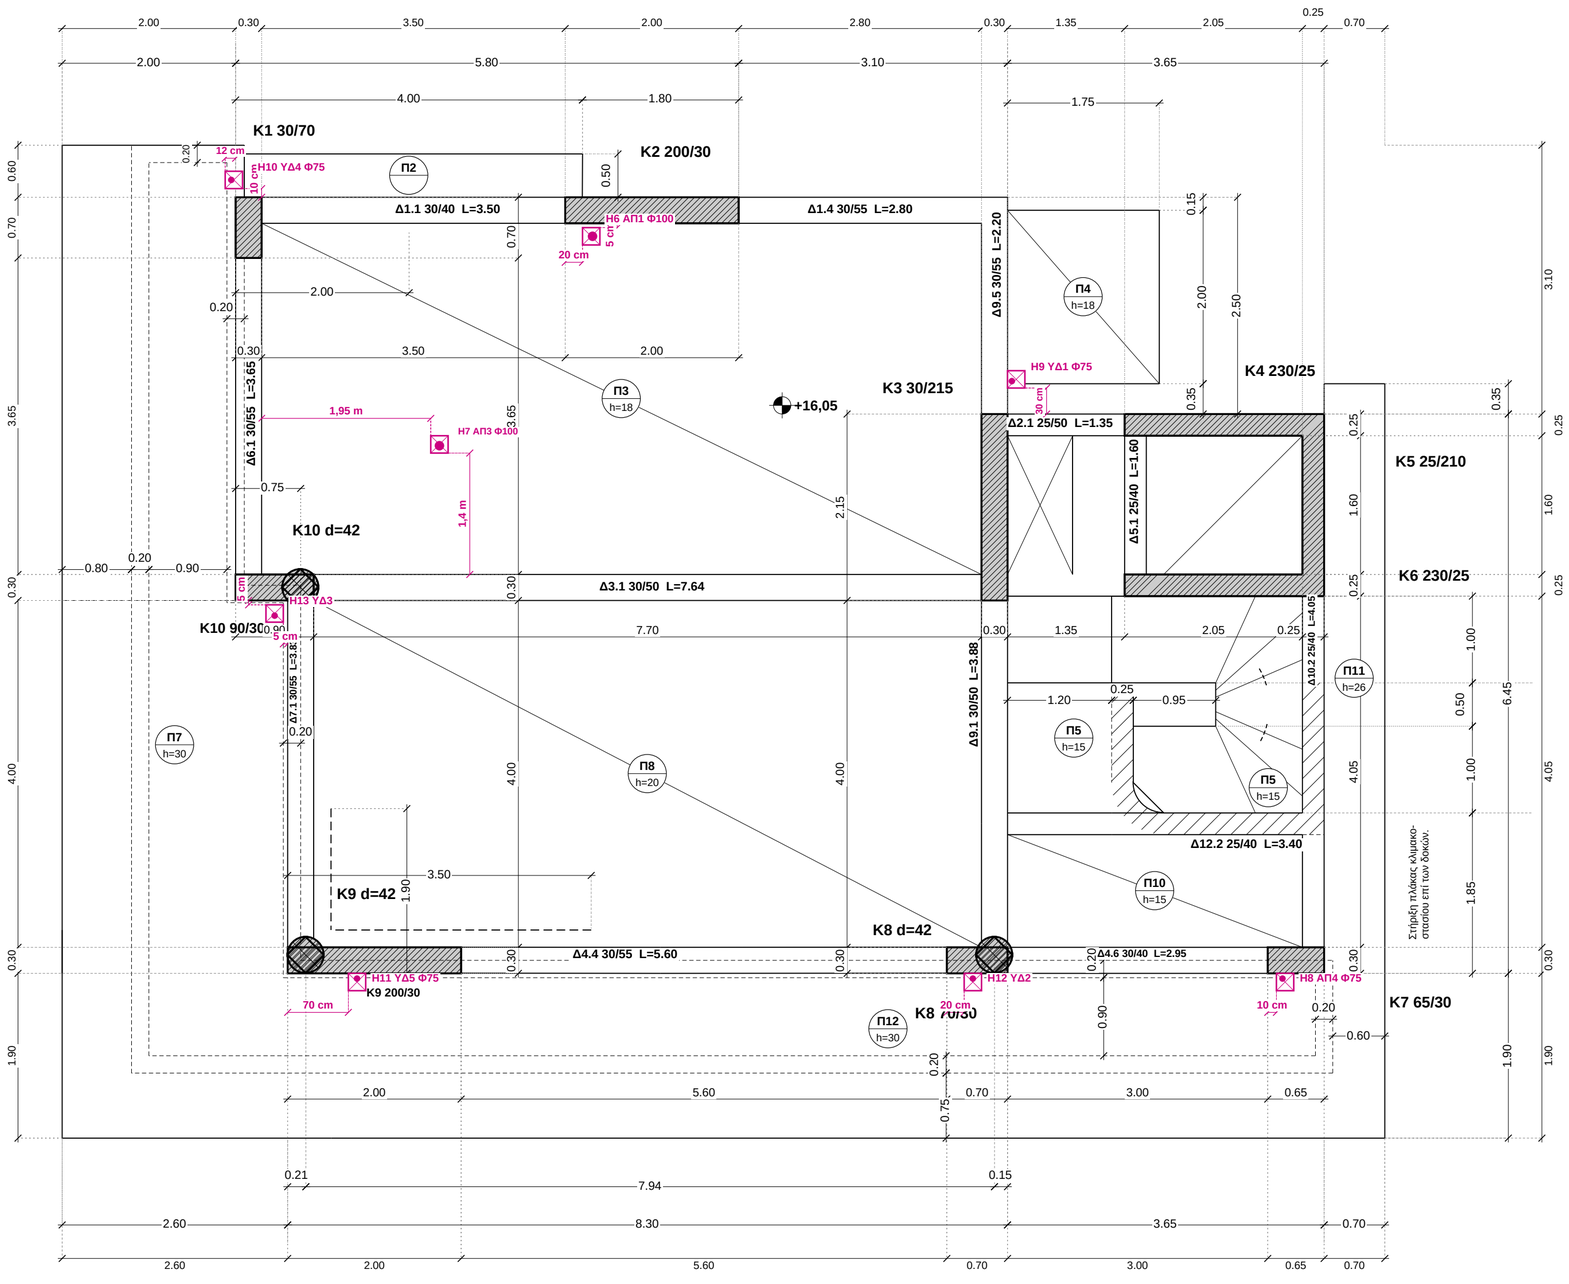

ΚΩΝΣΤΑΝΤΙΝΟΥΠΟΛΕΩΣ 12 & ΑΓ. ΒΑΡΒΑΡΑΣ, ΑΡΓΥΡΟΥΠΟΛΗ – ARKAD I.K.E.
Ξυλότυπος εργοταξίου – χωρίς οπλισμούς

ΞΥΛΟΤΥΠΟΣ ΟΡΟΦΗΣ Δ΄ ΟΡΟΦΟΥ

Σ7

ΣΤΑΘΜΗ ΑΝΩ ΠΛΑΚΑΣ
+16,05
ΚΛΙΜΑΚΑ 1:50
A2 · 100 %
0 1 2 m

K1 30/70	υποστύλωμα / τοιχείο (cm)
Δ1.1 30/40	δοκός: πλάτος / ύψος (το ύψος μαζί με την πλάκα)
L=3.50	καθαρό μήκος δοκού, παρειά με παρειά
Π3 h=15	πλάκα – πάχος (cm)
+0,30	στάθμη άνω μπετού (m)
μπλε	τομές επί τόπου / φυτευτά και οι στάθμες τους
⊠	οπή πλάκας 20 × 20 (αποχέτευση / υδρορροή)

Διαστάσεις σε m, από γωνία / παρειά κολόνας σε γωνία κολόνας. Οι αλυσίδες παρειών μετρήθηκαν από τη γεωμετρία του σχεδίου, οι υπόλοιπες είναι του μελετητή.

ΠΑΤΟΙ ΚΑΛΟΥΠΙΩΝ	στάθμη	ύψος*
Πλάκα h=15	**+15,90**	**2,95**
Πλάκα h=18	**+15,87**	**2,92**
Πλάκα h=20	**+15,85**	**2,90**
Πλάκα h=26	**+15,79**	**2,84**
Πλάκα h=30	**+15,75**	**2,80**
Δοκός ύψους 40	**+15,65**	**2,70**
Δοκός ύψους 50	**+15,55**	**2,60**
Δοκός ύψους 55	**+15,50**	**2,55**

* από την πλάκα του κάτω ορόφου (+12,95). Υπολογισμένα (στάθμη – ύψος)· όχι για ανεστραμμένες δοκούς / φυτευτά.

ΟΠΕΣ ΠΛΑΚΑΣ – ΚΟΥΤΙ 20 × 20
Θέση σε cm ως την ΑΚΜΗ του κουτιού, από παρειές σκυροδέματος.


- **H6 ΑΠ1 Φ100** — 20 ανατ. της Δ παρ. Κ2 · 5 νότια της Ν παρ. Κ2
- **H7 ΑΠ3 Φ100** — 1,95 m ανατ. της Α παρ. Δ6.1 · 1,4 m βόρ. της Β παρ. Δ3.1
- **H8 ΑΠ4 Φ75** — 10 ανατ. της Δ παρ. Κ7 · κολλητά στη Ν παρ. Κ7
- **H9 ΥΔ1 Φ75** — κολλητά στη Α παρ. Δ9.5 · 30 βόρ. της Β παρ. Κ3
- **H10 ΥΔ4 Φ75** — δυτ. ακμή 12 δυτ. της Δ παρ. Κ1 · 10 βόρ. της Β παρ. Κ1
- **H11 ΥΔ5 Φ75** — 70 ανατ. της Δ παρ. Κ9 · κολλητά στη Ν παρ. Κ9
- **H12 ΥΔ2 – σιφώνι δώματος Φ75** — 20 ανατ. της Δ παρ. Κ8 · κολλητά στη Ν παρ. Κ8
- **H13 ΥΔ3 – σιφώνι δώματος Φ75** — 5 δυτ. της Δ παρ. Δ7.1 · 5 νότια της Ν παρ. Κ10

Τεύχος αποχετεύσεων R19, φύλλο ΑΠ-16. Καμία οπή σε δοκό, καμία αναμονή σε στηθαίο.

ΣΗΜΕΙΩΣΕΙΣ


· Πρόβολοι: υποδοχή σιφωνιού και υδρορροή ΠΡΙΝ το μπετό, να μην κοπεί οπλισμός (μελετητής).

ΛΕΠΤΟΜΕΡΕΙΑ ΜΕΛΕΤΗΤΗ
πλάκα στη στάθμη +17,36

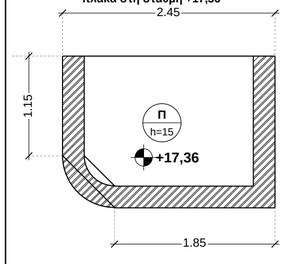

Βάση: Σ7_ΕΦ.pdf – ξυλότυπος οροφής Δ΄ ορόφου, Γ. Κόγιας (Drive 19/10/2026).
Οπλισμοί ΜΟΝΟ από το σχέδιο του μελετητή.

Έκδοση R03 – 10/11/2026

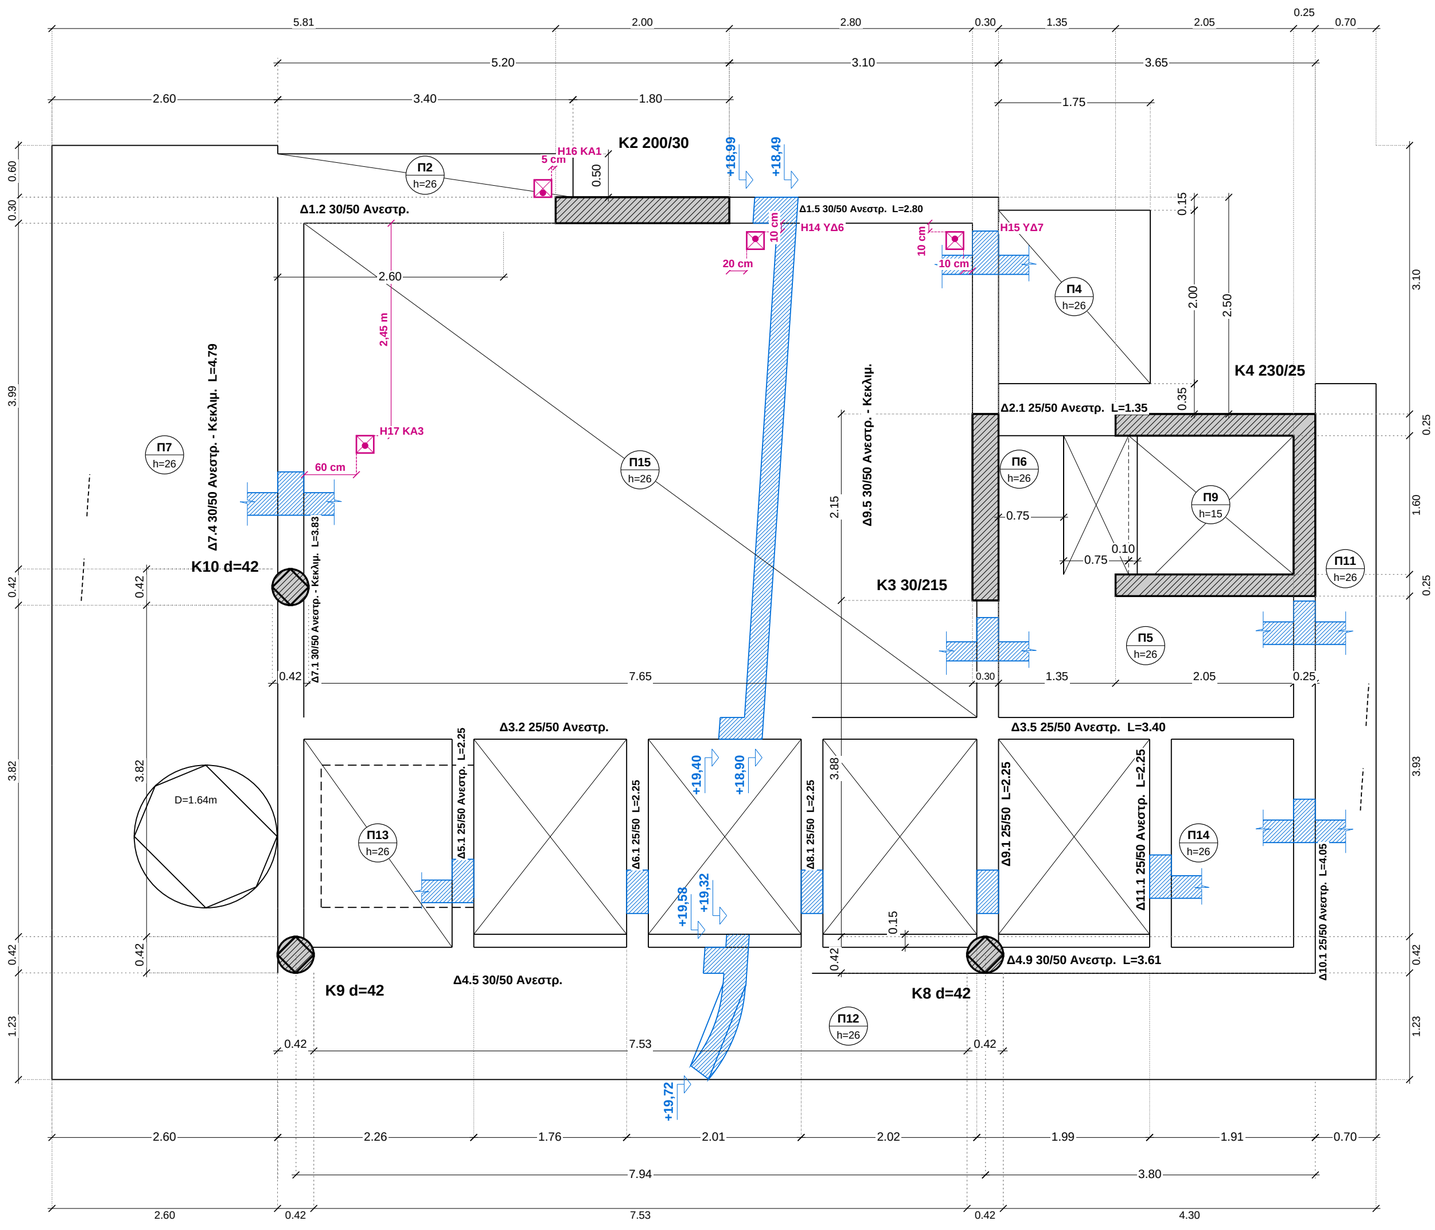

ΚΩΝΣΤΑΝΤΙΝΟΥΠΟΛΕΩΣ 12 & ΑΓ. ΒΑΡΒΑΡΑΣ, ΑΡΓΥΡΟΥΠΟΛΗ – ARKAD Ι.Κ.Ε.
Ξυλότυπος εργοταξίου – χωρίς οπλισμούς

ΞΥΛΟΤΥΠΟΣ ΣΟΦΙΤΑΣ (ΣΤΕΓΗ) Σ8

ΣΤΑΘΜΗ ΑΝΩ ΠΛΑΚΑΣ
+18,49 έως +19,72
ΚΛΙΜΑΚΑ 1:50 A2 · 100 %

0 1 2 m

Κ1 30/70	υποστύλωμα / τοιχείο (cm)
Δ1.1 30/40	δοκός: πλάτος / ύψος (το ύψος μαζί με την πλάκα)
L=3.50	καθαρό μήκος δοκού, παρειά με παρειά
Π3 h=15	πλάκα – πάχος (cm)
+0,30	στάθμη άνω μπετού (m)
μπλε	τομές επί τόπου / φυτευτά και οι στάθμες τους
☒	οπή πλάκας 20 × 20 (αποχέτευση / υδρορροή)

Διαστάσεις σε m, από γωνία / παρειά κολόνας σε γωνία κολόνας. Οι αλυσίδες παρειών μετρήθηκαν από τη γεωμετρία του σχεδίου, οι υπόλοιπες είναι του μελετητή.

ΟΠΕΣ ΠΛΑΚΑΣ – ΚΟΥΤΙ 20 × 20
Θέση σε cm ως την ΑΚΜΗ του κουτιού, από παρειές σκυροδέματος.

H14 ΥΔ6 – σιφώνι στέγης Φ75
20 ανατ. της Α παρ. Κ2 · 10 νότια της Ν παρ. Δ1.5

H15 ΥΔ7 – σιφώνι στέγης Φ75
10 δυτ. της Δ παρ. Δ9.5 · 10 νότια της Ν παρ. Δ1.5

H16 ΚΑ1 – αερισμός ΑΠ1 Φ75
5 δυτ. της Δ παρ. Κ2 · κολλητά στη Β παρ. Δ1.2

H17 ΚΑ3 – αερισμός ΑΠ3 Φ75
60 ανατ. της Α παρ. Δ7.4 · 2,45 m νότια της Ν παρ. Δ1.2

Τεύχος αποχετεύσεων R19, φύλλο ΑΠ-17.
Καμία οπή σε δοκό, καμία αναμονή σε στηθαίο.

ΣΗΜΕΙΩΣΕΙΣ

· Πρόβολοι: υποδοχή σιφωνιού και υδρορροή ΠΡΙΝ το μπετό, να μην κοπεί οπλισμός (μελετητής).

· Στέγη κεκλιμένη: στάθμες (μπλε) στις τομές επί τόπου. «Ανεστρ.» = ανεστραμμένη δοκός.

Βάση: Σ8.pdf – ξυλότυπος σοφίτας, Γ. Κόγιας (οριστική μελέτη 02/2026, Drive 06/11/2026).
Οπλισμοί ΜΟΝΟ από το σχέδιο του μελετητή.

Έκδοση R03 – 10/11/2026