

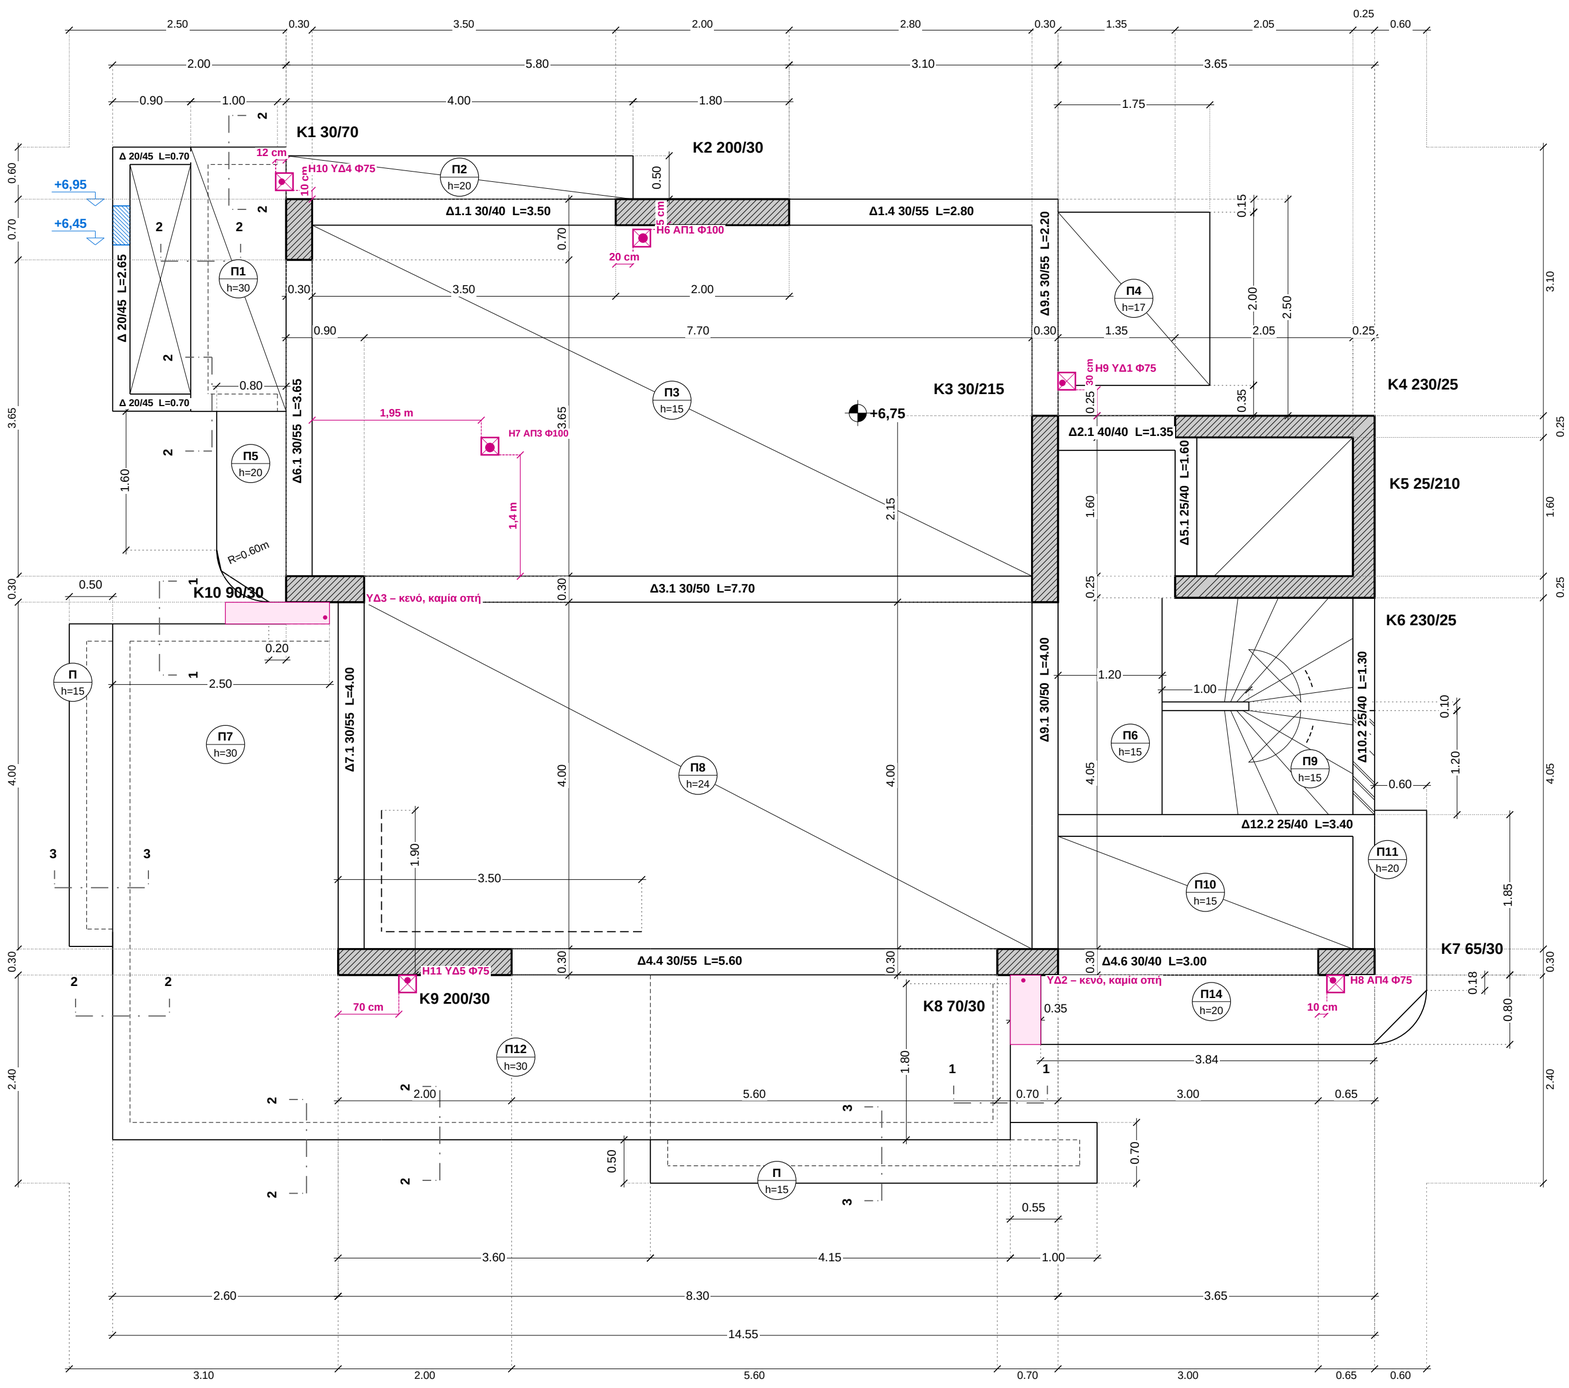


ΤΟΜΕΣ ΜΕΤΩΠΩΝ
(σκαρίφημα χωρίς κλίμακα)


ΤΟΜΗ 1-1

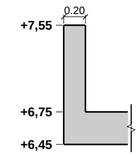

ΤΟΜΗ 2-2

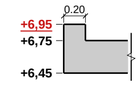

ΤΟΜΗ 3-3

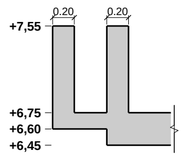

ΚΩΝΣΤΑΝΤΙΝΟΥΠΟΛΕΩΣ 12 & ΑΓ. ΒΑΡΒΑΡΑΣ, ΑΡΓΥΡΟΥΠΟΛΗ – ARKAD Ι.Κ.Ε.
Ξυλότυπος εργοταξίου – χωρίς οπλισμούς

ΞΥΛΟΤΥΠΟΣ ΟΡΟΦΗΣ Α΄ ΟΡΟΦΟΥ — Σ4

ΣΤΑΘΜΗ ΑΝΩ ΠΛΑΚΑΣ
+6,75
ΚΛΙΜΑΚΑ 1:50
A2 · 100 %
0 1 2 m

K1 30/70	υποστύλωμα / τοιχείο (cm)
Δ1.1 30/40	δοκός: πλάτος / ύψος (το ύψος μαζί με την πλάκα)
L=3.50	καθαρό μήκος δοκού, παρειά με παρειά
Π3 h=15	πλάκα – πάχος (cm)
+0,30	στάθμη άνω μπετού (m)
μπλε	τομές επί τόπου / φυτευτά και οι στάθμες τους
☒	οπή πλάκας 20 × 20 (αποχέτευση / υδρορροή)

Διαστάσεις σε m, από γωνία / παρειά κολόνας σε γωνία κολόνας. Οι αλυσίδες παρειών μετρήθηκαν από τη γεωμετρία του σχεδίου, οι υπόλοιπες είναι του μελετητή.

ΠΑΤΟΙ ΚΑΛΟΥΠΙΩΝ	στάθμη	ύψος*
Πλάκα h=15	**+6,60**	**2,95**
Πλάκα h=17	**+6,58**	**2,93**
Πλάκα h=20	**+6,55**	**2,90**
Πλάκα h=24	**+6,51**	**2,86**
Πλάκα h=30	**+6,45**	**2,80**
Δοκός ύψους 40	**+6,35**	**2,70**
Δοκός ύψους 50	**+6,25**	**2,60**
Δοκός ύψους 55	**+6,20**	**2,55**

* από την πλάκα του κάτω ορόφου (+3,65). Υπολογισμένα (στάθμη – ύψος)· όχι για ανεστραμμένες δοκούς / φυτευτά.

ΟΠΕΣ ΠΛΑΚΑΣ – ΚΟΥΤΙ 20 × 20
Θέση σε cm ως την ΑΚΜΗ του κουτιού, από παρειές σκυροδέματος.

H6 **ΑΠ1 Φ100** — 20 ανατ. της Δ παρ. K2 · 5 νότια της Ν παρ. K2
H7 **ΑΠ3 Φ100** — 1,95 m ανατ. της Α παρ. Δ6.1 · 1,4 m βόρ. της Β παρ. Δ3.1
H8 **ΑΠ4 Φ75** — 10 ανατ. της Δ παρ. K7 · κολλητά στη Ν παρ. K7
H9 **ΥΔ1 Φ75** — κολλητά στη Α παρ. Δ9.5 · 30 βόρ. της Β παρ. K3
H10 **ΥΔ4 Φ75** — δυτ. ακμή 12 δυτ. της Δ παρ. K1 · 10 βόρ. της Β παρ. K1
H11 **ΥΔ5 Φ75** — 70 ανατ. της Δ παρ. K9 · κολλητά στη Ν παρ. K9
ΥΔ2 κενό 35 cm νότια της K8 – ΚΑΜΙΑ οπή
ΥΔ3 κενό 25 cm δυτικά της K10 – ΚΑΜΙΑ οπή
Τεύχος αποχετεύσεων R19, φύλλο ΑΠ-13.
Καμία οπή σε δοκό, καμία αναμονή σε στηθαίο.

ΣΗΜΕΙΩΣΕΙΣ

· ΤΟΜΗ 2-2: μετόπη +6,45 έως +6,95 (ύψος 0,50 όπως Σ5) – αλλαγή 10/11/2026· ο μελετητής είχε +6,90. Να ενημερωθεί ο στατικός.
· Πρόβολοι: υποδοχή σιφωνιού και υδρορροή ΠΡΙΝ το μπετό, να μην κοπεί οπλισμός (μελετητής).
· Διαγραμμισμένο τοιχείο δίπλα στη σκάλα (0,60): έως το ύψος της σκάλας (μελετητής).

Βάση: Σ4_ΕΦ.pdf – ξυλότυπος οροφής Α΄ ορόφου, Γ. Κόγιας (Drive 19/10/2026).
Οπλισμοί ΜΟΝΟ από το σχέδιο του μελετητή.

Έκδοση R03 – 10/11/2026