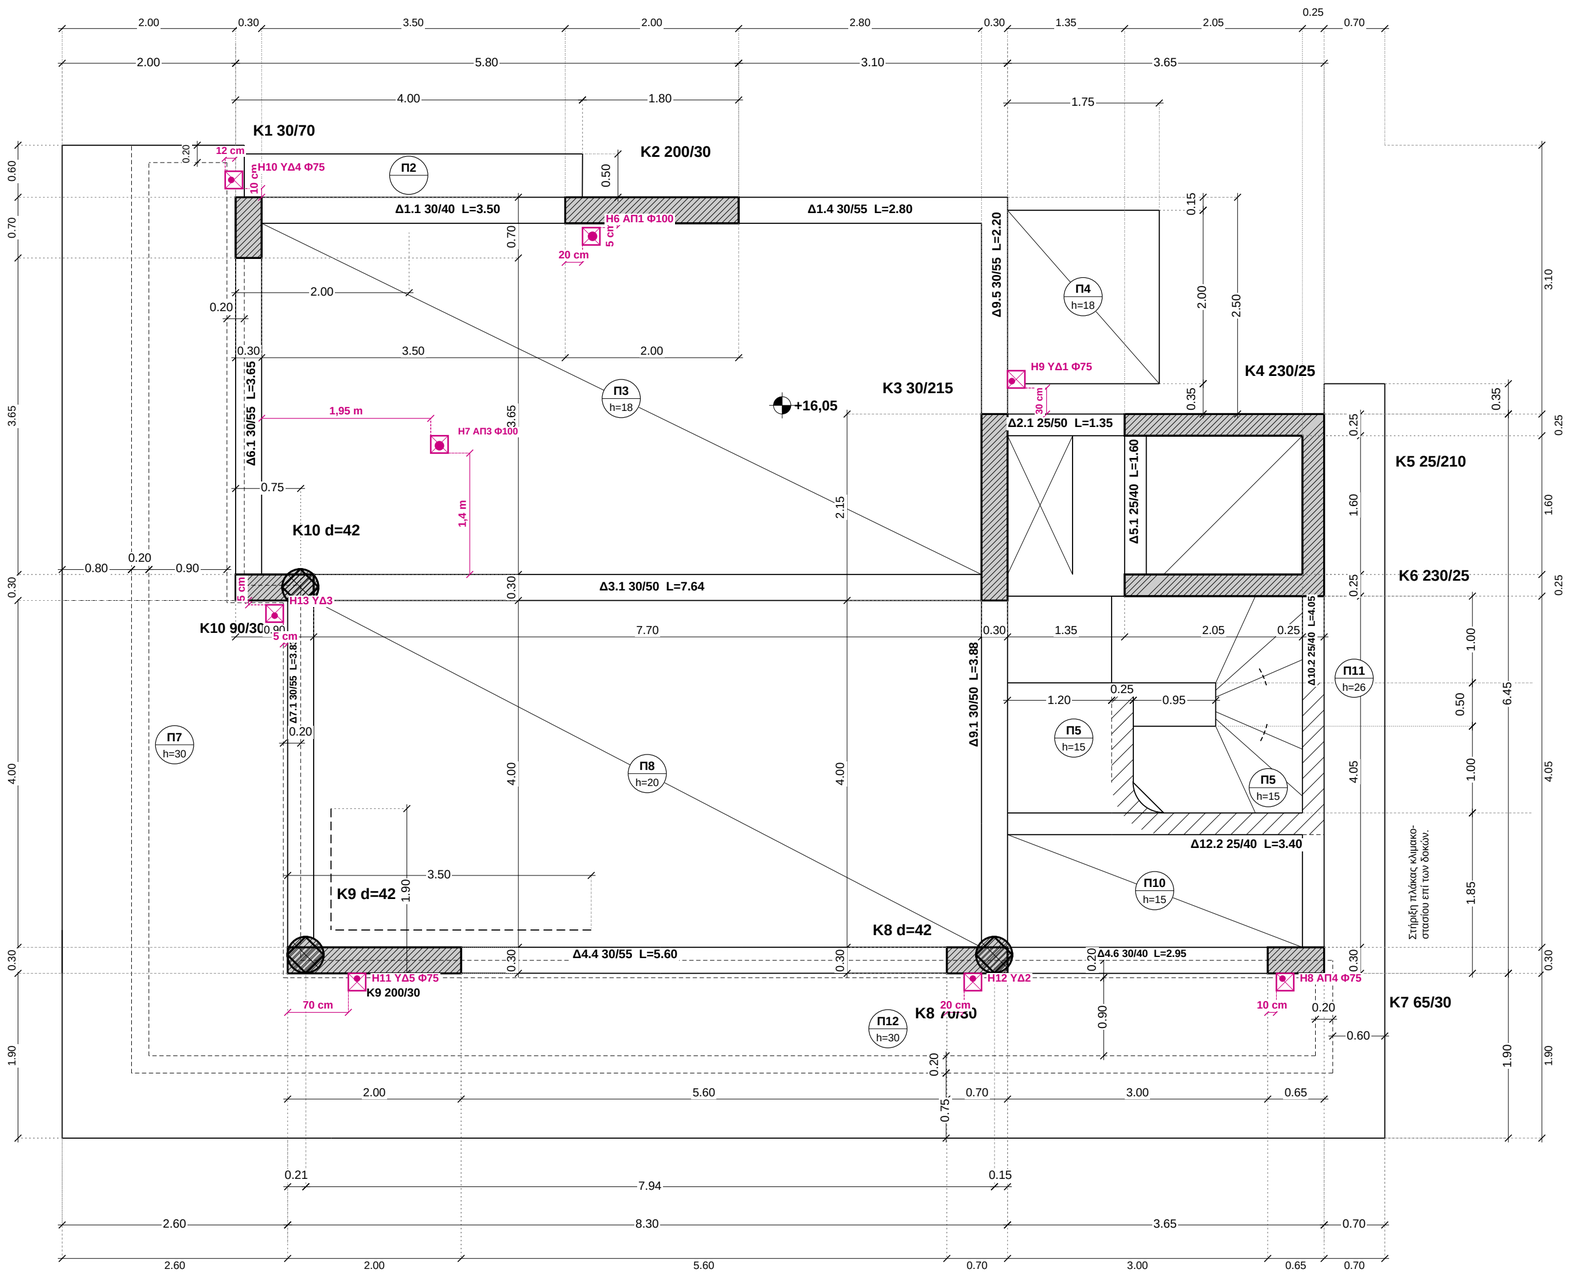


ΚΩΝΣΤΑΝΤΙΝΟΥΠΟΛΕΩΣ 12 & ΑΓ. ΒΑΡΒΑΡΑΣ, ΑΡΓΥΡΟΥΠΟΛΗ – ARKAD I.K.E.
Ξυλότυπος εργοταξίου – χωρίς οπλισμούς

ΞΥΛΟΤΥΠΟΣ ΟΡΟΦΗΣ Δ΄ ΟΡΟΦΟΥ

Σ7

ΣΤΑΘΜΗ ΑΝΩ ΠΛΑΚΑΣ
+16,05
ΚΛΙΜΑΚΑ 1:50
A2 · 100 %
0 1 2 m

K1 30/70	υποστύλωμα / τοιχείο (cm)
Δ1.1 30/40	δοκός: πλάτος / ύψος (το ύψος μαζί με την πλάκα)
L=3.50	καθαρό μήκος δοκού, παρειά με παρειά
Π3 h=15	πλάκα – πάχος (cm)
+0,30	στάθμη άνω μπετού (m)
μπλε	τομές επί τόπου / φυτευτά και οι στάθμες τους
⊠	οπή πλάκας 20 × 20 (αποχέτευση / υδρορροή)

Διαστάσεις σε m, από γωνία / παρειά κολόνας σε γωνία κολόνας. Οι αλυσίδες παρειών μετρήθηκαν από τη γεωμετρία του σχεδίου, οι υπόλοιπες είναι του μελετητή.

ΠΑΤΟΙ ΚΑΛΟΥΠΙΩΝ	στάθμη	ύψος*
Πλάκα h=15	**+15,90**	**2,95**
Πλάκα h=18	**+15,87**	**2,92**
Πλάκα h=20	**+15,85**	**2,90**
Πλάκα h=26	**+15,79**	**2,84**
Πλάκα h=30	**+15,75**	**2,80**
Δοκός ύψους 40	**+15,65**	**2,70**
Δοκός ύψους 50	**+15,55**	**2,60**
Δοκός ύψους 55	**+15,50**	**2,55**

* από την πλάκα του κάτω ορόφου (+12,95). Υπολογισμένα (στάθμη – ύψος)· όχι για ανεστραμμένες δοκούς / φυτευτά.

ΟΠΕΣ ΠΛΑΚΑΣ – ΚΟΥΤΙ 20 × 20
Θέση σε cm ως την ΑΚΜΗ του κουτιού, από παρειές σκυροδέματος.


- **H6 ΑΠ1 Φ100** — 20 ανατ. της Δ παρ. Κ2 · 5 νότια της Ν παρ. Κ2
- **H7 ΑΠ3 Φ100** — 1,95 m ανατ. της Α παρ. Δ6.1 · 1,4 m βόρ. της Β παρ. Δ3.1
- **H8 ΑΠ4 Φ75** — 10 ανατ. της Δ παρ. Κ7 · κολλητά στη Ν παρ. Κ7
- **H9 ΥΔ1 Φ75** — κολλητά στη Α παρ. Δ9.5 · 30 βόρ. της Β παρ. Κ3
- **H10 ΥΔ4 Φ75** — δυτ. ακμή 12 δυτ. της Δ παρ. Κ1 · 10 βόρ. της Β παρ. Κ1
- **H11 ΥΔ5 Φ75** — 70 ανατ. της Δ παρ. Κ9 · κολλητά στη Ν παρ. Κ9
- **H12 ΥΔ2 – σιφώνι δώματος Φ75** — 20 ανατ. της Δ παρ. Κ8 · κολλητά στη Ν παρ. Κ8
- **H13 ΥΔ3 – σιφώνι δώματος Φ75** — 5 δυτ. της Δ παρ. Δ7.1 · 5 νότια της Ν παρ. Κ10

Τεύχος αποχετεύσεων R19, φύλλο ΑΠ-16. Καμία οπή σε δοκό, καμία αναμονή σε στηθαίο.

ΣΗΜΕΙΩΣΕΙΣ

· Πρόβολοι: υποδοχή σιφωνιού και υδρορροή ΠΡΙΝ το μπετό, να μην κοπεί οπλισμός (μελετητής).

ΛΕΠΤΟΜΕΡΕΙΑ ΜΕΛΕΤΗΤΗ
πλάκα στη στάθμη +17,36

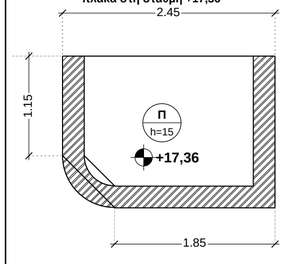

Βάση: Σ7_ΕΦ.pdf – ξυλότυπος οροφής Δ΄ ορόφου, Γ. Κόγιας (Drive 19/10/2026).
Οπλισμοί ΜΟΝΟ από το σχέδιο του μελετητή.

Έκδοση R03 – 10/11/2026