


**ΤΟΜΕΣ ΜΕΤΩΠΩΝ**
(σκαρίφημα χωρίς κλίμακα)

**ΤΟΜΗ 1-1**

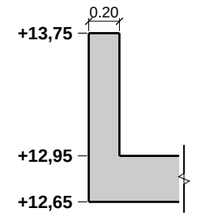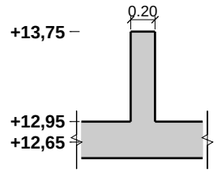


**ΤΟΜΗ 2-2**

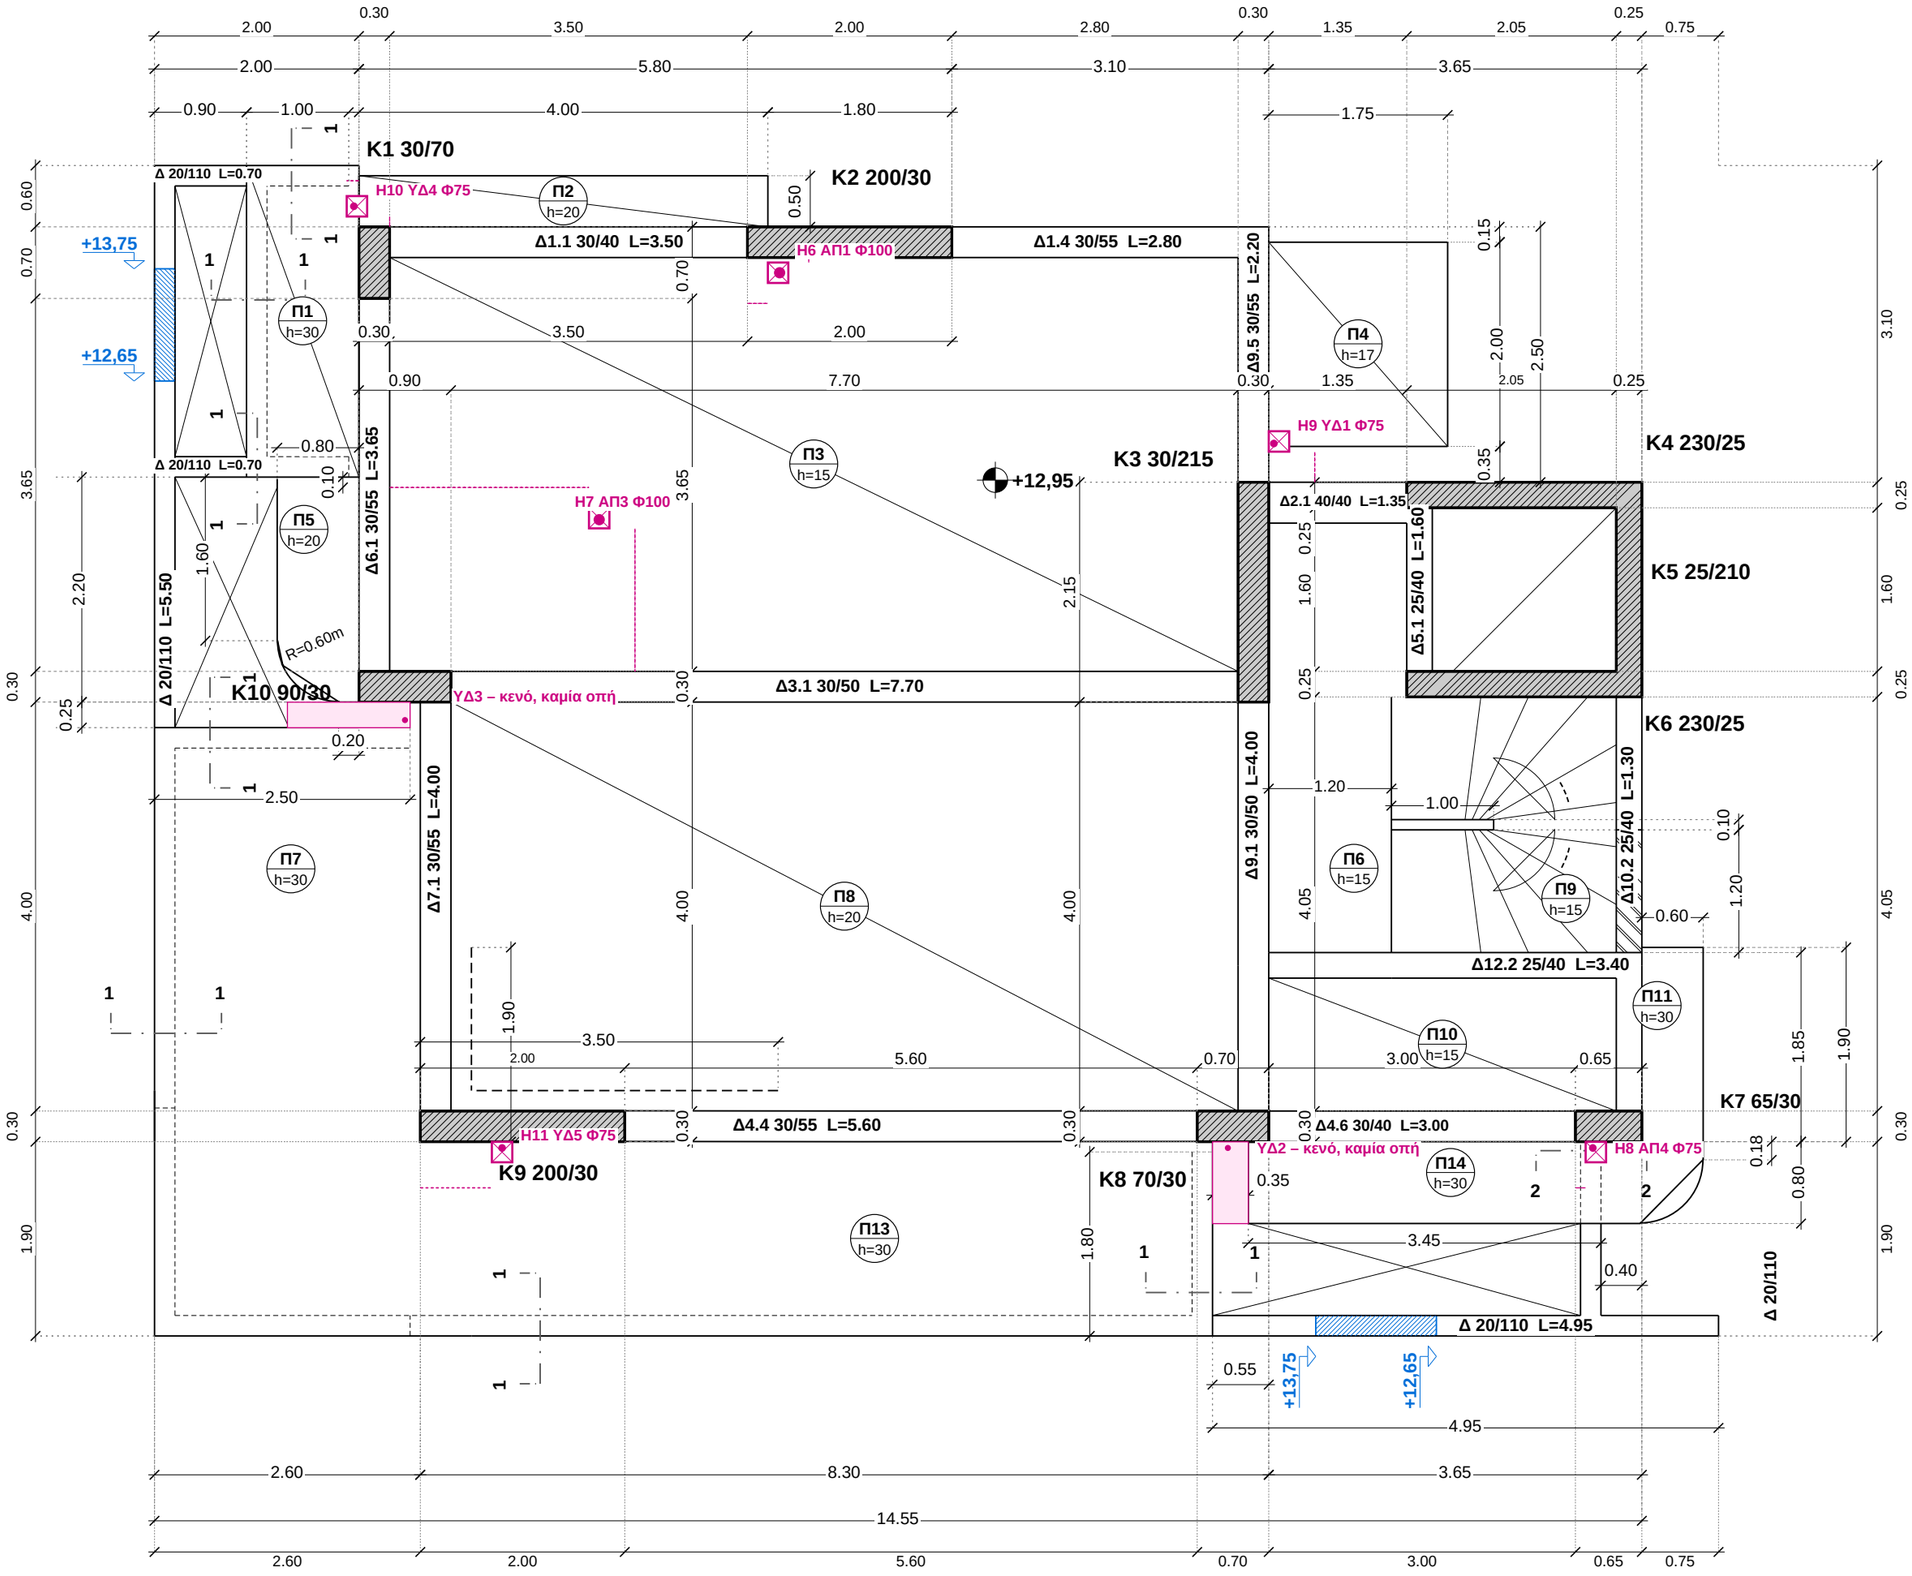


**ΚΩΝΣΤΑΝΤΙΝΟΥΠΟΛΕΩΣ 12 & ΑΓ. ΒΑΡΒΑΡΑΣ, ΑΡΓΥΡΟΥΠΟΛΗ – ARKAD Ι.Κ.Ε.**
Ξυλότυπος εργοταξίου – χωρίς οπλισμούς

# ΞΥΛΟΤΥΠΟΣ ΟΡΟΦΗΣ Γ΄ ΟΡΟΦΟΥ — Σ6

ΣΤΑΘΜΗ ΑΝΩ ΠΛΑΚΑΣ
**+12,95**
**ΚΛΙΜΑΚΑ 1:60** A3 · 100 %
0 1 2 m

**K1 30/70** υποστύλωμα / τοιχείο (cm)
**Δ1.1 30/40** δοκός: πλάτος / ύψος (το ύψος μαζί με την πλάκα)
**L=3.50** καθαρό μήκος δοκού, παρειά με παρειά
**Π3 h=15** πλάκα – πάχος (cm)
**+0,30** στάθμη άνω μπετού (m)
**μπλε** τομές επί τόπου / φυτευτά και οι στάθμες τους
☒ οπή πλάκας 20 × 20 (αποχέτευση / υδρορροή)

Διαστάσεις σε m, από γωνία / παρειά κολόνας σε γωνία κολόνας. Οι αλυσίδες παρειών μετρήθηκαν από τη γεωμετρία του σχεδίου, οι υπόλοιπες είναι του μελετητή.

| ΠΑΤΟΙ ΚΑΛΟΥΠΙΩΝ | στάθμη | ύψος* |
|---|---|---|
| Πλάκα h=15 | **+12,80** | **2,95** |
| Πλάκα h=17 | **+12,78** | **2,93** |
| Πλάκα h=20 | **+12,75** | **2,90** |
| Πλάκα h=30 | **+12,65** | **2,80** |
| Δοκός ύψους 40 | **+12,55** | **2,70** |
| Δοκός ύψους 50 | **+12,45** | **2,60** |
| Δοκός ύψους 55 | **+12,40** | **2,55** |

* από την πλάκα του κάτω ορόφου (+9,85). Υπολογισμένα (στάθμη − ύψος)· όχι για ανεστραμμένες δοκούς / φυτευτά.

ΟΠΕΣ ΠΛΑΚΑΣ – ΚΟΥΤΙ 20 × 20
Θέση σε cm ως την ΑΚΜΗ του κουτιού, από παρειές σκυροδέματος.

**H6** **ΑΠ1 Φ100** — 20 ανατ. της Δ παρ. K2 · 5 νότια της N παρ. K2
**H7** **ΑΠ3 Φ100** — 1,95 m ανατ. της A παρ. Δ6.1 · 1,4 m βόρ. της B παρ. Δ3.1
**H8** **ΑΠ4 Φ75** — 10 ανατ. της Δ παρ. K7 · κολλητά στη N παρ. K7
**H9** **ΥΔ1 Φ75** — κολλητά στη A παρ. Δ9.5 · 30 βόρ. της B παρ. K3
**H10** **ΥΔ4 Φ75** — δυτ. ακμή 12 δυτ. της Δ παρ. K1 · 10 βόρ. της B παρ. K1
**H11** **ΥΔ5 Φ75** — 70 ανατ. της Δ παρ. K9 · κολλητά στη N παρ. K9
**ΥΔ2** κενό 35 cm νότια της K8 – ΚΑΜΙΑ οπή
**ΥΔ3** κενό 25 cm δυτικά της K10 – ΚΑΜΙΑ οπή

**Τεύχος αποχετεύσεων R19, φύλλο ΑΠ-15.**
**Καμία οπή σε δοκό, καμία αναμονή σε στηθαίο.**

ΣΗΜΕΙΩΣΕΙΣ
· Πρόβολοι: υποδοχή σιφωνιού και υδρορροή ΠΡΙΝ το μπετό, να μην κοπεί οπλισμός (μελετητής).
· Διαγραμμισμένο τοιχείο δίπλα στη σκάλα (0,60): έως το ύψος της σκάλας (μελετητής).

Βάση: Σ6_ΕΦ.pdf – ξυλότυπος οροφής Γ΄ ορόφου, Γ. Κόγιας (Drive 19/10/2026).
**Οπλισμοί ΜΟΝΟ από το σχέδιο του μελετητή.**

**Έκδοση R02 – 10/11/2026**