
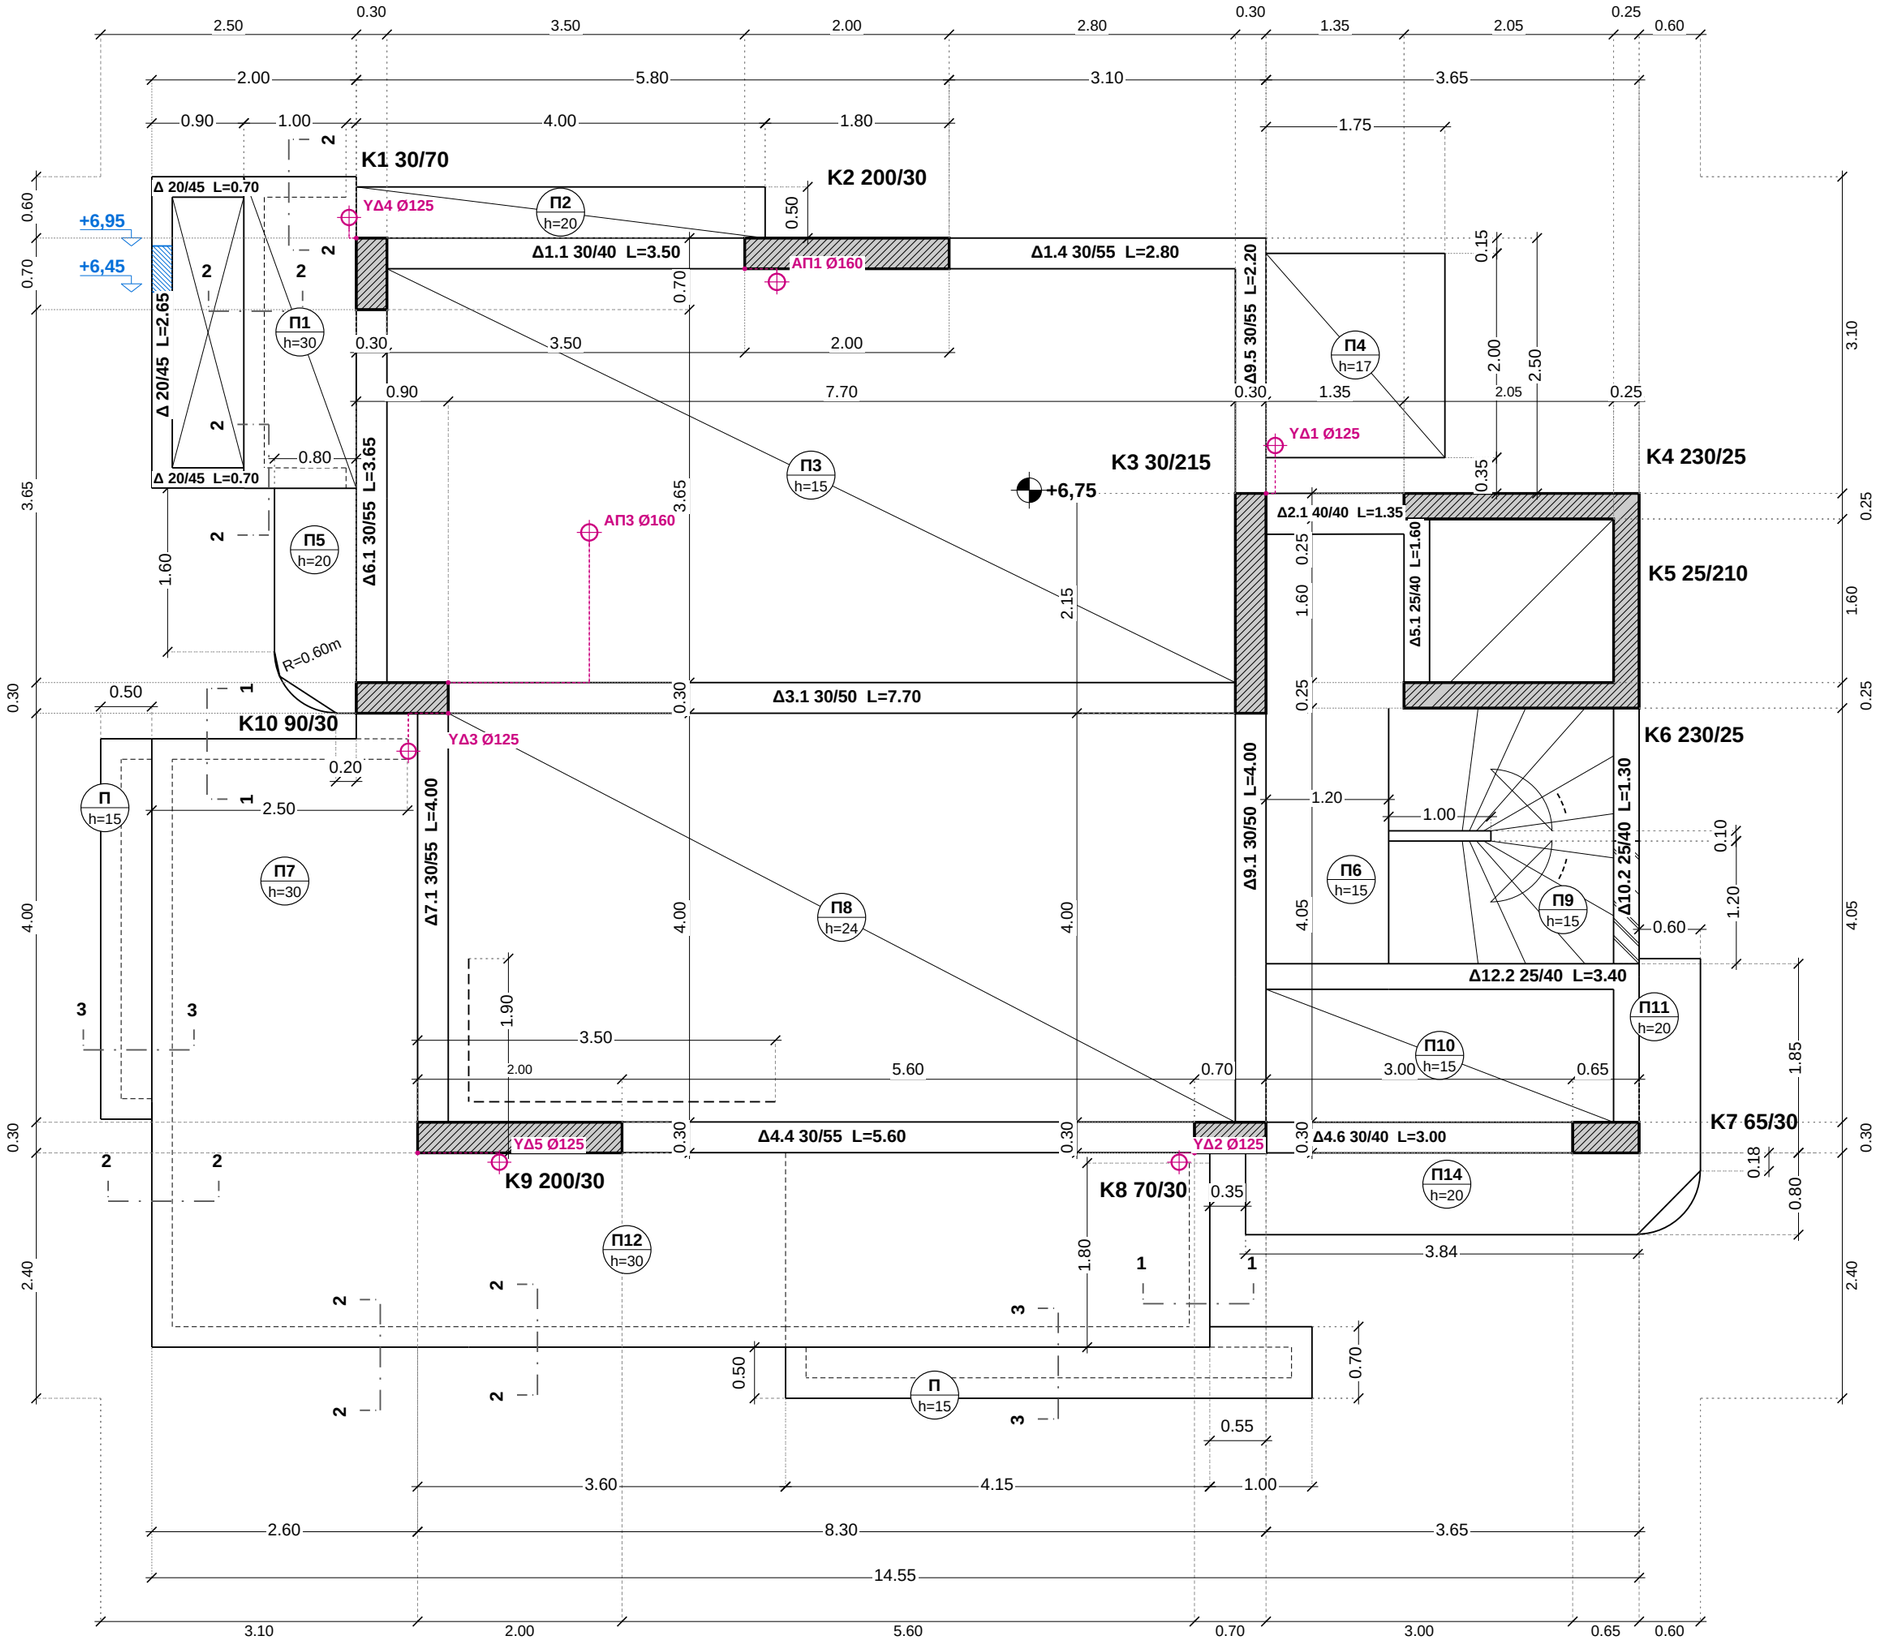



ΤΟΜΕΣ ΜΕΤΩΠΩΝ

(σκαρίφημα χωρίς κλίμακα)


ΤΟΜΗ 1-1

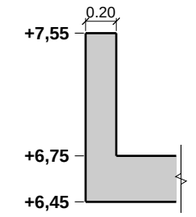

ΤΟΜΗ 2-2

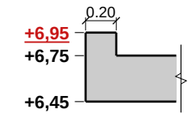

ΤΟΜΗ 3-3

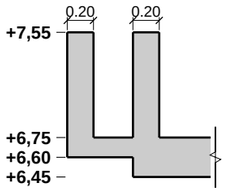

ΚΩΝΣΤΑΝΤΙΝΟΥΠΟΛΕΩΣ 12 & ΑΓ. ΒΑΡΒΑΡΑΣ, ΑΡΓΥΡΟΥΠΟΛΗ – ARKAD Ι.Κ.Ε.
Ξυλότυπος εργοταξίου – χωρίς οπλισμούς

ΞΥΛΟΤΥΠΟΣ ΟΡΟΦΗΣ Α΄ ΟΡΟΦΟΥ — Σ4

ΣΤΑΘΜΗ ΑΝΩ ΠΛΑΚΑΣ
+6,75
ΚΛΙΜΑΚΑ 1:60 A3 · 100 %

0 1 2 m

K1 30/70	υποστύλωμα / τοιχείο (cm)
Δ1.1 30/40	δοκός: πλάτος / ύψος (το ύψος μαζί με την πλάκα)
L=3.50	καθαρό μήκος δοκού, παρειά με παρειά
Π3 h=15	πλάκα – πάχος (cm)
+0,30	στάθμη άνω μπετού (m)
μπλε	τομές επί τόπου / φυτευτά και οι στάθμες τους
⌖	οπή (χιτώνιο) αποχέτευσης / υδρορροής

Διαστάσεις σε m, από γωνία / παρειά κολόνας σε γωνία κολόνας. Οι αλυσίδες παρειών μετρήθηκαν από τη γεωμετρία του σχεδίου, οι υπόλοιπες είναι του μελετητή.

ΠΑΤΟΙ ΚΑΛΟΥΠΙΩΝ	στάθμη	ύψος*
Πλάκα h=15	**+6,60**	**2,95**
Πλάκα h=17	**+6,58**	**2,93**
Πλάκα h=20	**+6,55**	**2,90**
Πλάκα h=24	**+6,51**	**2,86**
Πλάκα h=30	**+6,45**	**2,80**
Δοκός ύψους 40	**+6,35**	**2,70**
Δοκός ύψους 50	**+6,25**	**2,60**
Δοκός ύψους 55	**+6,20**	**2,55**

* από την πλάκα του κάτω ορόφου (+3,65). Υπολογισμένα (στάθμη − ύψος)· όχι για ανεστραμμένες δοκούς / φυτευτά.

ΟΠΕΣ – ΚΕΝΤΡΟ ΑΠΟ ΓΩΝΙΑ ΚΟΛΟΝΑΣ (m)

ΑΠ1 Ø160 στήλη λουτρού
→ 0,31 ↓ 0,13 από κάτω-αριστ. γωνία K2
ΑΠ3 Ø160 στήλη λουτρού γονέων
→ 1,38 ↑ 1,47 από πάνω-δεξιά γωνία K10
ΥΔ1 Ø125 υδρορροή ΒΑ εξώστη
→ 0,09 ↑ 0,47 από πάνω-δεξιά γωνία K3
ΥΔ2 Ø125 υδρορροή Ν
← 0,15 ↓ 0,09 από κάτω-αριστ. γωνία K8
ΥΔ3 Ø125 υδρορροή Δ
← 0,39 ↓ 0,37 από κάτω-δεξιά γωνία K10
ΥΔ4 Ø125 υδρορροή ΒΔ
← 0,07 ↑ 0,20 από πάνω-αριστ. γωνία K1
ΥΔ5 Ø125 υδρορροή Ν
→ 0,80 ↓ 0,09 από κάτω-αριστ. γωνία K9

Θέσεις κατά το τεύχος αποχετεύσεων R12 (27/10/2026) – ΕΠΙΒΕΒΑΙΩΣΗ ΠΡΙΝ ΤΟ ΜΠΕΤΟ. Καμία οπή σε δοκό.

ΣΗΜΕΙΩΣΕΙΣ

· ΤΟΜΗ 2-2: μετόπη +6,45 έως +6,95 (ύψος 0,50 όπως Σ5) – αλλαγή 10/11/2026· ο μελετητής είχε +6,90. Να ενημερωθεί ο στατικός.
· Πρόβολοι: υποδοχή σιφωνιού και υδρορροή ΠΡΙΝ το μπετό, να μην κοπεί οπλισμός (μελετητής).
· Διαγραμμισμένο τοιχείο δίπλα στη σκάλα (0,60): έως το ύψος της σκάλας (μελετητής).

Βάση: Σ4_ΕΦ.pdf – ξυλότυπος οροφής Α΄ ορόφου, Γ. Κόγιας (Drive 19/10/2026).
Οπλισμοί ΜΟΝΟ από το σχέδιο του μελετητή.

Έκδοση R01 – 10/11/2026