
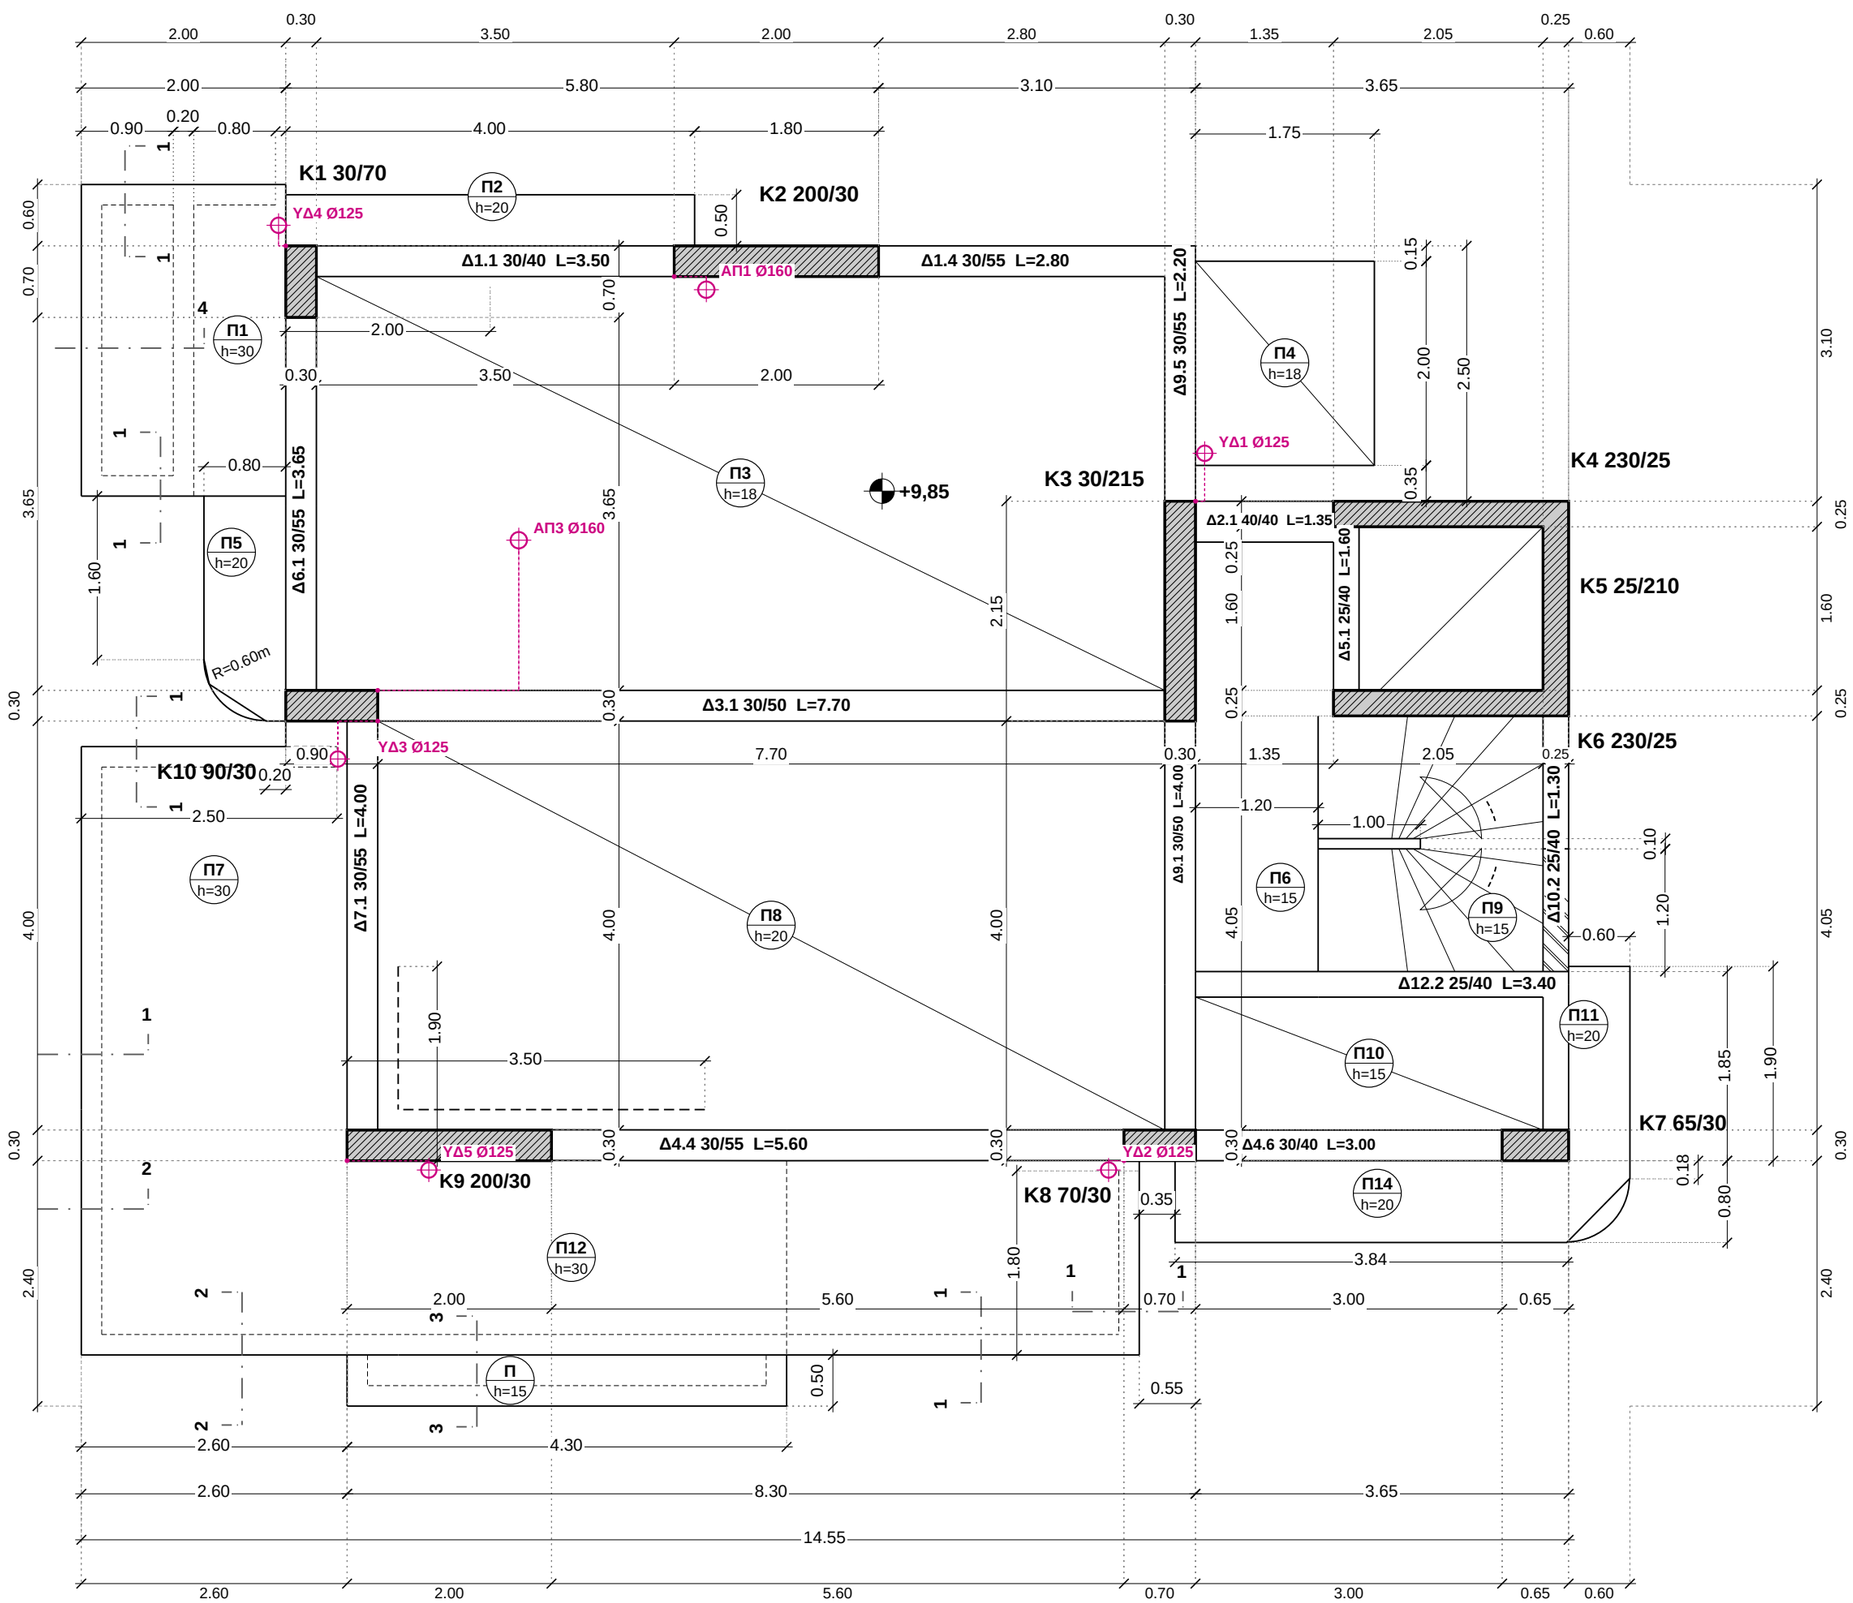



ΤΟΜΕΣ ΜΕΤΩΠΩΝ

(σκαρίφημα χωρίς κλίμακα)


ΤΟΜΗ 1-1

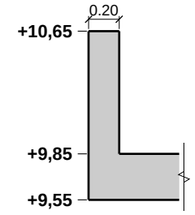


ΤΟΜΗ 2-2

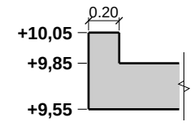

ΤΟΜΗ 3-3

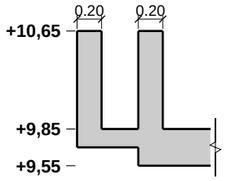

ΤΟΜΗ 4-4

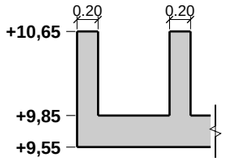

ΚΩΝΣΤΑΝΤΙΝΟΥΠΟΛΕΩΣ 12 & ΑΓ. ΒΑΡΒΑΡΑΣ, ΑΡΓΥΡΟΥΠΟΛΗ – ARKAD I.K.E.
Ξυλότυπος εργοταξίου – χωρίς οπλισμούς

ΞΥΛΟΤΥΠΟΣ ΟΡΟΦΗΣ Β΄ ΟΡΟΦΟΥ — Σ5

ΣΤΑΘΜΗ ΑΝΩ ΠΛΑΚΑΣ
+9,85

ΚΛΙΜΑΚΑ 1:60 A3 · 100 %

0 1 2 m

K1 30/70	υποστύλωμα / τοιχείο (cm)
Δ1.1 30/40	δοκός: πλάτος / ύψος (το ύψος μαζί με την πλάκα)
L=3.50	καθαρό μήκος δοκού, παρειά με παρειά
Π3 h=15	πλάκα – πάχος (cm)
+0,30	στάθμη άνω μπετού (m)
μπλε	τομές επί τόπου / φυτευτά και οι στάθμες τους
⊕	οπή (χιτώνιο) αποχέτευσης / υδρορροής

Διαστάσεις σε m, από γωνία / παρειά κολόνας σε γωνία κολόνας. Οι αλυσίδες παρειών μετρήθηκαν από τη γεωμετρία του σχεδίου, οι υπόλοιπες είναι του μελετητή.

ΠΑΤΟΙ ΚΑΛΟΥΠΙΩΝ	στάθμη	ύψος*
Πλάκα h=15	**+9,70**	**2,95**
Πλάκα h=18	**+9,67**	**2,92**
Πλάκα h=20	**+9,65**	**2,90**
Πλάκα h=30	**+9,55**	**2,80**
Δοκός ύψους 40	**+9,45**	**2,70**
Δοκός ύψους 50	**+9,35**	**2,60**
Δοκός ύψους 55	**+9,30**	**2,55**

* από την πλάκα του κάτω ορόφου (+6,75). Υπολογισμένα (στάθμη − ύψος)· όχι για ανεστραμμένες δοκούς / φυτευτά.

ΟΠΕΣ – ΚΕΝΤΡΟ ΑΠΟ ΓΩΝΙΑ ΚΟΛΟΝΑΣ (m)

- **ΑΠ1 Ø160** στήλη λουτρού — → 0,31 ↓ 0,13 από κάτω-αριστ. γωνία K2
- **ΑΠ3 Ø160** στήλη λουτρού γονέων — → 1,38 ↑ 1,47 από πάνω-δεξιά γωνία K10
- **ΥΔ1 Ø125** υδρορροή ΒΑ εξώστη — → 0,09 ↑ 0,47 από πάνω-δεξιά γωνία K3
- **ΥΔ2 Ø125** υδρορροή Ν — ← 0,15 ↓ 0,09 από κάτω-αριστ. γωνία K8
- **ΥΔ3 Ø125** υδρορροή Δ — ← 0,39 ↓ 0,37 από κάτω-δεξιά γωνία K10
- **ΥΔ4 Ø125** υδρορροή ΒΔ — ← 0,07 ↑ 0,20 από πάνω-αριστ. γωνία K1
- **ΥΔ5 Ø125** υδρορροή Ν — → 0,80 ↓ 0,09 από κάτω-αριστ. γωνία K9

Θέσεις κατά το τεύχος αποχετεύσεων R12 (27/10/2026) – ΕΠΙΒΕΒΑΙΩΣΗ ΠΡΙΝ ΤΟ ΜΠΕΤΟ. Καμία οπή σε δοκό.

ΣΗΜΕΙΩΣΕΙΣ

- Πρόβολοι: υποδοχή σιφωνιού και υδρορροή ΠΡΙΝ το μπετό, να μην κοπεί οπλισμός (μελετητής).
- Διαγραμμισμένο τοιχείο δίπλα στη σκάλα (0,60): έως το ύψος της σκάλας (μελετητής).

Βάση: Σ5_ΕΦ.pdf – ξυλότυπος οροφής Β΄ ορόφου, Γ. Κόγιας (Drive 19/10/2026).
Οπλισμοί ΜΟΝΟ από το σχέδιο του μελετητή.

Έκδοση R01 – 10/11/2026