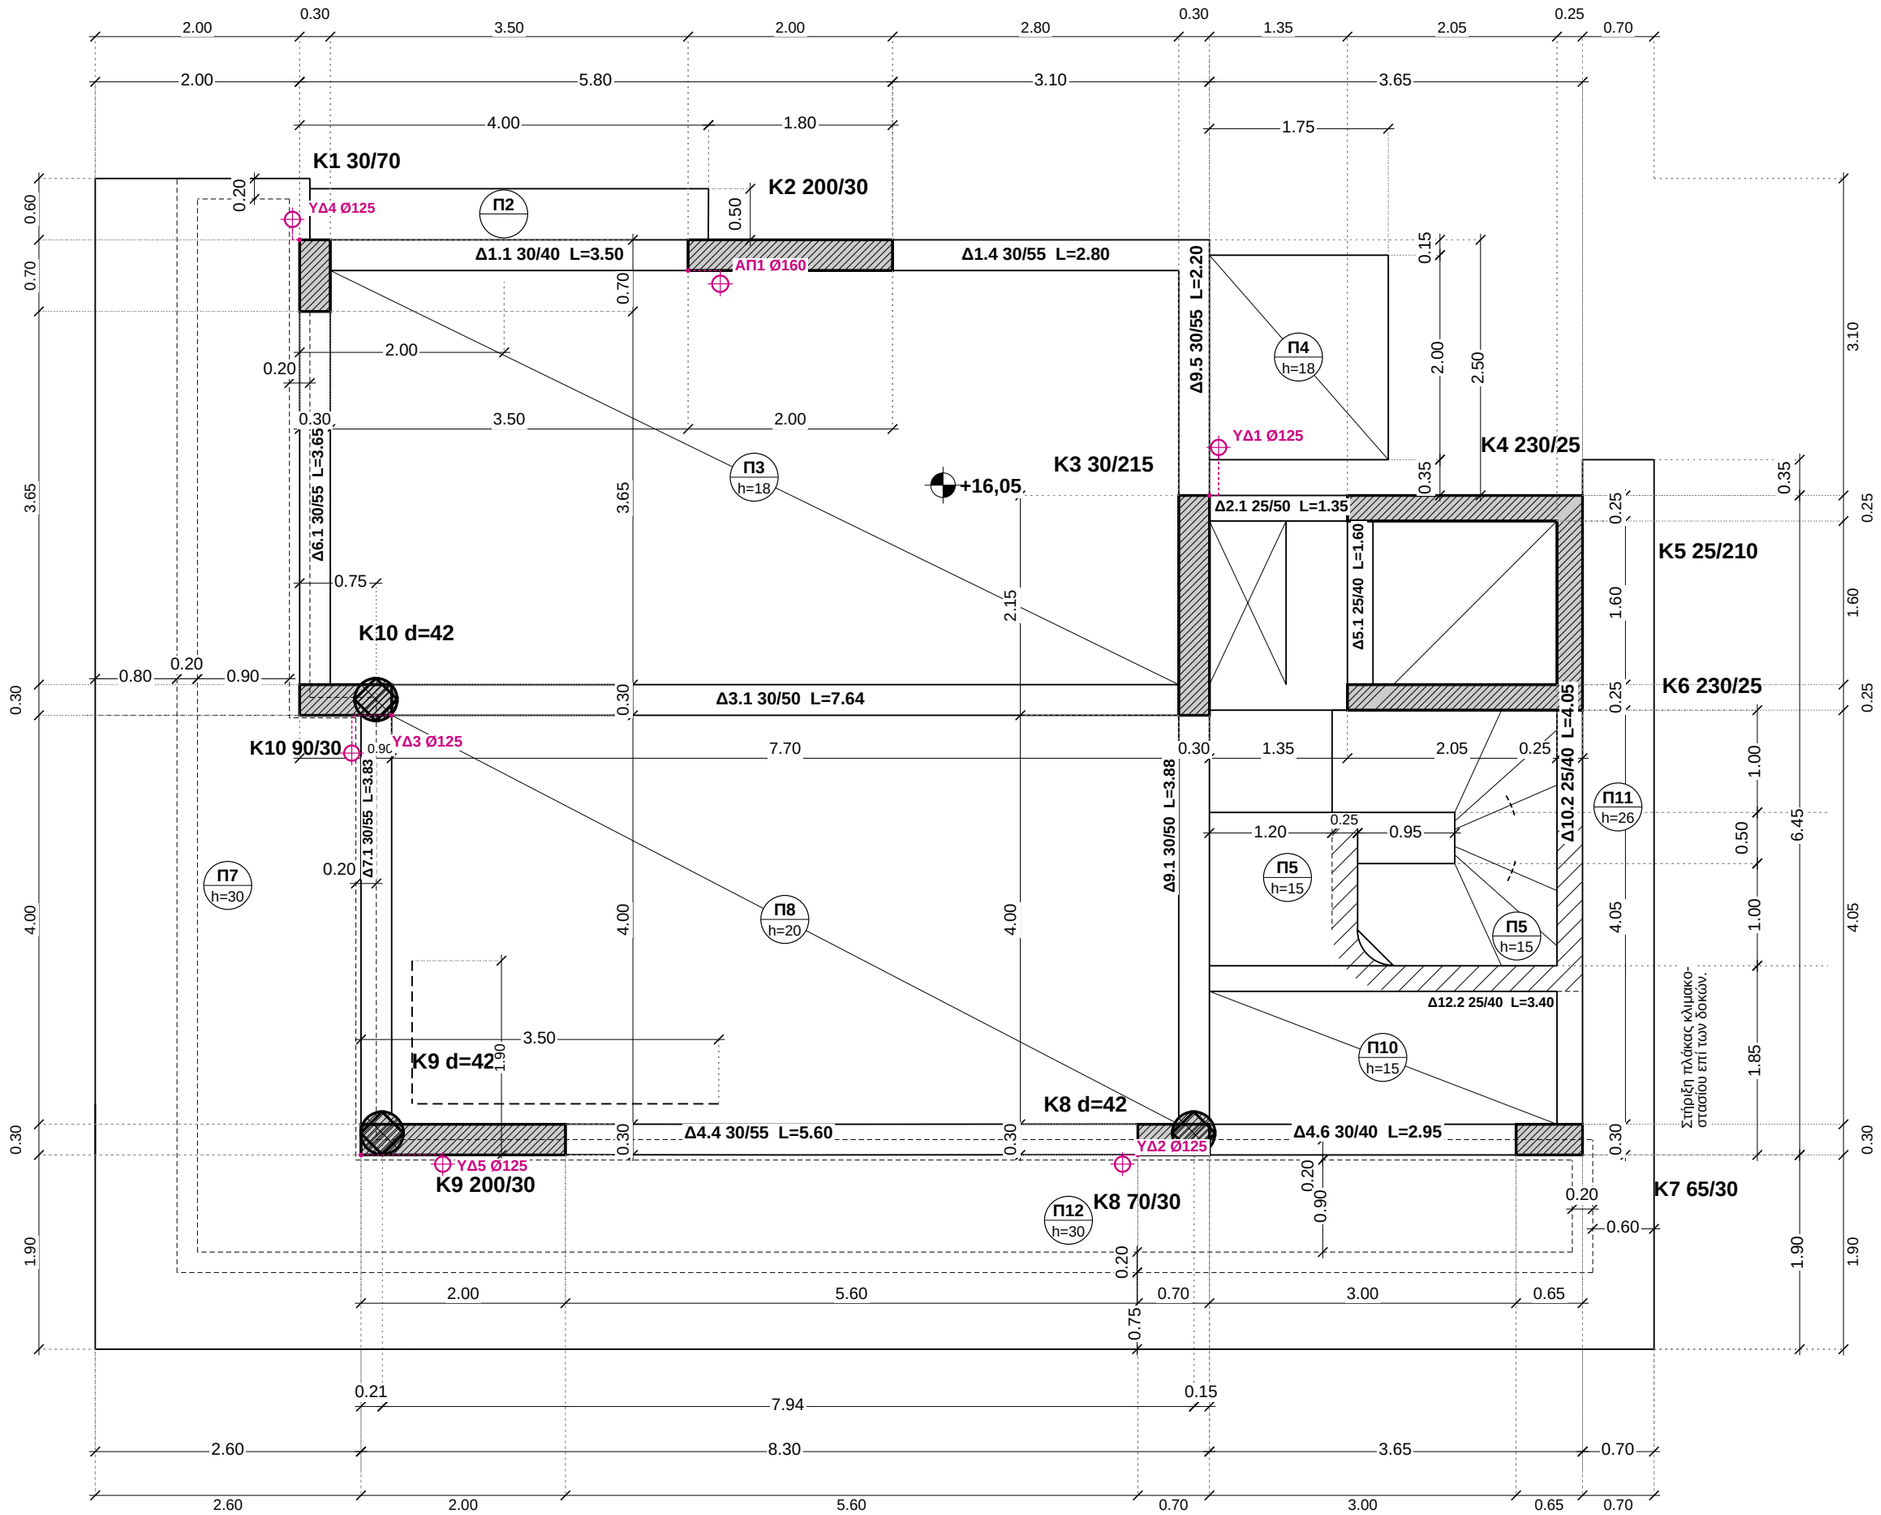


ΚΩΝΣΤΑΝΤΙΝΟΥΠΟΛΕΩΣ 12 & ΑΓ. ΒΑΡΒΑΡΑΣ, ΑΡΓΥΡΟΥΠΟΛΗ – ARKAD I.K.E.
Ξυλότυπος εργοταξίου – χωρίς οπλισμούς

ΞΥΛΟΤΥΠΟΣ ΟΡΟΦΗΣ Δ΄ ΟΡΟΦΟΥ

Σ7

ΣΤΑΘΜΗ ΑΝΩ ΠΛΑΚΑΣ
+16,05
ΚΛΙΜΑΚΑ 1:60
A3 · 100 %
0 1 2 m

K1 30/70 υποστύλωμα / τοιχείο (cm)
Δ1.1 30/40 δοκός: πλάτος / ύψος (το ύψος μαζί με την πλάκα)
L=3.50 καθαρό μήκος δοκού, παρειά με παρειά
Π3 h=15 πλάκα – πάχος (cm)
+0,30 στάθμη άνω μπετού (m)
μπλε τομές επί τόπου / φυτευτά και οι στάθμες τους
οπή (χιτώνιο) αποχέτευσης / υδρορροής
Διαστάσεις σε m, από γωνία / παρειά κολόνας σε γωνία κολόνας. Οι αλυσίδες παρειών μετρήθηκαν από τη γεωμετρία του σχεδίου, οι υπόλοιπες είναι του μελετητή.


ΠΑΤΟΙ ΚΑΛΟΥΠΙΩΝ	στάθμη	ύψος*
Πλάκα h=15	**+15,90**	**2,95**
Πλάκα h=18	**+15,87**	**2,92**
Πλάκα h=20	**+15,85**	**2,90**
Πλάκα h=26	**+15,79**	**2,84**
Πλάκα h=30	**+15,75**	**2,80**
Δοκός ύψους 40	**+15,65**	**2,70**
Δοκός ύψους 50	**+15,55**	**2,60**
Δοκός ύψους 55	**+15,50**	**2,55**

* από την πλάκα του κάτω ορόφου (+12,95). Υπολογισμένα (στάθμη − ύψος)· όχι για ανεστραμμένες δοκούς / φυτευτά.

ΟΠΕΣ – ΚΕΝΤΡΟ ΑΠΟ ΓΩΝΙΑ ΚΟΛΟΝΑΣ (m)
ΑΠ1 Ø160 στήλη λουτρού
→ 0,31 ↓ 0,13 από κάτω-αριστ. γωνία K2
ΥΔ1 Ø125 υδρορροή ΒΑ εξώστη
→ 0,09 ↑ 0,47 από πάνω-δεξιά γωνία K3
ΥΔ2 Ø125 υδρορροή Ν
← 0,15 ↓ 0,09 από κάτω-αριστ. γωνία K8
ΥΔ3 Ø125 υδρορροή Δ
← 0,39 ↓ 0,37 από κάτω-δεξιά γωνία K10
ΥΔ4 Ø125 υδρορροή ΒΔ
← 0,07 ↑ 0,20 από πάνω-αριστ. γωνία K1
ΥΔ5 Ø125 υδρορροή Ν
→ 0,80 ↓ 0,09 από κάτω-αριστ. γωνία K9
Θέσεις κατά το τεύχος αποχετεύσεων R12 (27/10/2026) – ΕΠΙΒΕΒΑΙΩΣΗ ΠΡΙΝ ΤΟ ΜΠΕΤΟ. Καμία οπή σε δοκό.

ΣΗΜΕΙΩΣΕΙΣ
· Πρόβολοι: υποδοχή σιφωνιού και υδρορροή ΠΡΙΝ το μπετό, να μην κοπεί οπλισμός (μελετητής).

ΛΕΠΤΟΜΕΡΕΙΑ ΜΕΛΕΤΗΤΗ
πλάκα στη στάθμη +17,36

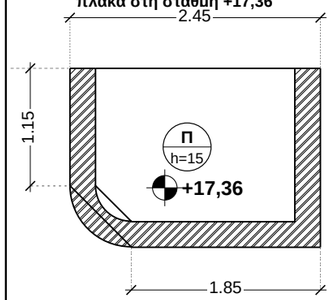

Βάση: Σ7_ΕΦ.pdf – ξυλότυπος οροφής Δ΄ ορόφου, Γ. Κόγιας (Drive 19/10/2026).
Οπλισμοί ΜΟΝΟ από το σχέδιο του μελετητή.

Έκδοση R01 – 10/11/2026