ΑΛΛΑΓΕΣ R15 (05/11/2026)

- Ντουλάπες χωνευτές: δωματίων 0,60 · πλυντηρίου 0,70
- Τ1-05 κομμένος στο 1,35 · Τ3-06 καταργήθηκε · W2.06 → 1,35–2,35 (*)
- Υπν.1: κουτί Τ2-09 (x 4,30–4,40) για χωνευτή ντουλάπα
- Τ2-05 → Τ2Ν-02 (1 φύλλο προς ντουλάπα)
- Λουτρά: πάγκος 0,50 · λεκάνη · 1 διαχωριστικό ντους
- Αλυσίδες διαστάσεων μέσα στους χώρους (χάραξη)

(*) προς επιβεβαίωση από τον αρχιτέκτονα (όψη)

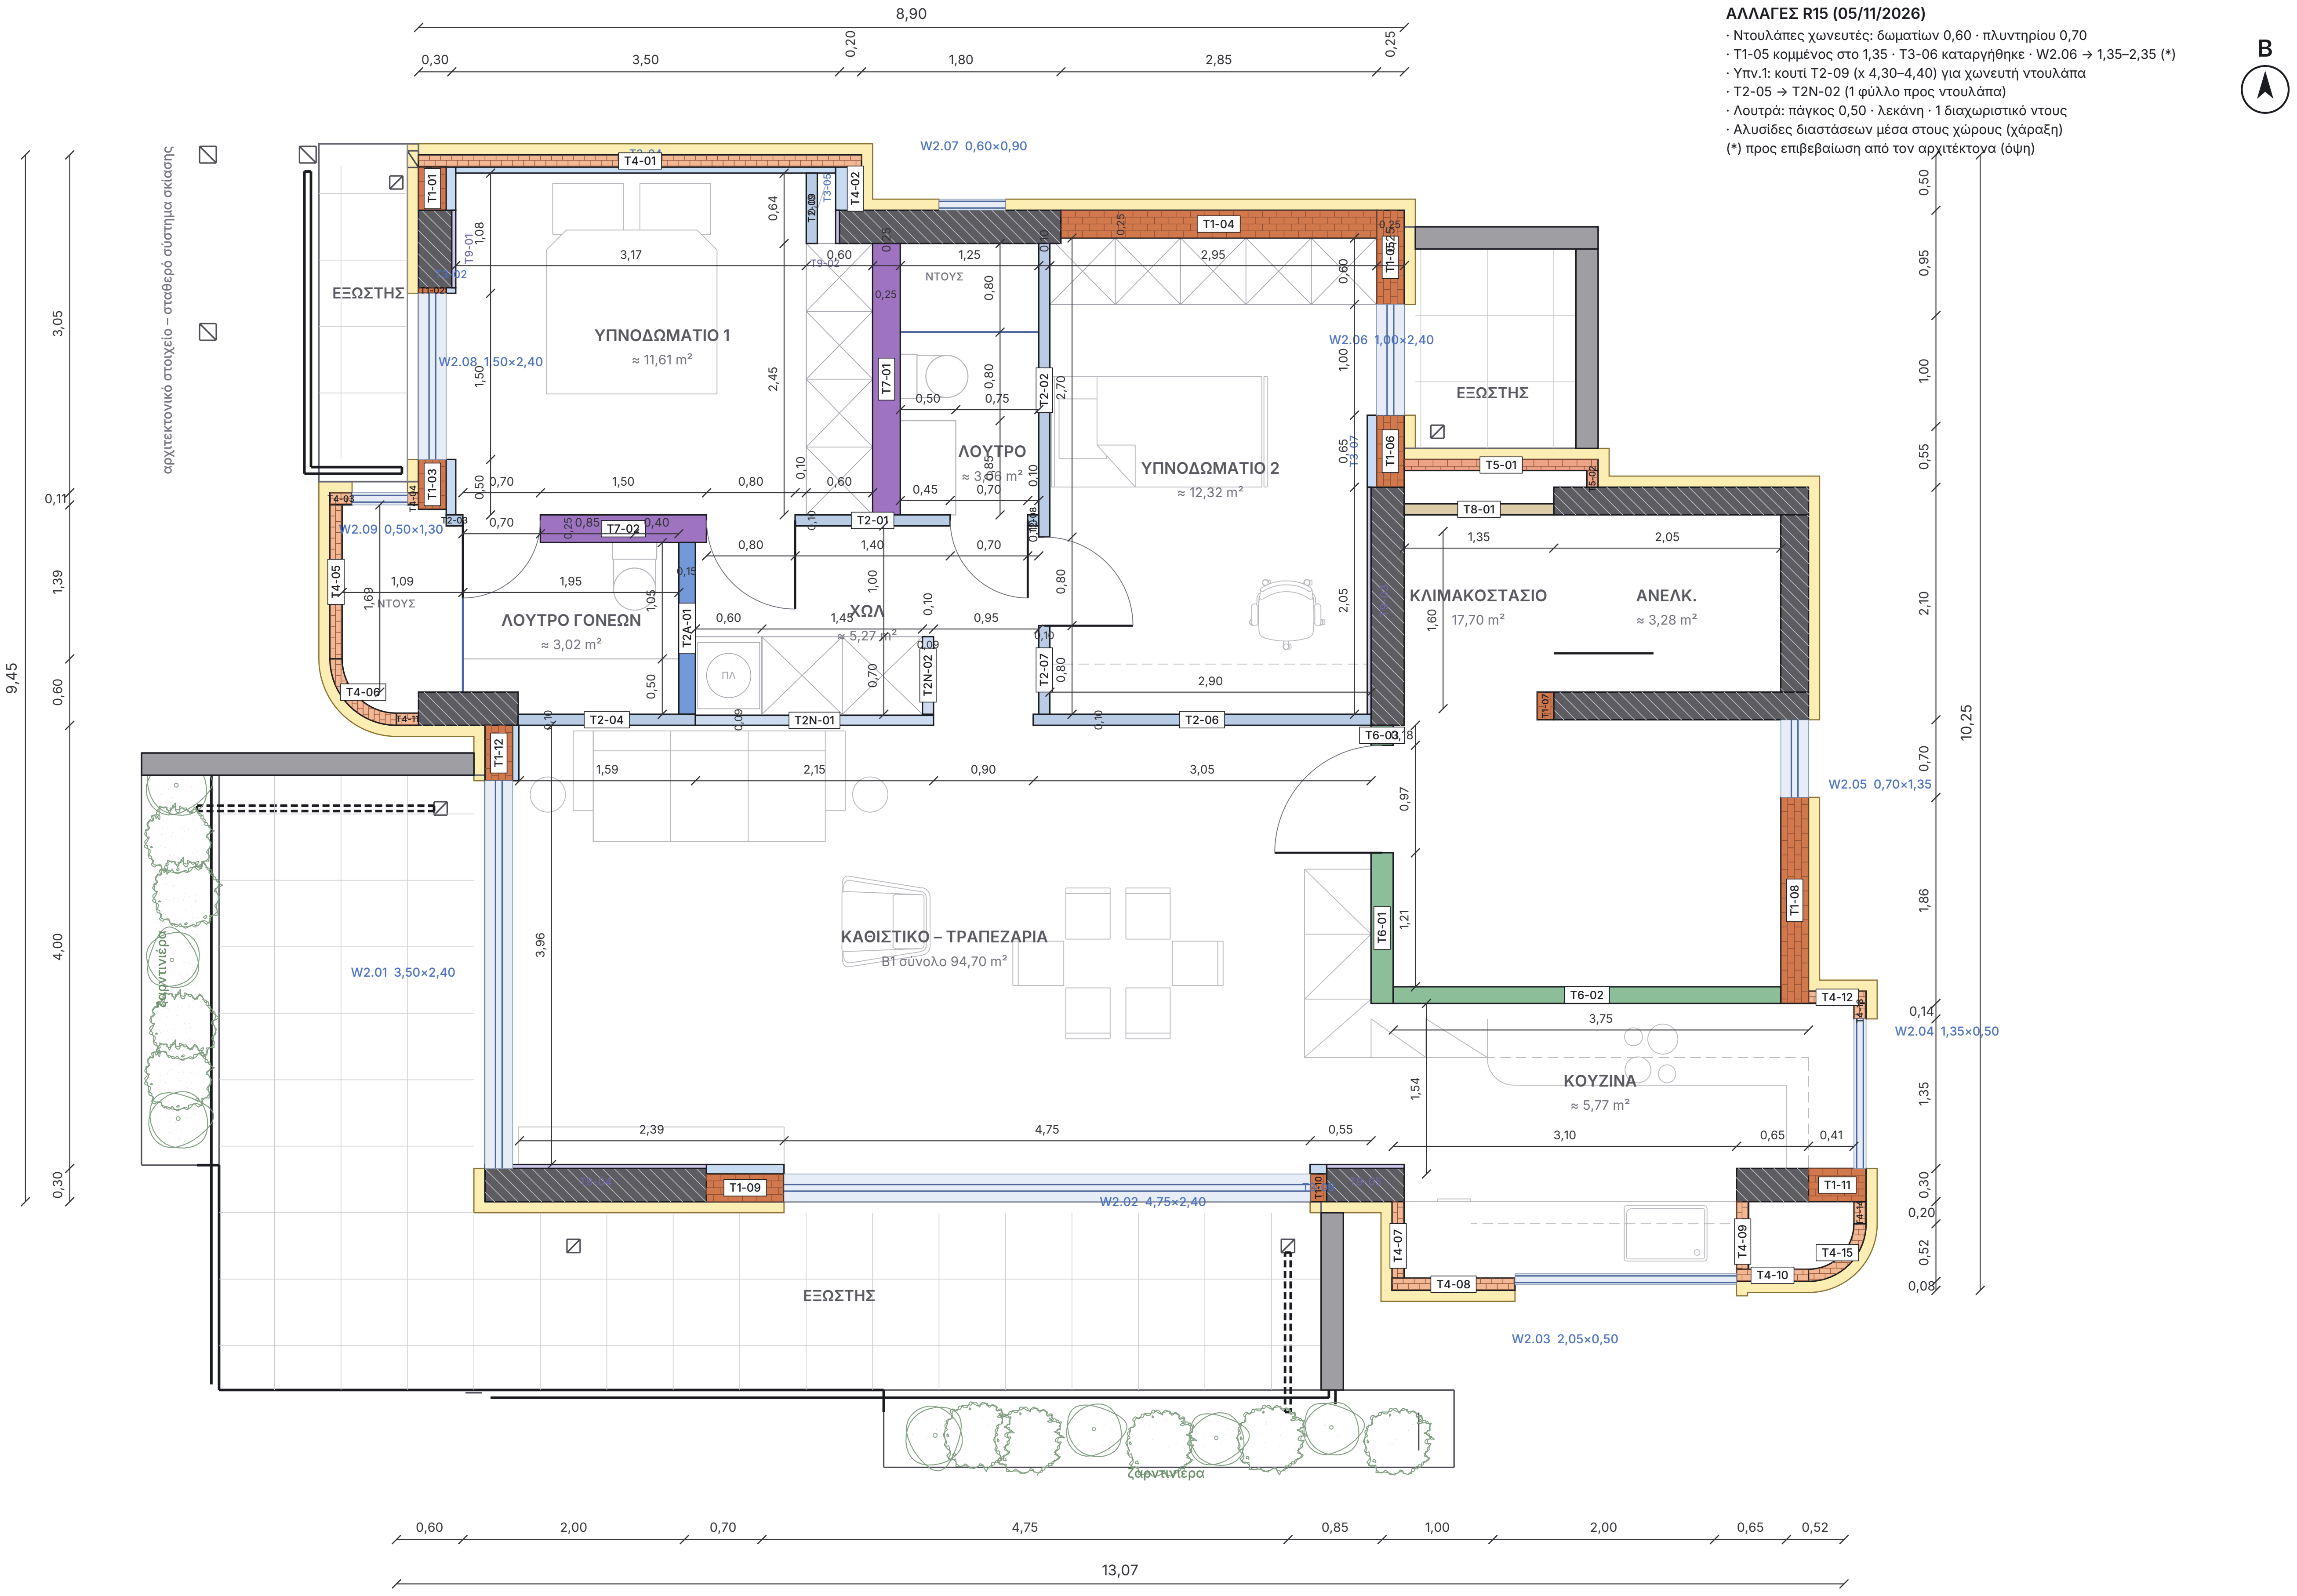

ΕΡΓΟ

ΠΕΝΤΑΟΡΟΦΟ ΚΤΗΡΙΟ ΚΑΤΟΙΚΙΩΝ – ΑΡΓΥΡΟΥΠΟΛΗ
Κωνσταντινουπόλεως 12 & Αγ. Βαρβάρας · Ο.Τ. 103-15
Εργοδότης: INTERKAT Α.Ε. · Κατασκευή: ARKAD Ι.Κ.Ε.

ΘΕΜΑ ΣΧΕΔΙΟΥ

ΚΑΤΟΨΗ ΤΟΙΧΟΠΟΙΙΩΝ – Β΄ ΟΡΟΦΟΣ
Είδη τοιχοποιιών · διαστάσεις χάραξης · κουφώματα · εξώστες
Β΄ ΟΡΟΦΟΣ – Β1

ΒΑΣΗ

Βάση: κάτοψη Α-10-2F (μελέτη εφαρμογής) · ξυλότυποι Σ · R14 + αλλαγές 05/11

ΑΡ. ΣΧΕΔΙΟΥ

T-01
Κλίμακα 1:60 · A3
05/11/2026 · R15

🟧 **T1** Εξωτερική οπτοπλινθοδομή 1:4

πάχος 25 cm

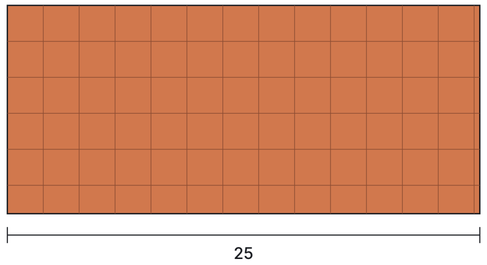

θερμομονωτικό τούβλο κάθετων οπών 25 cm · θερμοπρόσοψη 10 cm έξω · επένδυση T3 μέσα όπου σημειώνεται

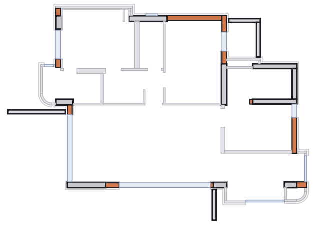

Τοίχοι: T1-01, T1-02, T1-03, T1-04, T1-05, T1-06, T1-07, T1-08, T1-09, T1-10, T1-11, T1-12

Μήκος 9,52 m · επιφάνεια ≈ 27,6 m²

🟧 **T4** Έρκερ – απλή οπτοπλινθοδομή 1:4

πάχος 11 cm

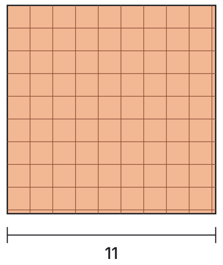

απλό τούβλο 6οπο 9 × 12 × 19 δρομικό ≈ 11 cm · σταθερή η εξωτερική παρειά · θερμοπρόσοψη 10 cm έξω

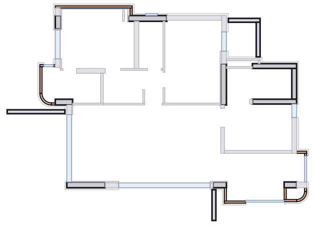

Τοίχοι: T4-01, T4-02, T4-03, T4-04, T4-05, T4-06, T4-07, T4-08, T4-09, T4-10, T4-11, T4-12, T4-13, T4-14, T4-15

Μήκος 12,02 m · επιφάνεια ≈ 34,8 m²

🟧 **T5** Οπτοπλινθοδομή πυρήνα 1:4

πάχος 10 cm

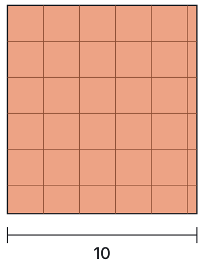

θερμομονωτικό τούβλο κάθετων οπών 10 cm · γύρω από τον πυρήνα (ανελκυστήρας – ηλεκτροστάσιο)

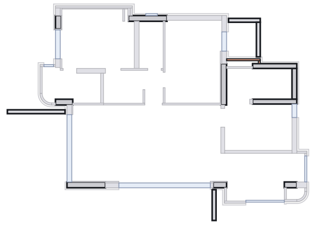

Τοίχοι: T5-01, T5-02

Μήκος 1,90 m · επιφάνεια ≈ 5,5 m²

🟦 **T3** Επένδυση τοίχου 1:4

πάχος 5,5 cm

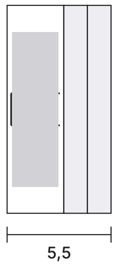

σκελετός 30 · 2 × γυψοσανίδα 12,5 · στις εσωτερικές παρειές των T1 – ΟΧΙ όπου πλακάκι ή ντουλάπα, ΟΧΙ στα έρκερ

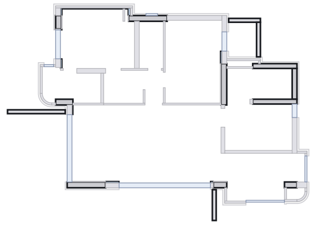

Τοίχοι: T3-01, T3-02, T3-03, T3-04, T3-05, T3-07, T3-08, T3-09, T3-10

Μήκος 6,80 m · επιφάνεια ≈ 19,7 m²

🟪 **T9** Επένδυση υποστυλώματος 1:4

πάχος 2,5 cm

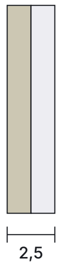

κόλλα + 1 × γυψοσανίδα 12,5 (ένα φύλλο) · στις παρειές υποστυλωμάτων μέσα στα διαμερίσματα – ΟΧΙ όπου πλακάκι ή ντουλάπα

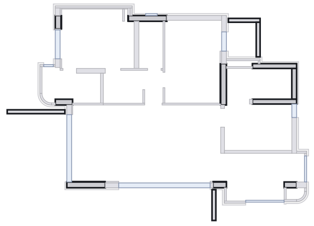

Τοίχοι: T9-01, T9-02, T9-03, T9-04, T9-05

Μήκος 5,75 m · επιφάνεια ≈ 16,7 m²

🟦 **T2** Χώρισμα γυψοσανίδας 1:4

πάχος 10 cm

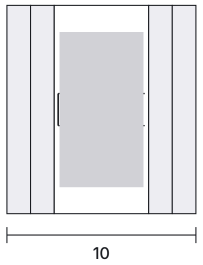

2 × γυψοσανίδα 12,5 · σκελετός CW 50 · 2 × γυψοσανίδα 12,5 · εσωτερικά χωρίσματα · ανθυγρή γυψοσανίδα στην πλευρά των λουτρών

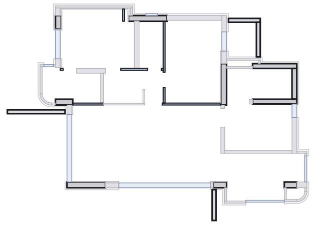

Τοίχοι: T2-01, T2-02, T2-03, T2-04, T2-06, T2-07, T2-08, T2-09

Μήκος 10,38 m · επιφάνεια ≈ 30,1 m²

🟦 **T2N** Χώρισμα γυψ. – πλευρά ντουλάπας 1:4

πάχος 8,75 cm

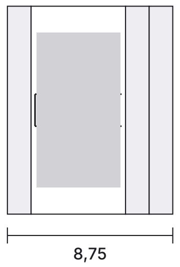

1 × γυψοσανίδα 12,5 (πλευρά ντουλάπας) · σκελετός CW 50 · 2 × γυψοσανίδα 12,5 · όπου η μία παρειά βλέπει σε ντουλάπα: ένα φύλλο αρκεί (κανόνας R15)

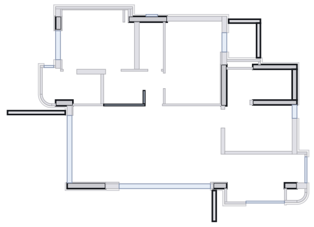

Τοίχοι: T2N-01, T2N-02

Μήκος 2,85 m · επιφάνεια ≈ 8,3 m²

🟦 **T2A** Χώρισμα γυψοσανίδας 15 1:4

πάχος 15 cm

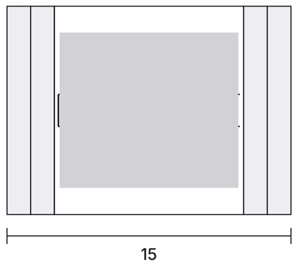

2 × γυψοσανίδα 12,5 · σκελετός CW 100 + πετροβάμβακας · 2 × γυψοσανίδα 12,5 · λουτρό γονέων / χωλ · υπνοδωμάτια

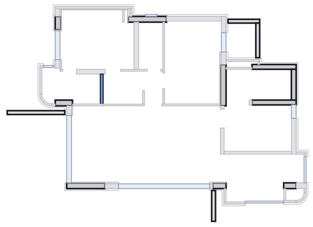

Τοίχοι: T2A-01

Μήκος 1,55 m · επιφάνεια ≈ 4,5 m²

🟪 **T7** Τοίχος λεκάνης WC 1:4

πάχος 25 cm

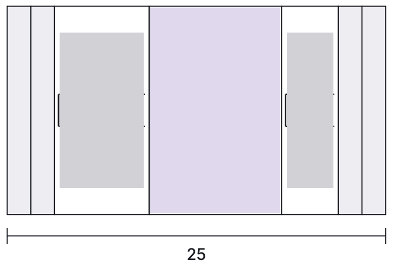

2 × γυψοσανίδα 12,5 · σκελετός CW 50 · κενό 12 cm (καζανάκι γυψοσανίδας στον σκελετό + κατακόρυφη στήλη Ø110, έξοδος Ø90) · σκελετός CW 30 · 2 × γυψοσανίδα 12,5 · ΟΛΟΙ οι τοίχοι λεκανών · ανθυγρή προς το λουτρό · στην πλευρά ντουλάπας 1 φύλλο

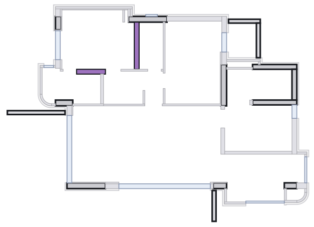

Τοίχοι: T7-01, T7-02

Μήκος 3,95 m · επιφάνεια ≈ 11,5 m²

🟩 **T6** Τοίχος κλιμακοστασίου 1:4

πάχος 15 cm

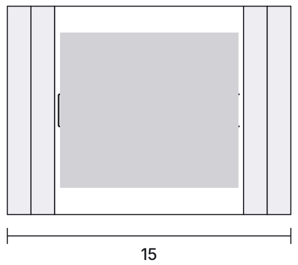

2 × γυψοσανίδα 12,5 πυράντοχη · σκελετός CW 100 + πετροβάμβακας · 2 × γυψοσανίδα 12,5 πυράντοχη · προς κοινόχρηστους χώρους · T6-01 (πόρτα εισόδου) μένει όπως η κάτοψη

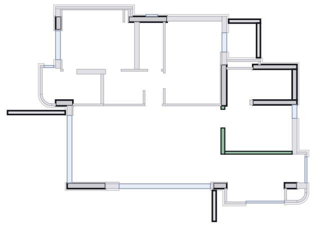

Τοίχοι: T6-01, T6-02, T6-03

Μήκος 5,06 m · επιφάνεια ≈ 14,7 m²

🟨 **T8** Τοίχος shaft 1:4

πάχος 10 cm

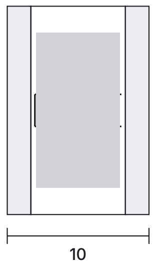

πλαίσιο + ανοιγόμενα φύλλα γυψοσανίδας · μέτωπο shaft ηλεκτρολογικών

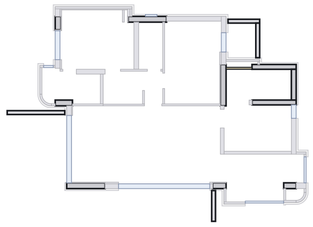

Τοίχοι: T8-01

Μήκος 1,35 m · επιφάνεια ≈ 3,9 m²

Επιφάνειες ενδεικτικές: μήκος × ύψος 2,90 m (τελικό δάπεδο – πλάκα) – οι τοίχοι ορίζονται μεταξύ ανοιγμάτων, χωρίς αφαίρεση κασών. T3 = επένδυση στην εσωτερική παρειά των T1 · T9 = περίμετρος υποστυλώματος × ύψος. R15: T2N = 1 φύλλο στην πλευρά ντουλάπας (T2N-01, T2N-02) · T7-01 1 φύλλο προς Υπν.1.

ΕΡΓΟ	ΘΕΜΑ ΣΧΕΔΙΟΥ	ΒΑΣΗ	ΑΡ. ΣΧΕΔΙΟΥ
ΠΕΝΤΑΟΡΟΦΟ ΚΤΗΡΙΟ ΚΑΤΟΙΚΙΩΝ – ΑΡΓΥΡΟΥΠΟΛΗ Κωνσταντινουπόλεως 12 & Αγ. Βαρβάρας · Ο.Τ. 103-15 Εργοδότης: INTERKAT A.E. · Κατασκευή: ARKAD I.K.E.	**ΕΙΔΗ ΤΟΙΧΟΠΟΙΙΩΝ – Β΄ ΟΡΟΦΟΣ** Είδη τοιχοποιιών · Β΄ ΟΡΟΦΟΣ – Β1 τομές 1:4 · μήκη – εμβαδά ανά είδος	Βάση: κάτοψη τοιχοποιιών T-01 · κάτοψη A-10-2F	**T-02** **Κλίμακα 1:4 · A3** 05/11/2026 · R15

ΠΡΟΜΕΤΡΗΣΗ ΥΛΙΚΩΝ ΤΟΙΧΟΠΟΙΙΩΝ – Β΄ ΟΡΟΦΟΣ – Β1

από την κάτοψη Τ-01 · H = 2,90 m (δάπεδο πλάκας – κάτω παρειά πλάκας) · μήκη στον άξονα κάθε τοίχου, χωρίς αφαίρεση κουφωμάτων (οι τοίχοι ορίζονται μεταξύ ανοιγμάτων) · R15

Είδος	Περιγραφή	Τοίχοι	Μήκος m	Επιφ. m²	Γυψοσ. κοινή m²	Γυψοσ. ανθυγρή m²	Γυψοσ. πυράντ. m²	Σκελετός CW m	Οδηγός UW m	Πετροβάμβ. m²	Θερμοτούβλα τεμ.	Κονίαμα m³	Κόλλα kg
■ **T1**	Εξωτερική οπτοπλινθοδομή · 25 cm T1-01, T1-02, T1-03, T1-04, T1-05, T1-06, T1-07, T1-08, T1-09, T1-10, T1-11, T1-12	12	9,52	27,61	–	–	–	–	–	–	461	0,41	–
■ **T4**	Έρκερ – απλή οπτοπλινθοδομή · 11 cm T4-01, T4-02, T4-03, T4-04, T4-05, T4-06, T4-07, T4-08, T4-09, T4-10, T4-11, T4-12, T4-13, T4-14, T4-15	15	12,02	34,85	–	–	–	–	–	–	1.342	0,69	–
■ **T5**	Οπτοπλινθοδομή πυρήνα · 10 cm T5-01, T5-02	2	1,90	5,51	–	–	–	–	–	–	92	0,03	–
■ **T3**	Επένδυση τοίχου · 5,5 cm T3-01, T3-02, T3-03, T3-04, T3-05, T3-07, T3-08, T3-09, T3-10	9	6,80	19,71	39,4	–	–	72,5	13,6	–	–	–	–
■ **T9**	Επένδυση υποστυλώματος · 2,5 cm T9-01, T9-02, T9-03, T9-04, T9-05	5	5,75	16,68	16,7	–	–	–	–	–	–	–	66,7
■ **T2**	Χώρισμα γυψοσανίδας · 10 cm T2-01, T2-02, T2-03, T2-04, T2-06, T2-07, T2-08, T2-09	8	10,38	32,22	94,6	34,2	–	89,9	20,8	–	–	–	–
■ **T2N**	Χώρισμα γυψ, – πλευρά ντουλάπας · 8,75 cm T2N-01, T2N-02	2	2,85	8,27	24,8	–	–	23,2	5,7	–	–	–	–
■ **T2A**	Χώρισμα γυψοσανίδας 15 · 15 cm T2A-01	1	1,55	4,49	9,0	9,0	–	11,6	3,1	4,5	–	–	–
■ **T7**	Τοίχος λεκάνης WC · 25 cm T7-01, T7-02	2	3,95	11,46	15,8	22,9	–	58,0	15,8	–	–	–	–
■ **T6**	Τοίχος κλιμακοστασίου · 15 cm T6-01, T6-02, T6-03	3	5,06	15,35	–	–	61,4	37,7	10,1	15,4	–	–	–
■ **T8**	Τοίχος shaft · 10 cm T8-01	1	1,35	3,91	7,8	–	–	11,6	2,7	–	–	–	–

ΛΙΣΤΑ ΠΑΡΑΓΓΕΛΙΑΣ (με φύρα: γυψοσανίδες +10 %, προφίλ +5 %)

Γυψοσανίδα κοινή 12,5 mm 1,20 × 3,00	**229,0 m²**	64 φύλλα
Γυψοσανίδα ανθυγρή (H2) 12,5 mm 1,20 × 3,00 – λουτρά: τοίχοι + οροφές (6,1 m² οροφές)	**79,4 m²**	23 φύλλα
Γυψοσανίδα πυράντοχη (F) 12,5 mm 1,20 × 3,00 – κλιμακοστάσιο	**67,6 m²**	19 φύλλα
Προφίλ CW50 (3,00 m)	**161,4 m**	54 τεμ.
Προφίλ CW30 (3,00 m)	**106,6 m**	36 τεμ.
Προφίλ CW100 (3,00 m)	**51,8 m**	18 τεμ.
Προφίλ UW50 (3,00 m)	**38,9 m**	13 τεμ.
Προφίλ UW30 (3,00 m)	**22,6 m**	8 τεμ.
Προφίλ UW100 (3,00 m)	**13,9 m**	5 τεμ.
Προφίλ CD60 (3,00 m) – ψευδοροφές λουτρών	**20,4 m**	7 τεμ.
Προφίλ UD28 (3,00 m) – ψευδοροφές λουτρών	**15,1 m**	6 τεμ.
Πετροβάμβακας 50 / 100 mm (T2A, T6)	**19,8 m²**	
Γυψόκολλα για κολλητή γυψοσανίδα (T9) ≈ 4 kg/m²	**66,7 kg**	3 σακιά 25 kg
Βίδες γυψοσανίδας TN 25 / 35 ≈ 22 τεμ/m² φύλλου	**7.519 τεμ.**	8 κουτιά 1.000
Στόκος αρμών ≈ 0,45 kg/m² τελικής επιφάνειας	**76,9 kg**	4 σακιά 25 kg
Ταινία αρμών ≈ 1,6 m/m² τελικής επιφάνειας	**273,4 m**	4 ρολά 90 m
Αναρτήσεις ψευδοροφής λουτρών (≈ 1,3 / m²)	**8 τεμ.**	
Θερμοτούβλο κάθετων οπών 25 (30 × 25 × 19) – T1	**484 τεμ.**	+5 % σπασίματα
Απλό τούβλο 6οπο 9 × 12 × 19 – T4 έρκερ	**1.409 τεμ.**	+5 % σπασίματα
Θερμοτούβλο κάθετων οπών 10 (30 × 10 × 19) – T5 πυρήνα	**97 τεμ.**	+5 % σπασίματα
Κονίαμα δόμησης	**1,14 m³**	

ΣΗΜΕΙΩΣΕΙΣ ΚΑΤΟΨΗΣ

- Θέσεις τοίχων και ανοιγμάτων όπως η κάτοψη Α-10-2F (Rev.11). Διαστάσεις στο τούβλο / μπετό, χωρίς τη θερμοπρόσοψη (κίτρινη λωρίδα 10 cm).
- ΝΤΟΥΛΑΠΕΣ ΧΩΝΕΥΤΕΣ (R15): δωματίων βάθος 0,60 · πλυντηρίου 0,70. Οι τοίχοι / πεσσοί που τις πλαισιώνουν έχουν ακριβώς το βάθος της ντουλάπας. Πίσω και δίπλα σε ντουλάπα καμία επένδυση T3 / T9.
- T1-05: κόπηκε στο 1,35 (περασιά με τη ντουλάπα Υπν.2) και καταργήθηκε η T3-06. Το W2.06 (1,00×2,40) μετατοπίζεται 10 cm βόρεια: 1,35–2,35. ΝΑ ΕΠΙΒΕΒΑΙΩΘΕΙ ΑΠΟ ΤΟΝ ΑΡΧΙΤΕΚΤΟΝΑ (όψη).
- Υπν.1: κουτί γυψοσανίδας T2 (x 4,30–4,40, από τον βόρειο τοίχο έως τη ντουλάπα) ώστε η ντουλάπα 0,60 να μπαίνει χωνευτή ανάμεσα σε αυτό και τον T2-01. Πόρτα 3,40–4,20.
- ΤΟΙΧΟΙ ΠΟΥ ΒΛΕΠΟΥΝ ΣΕ ΝΤΟΥΛΑΠΑ: 1 φύλλο γυψοσανίδας στην πλευρά της ντουλάπας (T2N-01, T2N-02 · T7-01 πλευρά Υπν.1).
- ΛΟΥΤΡΑ: σχεδιάζονται μόνο πάγκος νιπτήρα βάθους 0,50, λεκάνη και ένα διαχωριστικό ντους. Λουτρό: ντους βόρεια (0,80), διαχωριστικό στο y 1,60. Λουτρό γονέων: ντους στη δυτική εσοχή (W2.09), διαχωριστικό στο x 1,20.
- ΤΟΙΧΟΙ ΛΕΚΑΝΗΣ T7: 2 γυψ. + CW 50 (καζανάκι γυψοσανίδας) + κενό 12 + CW 30 + 2 γυψ. = 25 cm. T7-01: σταθερή η παρειά του λουτρού. T7-02: σταθερή η παρειά του Υπν.1.
- ΟΠΟΥ ΠΛΑΚΑΚΙ Ή ΝΤΟΥΛΑΠΑ: χωρίς γυψοσανίδα σε τούβλο / μπετό. Επενδύσεις T3 / T9 σε ενιαίο επίπεδο, χωρίς δόντια.
- T5-01 κόβεται στην άκρη του εξώστη (x 11,45) με επιστροφή T5-02 στο τοιχείο του ασανσέρ. Υποστυλώματα (σκούρο γκρι) κατά Σ5. Εξώστες από την κάτοψη Α-10-2F.

ΠΑΡΑΔΟΧΕΣ

- Γυψοσανίδες 12,5 mm σε φύλλα 1,20 × 3,00 (ένα φύλλο καθ' ύψος για H = 2,90). Ανθυγρή όπου η πλευρά βλέπει λουτρό / WC, πυράντοχη στον T6.
- Ορθοστάτες CW ανά 60 cm (+1 ανά τοίχο), οδηγοί UW δάπεδο + οροφή. T7: δύο σκελετοί (CW 50 + CW 30). T3: σκελετός 3άρι μίας πλευράς. T9: χωρίς σκελετό, σε γυψόκολλα.
- R15: στην πλευρά ντουλάπας ένα φύλλο (T2N-01, T2N-02, T7-01 προς Υπν.1) – αφαιρέθηκε από τα m² γυψοσανίδας.
- Υπέρθυρα πάνω από τις πόρτες (H – 2,20) προστέθηκαν στο είδος του τοίχου της πόρτας: 5 πόρτες.
- Τούβλα: T1 / T5 θερμομονωτικά κάθετων οπών (30 × 19 → ≈ 16,7 τεμ/m²) · T4 έρκερ απλό τούβλο 6οπο 9 × 12 × 19 δρομικό (≈ 38,5 τεμ/m²). ΠΡΟΣ ΕΠΙΒΕΒΑΙΩΣΗ οι διαστάσεις του προμηθευτή.
- ΛΟΥΤΡΑ: ό,τι είναι μέσα στο λουτρό (τοίχοι και οροφή) με ανθυγρή. Ψευδοροφές λουτρών: 1 × ανθυγρή 12,5 σε CD 60 / UD 28 (Λουτρό 3,06 m² · Λουτρό Γονέων 3,02 m²). Λοιπές ψευδοροφές στο τεύχος ανόψεων.
- Δεν περιλαμβάνονται: σοβάδες, πλακάκια, γωνιόκρανα γυψοσανίδας, κάσες / πρέκια, ηχομονωτικές ταινίες περιμέτρου.
- Όπου πλακάκι ή ντουλάπα: χωρίς γυψοσανίδα σε τούβλο / μπετό – ήδη εξαιρέθηκαν από την προμέτρηση.

ΘΕΡΜΟΠΡΟΣΟΨΗ (ETICS) 10 cm

ύψος ορόφου 3,10 m (με τη μετώπη πλάκας) · ύψη κουφωμάτων από τα label · όπως R14 (τα κουφώματα δεν άλλαξαν)

Περίμετρος όψεων	**47,76 m**
Κουφώματα (9 ανοίγματα)	**–29,61 m²**
Λαμπάδες + ανώφλια (βάθος ≈ 0,15)	**+6,63 m²**
ΚΑΘΑΡΗ ΕΠΙΦΑΝΕΙΑ	**125,1 m²**
Πλάκα EPS γραφιτούχο 10 cm (+5 %) · 263 πλ. 1,00×0,50	**131,3 m²**
Κόλλα – βασικός σοβάς ≈ 9 kg/m² · 46 σακιά	**1.126 kg**
Υαλόπλεγμα 160 g ≈ 1,15 m²/m² · 3 ρολά 50 m²	**143,8 m²**
Βύσματα ETICS ≈ 6 / m²	**750 τεμ.**
Γωνιόκρανα με πλέγμα (κουφώματα)	**46,4 m**
Αστάρι ≈ 0,25 kg/m²	**31 kg**
Τελικός σοβάς ≈ 2,5 kg/m²	**313 kg**

ΕΡΓΟ

ΠΕΝΤΑΟΡΟΦΟ ΚΤΗΡΙΟ ΚΑΤΟΙΚΙΩΝ – ΑΡΓΥΡΟΥΠΟΛΗ
Κωνσταντινουπόλεως 12 & Αγ. Βαρβάρας · Ο.Τ. 103-15
Εργοδότης: INTERKAT A.E. · Κατασκευή: ARKAD I.K.E.

ΘΕΜΑ ΣΧΕΔΙΟΥ

ΠΡΟΜΕΤΡΗΣΗ ΥΛΙΚΩΝ – Β΄ ΟΡΟΦΟΣ
Γυψοσανίδες · σκελετοί · τούβλα · αναλώσιμα
Β΄ ΟΡΟΦΟΣ – Β1

ΒΑΣΗ

Βάση: κάτοψη τοιχοποιιών Τ-01 · είδη Τ-02

ΑΡ. ΣΧΕΔΙΟΥ

Τ-03
— · A3
05/11/2026 · R15