
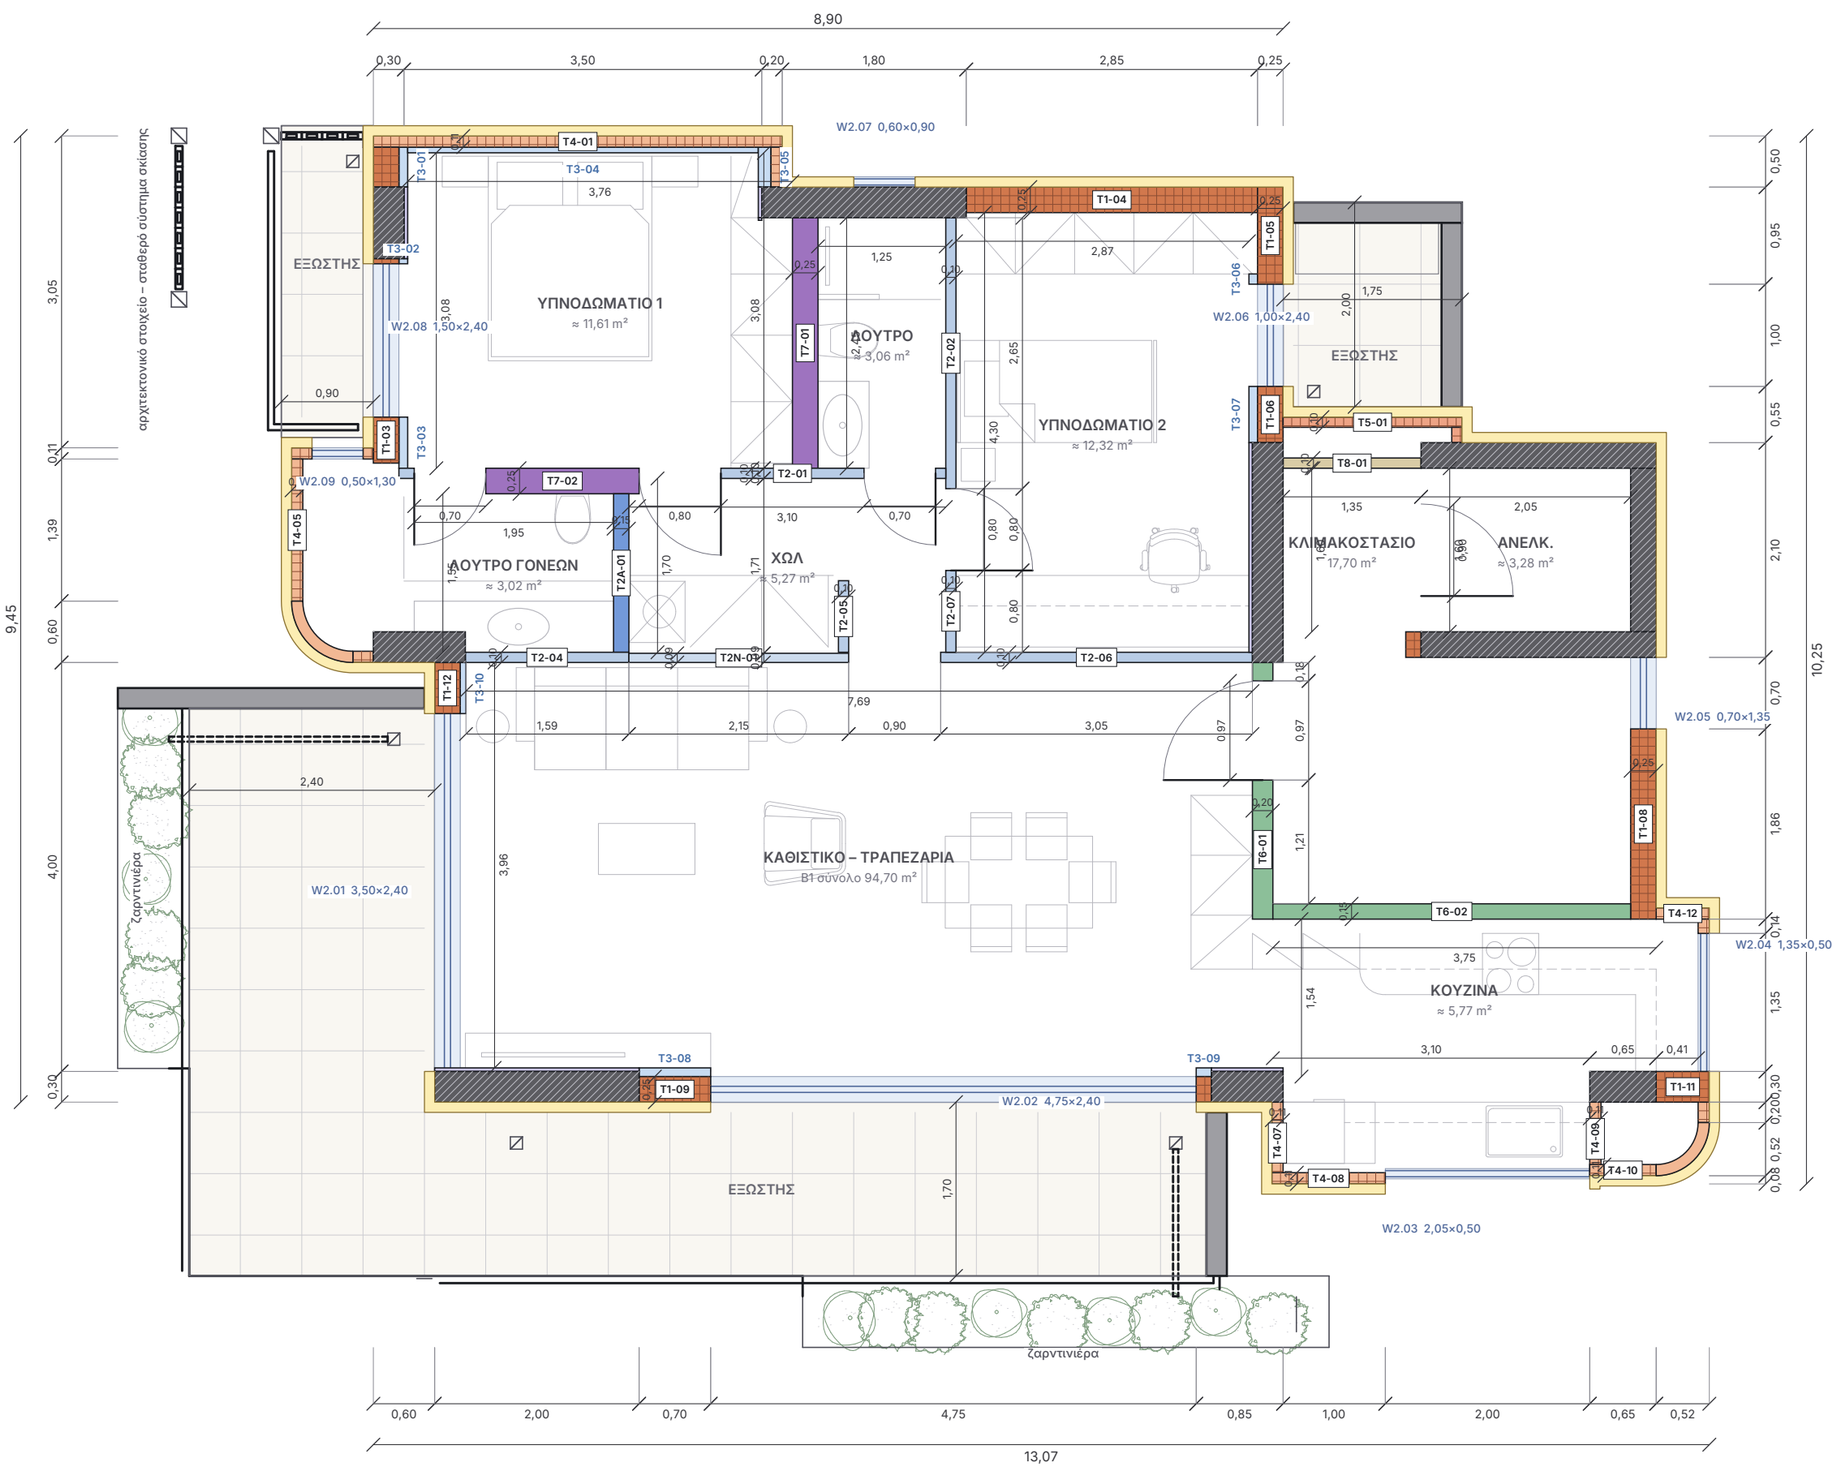



| ΕΡΓΟ | ΘΕΜΑ ΣΧΕΔΙΟΥ | ΒΑΣΗ | ΑΡ. ΣΧΕΔΙΟΥ |
|---|---|---|---|
| **ΠΕΝΤΑΟΡΟΦΟ ΚΤΗΡΙΟ ΚΑΤΟΙΚΙΩΝ – ΑΡΓΥΡΟΥΠΟΛΗ**<br>Κωνσταντινουπόλεως 12 & Αγ. Βαρβάρας · Ο.Τ. 103-15<br>Εργοδότης: INTERKAT Α.Ε. · Κατασκευή: ARKAD Ι.Κ.Ε. | **ΚΑΤΟΨΗ ΤΟΙΧΟΠΟΙΙΩΝ – Β΄ ΟΡΟΦΟΣ**<br>Είδη τοιχοποιιών · διαστάσεις · κουφώματα · εξώστες<br>Β΄ ΟΡΟΦΟΣ – Β1 | Βάση: κάτοψη Α-10-2F (μελέτη εφαρμογής) · ξυλότυποι Σ (υποστυλώματα) | **Τ-01**<br>**Κλίμακα 1:60 · Α3**<br>04/11/2026 · R14 |

## T1 Εξωτερική οπτοπλινθοδομή 1:4

**πάχος 25 cm**

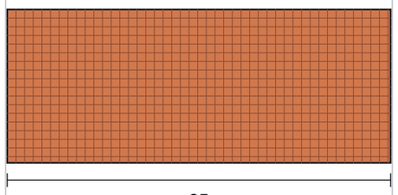


θερμομονωτικό τούβλο κάθετων οπών 25 cm
θερμοπρόσοψη 10 cm έξω · επένδυση Τ3 μέσα όπου σημειώνεται




Τοίχοι: T1-01, T1-02, T1-03, T1-04, T1-05, T1-06, T1-07, T1-08, T1-09, T1-10, T1-11, T1-12

**Μήκος 9,52 m · επιφάνεια ≈ 27,6 m²**

## T4 Έρκερ – απλή οπτοπλινθοδομή 1:4

**πάχος 11 cm**

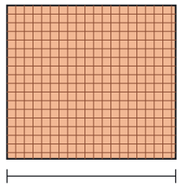


απλό τούβλο 6οπο 9 × 12 × 19 δρομικό ≈ 11 cm
σταθερή η εξωτερική παρειά · θερμοπρόσοψη 10 cm έξω




Τοίχοι: T4-01, T4-02, T4-03, T4-04, T4-05, T4-06, T4-07, T4-08, T4-09, T4-10, T4-11, T4-12, T4-13

**Μήκος 10,43 m · επιφάνεια ≈ 30,2 m²**

## T5 Οπτοπλινθοδομή πυρήνα 1:4

**πάχος 10 cm**

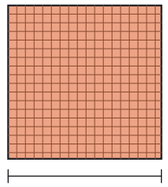


θερμομονωτικό τούβλο κάθετων οπών 10 cm
γύρω από τον πυρήνα (ανελκυστήρας – ηλεκτροστάσιο)




Τοίχοι: T5-01, T5-02

**Μήκος 1,90 m · επιφάνεια ≈ 5,5 m²**

## T3 Επένδυση τοίχου 1:4

**πάχος 5,5 cm**

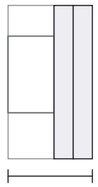


σκελετός 30 · 2 × γυψοσανίδα 12,5
στις εσωτερικές παρειές των Τ1 – ΟΧΙ όπου πλακάκι ή ντουλάπα, ΟΧΙ στα έρκερ



Τοίχοι: T3-01, T3-02, T3-03, T3-04, T3-05, T3-06, T3-07, T3-08, T3-09, T3-10


**Μήκος 6,80 m · επιφάνεια ≈ 19,7 m²**

## T9 Επένδυση υποστυλώματος 1:4

**πάχος 2,5 cm**




κόλλα + 1 × γυψοσανίδα 12,5 (ένα φύλλο)
στις παρειές υποστυλωμάτων μέσα στα διαμερίσματα – ΟΧΙ όπου πλακάκι ή ντουλάπα

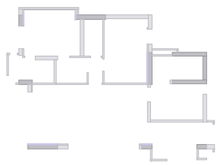


Τοίχοι: T9-01, T9-02, T9-03, T9-04, T9-05, T9-06

**Μήκος 5,78 m · επιφάνεια ≈ 16,8 m²**

## T2 Χώρισμα γυψοσανίδας 1:4

**πάχος 10 cm**

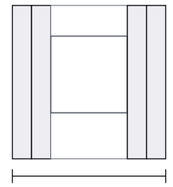


2 × γυψοσανίδα 12,5 · σκελετός CW 50 · 2 × γυψοσανίδα 12,5
εσωτερικά χωρίσματα · ανθυγρή γυψοσανίδα στην πλευρά των λουτρών




Τοίχοι: T2-01, T2-02, T2-03, T2-04, T2-05, T2-06, T2-07, T2-08


**Μήκος 10,45 m · επιφάνεια ≈ 30,3 m²**

## T2N Χώρισμα γυψοσανίδας – πλευρά ντουλάπας 1:4

**πάχος 8,75 cm**

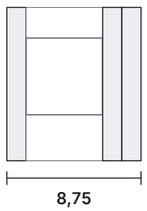


1 × γυψοσανίδα 12,5 (πλευρά ντουλάπας) · σκελετός CW 50 · 2 × γυψοσανίδα 12,5
πίσω από εντοιχισμένες ντουλάπες: ένα φύλλο αρκεί

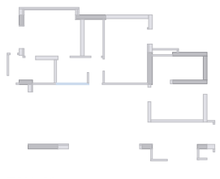


Τοίχοι: T2N-01

**Μήκος 2,15 m · επιφάνεια ≈ 6,2 m²**

## T2A Χώρισμα γυψοσανίδας 15 1:4

**πάχος 15 cm**

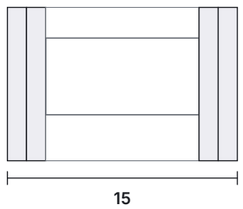


2 × γυψοσανίδα 12,5 · σκελετός CW 100 + πετροβάμβακας · 2 × γυψοσανίδα 12,5
λουτρό γονέων / χωλ · υπνοδωμάτια




Τοίχοι: T2A-01

**Μήκος 1,55 m · επιφάνεια ≈ 4,5 m²**

## T7 Τοίχος λεκάνης WC 1:4

**πάχος 25 cm**

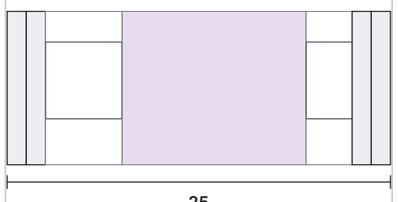


2 × γυψοσανίδα 12,5 · σκελετός CW 50 · κενό 12 cm (καζανάκι γυψοσανίδας στον σκελετό + κατακόρυφη στήλη Ø110, έξοδος Ø90) · σκελετός CW 30 · 2 × γυψοσανίδα 12,5
ΟΛΟΙ οι τοίχοι λεκανών · ανθυγρή προς το λουτρό · στην πλευρά ντουλάπας 1 φύλλο




Τοίχοι: T7-01, T7-02


**Μήκος 3,95 m · επιφάνεια ≈ 11,5 m²**

## T6 Τοίχος κλιμακοστασίου 1:4

**πάχος 15 cm**

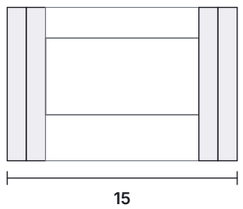


2 × γυψοσανίδα 12,5 πυράντοχη · σκελετός CW 100 + πετροβάμβακας · 2 × γυψοσανίδα 12,5 πυράντοχη
προς κοινόχρηστους χώρους · Τ6-01 (πόρτα εισόδου) μένει όπως η κάτοψη

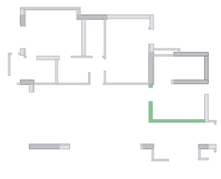


Τοίχοι: T6-01, T6-02, T6-03


**Μήκος 5,06 m · επιφάνεια ≈ 14,7 m²**

## T8 Τοίχος shaft 1:4

**πάχος 10 cm**

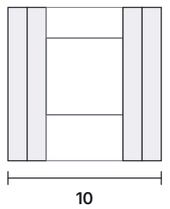


πλαίσιο + ανοιγόμενα φύλλα γυψοσανίδας
μέτωπο shaft ηλεκτρολογικών

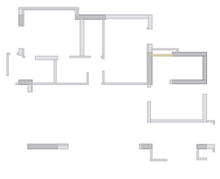

Τοίχοι: T8-01

**Μήκος 1,35 m · επιφάνεια ≈ 3,9 m²**

Επιφάνειες ενδεικτικές: μήκος × ύψος 2,90 m (τελικό δάπεδο – πλάκα) – οι τοίχοι ορίζονται μεταξύ ανοιγμάτων, χωρίς αφαίρεση κασών. Τ3 = επένδυση στην εσωτερική παρειά των Τ1 · Τ9 = περίμετρος υποστυλώματος × ύψος.

ΕΡΓΟ

**ΠΕΝΤΑΟΡΟΦΟ ΚΤΗΡΙΟ ΚΑΤΟΙΚΙΩΝ – ΑΡΓΥΡΟΥΠΟΛΗ**
Κωνσταντινουπόλεως 12 & Αγ. Βαρβάρας · Ο.Τ. 103-15
Εργοδότης: INTERKAT Α.Ε. · Κατασκευή: ARKAD Ι.Κ.Ε.

ΘΕΜΑ ΣΧΕΔΙΟΥ

**ΕΙΔΗ ΤΟΙΧΟΠΟΙΙΩΝ – Β΄ ΟΡΟΦΟΣ**
Είδη τοιχοποιιών · Β΄ ΟΡΟΦΟΣ – Β1
τομές 1:4 · μήκη – εμβαδά ανά είδος

ΒΑΣΗ

Βάση: κάτοψη τοιχοποιιών Τ-01 · κάτοψη Α-10-2F

ΑΡ. ΣΧΕΔΙΟΥ

**Τ-02**
**Κλίμακα 1:4 · Α3**
04/11/2026 · R14

# ΠΡΟΜΕΤΡΗΣΗ ΥΛΙΚΩΝ ΤΟΙΧΟΠΟΙΙΩΝ – Β΄ ΟΡΟΦΟΣ – Β1

από την κάτοψη Τ-01 · Η = 2,90 m (δάπεδο πλάκας – κάτω παρειά πλάκας) · μήκη στον άξονα κάθε τοίχου, χωρίς αφαίρεση κουφωμάτων (οι τοίχοι ορίζονται μεταξύ ανοιγμάτων)

| Είδος | Περιγραφή | Τοίχοι | Μήκος m | Επιφ. m² | Γυψοσ. κοινή m² | Γυψοσ. ανθυγρή m² | Γυψοσ. πυράντ. m² | Σκελετός CW m | Οδηγός UW m | Πετροβάμβ. m² | Θερμοτούβλα τεμ. | Κονίαμα m³ | Κόλλα kg |
|---|---|---|---|---|---|---|---|---|---|---|---|---|---|
| **T1** | Εξωτερική οπτοπλινθοδομή · 25 cm<br>T1-01, T1-02, T1-03, T1-04, T1-05, T1-06, T1-07, T1-08, T1-09, T1-10, T1-11, T1-12 | 12 | 9,52 | 27,61 | – | – | – | – | – | – | 461 | 0,41 | – |
| **T4** | Έρκερ – απλή οπτοπλινθοδομή · 11 cm<br>T4-01, T4-02, T4-03, T4-04, T4-05, T4-06, T4-07, T4-08, T4-09, T4-10, T4-11, T4-12, T4-13 | 13 | 10,43 | 30,25 | – | – | – | – | – | – | 1.165 | 0,60 | – |
| **T5** | Οπτοπλινθοδομή πυρήνα · 10 cm<br>T5-01, T5-02 | 2 | 1,90 | 5,51 | – | – | – | – | – | – | 92 | 0,03 | – |
| **T3** | Επένδυση τοίχου · 5,5 cm<br>T3-01, T3-02, T3-03, T3-04, T3-05, T3-06, T3-07, T3-08, T3-09, T3-10 | 10 | 6,80 | 19,71 | 39,4 | – | – | 75,4 | 13,6 | – | – | – | – |
| **T9** | Επένδυση υποστυλώματος · 2,5 cm<br>T9-01, T9-02, T9-03, T9-04, T9-05, T9-06 | 6 | 5,78 | 16,77 | 16,8 | – | – | – | – | – | – | – | 67,1 |
| **T2** | Χώρισμα γυψοσανίδας · 10 cm<br>T2-01, T2-02, T2-03, T2-04, T2-05, T2-06, T2-07, T2-08 | 8 | 10,45 | 31,36 | 96,9 | 28,5 | – | 89,9 | 20,9 | – | – | – | – |
| **T2N** | Χώρισμα γυψοσανίδας – πλευρά ντουλάπας · 8,8 cm<br>T2N-01 | 1 | 2,15 | 6,24 | 18,7 | – | – | 14,5 | 4,3 | – | – | – | – |
| **T2A** | Χώρισμα γυψοσανίδας 15 · 15 cm<br>T2A-01 | 1 | 1,55 | 4,49 | 9,0 | 9,0 | – | 11,6 | 3,1 | 4,5 | – | – | – |
| **T7** | Τοίχος λεκάνης WC · 25 cm<br>T7-01, T7-02 | 2 | 3,95 | 12,51 | 28,8 | 21,2 | – | 58,0 | 15,8 | – | – | – | – |
| **T6** | Τοίχος κλιμακοστασίου · 15 cm<br>T6-01, T6-02, T6-03 | 3 | 5,06 | 15,35 | – | – | 61,4 | 37,7 | 10,1 | 15,4 | – | – | – |
| **T8** | Τοίχος shaft · 10 cm<br>T8-01 | 1 | 1,35 | 3,92 | 7,8 | – | – | 11,6 | 2,7 | – | – | – | – |

## ΛΙΣΤΑ ΠΑΡΑΓΓΕΛΙΑΣ (με φύρα: γυψοσανίδες +10 %, προφίλ +5 %)

| | | |
|---|---|---|
| Γυψοσανίδα κοινή 12,5 mm 1,20 × 3,00 | **239,3 m²** | 67 φύλλα |
| Γυψοσανίδα ανθυγρή (H2) 12,5 mm 1,20 × 3,00 – λουτρά: τοίχοι + οροφές (6,1 m² οροφές) | **71,2 m²** | 20 φύλλα |
| Γυψοσανίδα πυράντοχη (F) 12,5 mm 1,20 × 3,00 – κλιμακοστάσιο | **67,6 m²** | 19 φύλλα |
| Προφίλ CW50 (3,00 m) | **158,1 m** | 53 τεμ. |
| Προφίλ CW30 (3,00 m) | **112,6 m** | 38 τεμ. |
| Προφίλ CW100 (3,00 m) | **53,2 m** | 18 τεμ. |
| Προφίλ UW50 (3,00 m) | **40,7 m** | 14 τεμ. |
| Προφίλ UW30 (3,00 m) | **24,1 m** | 9 τεμ. |
| Προφίλ UW100 (3,00 m) | **14,9 m** | 5 τεμ. |
| Προφίλ CD60 (3,00 m) | **20,4 m** | 7 τεμ. |
| Προφίλ UD28 (3,00 m) | **15,1 m** | 6 τεμ. |
| Πετροβάμβακας 50 / 100 mm (T2A, T6) | **20,8 m²** | |
| Γυψόκολλα για κολλητή γυψοσανίδα (T9) ≈ 4 kg/m² | **74 kg** | 3 σακιά 25 kg |
| Βίδες γυψοσανίδας TN 25 / 35 ≈ 22 τεμ/m² φύλλου | **8.269 τεμ.** | 9 κουτιά 1.000 |
| Στόκος αρμών ≈ 0,45 kg/m² τελικής επιφάνειας | **92 kg** | 4 σακιά 25 kg |
| Ταινία αρμών ≈ 1,6 m/m² τελικής επιφάνειας | **328 m** | 4 ρολά 90 m |
| Αναρτήσεις ψευδοροφής λουτρών (≈ 1,3 / m²) | **8 τεμ.** | |
| Θερμοτούβλο κάθετων οπών 25 (30 × 25 × 19) – Τ1 | **484 τεμ.** | +5 % σπασίματα |
| Θερμοτούβλο κάθετων οπών 10 (30 × 10 × 19) – Τ5 πυρήνα | **97 τεμ.** | +5 % σπασίματα |
| Απλό τούβλο 6οπο 9 × 12 × 19 – Τ4 έρκερ | **1.223 τεμ.** | +5 % σπασίματα |
| Κονίαμα δόμησης | **1,05 m³** | |

### ΣΗΜΕΙΩΣΕΙΣ ΚΑΤΟΨΗΣ

- Θέσεις τοίχων και ανοιγμάτων όπως η κάτοψη Α-10-2F (Rev.11). Οι διορθώσεις της 07/10 ΑΝΑΚΛΗΘΗΚΑΝ.
- ΤΟΙΧΟΙ ΛΕΚΑΝΗΣ Τ7 (ΟΛΟΙ): 2 γυψ. + CW 50 (καζανάκι γυψοσανίδας στον σκελετό, από πίσω Ø90 → στήλη Ø110) + κενό 12 + CW 30 + 2 γυψ. = 25 cm. Τ7-01: σταθερή η παρειά του λουτρού. Τ7-02: σταθερή η παρειά του Υπν.1, το πάχος προς το λουτρό γονέων.
- ΕΠΕΝΔΥΣΕΙΣ ΧΩΡΙΣ ΕΣΟΧΕΣ: σε κάθε τοίχο η Τ3 (τούβλα) και η Τ9 (κολώνες) τελειώνουν στο ίδιο επίπεδο – ενιαία επίπεδη επιφάνεια, χωρίς δόντια και γωνίες.
- ΟΠΟΥ ΠΛΑΚΑΚΙ Ή ΝΤΟΥΛΑΠΑ: ΧΩΡΙΣ γυψοσανίδα σε τούβλο / μπετό (λουτρά, κουζίνα, Τ1-04 ντουλάπα Υπν.2). Εξαίρεση: έρκερ Υπν.1 (Τ4-01 / Τ4-02) ντύνεται με Τ3.
- Ντουλάπα μπροστά σε τοίχο γυψοσανίδας: 1 φύλλο στην πλευρά της ντουλάπας (Τ2Ν-01). ΝΤΟΥΛΑΠΕΣ ΠΑΝΤΑ 0,60 – όπου ο τοίχος πάχυνε, η ντουλάπα μπαίνει μέσα στο δωμάτιο (Υπν.1: 4,30–4,90).
- Χωλ: πλυντήριο στη δυτική άκρη (3,30–3,85, κολλητά στον Τ2Α-01), ντουλάπα 3,90–5,25. Πόρτα Υπν.1 15 cm δυτικά (άνοιγμα 3,40–4,20, πάνω στο τέλος του Τ7-02) ώστε να μένουν 10 cm από τη ντουλάπα (μέτωπο 4,30). Πάγκοι νιπτήρα 0,50 σε όλα τα λουτρά. Πίσω από ντουλάπες δεν μπαίνει επένδυση (Τ3-06 από 1,35, Κ2 στο Υπν.1 χωρίς Τ9 πίσω από τη ντουλάπα).
- Τ5-01 κόβεται στην άκρη του εξώστη (x 11,45) με επιστροφή Τ5-02 πάνω στο τοιχείο του ασανσέρ. Θερμοπρόσοψη σε όλες τις όψεις (καμία μεσοτοιχία).
- Υποστυλώματα (σκούρο γκρι) κατά Σ5. Μπαλκόνια από την κάτοψη Α-10-2F (χωρίς κλίσεις).
- Τούβλα: Τ1 / Τ5 θερμομονωτικά κάθετων οπών · Τ4 έρκερ απλό τούβλο. ΘΕΡΜΟΠΡΟΣΟΨΗ 10 cm σε όλες τις εξωτερικές παρειές (κίτρινη λωρίδα) – οι διαστάσεις της κάτοψης είναι στο τούβλο / μπετό, χωρίς τη θερμοπρόσοψη.

### ΠΑΡΑΔΟΧΕΣ

- Γυψοσανίδες 12,5 mm σε φύλλα 1,20 × 3,00 (ένα φύλλο καθ' ύψος για Η = 2,90). Ανθυγρή όπου η πλευρά βλέπει λουτρό / WC (αυτόματα από τους χώρους), πυράντοχη στον Τ6.
- Ορθοστάτες CW ανά 60 cm, οδηγοί UW δάπεδο + οροφή. Τ7: δύο σκελετοί (CW 50 + CW 30). Τ3: σκελετός 3άρι μίας πλευράς. Τ9: χωρίς σκελετό, σε γυψόκολλα.
- Υπέρθυρα πάνω από τις πόρτες (Η – 2,20) προστέθηκαν στο είδος του τοίχου της πόρτας: 5 πόρτες.
- Τούβλα: Τ1 / Τ5 θερμομονωτικά κάθετων οπών (μήκος 30 × ύψος 19 → ≈ 16,7 τεμ/m², πάχος 25 / 10) · Τ4 έρκερ απλό τούβλο 6οπο 9 × 12 × 19 δρομικό (≈ 38,5 τεμ/m²). ΠΡΟΣ ΕΠΙΒΕΒΑΙΩΣΗ οι διαστάσεις του προμηθευτή.
- ΛΟΥΤΡΑ: ό,τι είναι μέσα στο λουτρό (τοίχοι και οροφή) υπολογίζεται με ανθυγρή. Ψευδοροφές λουτρών: 1 × ανθυγρή 12,5 σε CD 60 / UD 28 (Λουτρο 3,06 m² · Λουτρο Γονεων 3,02 m²). Οι ψευδοροφές των άλλων χώρων στο τεύχος ανόψεων.
- Δεν περιλαμβάνονται: σοβάδες, πλακάκια, γωνιόκρανα γυψοσανίδας, κάσες / πρέκια, ηχομονωτικές ταινίες περιμέτρου.
- Όπου πλακάκι ή ντουλάπα: χωρίς γυψοσανίδα σε τούβλο / μπετό – ήδη εξαιρέθηκαν από την προμέτρηση.

### ΘΕΡΜΟΠΡΟΣΟΨΗ (ETICS) 10 cm

ύψος ορόφου 3,10 m (με τη μετώπη πλάκας) · ύψη κουφωμάτων από τα label

| | |
|---|---|
| Περίμετρος όψεων | **47,76 m** |
| Κουφώματα (9 ανοίγματα) | **−29,61 m²** |
| Λαμπάδες + ανώφλια (βάθος ≈ 0,15) | **+6,63 m²** |
| **ΚΑΘΑΡΗ ΕΠΙΦΑΝΕΙΑ** | **125,1 m²** |
| Πλάκα EPS γραφιτούχο 10 cm (+5 %) · 263 πλ. 1,00×0,50 | **131,3 m²** |
| Κόλλα – βασικός σοβάς ≈ 9 kg/m² · 46 σακιά | **1.126 kg** |
| Υαλόπλεγμα 160 g ≈ 1,15 m²/m² · 3 ρολά 50 m² | **143,8 m²** |
| Βύσματα ETICS ≈ 6 / m² | **750 τεμ.** |
| Γωνιόκρανα με πλέγμα (κουφώματα) | **46,4 m** |
| Αστάρι ≈ 0,25 kg/m² | **31 kg** |
| Τελικός σοβάς ≈ 2,5 kg/m² | **313 kg** |

| ΕΡΓΟ | ΘΕΜΑ ΣΧΕΔΙΟΥ | ΒΑΣΗ | ΑΡ. ΣΧΕΔΙΟΥ |
|---|---|---|---|
| **ΠΕΝΤΑΟΡΟΦΟ ΚΤΗΡΙΟ ΚΑΤΟΙΚΙΩΝ – ΑΡΓΥΡΟΥΠΟΛΗ**<br>Κωνσταντινουπόλεως 12 & Αγ. Βαρβάρας · Ο.Τ. 103-15<br>Εργοδότης: INTERKAT Α.Ε. · Κατασκευή: ARKAD Ι.Κ.Ε. | **ΠΡΟΜΕΤΡΗΣΗ ΥΛΙΚΩΝ – Β΄ ΟΡΟΦΟΣ**<br>Γυψοσανίδες · σκελετοί · τούβλα · αναλώσιμα<br>Β΄ ΟΡΟΦΟΣ – Β1 | Βάση: κάτοψη τοιχοποιιών Τ-01 · είδη Τ-02 | **Τ-03**<br>— · A3<br>04/11/2026 · R14 |