
ΟΡΟΦΗ ΥΠΟΓΕΙΟΥ – ΣΥΛΛΕΚΤΗΡΑΣ ΛΥΜΑΤΩΝ

Κλίμακα 1:80

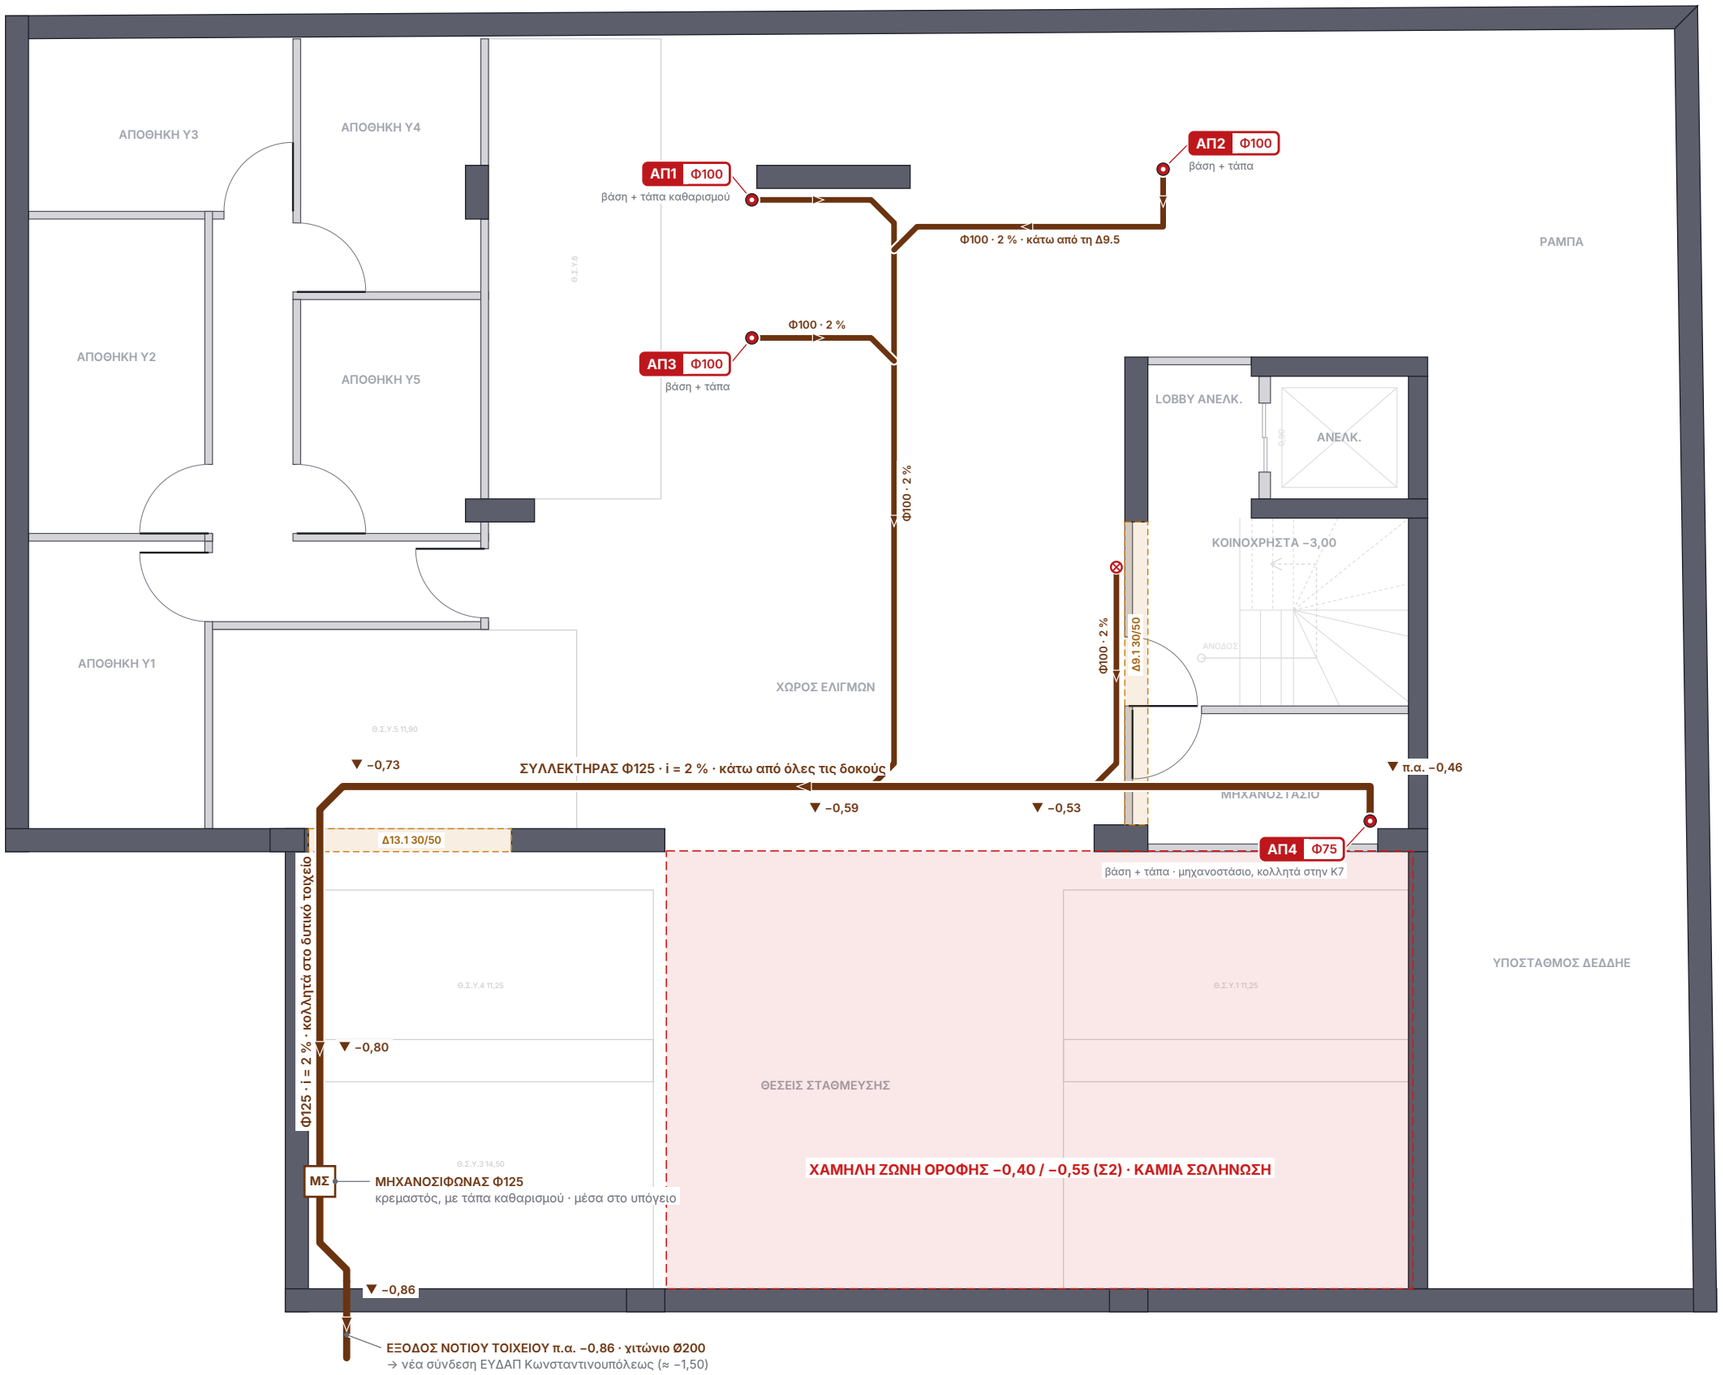


ΥΠΟΜΝΗΜΑ

- Συλλεκτήρας / κλάδοι υπογείου, κρεμαστοί κάτω από τις δοκούς
- Κατακόρυφη στήλη λυμάτων ΑΠ
- Πτώση στον κάτω όροφο
- Δοκός (ξυλότυποι Σ2–Σ7) – ΚΑΜΙΑ οπή
- Χαμηλή ζώνη οροφής υπογείου – καμία σωλήνωση

ΕΡΓΟ	ΘΕΜΑ ΣΧΕΔΙΟΥ	ΒΑΣΗ	ΑΡ. ΣΧΕΔΙΟΥ
ΠΕΝΤΑΟΡΟΦΟ ΚΤΗΡΙΟ ΚΑΤΟΙΚΙΩΝ – ΑΡΓΥΡΟΥΠΟΛΗ Κωνσταντινουπόλεως 12 & Αγ. Βαρβάρας · Ο.Τ. 103-15 Εργοδότης: INTERKAT Α.Ε. · Κατασκευή: ARKAD Ι.Κ.Ε.	**ΥΠΟΓΕΙΟ – ΣΥΛΛΕΚΤΗΡΑΣ ΛΥΜΑΤΩΝ** R19 · λύματα · ακάθαρτα · αερισμοί · όμβρια · οπές πλακών Οροφή υπογείου · συλλεκτήρας στο δυτικό τοιχείο · έξοδος −0,86	Σ2 εφαρμογής · τοιχοποιίες υπογείου R05	**ΑΠ-01** **Κλίμακα 1:80 · Α3** 10/11/2026 · R19

ΚΑΤΟΨΗ ΙΣΟΓΕΙΟΥ – ΑΠΟΧΕΤΕΥΣΗ & ΟΜΒΡΙΑ

Κλίμακα 1:60

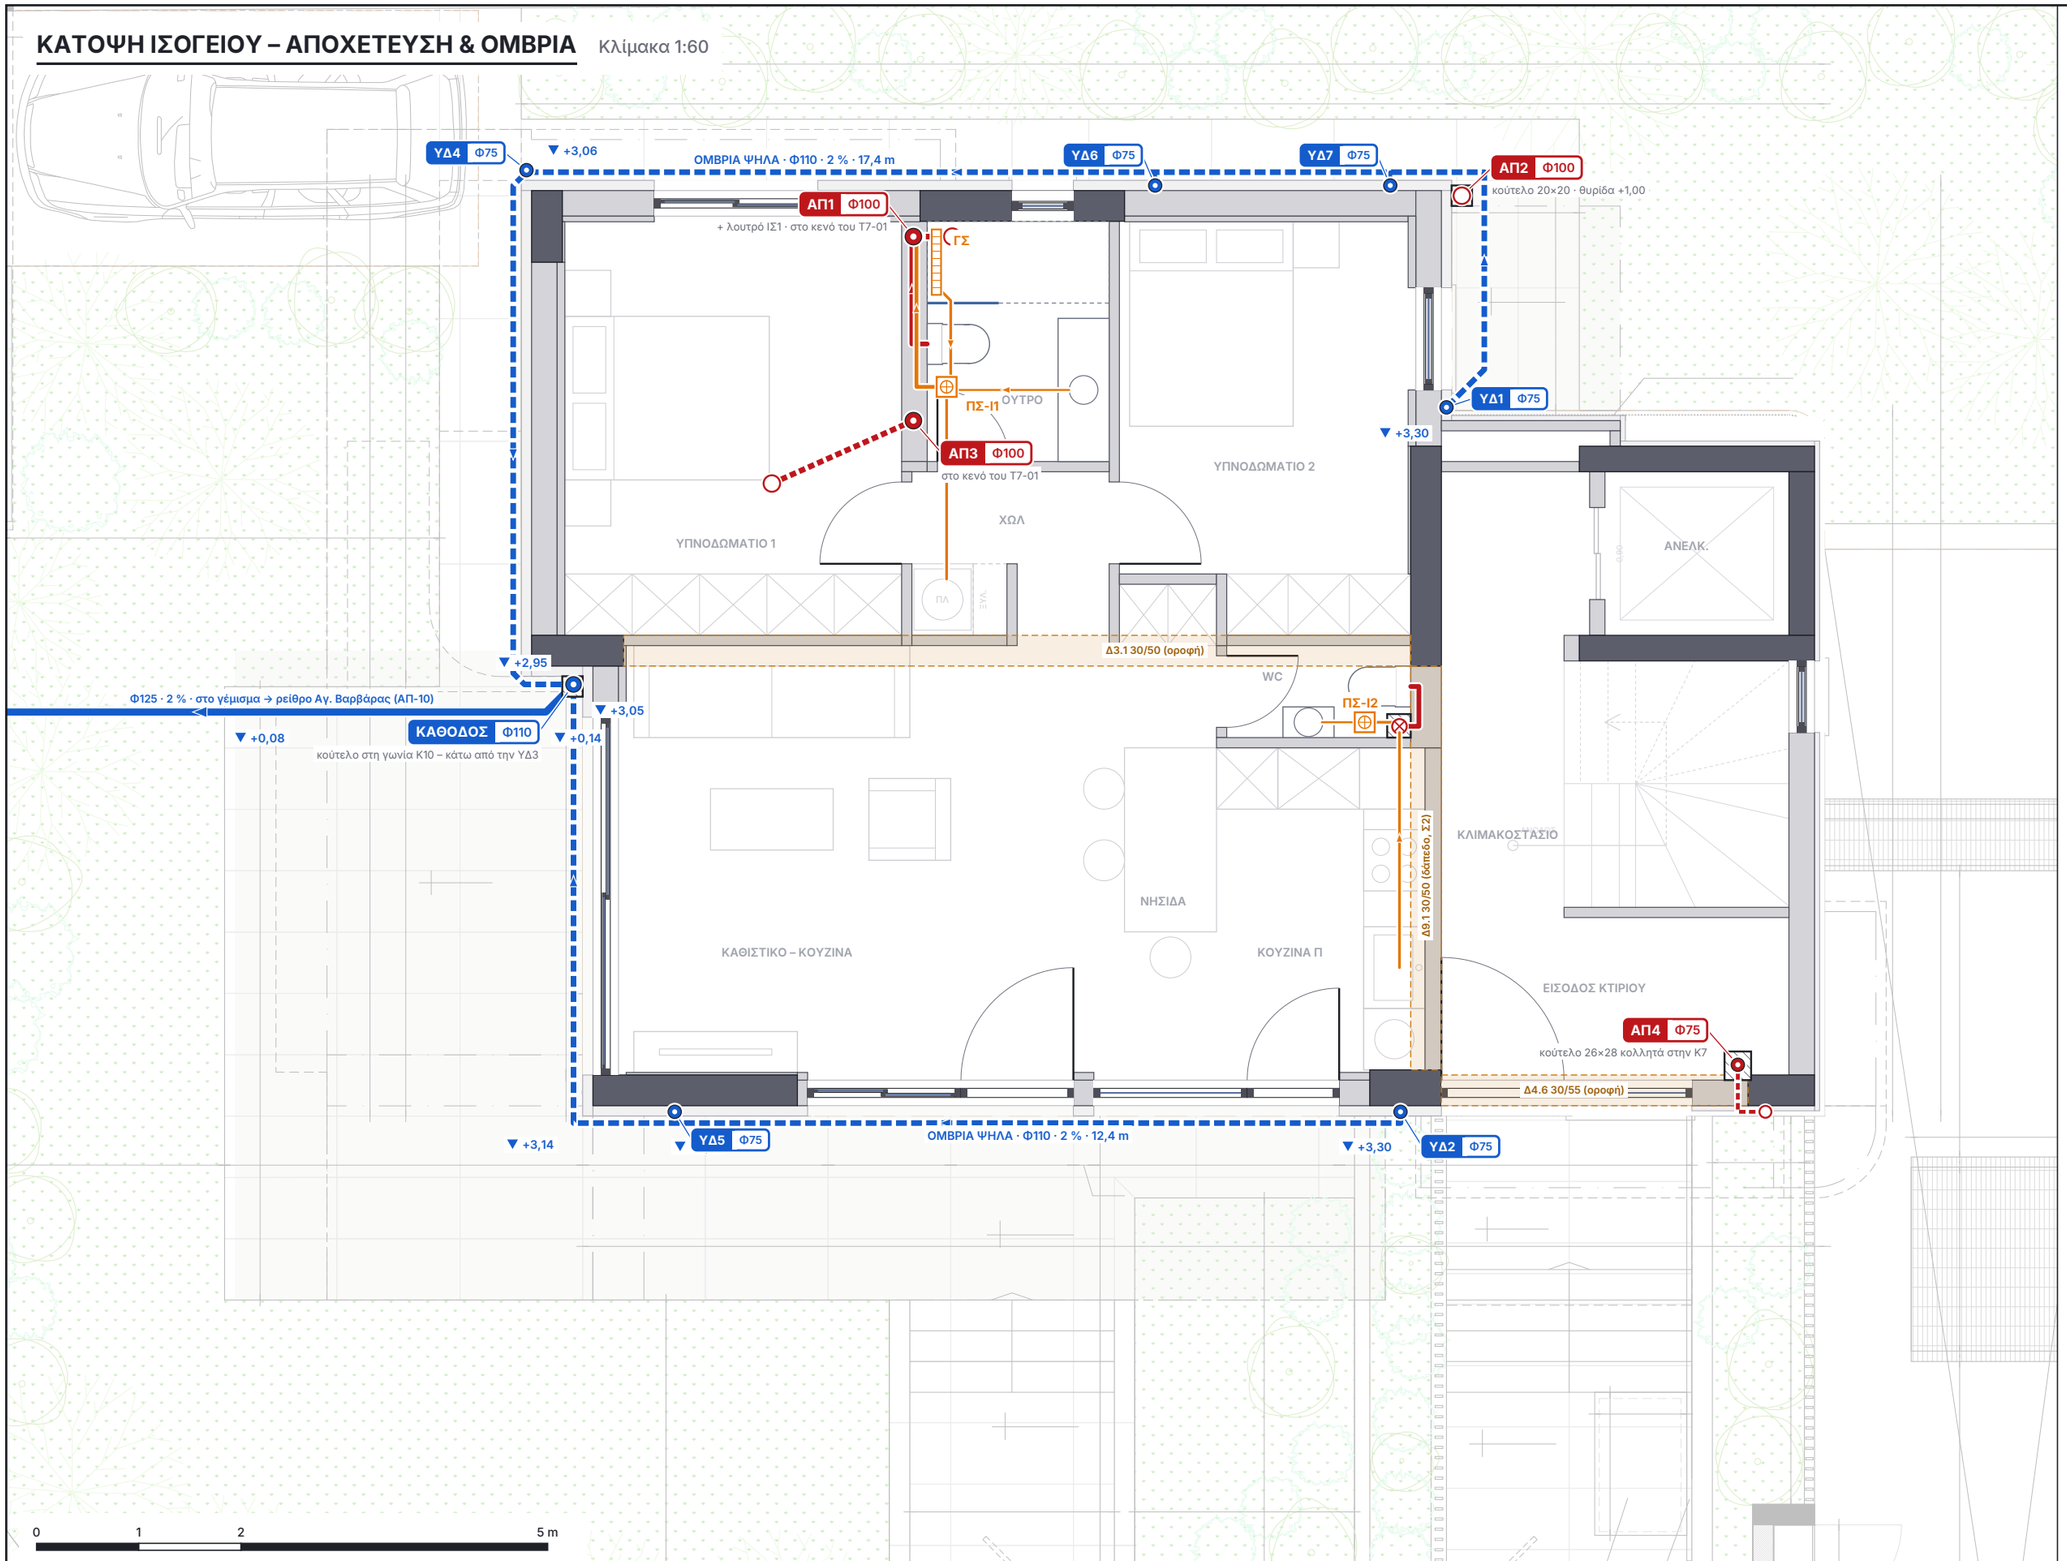


ΥΠΟΜΝΗΜΑ

- Λύματα: λεκάνη Φ90 · στήλη / αγωγός Φ100
- Ακάθαρτα: Φ40 νιπτήρας · Φ50 ντους, νεροχύτης, πλυντήριο · Φ75 έξοδος πατοσίφωνου
- Αγωγός στην οροφή του ορόφου (μετατόπιση στήλης 2×45°)
- Συλλεκτήρας ομβρίων ΨΗΛΑ +3,30 (οροφή προβόλων Α΄)
- Όμβρια: συλλεκτήρας / αγωγός
- Κατακόρυφη στήλη λυμάτων ΑΠ
- Στήλη που περνά / σταματά (χωρίς σύνδεση στον όροφο)
- Πτώση στον κάτω όροφο
- Πατοσίφωνο ΠΣ (σιφώνι δαπέδου με σχάρα)
- Γραμμικό σιφώνι ντους ΓΣ → πατοσίφωνο
- Κούτελο (κλειστό κανάλι γύρω από αγωγό)
- Υδρορροή ΥΔ Φ75 μέσα στη θερμοπρόσοψη
- Δοκός (Ξυλότυποι Σ2–Σ7) – ΚΑΜΙΑ οπή

ΕΡΓΟ	ΘΕΜΑ ΣΧΕΔΙΟΥ	ΒΑΣΗ	ΑΡ. ΣΧΕΔΙΟΥ
ΠΕΝΤΑΟΡΟΦΟ ΚΤΗΡΙΟ ΚΑΤΟΙΚΙΩΝ – ΑΡΓΥΡΟΥΠΟΛΗ Κωνσταντινουπόλεως 12 & Αγ. Βαρβάρας · Ο.Τ. 103-15 Εργοδότης: INTERKAT Α.Ε. · Κατασκευή: ARKAD Ι.Κ.Ε.	**ΙΣΟΓΕΙΟ – ΑΠΟΧΕΤΕΥΣΗ & ΟΜΒΡΙΑ** R19 · λύματα · ακάθαρτα · αερισμοί · όμβρια · οπές πλακών ΑΠ1 / ΑΠ3 στο κενό του Τ7-01 · κούτελα WC / ΑΠ4 · όμβρια 2 % · λεπτομέρειες στο ΑΠ-06	Σ2 / Σ3 εφαρμογής · τοιχοποιίες ισογείου R13	**ΑΠ-02** **Κλίμακα 1:60 · A3** 10/11/2026 · R19

ΚΑΤΟΨΗ Α΄ · Β΄ · Γ΄ ΟΡΟΦΟΥ (ΤΥΠΙΚΟΣ) – ΑΠΟΧΕΤΕΥΣΗ & ΥΔΡΟΡΡΟΕΣ

Κλίμακα 1:60

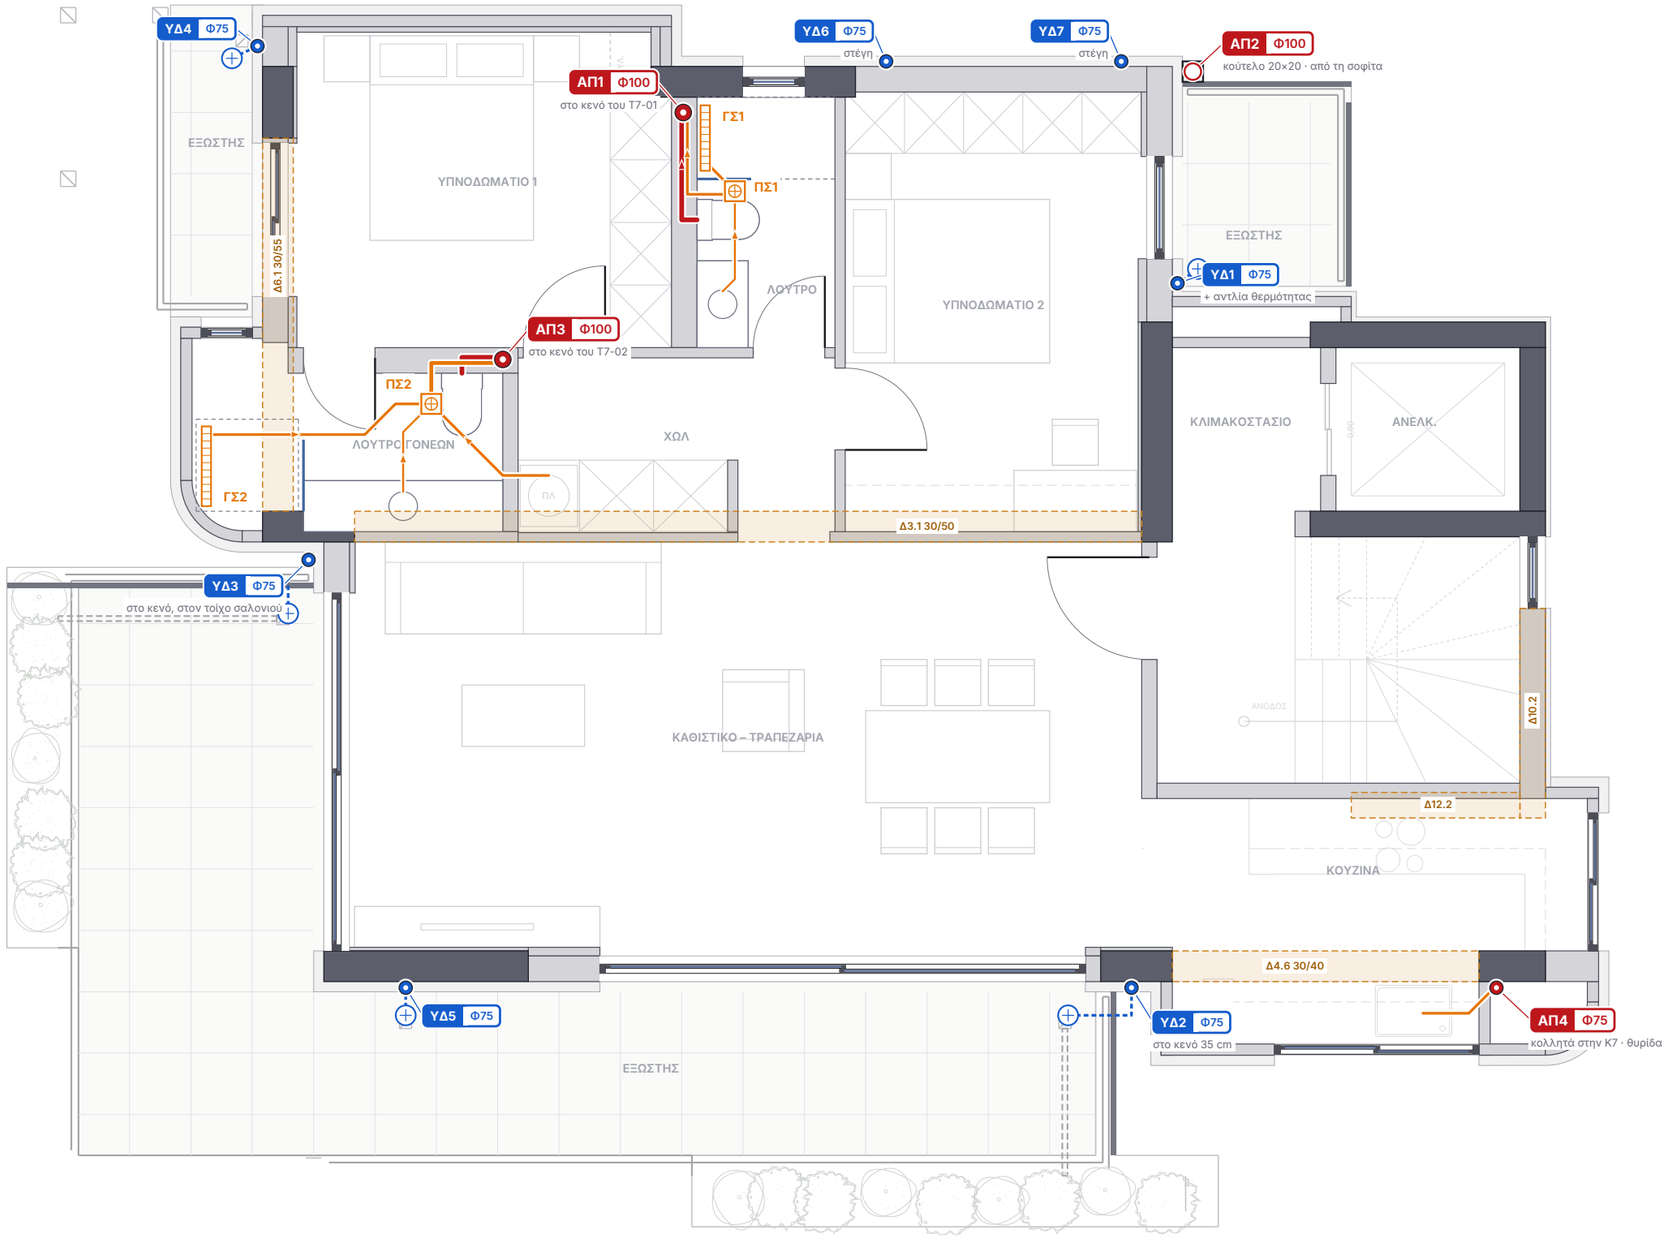

ΥΠΟΜΝΗΜΑ


- Λύματα: λεκάνη Φ90 · στήλη / αγωγός Φ100
- Ακάθαρτα: Φ40 νιπτήρας · Φ50 ντους, νεροχύτης, πλυντήριο · Φ75 έξοδος πατοσίφωνου
- Κατακόρυφη στήλη λυμάτων ΑΠ
- Στήλη που περνά / σταματά (χωρίς σύνδεση στον όροφο)
- Πατοσίφωνο ΠΣ (σιφώνι δαπέδου με σχάρα)
- Γραμμικό σιφώνι ντους ΓΣ → πατοσίφωνο
- Υδρορροή ΥΔ Φ75 μέσα στη θερμοπρόσοψη
- Σιφώνι ομβρίων εξώστη, πλευρική έξοδος
- Δοκός (ξυλότυποι Σ2–Σ7) – ΚΑΜΙΑ οπή

B

ΕΡΓΟ	ΘΕΜΑ ΣΧΕΔΙΟΥ	ΒΑΣΗ	ΑΡ. ΣΧΕΔΙΟΥ
ΠΕΝΤΑΟΡΟΦΟ ΚΤΗΡΙΟ ΚΑΤΟΙΚΙΩΝ – ΑΡΓΥΡΟΥΠΟΛΗ Κωνσταντινουπόλεως 12 & Αγ. Βαρβάρας · Ο.Τ. 103-15 Εργοδότης: INTERKAT Α.Ε. · Κατασκευή: ARKAD Ι.Κ.Ε.	**Α΄·Β΄·Γ΄ ΟΡΟΦΟΣ – ΑΠΟΧΕΤΕΥΣΗ** R19 · λύματα · ακάθαρτα · αερισμοί · όμβρια · οπές πλακών Τυπικός όροφος (Β1) · λεπτομέρειες στο ΑΠ-07	Σ4 / Σ5 · τοιχοποιίες τυπικού R26	**ΑΠ-03** **Κλίμακα 1:60 · Α3** 10/11/2026 · R19

ΚΑΤΟΨΗ Δ΄ ΟΡΟΦΟΥ – ΑΠΟΧΕΤΕΥΣΗ & ΥΔΡΟΡΡΟΕΣ

Κλίμακα 1:60

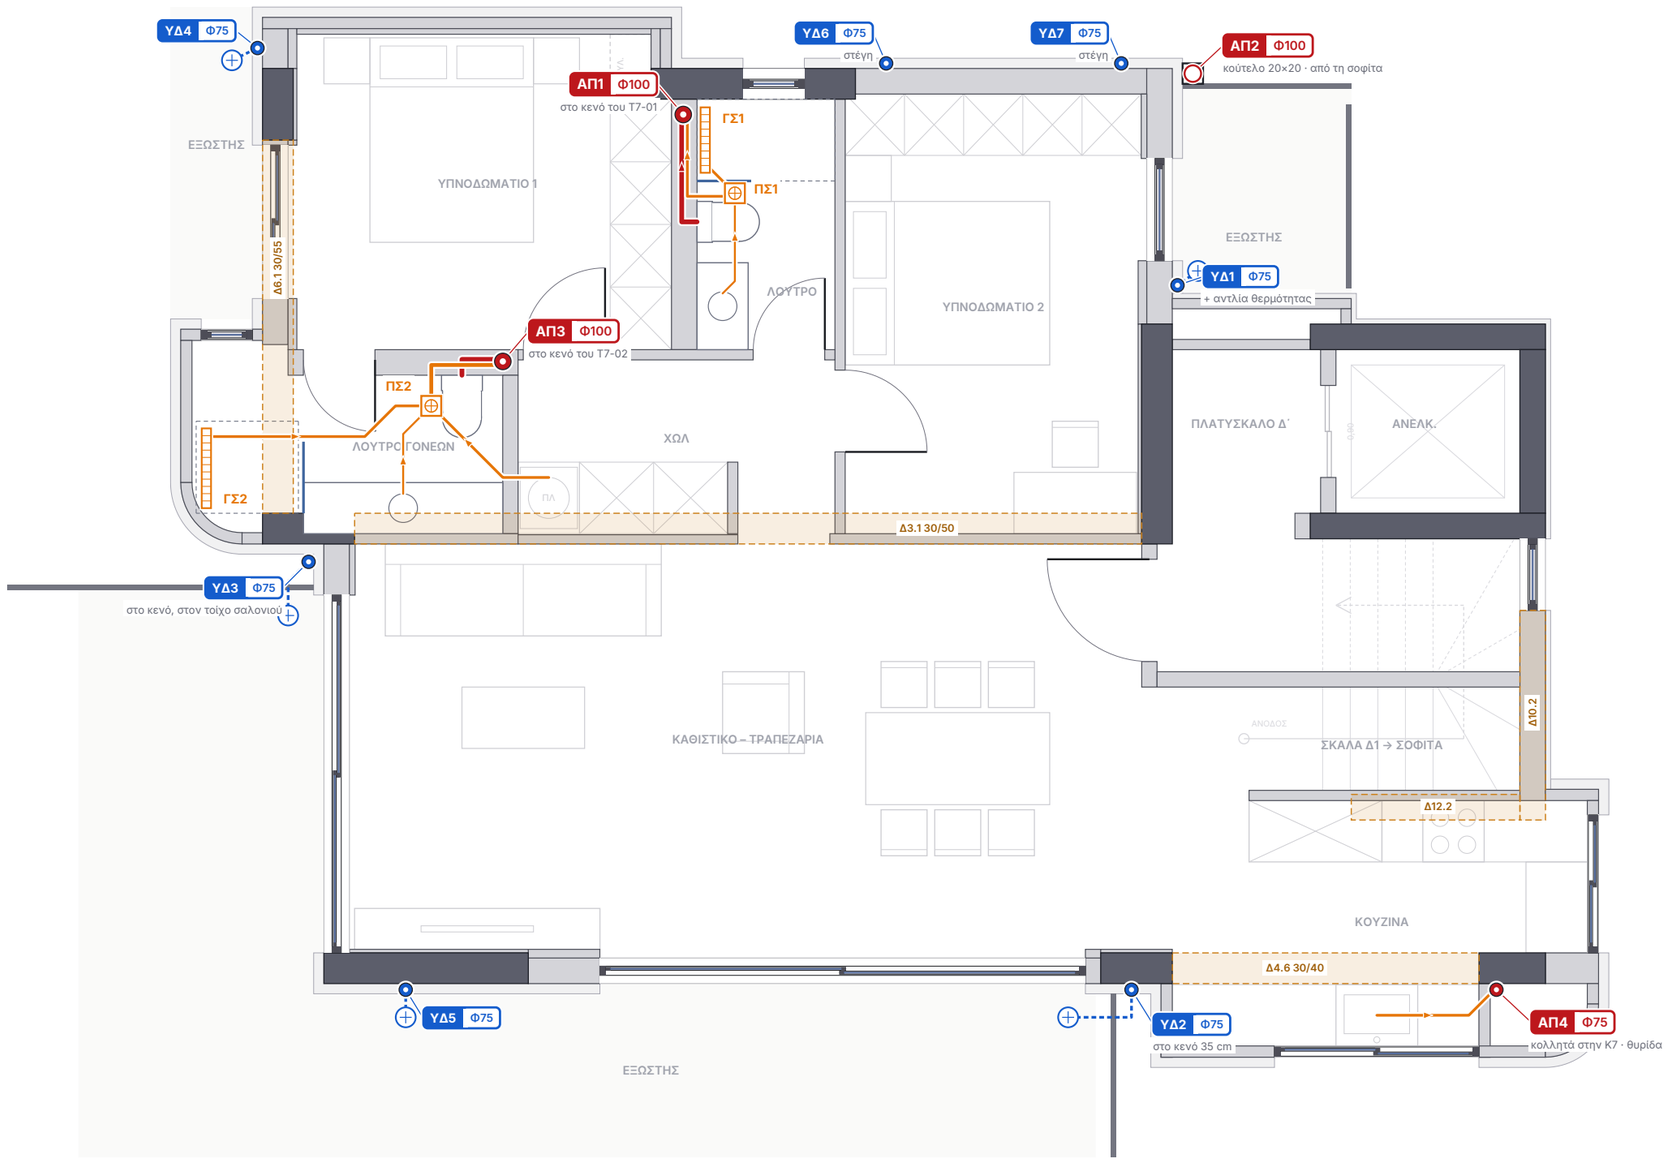

0 1 2 5 m

ΥΠΟΜΝΗΜΑ


- Λύματα: λεκάνη Φ90 · στήλη / αγωγός Φ100
- Ακάθαρτα: Φ40 νιπτήρας · Φ50 ντους, νεροχύτης, πλυντήριο · Φ75 έξοδος πατοσίφωνου
- Κατακόρυφη στήλη λυμάτων ΑΠ
- Στήλη που περνά / σταματά (χωρίς σύνδεση στον όροφο)
- Πατοσίφωνο ΠΣ (σιφώνι δαπέδου με σχάρα)
- Γραμμικό σιφώνι ντους ΓΣ → πατοσίφωνο
- Υδρορροή ΥΔ Φ75 μέσα στη θερμοπρόσοψη
- Σιφώνι ομβρίων εξώστη, πλευρική έξοδος
- Δοκός (ξυλότυποι Σ2–Σ7) – ΚΑΜΙΑ οπή
- Αερισμός ΚΑ Φ75 (βγαίνει έξω και ανεβαίνει στη θερμοπρόσοψη)

B

ΕΡΓΟ	ΘΕΜΑ ΣΧΕΔΙΟΥ	ΒΑΣΗ	ΑΡ. ΣΧΕΔΙΟΥ
ΠΕΝΤΑΟΡΟΦΟ ΚΤΗΡΙΟ ΚΑΤΟΙΚΙΩΝ – ΑΡΓΥΡΟΥΠΟΛΗ Κωνσταντινουπόλεως 12 & Αγ. Βαρβάρας · Ο.Τ. 103-15 Εργοδότης: INTERKAT Α.Ε. · Κατασκευή: ARKAD Ι.Κ.Ε.	**Δ΄ ΟΡΟΦΟΣ – ΑΠΟΧΕΤΕΥΣΗ** R19 · λύματα · ακάθαρτα · αερισμοί · όμβρια · οπές πλακών Δ1 κάτω επίπεδο · λουτρά όπως ο τυπικός (ΑΠ-07)	Σ7 · τοιχοποιίες Δ΄ R05	**ΑΠ-04** **Κλίμακα 1:60 · Α3** 10/11/2026 · R19

ΚΑΤΟΨΗ ΣΟΦΙΤΑΣ – ΑΠΟΧΕΤΕΥΣΗ & ΑΕΡΙΣΜΟΙ

Κλίμακα 1:60

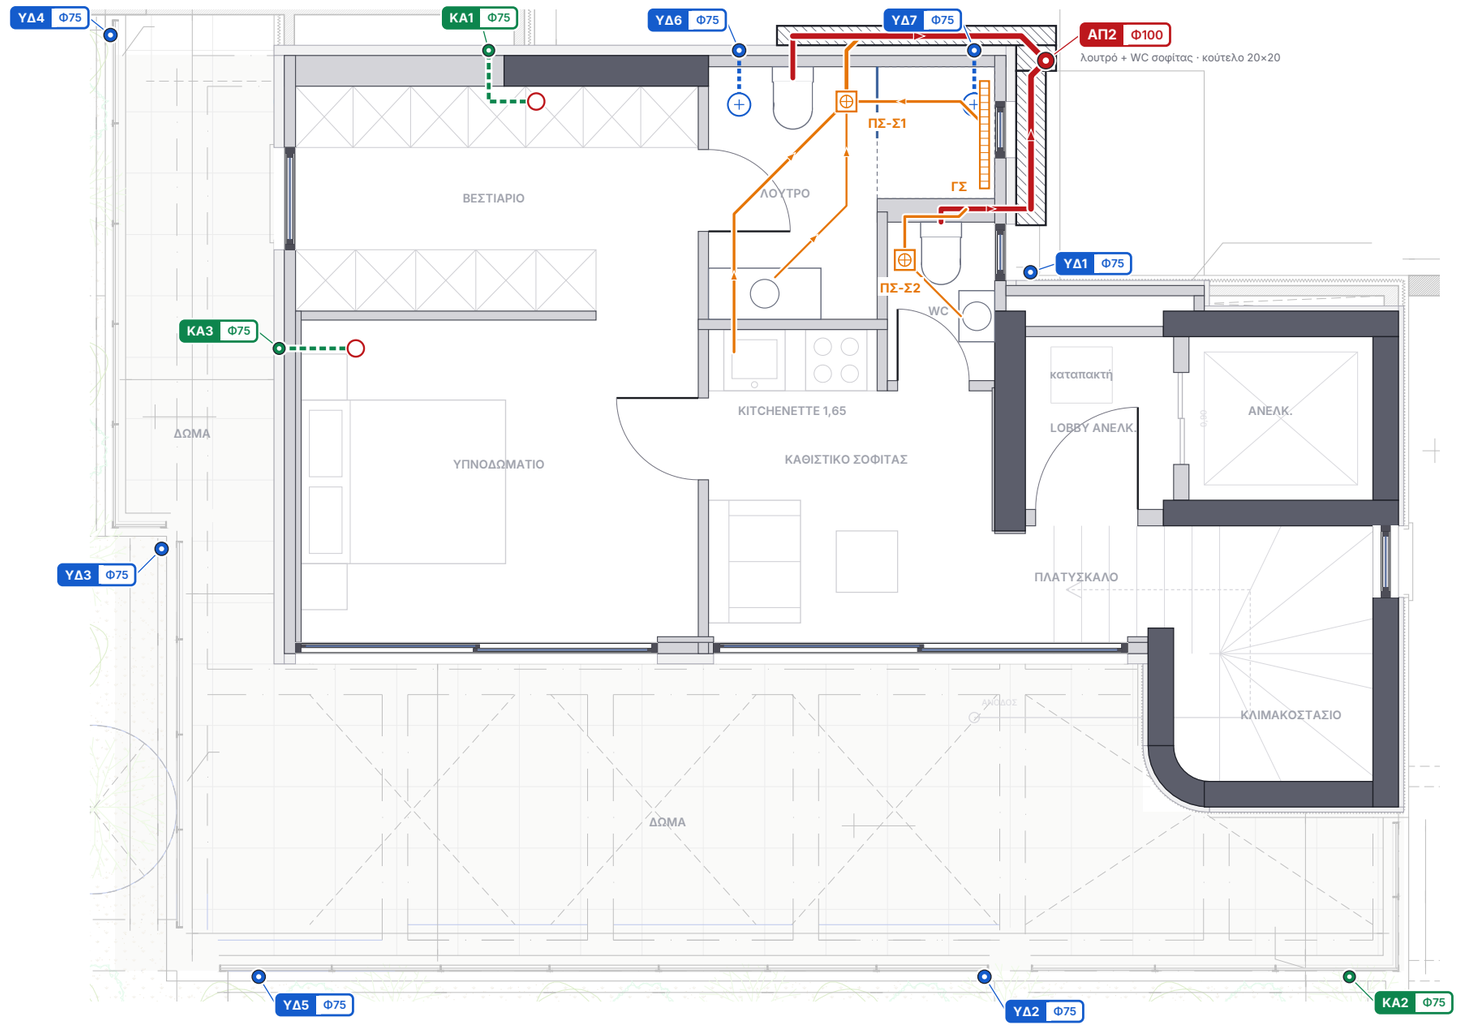

0 1 2 5 m

ΥΠΟΜΝΗΜΑ

- Λύματα: λεκάνη Φ90 · στήλη / αγωγός Φ100
- Ακάθαρτα: Φ40 νιπτήρας · Φ50 ντους, νεροχύτης, πλυντήριο · Φ75 έξοδος πατοσίφωνου
- Αερισμός ΚΑ Φ75 (βγαίνει έξω και ανεβαίνει στη θερμοπρόσοψη)
- Κατακόρυφη στήλη λυμάτων ΑΠ
- Στήλη που περνά / σταματά (χωρίς σύνδεση στον όροφο)
- Πατοσίφωνο ΠΣ (σιφώνι δαπέδου με σχάρα)
- Γραμμικό σιφώνι ντους ΓΣ → πατοσίφωνο
- Κούτελο (κλειστό κανάλι γύρω από αγωγό)
- Άνοδος αερισμού στη θερμοπρόσοψη
- Υδρορροή ΥΔ Φ75 μέσα στη θερμοπρόσοψη

B

ΕΡΓΟ

ΠΕΝΤΑΟΡΟΦΟ ΚΤΗΡΙΟ ΚΑΤΟΙΚΙΩΝ – ΑΡΓΥΡΟΥΠΟΛΗ
Κωνσταντινουπόλεως 12 & Αγ. Βαρβάρας · Ο.Τ. 103-15
Εργοδότης: INTERKAT Α.Ε. · Κατασκευή: ARKAD Ι.Κ.Ε.

ΘΕΜΑ ΣΧΕΔΙΟΥ

ΣΟΦΙΤΑ – ΑΠΟΧΕΤΕΥΣΗ & ΑΕΡΙΣΜΟΙ
R19 · λύματα · ακάθαρτα · αερισμοί · όμβρια · οπές πλακών
Δ1 πάνω επίπεδο · έξοδοι λουτρού / WC · κούτελα · λεπτομέρεια στο ΑΠ-08

ΒΑΣΗ


A-10-S · A-30-ΒΒ · Σ7 / Σ8 · τοιχοποιίες σοφίτας R04

ΑΡ. ΣΧΕΔΙΟΥ


ΑΠ-05
Κλίμακα 1:60 · Α3
10/11/2026 · R19

ΙΣΟΓΕΙΟ – ΛΕΠΤΟΜΕΡΕΙΕΣ ΥΓΡΩΝ ΧΩΡΩΝ


Κλίμακα 1:25

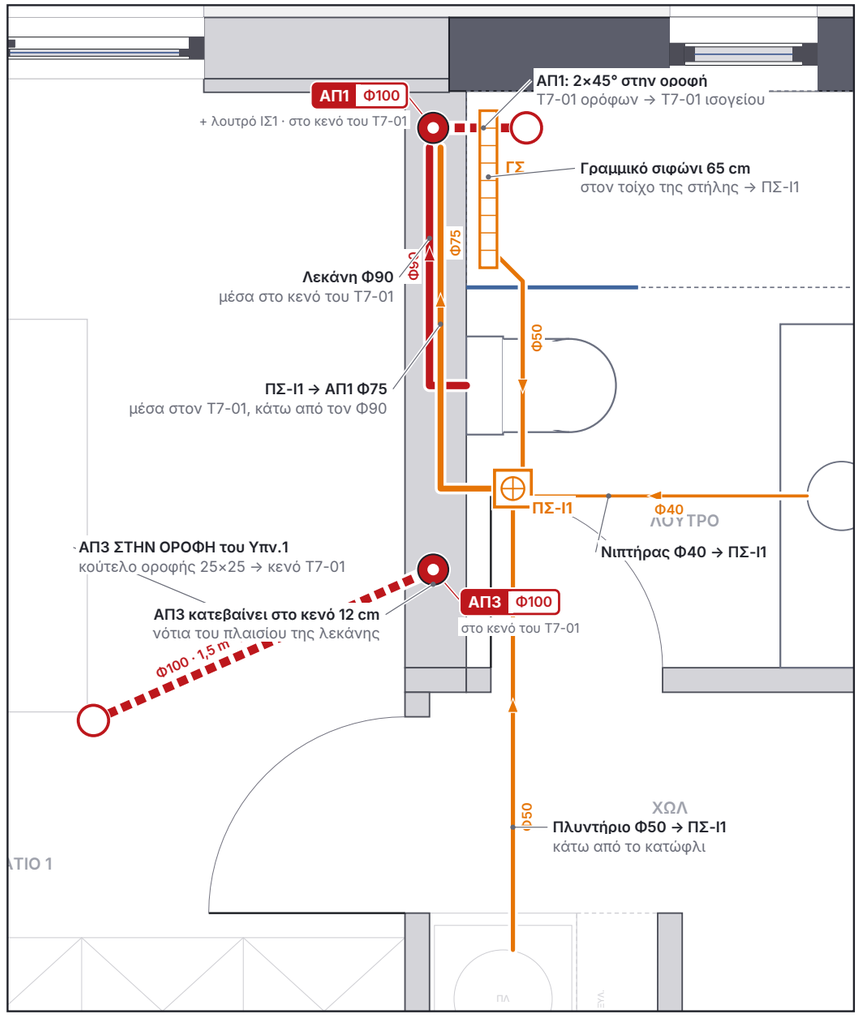

1 **ΛΟΥΤΡΟ ΙΣΟΓΕΙΟΥ → ΑΠ1 · ΑΠ3 ΣΤΟ ΚΕΝΟ ΤΟΥ Τ7-01** Κλίμακα 1:25

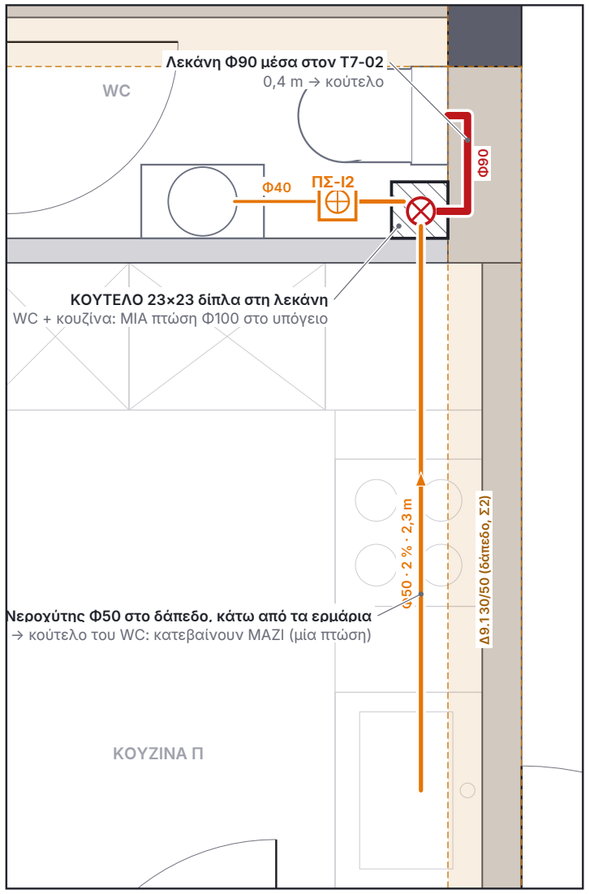

2 **WC + ΚΟΥΖΙΝΑ – ΚΟΥΤΕΛΟ** Κλίμακα 1:25

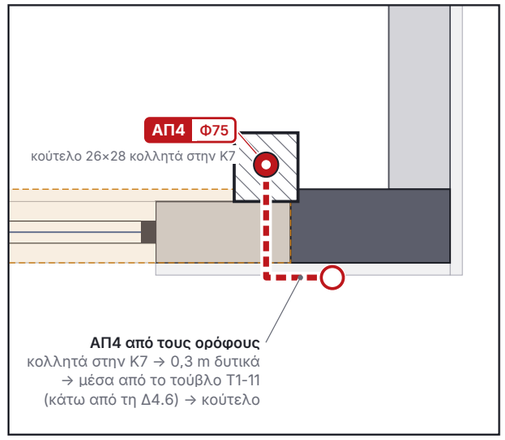

3 **ΑΠ4 ΣΤΗΝ Κ7** Κλίμακα 1:25

ΥΠΟΜΝΗΜΑ


- Λύματα: λεκάνη Φ90 · στήλη / αγωγός Φ100
- Ακάθαρτα: Φ40 νιπτήρας · Φ50 ντους, νεροχύτης, πλυντήριο · Φ75 έξοδος πατοσίφωνου
- Αγωγός στην οροφή του ορόφου (μετατόπιση στήλης 2×45°)
- Κατακόρυφη στήλη λυμάτων ΑΠ
- Στήλη που περνά / σταματά (χωρίς σύνδεση στον όροφο)
- Πτώση στον κάτω όροφο
- Πατοσίφωνο ΠΣ (σιφώνι δαπέδου με σχάρα)
- Γραμμικό σιφώνι ντους ΓΣ → πατοσίφωνο
- Κούτελο (κλειστό κανάλι γύρω από αγωγό)
- Δοκός (ξυλότυποι Σ2–Σ7) – ΚΑΜΙΑ οπή

B


ΕΡΓΟ	ΘΕΜΑ ΣΧΕΔΙΟΥ	ΒΑΣΗ	ΑΡ. ΣΧΕΔΙΟΥ
ΠΕΝΤΑΟΡΟΦΟ ΚΤΗΡΙΟ ΚΑΤΟΙΚΙΩΝ – ΑΡΓΥΡΟΥΠΟΛΗ Κωνσταντινουπόλεως 12 & Αγ. Βαρβάρας · Ο.Τ. 103-15 Εργοδότης: INTERKAT Α.Ε. · Κατασκευή: ARKAD Ι.Κ.Ε.	**ΙΣΟΓΕΙΟ – ΛΕΠΤΟΜΕΡΕΙΕΣ ΥΓΡΩΝ ΧΩΡΩΝ** R19 · λύματα · ακάθαρτα · αερισμοί · όμβρια · οπές πλακών Λουτρό · WC / κουζίνα · ΑΠ4 στην Κ7	ΑΠ-02 · τοιχοποιίες ισογείου R13	**ΑΠ-06** **Κλίμακα 1:25 · Α3** 10/11/2026 · R19

Α΄ · Β΄ · Γ΄ · Δ΄ ΟΡΟΦΟΣ – ΛΕΠΤΟΜΕΡΕΙΕΣ ΥΓΡΩΝ ΧΩΡΩΝ


Κλίμακα 1:25

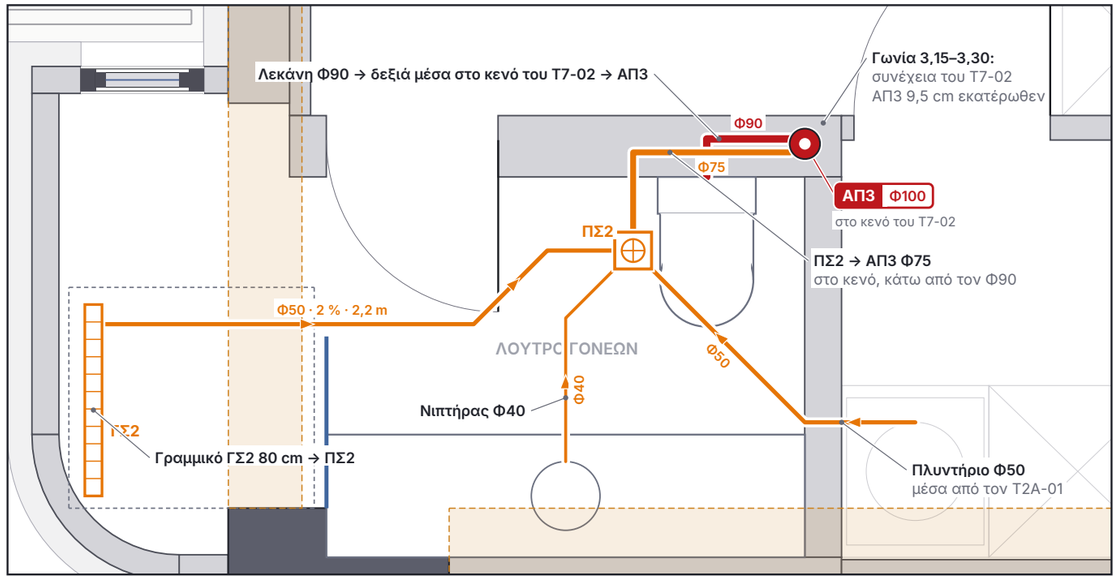


1 ΛΟΥΤΡΟ ΓΟΝΕΩΝ → ΑΠ3 Κλίμακα 1:25

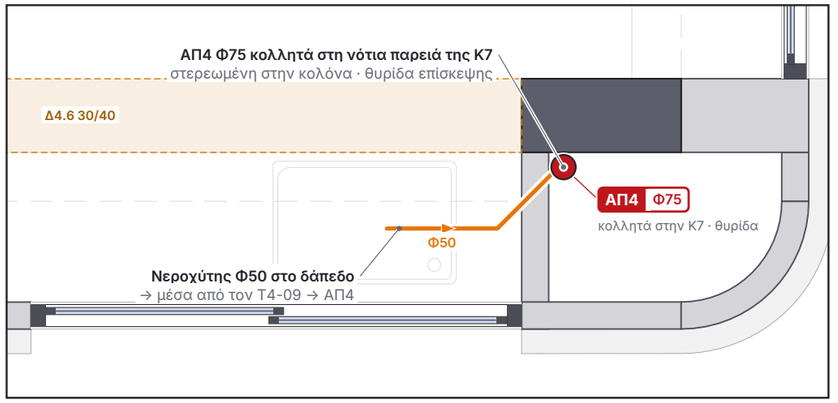


3 ΚΟΥΖΙΝΑ → ΑΠ4 ΚΟΛΛΗΤΑ ΣΤΗΝ Κ7 Κλίμακα 1:25

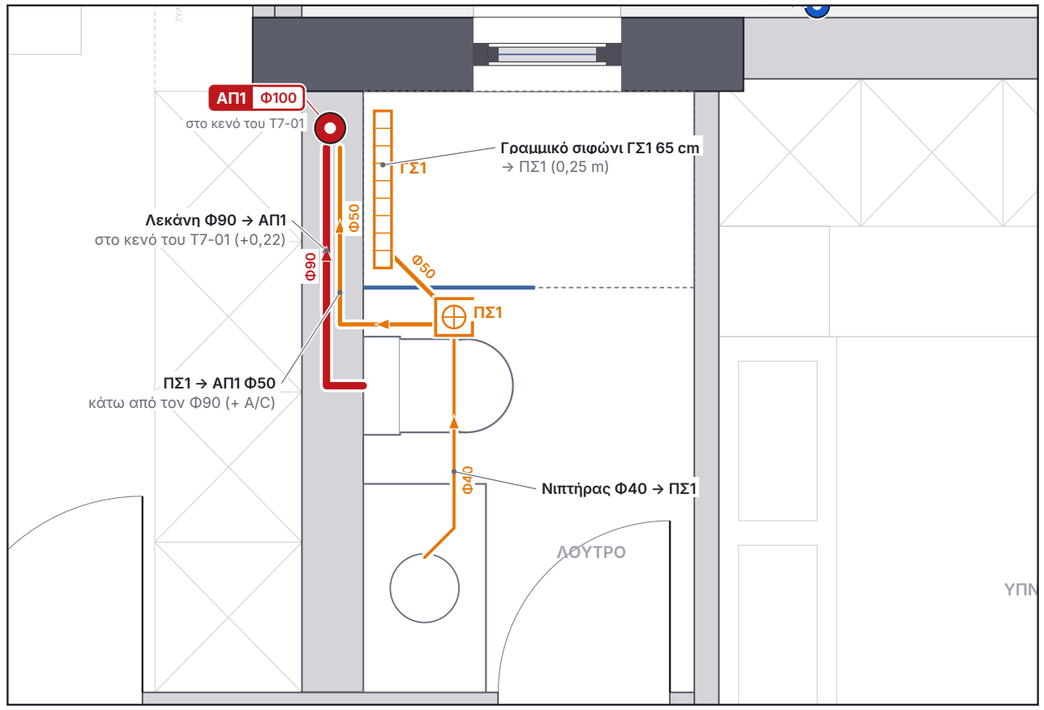

2 ΛΟΥΤΡΟ → ΑΠ1 Κλίμακα 1:25

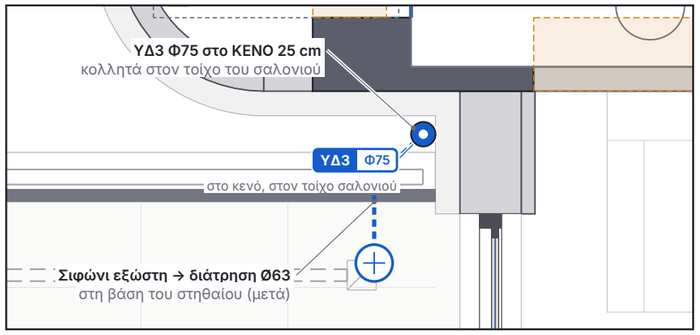

4 ΥΔ3 ΣΤΟ ΚΕΝΟ 25 cm – ΣΤΟΝ ΤΟΙΧΟ ΤΟΥ ΣΑΛΟΝΙΟΥ Κλίμακα 1:25

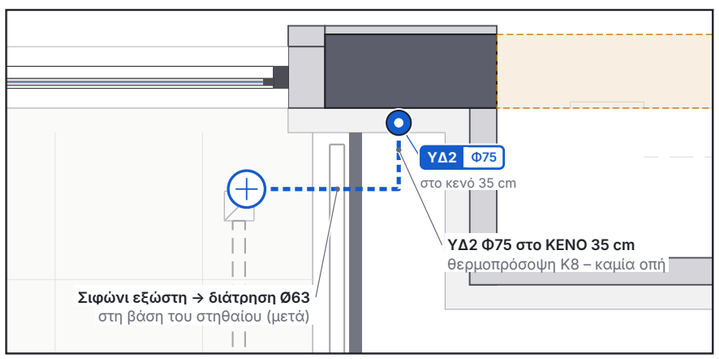

5 ΥΔ2 ΣΤΟ ΚΕΝΟ 35 cm (Κ8) Κλίμακα 1:25

ΥΠΟΜΝΗΜΑ


- Λύματα: λεκάνη Φ90 · στήλη / αγωγός Φ100
- Ακάθαρτα: Φ40 νιπτήρας · Φ50 ντους, νεροχύτης, πλυντήριο · Φ75 έξοδος πατοσίφωνου
- Κατακόρυφη στήλη λυμάτων ΑΠ
- Στήλη που περνά / σταματά (χωρίς σύνδεση στον όροφο)
- Πατοσίφωνο ΠΣ (σιφώνι δαπέδου με σχάρα)
- Γραμμικό σιφώνι ντους ΓΣ → πατοσίφωνο
- Υδρορροή ΥΔ Φ75 μέσα στη θερμοπρόσοψη
- Σιφώνι ομβρίων εξώστη, πλευρική έξοδος
- Δοκός (ξυλότυποι Σ2–Σ7) – ΚΑΜΙΑ οπή

B

ΕΡΓΟ	ΘΕΜΑ ΣΧΕΔΙΟΥ	ΒΑΣΗ	ΑΡ. ΣΧΕΔΙΟΥ
ΠΕΝΤΑΟΡΟΦΟ ΚΤΗΡΙΟ ΚΑΤΟΙΚΙΩΝ – ΑΡΓΥΡΟΥΠΟΛΗ Κωνσταντινουπόλεως 12 & Αγ. Βαρβάρας · Ο.Τ. 103-15 Εργοδότης: INTERKAT Α.Ε. · Κατασκευή: ARKAD Ι.Κ.Ε.	**Α΄·Β΄·Γ΄·Δ΄ – ΛΕΠΤΟΜΕΡΕΙΕΣ ΥΓΡΩΝ ΧΩΡΩΝ** R19 · λύματα · ακάθαρτα · αερισμοί · όμβρια · οπές πλακών Λουτρό γονέων · λουτρό · κουζίνα · υδρορροές στα κενά (ίδια και στον Δ΄)	ΑΠ-03 / ΑΠ-04 · τοιχοποιίες τυπικού R26	**ΑΠ-07** **Κλίμακα 1:25 · Α3** 10/11/2026 · R19

ΣΟΦΙΤΑ – ΛΕΠΤΟΜΕΡΕΙΑ ΥΓΡΩΝ ΧΩΡΩΝ

Κλίμακα 1:20

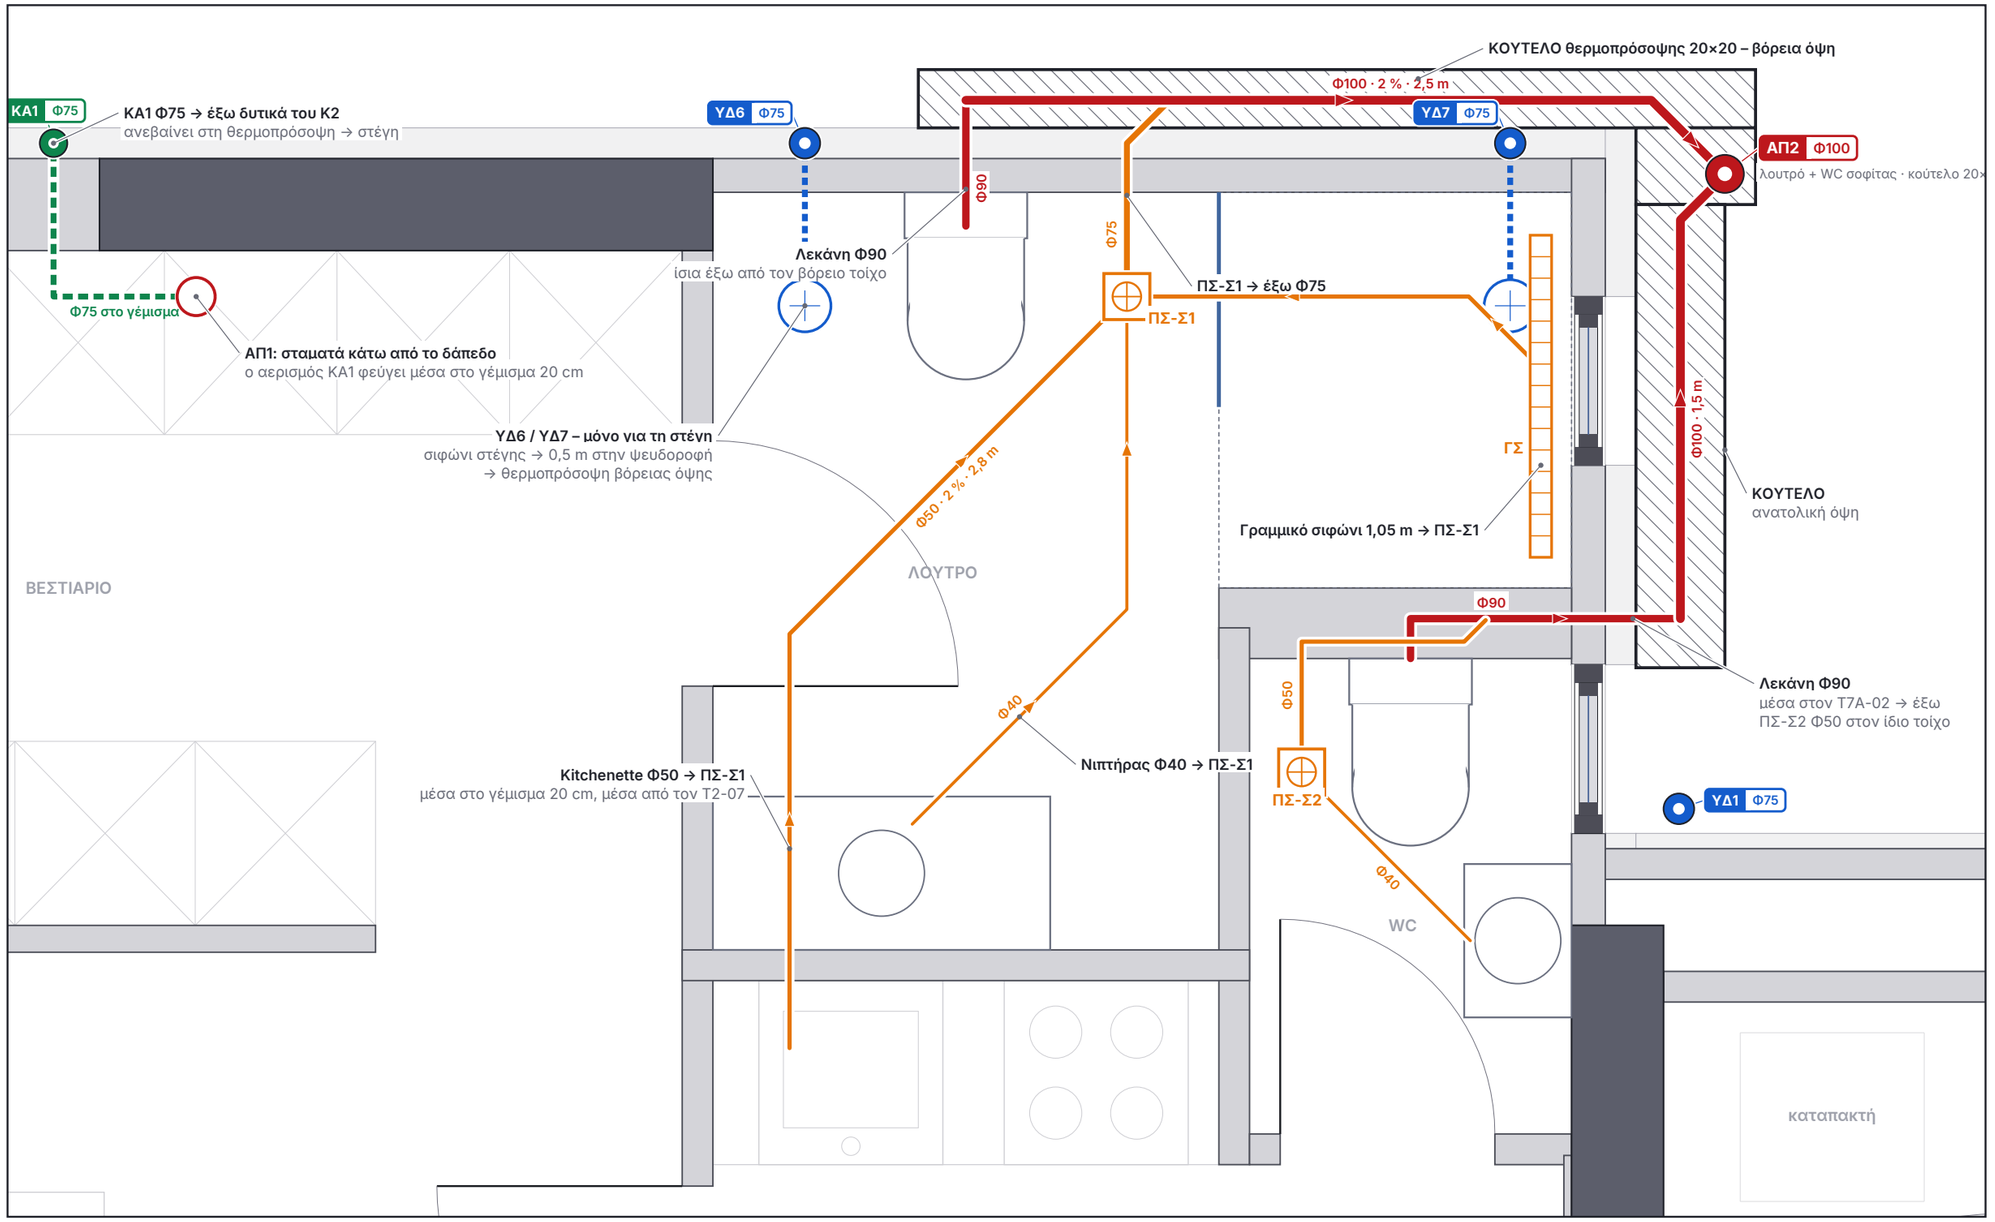

1 **ΛΟΥΤΡΟ · WC · ΚΙΤCHENETTE ΣΟΦΙΤΑΣ – ΕΞΟΔΟΙ & ΚΟΥΤΕΛΑ → ΑΠ2** Κλίμακα 1:20

ΥΠΟΜΝΗΜΑ


- Λύματα: λεκάνη Φ90 · στήλη / αγωγός Φ100
- Ακάθαρτα: Φ40 νιπτήρας · Φ50 ντους, νεροχύτης, πλυντήριο · Φ75 έξοδος πατοσίφωνου
- Αερισμός ΚΑ Φ75 (βγαίνει έξω και ανεβαίνει στη θερμοπρόσοψη)
- Κατακόρυφη στήλη λυμάτων ΑΠ
- Στήλη που περνά / σταματά (χωρίς σύνδεση στον όροφο)
- Πατοσίφωνο ΠΣ (σιφώνι δαπέδου με σχάρα)
- Γραμμικό σιφώνι ντους ΓΣ → πατοσίφωνο
- Κούτελο (κλειστό κανάλι γύρω από αγωγό)
- Άνοδος αερισμού στη θερμοπρόσοψη

B

ΕΡΓΟ	ΘΕΜΑ ΣΧΕΔΙΟΥ	ΒΑΣΗ	ΑΡ. ΣΧΕΔΙΟΥ
ΠΕΝΤΑΟΡΟΦΟ ΚΤΗΡΙΟ ΚΑΤΟΙΚΙΩΝ – ΑΡΓΥΡΟΥΠΟΛΗ Κωνσταντινουπόλεως 12 & Αγ. Βαρβάρας · Ο.Τ. 103-15 Εργοδότης: INTERKAT Α.Ε. · Κατασκευή: ARKAD Ι.Κ.Ε.	**ΣΟΦΙΤΑ – ΛΕΠΤΟΜΕΡΕΙΑ ΥΓΡΩΝ ΧΩΡΩΝ** R19 · λύματα · ακάθαρτα · αερισμοί · όμβρια · οπές πλακών Λουτρό · WC · kitchenette · εξωτερικοί Φ100 σε κούτελο	ΑΠ-05 · Α-10-S · Α-30-ΒΒ · τοιχοποιίες σοφίτας R04	**ΑΠ-08** **Κλίμακα 1:20 · Α3** 10/11/2026 · R19

ΚΑΤΑΚΟΡΥΦΟ ΔΙΑΓΡΑΜΜΑ ΑΠΟΧΕΤΕΥΣΗΣ & ΟΜΒΡΙΩΝ

Χωρίς κλίμακα

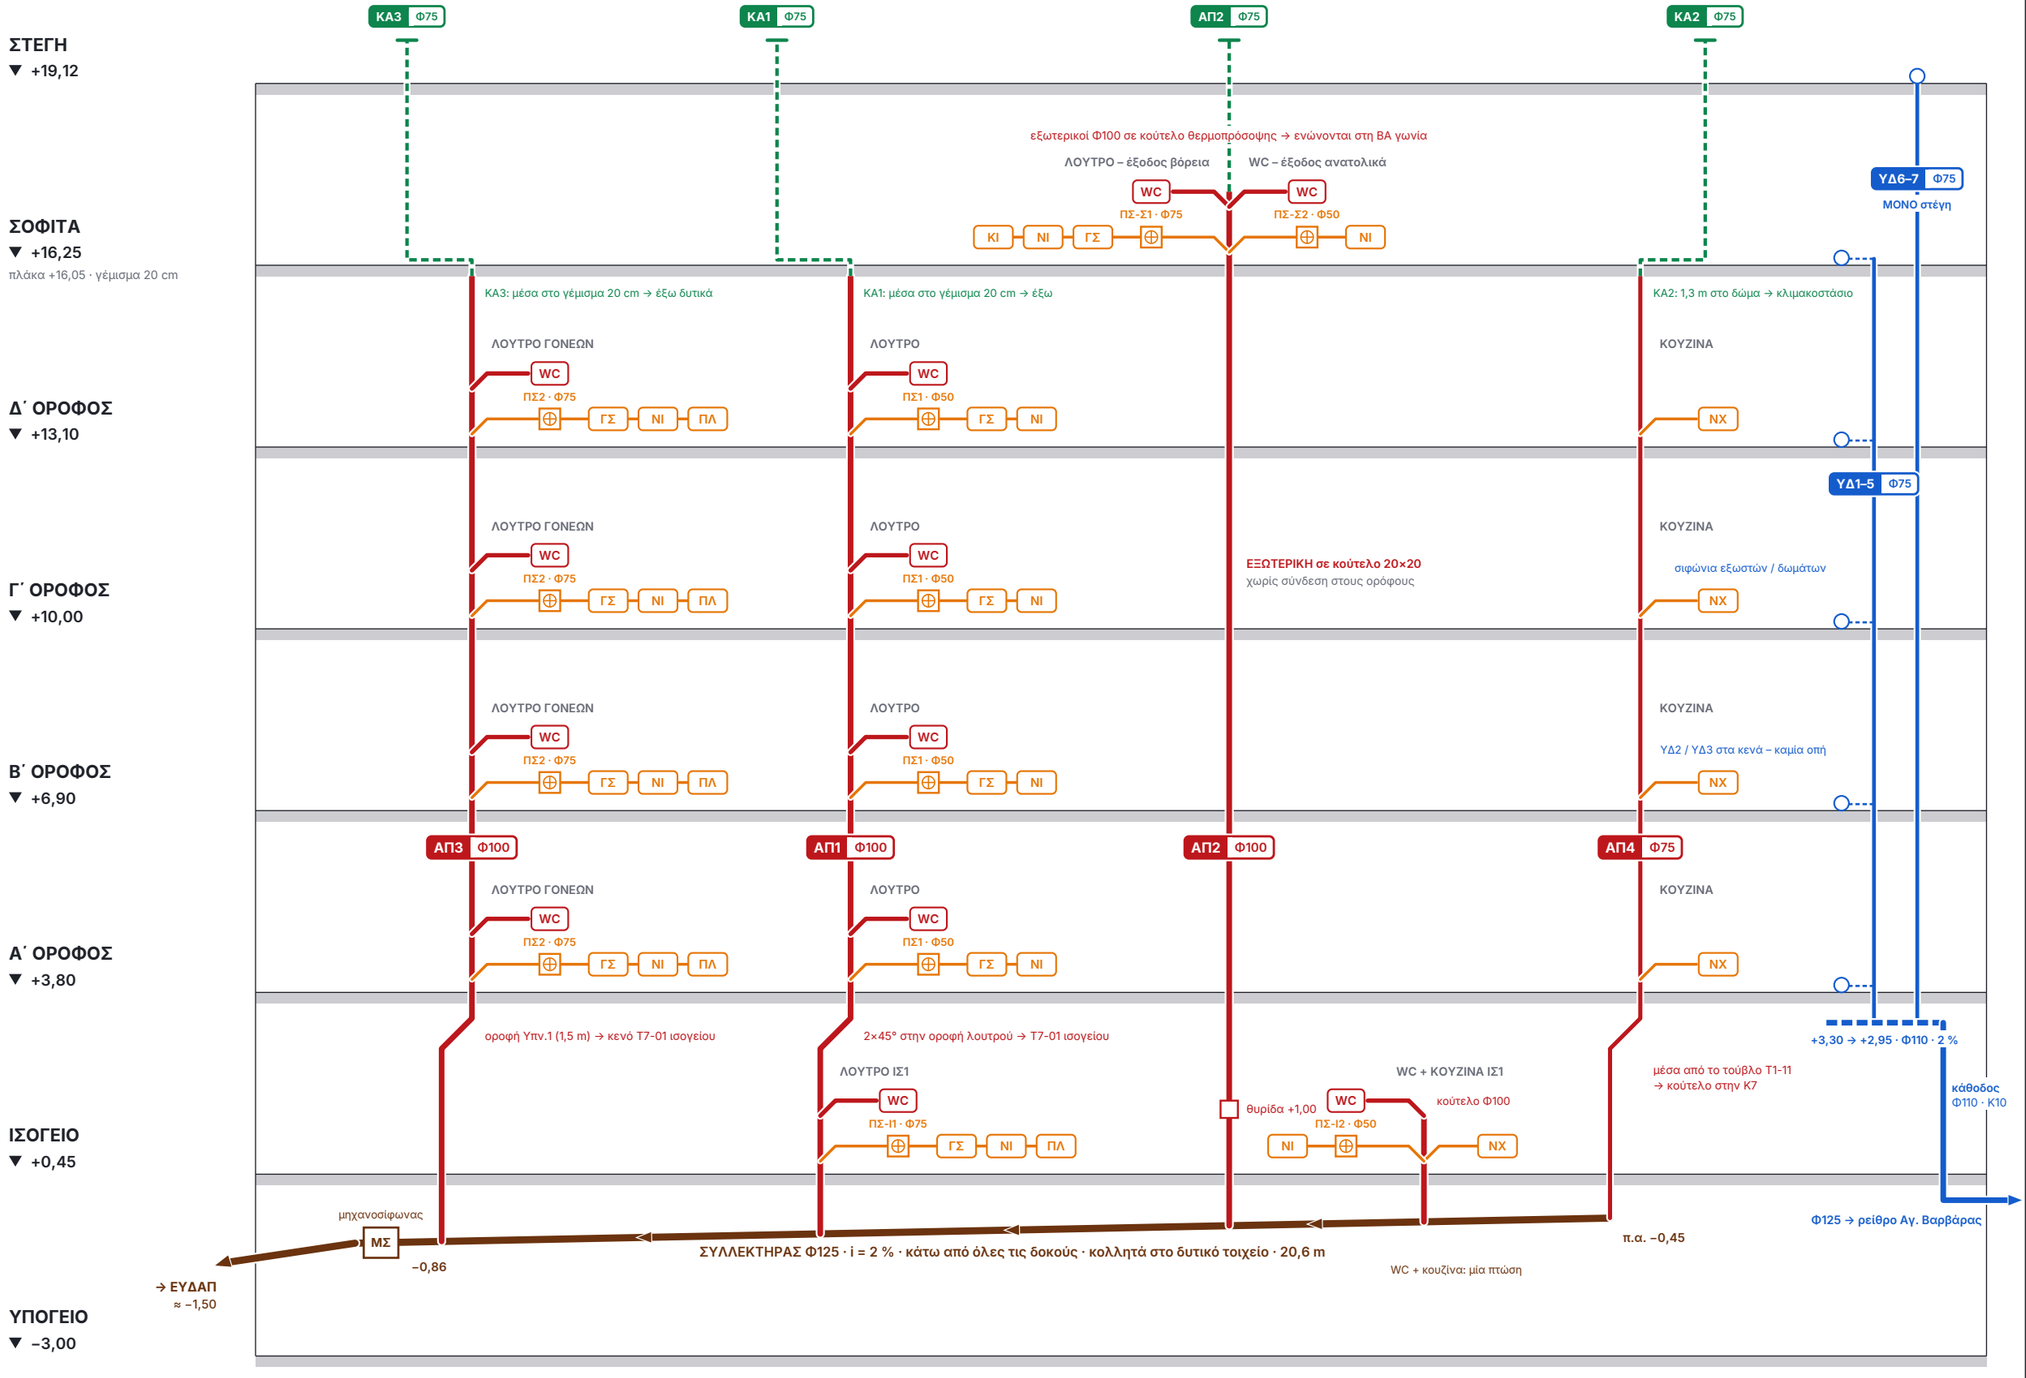

ΥΠΟΜΝΗΜΑ


- Λύματα: λεκάνη Φ90 · στήλη / αγωγός Φ100
- Ακάθαρτα: Φ40 νιπτήρας · Φ50 ντους, νεροχύτης, πλυντήριο · Φ75 έξοδος πατοσίφωνου
- Αερισμός ΚΑ Φ75 (βγαίνει έξω και ανεβαίνει στη θερμοπρόσοψη)
- Όμβρια: συλλεκτήρας / αγωγός
- Συλλεκτήρας ομβρίων ΨΗΛΑ +3,30 (οροφή προβόλων Α΄)
- Συλλεκτήρας / κλάδοι υπογείου, κρεμαστοί κάτω από τις δοκούς
- Πατοσίφωνο ΠΣ (σιφώνι δαπέδου με σχάρα)

ΣΥΝΤΟΜΟΓΡΑΦΙΕΣ

- **WC** λεκάνη κρεμαστή – Φ90 μέσα στον τοίχο λεκάνης
- **ΓΣ** γραμμικό σιφώνι ντους – Φ50 → πατοσίφωνο
- **ΝΙ** νιπτήρας – Φ40 → πατοσίφωνο
- **ΠΛ** πλυντήριο ρούχων – Φ50 → πατοσίφωνο
- **ΚΙ** kitchenette σοφίτας – Φ50 → πατοσίφωνο ΠΣ-Σ1
- **ΝΧ** νεροχύτης κουζίνας (+ πλυντήριο πιάτων) – Φ50
- **ΠΣ** πατοσίφωνο · δίπλα η διατομή εξόδου
- **ΚΑ** αερισμός στήλης Φ75 ως πάνω από τη στέγη

Β


ΕΡΓΟ	ΘΕΜΑ ΣΧΕΔΙΟΥ	ΒΑΣΗ	ΑΡ. ΣΧΕΔΙΟΥ
ΠΕΝΤΑΟΡΟΦΟ ΚΤΗΡΙΟ ΚΑΤΟΙΚΙΩΝ – ΑΡΓΥΡΟΥΠΟΛΗ Κωνσταντινουπόλεως 12 & Αγ. Βαρβάρας · Ο.Τ. 103-15 Εργοδότης: INTERKAT Α.Ε. · Κατασκευή: ARKAD Ι.Κ.Ε.	**ΚΑΤΑΚΟΡΥΦΟ ΔΙΑΓΡΑΜΜΑ** R19 · λύματα · ακάθαρτα · αερισμοί · όμβρια · οπές πλακών Στήλες ΑΠ1–ΑΠ4 · αερισμοί · συλλεκτήρας · όμβρια	ΑΠ-01 … ΑΠ-05	**ΑΠ-09** **Χωρίς κλίμακα · Α3** 10/11/2026 · R19

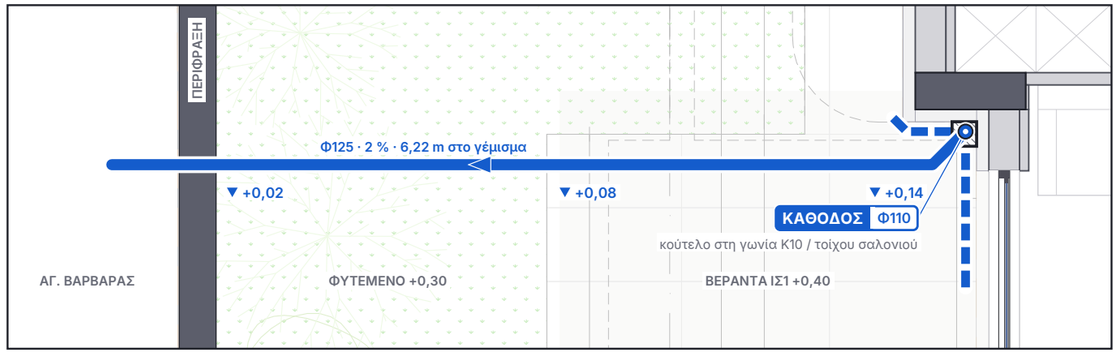

1 **ΚΑΤΟΨΗ – ΚΑΘΟΔΟΣ ΟΜΒΡΙΩΝ ΣΤΗ ΓΩΝΙΑ Κ10 → ΡΕΙΘΡΟ ΑΓ. ΒΑΡΒΑΡΑΣ** Κλίμακα 1:50

ΣΤΑΘΜΕΣ ΑΓΩΓΟΥ Φ125 (εξωτ. Ø125) – κλίση 2 %

Θέση	Απόσταση	Άντυγα	Ράχη	Πάνω από την πλάκα ±0,00	Κάλυψη ως το τελικό
Πόδι καθόδου (γωνία Κ10)	0,38 m	+0,14	+0,26	13,7 cm	13,8 cm
Άκρη βεράντας (x −2,10)	3,42 m	+0,08	+0,20	7,7 cm	9,8 cm
Εσωτ. παρειά περίφραξης	6,22 m	+0,02	+0,15	2,1 cm	15,4 cm
Εξωτ. παρειά περίφραξης	6,52 m	+0,01	+0,14	1,5 cm	5,0 cm

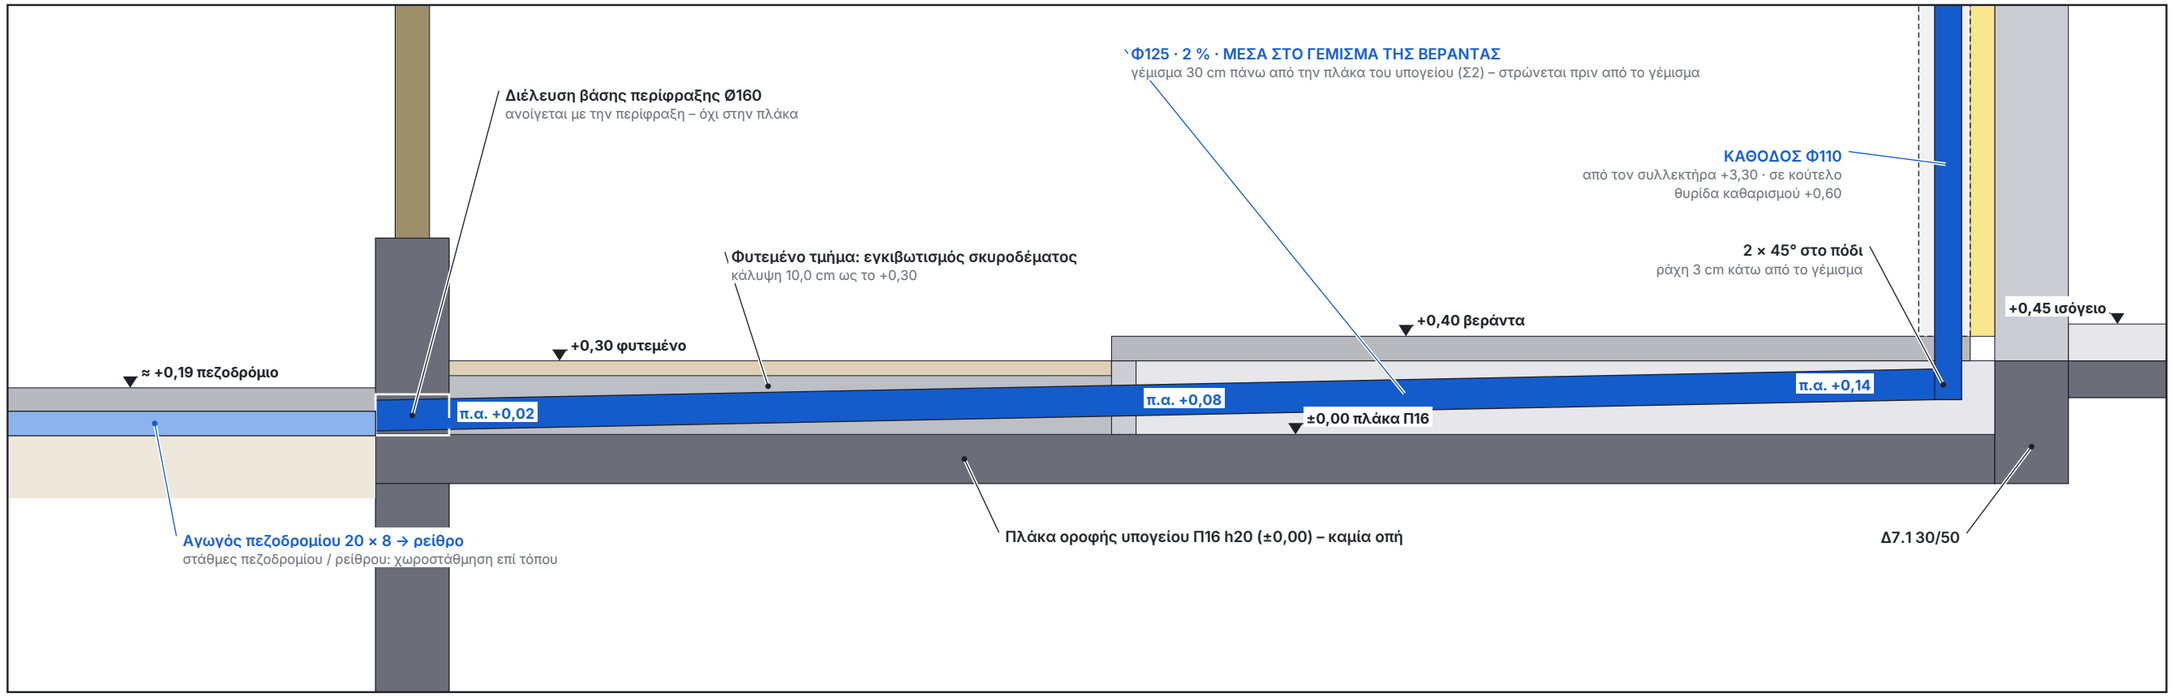

2 **ΤΟΜΗ ΣΤΟΝ ΑΞΟΝΑ ΤΟΥ ΑΓΩΓΟΥ (βλέποντας προς βορρά)** Κλίμακα 1:25

B

ΕΡΓΟ

ΠΕΝΤΑΟΡΟΦΟ ΚΤΗΡΙΟ ΚΑΤΟΙΚΙΩΝ – ΑΡΓΥΡΟΥΠΟΛΗ
Κωνσταντινουπόλεως 12 & Αγ. Βαρβάρας · Ο.Τ. 103-15
Εργοδότης: INTERKAT Α.Ε. · Κατασκευή: ARKAD Ι.Κ.Ε.

ΘΕΜΑ ΣΧΕΔΙΟΥ


ΟΜΒΡΙΑ ΙΣΟΓΕΙΟΥ – ΚΑΘΟΔΟΣ & ΕΞΟΔΟΣ
R19 · λύματα · ακάθαρτα · αερισμοί · όμβρια · οπές πλακών
Κάθοδος Φ110 στην Κ10 · Φ125 στο γέμισμα → Αγ. Βαρβάρας

ΒΑΣΗ

Σ2_ΕΦ · Α-30-ΑΑ · Α-40 · ΑΠ-02

ΑΡ. ΣΧΕΔΙΟΥ

ΑΠ-10
Κλίμακες 1:50 · 1:25 · Α3
10/11/2026 · R19

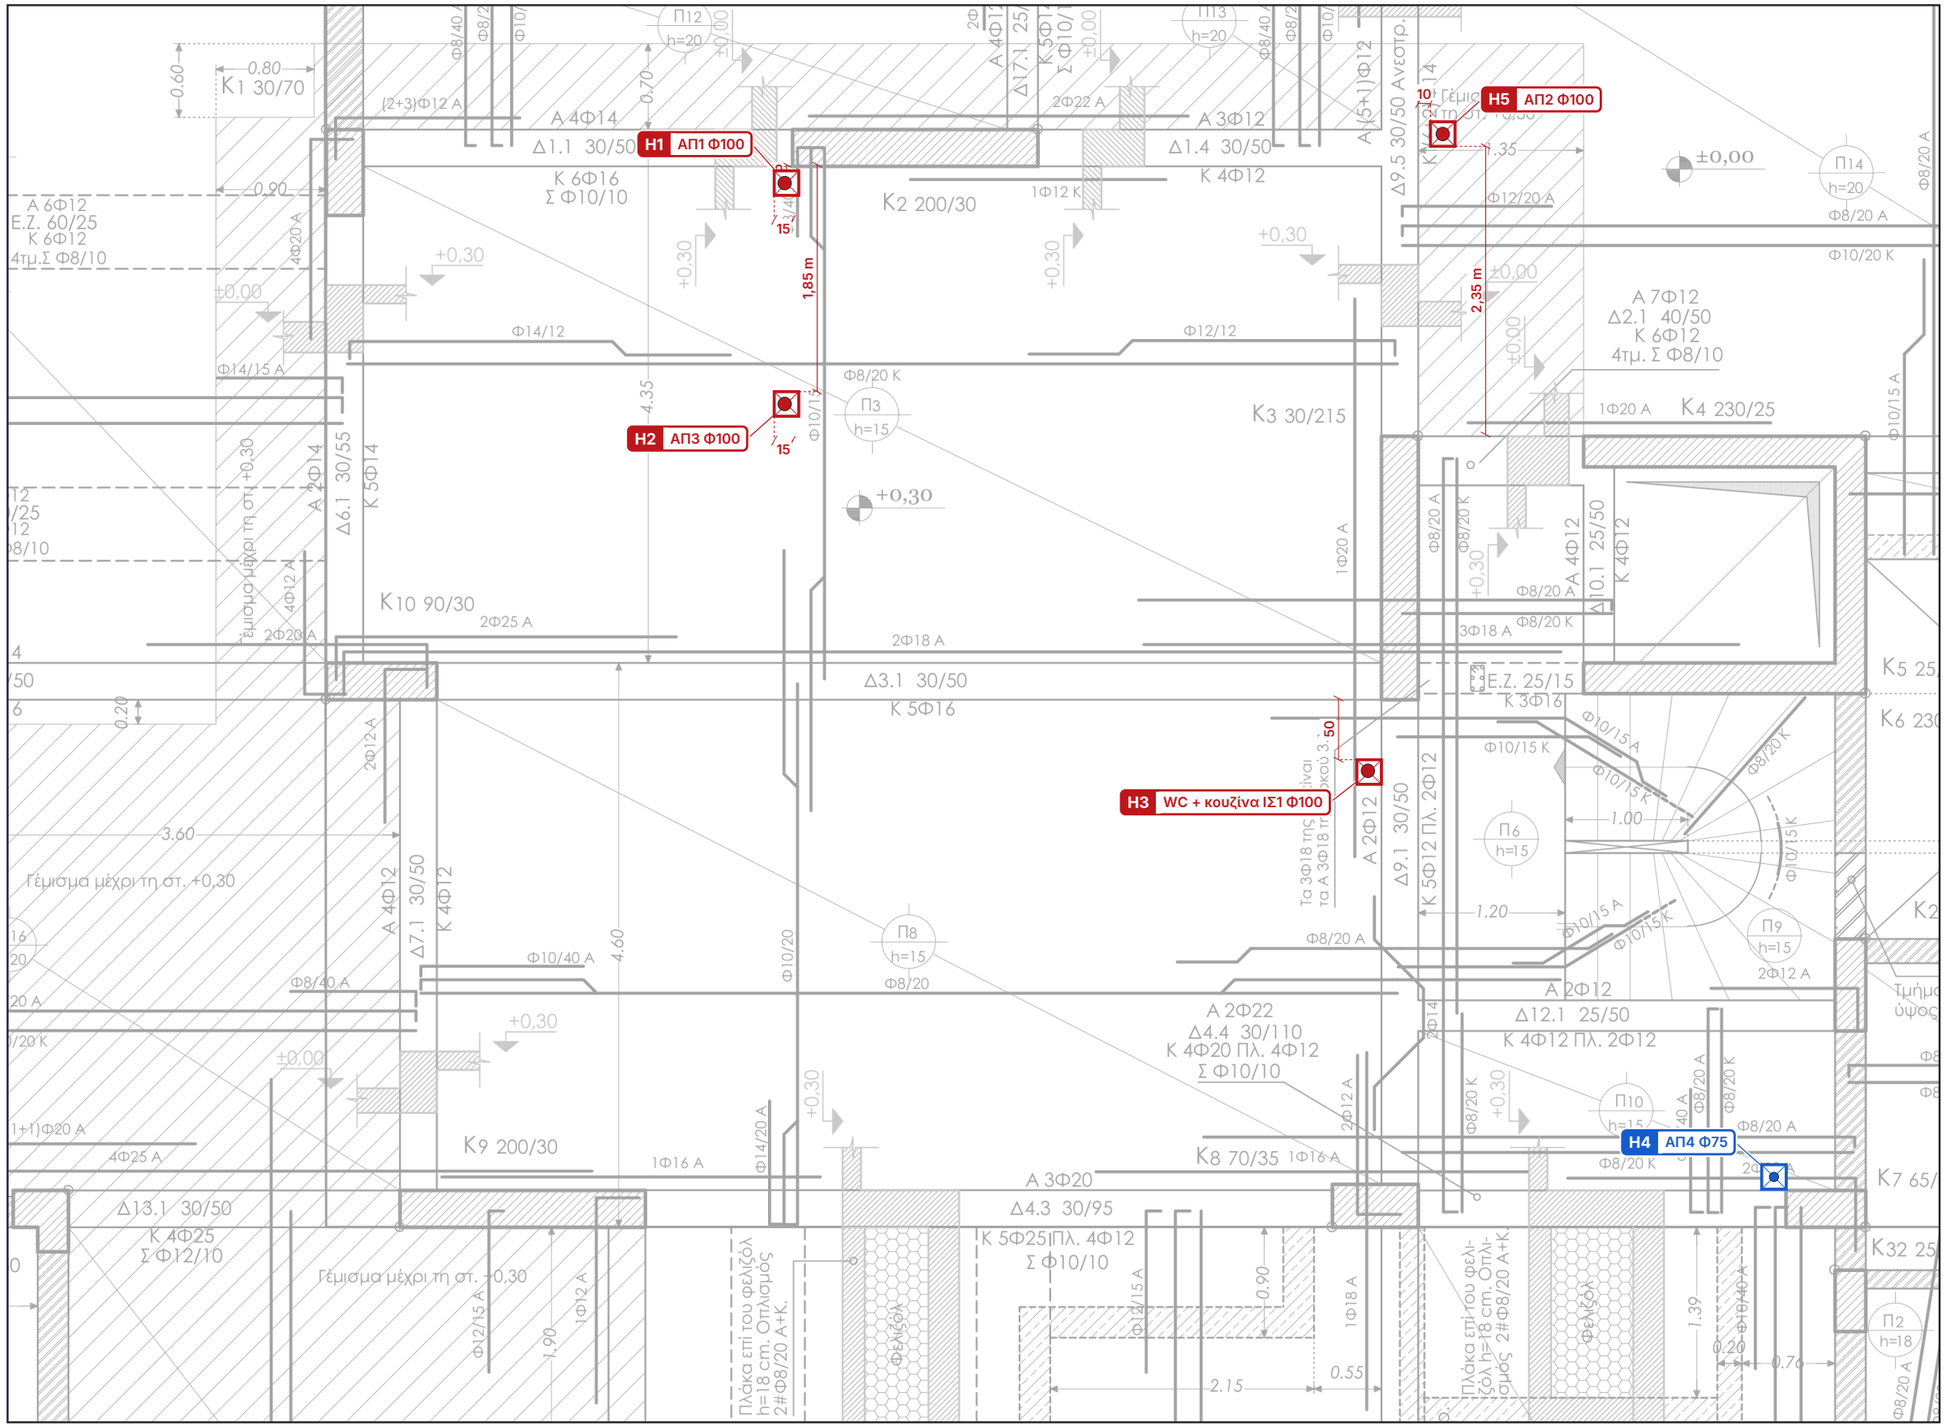

2 ΟΠΕΣ ΠΛΑΚΑΣ ΟΡΟΦΗΣ ΥΠΟΓΕΙΟΥ (Σ2 · +0,30) – κουτιά 20 × 20, διαστάσεις σε cm από παρειές σκυροδέματος Κλίμακα 1:50

ΟΠΕΣ ΠΛΑΚΑΣ Σ2

Όλες κουτί 20 × 20 cm. Η θέση δίνεται ως την ΑΚΜΗ του κουτιού.

H1 **ΑΠ1 Φ100**
δυτ. ακμή 15 δυτ. της Δ παρ. Κ2 · 5 νότια της Ν παρ. Κ2


H2 **ΑΠ3 Φ100**
δυτ. ακμή 15 δυτ. της Δ παρ. Κ2 · 1,85 m νότια της Ν παρ. Κ2

H3 **WC + κουζίνα ΙΣ1 Φ100**
κολλητά στη Δ παρ. Δ9.1 · 50 νότια της Ν παρ. Κ3

H4 **ΑΠ4 Φ75**
ανατ. ακμή στην ευθεία της Δ παρ. Κ7 · κολλητά στη Β παρ. δοκού Κ8–Κ7

H5 **ΑΠ2 Φ100**
10 ανατ. της Α παρ. Δ9.5 · 2,35 m βόρ. της Β παρ. Κ3


X1 **Έξοδος συλλεκτήρα Φ125**
χιτώνιο Ø200 στο ΝΟΤΙΟ ΤΟΙΧΕΙΟ του υπογείου (όχι στην πλάκα) · άξονας 50 cm ανατ. της εσωτ. παρειάς του δυτικού τοιχείου · άντυγα σωλήνα −0,86

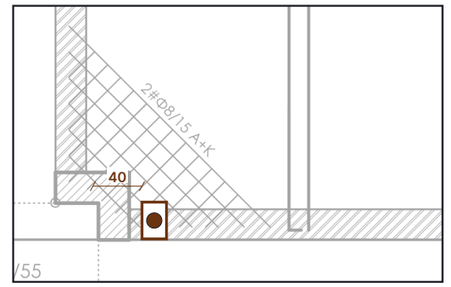

X X1 – ΝΟΤΙΟ ΤΟΙΧΕΙΟ Κλίμακα 1:50

B

ΕΡΓΟ	ΘΕΜΑ ΣΧΕΔΙΟΥ	ΒΑΣΗ	ΑΡ. ΣΧΕΔΙΟΥ
ΠΕΝΤΑΟΡΟΦΟ ΚΤΗΡΙΟ ΚΑΤΟΙΚΙΩΝ – ΑΡΓΥΡΟΥΠΟΛΗ Κωνσταντινουπόλεως 12 & Αγ. Βαρβάρας · Ο.Τ. 103-15 Εργοδότης: INTERKAT Α.Ε. · Κατασκευή: ARKAD Ι.Κ.Ε.	**ΟΠΕΣ ΠΛΑΚΑΣ ΟΡΟΦΗΣ ΥΠΟΓΕΙΟΥ** R19 · λύματα · ακάθαρτα · αερισμοί · όμβρια · οπές πλακών Σ2 (+0,30) · κουτιά 20 × 20 · θέσεις από παρειές σκυροδέματος	Υπόβαθρο: ξυλότυπος Σ2_ΕΦ	**ΑΠ-11** **Κλίμακα 1:50 · Α3** 10/11/2026 · R19

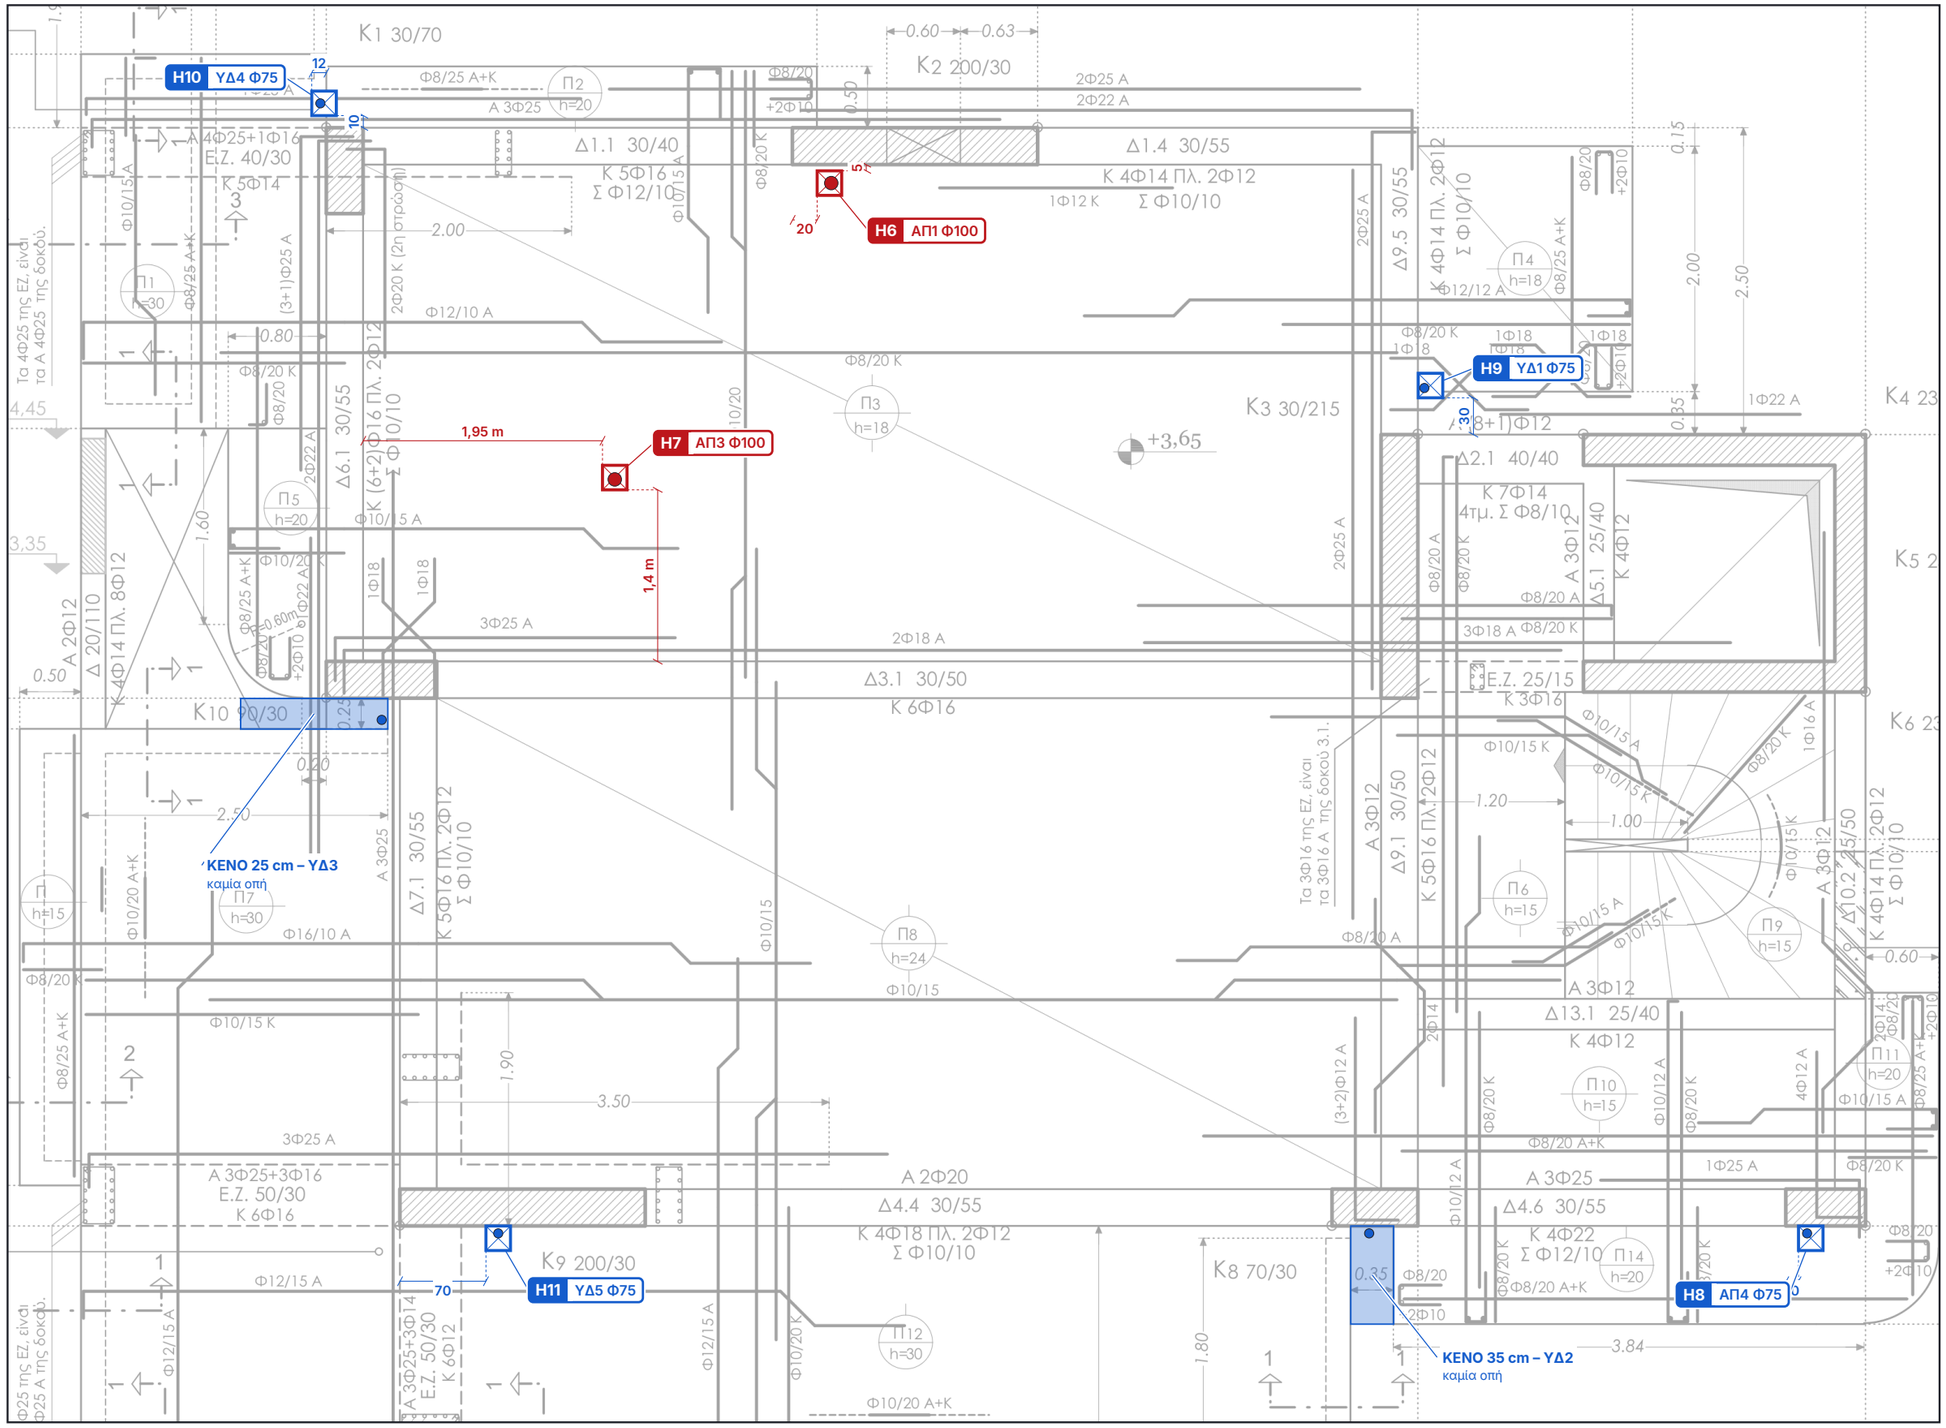

3 **ΟΠΕΣ ΠΛΑΚΑΣ ΟΡΟΦΗΣ ΙΣΟΓΕΙΟΥ (Σ3 · +3,65) – κουτιά 20 × 20, διαστάσεις σε cm από παρειές σκυροδέματος** Κλίμακα 1:50


ΟΠΕΣ ΠΛΑΚΑΣ Σ3

Όλες κουτί 20 × 20 cm. Η θέση δίνεται ως την ΑΚΜΗ του κουτιού.

- **H6** **ΑΠ1 Φ100** — 20 ανατ. της Δ παρ. Κ2 · 5 νότια της Ν παρ. Κ2
- **H7** **ΑΠ3 Φ100** — 1,95 m ανατ. της Α παρ. Δ6.1 · 1,4 m βόρ. της Β παρ. Δ3.1
- **H8** **ΑΠ4 Φ75** — 10 ανατ. της Δ παρ. Κ7 · κολλητά στη Ν παρ. Κ7
- **H9** **ΥΔ1 Φ75** — κολλητά στη Α παρ. Δ9.5 · 30 βόρ. της Β παρ. Κ3
- **H10** **ΥΔ4 Φ75** — δυτ. ακμή 12 δυτ. της Δ παρ. Κ1 · 10 βόρ. της Β παρ. Κ1
- **H11** **ΥΔ5 Φ75** — 70 ανατ. της Δ παρ. Κ9 · κολλητά στη Ν παρ. Κ9

B

ΕΡΓΟ	ΘΕΜΑ ΣΧΕΔΙΟΥ	ΒΑΣΗ	ΑΡ. ΣΧΕΔΙΟΥ
ΠΕΝΤΑΟΡΟΦΟ ΚΤΗΡΙΟ ΚΑΤΟΙΚΙΩΝ – ΑΡΓΥΡΟΥΠΟΛΗ Κωνσταντινουπόλεως 12 & Αγ. Βαρβάρας · Ο.Τ. 103-15 Εργοδότης: INTERKAT Α.Ε. · Κατασκευή: ARKAD Ι.Κ.Ε.	**ΟΠΕΣ ΠΛΑΚΑΣ ΟΡΟΦΗΣ ΙΣΟΓΕΙΟΥ** R19 · λύματα · ακάθαρτα · αερισμοί · όμβρια · οπές πλακών Σ3 (+3,65) · κουτιά 20 × 20 · θέσεις από παρειές σκυροδέματος	Υπόβαθρο: ξυλότυπος Σ3_ΕΦ	**ΑΠ-12** **Κλίμακα 1:50 · A3** 10/11/2026 · R19

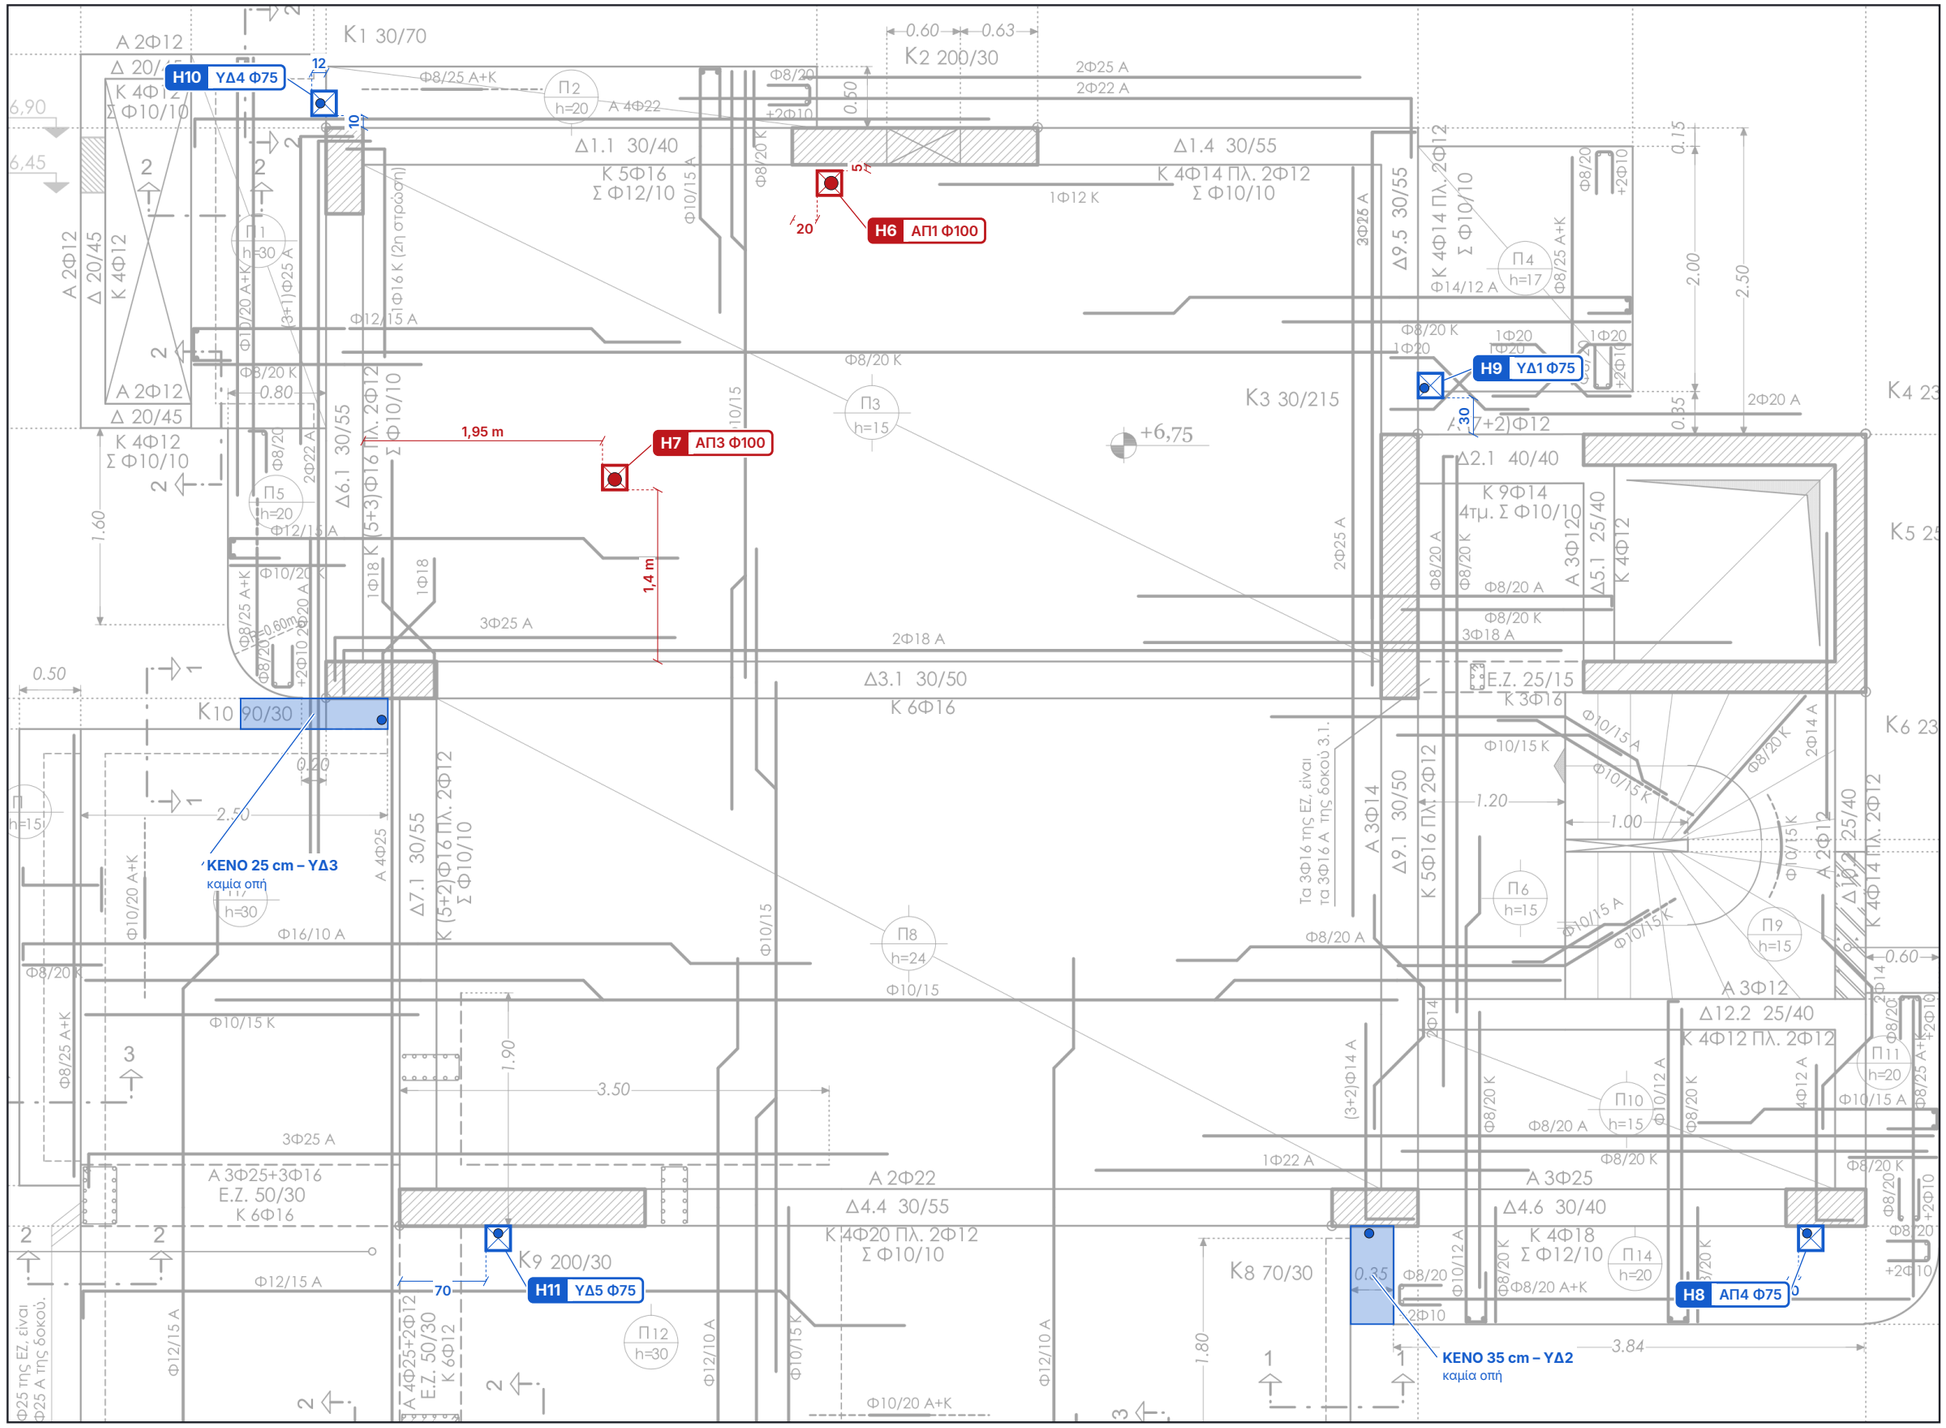

4 **ΟΠΕΣ ΠΛΑΚΑΣ ΟΡΟΦΗΣ Α΄ ΟΡΟΦΟΥ (Σ4 · +6,75) – κουτιά 20 × 20, διαστάσεις σε cm από παρειές σκυροδέματος** Κλίμακα 1:50


ΟΠΕΣ ΠΛΑΚΑΣ Σ4

Όλες κουτί 20 × 20 cm. Η θέση δίνεται ως την ΑΚΜΗ του κουτιού.

- **H6** **ΑΠ1 Φ100** — 20 ανατ. της Δ παρ. Κ2 · 5 νότια της Ν παρ. Κ2
- **H7** **ΑΠ3 Φ100** — 1,95 m ανατ. της Α παρ. Δ6.1 · 1,4 m βόρ. της Β παρ. Δ3.1
- **H8** **ΑΠ4 Φ75** — 10 ανατ. της Δ παρ. Κ7 · κολλητά στη Ν παρ. Κ7
- **H9** **ΥΔ1 Φ75** — κολλητά στη Α παρ. Δ9.5 · 30 βόρ. της Β παρ. Κ3
- **H10** **ΥΔ4 Φ75** — δυτ. ακμή 12 δυτ. της Δ παρ. Κ1 · 10 βόρ. της Β παρ. Κ1
- **H11** **ΥΔ5 Φ75** — 70 ανατ. της Δ παρ. Κ9 · κολλητά στη Ν παρ. Κ9

B

ΕΡΓΟ	ΘΕΜΑ ΣΧΕΔΙΟΥ	ΒΑΣΗ	ΑΡ. ΣΧΕΔΙΟΥ
ΠΕΝΤΑΟΡΟΦΟ ΚΤΗΡΙΟ ΚΑΤΟΙΚΙΩΝ – ΑΡΓΥΡΟΥΠΟΛΗ Κωνσταντινουπόλεως 12 & Αγ. Βαρβάρας · Ο.Τ. 103-15 Εργοδότης: INTERKAT Α.Ε. · Κατασκευή: ARKAD Ι.Κ.Ε.	**ΟΠΕΣ ΠΛΑΚΑΣ ΟΡΟΦΗΣ Α΄ ΟΡΟΦΟΥ** R19 · λύματα · ακάθαρτα · αερισμοί · όμβρια · οπές πλακών Σ4 (+6,75) · κουτιά 20 × 20 · θέσεις από παρειές σκυροδέματος	Υπόβαθρο: ξυλότυπος Σ4_ΕΦ	**ΑΠ-13** **Κλίμακα 1:50 · Α3** 10/11/2026 · R19

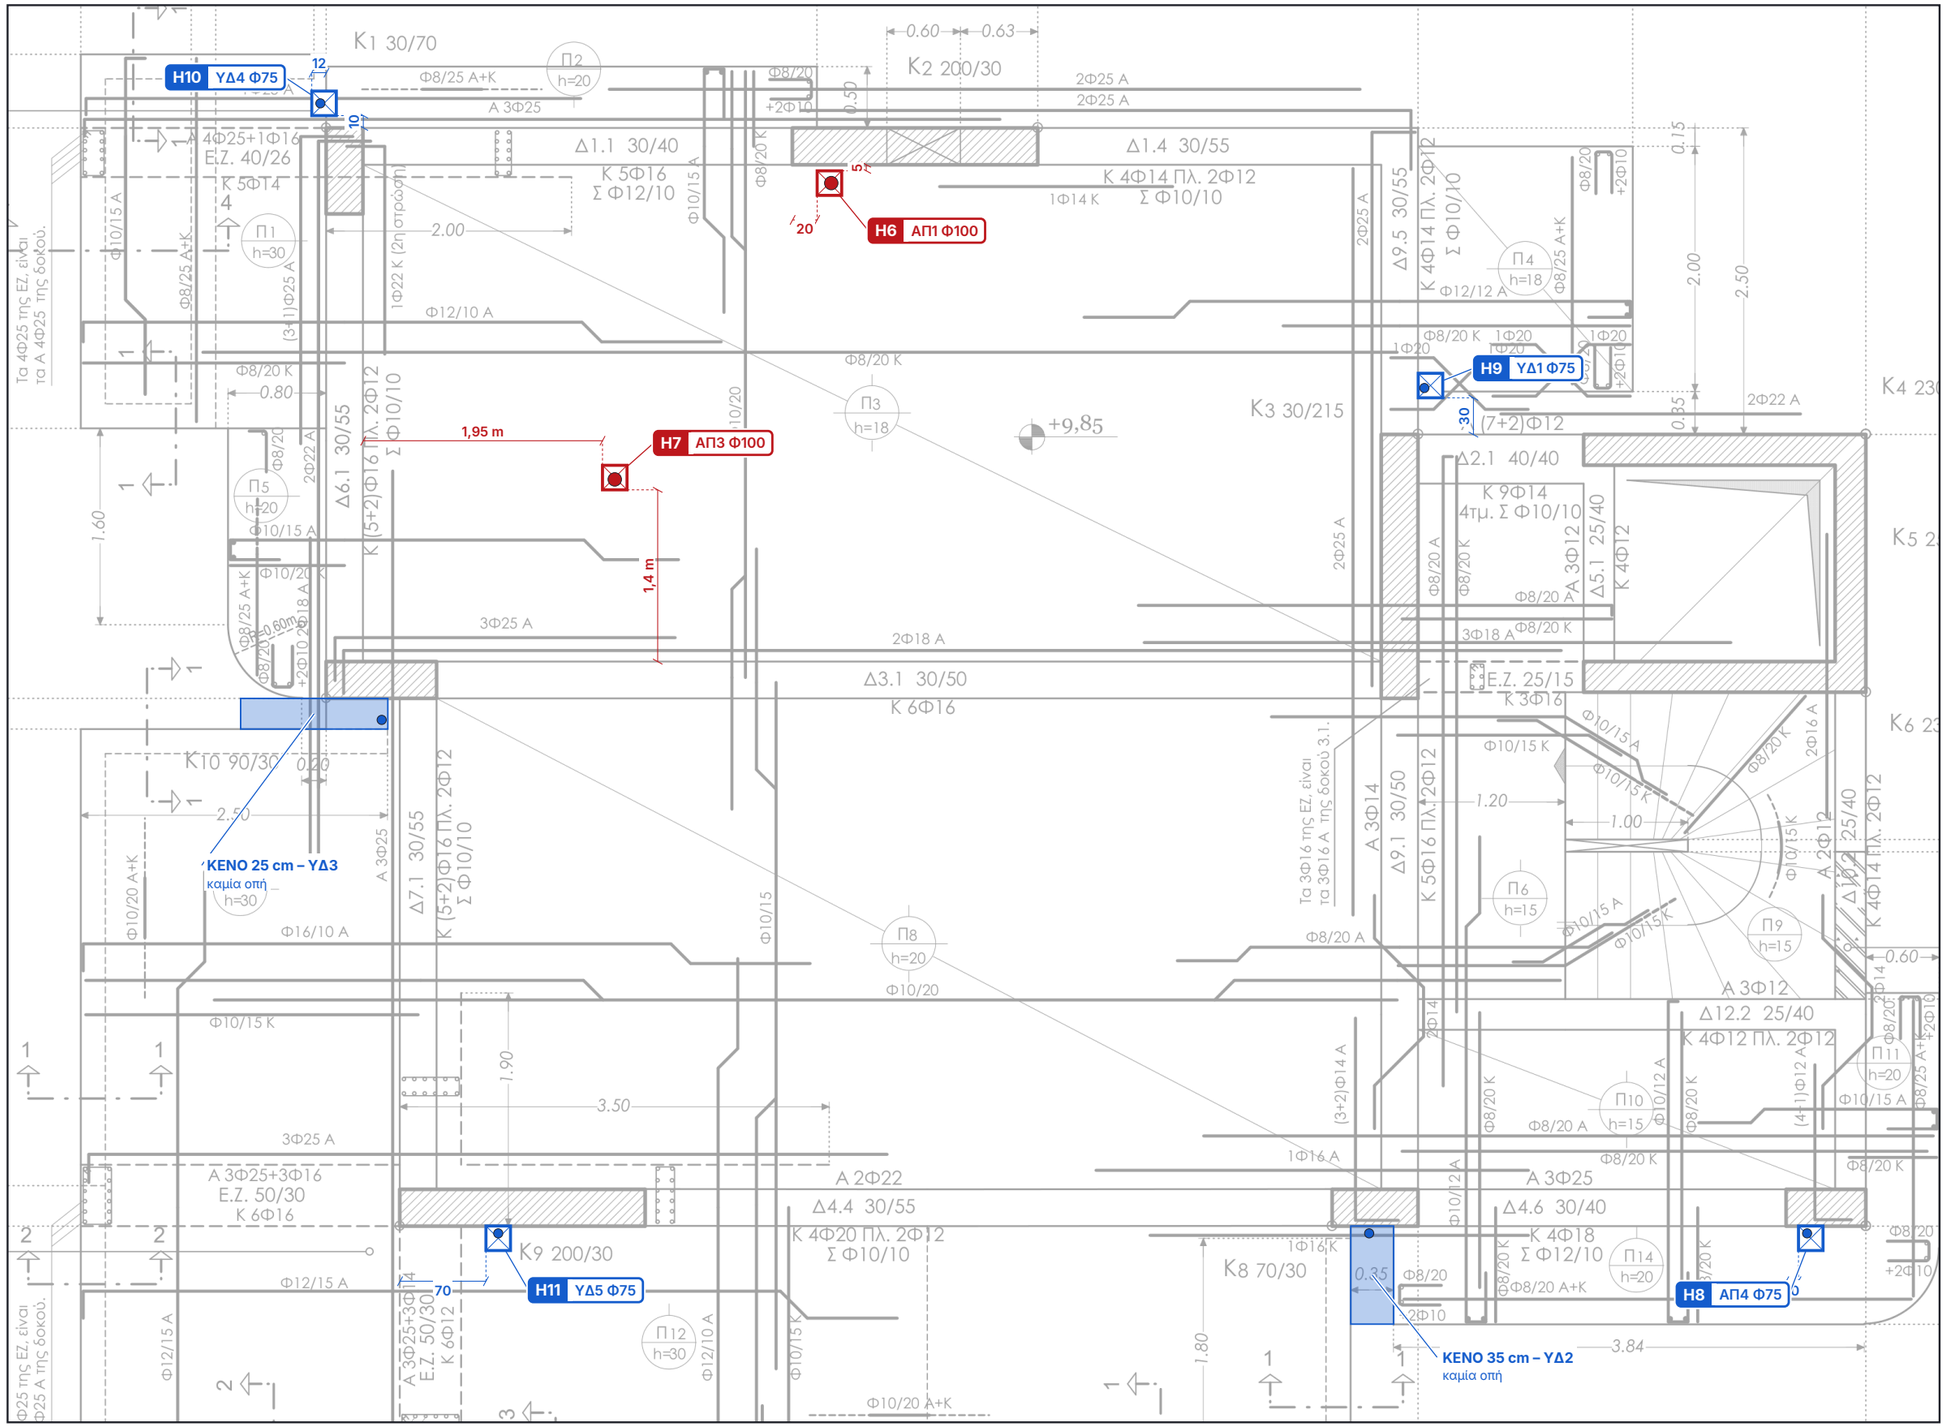

5 **ΟΠΕΣ ΠΛΑΚΑΣ ΟΡΟΦΗΣ Β΄ ΟΡΟΦΟΥ (Σ5 · +9,85) – κουτιά 20 × 20, διαστάσεις σε cm από παρειές σκυροδέματος** Κλίμακα 1:50


B

ΟΠΕΣ ΠΛΑΚΑΣ Σ5

Όλες κουτί 20 × 20 cm. Η θέση δίνεται ως την ΑΚΜΗ του κουτιού.

- **H6** **ΑΠ1 Φ100**
  20 ανατ. της Δ παρ. Κ2 · 5 νότια της Ν παρ. Κ2
- **H7** **ΑΠ3 Φ100**
  1,95 m ανατ. της Α παρ. Δ6.1 · 1,4 m βόρ. της Β παρ. Δ3.1
- **H8** **ΑΠ4 Φ75**
  10 ανατ. της Δ παρ. Κ7 · κολλητά στη Ν παρ. Κ7
- **H9** **ΥΔ1 Φ75**
  κολλητά στη Α παρ. Δ9.5 · 30 βόρ. της Β παρ. Κ3
- **H10** **ΥΔ4 Φ75**
  δυτ. ακμή 12 δυτ. της Δ παρ. Κ1 · 10 βόρ. της Β παρ. Κ1
- **H11** **ΥΔ5 Φ75**
  70 ανατ. της Δ παρ. Κ9 · κολλητά στη Ν παρ. Κ9

ΕΡΓΟ	ΘΕΜΑ ΣΧΕΔΙΟΥ	ΒΑΣΗ	ΑΡ. ΣΧΕΔΙΟΥ
ΠΕΝΤΑΟΡΟΦΟ ΚΤΗΡΙΟ ΚΑΤΟΙΚΙΩΝ – ΑΡΓΥΡΟΥΠΟΛΗ Κωνσταντινουπόλεως 12 & Αγ. Βαρβάρας · Ο.Τ. 103-15 Εργοδότης: INTERKAT Α.Ε. · Κατασκευή: ARKAD Ι.Κ.Ε.	**ΟΠΕΣ ΠΛΑΚΑΣ ΟΡΟΦΗΣ Β΄ ΟΡΟΦΟΥ** R19 · λύματα · ακάθαρτα · αερισμοί · όμβρια · οπές πλακών Σ5 (+9,85) · κουτιά 20 × 20 · θέσεις από παρειές σκυροδέματος	Υπόβαθρο: ξυλότυπος Σ5_ΕΦ	**ΑΠ-14** **Κλίμακα 1:50 · Α3** 10/11/2026 · R19

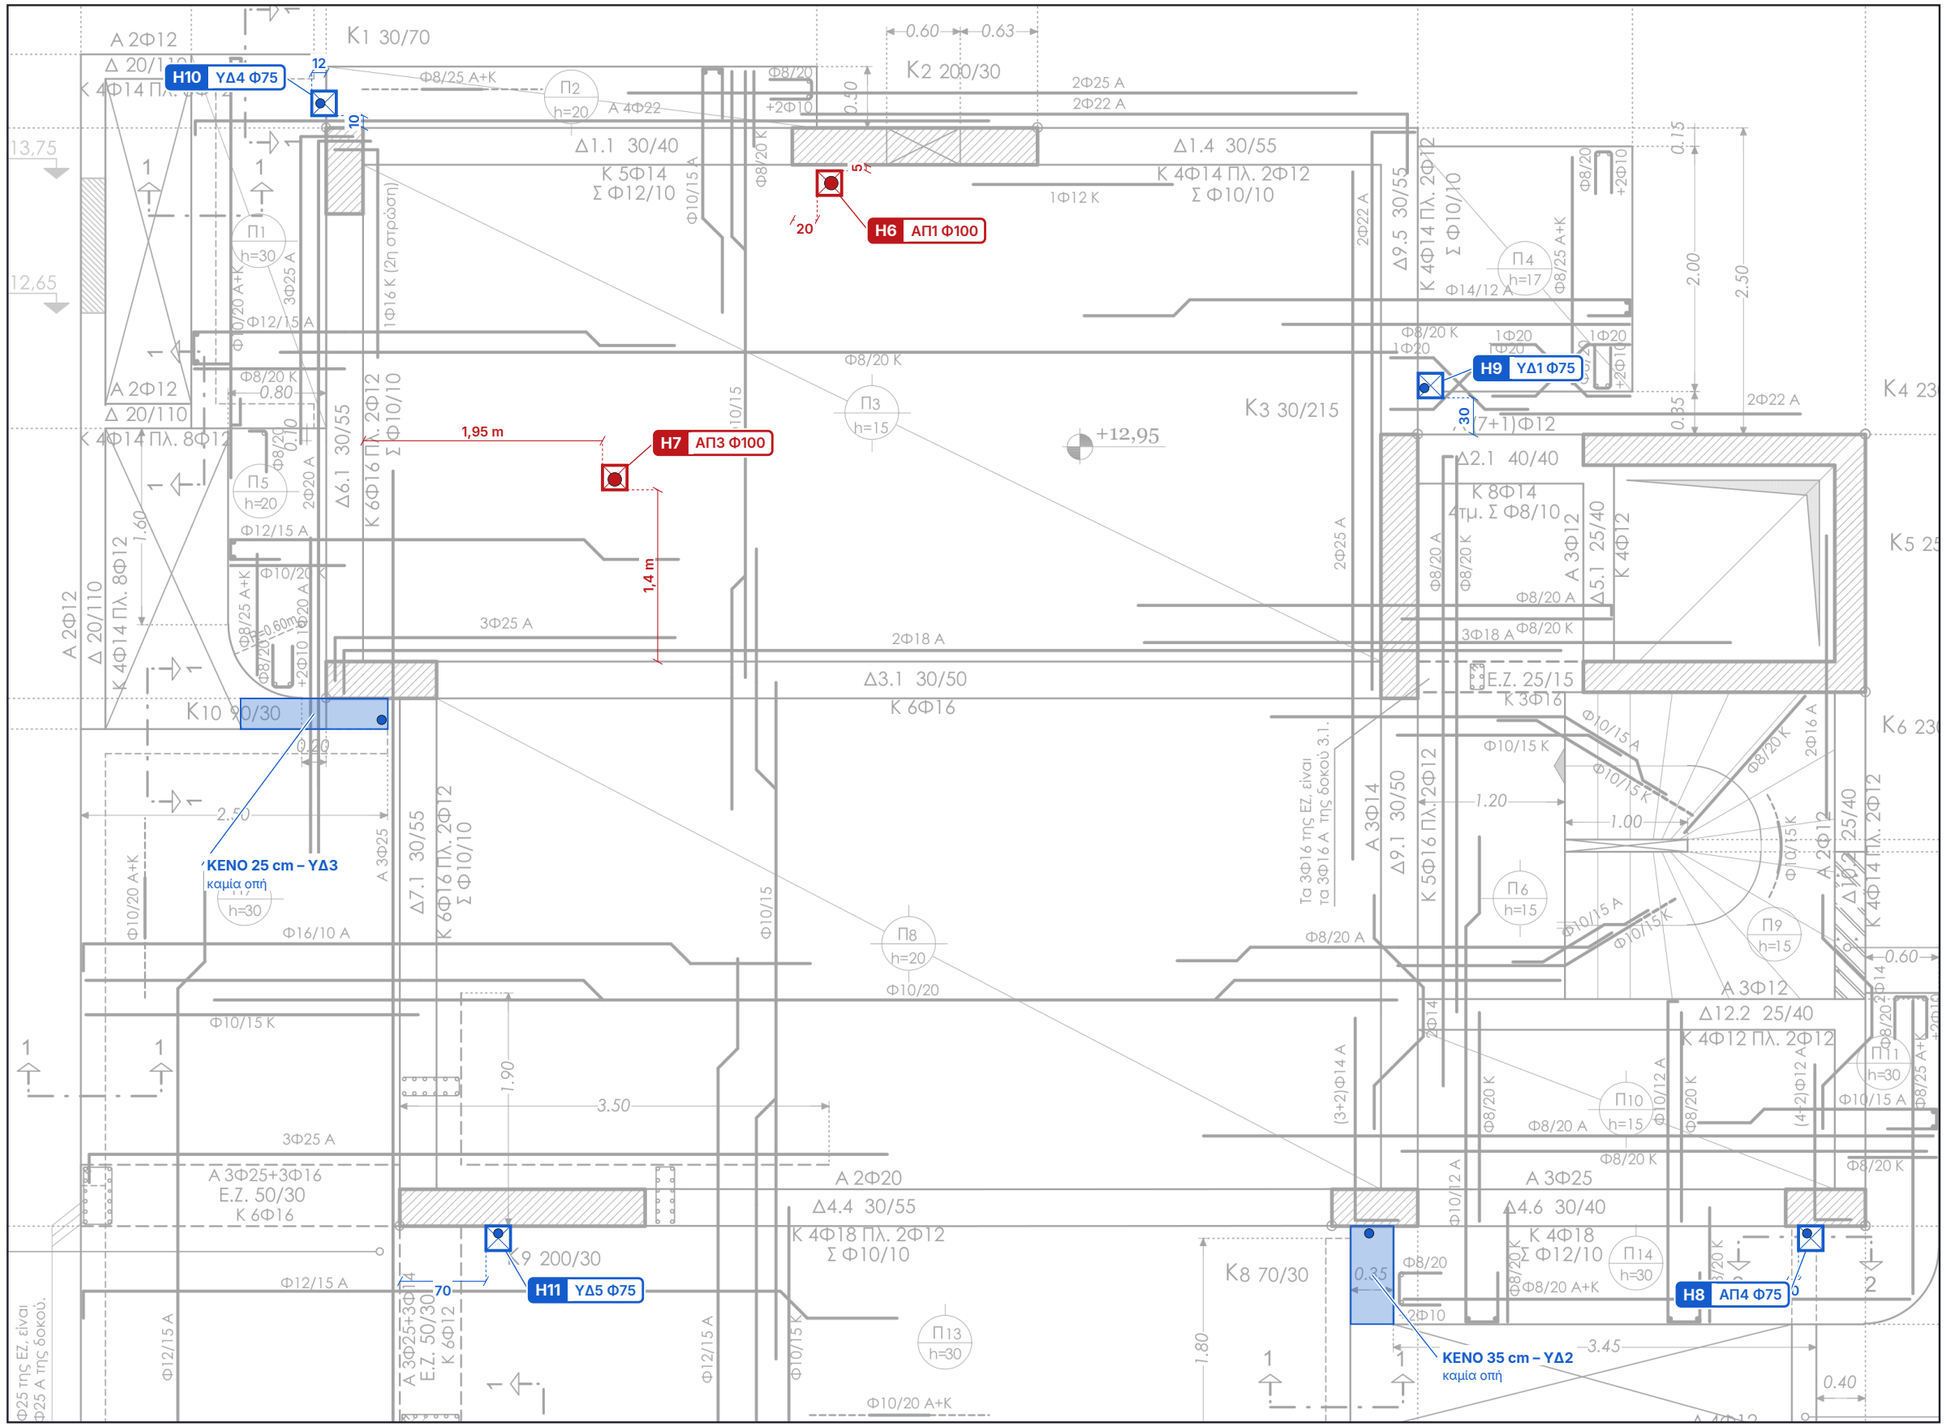

6 **ΟΠΕΣ ΠΛΑΚΑΣ ΟΡΟΦΗΣ Γ΄ ΟΡΟΦΟΥ (Σ6 · +12,95) – κουτιά 20 × 20, διαστάσεις σε cm από παρειές σκυροδέματος** Κλίμακα 1:50


ΟΠΕΣ ΠΛΑΚΑΣ Σ6

Όλες κουτί 20 × 20 cm. Η θέση δίνεται ως την ΑΚΜΗ του κουτιού.

- **H6** **ΑΠ1 Φ100**
  20 ανατ. της Δ παρ. Κ2 · 5 νότια της Ν παρ. Κ2
- **H7** **ΑΠ3 Φ100**
  1,95 m ανατ. της Α παρ. Δ6.1 · 1,4 m βόρ. της Β παρ. Δ3.1
- **H8** **ΑΠ4 Φ75**
  10 ανατ. της Δ παρ. Κ7 · κολλητά στη Ν παρ. Κ7
- **H9** **ΥΔ1 Φ75**
  κολλητά στη Α παρ. Δ9.5 · 30 βόρ. της Β παρ. Κ3
- **H10** **ΥΔ4 Φ75**
  δυτ. ακμή 12 δυτ. της Δ παρ. Κ1 · 10 βόρ. της Β παρ. Κ1
- **H11** **ΥΔ5 Φ75**
  70 ανατ. της Δ παρ. Κ9 · κολλητά στη Ν παρ. Κ9

B

ΕΡΓΟ	ΘΕΜΑ ΣΧΕΔΙΟΥ	ΒΑΣΗ	ΑΡ. ΣΧΕΔΙΟΥ
ΠΕΝΤΑΟΡΟΦΟ ΚΤΗΡΙΟ ΚΑΤΟΙΚΙΩΝ – ΑΡΓΥΡΟΥΠΟΛΗ Κωνσταντινουπόλεως 12 & Αγ. Βαρβάρας · Ο.Τ. 103-15 Εργοδότης: INTERKAT Α.Ε. · Κατασκευή: ARKAD Ι.Κ.Ε.	**ΟΠΕΣ ΠΛΑΚΑΣ ΟΡΟΦΗΣ Γ΄ ΟΡΟΦΟΥ** R19 · λύματα · ακάθαρτα · αερισμοί · όμβρια · οπές πλακών Σ6 (+12,95) · κουτιά 20 × 20 · θέσεις από παρειές σκυροδέματος	Υπόβαθρο: ξυλότυπος Σ6_ΕΦ	**ΑΠ-15** **Κλίμακα 1:50 · Α3** 10/11/2026 · R19

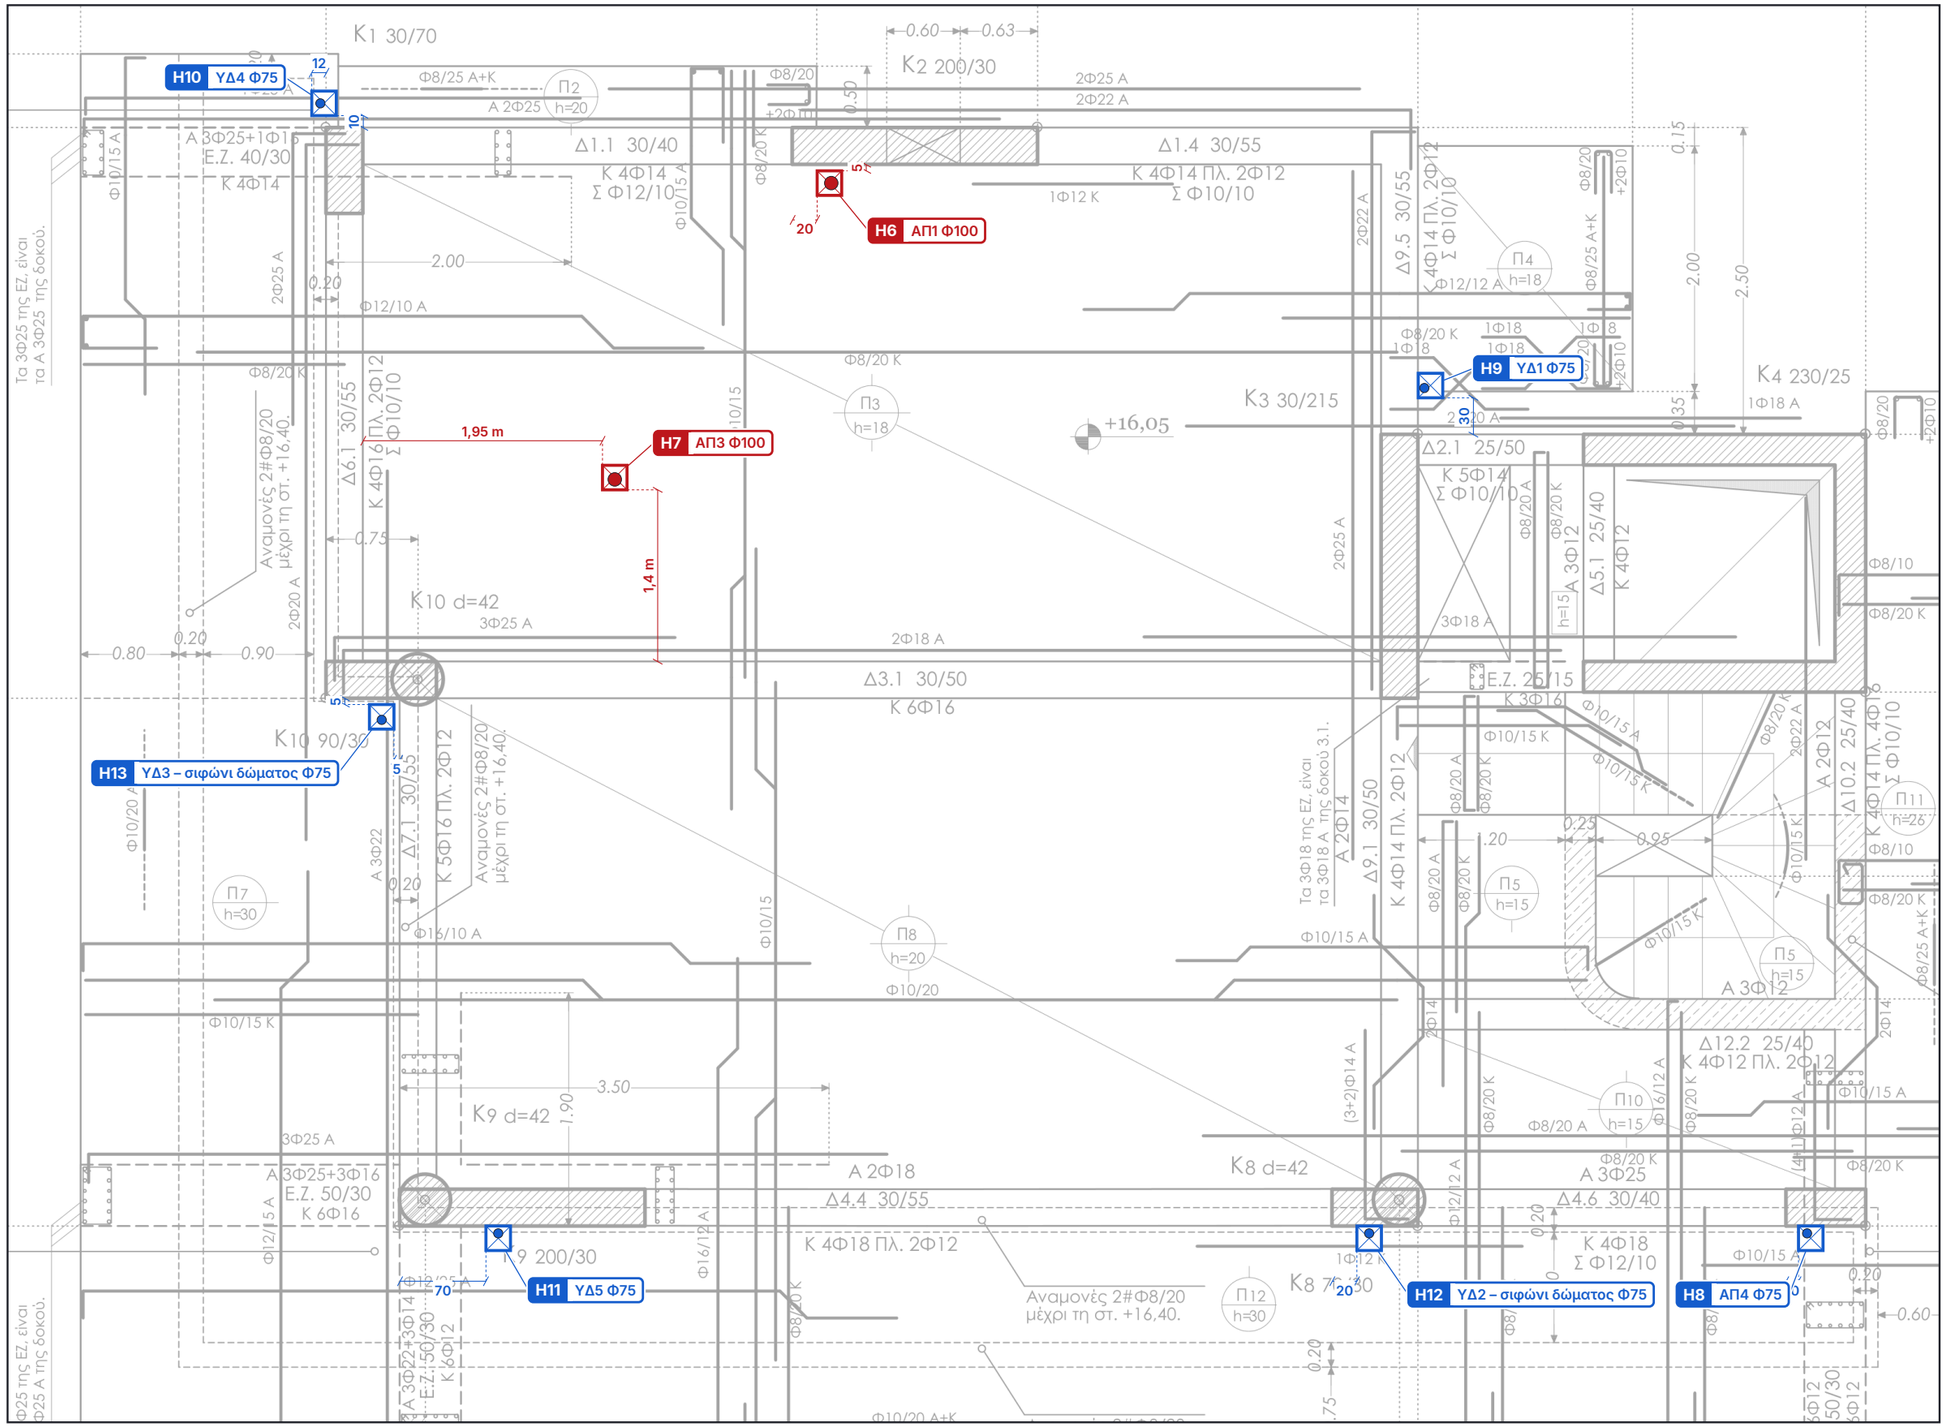

7 **ΟΠΕΣ ΠΛΑΚΑΣ ΟΡΟΦΗΣ Δ΄ ΟΡΟΦΟΥ (ΔΩΜΑ) (Σ7 · +16,05) – κουτιά 20 × 20, διαστάσεις σε cm από παρειές σκυροδέματος** Κλίμακα 1:50


B

ΟΠΕΣ ΠΛΑΚΑΣ Σ7

Όλες κουτί 20 × 20 cm. Η θέση δίνεται ως την ΑΚΜΗ του κουτιού.

- **H6** **ΑΠ1 Φ100**
  20 ανατ. της Δ παρ. K2 · 5 νότια της N παρ. K2
- **H7** **ΑΠ3 Φ100**
  1,95 m ανατ. της A παρ. Δ6.1 · 1,4 m βόρ. της B παρ. Δ3.1
- **H8** **ΑΠ4 Φ75**
  10 ανατ. της Δ παρ. K7 · κολλητά στη N παρ. K7
- **H9** **ΥΔ1 Φ75**
  κολλητά στη A παρ. Δ9.5 · 30 βόρ. της B παρ. K3
- **H10** **ΥΔ4 Φ75**
  δυτ. ακμή 12 δυτ. της Δ παρ. K1 · 10 βόρ. της B παρ. K1
- **H11** **ΥΔ5 Φ75**
  70 ανατ. της Δ παρ. K9 · κολλητά στη N παρ. K9
- **H12** **ΥΔ2 – σιφώνι δώματος Φ75**
  20 ανατ. της Δ παρ. K8 · κολλητά στη N παρ. K8
- **H13** **ΥΔ3 – σιφώνι δώματος Φ75**
  5 δυτ. της Δ παρ. Δ7.1 · 5 νότια της N παρ. K10

ΕΡΓΟ	ΘΕΜΑ ΣΧΕΔΙΟΥ	ΒΑΣΗ	ΑΡ. ΣΧΕΔΙΟΥ
ΠΕΝΤΑΟΡΟΦΟ ΚΤΗΡΙΟ ΚΑΤΟΙΚΙΩΝ – ΑΡΓΥΡΟΥΠΟΛΗ Κωνσταντινουπόλεως 12 & Αγ. Βαρβάρας · Ο.Τ. 103-15 Εργοδότης: INTERKAT Α.Ε. · Κατασκευή: ARKAD Ι.Κ.Ε.	**ΟΠΕΣ ΠΛΑΚΑΣ ΟΡΟΦΗΣ Δ΄ ΟΡΟΦΟΥ (ΔΩΜΑ)** R19 · λύματα · ακάθαρτα · αερισμοί · όμβρια · οπές πλακών Σ7 (+16,05) · κουτιά 20 × 20 · θέσεις από παρειές σκυροδέματος	Υπόβαθρο: ξυλότυπος Σ7_ΕΦ	**ΑΠ-16** **Κλίμακα 1:50 · A3** 10/11/2026 · R19

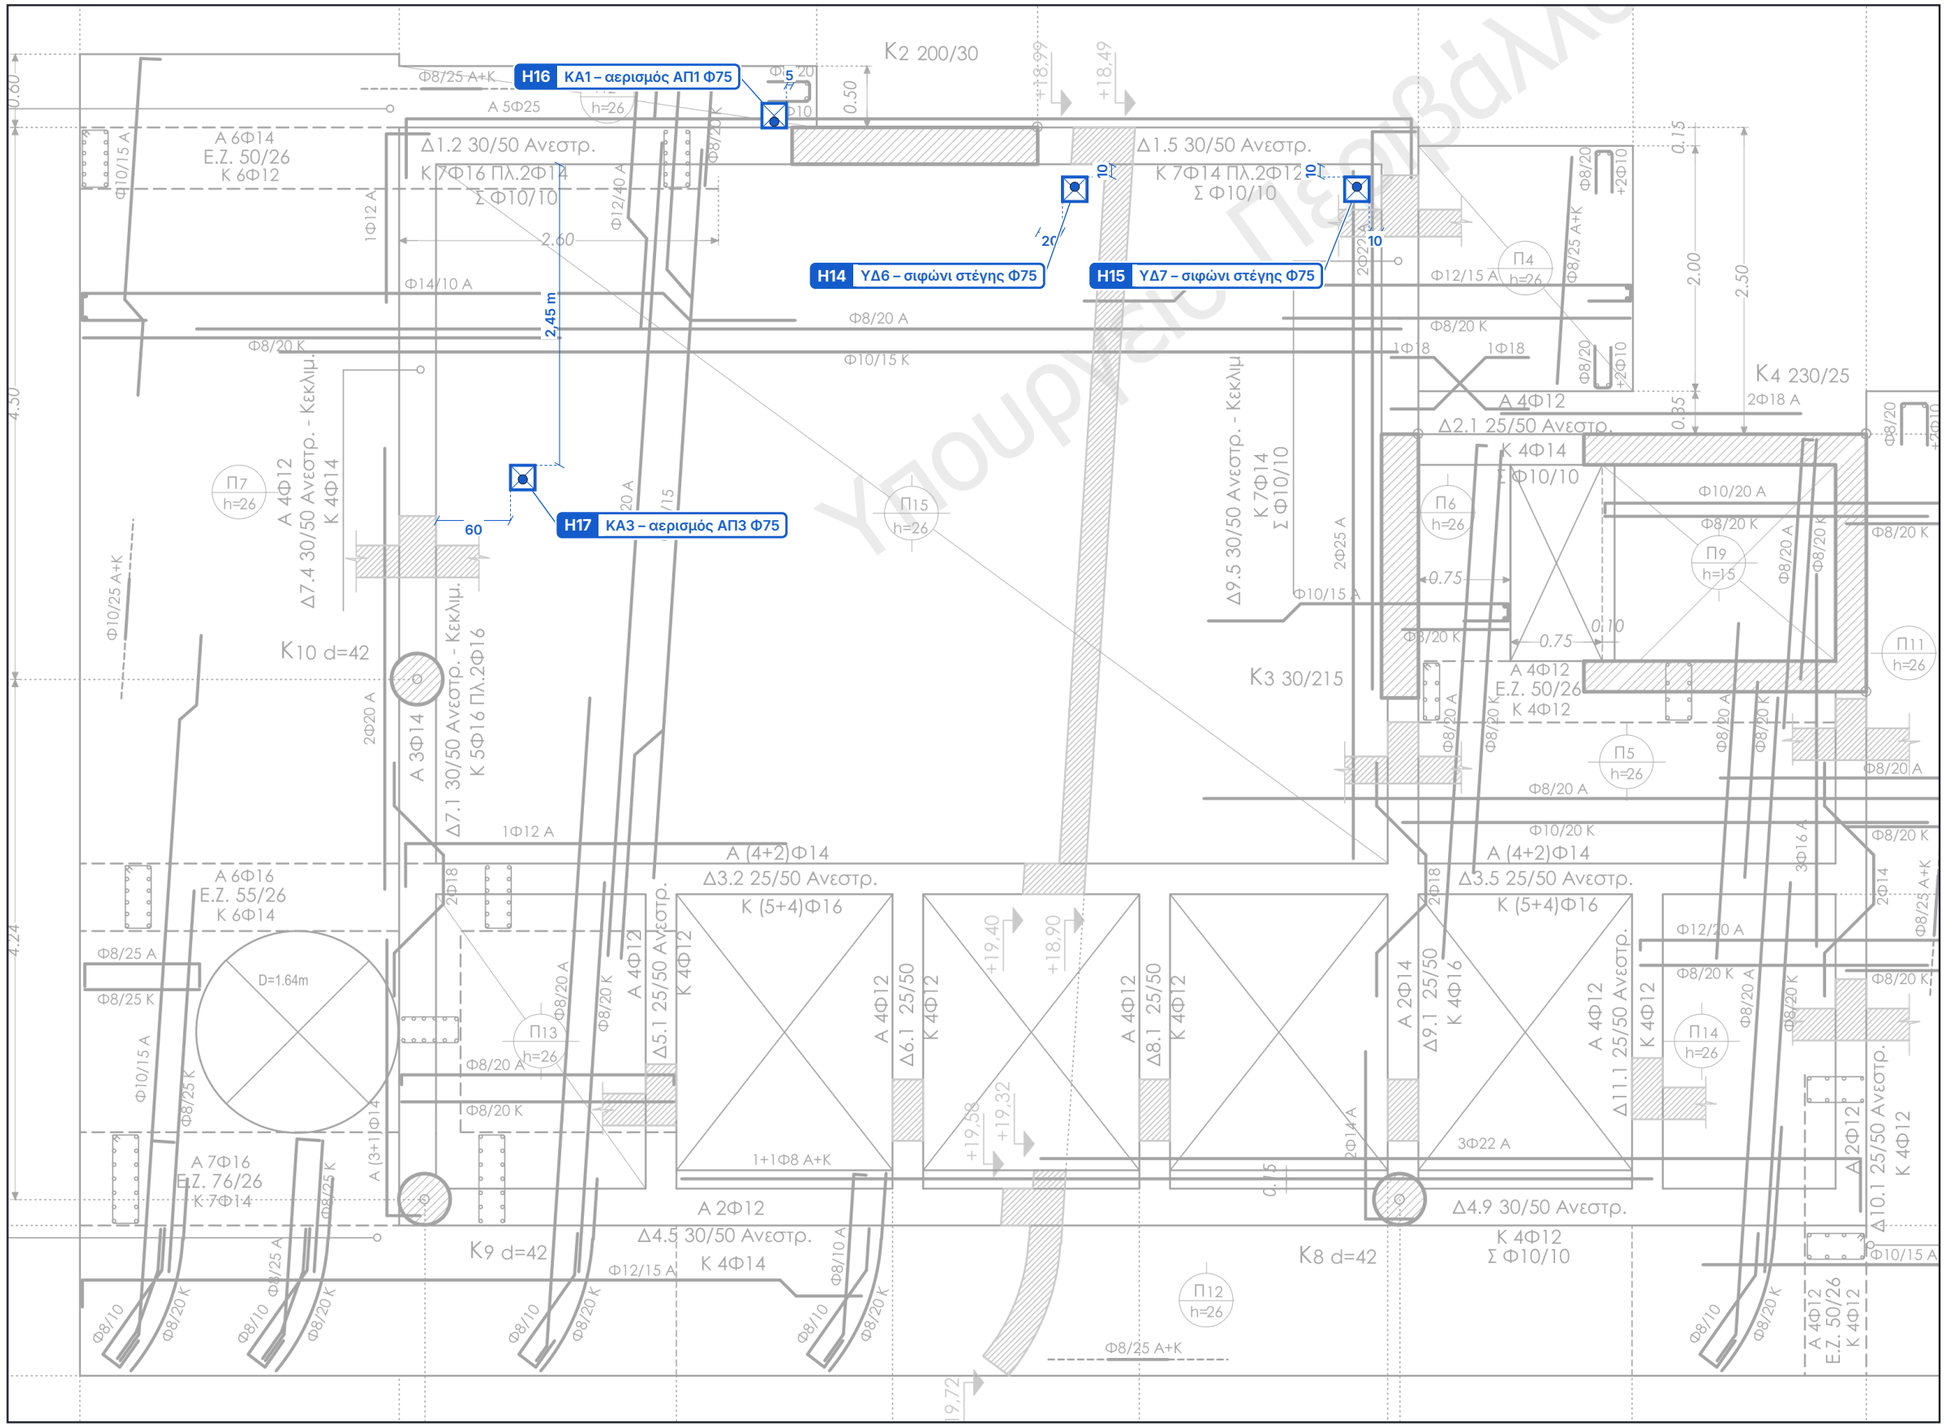

8 **ΟΠΕΣ ΠΛΑΚΑΣ ΣΤΕΓΗΣ (ΟΡΟΦΗ ΣΟΦΙΤΑΣ) (Σ8 · +18,49 … +19,32) – κουτιά 20 × 20, διαστάσεις σε cm από παρειές σκυροδέματος** Κλίμακα 1:50

B

ΟΠΕΣ ΠΛΑΚΑΣ Σ8

Όλες κουτί 20 × 20 cm. Η θέση δίνεται ως την ΑΚΜΗ του κουτιού.

H14 **ΥΔ6 – σιφώνι στέγης Φ75**
20 ανατ. της Α παρ. Κ2 · 10 νότια της Ν παρ. Δ1.5

H15 **ΥΔ7 – σιφώνι στέγης Φ75**
10 δυτ. της Δ παρ. Δ9.5 · 10 νότια της Ν παρ. Δ1.5

H16 **ΚΑ1 – αερισμός ΑΠ1 Φ75**
5 δυτ. της Δ παρ. Κ2 · κολλητά στη Β παρ. Δ1.2

H17 **ΚΑ3 – αερισμός ΑΠ3 Φ75**
60 ανατ. της Α παρ. Δ7.4 · 2,45 m νότια της Ν παρ. Δ1.2

ΕΡΓΟ	ΘΕΜΑ ΣΧΕΔΙΟΥ	ΒΑΣΗ	ΑΡ. ΣΧΕΔΙΟΥ
ΠΕΝΤΑΟΡΟΦΟ ΚΤΗΡΙΟ ΚΑΤΟΙΚΙΩΝ – ΑΡΓΥΡΟΥΠΟΛΗ Κωνσταντινουπόλεως 12 & Αγ. Βαρβάρας · Ο.Τ. 103-15 Εργοδότης: INTERKAT Α.Ε. · Κατασκευή: ARKAD Ι.Κ.Ε.	**ΟΠΕΣ ΠΛΑΚΑΣ ΣΤΕΓΗΣ (ΟΡΟΦΗ ΣΟΦΙΤΑΣ)** R19 · λύματα · ακάθαρτα · αερισμοί · όμβρια · οπές πλακών Σ8 (+18,49 … +19,32) · κουτιά 20 × 20 · θέσεις από παρειές σκυροδέματος	Υπόβαθρο: ξυλότυπος Σ8	**ΑΠ-17** **Κλίμακα 1:50 · A3** 10/11/2026 · R19