ΑΡΓΥΡΟΥΠΟΛΗ · ΚΩΝΣΤΑΝΤΙΝΟΥΠΟΛΕΩΣ 12 & ΑΓ. ΒΑΡΒΑΡΑΣ

ΔΙΑΜΕΡΙΣΜΑ Β1 · Β΄ ΟΡΟΦΟΣ

Κάτοψη · κάτοψη τοιχοποιιών · ανόψη οροφής και Η/Μ οροφής

ΣΤΟΙΧΕΙΑ ΕΡΓΟΥ

Έργο	**Ανέγερση πενταόροφου κτηρίου κατοικιών με υπόγειο, σοφίτα και δώμα – κοπή 7 δέντρων**
Θέση	**Οδός Κωνσταντινουπόλεως 12 & Αγίας Βαρβάρας** Ο.Τ. 103-15 · Δήμος Ελληνικού – Αργυρούπολης Π.Ε. Νοτίου Τομέα · Περιφέρεια Αττικής
Εργοδότης	**INTERKAT Α.Ε.**
Κατασκευή	**ARKAD Ι.Κ.Ε.**
Αρχιτεκτονική μελέτη	**Παπαβασιλείου Μάρα · Δίσκος Αλέξανδρος** (Α-10-2F «Κάτοψη Β΄ ορόφου», μελέτη εφαρμογής, 23/07/2026)
Στατική μελέτη	**Κόγιας (ξυλότυπος Σ5 – οροφή Β΄ ορόφου, +9,85)**
Μελέτες Η/Μ αδείας	**Ψ03 ψύξη · ΕΠ04 ενεργητική πυροπροστασία**

ΣΤΟΙΧΕΙΑ ΔΙΑΜΕΡΙΣΜΑΤΟΣ


Διαμέρισμα	**Β1 · Β΄ όροφος**
Εμβαδόν κατά άδεια	**94,70 m²**
Χώροι	**2 υπνοδωμάτια · 2 λουτρά · χωλ** ενιαίο καθιστικό – τραπεζαρία – κουζίνα
Εξώστες	**Δυτικός · νότιος · ΒΑ (εξωτ. μονάδα κλιματισμού)**
Στάθμες	**Τελικό δάπεδο +6,90 · πλάκα +6,75** άνω πλάκα οροφής +9,85 · ύψος ορόφου 3,10
Καθαρό ύψος	**+2,67 υπνοδωμάτια · +2,65 καθιστικό** +2,45 κουζίνα / χωλ / λουτρό · +2,40 λουτρό γονέων

ΚΑΘΑΡΑ ΕΜΒΑΔΑ ΧΩΡΩΝ (εντός τελικών παρειών, Rev.11)


Καθιστικό – τραπεζαρία – κουζίνα	40,51 m²
Υπνοδωμάτιο 2	12,15 m²
Υπνοδωμάτιο 1	11,46 m²
Χωλ	5,18 m²
Λουτρό γονέων	4,96 m²
Λουτρό	3,18 m²
Σύνολο καθαρών χώρων	**77,44 m²**

ΠΕΡΙΕΧΟΜΕΝΑ

01	**Α-01**	Κάτοψη Β΄ ορόφου – αρχιτεκτονική (απόσπασμα Α-10-2F)	1:50
02	**Τ-01**	Κάτοψη τοιχοποιιών Β΄ ορόφου (Rev.11)	1:50
03	**Τ-02**	Είδη τοιχοποιιών – σύνθεση, πάχη, μήκη	1:4
04	**ΑΝ-00**	Γενική ανόψη οροφής	1:50
05	**ΑΝ-01**	Ανόψη – στάθμες ψευδοροφής, δοκοί, κουρτινόδρομοι	1:50
06	**ΑΝ-02**	Ανόψη – κλιματισμός, θυρίδες επίσκεψης	1:50
07	**ΑΝ-03**	Ανόψη – φωτισμός, πυρανίχνευση, Wi-Fi	1:50
08	**ΑΝ-04**	Τομές ψευδοροφής Α–Α έως Ε–Ε	1:20
09	**ΑΝ-05**	Λεπτομέρειες ψευδοροφής	1:10
10	**ΑΝ-06**	Πίνακες Α – στάθμες, κουρτίνες, κλιματισμός	—
11	**ΑΝ-07**	Πίνακες Β – φωτισμός, ασθενή, υλικά	—
12	**ΑΝ-08**	Έλεγχος συντονισμού, αναθεωρήσεις, ανοικτά σημεία	—
13	**ΑΝ-09**	Όδευση ψυκτικών μονάδας καθιστικού	1:31

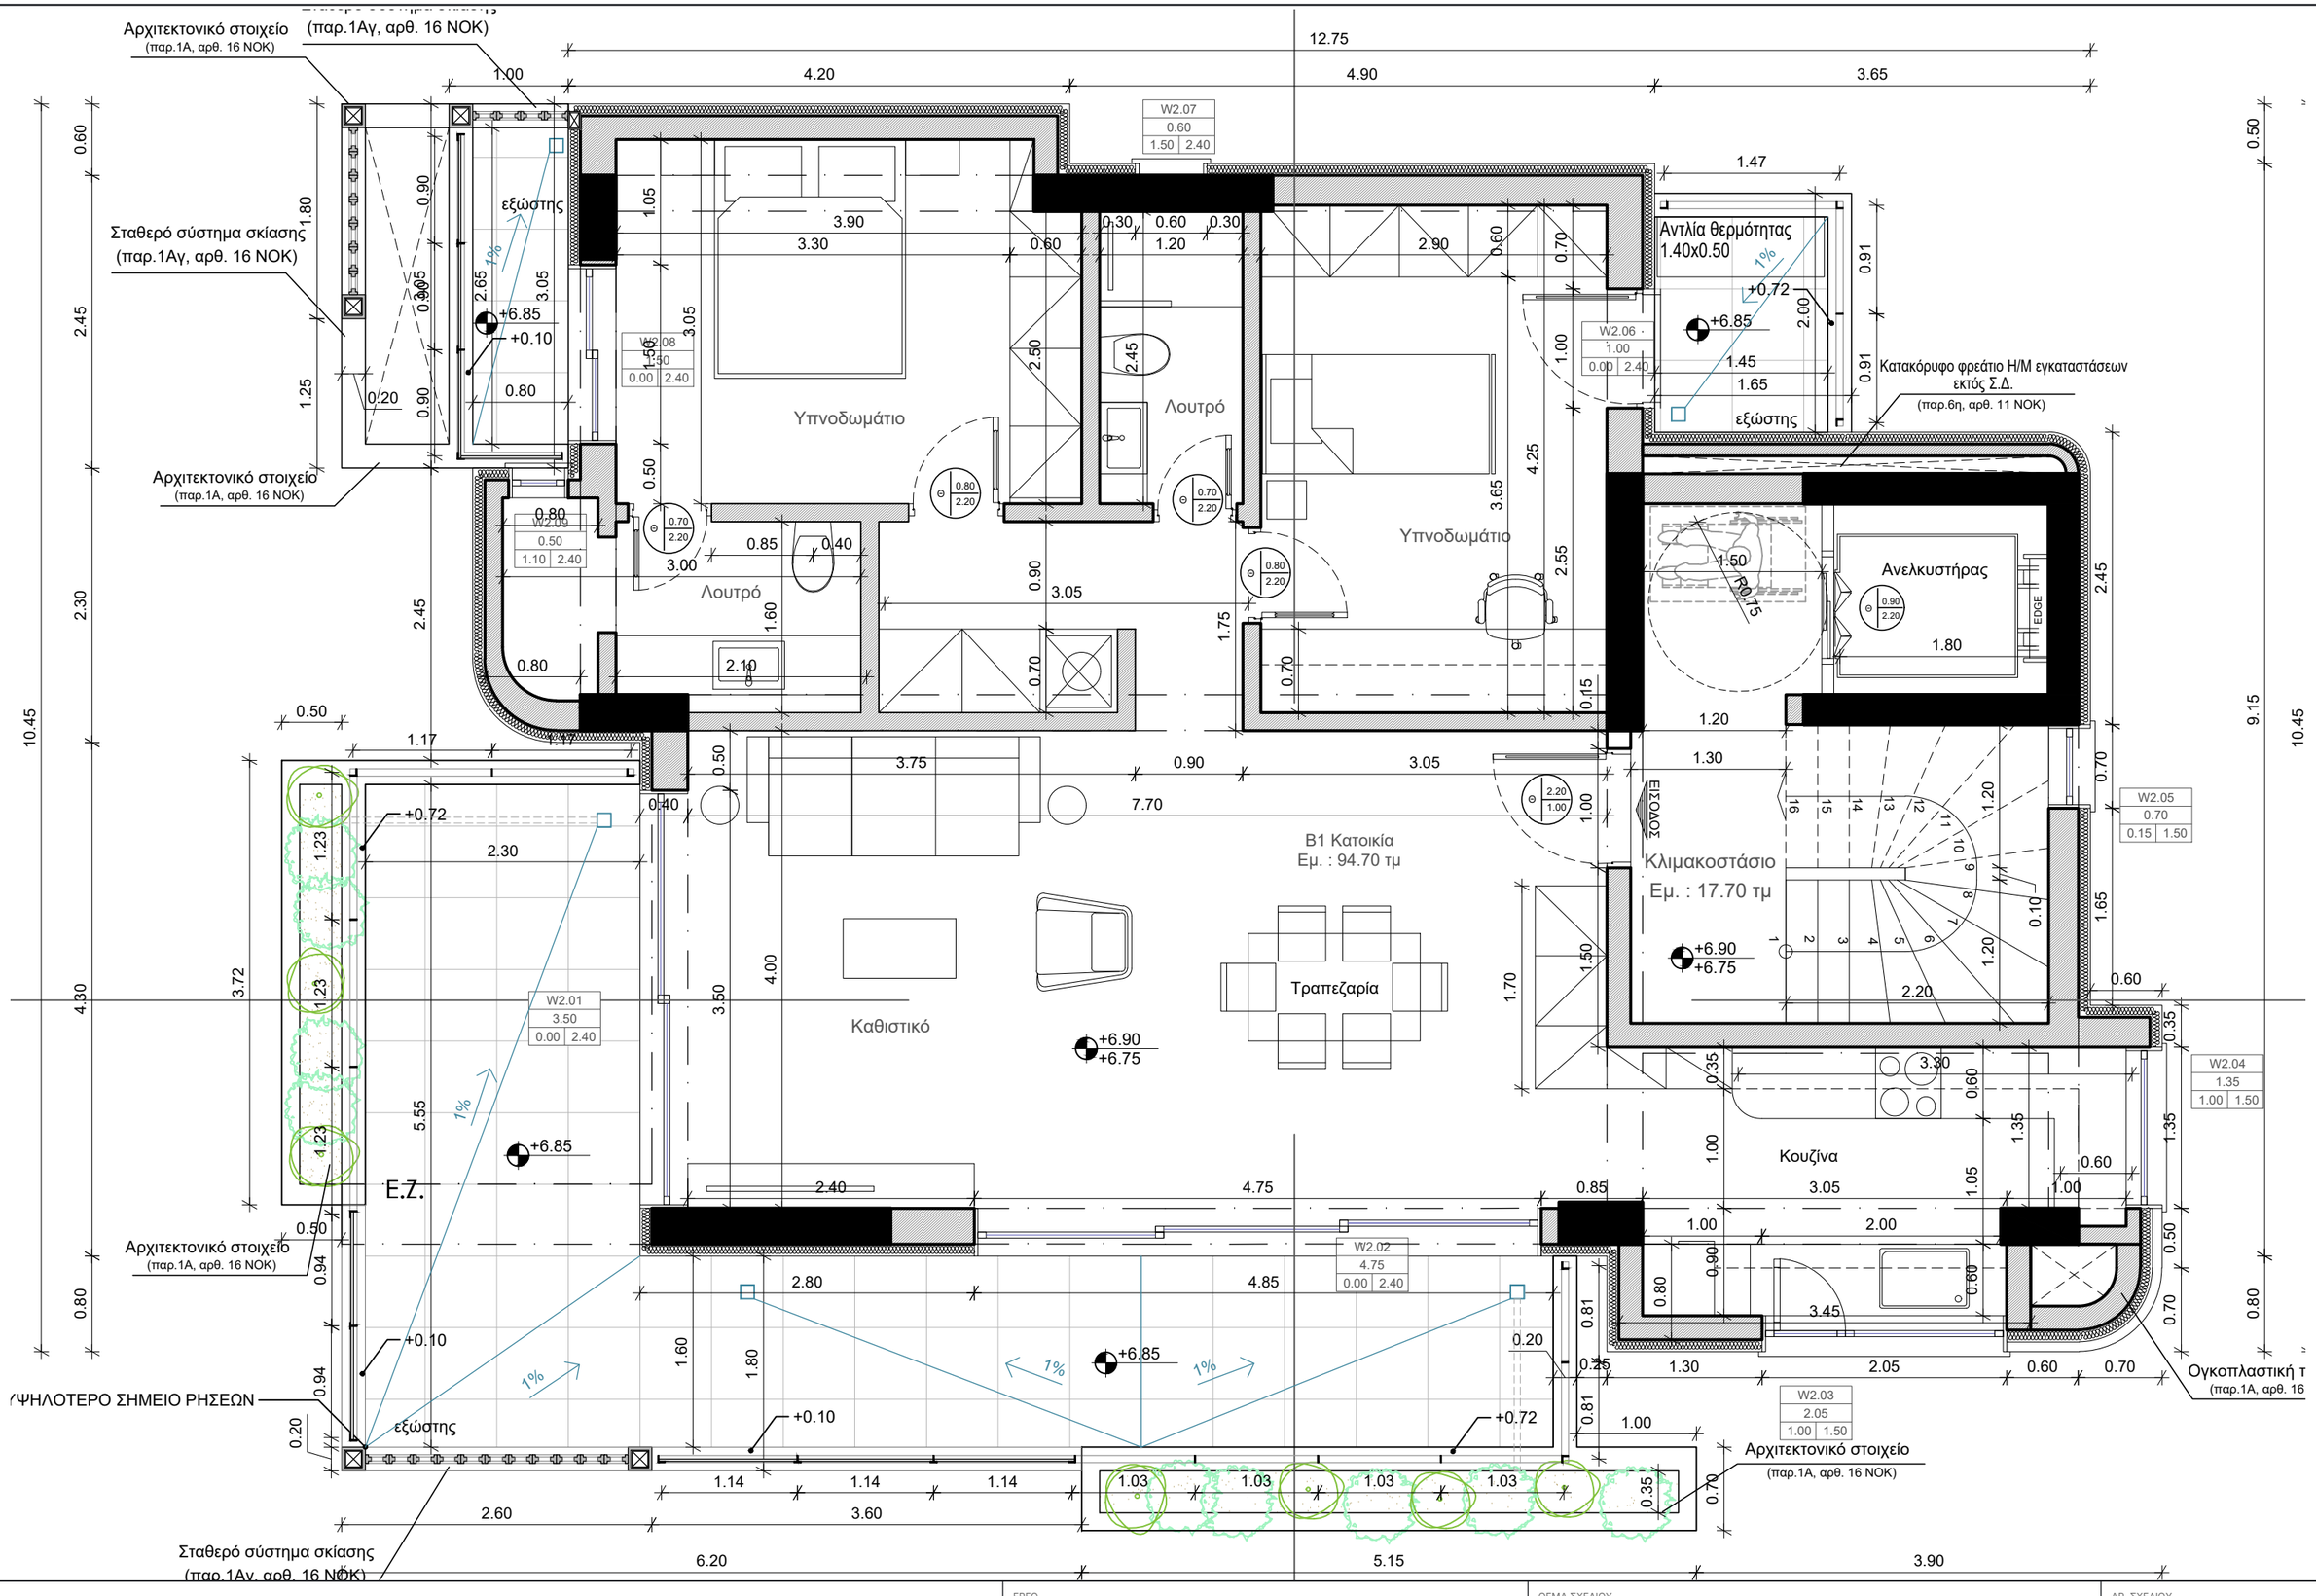

	ΕΡΓΟ **ΠΕΝΤΑΟΡΟΦΟ ΚΤΗΡΙΟ ΚΑΤΟΙΚΙΩΝ – ΑΡΓΥΡΟΥΠΟΛΗ** Κωνσταντινουπόλεως 12 & Αγ. Βαρβάρας · Ο.Τ. 103-15 Εργοδότης: INTERKAT Α.Ε. · Κατασκευή: ARKAD Ι.Κ.Ε.	ΘΕΜΑ ΣΧΕΔΙΟΥ **ΚΑΤΟΨΗ Β΄ ΟΡΟΦΟΥ – ΑΡΧΙΤΕΚΤΟΝΙΚΗ** Απόσπασμα του σχεδίου αδείας / εφαρμογής Α-10-2F (Παπαβασιλείου – Δίσκος, 23/07/2026) Βάση: κάτοψη τοιχοποιών Rev.11 (EDGE A-10-2F) · ξυλότυπος Σ5 (+9,85) · μελέτες αδείας Ψ03, ΕΠ04	ΑΡ. ΣΧΕΔΙΟΥ **Α-01** Κλίμακα 1:50 · Α3 26/10/2026 · R08

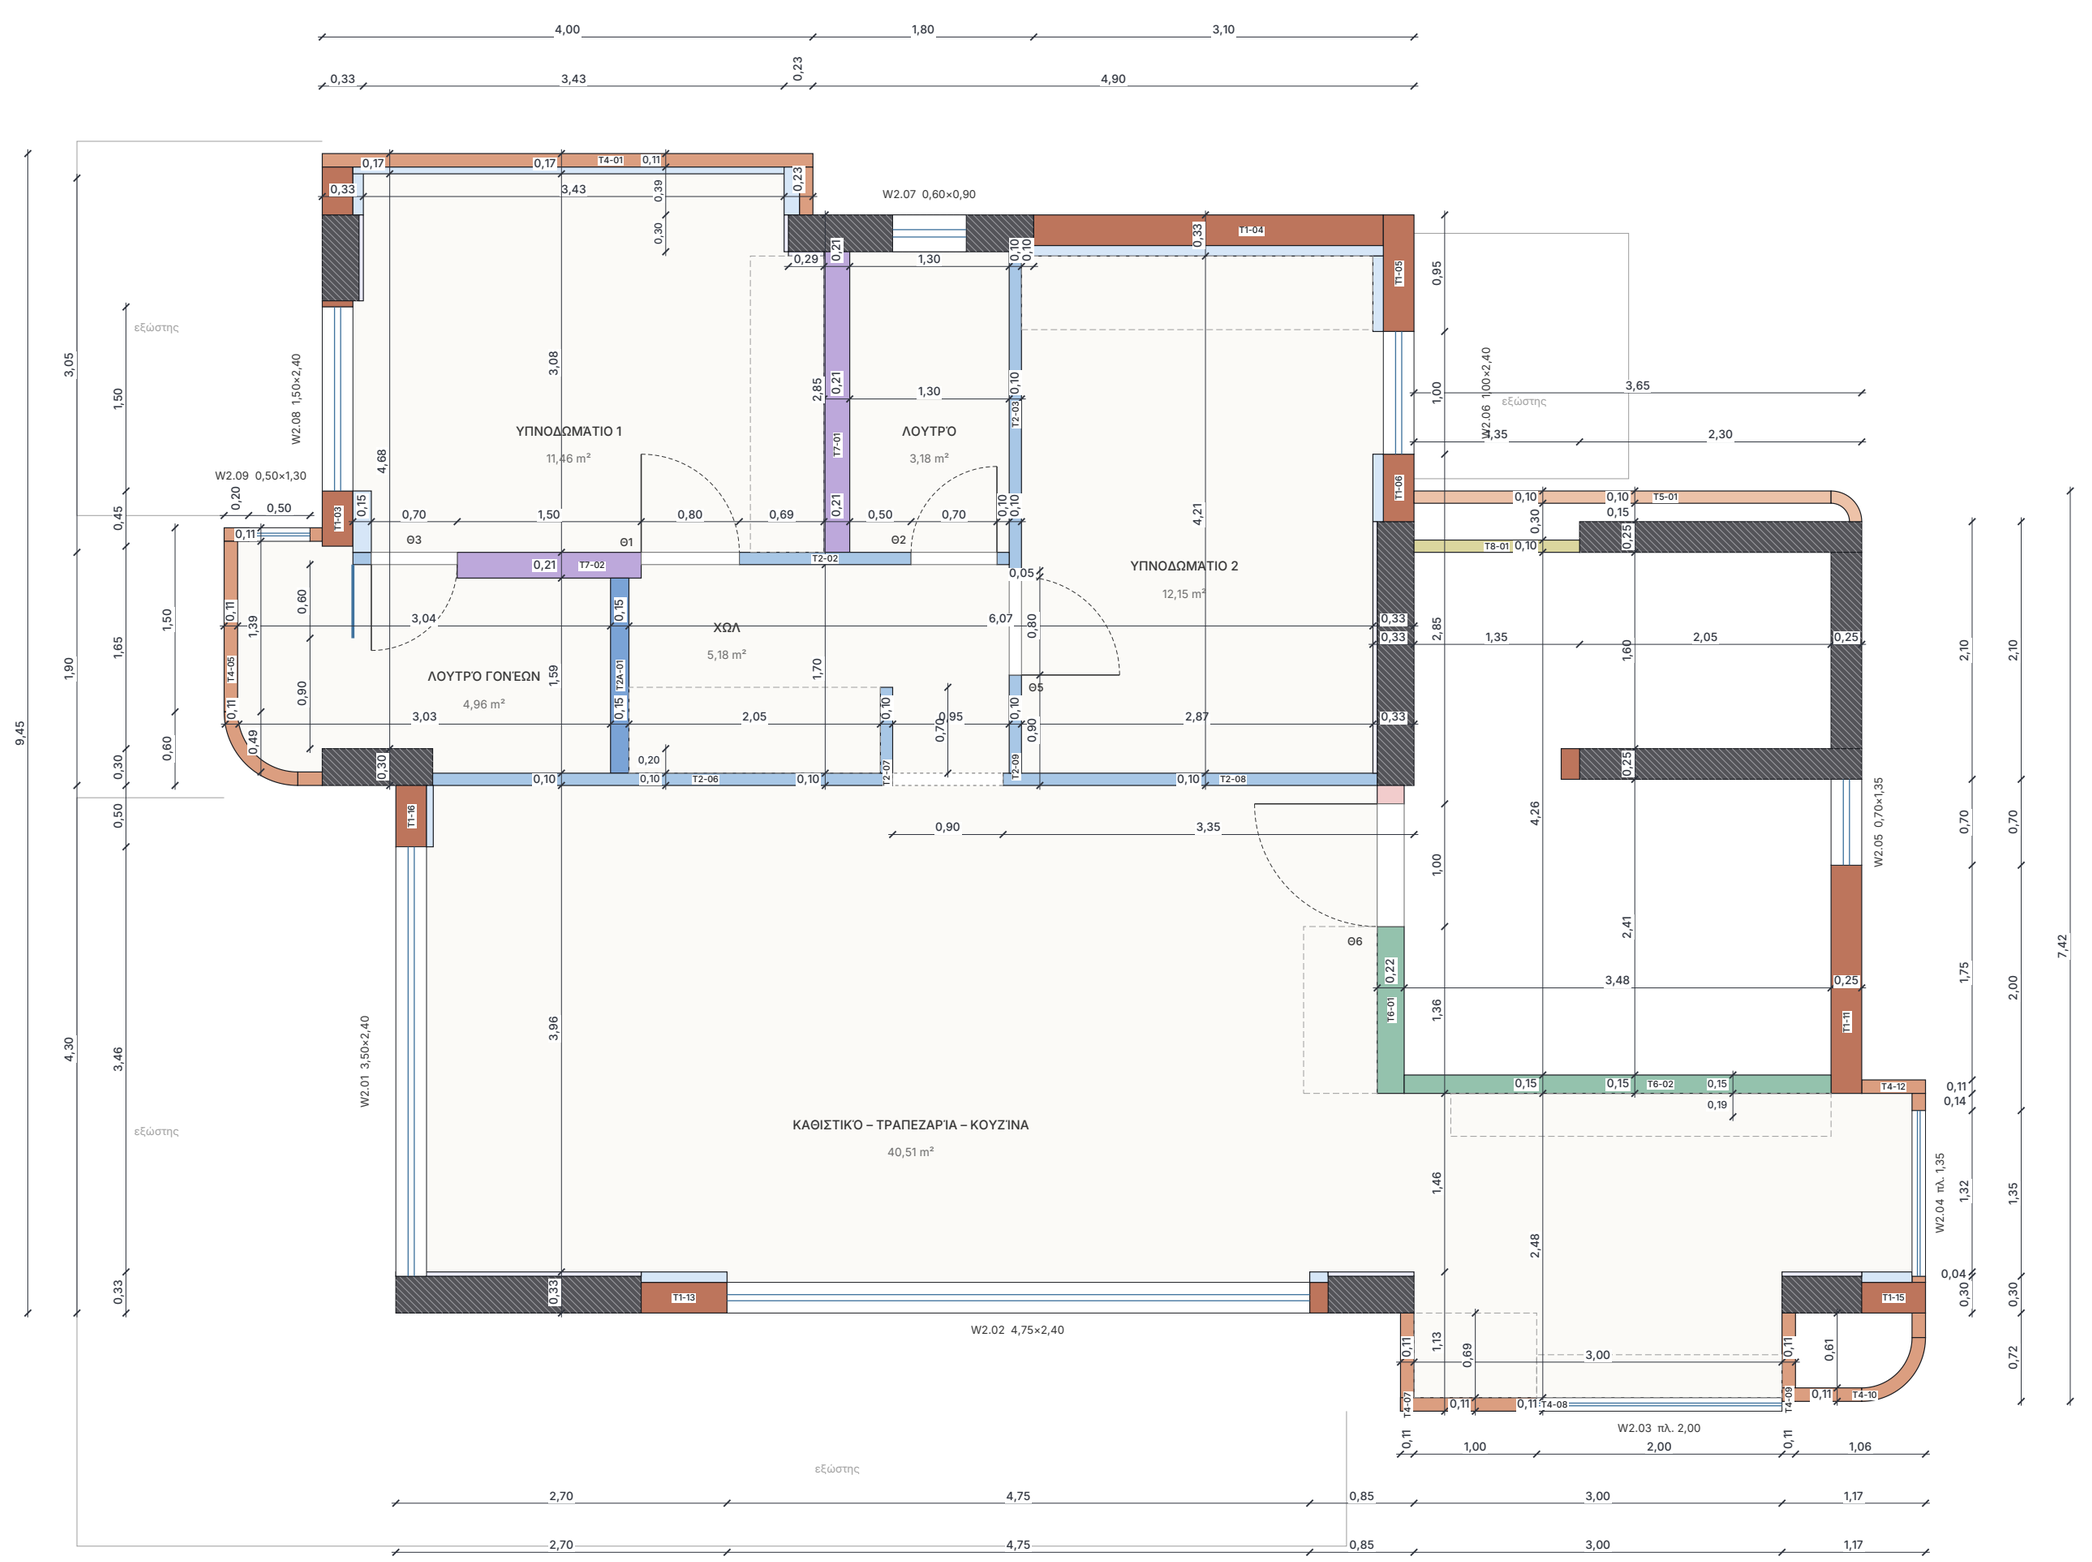

ΕΙΔΗ ΤΟΙΧΟΠΟΙΙΩΝ

- Οπλισμένο σκυρόδεμα (υποστυλώματα / τοιχία)
- T1 Εξωτερική οπτοπλινθοδομή 25 cm – σταθερή η εξωτερική παρειά
- T4 Έρκερ: απλή οπτοπλινθοδομή 11 cm – σταθερή η εξωτερική παρειά
- T5 Οπτοπλινθοδομή 10 cm περιμετρικά του πυρήνα
- T2 Γυψοσανίδα: σκελετός 5 cm + διπλή γυψοσανίδα εκατέρωθεν = 10 cm
- T2A Γυψοσανίδα 15 cm
- T7 Τοίχος λεκάνης WC 21 cm (εντοιχισμένο καζανάκι)
- T6 Κλιμακοστάσιο: γυψοσανίδα 15–22 cm (σταθερή η παρειά προς το κλιμακοστάσιο)
- T8 Τοίχος shaft πλατύσκαλου: γυψοσανίδα με ανοιγόμενα φύλλα
- T3 Εσωτερική επένδυση 5,5 cm (σκελετός 3 + διπλή γυψοσανίδα) στις εσωτ. παρειές T1 / T4
- T9 Κολλητή γυψοσανίδα 12,5 mm + κόλλα ≈ 2,5 cm στις παρειές υποστυλωμάτων

ΕΡΓΟ

ΠΕΝΤΑΟΡΟΦΟ ΚΤΗΡΙΟ ΚΑΤΟΙΚΙΩΝ – ΑΡΓΥΡΟΥΠΟΛΗ

Κωνσταντινουπόλεως 12 & Αγ. Βαρβάρας · Ο.Τ. 103-15

Εργοδότης: INTERKAT Α.Ε. · Κατασκευή: ARKAD Ι.Κ.Ε.

ΘΕΜΑ ΣΧΕΔΙΟΥ

ΚΑΤΟΨΗ ΤΟΙΧΟΠΟΙΙΩΝ Β΄ ΟΡΟΦΟΥ

Είδη τοιχοποιιών · διαστάσεις τελικών παρειών · κουφώματα (Rev.11)

Βάση: κάτοψη τοιχοποιιών Rev.11 (EDGE A-10-2F) · ξυλότυπος Σ5 (+9,85) · μελέτες αδείας Ψ03, ΕΠ04

ΑΡ. ΣΧΕΔΙΟΥ

T-01


Κλίμακα 1:50 · A3

26/10/2026 · R08

T1 Εξωτερική οπτοπλινθοδομή


1:4

πάχος 25 cm

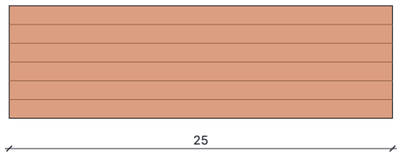

οπτοπλινθοδομή 25 cm

Σταθερή η εξωτερική παρειά. Εσωτερικά επένδυση Τ3 όπου σημειώνεται.

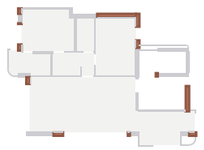


Τοίχοι: T1-01, T1-02, T1-03, T1-04, T1-05, T1-06, T1-08, T1-11, T1-13, T1-14, T1-15, T1-16

Μήκος 9,52 m · επιφάνεια ≈ 27,6 m²

T4 Έρκερ – απλή οπτοπλινθοδομή


1:4

πάχος 11 cm

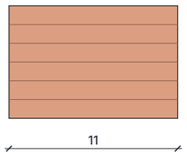

οπτοπλινθοδομή 11 cm

Έρκερ. Σταθερή η εξωτερική παρειά.

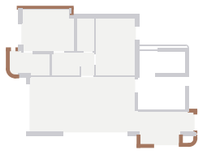


Τοίχοι: T4-01, T4-02, T4-03, T4-04, T4-05, T4-06, T4-07, T4-08, T4-09, T4-10, T4-11, T4-12, T4-13, T4-14 + 2 καμπύλοι

Μήκος 12,13 m · επιφάνεια ≈ 35,2 m²

T5 Οπτοπλινθοδομή πυρήνα


1:4

πάχος 10 cm

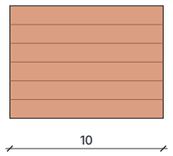

οπτοπλινθοδομή 10 cm

Γύρω από τον πυρήνα (ανελκυστήρας – κλιμακοστάσιο).

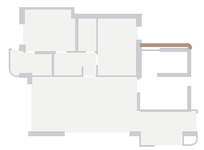


Τοίχοι: T5-01 + 1 καμπύλος

Μήκος 3,71 m · επιφάνεια ≈ 10,8 m²

T3 Επένδυση τοίχου

1:4

πάχος 5,5 cm

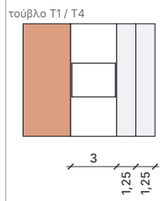

σκελετός 30
2 × γυψοσανίδα 12,5

Στις εσωτερικές παρειές των Τ1 (και του έρκερ Υπν.1).




Τοίχοι: T3-01, T3-02, T3-03, T3-04, T3-05, T3-11, T3-12, T3-13, T3-16, T3-14, T3-15

Μήκος 10,70 m · επιφάνεια ≈ 31,0 m²

T9 Επένδυση υποστυλώματος


1:4

πάχος 3,5 cm

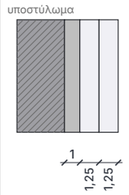

κόλλα
2 × γυψοσανίδα 12,5

Στις παρειές υποστυλωμάτων μέσα στο διαμέρισμα.

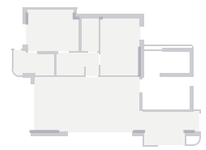


Τοίχοι: T9-01, T9-02, T9-04, T9-07, T9-08, T9-09, T9-12, T9-15

Μήκος 6,79 m · επιφάνεια ≈ 19,7 m²

T2 Χώρισμα γυψοσανίδας


1:4

πάχος 10 cm

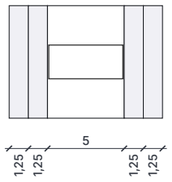

2 × γυψοσανίδα 12,5
σκελετός CW 50
2 × γυψοσανίδα 12,5

Εσωτερικά χωρίσματα. Ανθυγρή γυψοσανίδα στην πλευρά των λουτρών.

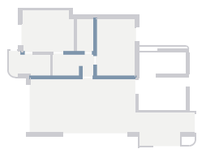


Τοίχοι: T2-02, T2-03, T2-03β, T2-06, T2-07, T2-08, T2-09, T2-10β

Μήκος 12,60 m · επιφάνεια ≈ 36,5 m²

T2A Χώρισμα γυψοσανίδας 15


1:4

πάχος 15 cm

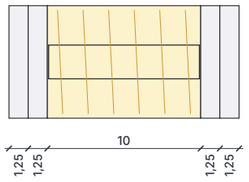

2 × γυψοσανίδα 12,5
σκελετός CW 100 + πετροβάμβακας
2 × γυψοσανίδα 12,5

Λουτρό γονέων / χωλ.

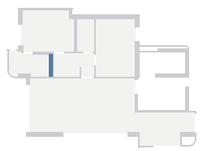


Τοίχοι: T2A-01

Μήκος 1,59 m · επιφάνεια ≈ 4,6 m²

T7 Τοίχος λεκάνης WC

1:4

πάχος 21 cm

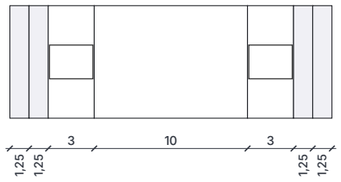

2 × γυψοσανίδα 12,5
σκελετός 30
κενό 10 cm: καζανάκι / σωληνώσεις
σκελετός 30
2 × γυψοσανίδα 12,5

Τοίχοι λεκανών WC με εντοιχισμένο καζανάκι. Ανθυγρή προς το λουτρό.




Τοίχοι: T7-01, T7-02

Μήκος 3,95 m · επιφάνεια ≈ 11,5 m²

T6 Τοίχος κλιμακοστασίου


1:4

πάχος 15 cm

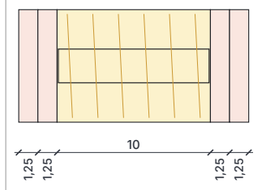

2 × γυψοσανίδα 12,5 πυράντοχη
σκελετός CW 100 + πετροβάμβακας
2 × γυψοσανίδα 12,5 πυράντοχη

Πρόταση. Τ6-01 (πόρτα ασφαλείας εισόδου): 22 cm, ίδια σύνθεση με σκελετό 170.

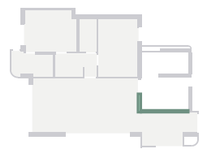


Τοίχοι: T6-01, T6-02

Μήκος 4,84 m · επιφάνεια ≈ 14,0 m²

T8 Τοίχος shaft


1:4

πάχος 10 cm

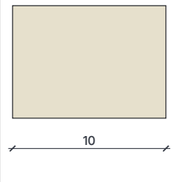

πλαίσιο + ανοιγόμενα φύλλα (τύπου ντουλάπας)

Μέτωπο shaft πλατύσκαλου, επισκέψιμο.

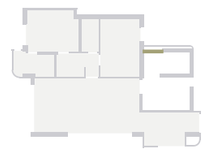

Τοίχοι: T8-01

Μήκος 1,35 m · επιφάνεια ≈ 3,9 m²

Επιφάνειες ενδεικτικές: μήκος × ύψος 2,90 m (πλάκα–πλάκα 3,10 – πλάκα 0,20), χωρίς αφαίρεση ανοιγμάτων και δοκών, χωρίς φύρα.

ΕΡΓΟ

ΠΕΝΤΑΟΡΟΦΟ ΚΤΗΡΙΟ ΚΑΤΟΙΚΙΩΝ – ΑΡΓΥΡΟΥΠΟΛΗ

Κωνσταντινουπόλεως 12 & Αγ. Βαρβάρας · Ο.Τ. 103-15

Εργοδότης: INTERKAT Α.Ε. · Κατασκευή: ARKAD Ι.Κ.Ε.

ΘΕΜΑ ΣΧΕΔΙΟΥ

ΕΙΔΗ ΤΟΙΧΟΠΟΙΙΩΝ Β΄ ΟΡΟΦΟΥ

Σύνθεση και πάχος ανά τύπο (οριζόντιες τομές 1:4) · πού εφαρμόζεται · μήκη


Βάση: κάτοψη τοιχοποιών Rev.11 (EDGE A-10-2F) · ξυλότυπος Σ5 (+9,85) · μελέτες αδείας Ψ03, ΕΠ04

ΑΡ. ΣΧΕΔΙΟΥ

Τ-02

Κλίμακα 1:4 · Α3

26/10/2026 · R08

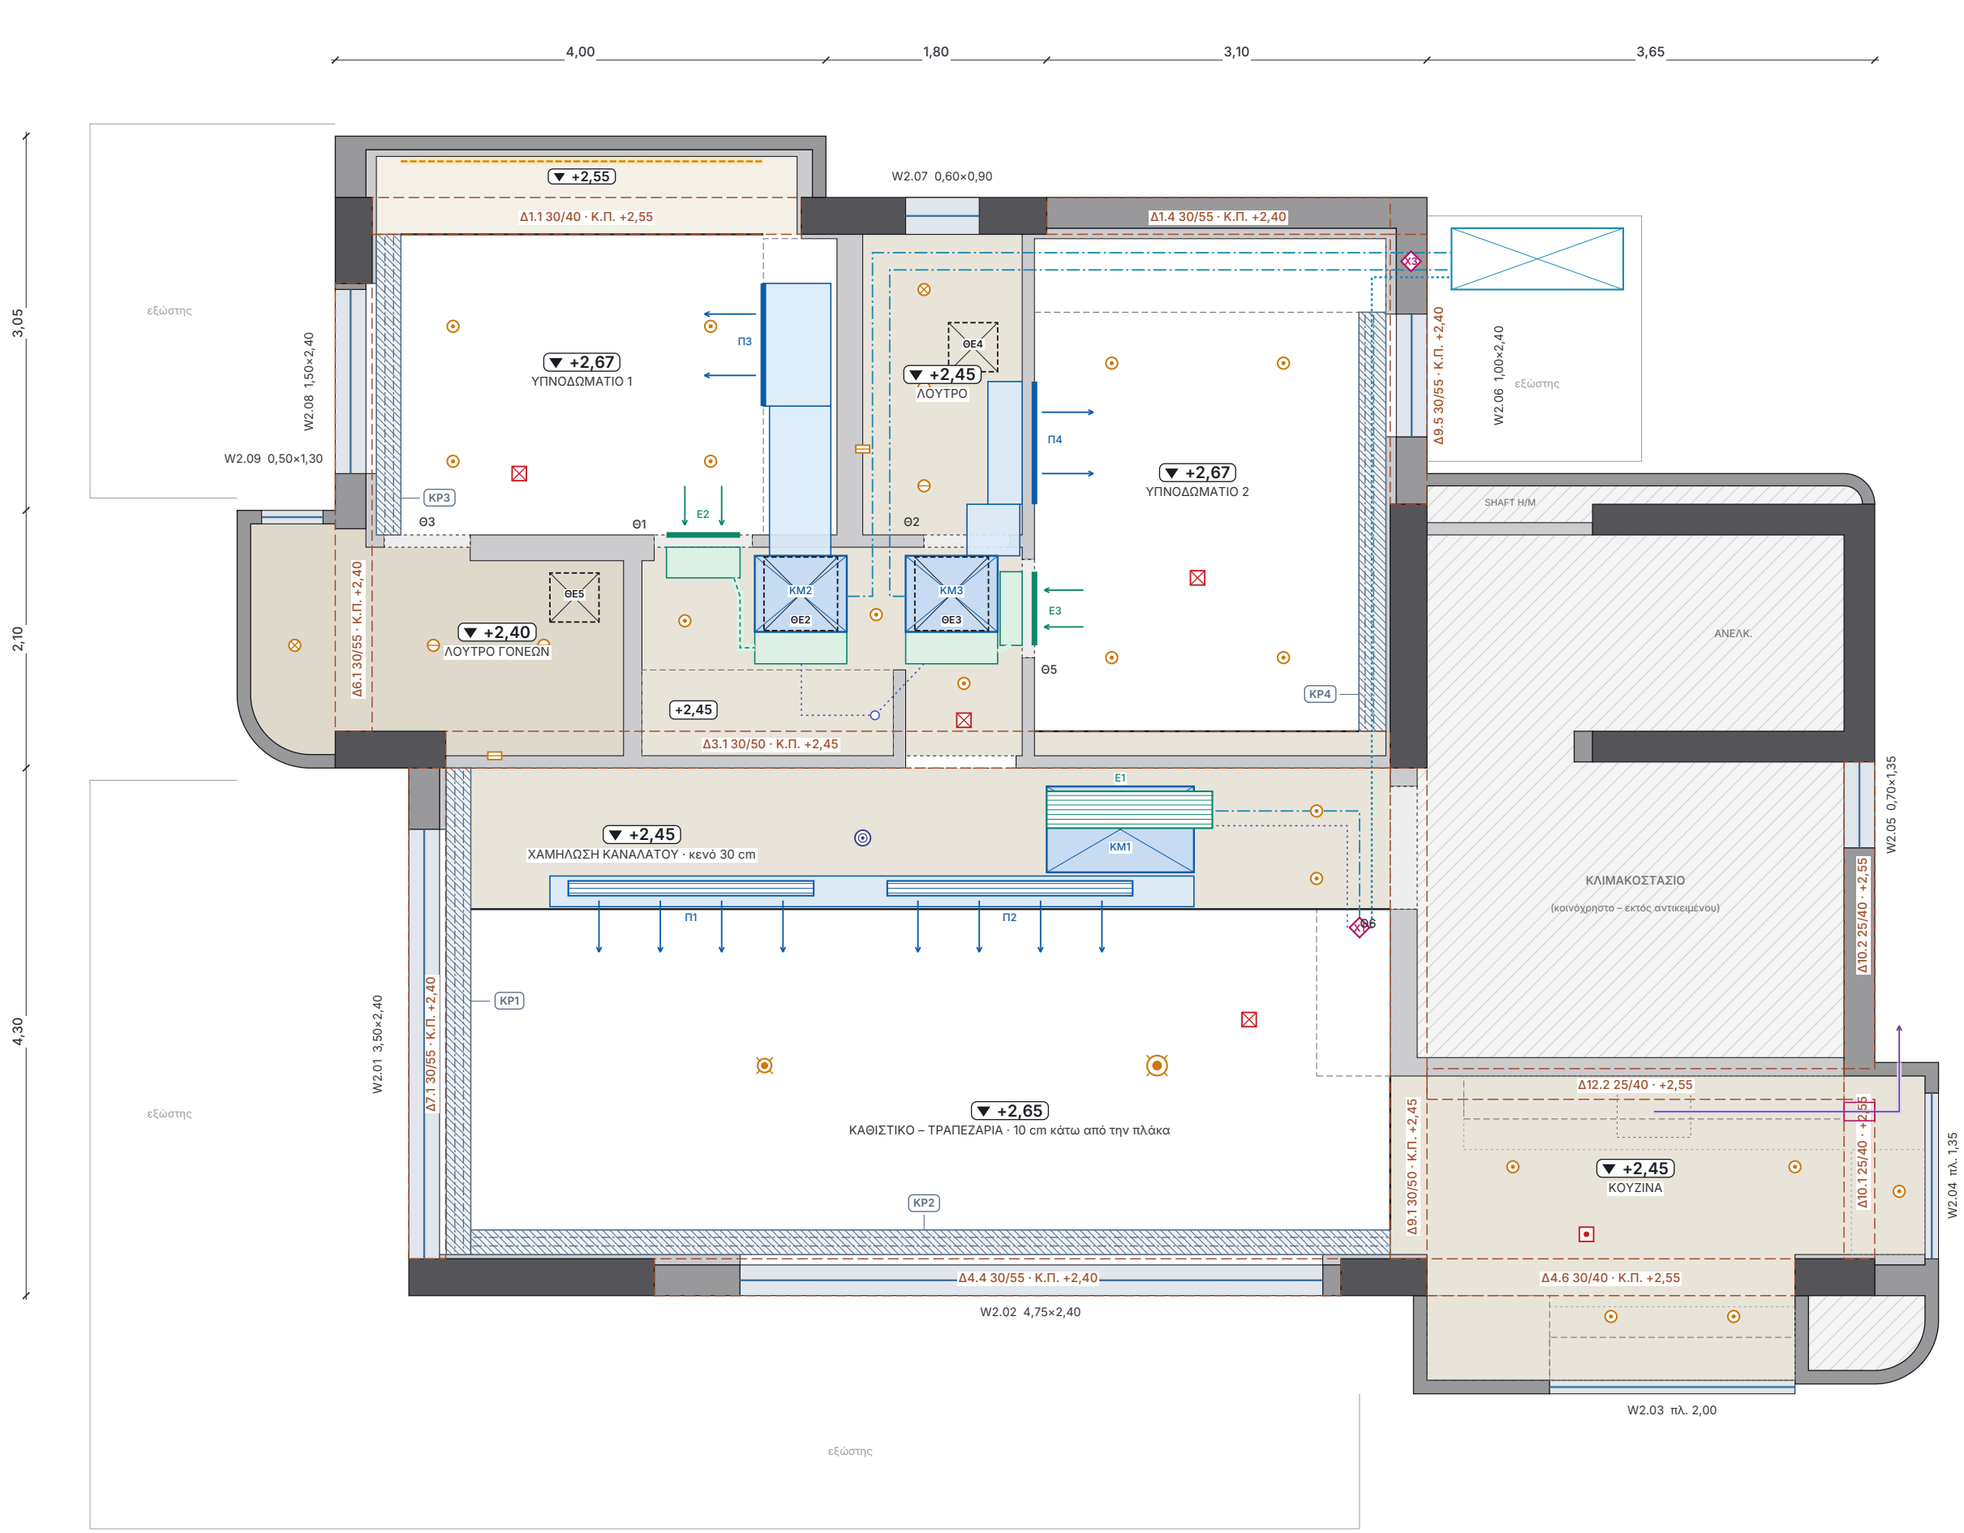

ΥΠΟΜΝΗΜΑ

- στάθμες ψευδοροφής από τελικό δάπεδο (αναλυτικά: AN-01)
- δοκός – Κ.Π. = κάτω παρειά
- ΚΡ εσοχή διπλού κουρτινόδρομου
- ΚΜ καναλάτη μονάδα · αεραγωγοί (αναλυτικά: AN-02)
- Π / Ε στόμια προσαγωγής / επιστροφής
- ΘΕ θυρίδα επίσκεψης
- spot / κρεμαστό (αναλυτικά: AN-03)
- ανιχνευτής πυρανίχνευσης / Wi-Fi
- Χ κατέβασμα / έξοδος σωληνώσεων – καμία οπή σε σκυρόδεμα
- κρυφό LED πίσω από το κρεβάτι

ΕΡΓΟ

ΠΕΝΤΑΟΡΟΦΟ ΚΤΗΡΙΟ ΚΑΤΟΙΚΙΩΝ – ΑΡΓΥΡΟΥΠΟΛΗ

Κωνσταντινουπόλεως 12 & Αγ. Βαρβάρας · Ο.Τ. 103-15

Εργοδότης: INTERKAT Α.Ε. · Κατασκευή: ARKAD Ι.Κ.Ε.

ΘΕΜΑ ΣΧΕΔΙΟΥ

ΓΕΝΙΚΗ ΑΝΟΨΗ ΟΡΟΦΗΣ Β΄ ΟΡΟΦΟΥ

Συνδυαστικό σχέδιο: στάθμες · καναλάτο · φωτισμός · κουρτινόδρομοι · θυρίδες · λοιπά Η/Μ


Βάση: κάτοψη τοιχοποιών Rev.11 (EDGE A-10-2F) · ξυλότυπος Σ5 (+9,85) · μελέτες αδείας Ψ03, ΕΠ04

ΑΡ. ΣΧΕΔΙΟΥ

AN-00

Κλίμακα 1:50 · Α3

26/10/2026 · R08

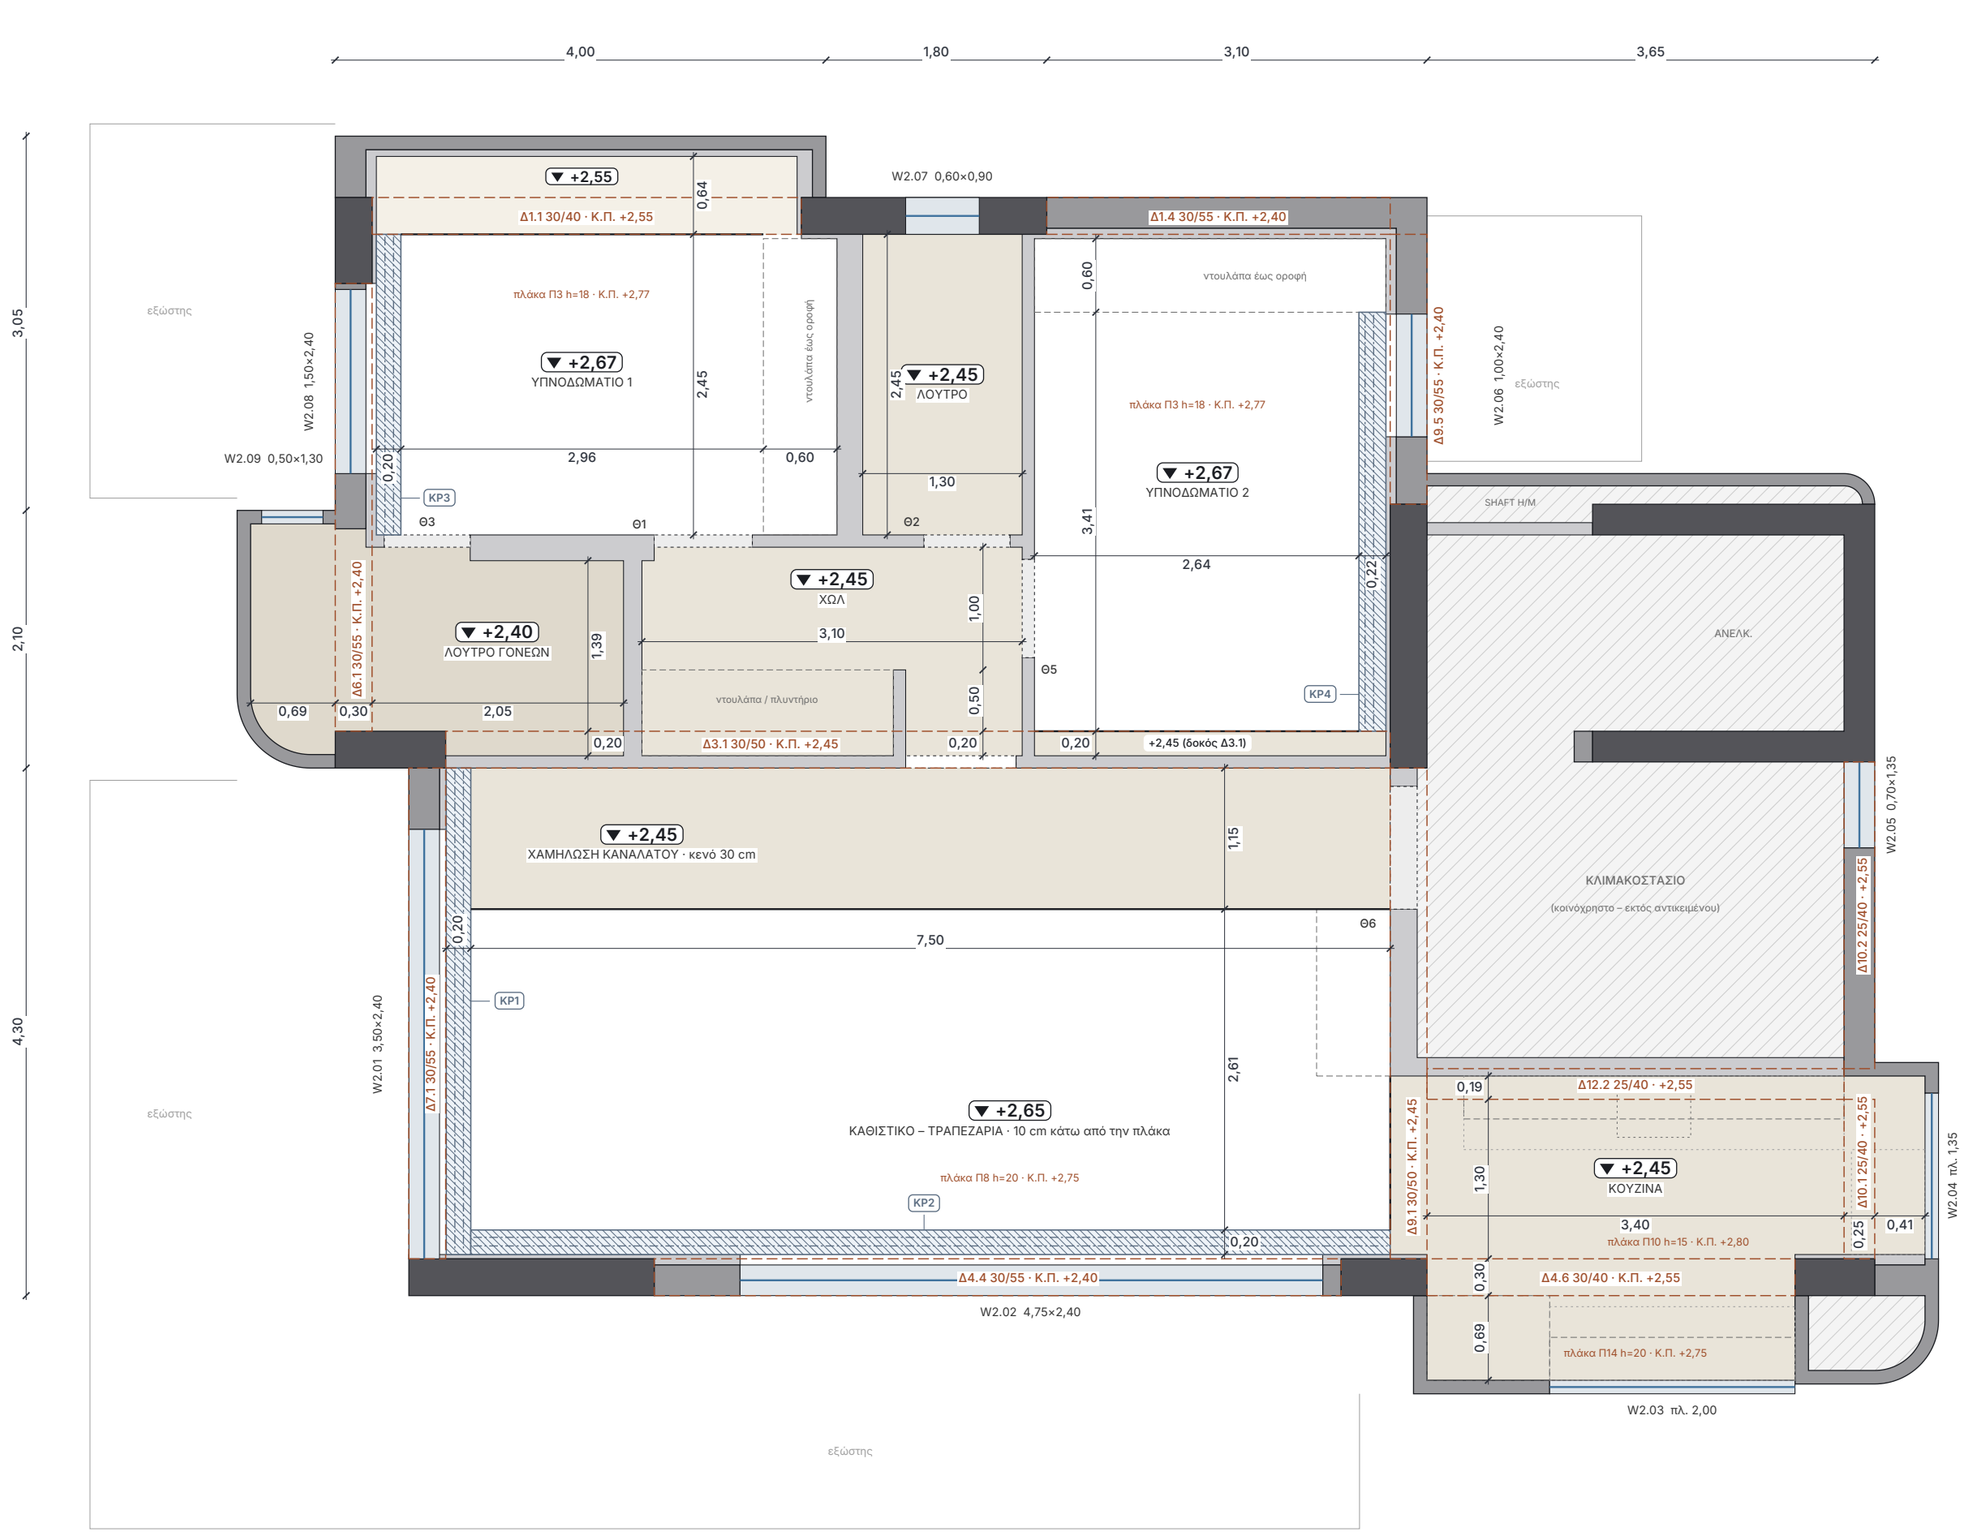

ΥΠΟΜΝΗΜΑ

- +2,65 / +2,67 βασική ψευδοροφή = 10 cm κάτω από την πλάκα
- +2,55 περασιά με τη δοκό 40 cm (κεφαλάρι Υπν.1)
- +2,45 περασιά με δοκούς 50 cm (καναλάτο, χωλ, λουτρό, κουζίνα)
- +2,40 περασιά με δοκό 55 cm (λουτρό γονέων)
- δοκός (Σ5) · Κ.Π. = κάτω παρειά από τελικό δάπεδο
- KP εσοχή διπλού κουρτινόδρομου, ανοιχτή έως την πλάκα
- αλλαγή στάθμης ψευδοροφής
- Στάθμες από τελικό δάπεδο (+6,90) · διαστάσεις σε m

ΕΡΓΟ

ΠΕΝΤΑΟΡΟΦΟ ΚΤΗΡΙΟ ΚΑΤΟΙΚΙΩΝ – ΑΡΓΥΡΟΥΠΟΛΗ

Κωνσταντινουπόλεως 12 & Αγ. Βαρβάρας · Ο.Τ. 103-15

Εργοδότης: INTERKAT Α.Ε. · Κατασκευή: ARKAD Ι.Κ.Ε.

ΘΕΜΑ ΣΧΕΔΙΟΥ

ΑΝΟΨΗ ΟΡΟΦΗΣ Β΄ ΟΡΟΦΟΥ – ΣΤΑΘΜΕΣ

Στάθμες ψευδοροφής · δοκοί · χαμηλώσεις · κουρτινόδρομοι


Βάση: κάτοψη τοιχοποιών Rev.11 (EDGE A-10-2F) · ξυλότυπος Σ5 (+9,85) · μελέτες αδείας Ψ03, ΕΠ04

ΑΡ. ΣΧΕΔΙΟΥ

ΑΝ-01

Κλίμακα 1:50 · Α3

26/10/2026 · R08

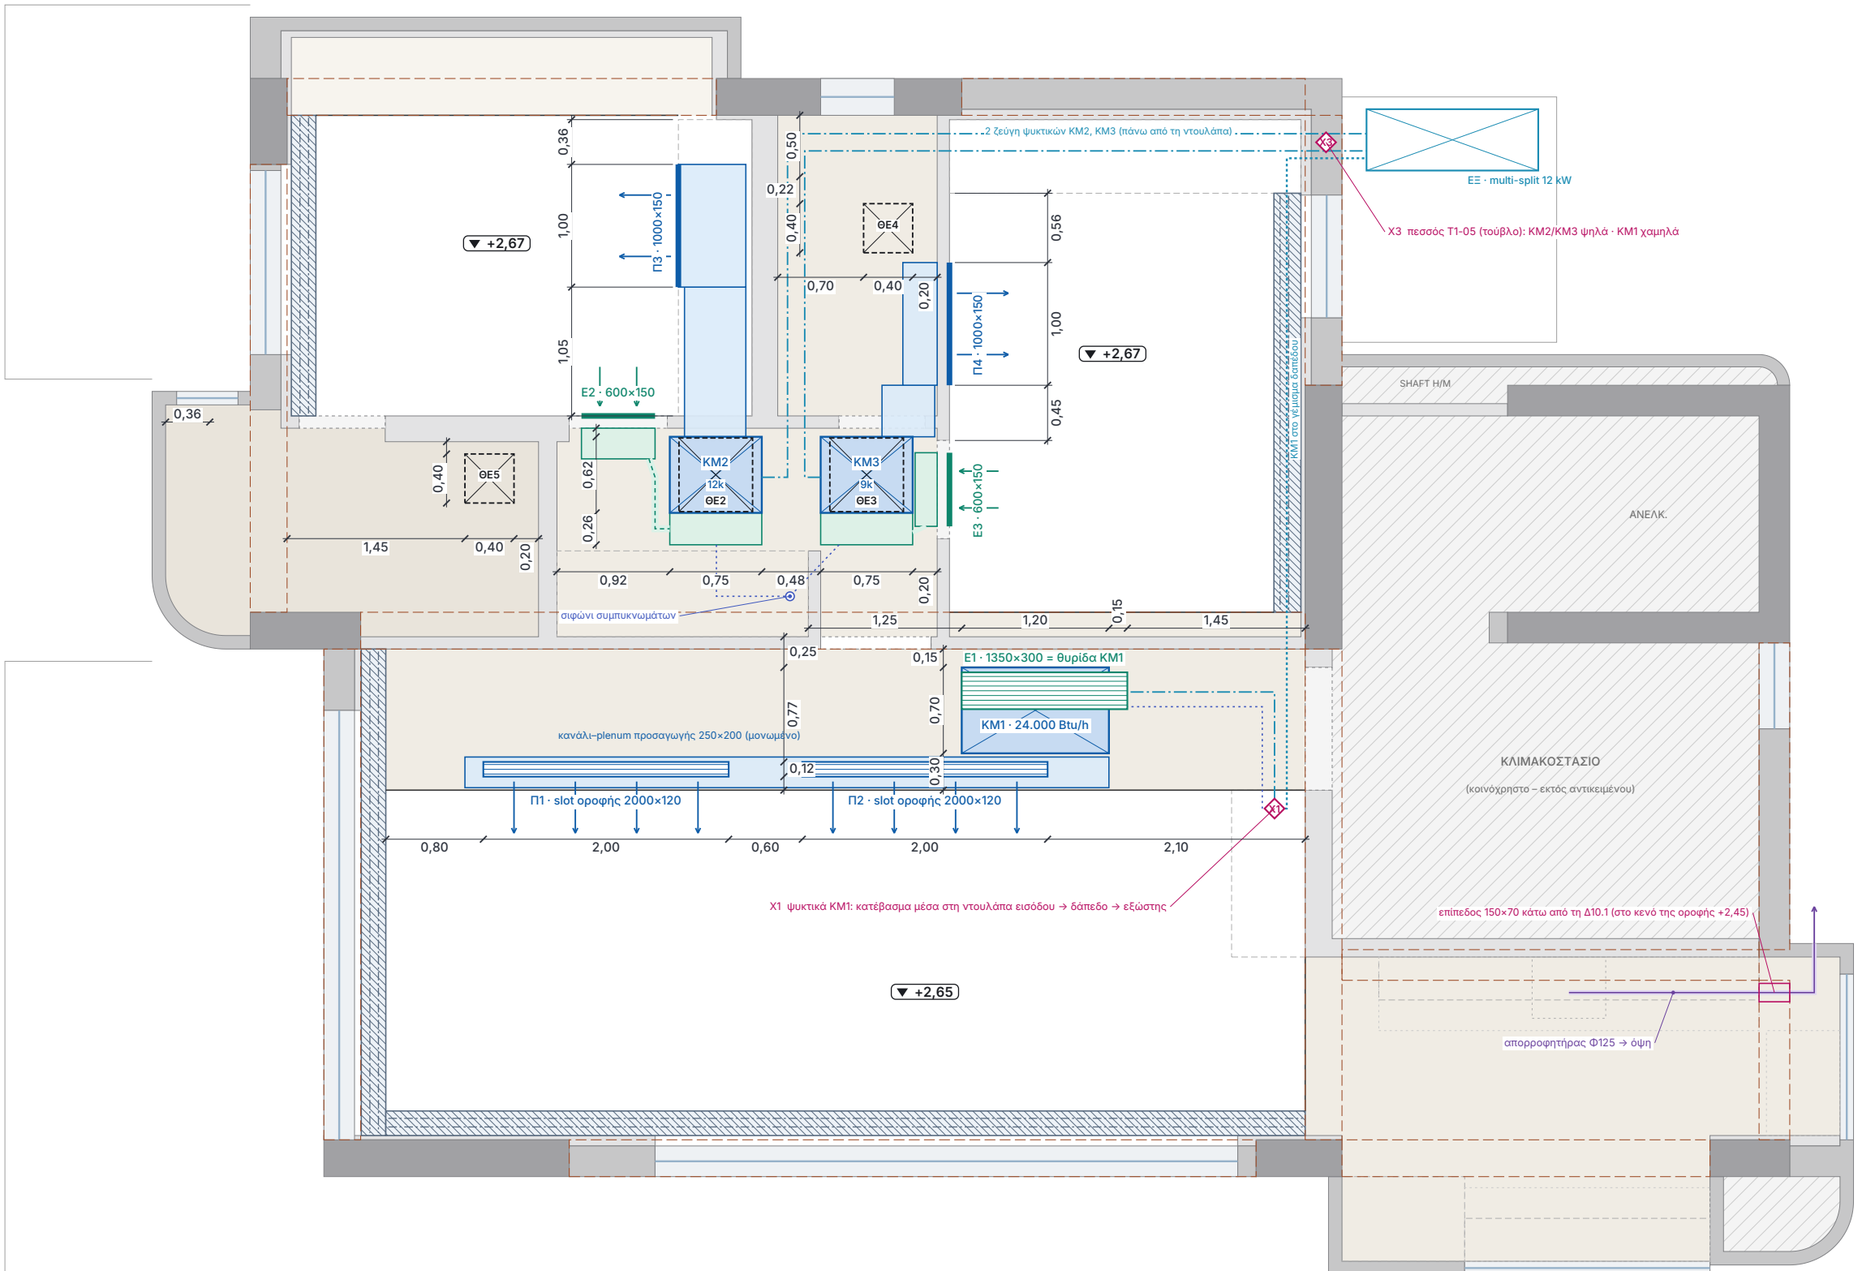

ΥΠΟΜΝΗΜΑ

ΚΜ καναλάτη μονάδα οροφής (slim, ύψος ≤ 20–25 cm) αεραγωγός / plenum προσαγωγής (μονωμένο) κιβώτιο / εύκαμπτος επιστροφής
Π στόμιο προσαγωγής σε κατακόρυφη μετώπη / τοίχο
Ε στόμιο επιστροφής με φίλτρο
Π1/Π2 γραμμικό slot οροφής στο ταβάνι της χαμήλωσης

ΘΕ θυρίδα επίσκεψης (αφανής, βαφόμενη)
ψυκτικές σωληνώσεις (ενδεικτική όδευση)
αποχέτευση συμπυκνωμάτων
ψυκτικές σωληνώσεις ΚΜ1 στο γέμισμα δαπέδου
Χ κατέβασμα / έξοδος σωληνώσεων – καμία οπή σε σκυρόδεμα

ΕΡΓΟ

ΠΕΝΤΑΟΡΟΦΟ ΚΤΗΡΙΟ ΚΑΤΟΙΚΙΩΝ – ΑΡΓΥΡΟΥΠΟΛΗ

Κωνσταντινουπόλεως 12 & Αγ. Βαρβάρας · Ο.Τ. 103-15

Εργοδότης: INTERKAT Α.Ε. · Κατασκευή: ARKAD Ι.Κ.Ε.

ΘΕΜΑ ΣΧΕΔΙΟΥ

ΑΝΟΨΗ Β΄ ΟΡΟΦΟΥ – ΚΛΙΜΑΤΙΣΜΟΣ / ΕΞΑΕΡΙΣΜΟΣ

Καναλάτες μονάδες · αεραγωγοί · στόμια · θυρίδες επίσκεψης · εξαερισμοί

Βάση: κάτοψη τοιχοποιών Rev.11 (EDGE A-10-2F) · ξυλότυπος Σ5 (+9,85) · μελέτες αδείας Ψ03, ΕΠ04

ΑΡ. ΣΧΕΔΙΟΥ

ΑΝ-02

Κλίμακα 1:50 · Α3

26/10/2026 · R08



ΥΠΟΜΝΗΜΑ

- χωνευτό spot LED 7–9 W, 2700 K, CRI ≥ 90, βαθιά λυχνία (UGR < 19)
- χωνευτό spot IP44 (λουτρά)
- χωνευτό spot IP65 (πάνω από ντους)
- ΚΡΕΜ παροχή οροφής για φωτιστικό επιλογής πελάτη (κουτί + ενίσχυση στήριξης)
- LED3 κρυφό γραμμικό πίσω από το κρεβάτι (σχισμή 8 cm)
- παροχή φωτισμού καθρέπτη (τοίχος)
- ΑΚ ανιχνευτής καπνού (μελέτη ΕΠ04)
- ΑΘ θερμοδιαφορικός ανιχνευτής (κουζίνα)
- access point Wi-Fi οροφής (PoE)
- κύκλωμα / ομάδα αφής (βλ. πίνακα AN-07)

ΕΡΓΟ

ΠΕΝΤΑΟΡΟΦΟ ΚΤΗΡΙΟ ΚΑΤΟΙΚΙΩΝ – ΑΡΓΥΡΟΥΠΟΛΗ

Κωνσταντινουπόλεως 12 & Αγ. Βαρβάρας · Ο.Τ. 103-15

Εργοδότης: INTERKAT Α.Ε. · Κατασκευή: ARKAD Ι.Κ.Ε.

ΘΕΜΑ ΣΧΕΔΙΟΥ

ΑΝΟΨΗ Β΄ ΟΡΟΦΟΥ – ΦΩΤΙΣΜΟΣ / ΑΣΘΕΝΗ

Χωνευτά spots · παροχές κρεμαστών · πυρανίχνευση · Wi-Fi

Βάση: κάτοψη τοιχοποιιών Rev.11 (EDGE A-10-2F) · ξυλότυπος Σ5 (+9,85) · μελέτες αδείας Ψ03, ΕΠ04

ΑΡ. ΣΧΕΔΙΟΥ


AN-03

Κλίμακα 1:50 · A3

26/10/2026 · R08


ΤΟΜΗ Α–Α · ΚΑΘΙΣΤΙΚΟ (x = 5,90)

άνοιγμα Α1 – δοκός Δ3.1 – χαμήλωση καναλάτου με slot οροφής – ψευδοροφή – εσοχή κουρτινών – Δ4.4 · 1:20

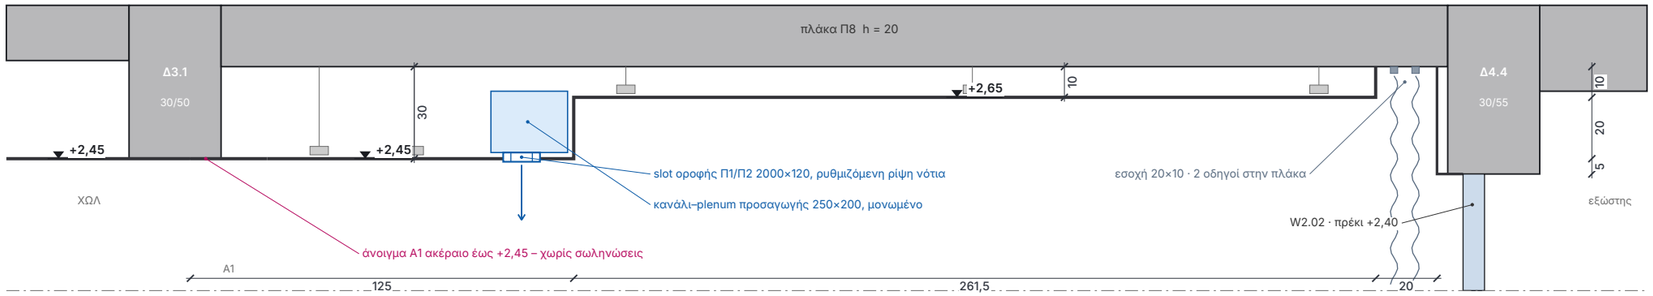


ΤΟΜΗ Β–Β · ΚΕΦΑΛΑΡΙ ΥΠΝ.1 (x = 2,81)

έρκερ – δοκός Δ1.1 – κρυφό LED πίσω από το κρεβάτι · 1:20

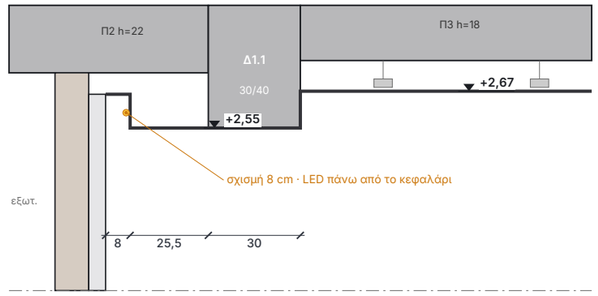


ΤΟΜΗ Γ–Γ · ΝΤΟΥΛΑΠΑ ΥΠΝ.1 – ΧΩΛ (x = 4,60)

αεραγωγός πάνω από τη ντουλάπα – μονάδα ΚΜ2 στο χωλ – θυρίδα – δοκός Δ3.1 · 1:20

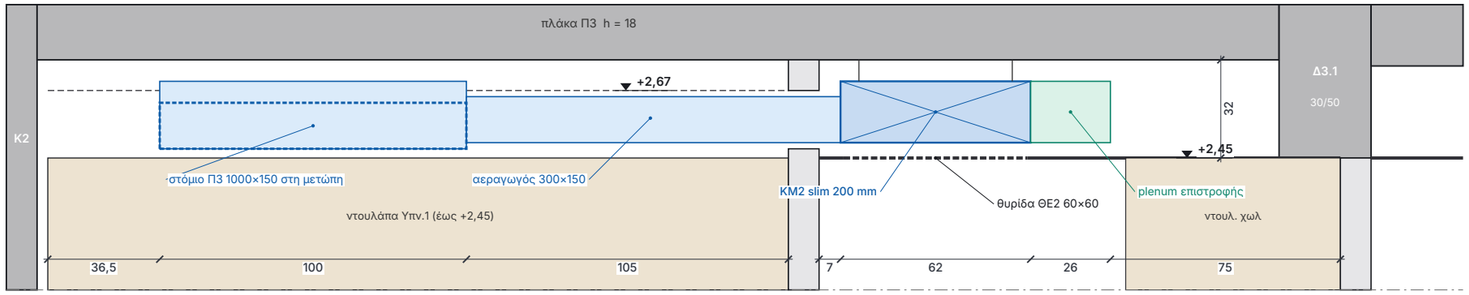


ΤΟΜΗ Δ–Δ · ΚΟΥΖΙΝΑ (x = 11,55)

οροφή +2,45 περασιά με τη Δ9.1 του ανοίγματος – καλύπτει Δ12.2 / Δ4.6 κατά 10 cm · 1:20

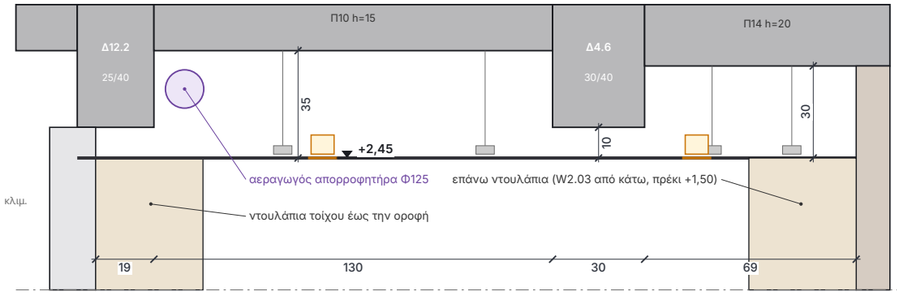

ΤΟΜΗ Ε–Ε · ΣΤΟΜΙΑ ΥΠΝΟΔΩΜΑΤΙΩΝ (y = 2,10)


Υπν.1 (μετώπη ντουλάπας) – λουτρό (κενό με plenum) – Υπν.2 (στόμιο στον τοίχο) · 1:20

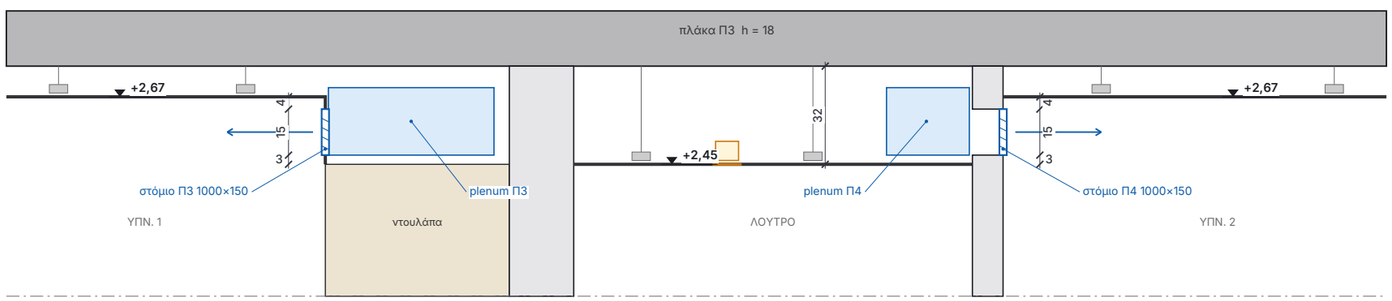

ΣΗΜΕΙΩΣΕΙΣ ΤΟΜΩΝ

1. Οι τομές δείχνουν μόνο το άνω τμήμα του ορόφου (πάνω από +2,00). Στάθμες από το τελικό δάπεδο (+6,90).
2. Άνω στάθμη πλάκας +2,95 (= +9,85). Κάτω παρειές: πλάκα h20 +2,75 · h18 +2,77 · h15 +2,80 · δοκός 40 +2,55 · δοκός 50 +2,45 · δοκός 55 +2,40.
3. Ψευδοροφή: γυψοσανίδα 12,5 mm σε μονό σκελετό CD 60/27 με αναρτήρες άμεσης στήριξης· ανθυγρή στα λουτρά.
4. Κάτω από δοκούς η γυψοσανίδα κολλιέται απευθείας (≈1,5 cm φινίρισμα) – η χαμήλωση φέρεται περασιά με αυτήν.
5. Στις χαμηλώσεις καναλάτου το καθαρό κενό είναι ≥ 27 cm (μονάδα slim ≤ 20–25 cm + ανάρτηση).
6. Χωνευτά φωτιστικά: ύψος σώματος ≤ 75 mm (διαθέσιμο κενό 87 mm στη βασική ψευδοροφή).
7. Εσοχή κουρτινών: 2 οδηγοί στα 7 και 14 cm από τον τοίχο (10 / 17 cm στο ανοιγοανακλινόμενο του Υπν.2), βιδωμένοι στην πλάκα.
8. Ψυκτικά ΚΜ1: από τη μονάδα στο κενό της χαμήλωσης ως την πίσω γωνία της ντουλάπας εισόδου ΝΤ4, κατέβασμα μέσα στη ντουλάπα (σε κουτί), γέμισμα δαπέδου μπροστά στην πόρτα και κατά μήκος του ανατολικού τοίχου του Υπν.2, έξοδος χαμηλά από τον πεσσό Τ1-05 στον εξώστη – καμία οπή σε δοκό, κανένας τοίχος δεν αλλάζει.


ΘΕΣΕΙΣ ΤΟΜΩΝ 1:250

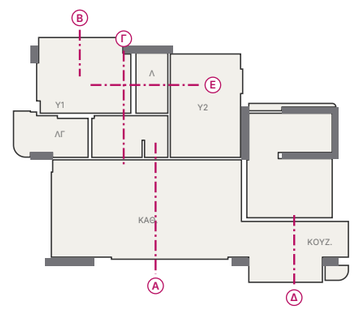

	ΕΡΓΟ **ΠΕΝΤΑΟΡΟΦΟ ΚΤΗΡΙΟ ΚΑΤΟΙΚΙΩΝ – ΑΡΓΥΡΟΥΠΟΛΗ** Κωνσταντινουπόλεως 12 & Αγ. Βαρβάρας · Ο.Τ. 103-15 Εργοδότης: INTERKAT Α.Ε. · Κατασκευή: ARKAD Ι.Κ.Ε.	ΘΕΜΑ ΣΧΕΔΙΟΥ **ΤΟΜΕΣ ΨΕΥΔΟΡΟΦΗΣ Β΄ ΟΡΟΦΟΥ** Τομές Α–Α έως Ε–Ε: σχέση δοκών – ψευδοροφής – καναλάτου – κουρτινών Βάση: κάτοψη τοιχοποιιών Rev.11 (EDGE A-10-2F) · ξυλότυπος Σ5 (+9,85) · μελέτες αδείας Ψ03, ΕΠ04	ΑΡ. ΣΧΕΔΙΟΥ **AN-04** Κλίμακα 1:20 · A3 26/10/2026 · R08


ΛΕΠΤΟΜΕΡΕΙΑ 1 · ΧΑΜΗΛΩΣΗ ΚΑΝΑΛΑΤΟΥ ΚΑΘΙΣΤΙΚΟΥ

δοκός Δ3.1 – κανάλι προσαγωγής – slot οροφής · 1:10

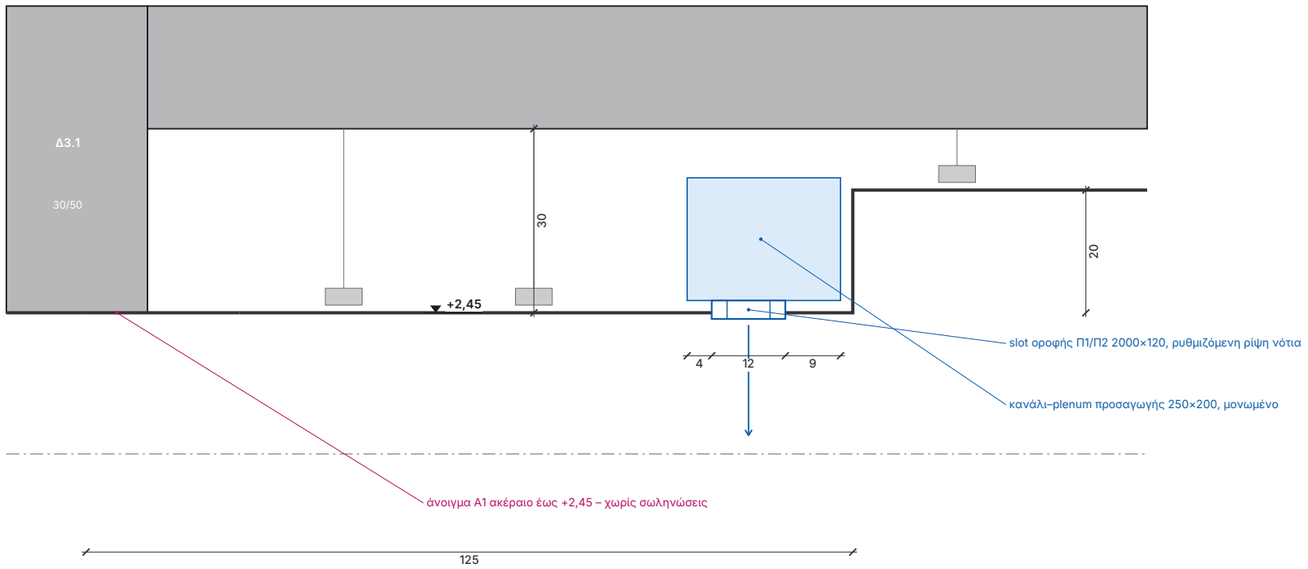


ΛΕΠΤΟΜΕΡΕΙΑ 2 · ΕΣΟΧΗ ΔΙΠΛΟΥ ΚΟΥΡΤΙΝΟΔΡΟΜΟΥ

KP1 / KP2 / KP3 (KP4: 22 cm) – δοκός όψης – πρέκι κουφώματος +2,40 · 1:10

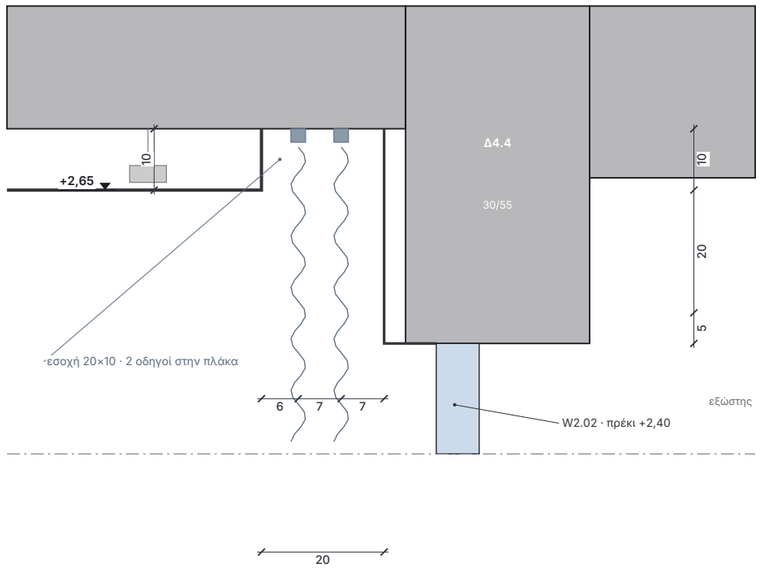


ΛΕΠΤΟΜΕΡΕΙΑ 3 · ΣΤΟΜΙΟ Π3 ΣΤΗ ΜΕΤΩΠΗ ΤΗΣ ΝΤΟΥΛΑΠΑΣ

Υπν.1 – plenum πάνω από τη ντουλάπα · 1:10

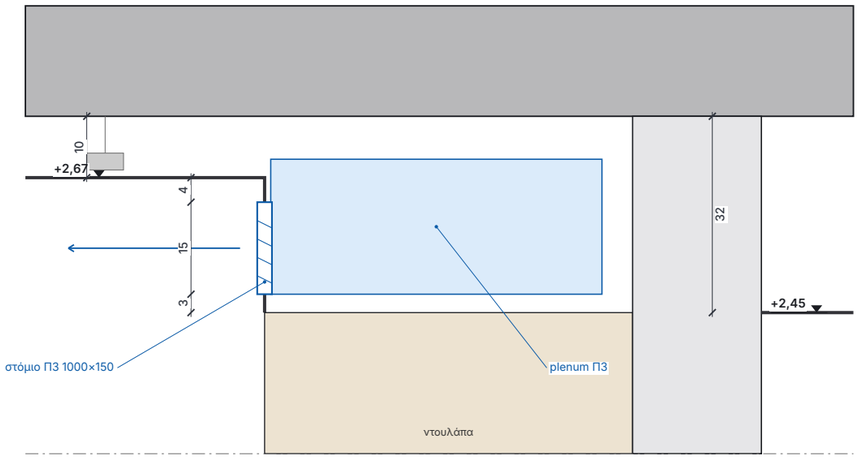


ΛΕΠΤΟΜΕΡΕΙΑ 4 · ΣΤΟΜΙΟ Π4 / Ε3 ΣΕ ΤΟΙΧΟ

plenum στο κενό του λουτρού / χωλ – ψευδοροφή Υπν. +2,67 · 1:10

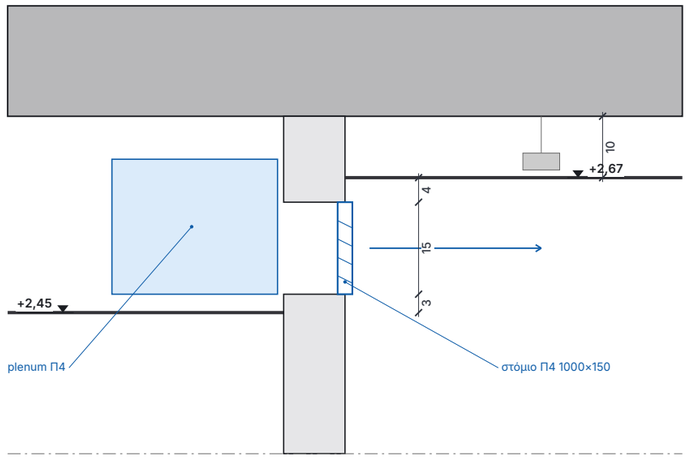

ΛΕΠΤΟΜΕΡΕΙΑ 5 · ΚΡΥΦΟ LED ΠΙΣΩ ΑΠΟ ΤΟ ΚΡΕΒΑΤΙ

έρκερ Υπν.1 – δοκός Δ1.1 – σχισμή 8 cm · 1:10

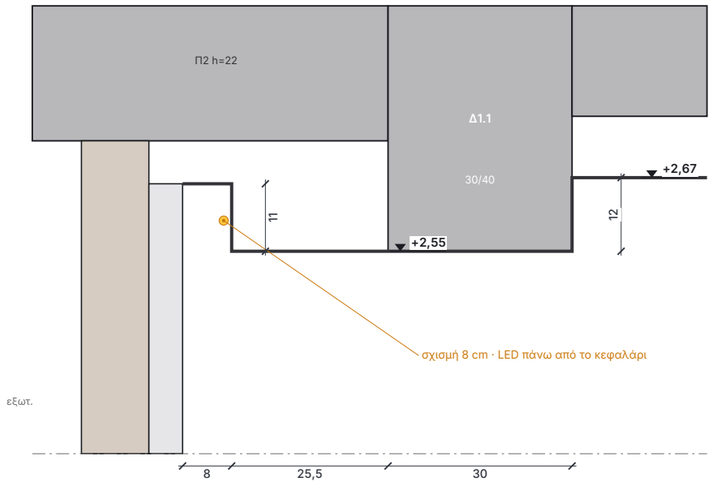

	ΕΡΓΟ **ΠΕΝΤΑΟΡΟΦΟ ΚΤΗΡΙΟ ΚΑΤΟΙΚΙΩΝ – ΑΡΓΥΡΟΥΠΟΛΗ** Κωνσταντινουπόλεως 12 & Αγ. Βαρβάρας · Ο.Τ. 103-15 Εργοδότης: INTERKAT Α.Ε. · Κατασκευή: ARKAD Ι.Κ.Ε.	ΘΕΜΑ ΣΧΕΔΙΟΥ **ΛΕΠΤΟΜΕΡΕΙΕΣ ΨΕΥΔΟΡΟΦΗΣ** Χαμήλωση καναλάτου · εσοχή κουρτινών · στόμια υπνοδωματίων · κρυφό LED κεφαλαριού Βάση: κάτοψη τοιχοποιών Rev.11 (EDGE A-10-2F) · ξυλότυπος Σ5 (+9,85) · μελέτες αδείας Ψ03, ΕΠ04	ΑΡ. ΣΧΕΔΙΟΥ **AN-05** Κλίμακα 1:10 · Α3 26/10/2026 · R08

1 · ΣΤΑΘΜΕΣ ΨΕΥΔΟΡΟΦΗΣ ΑΝΑ ΧΩΡΟ

Στάθμες από το τελικό δάπεδο του ορόφου (Τ.Δ. = +6,90). Άνω στάθμη πλάκας οροφής +2,95 (= +9,85). Κ.Π. = κάτω παρειά σκυροδέματος. Κανόνας: βασική ψευδοροφή 10 cm κάτω από την πλάκα· κάθε χαμήλωση φέρεται «περασιά» με την κάτω παρειά της δοκού του χώρου – πουθενά χαμηλότερα.

Χώρος	Πλάκα · Κ.Π.	Δοκοί στον χώρο · Κ.Π.	Ψευδοροφή	Κενό	Τι καθορίζει τη στάθμη
Καθιστικό – Τραπεζαρία	Π8 h20 · +2,75	καμία δεν διασχίζει· περιμετρικά Δ3.1/Δ9.1 +2,45, Δ7.1/Δ4.4 +2,40	+2,65	10 cm	Βασική στάθμη: το ελάχιστο για χωνευτά spots (σώμα ≤ 75 mm).
Χαμήλωση καναλάτου (βόρεια ζώνη 1,15 m)	Π8 h20 · +2,75	Δ3.1, Δ9.1 · +2,45	+2,45	30 cm	Περασιά με τη Δ3.1. Η νότια ακμή ευθυγραμμίζεται με τη νότια παρειά της κάσας της πόρτας εισόδου. Μονάδα ΚΜ1 + κανάλι + slot οροφής. Μόνο εδώ χαμηλώνει το καθιστικό.
Κουζίνα	Π10 h15 · +2,80 Π14, Π11 h20 · +2,75	Δ12.2, Δ4.6 (διασχίζει), Δ10.1 · +2,55 · στο άνοιγμα Δ9.1 · +2,45	+2,45	35 / 30 cm	Περασιά με τη Δ9.1 του ανοίγματος καθιστικό–κουζίνα: ενιαία οροφή χωρίς «δόντι» στο άνοιγμα. Οι τρεις δοκοί των 40 cm κρύβονται 10 cm πάνω από την οροφή. Ο αεραγωγός του απορροφητήρα χωράει ολόκληρος στο κενό.
Χωλ	Π3 h18 · +2,77	Δ3.1 · +2,45 (νότια)	+2,45	32 cm	Περασιά με τη Δ3.1. Ζώνη Η/Μ: μονάδες ΚΜ2, ΚΜ3, θυρίδες, ψυκτικά.
Λουτρό	Π3 h18 · +2,77	καμία (βόρεια τοιχίο Κ2)	+2,45	32 cm	Αποχέτευση άνω ορόφου, plenum στομίου Π4, εξαερισμός. Ίδια στάθμη με το χωλ.
Λουτρό γονέων	Π3 h18 · +2,77 Π5 h22 · +2,73	Δ6.1 (διασχίζει) · +2,40 Δ3.1 · +2,45	+2,40	37 / 33 cm	Περασιά με τη Δ6.1 (δοκός 55 cm) που περνά μέσα από τον χώρο. Χαμηλότερο σημείο του διαμερίσματος.
Υπνοδωμάτιο 1	Π3 h18 · +2,77	περιμετρικά Δ6.1 +2,40 (δυτ. τοίχος)	+2,67	10 cm	Πλήρες ύψος – χωρίς χαμήλωση για κλιματισμό (στόμιο στη μετώπη της ντουλάπας).
Ζώνη κεφαλαριού Υπν.1 (έρκερ, 63 cm)	Π2 h22 · +2,73	Δ1.1 (διασχίζει) · +2,55	+2,55	18 cm	Περασιά με τη Δ1.1 – καθαρή αλλαγή στάθμης, χωρίς κρυφό φωτισμό.
Υπνοδωμάτιο 2	Π3 h18 · +2,77	περιμετρικά Δ1.4, Δ9.5 +2,40 · Δ3.1 +2,45 (νότια λωρίδα 20 cm, επένδυση)	+2,67	10 cm	Πλήρες ύψος – στόμιο στον τοίχο προς το λουτρό.

Ονομαστικές στάθμες. Όπου η ψευδοροφή είναι περασιά με δοκό, η γυψοσανίδα κολλιέται απευθείας στο σκυρόδεμα: η τελική επιφάνεια βγαίνει ≈1,5 cm κάτω από το μπετό (αναπόφευκτο πάχος φινιρίσματος).

2 · ΕΣΟΧΕΣ ΚΟΥΡΤΙΝΩΝ

Εσοχή ανοικτή έως την πλάκα (χωρίς κουτί), οδηγοί βιδωμένοι στο σκυρόδεμα. Χωράει διπλή κουρτίνα (διαφανής + συσκότιση) με πτυχή.

Αρ.	Κούφωμα	Θέση	Πλάτος	Βάθος	Οδηγοί από τοίχο	Μήκος
ΚΡ1	W2.01 · 3,50×2,40 συρόμενο δίφυλλο	Καθιστικό – δυτικά	20 cm	10 cm (έως +2,75)	7 και 14 cm	3,97 m
ΚΡ2	W2.02 · 4,75×2,40 συρόμενο τρίφυλλο	Καθιστικό – νότια	20 cm	10 cm (έως +2,75)	7 και 14 cm	7,50 m
ΚΡ3	W2.08 · 1,50×2,40 συρόμενο	Υπν.1 – δυτικά	20 cm	10 cm (έως +2,77)	7 και 14 cm	2,45 m
ΚΡ4	W2.06 · 1,00×2,40 ανοιγοανακλινόμενο	Υπν.2 – ανατολικά	22 cm	10 cm (έως +2,77)	10 και 17 cm (χώρος για το φύλλο σε ανάκλιση)	3,42 m
—	W2.03, W2.04 κουζίνας · W2.07, W2.09 λουτρών		—	—	ρολοκουρτίνα μέσα στον λαμπά	—

Οι εσοχές πηγαίνουν από τοίχο σε τοίχο ώστε η κουρτίνα να «παρκάρει» εκτός του ανοίγματος. Κανένα spot σε απόσταση < 30 cm και κανένα στόμιο πάνω ή απέναντι σε εσοχή.

3 · ΚΛΙΜΑΤΙΣΜΟΣ – ΚΑΝΑΛΑΤΕΣ ΜΟΝΑΔΕΣ

Τρεις εσωτερικές καναλάτες χαμηλού προφίλ στην εξωτερική multi-split 12 kW της μελέτης Ψ03 (ΒΑ εξώστης). Μία μονάδα ανά φάτνωμα δοκών: κανένας αεραγωγός δεν περνά κάτω από δοκό.

Αρ.	Ισχύς · ύψος	Θέση	Προσαγωγή	Επιστροφή	Πρόσβαση
ΚΜ1	24.000 Btu/h ύψος ≤ 245 mm	Χαμήλωση καθιστικού, δίπλα στο άνοιγμα Α1 (x 6,60–7,80)	Κανάλι–plenum 250×200 μονωμένο κατά μήκος της χαμήλωσης → slot οροφής Π1, Π2	Ε1 1350×300 στο ταβάνι κάτω από τη μονάδα, προς την πλευρά συνδέσεων (ανοιγόμενο, με φίλτρο)	μέσω του Ε1 – χωρίς ξεχωριστή θυρίδα
ΚΜ2	12.000 Btu/h ύψος ≤ 200 mm	Κενό χωλ (32 cm)	Αεραγωγός 300×150 πάνω από τη ντουλάπα Υπν.1 → plenum → Π3	Ε2 πάνω από τη θύρα Θ1 → εύκαμπτος Φ200	ΘΕ2 60×60
ΚΜ3	9.000 Btu/h ύψος ≤ 200 mm	Κενό χωλ (32 cm)	Αεραγωγός 300×150 πάνω από τη Θ2, μέσα από το κενό του λουτρού → plenum → Π4	Ε3 πάνω από τη θύρα Θ5 → εύκαμπτος Φ160	ΘΕ3 60×60

Αρ.	Είδος	Διάσταση	Θέση · στάθμη	Ρίψη
Π1	προσαγωγή	slot οροφής 2000×120, 2 σχισμές	στο ταβάνι της χαμήλωσης (+2,45), x 2,70–4,70	νότια, κατά μήκος της οροφής +2,65 (ρυθμιζόμενα πτερύγια)
Π2	προσαγωγή	slot οροφής 2000×120, 2 σχισμές	στο ταβάνι της χαμήλωσης (+2,45), x 5,30–7,30	νότια (ρυθμιζόμενα πτερύγια)
Π3	προσαγωγή	γραμμικό 1000×150	μετώπη πάνω από τη ντουλάπα Υπν.1, +2,48 έως +2,63	προς δυτικά, κάτω από την οροφή +2,67
Π4	προσαγωγή	γραμμικό 1000×150	τοίχος Υπν.2 προς λουτρό, +2,48 έως +2,63	προς ανατολικά
Ε1	επιστροφή + θυρίδα	1350×300 ανοιγόμενο με φίλτρο	ταβάνι χαμήλωσης (+2,45), κάτω από την ΚΜ1	—
Ε2	επιστροφή	600×150 με φίλτρο	τοίχος πάνω από τη Θ1, +2,48 έως +2,63	—
Ε3	επιστροφή	600×150 με φίλτρο	τοίχος πάνω από τη Θ5, +2,48 έως +2,63	—

Αρ.	Διάστ.	Θυρίδα επίσκεψης – τι εξυπηρετεί
ΘΕ2	60×60	ΚΜ2 (Υπν.1)
ΘΕ3	60×60	ΚΜ3 (Υπν.2)
ΘΕ4	40×40	Λουτρό: plenum/ρύθμιση Π4, παγίδες αποχέτευσης άνω ορόφου
ΘΕ5	40×40	Λουτρό γονέων: αποχέτευση άνω ορόφου (θέση κατά υδραυλικό)

Ψυκτικά: ξεχωριστό ζεύγος σωλήνων για κάθε μονάδα έως την εξωτερική (3 ζεύγη). ΚΜ1: κενό χαμήλωσης → πίσω γωνία ντουλάπας εισόδου ΝΤ4 → κατέβασμα μέσα στη ντουλάπα → γέμισμα δαπέδου (μπροστά στην πόρτα εισόδου, κατά μήκος του ανατολικού τοίχου του Υπν.2) → πεσσός Τ1-05 χαμηλά → εξώστης, ≈ 10 m· συμπυκνώματα με την αντλία της μονάδας μαζί με τα ψυκτικά σε σιφώνι/υδρορροή εξώστη. ΚΜ2, ΚΜ3: κενό χωλ → κενό λουτρού → πάνω από τη ντουλάπα Υπν.2 → αυλάκι στον πεσσό Τ1-05 ψηλά → εξώστης· συμπυκνώματα σε σιφώνι στη ντουλάπα του χωλ. Καμία οπή σε δοκό.

4 · ΕΞΑΕΡΙΣΜΟΣ

Αρ.	Χώρος	Λύση
—	Λουτρό, Λουτρό γονέων	Χωρίς μηχανικό εξαερισμό (απόφαση ιδιοκτήτη R02). Φυσικός αερισμός από τα ανοιγόμενα παράθυρα W2.07 (0,60×0,90) και W2.09 (0,50×1,30).
ΑΠ	Κουζίνα	Απορροφητήρας στα βόρεια ντουλάπια. Αεραγωγός Φ125 στο κενό της οροφής (y = 7,95) → ανατολικός έρκερ → όψη. Κάτω από τη Δ10.1 περνά ως επίπεδος 150×70 μέσα στο κουτί των ντουλαπιών (βλ. ΑΝ-08, σημείο 4).

5 · ΦΩΤΙΣΜΟΣ – ΚΥΚΛΩΜΑΤΑ

25 χωνευτά spots μόνο στους χώρους που τα χρειάζονται (είσοδος, χωλ, λουτρά, κουζίνα, υπνοδωμάτια), 2 παροχές οροφής στο καθιστικό – τραπεζαρία για φωτιστικά επιλογής πελάτη, κρυφό LED μόνο πίσω από το κρεβάτι. Θερμό λευκό 2700 K, CRI ≥ 90, ίδια σειρά παντού.

Κύκλ.	Χώρος	Φωτιστικά	Έλεγχος · σχόλιο
α	Καθιστικό	ΚΡΕΜ0 · παροχή οροφής (κουτί + ενίσχυση στήριξης)	Αναμονή dimmer. Θέση στο κέντρο του καθιστικού (x = 4,30) – ο πελάτης βάζει κρεμαστό, πλαφονιέρα ή τίποτα. Χωρίς spots.
β	Είσοδος	Ε1, Ε2 · 2 spots	Διακόπτης δίπλα στην πόρτα εισόδου (αλέ-ρετούρ με το χωλ). Και τα δύο στη χαμήλωση +2,45, στον ίδιο άξονα x = 8,80 – φωτίζουν την πόρτα και το πλατύσκαλο εισόδου.
γ	Τραπεζαρία	ΚΡΕΜ1 · παροχή κρεμαστού	Αναμονή dimmer. Στο κέντρο του τραπεζιού (x = 7,50) – οριστικοποίηση με την επίπλωση.
ε	Κουζίνα	Μ1–Μ6 · 6 spots	On/off. Μ1–Μ3 (y = 8,40) μπροστά από τα βόρεια ντουλάπια, Μ4–Μ5 (y = 9,62) μπροστά από τα νότια, Μ6 στον έρκερ. Φωτίζουν τους πάγκους χωρίς LED.
η	Χωλ	Χ1–Χ3 · 3 spots	Αλέ-ρετούρ. Χ1 στη δυτική άκρη, Χ2 ανάμεσα στις δύο μονάδες, Χ3 στο πέρασμα προς το καθιστικό. Οι μονάδες ΚΜ2/ΚΜ3 και οι θυρίδες τους πιάνουν το υπόλοιπο ταβάνι του χωλ.
θ	Υπνοδωμάτιο 1	Υ1–Υ4 · 4 spots	Dimmer, αλέ-ρετούρ από το κεφαλάρι. Εκτός του ίχνους του μαξιλαριού.
ι	Υπνοδωμάτιο 1	LED3 · κρυφό γραμμικό πίσω από το κρεβάτι	Dimmer, ξεχωριστός διακόπτης στο κεφαλάρι.
κ	Υπνοδωμάτιο 2	Π1–Π4 · 4 spots	Dimmer, αλέ-ρετούρ από το κρεβάτι.
μ	Λουτρό	Λ1 (IP65, πάνω από το ντους) · Λ01, Λ02 (IP44) · παροχή καθρέπτη	Γενικός + καθρέπτης σε ξεχωριστό διακόπτη.
ν	Λουτρό γονέων	Γ1 (IP65, πάνω από το ντους) · Γ01, Γ02 (IP44) · παροχή καθρέπτη	Όπως το μ.

Τύπος	Προδιαγραφή
Spot (19 τεμ.)	Χωνευτό LED 7–9 W, 2700 K, CRI ≥ 90, δέσμη 36–40°, βαθιά τοποθετημένη πηγή (UGR < 19), λευκό στεφάνι ή trimless. Ύψος σώματος ≤ 75 mm – διαθέσιμο κενό 87 mm.
Spot λουτρών (4 τεμ.)	Ίδια σειρά σε IP44.
Spot ντους (2 τεμ.)	Ίδια σειρά σε IP65 (ζώνη 1), SELV ή κλάση II.
Κρυφό LED κεφαλαριού	Ταινία ~10 W/m, 2700 K, CRI ≥ 90, σε προφίλ αλουμινίου με οπάλ κάλυμμα, μέσα σε σχισμή 8 cm στη λωρίδα +2,55. Dimmable τροφοδοτικό στο κενό της λωρίδας (18 cm).
Παροχές ΚΡΕΜ0, ΚΡΕΜ1	Κουτί σύνδεσης στην οροφή + ενίσχυση στήριξης (ντίζα στην πλάκα) για φωτιστικό έως 15 kg. Το φωτιστικό είναι επιλογή πελάτη.

6 · ΠΥΡΑΝΙΧΝΕΥΣΗ – ΑΣΘΕΝΗ

Κατά τη μελέτη ενεργητικής πυροπροστασίας της αδείας (Π.Δ. 41/2018): αυτόματη πυρανίχνευση σε όλους τους χώρους πλην W.C.

Αρ.	Είδος	Χώρος	Θέση
ΑΚ1	ανιχνευτής καπνού	Καθιστικό – τραπεζαρία	Εκτός κέντρου: στην ανατολική πλευρά, 55 cm μπροστά από τη ντουλάπα εισόδου (8,25 · 7,20), ≥ 1,80 m από τα στόμια προσαγωγής. Καλύπτει όλο τον χώρο (ακτίνα κάλυψης ~7,5 m).
ΑΚ2	ανιχνευτής καπνού	Υπνοδωμάτιο 1	≥ 50 cm από τοίχο, εκτός της ροής του Π3.
ΑΚ3	ανιχνευτής καπνού	Υπνοδωμάτιο 2	Κέντρο χώρου.
ΑΚ4	ανιχνευτής καπνού	Χωλ	Στον άξονα του περάσματος προς την είσοδο.
ΑΘ5	θερμοδιαφορικός	Κουζίνα	Θερμοδιαφορικός και όχι καπνού, για να μη δίνει ψευδείς συναγερμούς από το μαγείρεμα.
WiFi	access point οροφής	Χαμήλωση καθιστικού	Ένα σημείο στο κέντρο βάρους του διαμερίσματος (PoE, καλώδιο UTP από τον πίνακα ασθενών).

7 · ΤΙ ΕΞΕΤΑΣΤΗΚΕ ΚΑΙ ΔΕΝ ΜΠΗΚΕ

Για να μείνει η οροφή καθαρή, τα παρακάτω δεν προβλέπονται.

Στοιχείο	Γιατί όχι
Κρυφός φωτισμός LED (εκτός κεφαλαριού)	Απόφαση ιδιοκτήτη: κρυφό LED μόνο πίσω από το κρεβάτι του Υπν.1. Η χαμήλωση του καθιστικού μένει καθαρή αλλαγή στάθμης.
Spots στο καθιστικό – τραπεζαρία	Απόφαση ιδιοκτήτη: ο πελάτης επιλέγει τα φωτιστικά του. Προβλέπονται μόνο οι δύο παροχές οροφής ΚΡΕΜ0, ΚΡΕΜ1.
Μηχανικός εξαερισμός λουτρών	Απόφαση ιδιοκτήτη: τα δύο λουτρά έχουν ανοιγόμενο παράθυρο (W2.07, W2.09), επιτρεπτό κατά τον Κτιριοδομικό.
Sprinklers	Δεν απαιτούνται από τη μελέτη πυροπροστασίας της αδείας για κατοικία αυτού του ύψους.
Κάμερες ασφαλείας	Δεν έχουν θέση στο εσωτερικό κατοικίας. Η είσοδος καλύπτεται από τα κοινόχρηστα και τη θυροτηλεόραση.
Ανιχνευτές κίνησης συναγερμού	Τοποθετούνται σε γωνία τοίχου, όχι στην οροφή. Προβλέπεται μόνο σωλήνωση αναμονής από τον ηλεκτρολόγο.
Ηχεία οροφής	Θέλουν κενό ≥ 12 cm – δεν χωρούν στη βασική ψευδοροφή των 10 cm χωρίς πρόσθετη χαμήλωση.
Στόμια / spots στις λωρίδες δοκών	Κάτω από δοκούς δεν υπάρχει κενό· οι λωρίδες μένουν καθαρές.

8 · ΥΛΙΚΑ ΨΕΥΔΟΡΟΦΗΣ

Στοιχείο	Προδιαγραφή
Βασική ψευδοροφή	Γυψοσανίδα 12,5 mm σε μονό μεταλλικό σκελετό CD 60/27 με αναρτήρες άμεσης στήριξης, άξονες 50 cm.
Λουτρά	Ανθυγρή γυψοσανίδα, ίδιος σκελετός, στόκος/αστάρι υγρών χώρων.
Χαμηλώσεις – μετώπες	Διπλός σκελετός όπου κρέμονται μονάδες· οι μονάδες αναρτώνται ανεξάρτητα από την πλάκα με ντίζες και αντικραδασμικά.
Θυρίδες	Αλουμινίου με γυψοσανίδα, αφανείς (βαφόμενες), με ασφάλεια.
Ακμές	Γωνιόκρανα σε όλες τις ακμές χαμηλώσεων και εσοχών· σκοτία 1 cm μόνο αν ζητηθεί.

ΑΛΛΑΓΕΣ ΑΝΑΘΕΩΡΗΣΕΩΝ R02 – R08 · 26/10/2026

Θέμα	Τι άλλαξε σε σχέση με το R01
Καναλάτη καθιστικού	Μένει στη χαμήλωση του καθιστικού, μετακινείται δίπλα στο άνοιγμα Α1. Στόμια προσαγωγής Π1/Π2 στο ταβάνι της χαμήλωσης (slot οροφής) αντί για μετωπικά. Οι σωληνώσεις βγαίνουν προς το χωλ μέσα από πόρταλ 25 cm στο άνοιγμα Α1 – κανένα χιτώνιο σε δοκό.
Φωτισμός	Χωρίς κρυφούς φωτισμούς LED (καταργήθηκαν LED1–LED3, LED ντουλαπιών, εσοχές ντους, σενάρια, ελεγχόμενες πρίζες). Spots μόνο σε χωλ, λουτρά, κουζίνα, υπνοδωμάτια. Καθιστικό χωρίς spots: μία παροχή οροφής επιλογής πελάτη (KPEM0). Τραπεζαρία: παροχή κρεμαστού (KPEM1).
Υπνοδωμάτια	4 spots ανά δωμάτιο (όπως R00). Χωρίς κρεμαστά κομοδίνων.
Λουτρά	Χωρίς μηχανικό εξαερισμό (ΑΝ1, ΑΝ2 και χιτώνιο Χ2 καταργήθηκαν) – αερισμός από τα παράθυρα W2.07, W2.09.
Κουζίνα	6 spots μπροστά από τα επάνω ντουλάπια (3 βόρεια, 2 νότια, 1 έρκερ) – φωτίζουν τους πάγκους χωρίς LED.
R03 · Ψυκτικά ΚΜ1	Καταργείται το πόρταλ: το άνοιγμα Α1 μένει ακέραιο στο +2,45. Οι σωληνώσεις κατεβαίνουν σε αυλάκι τοίχου και περνούν στο γέμισμα του δαπέδου προς τη ντουλάπα του χωλ.
R03 · Φωτισμός	Κρυφό LED πίσω από το κρεβάτι του Υπν.1. Χωλ από 2 σε 3 spots. Νέα spots εισόδου Ε1, Ε2.
R04 · Κουζίνα	Οροφή από +2,55 σε +2,45, περασιά με τη Δ9.1 του ανοίγματος – χωρίς σκαλοπάτι. Επάνω ντουλάπια έως +2,45.
R04 · Είσοδος	Τα δύο spots της εισόδου στην ίδια στάθμη (χαμήλωση +2,45), στον άξονα x = 8,80.
R05 · Πυρανίχνευση	Ο ανιχνευτής ΑΚ1 φεύγει από το κέντρο του καθιστικού, στην ανατολική πλευρά δίπλα στον τοίχο της εισόδου.
R06 · Χαμήλωση καθιστικού	Βάθος από 1,10 σε 1,15 m: η νότια ακμή της χαμήλωσης ευθυγραμμίζεται με την κάσα της πόρτας εισόδου. Κανάλι και slot Π1/Π2 μετακινήθηκαν 5 cm νότια.
R07 · Θυρίδα καθιστικού	Καταργείται η θυρίδα ΘΕ1 60×60 στη χαμήλωση. Η επίσκεψη της ΚΜ1 γίνεται από το ανοιγόμενο στόμιο επιστροφής Ε1, που μεγάλωσε σε 1350×300 και πιάνει και την πλευρά συνδέσεων της μονάδας.
R08 · Ψυκτικά ΚΜ1	Κατέβασμα μέσα στη νέα ντουλάπα εισόδου NT4 (δίπλα στην πόρτα, προς την κουζίνα), δάπεδο έως τον πεσσό Τ1-05, έξοδος χαμηλά στον εξώστη. Καμία επένδυση ή αλλαγή τοίχου. Ε1 μετακινήθηκε 15 cm ανατολικά (συνδέσεις μονάδας προς την είσοδο). ΑΚ1 στο 8,25 · 7,20.

9 · ΕΛΕΓΧΟΣ ΣΥΝΤΟΝΙΣΜΟΥ

Γεωμετρικός έλεγχος όλων των στοιχείων της ανόψης μεταξύ τους και με τον ξυλότυπο Σ5, με τις συντεταγμένες του σχεδίου.

Ομάδα	Τι ελέγχεται	Έλεγχοι	Αποκλίσεις
ΣΤΑΘΜΕΣ	Κάθε ζώνη ψευδοροφής ≥ κάτω παρειά της χαμηλότερης δοκού (+2,40).	11	0
ΔΟΚΟΙ	Κάθε δοκός που τέμνει ζώνη καλύπτεται από την ψευδοροφή – καμία δεν μένει να προεξέχει, καμία ψευδοροφή κάτω από δοκό.	9	0
ΚΛΙΜΑΤΙΣΜΟΣ	Διαθέσιμο κενό ≥ απαιτούμενο για κάθε μονάδα, αεραγωγό, plenum· κανένα στο ίχνος δοκού.	12	0
ΦΩΤΙΣΜΟΣ	Κάθε spot έχει κενό ≥ 8 cm, δεν πέφτει σε δοκό / αεραγωγό / θυρίδα / εσοχή, απέχει ≥ 25 cm από κάθε άλλο σημείο οροφής.	29	0
ΠΥΡΑΝΙΧΝΕΥΣΗ	Ανιχνευτές ≥ 50 cm από τοίχο και ≥ 1,00 m από στόμιο προσαγωγής.	5	0
ΣΤΟΜΙΑ	Κανένα spot σε < 40 cm από στόμιο, κανένα στόμιο σε εσοχή κουρτίνας, ελεύθερη ρίψη ≥ 2,5 m κατά μήκος της οροφής.	6	0
ΘΥΡΙΔΕΣ	Κάθε μονάδα έχει θυρίδα στο ίχνος της· οι θυρίδες δεν πέφτουν σε δοκό ή φωτιστικό.	7	0
ΚΟΥΡΤΙΝΕΣ	Πλάτος ≥ 20 cm, βάθος 10 cm έως την πλάκα, κανένα spot < 30 cm, κανένα στόμιο.	4	0
ΣΥΝΟΛΟ		83	0

Ο έλεγχος είναι γεωμετρικός, πάνω στα δεδομένα του σχεδίου. Δεν υποκαθιστά την επιμέτρηση επί τόπου μετά το ξεκαλούπωμα: οι πραγματικές κάτω παρειές δοκών και πλακών μετρώνται πριν στηθεί ο σκελετός.

10 · ΑΠΟΚΛΙΣΕΙΣ ΑΠΟ ΤΗ ΜΕΛΕΤΗ ΑΔΕΙΑΣ

Όλα τα υπόλοιπα ακολουθούν τα σχέδια αδείας και την κάτοψη τοιχοποιιών Rev.11.

Θέμα	Τι αλλάζει και γιατί
Θέση καναλάτης 24.000	Η Ψ03 τη δείχνει πάνω από το χωλ. Από εκεί οι αεραγωγοί θα έπρεπε να περάσουν κάτω από τη Δ3.1 (+2,45), δηλαδή ψευδοροφή στο +2,20. Μεταφέρθηκε στη βόρεια ζώνη του καθιστικού, στην ίδια πλευρά της δοκού με τον χώρο που εξυπηρετεί.
Κλιματισμός υπνοδωματίων	Η Ψ03 προβλέπει μονάδες τοίχου 12.000 και 9.000. Εδώ σχεδιάστηκαν καναλάτες ίδιας ισχύος στο κενό του χωλ, ώστε να είναι κρυφές. Η εξωτερική μονάδα και οι ισχείς δεν αλλάζουν. Είναι επιλογή – βλ. σημείο 6.
Ανιχνευτής κουζίνας	Θερμοδιαφορικός αντί καπνού (συνήθης πρακτική· επιβεβαίωση από τον μελετητή πυροπροστασίας).

11 · ΑΝΟΙΚΤΑ ΣΗΜΕΙΑ – ΤΙ ΧΡΕΙΑΖΕΤΑΙ ΑΠΟΦΑΣΗ

Α. ΚΑΤΑΣΚΕΥΑΣΤΙΚΑ – ΠΡΙΝ ΤΗ ΣΚΥΡΟΔΕΤΗΣΗ ΚΑΙ ΤΙΣ ΤΟΙΧΟΠΟΙΙΕΣ


1. Καμία οπή ή χιτώνιο σε δοκό ή τοιχίο, κανένας τοίχος δεν αλλάζει. Τα ψυκτικά και τα συμπυκνώματα της ΚΜ1 κατεβαίνουν μέσα στη ντουλάπα εισόδου NT4 (κουτί στην πίσω γωνία, x ≈ 9,15–9,40), περνούν στο γέμισμα του δαπέδου (μονωμένα, ενιαία χωρίς ενώσεις, μέσα σε σωλήνα προστασίας) μπροστά στην πόρτα εισόδου και κατά μήκος του ανατολικού τοίχου του Υπν.2, και βγαίνουν στον εξώστη χαμηλά μέσα από τον πεσσό Τ1-05. Πρέπει να μπουν ΠΡΙΝ το γέμισμα. Η ντουλάπα φτάνει ως την οροφή.
2. Χ3 – πεσσός από τούβλο Τ1-05 (ΒΑ γωνία Υπν.2, ανάμεσα στον βόρειο τοίχο και το παράθυρο W2.06): ψηλά αυλάκι για ΚΜ2/ΚΜ3 κάτω από τη Δ9.5, χαμηλά διέλευση για την ΚΜ1. Συμπυκνώματα ΚΜ1 σε σιφώνι ή υδρορροή του εξώστη – επιβεβαίωση από τον υδραυλικό.
3. Δοκός Δ10.1 (ανατολικά της κουζίνας): στον ξυλότυπο Σ5 δεν έχει ετικέτα διατομής. Θεωρήθηκε 25/40 όπως η συνέχειά της Δ10.2. Αν είναι υψηλότερη, αλλάζει η στάθμη στη λωρίδα του έρκερ της κουζίνας.
4. Απορροφητήρας: με την κουζίνα στο +2,45 ο αεραγωγός περνά κάτω από τη Δ10.1 (+2,55) ως επίπεδος 150×70 μέσα στο κενό της οροφής – δεν υπάρχει πια κανένα δίκτυο έξω από την ψευδοροφή.

Β. ΑΠΟΦΑΣΕΙΣ ΙΔΙΟΚΤΗΤΗ / ΠΕΛΑΤΗ

5. Φωτιστικά καθιστικού και τραπεζαρίας: προβλέπονται μόνο δύο παροχές οροφής (KPEM0 στο καθιστικό, KPEM1 στην τραπεζαρία) με κουτί σύνδεσης και ενίσχυση στήριξης στην πλάκα. Ο πελάτης επιλέγει φωτιστικό (κρεμαστό, πλαφονιέρα ή τίποτα + φωτιστικά δαπέδου). Οι θέσεις οριστικοποιούνται με την επίπλωση πριν κλείσει η γυψοσανίδα.
6. Καναλάτα και στα υπνοδωμάτια; Αν μείνουν οι μονάδες τοίχου της Ψ03, καταργούνται τα ΚΜ2, ΚΜ3, Π3, Π4, Ε2, Ε3, ΘΕ2, ΘΕ3 και το χωλ μπορεί να ανέβει στο +2,67 (εκτός από τη λωρίδα της Δ3.1). Οι οροφές των υπνοδωματίων δεν αλλάζουν σε καμία περίπτωση.
7. Λουτρό γονέων στο +2,40: είναι περασιά με τη Δ6.1 που διασχίζει τον χώρο. Εναλλακτικά +2,45 με τη δοκό να προεξέχει 5 cm ως «νεύρο» – δεν προτείνεται.

Γ. ΣΥΝΤΟΝΙΣΜΟΣ ΣΥΝΕΡΓΕΙΩΝ

8. Ψυκτικός / μηχανολόγος: τελική επιλογή μονάδων με ύψος ≤ 245 mm (KM1) και ≤ 200 mm (KM2, KM3) και στατική πίεση για τα μήκη του σχεδίου. Έλεγχος ταχύτητας στο κανάλι 250×200 της ΚΜ1 (στόχος ≤ 4–5 m/s) και επιλογή slot οροφής με ρυθμιζόμενα πτερύγια (ρίψη νότια, κατά μήκος της οροφής +2,65).
9. Υδραυλικός: οι αποχετεύσεις των λουτρών του Γ΄ ορόφου περνούν στα κενά των δύο λουτρών (32–37 cm). Οι θυρίδες ΘΕ4, ΘΕ5 μετακινούνται επί τόπου κάτω από τις παγίδες.
10. Ηλεκτρολόγος: κυκλώματα α–ν, dimmers στα υπνοδωμάτια, UTP για το access point, καλωδίωση πυρανίχνευσης πριν κλείσει η οροφή. Οι δύο παροχές KPEM0/KPEM1 με αναμονή διακόπτη (dimmer) στο καθιστικό· τροφοδοτικό του LED κεφαλαριού επισκέψιμο.
11. Παράθυρο κουζίνας W2.03: για να μπουν επάνω ντουλάπια και στη νότια πλευρά, το πρέκι πρέπει να είναι στο 1,50 όπως γράφει η κάτοψη (παράθυρο-λωρίδα ανάμεσα σε πάγκο και ντουλάπια). Ο πίνακας κουφωμάτων γράφει 2,35 – να διορθωθεί ΠΡΙΝ την παραγγελία του κουφώματος και το χτίσιμο του πρεκιού.
12. Μέτρηση επί τόπου μετά το ξεκαλούπωμα: οι στάθμες του σχεδίου βασίζονται στις θεωρητικές διατομές του Σ5. Ανοχές σκυροδέτησης ±1–2 cm απορροφώνται στη βασική ψευδοροφή, όχι στις λωρίδες δοκών.

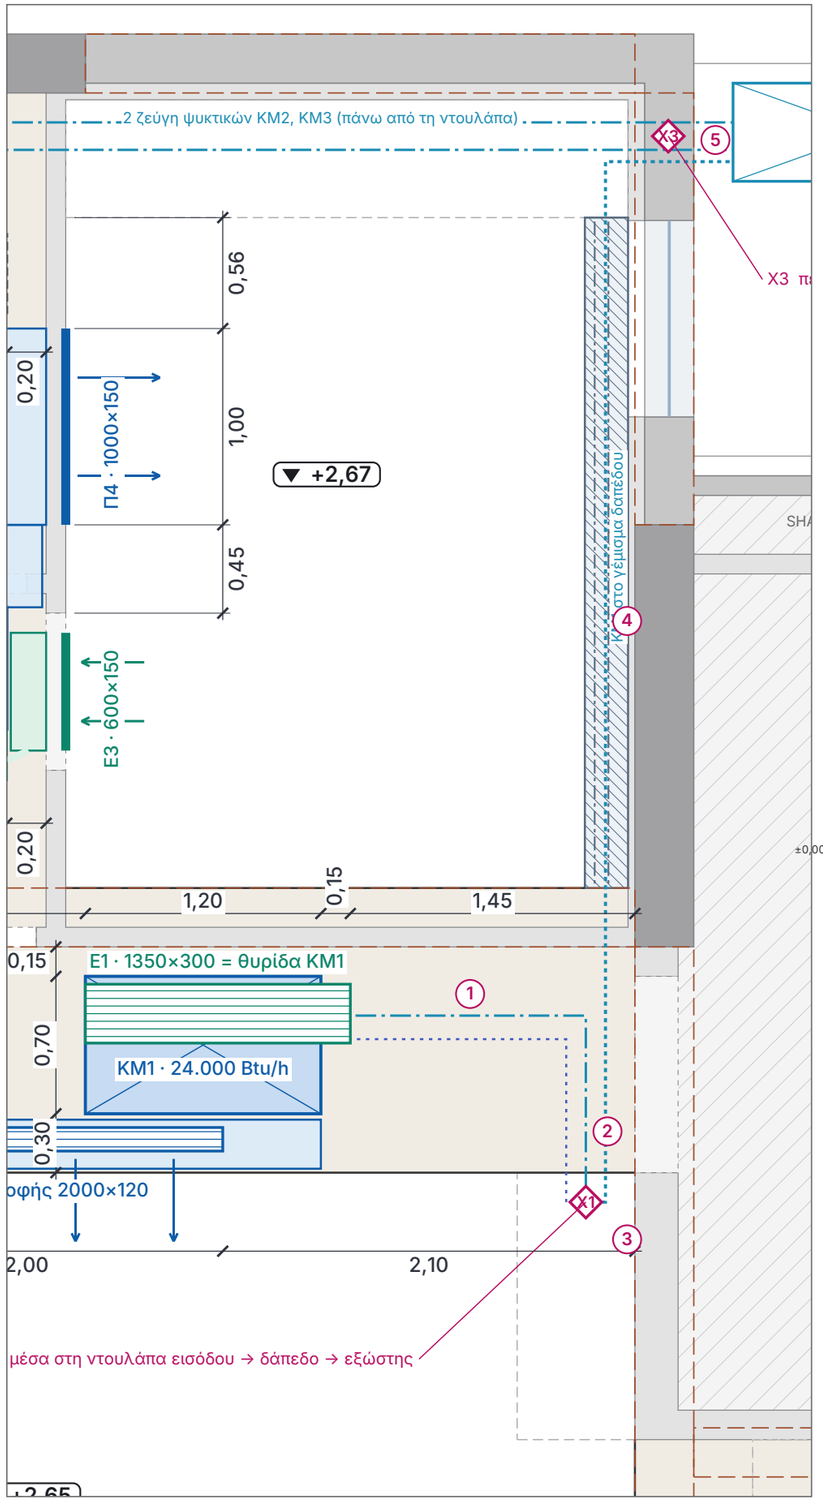


Απόσπασμα ΑΝ-02 (κλίμακα ≈ 1:31)

ΠΩΣ ΠΕΡΝΟΥΝ ΟΙ ΣΩΛΗΝΕΣ ΤΗΣ ΚΜ1 (ΣΑΛΟΝΙ) ΣΤΟΝ ΕΞΩΣΤΗ

Γύρω από το καθιστικό και οι τέσσερις τοίχοι είναι ακριβώς κάτω από δοκούς (Δ3.1, Δ9.1, Δ7.1, Δ4.4), περασιά. Ο σωλήνας δεν μπορεί να «μπει» σε τοίχο από την οροφή χωρίς να φαίνεται. Γι' αυτό κατεβαίνει μέσα στη ντουλάπα της εισόδου, που φτάνει ως την οροφή, και συνεχίζει στο δάπεδο. Καμία οπή σε δοκό, κανένας τοίχος δεν αλλάζει.

1. **Στο ταβάνι**
   Από τις συνδέσεις της μονάδας (ανατολική πλευρά) τα ψυκτικά και το σωληνάκι συμπυκνωμάτων πάνε ανατολικά μέσα στο κενό της χαμήλωσης (+2,45, κενό 30 cm), ως πάνω από τη ντουλάπα εισόδου.
2. **Μέσα στη ντουλάπα**
   Κατεβαίνουν κατακόρυφα στην πίσω γωνία της ντουλάπας εισόδου ΝΤ4 (προς τον τοίχο της εισόδου), μέσα σε κουτί από μοριοσανίδα / γυψοσανίδα ≈ 12×12 cm. Η ντουλάπα φτάνει ως την οροφή, άρα δεν φαίνεται τίποτα.
3. **Στο δάπεδο**
   Στο κάτω μέρος της ντουλάπας μπαίνουν στο γέμισμα του δαπέδου (15 cm από την πλάκα έως το τελικό δάπεδο), μέσα σε εύκαμπτο σωλήνα προστασίας, μονωμένα, χωρίς ενώσεις.
4. **Κάτω από το Υπν.2**
   Περνούν μπροστά από την πόρτα εισόδου, κάτω από τον τοίχο καθιστικού / Υπν.2 και συνεχίζουν βόρεια κατά μήκος του ανατολικού τοίχου του Υπν.2 (≈ 5,3 m στο δάπεδο).
5. **Έξοδος στον εξώστη**
   Στη γωνία του Υπν.2 βγαίνουν χαμηλά (≈ +0,10) μέσα από τον πεσσό από τούβλο Τ1-05 στον ΒΑ εξώστη και συνδέονται στην εξωτερική μονάδα. Τα συμπυκνώματα (με την αντλία της μονάδας) σε σιφώνι / υδρορροή του εξώστη.

ΑΝΑΠΤΥΓΜΑ ΔΙΑΔΡΟΜΗΣ (σχηματικό – ύψη υπό κλίμακα 1:50)

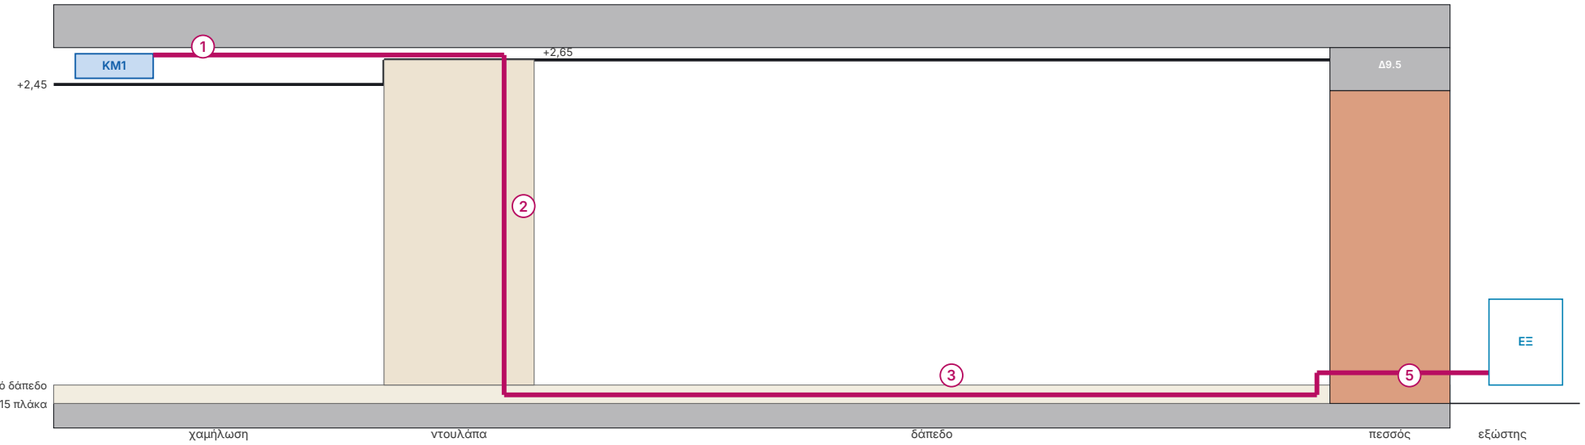

	ΕΡΓΟ **ΠΕΝΤΑΟΡΟΦΟ ΚΤΗΡΙΟ ΚΑΤΟΙΚΙΩΝ – ΑΡΓΥΡΟΥΠΟΛΗ** Κωνσταντινουπόλεως 12 & Αγ. Βαρβάρας · Ο.Τ. 103-15 Εργοδότης: INTERKAT Α.Ε. · Κατασκευή: ARKAD Ι.Κ.Ε.	ΘΕΜΑ ΣΧΕΔΙΟΥ **ΟΔΕΥΣΗ ΨΥΚΤΙΚΩΝ ΚΜ1 – ΚΑΘΙΣΤΙΚΟ** Κατέβασμα μέσα στη ντουλάπα εισόδου · γέμισμα δαπέδου · έξοδος από τον πεσσό Τ1-05 Βάση: κάτοψη τοιχοποιιών Rev.11 (EDGE A-10-2F) · ξυλότυπος Σ5 (+9,85) · μελέτες αδείας Ψ03, ΕΠ04	ΑΡ. ΣΧΕΔΙΟΥ **ΑΝ-09** Κλίμακα 1:31 / σχηματικό · Α3 26/10/2026 · R08