ΑΠΟΧΕΤΕΥΣΕΙΣ & ΥΔΡΟΡΡΟΕΣ

Πενταόροφο κτήριο κατοικιών – Κωνσταντινουπόλεως 12 & Αγ. Βαρβάρας, Αργυρούπολη

Τεύχος R12 · 27/10/2026 · INTERKAT Α.Ε. / ARKAD Ι.Κ.Ε.

ΠΕΡΙΕΧΟΜΕΝΑ (σειρά: από κάτω προς τα πάνω, μετά λεπτομέρειες και έλεγχος)

ΑΠ-01	Κατακόρυφο διάγραμμα στηλών & υδρορροών · αναμονές πλακών	σχηματικό	σελ. 2
ΑΠ-02	Οροφή υπογείου – συλλεκτήρας κάτω από τις δοκούς · έξοδος −0,84	1:50	σελ. 3
ΑΠ-03	ΑΠ4 – εξωτερική στο κενό της καμπύλης · κουτί χώλ ισογείου	1:30	σελ. 4
ΑΠ-04	Ισόγειο ΙΣ1 – πτώσεις · υδρορροές ψηλά → κάθοδος στην είσοδο	1:50	σελ. 5
ΑΠ-05	Β΄ όροφος (τυπικός Α΄–Δ΄) – κάτοψη Β1	1:50	σελ. 6
ΑΠ-06	Λεπτομέρειες Β1 – θέσεις στηλών, αναμονή πλάκας, θερμοπρόσοψη	1:25 / 1:15 / 1:10	σελ. 7
ΑΠ-07	Τοίχοι εγκατάστασης λουτρών Β1	1:20	σελ. 8
ΑΠ-08	Σοφίτα (Δ1) – λουτρό → ΑΠ1 · WC → ΑΠ2 · όλοι οι αερισμοί έξω	1:50	σελ. 9
ΑΠ-09	Παρατηρήσεις αριθμημένες – προς απάντηση	—	σελ. 10

Κύριες αρχές

- ΑΠ1 (λουτρά + λουτρό σοφίτας), ΑΠ3 (λουτρά γονέων) εσωτερικές · ΑΠ2 (WC σοφίτας) και ΑΠ4 (κουζίνες) εξωτερικές.
- Καμία σωλήνωση στις χαμηλές ζώνες · ΚΑΜΙΑ διάτρηση δοκού: συλλεκτήρας κάτω από τις δοκούς, π.α. −0,65 → −0,84 · ΕΥΔΑΠ −1,50.
- Όλοι οι αερισμοί βγαίνουν έξω από τοίχους και ανεβαίνουν στη θερμοπρόσοψη (ΚΑ1, ΑΠ2, ΚΑ2, ΚΑ3) – κανένας σε οροφή.
- Υδρορροές μέσα στη θερμοπρόσοψη, συλλεκτήρες ψηλά στο +3,30, μία κάθοδος στον τοίχο της εισόδου → ρείθρο Κωνσταντινουπόλεως.
- Λεκάνες κρεμαστές με εντοιχισμένο καζανάκι, σωλήνας λεκάνης μέσα στους τοίχους.

ΕΡΓΟ

ΠΕΝΤΑΟΡΟΦΟ ΚΤΗΡΙΟ ΚΑΤΟΙΚΙΩΝ – ΑΡΓΥΡΟΥΠΟΛΗ

Κωνσταντινουπόλεως 12 & Αγ. Βαρβάρας · Ο.Τ. 103-15

Εργοδότης: INTERKAT Α.Ε. · Κατασκευή: ARKAD Ι.Κ.Ε.

ΘΕΜΑ ΣΧΕΔΙΟΥ

ΕΞΩΦΥΛΛΟ – ΠΕΡΙΕΧΟΜΕΝΑ

Αποχετεύσεις & υδρορροές όλων των επιπέδων

9 φύλλα – R12

Βάση: Α-10 (αρχιτεκτονικά) · Σ2 εφαρμογής · τομή Α-30-ΑΑ

ΑΡ. ΣΧΕΔΙΟΥ


ΑΠ-00

— · A2

27/10/2026 · R12

ΚΑΤΑΚΟΡΥΦΟ ΔΙΑΓΡΑΜΜΑ ΣΤΗΛΩΝ & ΥΔΡΟΡΡΟΩΝ (σχηματικό)

R12 · ΑΠ1 / ΑΠ3 εσωτερικές · ΑΠ2 / ΑΠ4 εξωτερικές · όλοι οι αερισμοί έξω (ΚΑ1 · ΑΠ2 · ΚΑ2 · ΚΑ3) · όμβρια ψηλά → είσοδος

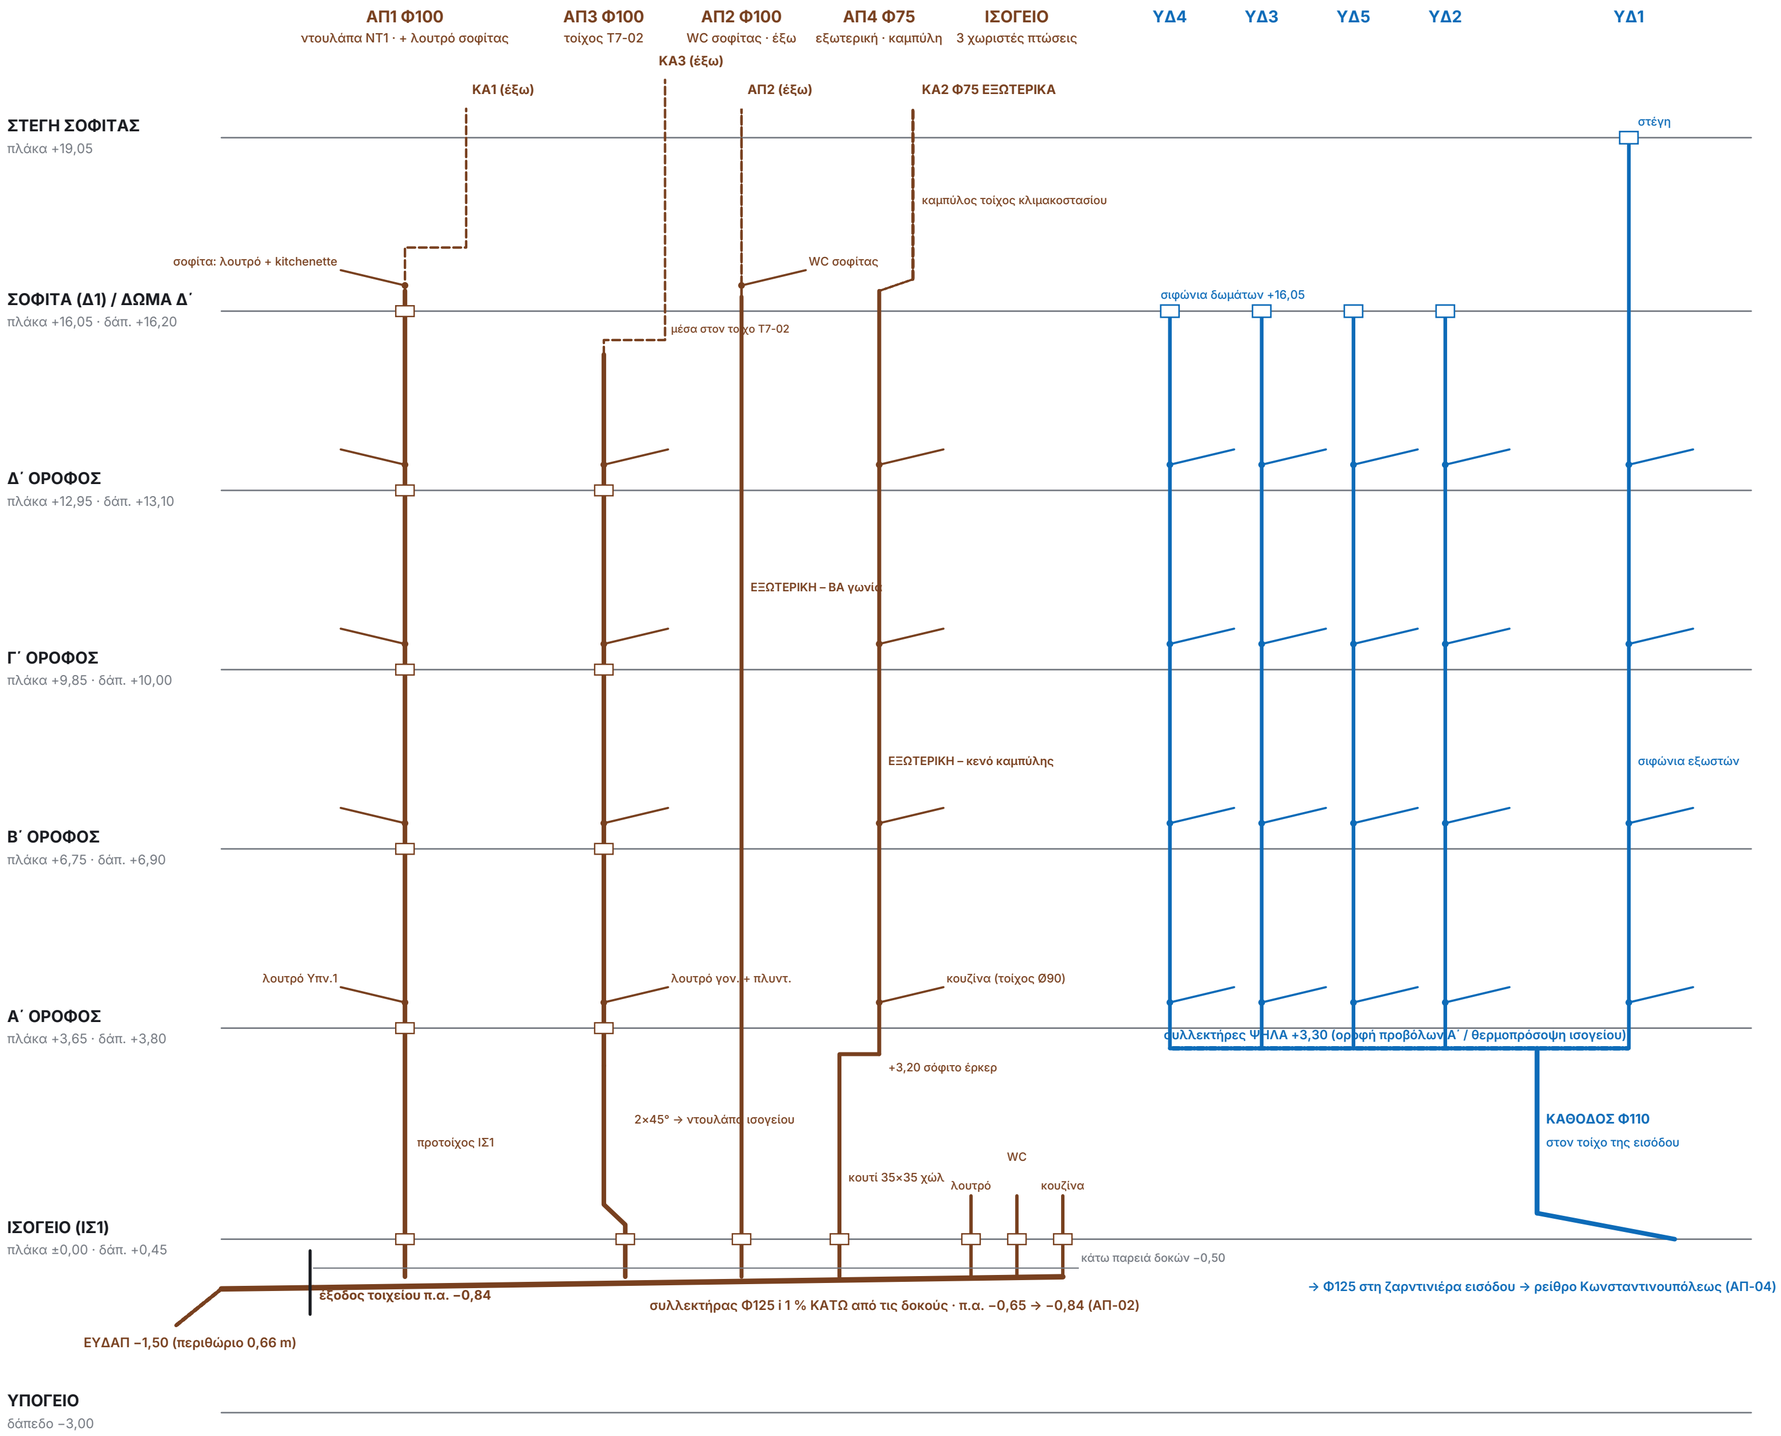

ΑΝΑΜΟΝΕΣ ΠΛΑΚΩΝ (χιτώνια)

στοιχείο	x / y (m)	Ø	πλάκες
ΑΠ1	4,83 / 0,93	160	±0,00 · 3,65 · 6,75 · 9,85 12,95 · 16,05
ΑΠ3	3,08 / 3,38	160	3,65 · 6,75 · 9,85 · 12,95
ΑΠ3 ισόγ.	3,15 / 3,95	160	±0,00 (ντουλάπα ισογείου)
ΑΠ2	9,79 / 0,72	160	εξωτερική · μόνο ±0,00
ΑΠ4	13,35 / 9,69	—	εξωτερική · καμία αναμονή
ΑΠ4 ισόγ.	12,85 / 8,97	160	±0,00 (κουτί χώλ)
ΑΠ4 τοίχος	+3,20	160	διέλευση τοιχείου έρκερ
ΚΑ1–ΚΑ3	εξωτερικά	—	καμία διάτρηση οροφής
ισόγειο ΙΣ1	βλ. ΑΠ-02	75–160	±0,00 · 3 πτώσεις
ΥΔ1–ΥΔ5	βλ. ΑΠ-08	125	σιφώνια δωμάτων / στέγης

ΣΗΜΕΙΩΣΕΙΣ

- ΑΠ2 μόνο για το WC σοφίτας (εξωτερική).
- ΑΠ4 εξωτερική στο κενό της καμπύλης (ΑΠ-03).
- Όλοι οι αερισμοί έξω – κανένας σε οροφή.
- Καμία διάτρηση δοκού – έξοδος π.α. −0,84.
- Όροφοι Α΄–Δ΄: ίδια διάταξη με το Β1 (ΑΠ-05).
- Χιτώνια πριν τη σκυροδέτηση, αξονικά ±1 cm.
- Τάπα καθαρισμού στη βάση κάθε στήλης.
- Καμία υδρορροή στο υπόγειο ή στον κήπο.

ΥΠΟΜΝΗΜΑ

- στήλη / συλλεκτήρας λυμάτων
- αερισμός
- υδρορροή / κάθοδος
- συλλεκτήρας ομβρίων ψηλά
- χιτώνιο πλάκας

ΕΡΓΟ


ΠΕΝΤΑΟΡΟΦΟ ΚΤΗΡΙΟ ΚΑΤΟΙΚΙΩΝ – ΑΡΓΥΡΟΥΠΟΛΗ
Κωνσταντινουπόλεως 12 & Αγ. Βαρβάρας · Ο.Τ. 103-15
Εργοδότης: INTERKAT Α.Ε. · Κατασκευή: ARKAD Ι.Κ.Ε.

ΘΕΜΑ ΣΧΕΔΙΟΥ

ΚΑΤΑΚΟΡΥΦΟ ΔΙΑΓΡΑΜΜΑ & ΑΝΑΜΟΝΕΣ
Στήλες ΑΠ1–ΑΠ4 · αερισμοί έξω · πτώσεις ισογείου
Υδρορροές ΥΔ1–ΥΔ5 → συλλεκτήρες ψηλά → κάθοδος εισόδου
Βάση: τομή Α-30-ΑΑ (στάθμες) · ΑΠ-02 … ΑΠ-08

ΑΡ. ΣΧΕΔΙΟΥ

ΑΠ-01
Σχηματικό · Α2
27/10/2026 · R12

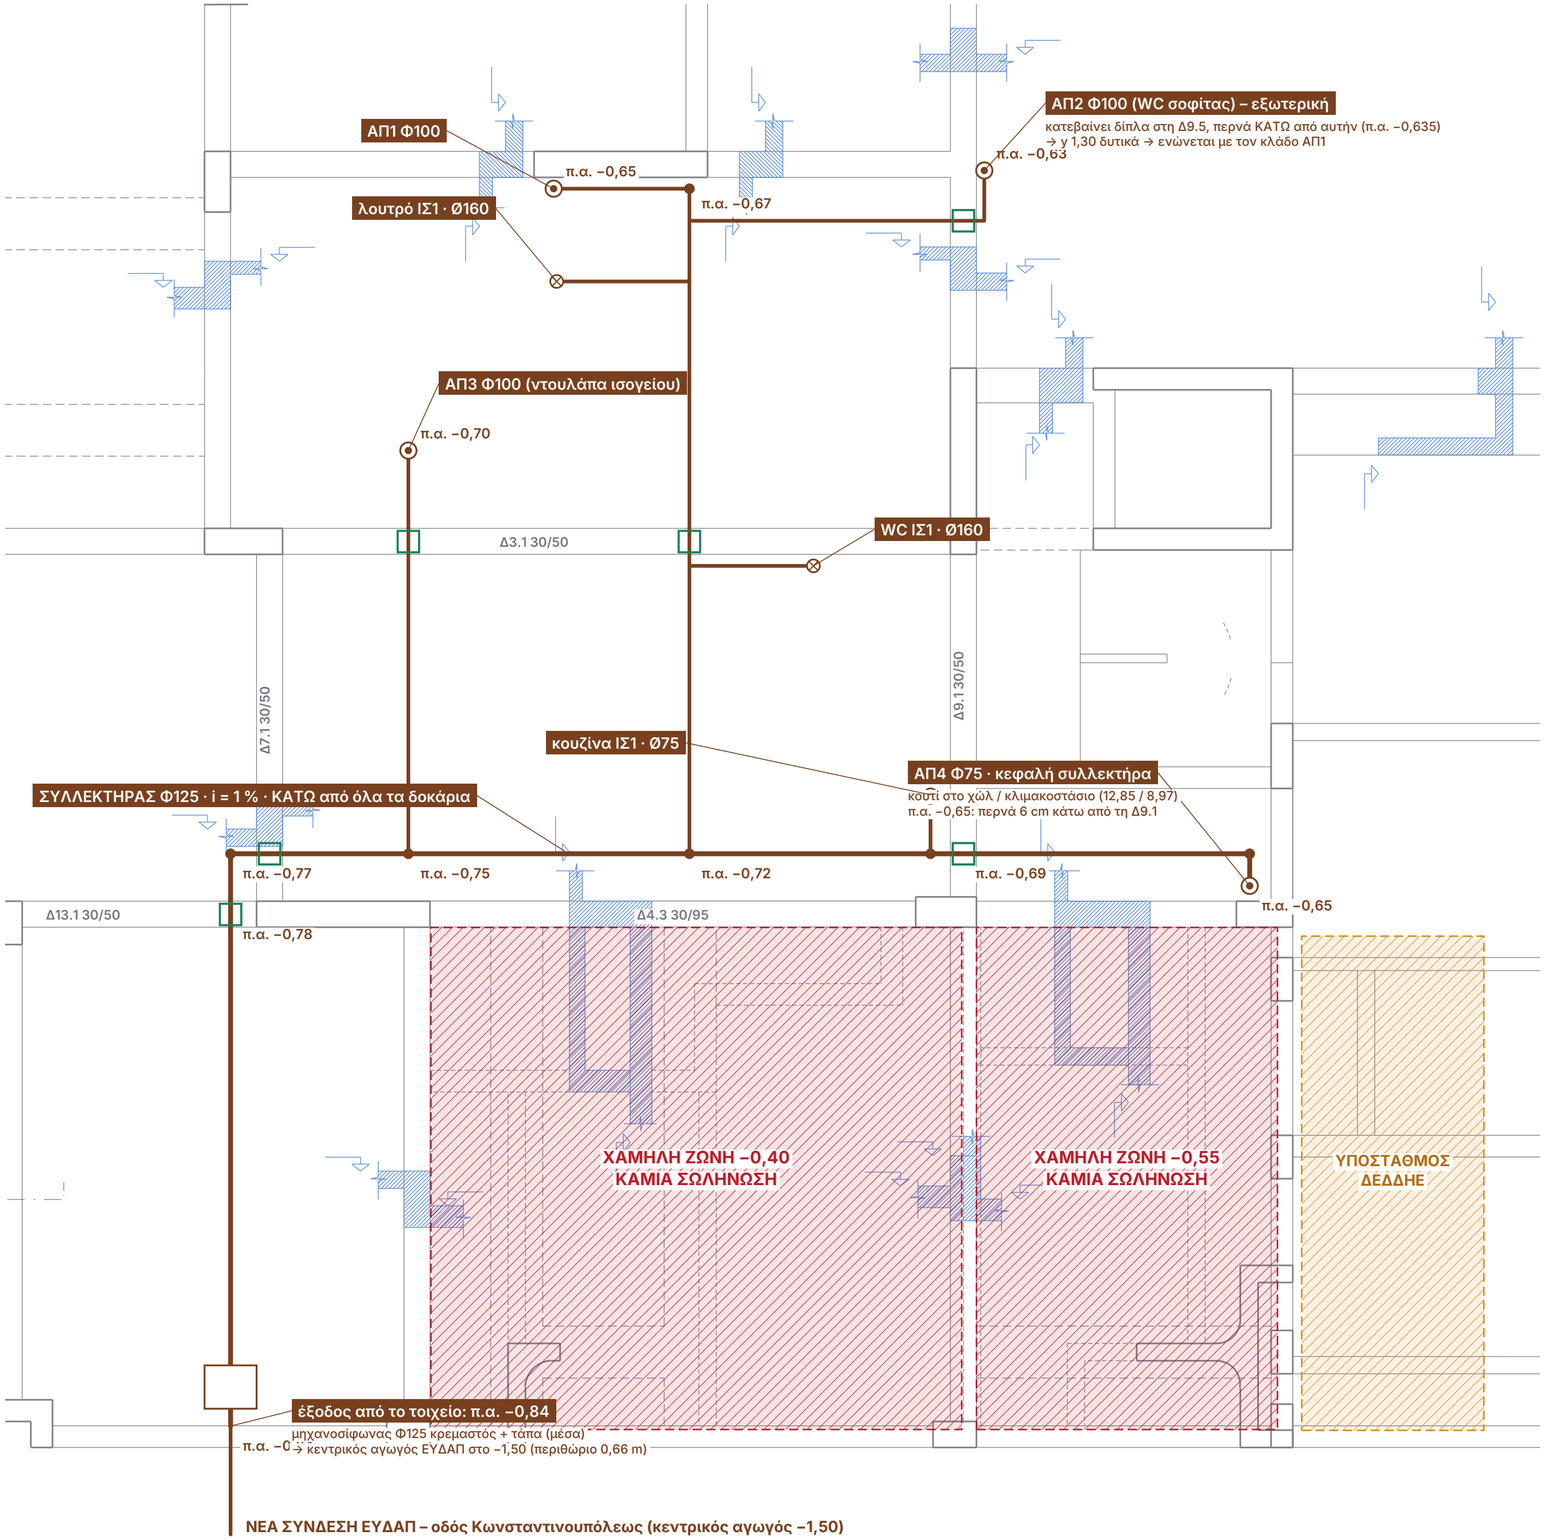

ΟΡΟΦΗ ΥΠΟΓΕΙΟΥ – ΣΥΛΛΕΚΤΗΡΑΣ ΛΥΜΑΤΩΝ

βάση: ξυλότυπος Σ2 εφαρμογής (μόνο φέρων οργανισμός) · 1:50

B

ΚΑΝΟΝΕΣ

- ΚΑΜΙΑ ΔΙΑΤΡΗΣΗ ΔΟΚΟΥ. Ο συλλεκτήρας κρέμεται ΚΑΤΩ από όλα τα δοκάρια (30/50 → κάτω παρειά −0,50). Τίποτα στις χαμηλές ζώνες.
- Κλίση 1 % σε όλο το μήκος (18,7 m από την κεφαλή ΑΠ4 ως το τοιχείο)· μόνο ο κλάδος ΑΠ1 στο x 6,39 έχει 0.7 % (ελάχιστο 0,5 % EN 12056-2).
- Διαδρομή: ΑΠ4 → y 8,60 δυτικά → x 1,10 νότια → τοιχείο ΝΔ → ΕΥΔΑΠ. Κλάδοι: ΑΠ1 + ΑΠ2 (x 6,39), ΑΠ3 (x 3,15), λουτρό/WC/κουζίνα ΙΣ1.
- Γιατί −0,65: κάτω παρειά δοκών −0,50, σωλήνας 12,5 cm, ανοχή 2,5–6 cm.
- Κεντρικός αγωγός ΕΥΔΑΠ: −1,50 από το ±0,00.

ΣΤΑΘΜΕΣ (π.α. = πυθμένας, άνω = πάνω παρειά σωλήνα)

σημείο	π.α.	άνω παρειά	δοκός	περιθώριο
κεφαλή ΑΠ4	**−0,65**	−0,53	—	
κάτω από Δ9.1	**−0,69**	−0,56	−0,50	6 cm
σύνδεση ΑΠ1	**−0,72**	−0,59	—	
κεφαλή ΑΠ2	**−0,63**	−0,52	—	
ΑΠ2 κάτω από Δ9.5	**−0,64**	−0,53	−0,50	3 cm
ΑΠ1 κάτω από Δ3.1	**−0,69**	−0,57	−0,50	7 cm
σύνδεση ΑΠ3	**−0,75**	−0,63	—	
κάτω από Δ7.1	**−0,77**	−0,64	−0,50	14 cm
κάτω από Δ13.1	**−0,78**	−0,65	−0,50	15 cm
ΕΞΟΔΟΣ ΤΟΙΧΕΙΟΥ	**−0,84**	−0,71	—	
αγωγός ΕΥΔΑΠ	**−1,50**		—	

Βγαίνουμε από το τοιχείο με πυθμένα −0,84 → 0,66 m πάνω από τον αγωγό ΕΥΔΑΠ (−1,50).
Καθαρό ύψος κάτω από τον σωλήνα: 2,35 στην αρχή → 2,16 στη ΝΔ γωνία (δάπεδο −3,00).

ΑΝΑΜΟΝΕΣ ΠΛΑΚΑΣ ΟΡΟΦΗΣ ΥΠΟΓΕΙΟΥ

ΑΠ1	4,83 / 0,93	Ø160
ΑΠ2 (εξωτ., δίπλα στη Δ9.5)	9,79 / 0,72	Ø160
ΑΠ3 (μετά τη μετατόπιση)	3,15 / 3,95	Ø160
ΑΠ4 (κουτί χώλ)	12,85 / 8,97	Ø125
λουτρό ΙΣ1 (λεκάνη + ΠΣ-Ι1)	4,86 / 2,00	Ø160
WC ΙΣ1 (λεκάνη + ΠΣ-Ι2)	7,82 / 5,28	Ø160
νεροχύτης κουζίνας ΙΣ1	9,17 / 7,92	Ø75

ΑΝΟΙΚΤΑ

- ΕΥΔΑΠ: επιβεβαίωση βάθους −1,50 και θέσης σύνδεσης ΝΔ.
- Καθαρό ύψος 2,16 στη ΝΔ γωνία – έλεγχος χρήσης χώρου (στάθμευση ≥ 2,20).
- Συντονισμός με αεραγωγούς / καλωδιώσεις κάτω από την οροφή.

0 1 2 3 4 5 m

ΥΠΟΜΝΗΜΑ

- συλλεκτήρας / κλάδοι Φ125
- βάση στήλης
- πτώση από το ισόγειο
- τάπα καθαρισμού
- πέρασμα ΚΑΤΩ από δοκό (πράσινο)
- χαμηλή ζώνη – καμία σωλήνωση

ΕΡΓΟ

ΠΕΝΤΑΟΡΟΦΟ ΚΤΗΡΙΟ ΚΑΤΟΙΚΙΩΝ – ΑΡΓΥΡΟΥΠΟΛΗ
Κωνσταντινουπόλεως 12 & Αγ. Βαρβάρας · Ο.Τ. 103-15
Εργοδότης: INTERKAT Α.Ε. · Κατασκευή: ARKAD Ι.Κ.Ε.

ΘΕΜΑ ΣΧΕΔΙΟΥ

ΟΡΟΦΗ ΥΠΟΓΕΙΟΥ – ΣΥΛΛΕΚΤΗΡΑΣ
Συλλεκτήρας κάτω από τα δοκάρια – χωρίς διατρήσεις · + κλάδος ΑΠ2
Στάθμες πυθμένα · έξοδος −0,84 → ΕΥΔΑΠ −1,50
Βάση: ξυλότυπος οροφής υπογείου Σ2 εφαρμογής · Α-10-Β · τομή Α-30-ΑΑ


ΑΡ. ΣΧΕΔΙΟΥ

ΑΠ-02
Κλίμακα 1:50 · Α2
27/10/2026 · R12


ΑΠ4 (ΚΟΥΖΙΝΕΣ) – ΕΞΩΤΕΡΙΚΗ, ΜΕΣΑ ΣΤΟ ΚΕΝΟ ΤΗΣ ΚΑΜΠΥΛΗΣ ΓΩΝΙΑΣ

θέση 13,35 / 9,69 στους ορόφους · στο ισόγειο μπαίνει σε κουτί στο κλιμακοστάσιο / χώλ · κανένα τρύπημα δοκού


ΤΥΠΙΚΟΣ ΟΡΟΦΟΣ (Β1) · 1:30

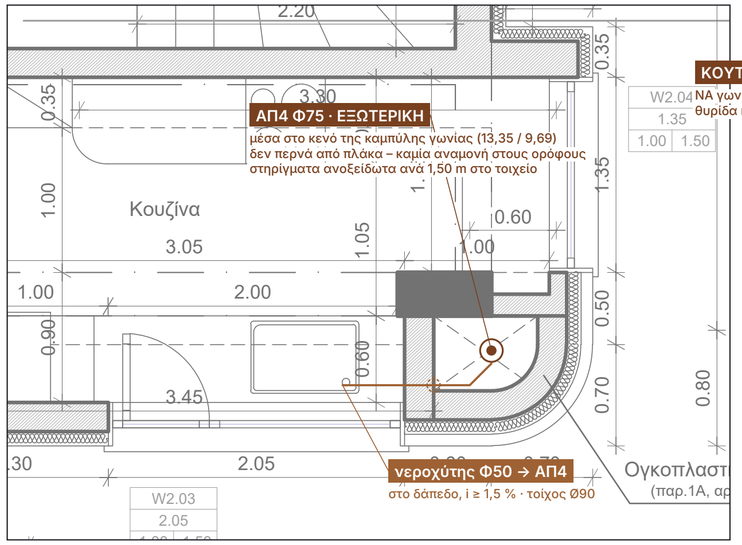


ΙΣΟΓΕΙΟ · 1:30

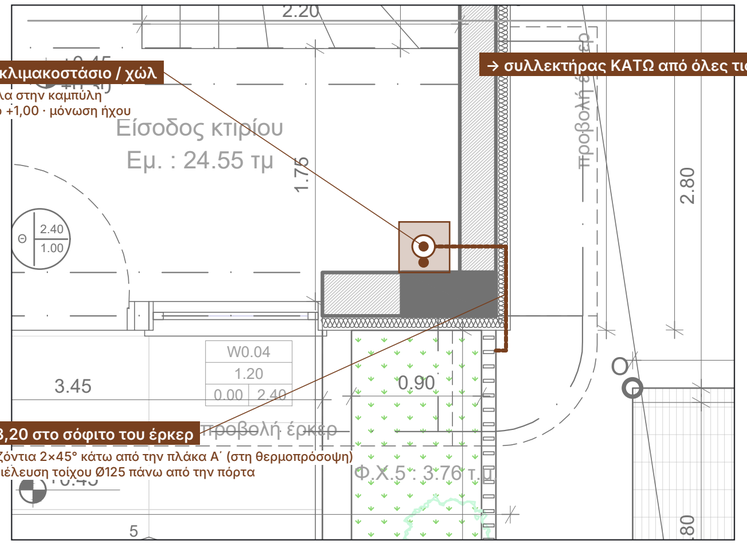

ΟΡΟΦΗ ΥΠΟΓΕΙΟΥ · 1:30

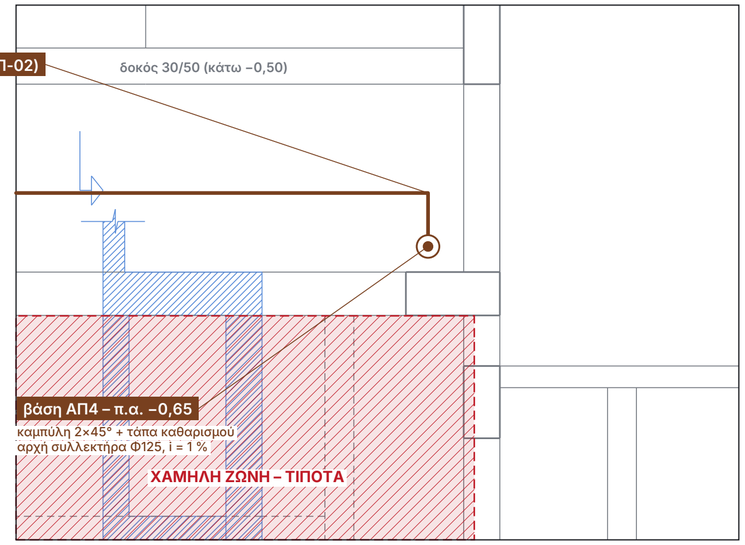

ΣΧΗΜΑΤΙΚΗ ΤΟΜΗ ΤΗΣ ΑΠ4 (όλα τα επίπεδα)

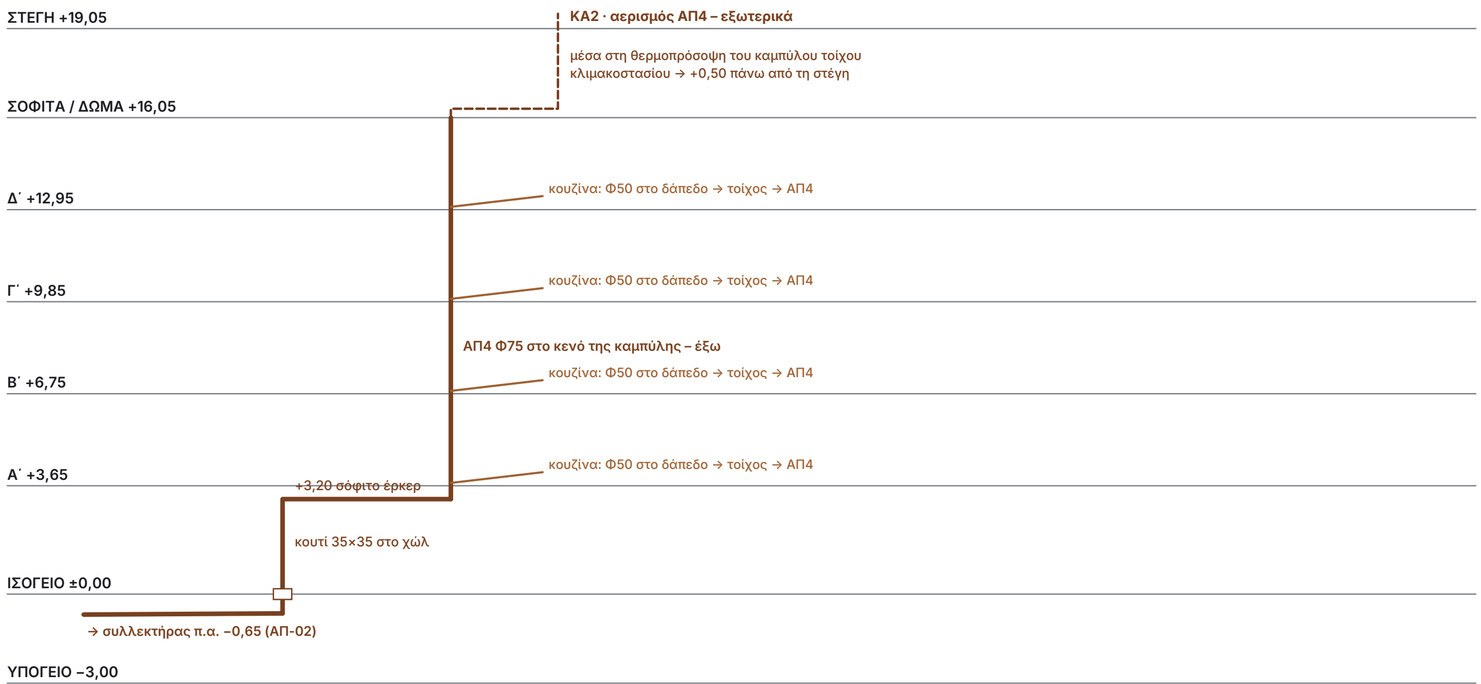

ΛΥΣΗ R11

- Η ΑΠ4 μένει ΕΞΩΤΕΡΙΚΗ, μέσα στο κενό της καμπύλης ΝΑ γωνίας: δεν φαίνεται και δεν περνά από διαμερίσματα.
- Δεν κατεβαίνει στον κήπο ούτε στη χαμηλή ζώνη: στο +3,20 (σόφιτο έρκερ) στρίβει 2×45° και μπαίνει σε ΚΟΥΤΙ 35×35 στη γωνία του κλιμακοστασίου / χώλ.
- Στο υπόγειο πέφτει στη ψηλή ζώνη (12,85 / 8,97) και ξεκινά ο συλλεκτήρας στο π.α. −0,65, ΚΑΤΩ από τις δοκούς – καμία διάτρηση.
- Νεροχύτες: Φ50 μέσα στο δάπεδο → διέλευση τοίχου Ø90 → ΑΠ4 (μικρός κλάδος – επιτρέπεται).
- Αερισμός ΚΑ2: συνεχίζει ως το δώμα, πάει στον καμπύλο τοίχο του κλιμακοστασίου και ανεβαίνει εξωτερικά στη θερμοπρόσοψη – όχι μέσα στη σοφίτα.

Προς έγκριση

- Αρχιτέκτονας: κουτί 35×35 στο χώλ, σόφιτο έρκερ.
- Στατικός: διέλευση τοιχείου Ø125 στο +3,20.
- Εναλλακτικά: μέσα στο «μάτι» της σκάλας (αν προτιμάς).

ΥΠΟΜΝΗΜΑ

- στήλη ΑΠ4 Φ75
- κλάδος νεροχύτη Φ50
- διαδρομή στο σόφιτο +3,20
- αερισμός
- χαμηλή ζώνη

ΕΡΓΟ

ΠΕΝΤΑΟΡΟΦΟ ΚΤΗΡΙΟ ΚΑΤΟΙΚΙΩΝ – ΑΡΓΥΡΟΥΠΟΛΗ
Κωνσταντινουπόλεως 12 & Αγ. Βαρβάρας · Ο.Τ. 103-15
Εργοδότης: INTERKAT Α.Ε. · Κατασκευή: ARKAD Ι.Κ.Ε.

ΘΕΜΑ ΣΧΕΔΙΟΥ

ΑΠ4 – ΕΞΩΤΕΡΙΚΗ ΣΤΗΛΗ ΚΟΥΖΙΝΩΝ
Στο κενό της καμπύλης ΝΑ γωνίας · κουτί στο χώλ ισογείου
Βάση στη ψηλή ζώνη υπογείου · αερισμός ΚΑ2 εξωτερικά
Βάση: Α-10-2F · Α-10-GF · ξυλότυπος Σ2 εφαρμογής · τομή Α-30-ΑΑ

ΑΡ. ΣΧΕΔΙΟΥ

ΑΠ-03
Κλίμακα 1:30 · Α2
27/10/2026 · R12

ΙΣΟΓΕΙΟ – ΑΠΟΧΕΤΕΥΣΗ & ΟΜΒΡΙΑ

κάτοψη ισογείου (A-10-GF) · 1:50

B

ΛΥΜΑΤΑ ΙΣΟΓΕΙΟΥ

- Το ισόγειο ΔΕΝ συνδέεται στις στήλες. Κάθε χώρος έχει μία κατακόρυφη πτώση μέσα από την πλάκα (±0,00) προς τον συλλεκτήρα της οροφής υπογείου (ΑΠ-02).
- Οι μεγάλες σωληνώσεις προς το υπόγειο (λεκάνες, στήλες) πέφτουν ίσια, χωρίς οριζόντια μέσα στο γέμισμα. Οι μικροί κλάδοι (ΠΣ, νιπτήρες, γραμμικό) στο δάπεδο.
- Λεκάνες κρεμαστές με εντοιχισμένο καζανάκι· η λεκάνη πέφτει μέσα στον προτοίχο.
- Πατοσίφωνα σχεδόν κάτω από τις λεκάνες· γραμμικό και νιπτήρες → πατοσίφωνο.

ΣΤΗΛΕΣ ΠΟΥ ΔΙΕΡΧΟΝΤΑΙ ΤΟ ΙΣΟΓΕΙΟ

- ΑΠ1: μέσα στον προτοίχο του λουτρού ΙΣ1 (ίδιος με το πλαίσιο της λεκάνης). Το λουτρό χάνει 20 cm στο πλάτος (1,70 → 1,50) – προς έγκριση αρχιτέκτονα.
- ΑΠ3: στο ισόγειο μετατοπίζεται 0,57 m νότια με 2×45° στην οροφή (+3,25, μικρό σόφιτο 25 cm δίπλα στον τοίχο) και κατεβαίνει μέσα στη ντουλάπα του ισογείου.
- ΑΠ4 (κουζίνες): ΕΞΩΤΕΡΙΚΗ, μέσα στο κενό της καμπύλης ΝΑ γωνίας των ορόφων. Κάτω από τον έρκερ (+3,20) περνά ψηλά στην οροφή του, μπαίνει από τον ανατολικό τοίχο και κατεβαίνει σε κουτί 35×35 στη γωνία χώλ/κλιμακοστασίου → υπόγειο.
- ΑΠ2 ΚΑΤΑΡΓΕΙΤΑΙ: η σοφίτα συνδέεται στην ΑΠ1 (ΑΠ-08).

ΟΜΒΡΙΑ – ΑΠΟ ΨΗΛΑ, ΚΑΘΟΔΟΣ ΣΤΗΝ ΕΙΣΟΔΟ

- ΚΑΝΕΝΑ δίκτυο στον κήπο. Οι ΥΔ1–ΥΔ5 σταματούν στο +3,30 (κάτω από την πλάκα Α΄) και ενώνονται σε δύο οριζόντιους συλλεκτήρες ΨΗΛΑ, κρυμμένους στη μόνωση της οροφής των προβόλων / εξωστών Α΄ ή στη θερμοπρόσοψη του ισογείου (κλίση 0,5 %): ΥΔ1 → βόρεια οροφή → ΥΔ4 → ΥΔ3 → ΥΔ5 → ΥΔ2 (ένας συλλεκτήρας, 31 m, 0,5 %, +3,35 → +3,20). Ο ανατολικός μένει ελεύθερος για την ΑΠ4.
- Κατεβαίνει σε ΜΙΑ κάθοδο Φ110 στον τοίχο δίπλα στην πόρτα εισόδου.
- Από τη βάση της καθόδου μόνο ένα τμήμα Φ125 (5,7 m) μέσα στη ζαρντινιέρα Φ.Χ.4 ως το ρείθρο της Κωνσταντινουπόλεως, δίπλα στην πεζή είσοδο.
- Τάπες καθαρισμού σε κάθε γωνία των συλλεκτήρων (επισκέψιμες από την οροφή).

ΑΝΟΙΚΤΑ

- Αρχιτέκτονας: προτοίχος λουτρού ΙΣ1, σόφιτο ΑΠ3, κουτί ΑΠ4 στο χώλ, πάχος οροφής προβόλων για τους συλλεκτήρες ομβρίων (≥ 15 cm μόνωση/ψευδοροφή).
- Θέση πλυντηρίου ΙΣ1 (δεν φαίνεται στην κάτοψη) → σε πατοσίφωνο.
- Τοπογράφος: στάθμη ρείθρου για την έξοδο.

0 1 2 3 4 5 m

ΥΠΟΜΝΗΜΑ

- στήλη λυμάτων (διέρχεται)
- υδρορροή Φ75 στη θερμοπρόσοψη
- κλάδος Φ50 στο δάπεδο
- κατακόρυφη πτώση μέσα από την πλάκα
- πατοσίφωνο ΠΣ
- γραμμικό σιφώνι ντουζιέρας
- συλλεκτήρας ομβρίων ΨΗΛΑ (+3,30)
- Φ125 κάθοδος → ρείθρο
- φρεάτιο ελέγχου Φ2

ΕΡΓΟ


ΠΕΝΤΑΟΡΟΦΟ ΚΤΗΡΙΟ ΚΑΤΟΙΚΙΩΝ – ΑΡΓΥΡΟΥΠΟΛΗ
Κωνσταντινουπόλεως 12 & Αγ. Βαρβάρας · Ο.Τ. 103-15
Εργοδότης: INTERKAT A.E. · Κατασκευή: ARKAD I.K.E.

ΘΕΜΑ ΣΧΕΔΙΟΥ

ΙΣΟΓΕΙΟ – ΑΠΟΧΕΤΕΥΣΗ & ΟΜΒΡΙΑ
Πτώσεις ισογείου · ΑΠ3 στη ντουλάπα · ΑΠ4 εξωτερική → κουτί χώλ
Υδρορροές ψηλά → κάθοδος στην είσοδο → ρείθρο Κωνσταντινουπόλεως
Βάση: αρχιτεκτονική κάτοψη ισογείου A-10-GF · ξυλότυπος Σ2 · τομή A-30-AA

ΑΡ. ΣΧΕΔΙΟΥ

ΑΠ-04
Κλίμακα 1:50 · A2
27/10/2026 · R12

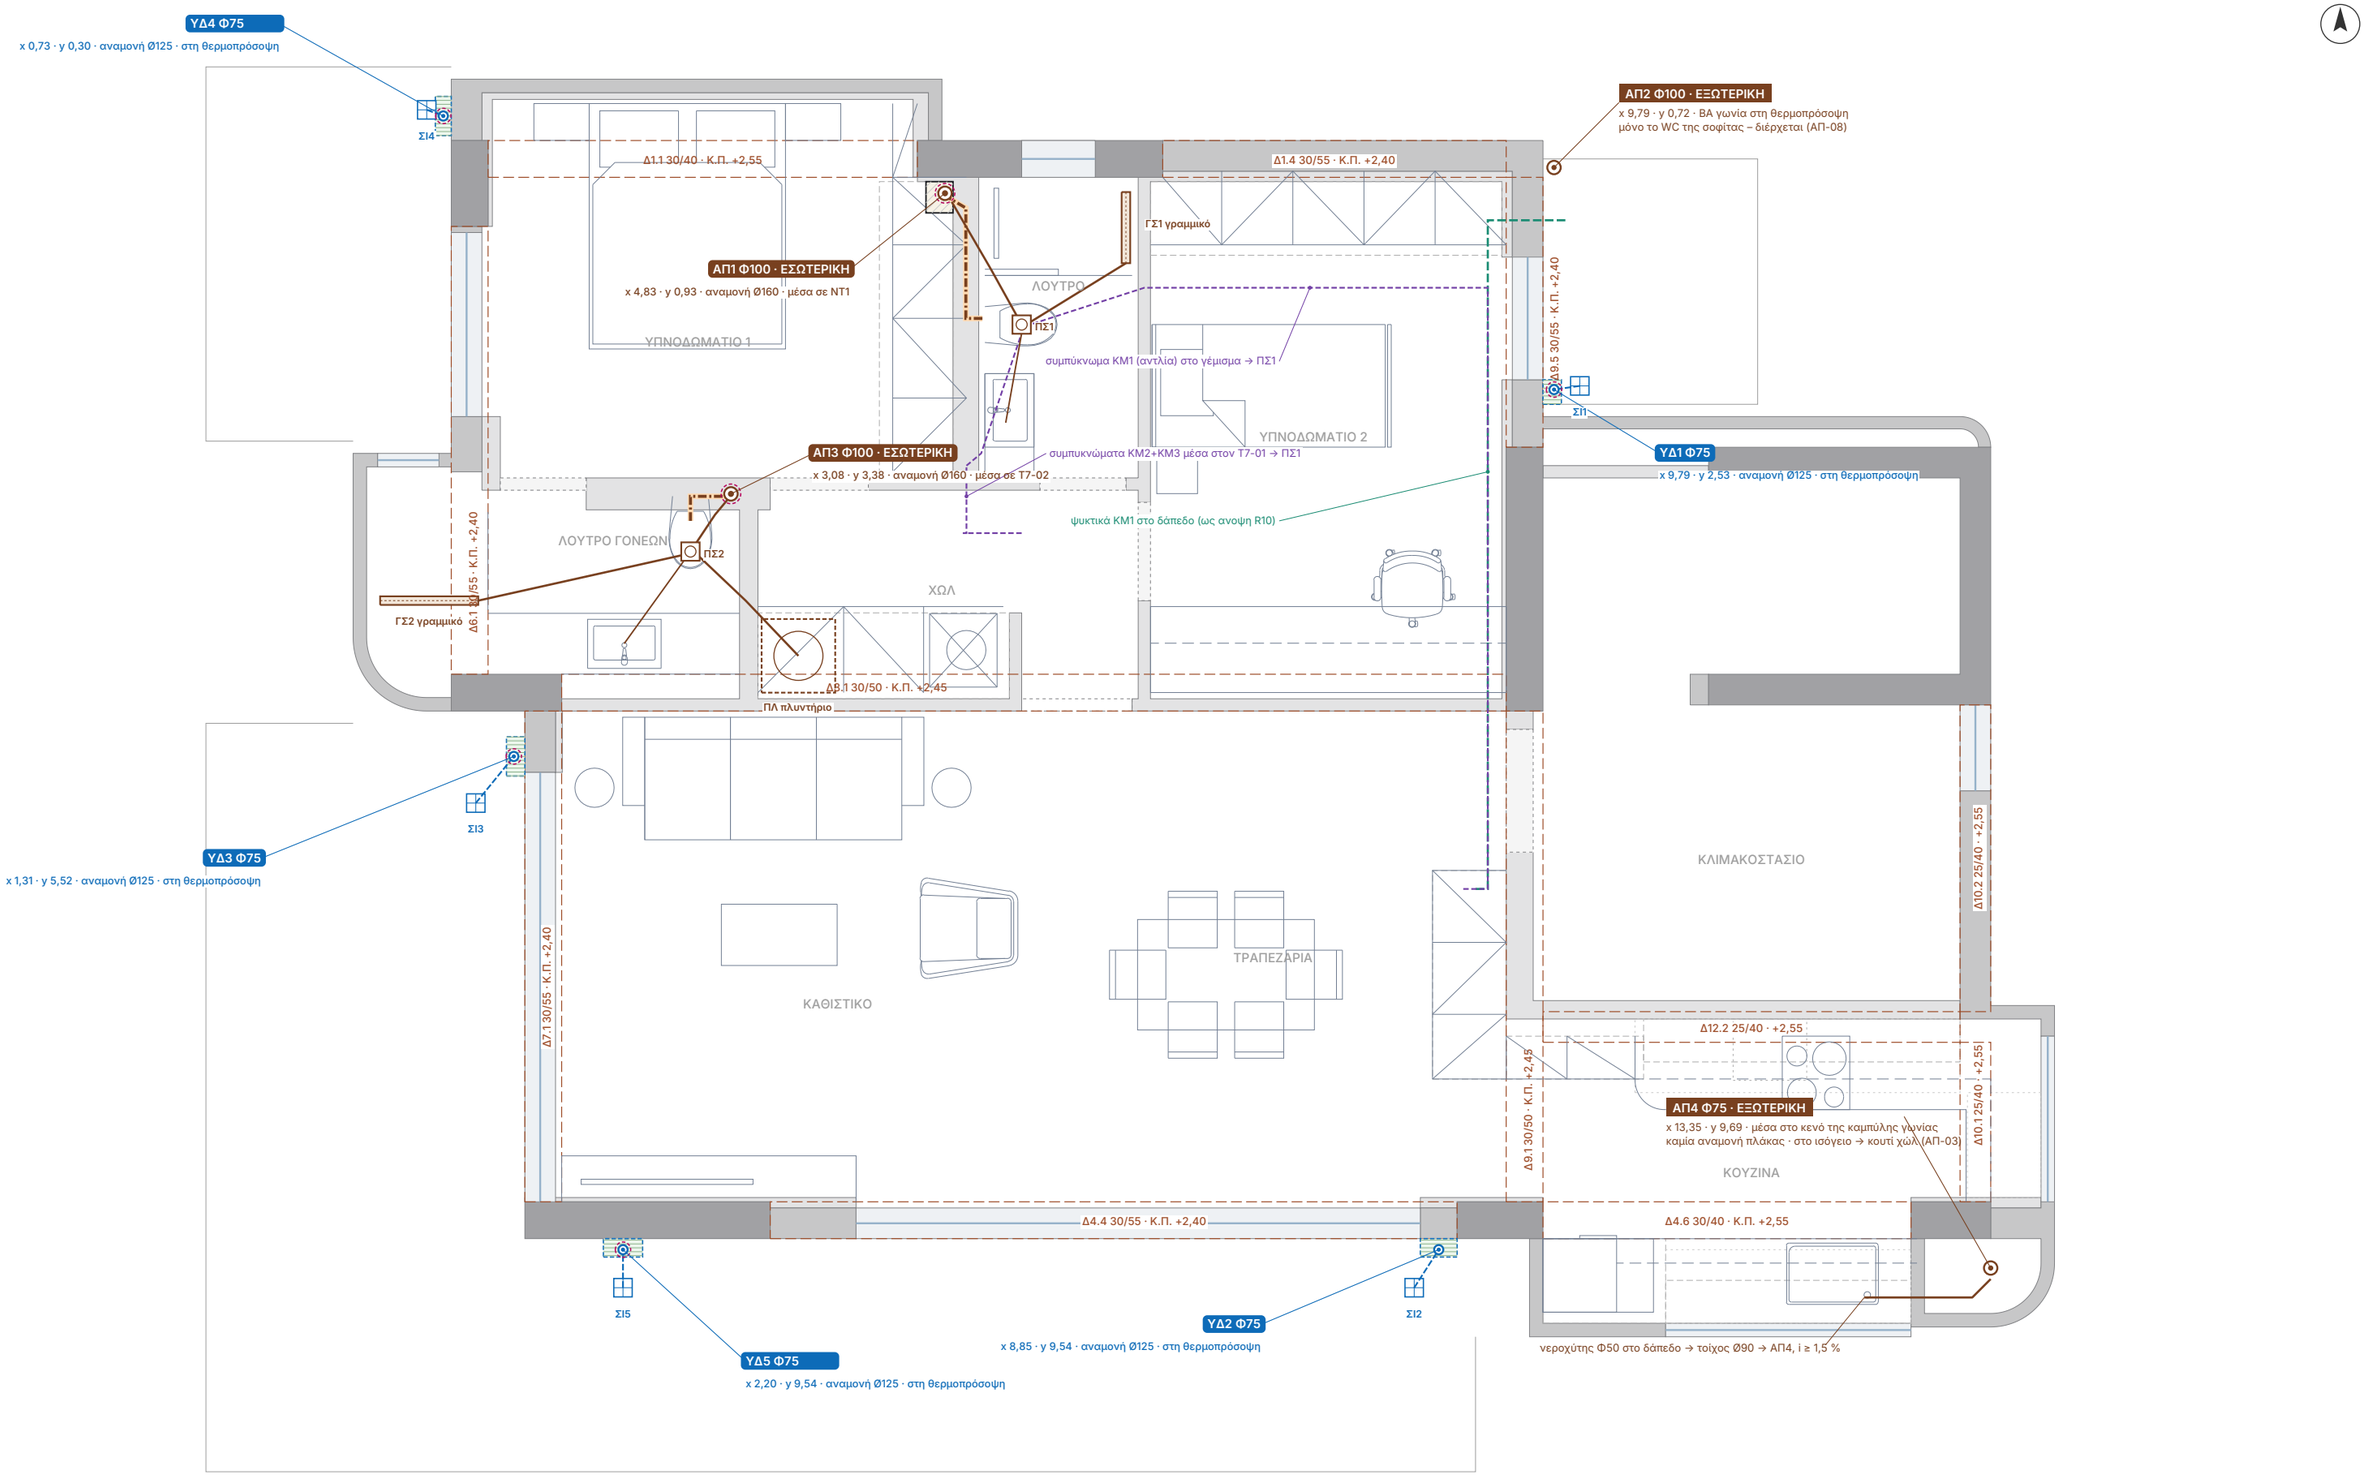

ΥΠΟΜΝΗΜΑ

- στήλη λυμάτων Φ100 (PP Ø110) / κουζίνας Φ75
- υδρορροή Φ75 (PVC Ø75)
- αναμονή πλάκας (σωλ. Ø160 / Ø125)
- γωνία μέσα σε ντουλάπα (γυψοσανίδα)
- τοπική πάχυνση θερμοπρόσοψης (σωλήνας μέσα)
- λεκάνη WC Φ90 ΜΕΣΑ στον τοίχο (+0,22)
- κλάδοι Φ75 / Φ50 / Φ40 (γέμισμα / ντουλάπια)
- γραμμικό σιφώνι ντουζιέρας ΓΣ → ΠΣ
- πατοσίφωνο ΠΣ (γραμμικό + νιπτήρας + A/C)
- συμπυκνώματα A/C → πατοσίφωνα
- ψυκτικά ΚΜ1 στο δάπεδο (ανοψη R10)

ΕΡΓΟ

ΠΕΝΤΑΟΡΟΦΟ ΚΤΗΡΙΟ ΚΑΤΟΙΚΙΩΝ – ΑΡΓΥΡΟΥΠΟΛΗ

Κωνσταντινουπόλεως 12 & Αγ. Βαρβάρας · Ο.Τ. 103-15

Εργοδότης: INTERKAT A.E. · Κατασκευή: ARKAD I.K.E.

ΘΕΜΑ ΣΧΕΔΙΟΥ

ΚΑΤΑΚΟΡΥΦΕΣ ΣΤΗΛΕΣ – ΚΑΤΟΨΗ Β΄ ΟΡΟΦΟΥ

Στήλες, αναμονές, κλάδοι, γραμμικά, πατοσίφωνα, συμπυκνώματα A/C

Βάση: αρχιτεκτονική κάτοψη Β΄ ορόφου Α-10-2F · ξυλότυποι Σ4, Σ5 · τομή Α-30-ΑΑ


ΑΡ. ΣΧΕΔΙΟΥ

ΑΠ-05


Κλίμακα 1:50 · Α3

27/10/2026 · R12


ΑΠ1 · ΛΟΥΤΡΟ / ΝΤΟΥΛΑΠΑ ΥΠΝ.1 (ΝΤ1) · 1:25

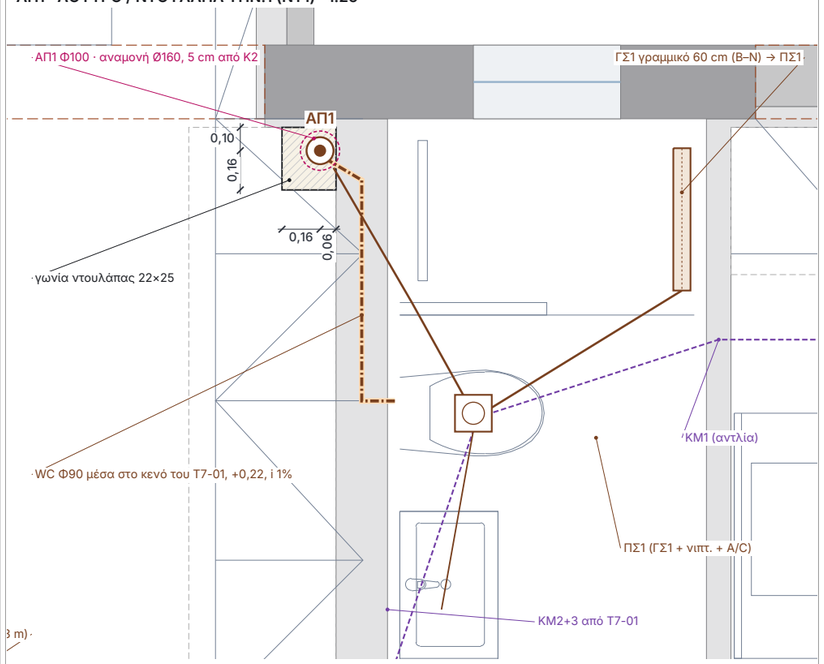


ΑΠ3 · ΛΟΥΤΡΟ ΓΟΝΕΩΝ – ΜΕΣΑ ΣΤΟΝ Τ7-02 · 1:25

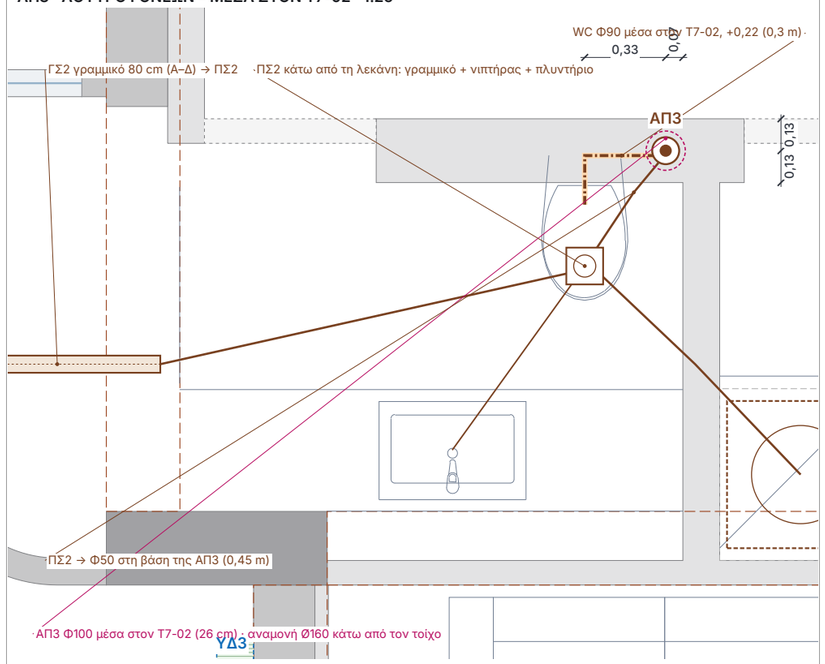


ΛΕΠΤΟΜΕΡΕΙΑ ΑΝΑΜΟΝΗΣ ΠΛΑΚΑΣ · 1:15

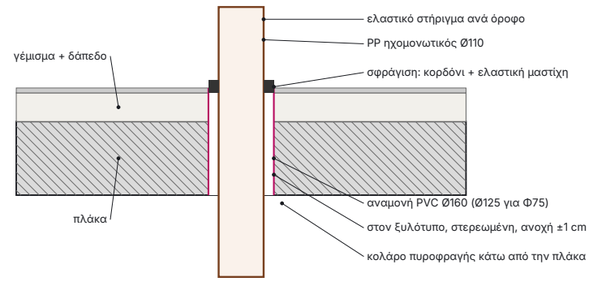


ΛΕΠΤΟΜΕΡΕΙΑ ΥΔΡΟΡΡΟΗΣ ΣΤΗ ΘΕΡΜΟΠΡΟΣΟΨΗ · 1:10 (οριζ. τομή)

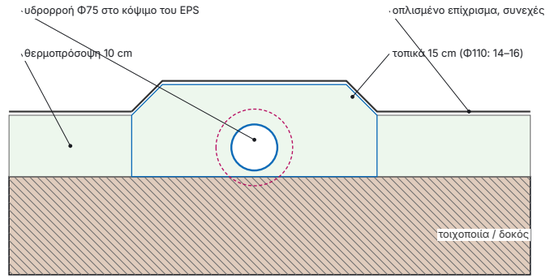

ΥΔ1 · ΒΑ ΕΞΩΣΤΗΣ (ΘΕΡΜΟΠΡΟΣΟΨΗ) · 1:25

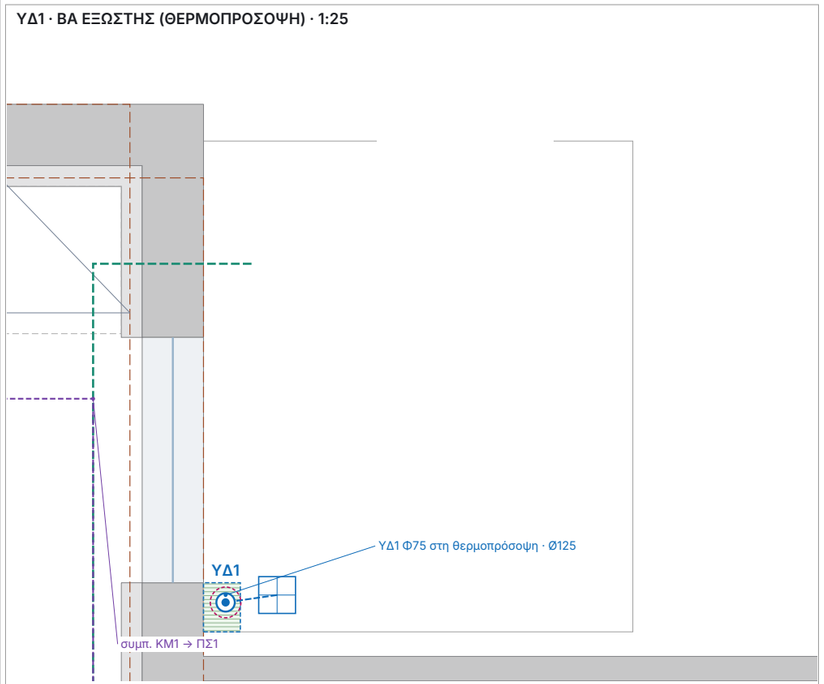

ΥΔ2 · Ν ΕΞΩΣΤΗΣ (ΘΕΡΜΟΠΡΟΣΟΨΗ) · 1:25

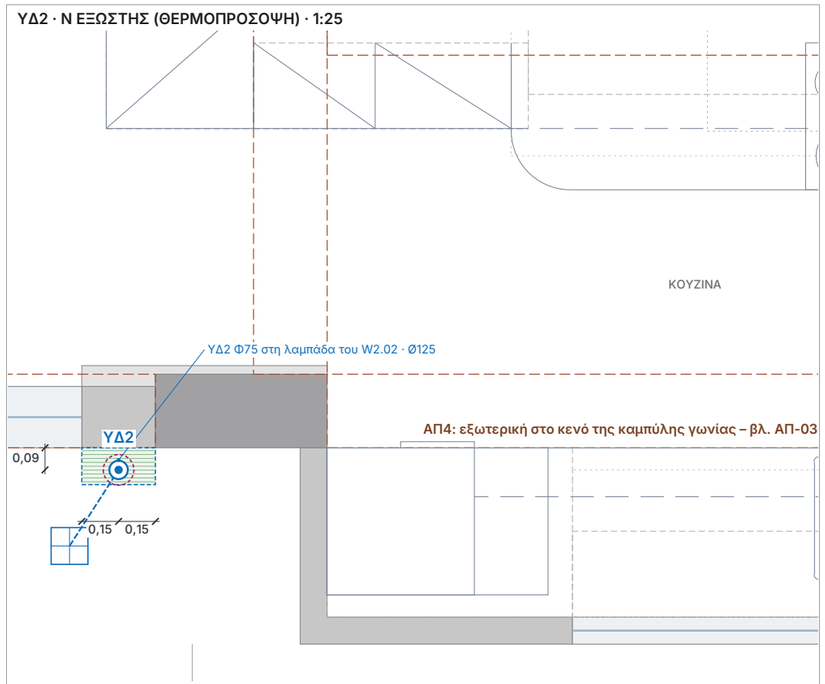


ΓΕΝΙΚΕΣ ΣΗΜΕΙΩΣΕΙΣ


1. Οι αναμονές μπαίνουν σε ΟΛΕΣ τις πλάκες της κατακόρυφης (βλ. ΑΠ-01), στις ίδιες συντεταγμένες – κατακορυφότητα ±1 cm, έλεγχος με νήμα/λέιζερ πριν το μπετόν.
2. Καμία αναμονή μέσα σε δοκό ή υποστύλωμα· απόσταση ≥5 cm από παρειές. Οι νέες θέσεις απαιτούν ΕΓΚΡΙΣΗ ΣΤΑΤΙΚΟΥ (οπές Ø160 σε πλάκες Π3, Π8, Π12).
3. ΑΠ1 στη γωνία της ΝΤ1, ΑΠ3 μέσα στον Τ7-02 (26 cm) – ΚΑΝΕΝΑ κουτί (βλ. ΑΠ-07). PP ηχομονωτικός Ø110, γυψοσανίδα + ορυκτοβάμβακας, κολάρο πυροφραγής ανά πλάκα. Λεκάνες (εντοιχισμένο καζανάκι): Φ90 οριζόντια ΜΕΣΑ στους Τ7-01 / Τ7-02, +0,22, i 1% – ΟΧΙ στο δάπεδο. Πλυντήριο στο δυτικό άκρο της ΝΤ3 → πατοσίφωνο ΠΣ2.
4. ΥΔ1–ΥΔ5 κρυμμένες ΜΕΣΑ στη θερμοπρόσοψη: σωλήνας στο υπόστρωμα, EPS κομμένο από πίσω, τοπική πάχυνση 14–15 cm σε λωρίδα ~0,30 (βλ. λεπτομέρεια).
5. Θυρίδα ελέγχου (καθαρισμού) σε κάθε στήλη στο ισόγειο και τάπα στη βάση (υπόγειο).
6. Αερισμός στηλών πάνω από το δώμα με καπέλο – ύψη/αποστάσεις από ανοίγματα κατά ΤΟΤΕΕ 2412/86 (επιβεβαίωση μηχανολόγου μελετητή).
7. Γραμμικά ΓΣ1/ΓΣ2 (χωρίς σιφώνι) → πατοσίφωνα ΠΣ1/ΠΣ2 μαζί με νιπτήρες και ΟΛΑ τα συμπυκνώματα Α/C (ΚΜ1 με αντλία, ΚΜ2–ΚΜ3 με βαρύτητα) → στήλη με Φ50. Κουζίνες: ΑΠ4 Φ75 εξωτερική στο κενό της καμπύλης (ΑΠ-03). Σιφώνια ΣΙ1–ΣΙ5 → υδρορροές.
8. WC ισογείου: απευθείας κάτω στον συλλέκτήρα της οροφής υπογείου (όχι στήλη).
9. ΥΔ4 (ΒΔ εξώστης) και ΥΔ5 (Ν εξώστης δυτικά) μέσα στη θερμοπρόσοψη.

	ΕΡΓΟ **ΠΕΝΤΑΟΡΟΦΟ ΚΤΗΡΙΟ ΚΑΤΟΙΚΙΩΝ – ΑΡΓΥΡΟΥΠΟΛΗ** Κωνσταντινουπόλεως 12 & Αγ. Βαρβάρας · Ο.Τ. 103-15 Εργοδότης: INTERKAT Α.Ε. · Κατασκευή: ARKAD Ι.Κ.Ε.	ΘΕΜΑ ΣΧΕΔΙΟΥ **ΚΑΤΑΚΟΡΥΦΕΣ ΣΤΗΛΕΣ – ΛΕΠΤΟΜΕΡΕΙΕΣ** Θέσεις 1:25 με αποστάσεις από φέροντα · αναμονή 1:15 · θερμοπρόσοψη 1:10 Βάση: αρχιτεκτονική κάτοψη Β΄ ορόφου Α-10-2F · ξυλότυποι Σ4, Σ5 · τομή Α-30-ΑΑ	ΑΡ. ΣΧΕΔΙΟΥ **ΑΠ-06** Κλίμακα 1:25 / 1:15 / 1:10 · Α3 27/10/2026 · R12


ΛΟΥΤΡΟ + ΝΤΟΥΛΑΠΑ ΥΠΝ.1 · 1:20

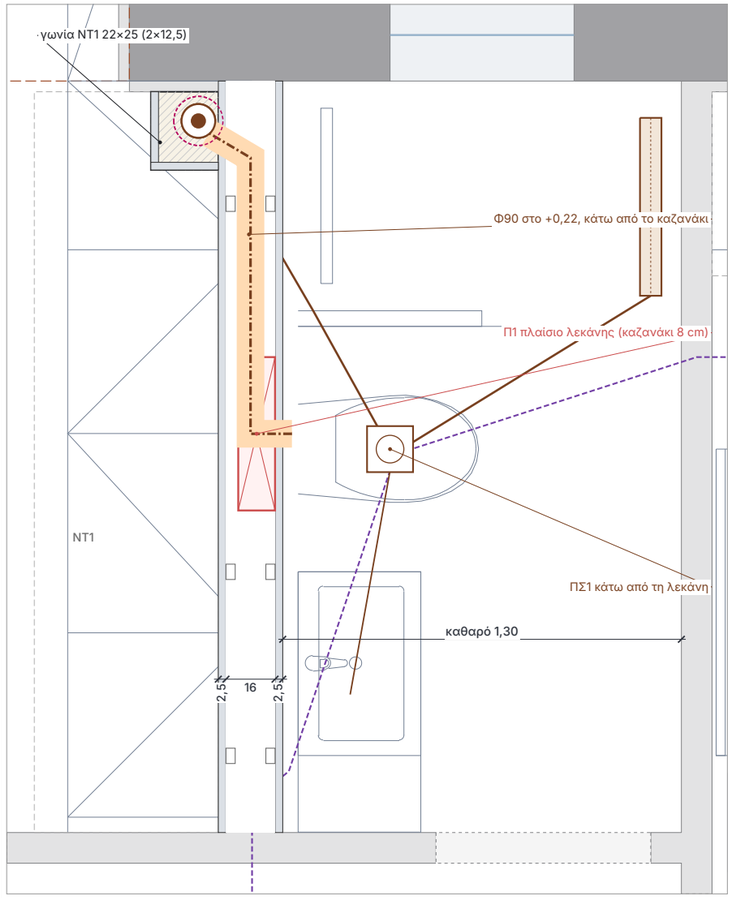


ΛΟΥΤΡΟ ΓΟΝΕΩΝ + ΧΩΛ · 1:20

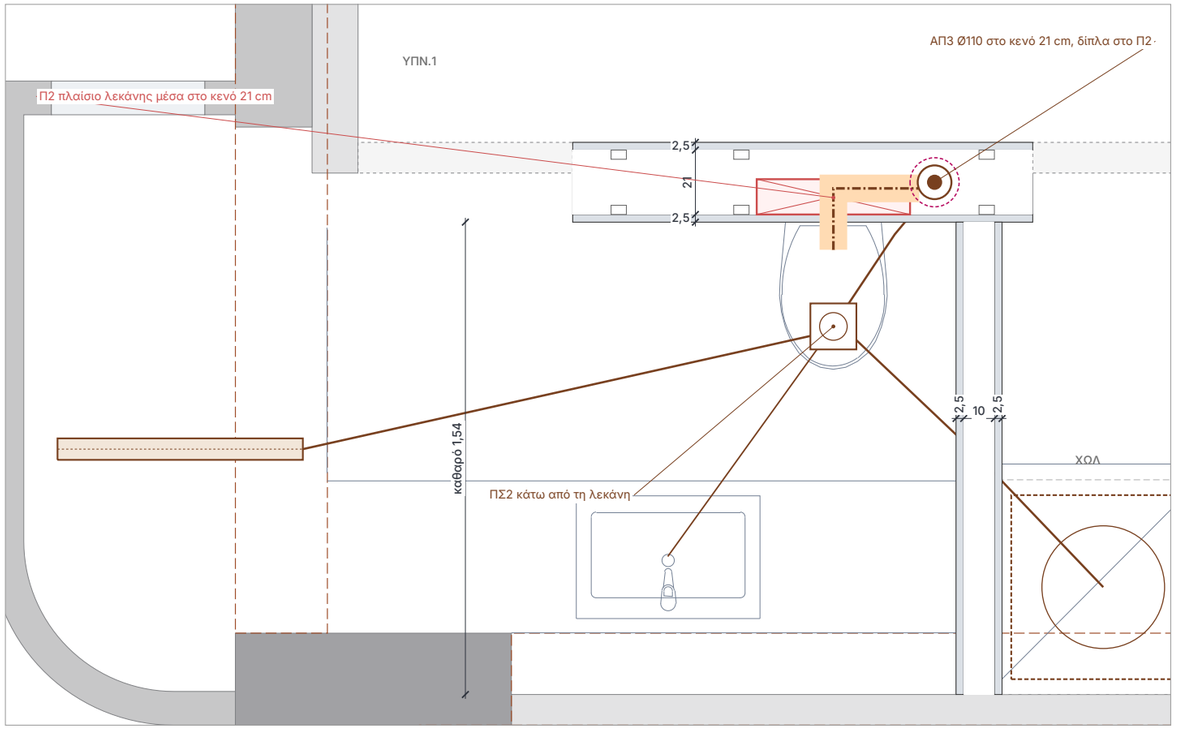

ΤΟΜΗ ΤΟΙΧΟΥ ΛΕΚΑΝΗΣ Τ7-02 ΣΤΗ ΣΤΗΛΗ ΑΠ3 · 1:20

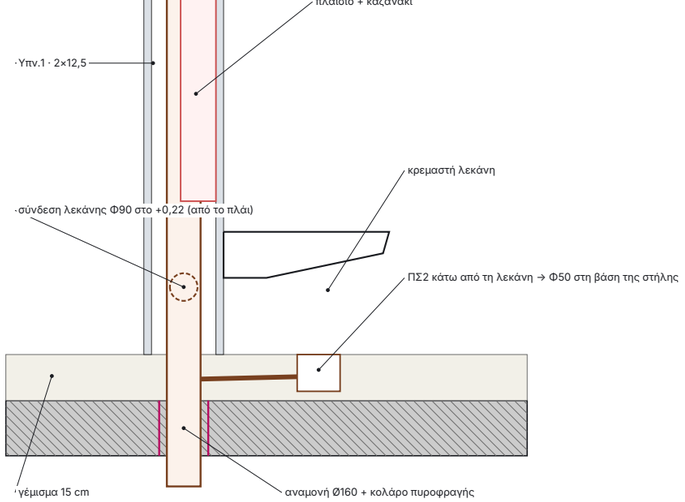


Τ7-01 · ΤΟΙΧΟΣ ΛΕΚΑΝΗΣ ΛΟΥΤΡΟΥ · 21 cm (ως έχει)

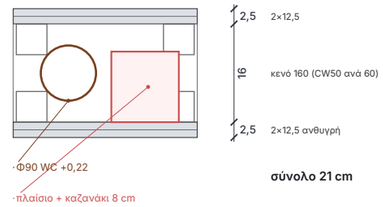


σύνολο 21 cm

Τ7-02 · ΤΟΙΧΟΣ ΛΕΚΑΝΗΣ + ΣΤΗΛΗ ΑΠ3 · 26 cm (νέο)

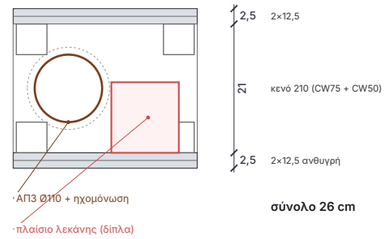


σύνολο 26 cm

Τ2Α-01 · ΛΟΥΤΡΟ ΓΟΝΕΩΝ / ΧΩΛ · 15 cm (ως έχει)

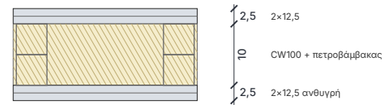

σύνολο 15 cm

ΓΩΝΙΑ ΑΠ1 ΣΤΗ ΝΤΟΥΛΑΠΑ ΝΤ1 · 22×25

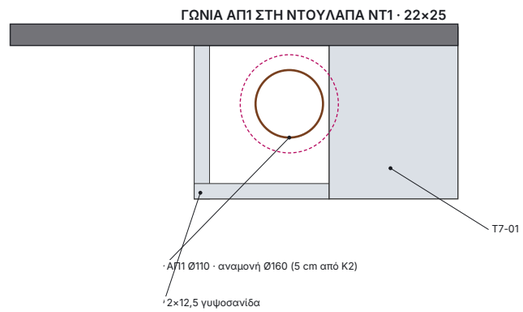

ΚΑΝΟΝΕΣ ΤΟΙΧΩΝ ΕΓΚΑΤΑΣΤΑΣΗΣ

- Τ7-01 μένει 21 cm (κενό 16 cm): χωράει πλαίσιο + καζανάκι 8 cm και Φ90 οριζόντια ΚΑΤΩ από το καζανάκι.
- Τ7-02 γίνεται 26 cm (+5 cm προς το λουτρό, η παρειά Υπν.1 μένει): κενό 21 cm για Ø110 + στηρίγματα + ηχομόνωση. Η ΑΠ3 μπαίνει ΔΙΠΛΑ στο πλαίσιο (x 3,08), ποτέ πίσω του. Λουτρό γονέων καθαρό 1,54 (μπροστά από λεκάνη 1,00).
- Τ2Α-01 μένει 15 cm – δεν περνά κανένας σωλήνας μέσα του. Πόρτες Θ1, Θ3 χωρίς αλλαγή. Χωλ χωρίς κουτί.
- Πατοσίφωνα ΠΣ1/ΠΣ2 κάτω από τις κρεμαστές λεκάνες: γραμμικό + νιπτήρας (+ πλυντήριο / A/C) → Φ50 → στήλη.
- Τα πλαίσια, οι στήλες και οι αναμονές μπαίνουν ΠΡΙΝ το γέμισμα· ο σκελετός κλείνει μετά τη δοκιμή στεγανότητας.

	ΕΡΓΟ **ΠΕΝΤΑΟΡΟΦΟ ΚΤΗΡΙΟ ΚΑΤΟΙΚΙΩΝ – ΑΡΓΥΡΟΥΠΟΛΗ** Κωνσταντινουπόλεως 12 & Αγ. Βαρβάρας · Ο.Τ. 103-15 Εργοδότης: INTERKAT Α.Ε. · Κατασκευή: ARKAD Ι.Κ.Ε.	ΘΕΜΑ ΣΧΕΔΙΟΥ **ΤΟΙΧΟΙ ΕΓΚΑΤΑΣΤΑΣΗΣ ΛΟΥΤΡΩΝ** Πάχη & στρώσεις, πλαίσια λεκανών, στήλες μέσα στους τοίχους, πατοσίφωνα Βάση: αρχιτεκτονική κάτοψη Β΄ ορόφου Α-10-2F · ξυλότυποι Σ4, Σ5 · τομή Α-30-ΑΑ	ΑΡ. ΣΧΕΔΙΟΥ **ΑΠ-07** Κλίμακα 1:20 / 1:15 / 1:10 · Α3 27/10/2026 · R12

ΣΟΦΙΤΑ – ΑΠΟΧΕΤΕΥΣΗ & ΑΕΡΙΣΜΟΙ

κάτοψη σοφίτας (A-10-S) · 1:40 · R12

B

ΑΠΟΧΕΤΕΥΣΗ

- ΛΟΥΤΡΟ + KITCHENETTE → ΑΠ1 (στη βόρεια ντουλάπα). Λεκάνη Φ90 στον βόρειο προτοίχο 18 cm (ντουλάπα 0,65 → 0,47). Γραμμικό + νιπτήρας → ΠΣ-Σ1 → Φ75 στο δάπεδο → ΑΠ1.
- WC → ΑΠ2 Φ100 ΕΞΩΤΕΡΙΚΗ, στη ΒΑ γωνία μέσα στη θερμοπρόσοψη. Λεκάνη Φ90 μέσα στον βόρειο τοίχο του WC και στον ανατολικό τοίχο (κάτω από τα ψηλά παράθυρα) – 2,6 m, χωρίς δάπεδο. Νιπτήρας → ΠΣ-Σ2 → Φ50 → ίδιος σωλήνας.
- Κανένας σωλήνας λεκάνης στο δάπεδο. Κανένα κουτί.

ΑΕΡΙΣΜΟΙ – ΟΛΟΙ ΕΞΩ, ΚΑΝΕΝΑΣ ΣΕ ΟΡΟΦΗ

- ΑΠ1 → ΚΑ1: ανεβαίνει στη ντουλάπα ως +1,10, βγαίνει από τον βόρειο τοίχο δυτικά του Κ2 → θερμοπρόσοψη → +0,50 από τη στέγη.
- ΑΠ2: είναι ήδη έξω – συνεχίζει ίσια πάνω ως τη στέγη.
- ΑΠ3 → ΚΑ3: στον Δ΄ μέσα στον τοίχο Τ7-02 (0,6 m), περνά την πλάκα μέσα στον δυτικό τοίχο της σοφίτας → θερμοπρόσοψη → στέγη.
- ΑΠ4 → ΚΑ2: από το κενό της καμπύλης → τοίχος κλιμακοστασίου.
- Κάθε αερισμός: πρώτα κατακόρυφα πάνω από τα είδη, μετά έξω.

ΟΜΒΡΙΑ

- ΥΔ2–ΥΔ5 από σιφώνια δωμάτων +16,05 · ΥΔ1 από τη στέγη. Κάτω στο ισόγειο: συλλεκτήρας ψηλά → κάθοδος στην είσοδο.

0 1 2 3 4 5 m

ΥΠΟΜΝΗΜΑ

- στήλη
- λεκάνη Φ90 μέσα σε τοίχο
- Φ75 στο δάπεδο
- κλάδος Φ50 στο δάπεδο
- αερισμός → έξω
- πατοσίφωνο ΠΣ
- γραμμικό σιφώνι
- σιφώνι δώματος
- υδρορροή στέγης

ΕΡΓΟ

ΠΕΝΤΑΟΡΟΦΟ ΚΤΗΡΙΟ ΚΑΤΟΙΚΙΩΝ – ΑΡΓΥΡΟΥΠΟΛΗ
Κωνσταντινουπόλεως 12 & Αγ. Βαρβάρας · Ο.Τ. 103-15
Εργοδότης: INTERKAT Α.Ε. · Κατασκευή: ARKAD Ι.Κ.Ε.

ΘΕΜΑ ΣΧΕΔΙΟΥ

ΣΟΦΙΤΑ – ΑΠΟΧΕΤΕΥΣΗ & ΑΕΡΙΣΜΟΙ
Λουτρό → ΑΠ1 · WC → ΑΠ2 εξωτερική
Όλοι οι αερισμοί έξω από τοίχους – ΚΑ1 / ΑΠ2 / ΚΑ2 / ΚΑ3

Βάση: αρχιτεκτονική κάτοψη σοφίτας A-10-S · κάτοψη δώματος A-10-R

ΑΡ. ΣΧΕΔΙΟΥ

ΑΠ-08

Κλίμακα 1:40 · A2
27/10/2026 · R12

ΠΑΡΑΤΗΡΗΣΕΙΣ ΠΡΟΣ ΑΠΑΝΤΗΣΗ – R12

απάντησε με τον αριθμό (π.χ. «1 ΟΚ, 4 κουτί, 6 κρατάμε»)

No	ΘΕΜΑ	ΠΡΟΤΑΣΗ R12	ΦΥΛΛΟ	ΕΡΩΤΗΣΗ
1	**WC σοφίτας – δική του αποχέτευση**	ΑΠ2 Φ100 εξωτερική στη ΒΑ γωνία (θερμοπρόσοψη), μόνο για το WC σοφίτας. Λεκάνη Φ90 στον βόρειο + ανατολικό τοίχο του WC (2,6 m), όχι δάπεδο.	ΑΠ-08/01	ΟΚ η ΑΠ2 ή μύλος WC (Φ32) → ΑΠ1;
2	**ΑΠ2 στο ισόγειο / υπόγειο**	Κατεβαίνει στη ΒΑ γωνία, περνά κατακόρυφα το γέμισμα +0,30, πλάκα δίπλα στη Δ9.5, κάτω από τη Δ9.5 (2,5 cm) → y 1,30 → κλάδος ΑΠ1 (0,7 %).	ΑΠ-02/04	ΟΚ η θυρίδα στη γωνία της βεράντας;
3	**Αερισμός ΑΠ1 (ΚΑ1)**	Ανεβαίνει στη ντουλάπα ως +1,10, βγαίνει από τον βόρειο τοίχο της σοφίτας δυτικά του Κ2 → πάνω στη θερμοπρόσοψη → +0,50 από τη στέγη.	ΑΠ-08	Δεκτό να φαίνεται στη βόρεια όψη;
4	**Αερισμός ΑΠ3 (ΚΑ3)**	Στον Δ΄ οριζόντια 0,6 m ΜΕΣΑ στον τοίχο Τ7-02 (όχι οροφή) → πλάκα μέσα στον δυτικό τοίχο της σοφίτας → έξω στη θερμοπρόσοψη → στέγη.	ΑΠ-08	ΟΚ ή κουτί 12×12 στη σοφίτα;
5	**Αερισμός ΑΠ4 (ΚΑ2)**	Από το κενό της καμπύλης, 1,8 m πάνω στο δώμα του έρκερ → καμπύλος τοίχος κλιμακοστασίου → θερμοπρόσοψη → στέγη.	ΑΠ-03/08	ΟΚ ο σωλήνας 1,8 m στο δώμα;
6	**Γιατί −0,65 στο υπόγειο**	Δοκοί 30/50 → κάτω −0,50 · σωλήνας 12,5 cm · ανοχή → −0,65 στην αρχή. Στο −0,61 κερδίζουμε 4 cm (2,20 στη ΝΔ γωνία) αλλά μένουν 2 cm και δεν χωρά η ΑΠ2.	ΑΠ-02	Κρατάμε −0,65;
7	**Ύψος στη ΝΔ γωνία υπογείου**	2,35 → 2,16 κάτω από τον συλλεκτήρα στη ΝΔ γωνία.	ΑΠ-02	Υπάρχει θέση στάθμευσης εκεί;
8	**Σύνδεση ΕΥΔΑΠ**	Έξοδος τοιχείου ΝΔ π.α. −0,84 → κεντρικός −1,50 (περιθώριο 0,66 m).	ΑΠ-02	Επιβεβαιωμένο το −1,50 / θέση;
9	**ΑΠ4 στο ισόγειο**	Στο +3,20 (σόφιτο έρκερ) 2×45° → κουτί 35×35 στη ΝΑ γωνία χώλ / κλιμακοστασίου.	ΑΠ-03/04	Σωστά κατάλαβα την «τρύπα στην καμπύλη»;
10	**ΑΠ3 στο ισόγειο**	2×45° στην οροφή του ισογείου (σόφιτο 25 cm) → ντουλάπα ισογείου 3,15 / 3,95.	ΑΠ-04	ΟΚ το σόφιτο 25 cm;
11	**Υδρορροές**	Ένας συλλεκτήρας ψηλά +3,30 στην οροφή των προβόλων Α΄ → μία κάθοδος στην είσοδο.	ΑΠ-04	—
12	**Όροφοι Α΄, Γ΄, Δ΄**	Ίδιοι με το Β1 (ίδιοι τοίχοι εγκατάστασης / ντουλάπες).	ΑΠ-05	Είναι ίδιοι;

ΕΡΓΟ

ΠΕΝΤΑΟΡΟΦΟ ΚΤΗΡΙΟ ΚΑΤΟΙΚΙΩΝ – ΑΡΓΥΡΟΥΠΟΛΗ
Κωνσταντινουπόλεως 12 & Αγ. Βαρβάρας · Ο.Τ. 103-15
Εργοδότης: INTERKAT Α.Ε. · Κατασκευή: ARKAD Ι.Κ.Ε.

ΘΕΜΑ ΣΧΕΔΙΟΥ

ΠΑΡΑΤΗΡΗΣΕΙΣ – ΑΝΟΙΚΤΑ
Αριθμημένες παρατηρήσεις προς απάντηση
Ίδια αρίθμηση με το μήνυμα

Βάση: ΑΠ-01 … ΑΠ-08 R12

ΑΡ. ΣΧΕΔΙΟΥ

ΑΠ-09
— · A2
27/10/2026 · R12