
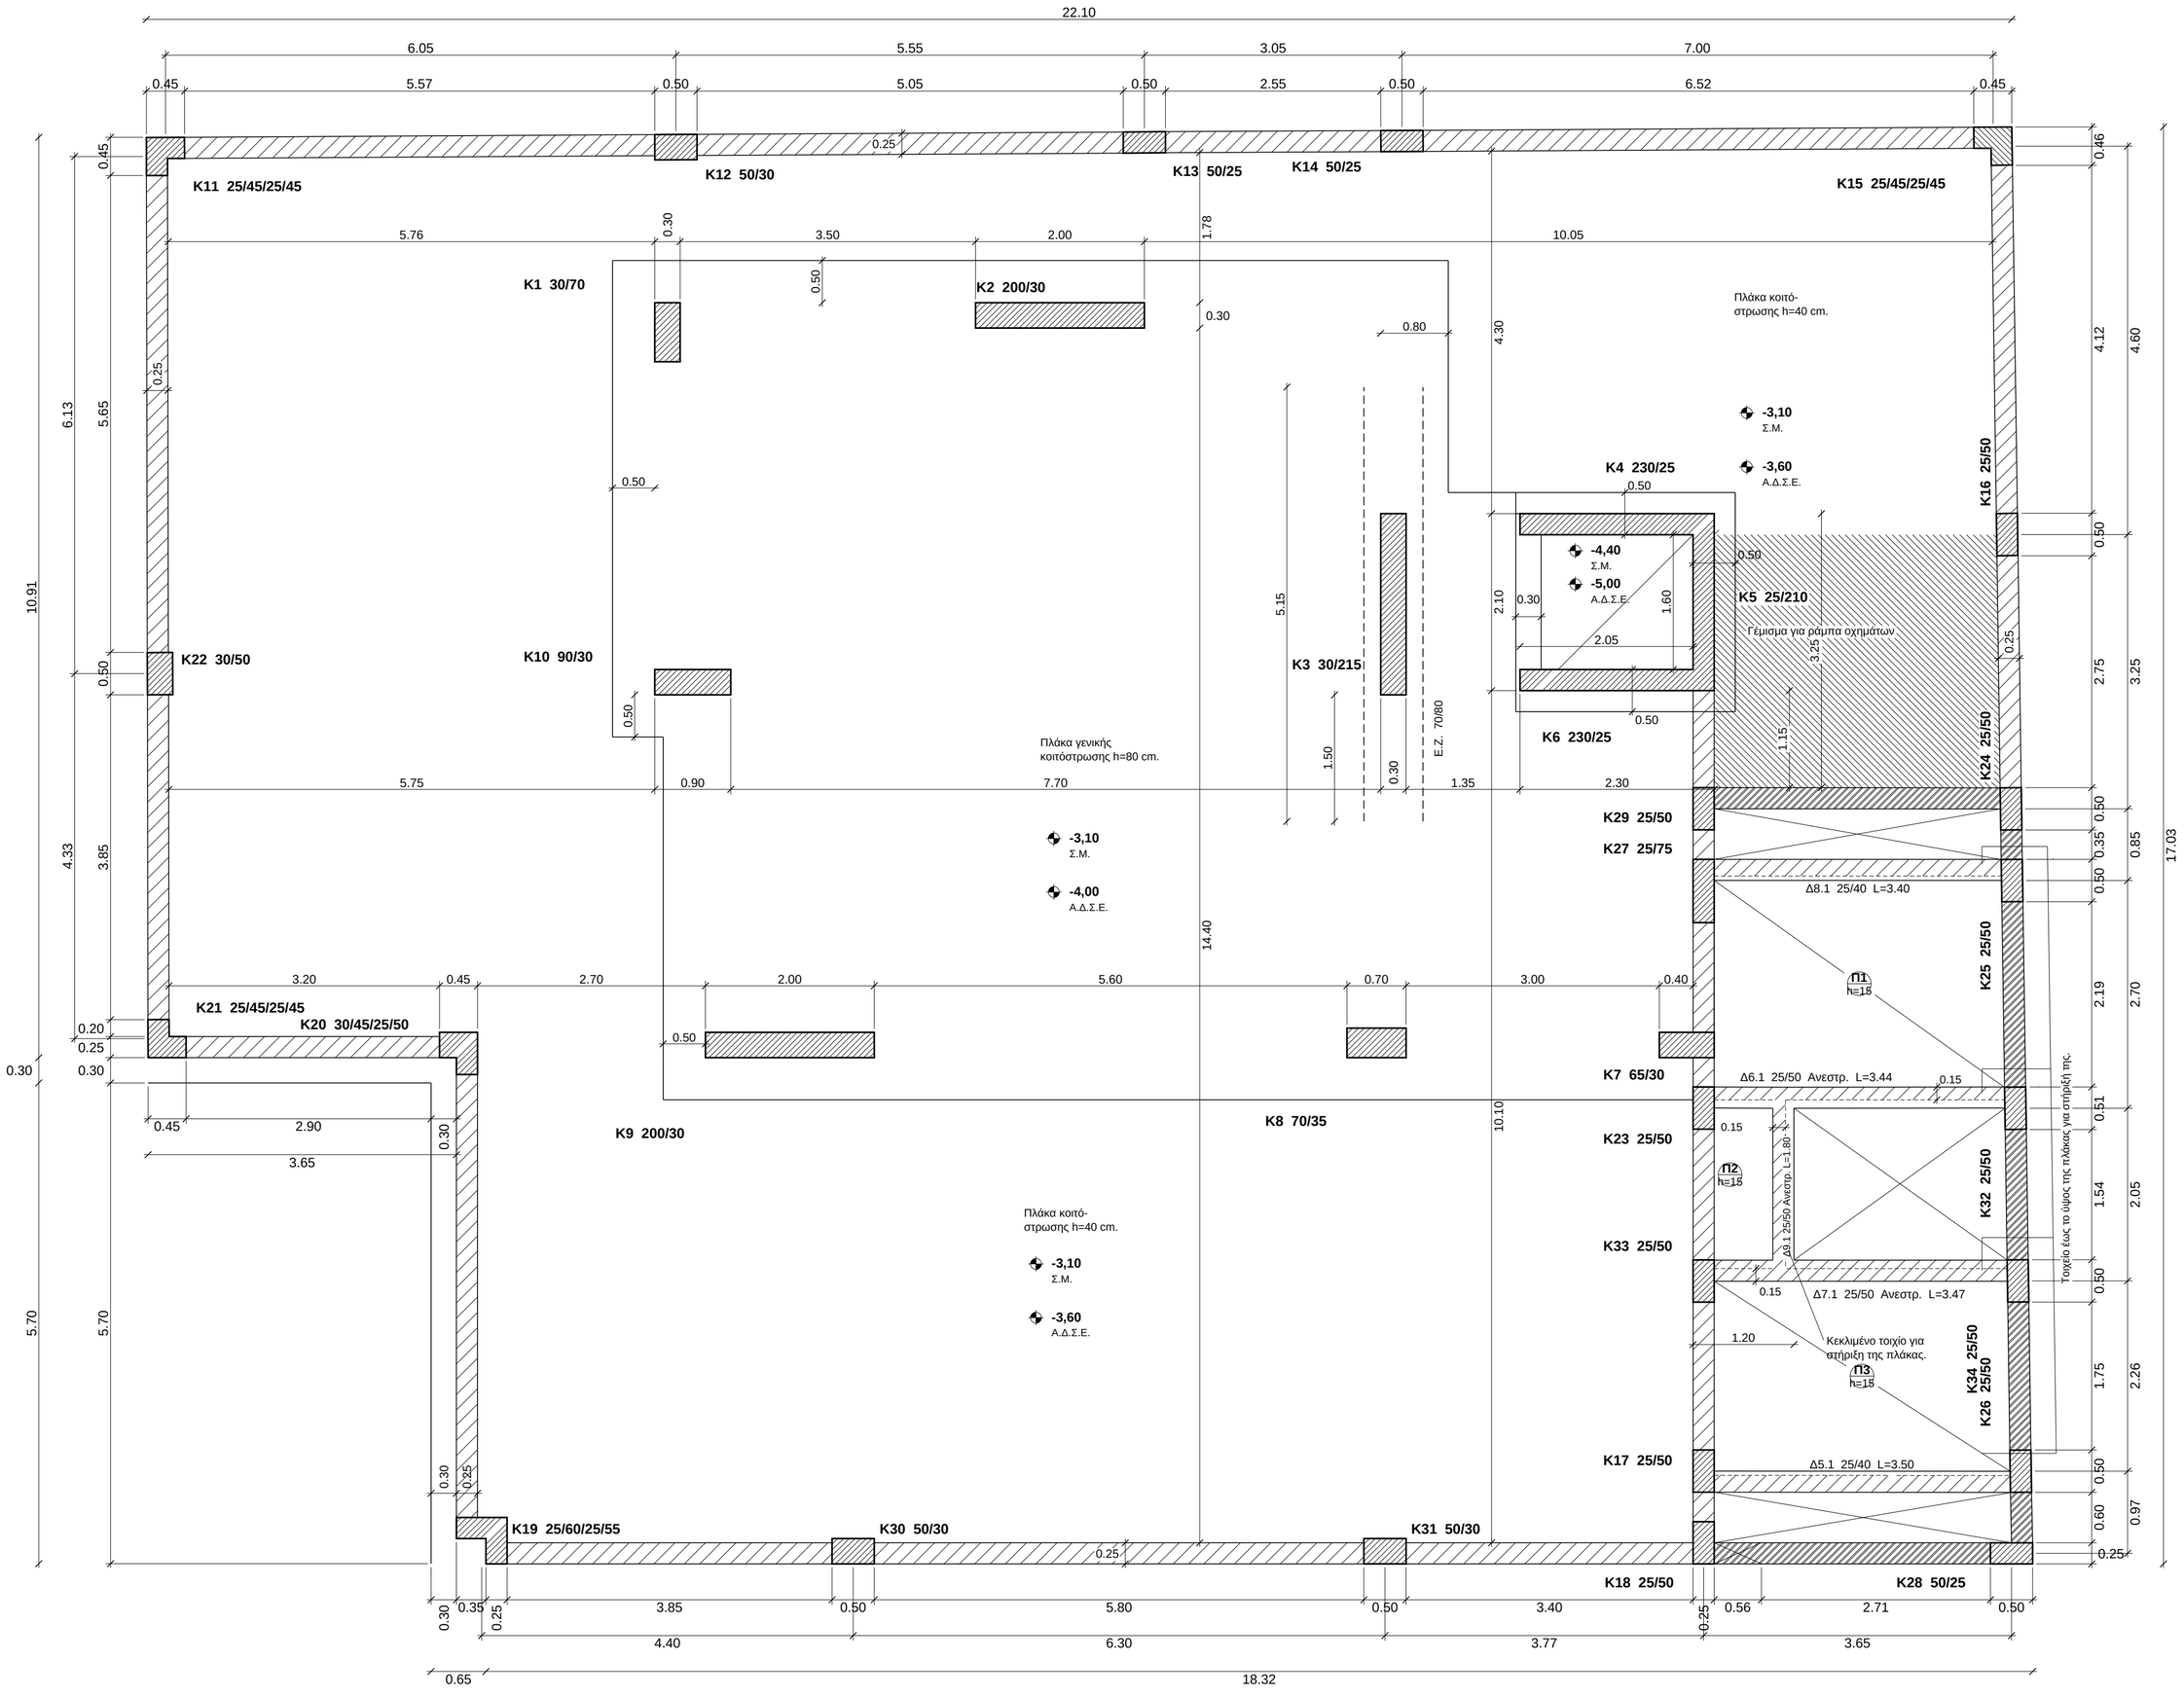


ΞΥΛΟΤΥΠΟΣ ΘΕΜΕΛΙΩΣΗΣ (-4,00 / -3,60)

ΚΛΙΜΑΚΑ 1:50 (Α2)

0 1 2 m

ΚΩΝΣΤΑΝΤΙΝΟΥΠΟΛΕΩΣ 12 &
ΑΓΙΑΣ ΒΑΡΒΑΡΑΣ, ΑΡΓΥΡΟΥΠΟΛΗ

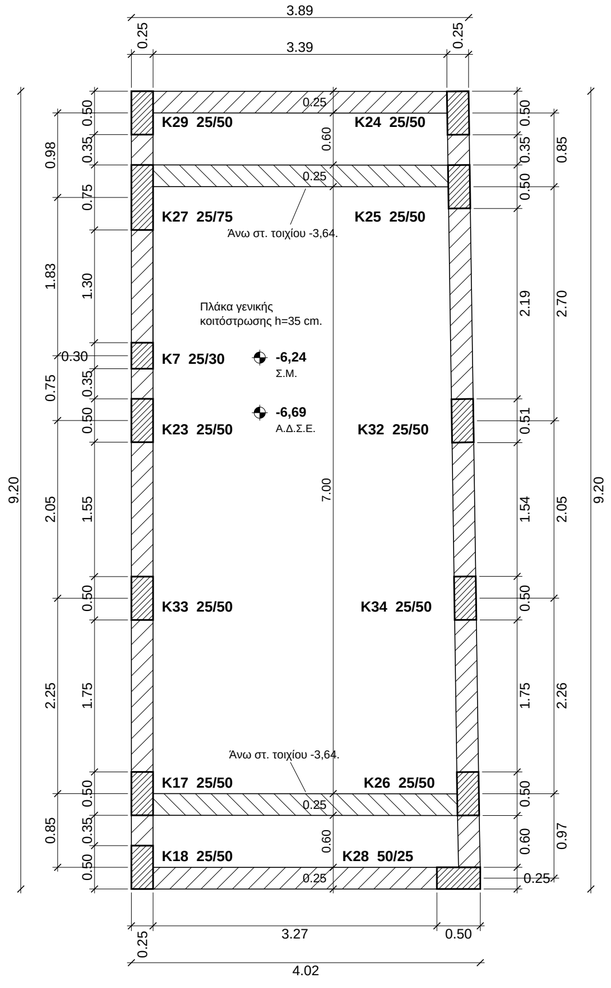

ΞΥΛΟΤΥΠΟΣ ΘΕΜΕΛΙΩΣΗΣ ΥΠΟΣΤΑΘΜΟΥ (-6,69)

ΞΥΛΟΤΥΠΟΣ ΘΕΜΕΛΙΩΣΗΣ ΥΠΟΣΤΑΘΜΟΥ (-6,69)

ΚΛΙΜΑΚΑ 1:50 (Α2)

0 1 2 m

ΚΩΝΣΤΑΝΤΙΝΟΥΠΟΛΕΩΣ 12 &
ΑΓΙΑΣ ΒΑΡΒΑΡΑΣ, ΑΡΓΥΡΟΥΠΟΛΗ