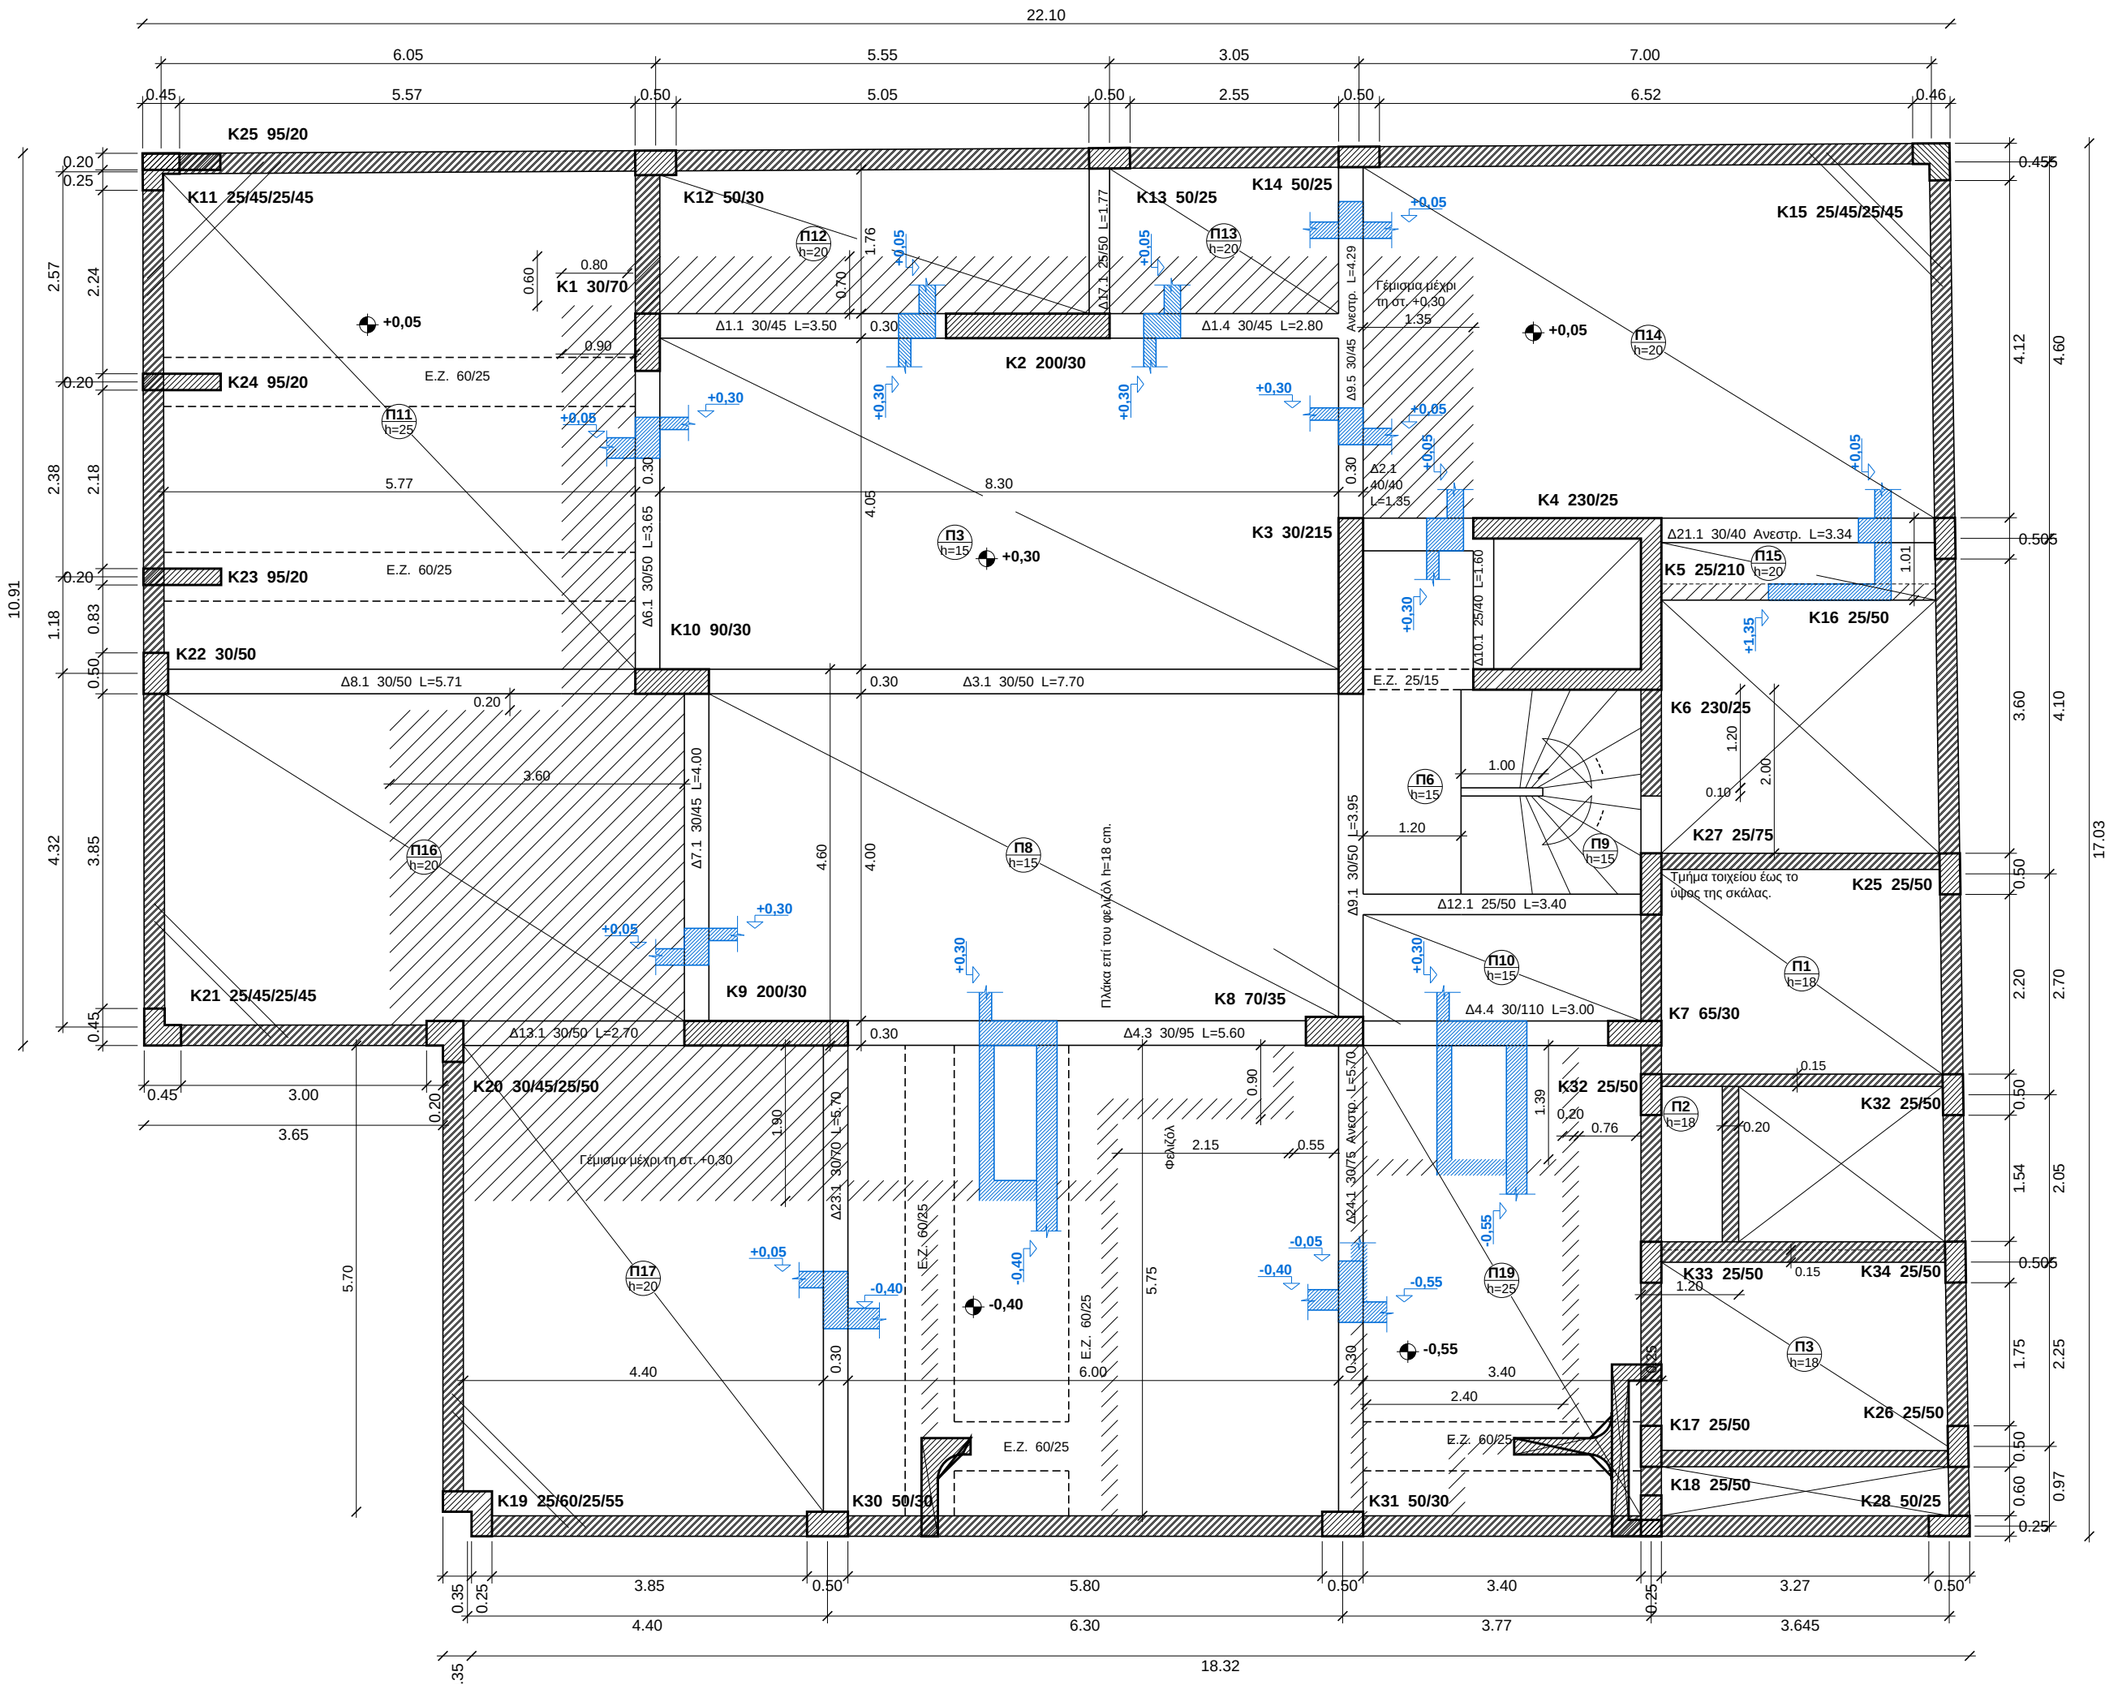


ΕΡΓΟ

ΑΝΕΓΕΡΣΗ ΠΕΝΤΑΟΡΟΦΟΥ ΚΤΗΡΙΟΥ ΚΑΤΟΙΚΙΩΝ ΜΕ ΥΠΟΓΕΙΟ, ΣΟΦΙΤΑ ΚΑΙ ΔΩΜΑ

ΘΕΣΗ

ΚΩΝΣΤΑΝΤΙΝΟΥΠΟΛΕΩΣ 12 &
ΑΓΙΑΣ ΒΑΡΒΑΡΑΣ – Ο.Τ. 103-15
ΔΗΜΟΣ ΕΛΛΗΝΙΚΟΥ-ΑΡΓΥΡΟΥΠΟΛΗΣ

ΕΡΓΟΔΟΤΗΣ

ARKAD I.K.E.

ΜΕΛΕΤΗΤΗΣ ΣΤΑΤΙΚΩΝ

ΓΙΩΡΓΟΣ ΚΟΓΙΑΣ
ΠΟΛΙΤΙΚΟΣ ΜΗΧΑΝΙΚΟΣ

ΘΕΜΑ ΣΧΕΔΙΟΥ

ΞΥΛΟΤΥΠΟΣ ΟΡΟΦΗΣ ΥΠΟΓΕΙΟΥ (+0,05 / +0,30)
ΓΕΩΜΕΤΡΙΑ – ΠΛΗΡΗΣ ΔΙΑΣΤΑΣΙΟΛΟΓΗΣΗ
(ΧΩΡΙΣ ΟΠΛΙΣΜΟΥΣ)

ΒΑΣΗ

Εγκεκριμένο σχέδιο Σ2
Οριστική μελέτη, 02/2024
κλ. 1:50 (Fespa)

ΚΛΙΜΑΚΑ

1:75 (A3)

ΑΡ. ΣΧΕΔΙΟΥ / ΗΜΕΡΟΜΗΝΙΑ

Σ2 – ΓΕΩΜΕΤΡΙΑ 1:75
21/09/2026

Διαστάσεις σε m · b/h σε cm
h πλάκας σε cm
L = καθαρό μήκος δοκού
μεταξύ παρειών στηρίξεων
Ανεστρ. = ανεστραμμένη δοκός
Οπλισμοί κατά Σ2

0 1 2
m (1:75)