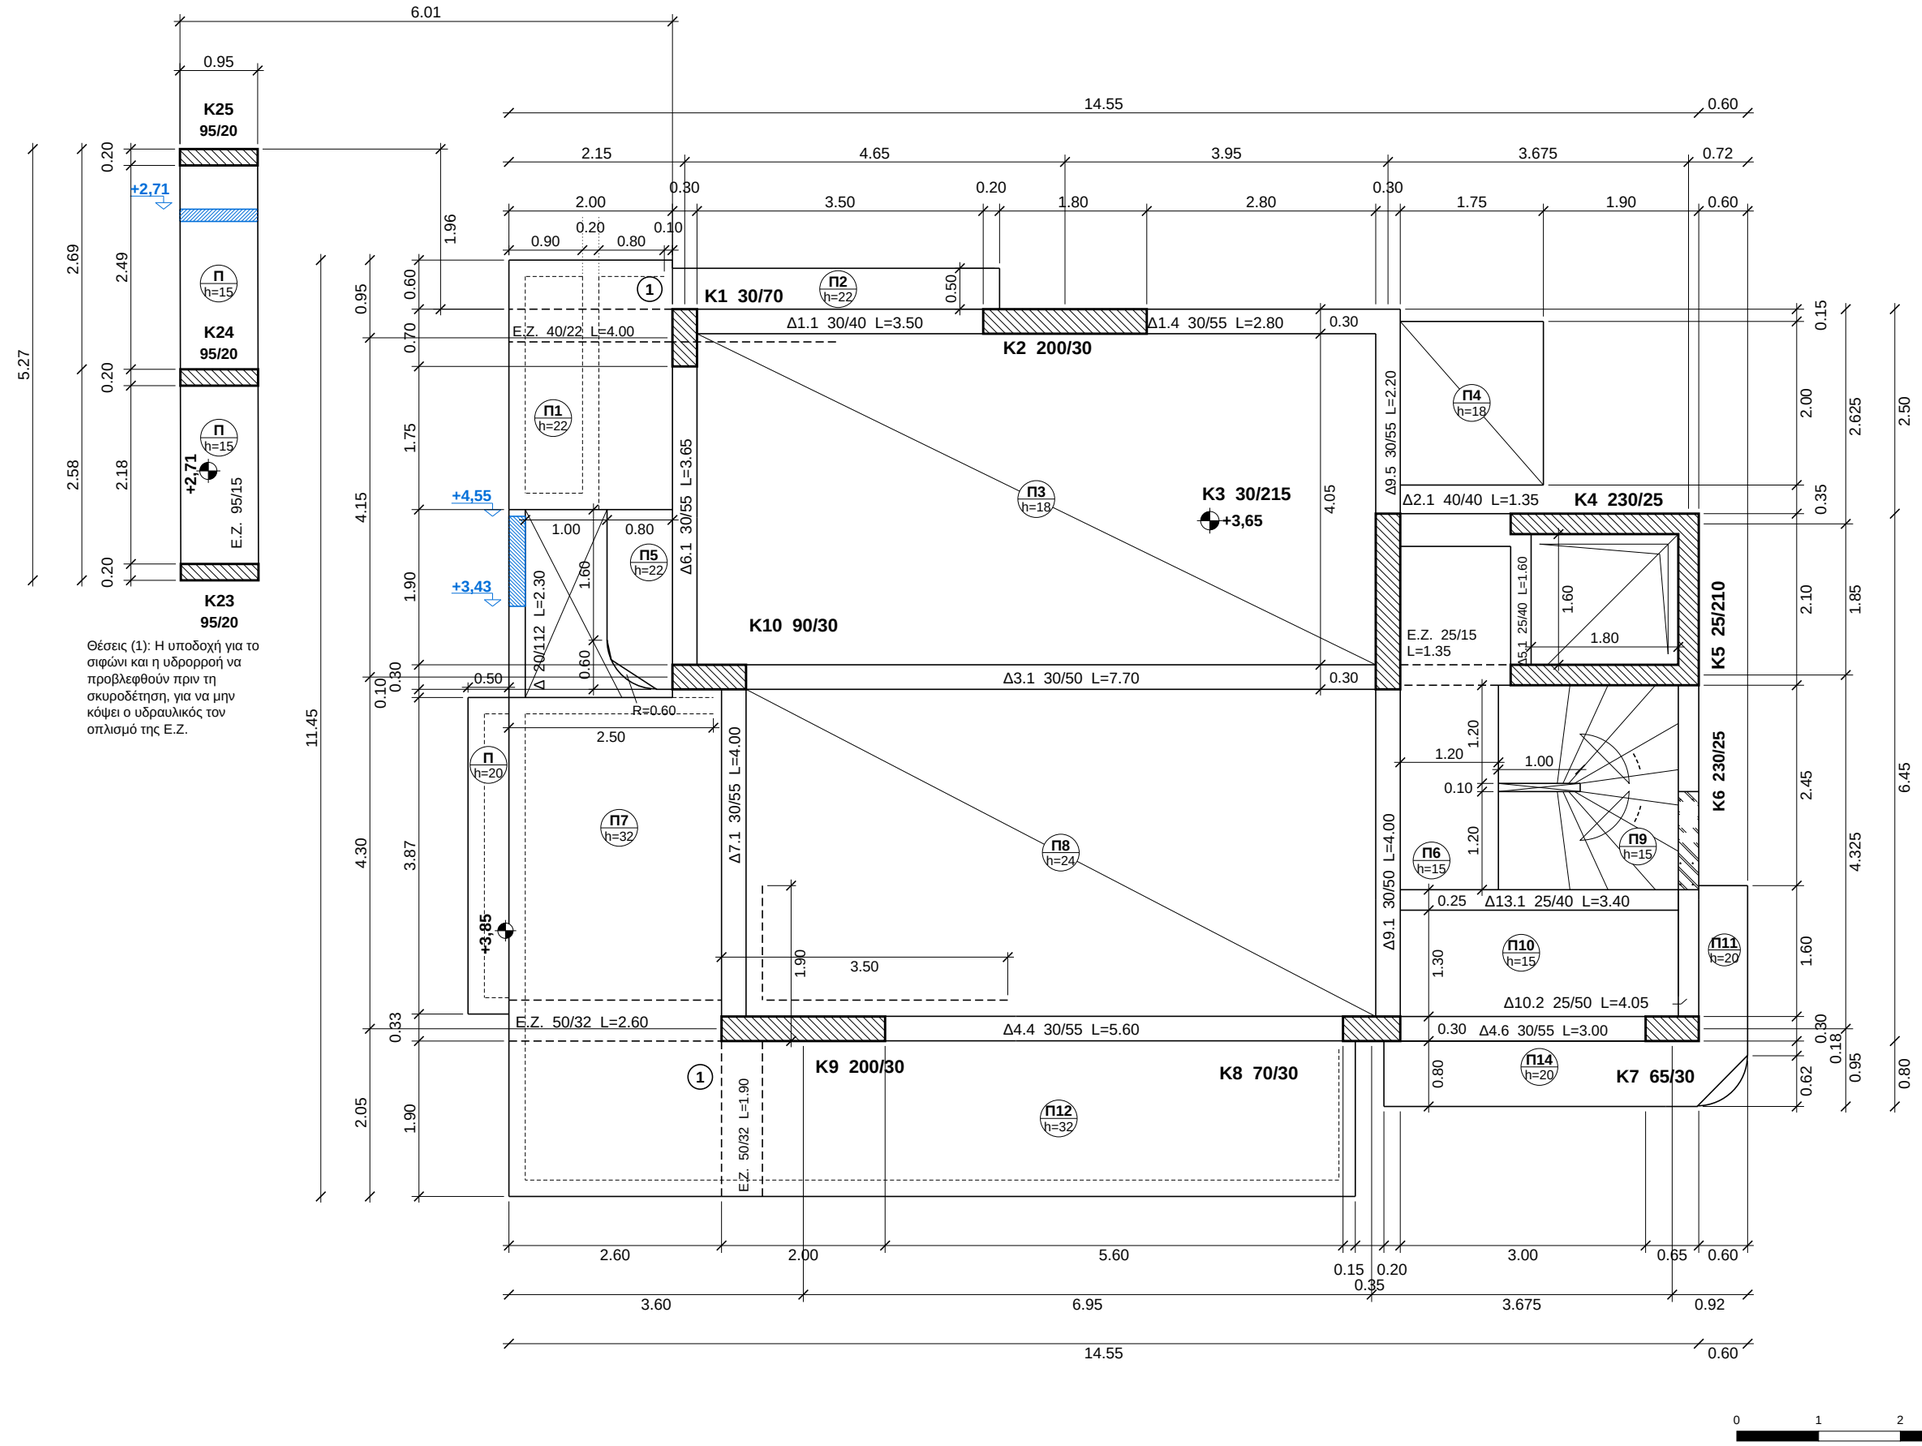


Θέσεις (1): Η υποδοχή για το σιφώνι και η υδρορροή να προβλεφθούν πριν τη σκυροδέτηση, για να μην κόψει ο υδραυλικός τον οπλισμό της Ε.Ζ.

0 1 2 3 4 5 m (1:75)

ΕΡΓΟ	ΘΕΜΑ ΣΧΕΔΙΟΥ	ΒΑΣΗ	ΚΛΙΜΑΚΑ	ΑΡ. ΣΧΕΔΙΟΥ / ΗΜΕΡΟΜΗΝΙΑ
ΑΝΕΓΕΡΣΗ ΠΕΝΤΑΟΡΟΦΟΥ ΚΤΗΡΙΟΥ ΚΑΤΟΙΚΙΩΝ ΜΕ ΥΠΟΓΕΙΟ, ΣΟΦΙΤΑ ΚΑΙ ΔΩΜΑ **ΟΔΟΣ ΚΩΝΣΤΑΝΤΙΝΟΥΠΟΛΕΩΣ 12 & ΑΓΙΑΣ ΒΑΡΒΑΡΑΣ – Ο.Τ. 103-15, ΔΗΜΟΣ ΕΛΛΗΝΙΚΟΥ-ΑΡΓΥΡΟΥΠΟΛΗΣ** ΕΡΓΟΔΟΤΗΣ: ARKAD I.K.E. ΜΕΛΕΤΗΤΗΣ ΣΤΑΤΙΚΩΝ: ΓΙΩΡΓΟΣ ΚΟΓΙΑΣ, ΠΟΛΙΤΙΚΟΣ ΜΗΧΑΝΙΚΟΣ	**ΞΥΛΟΤΥΠΟΣ ΟΡΟΦΗΣ ΙΣΟΓΕΙΟΥ (+3,65)** **ΓΕΩΜΕΤΡΙΑ – ΠΛΗΡΗΣ ΔΙΑΣΤΑΣΙΟΛΟΓΗΣΗ** **(ΧΩΡΙΣ ΟΠΛΙΣΜΟΥΣ)** Διαστάσεις σε m · b/h σε cm · h πλάκας σε cm · L = καθαρό μήκος δοκού μεταξύ παρειών στηρίξεων	Εγκεκριμένο σχέδιο Σ3 Οριστική μελέτη, 02/2024 κλ. 1:50 (Fespa)	**1:75** **A3**	**Σ3 – ΓΕΩΜΕΤΡΙΑ 1:75** **21/09/2026**