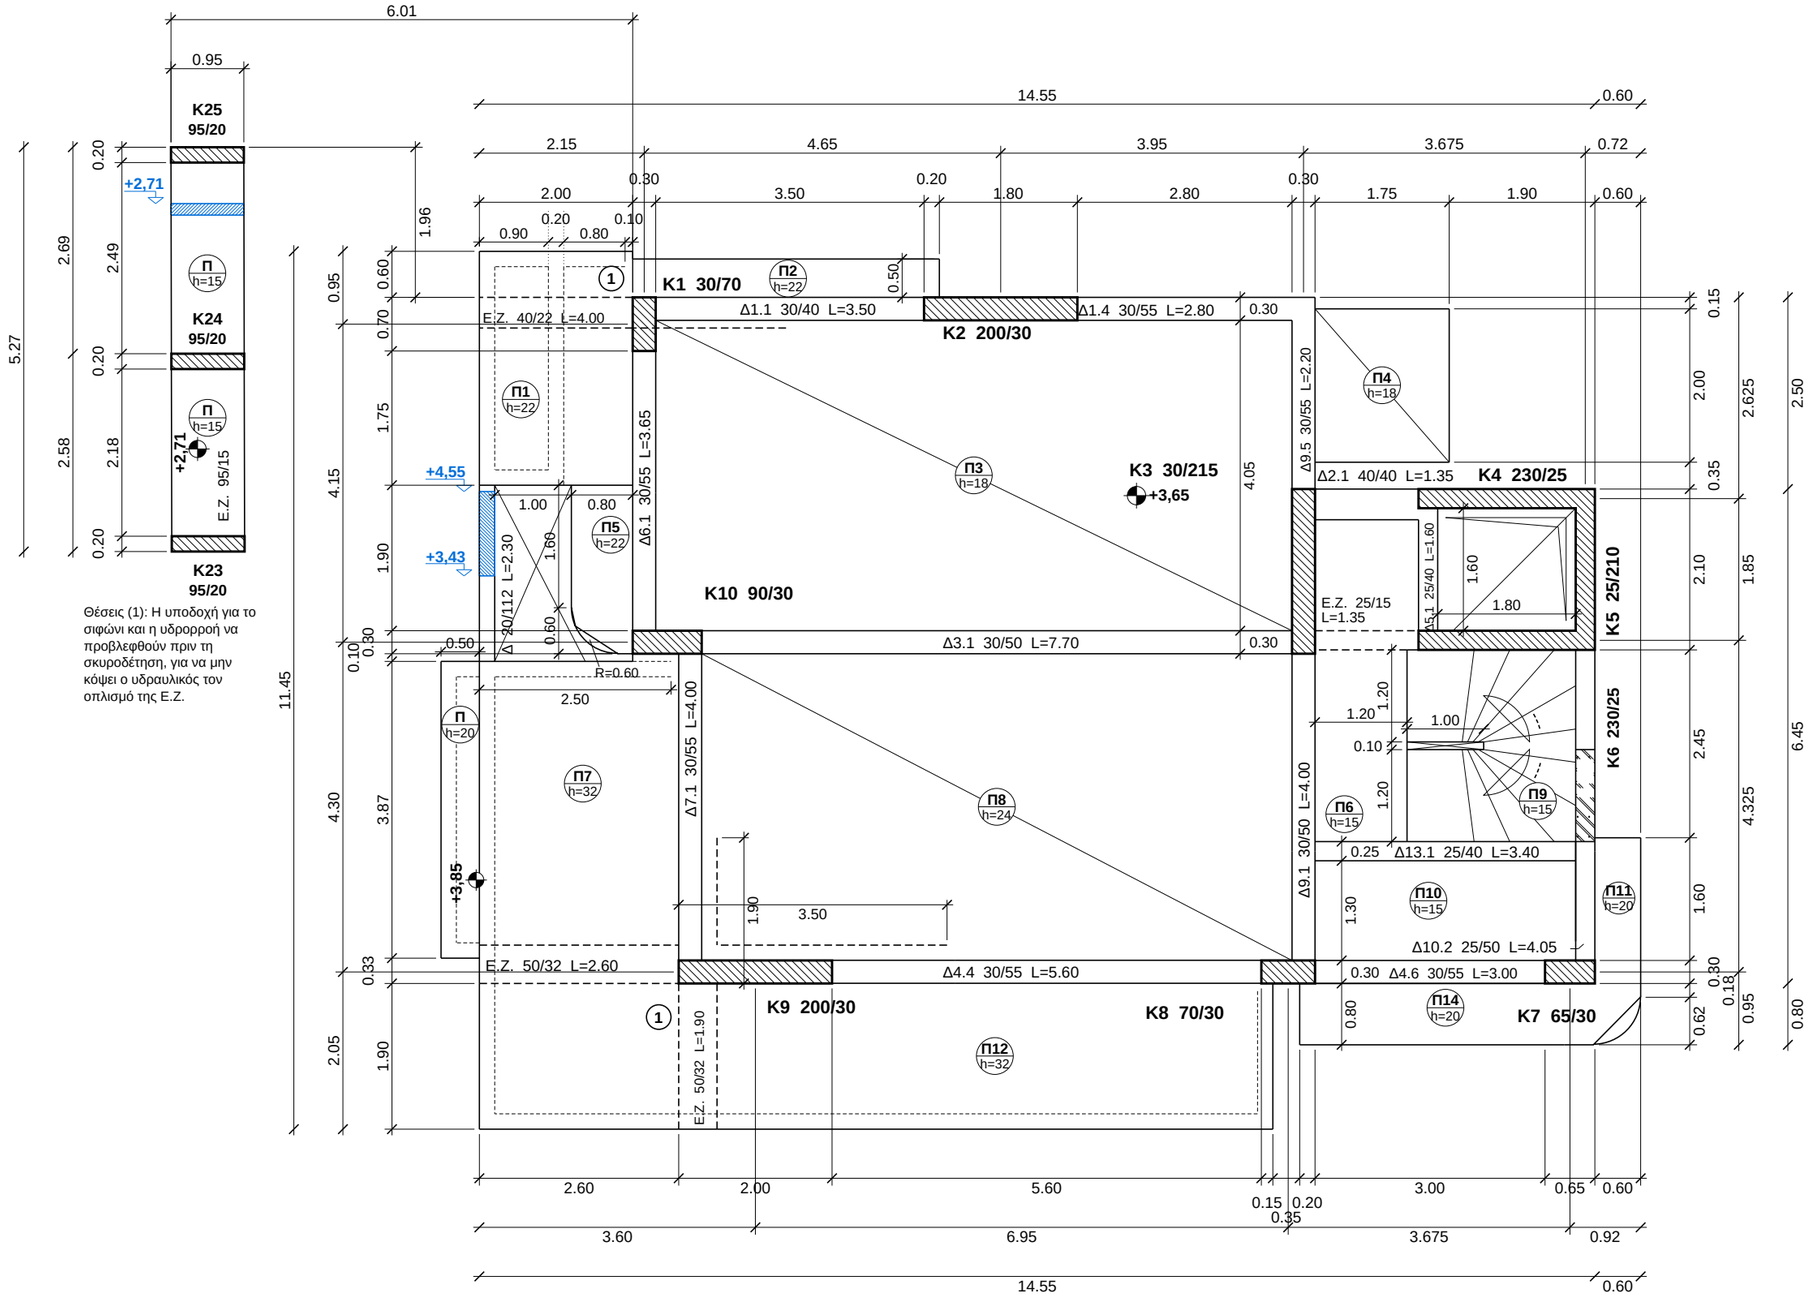


Θέσεις (1): Η υποδοχή για το σιφώνι και η υδρορροή να προβλεφθούν πριν τη σκυροδέτηση, για να μην κόψει ο υδραυλικός τον οπλισμό της Ε.Ζ.

ΥΠΟΣΤΥΛΩΜΑΤΑ / ΤΟΙΧΙΑ

Στοιχείο	b/h (cm)	Παρατήρηση
K1	30/70	
K2	200/30	τοιχίο
K3	30/215	τοιχίο
K4	230/25	πυρήνας ανελκ.
K5	25/210	πυρήνας ανελκ.
K6	230/25	πυρήνας ανελκ.
K7	65/30	
K8	70/30	
K9	200/30	τοιχίο
K10	90/30	
K23, K24, K25	95/20	διακοσμ. μετώπη +2,71

ΔΟΚΟΙ (L = καθαρό μήκος μεταξύ παρειών στηρίξεων)

Δοκός	b/h (cm)	L (m)	Από – έως
Δ1.1	30/40	3.50	K1 – K2
Δ1.4	30/55	2.80	K2 – Δ9.5
Δ2.1	40/40	1.35	K3 – K4
Δ3.1	30/50	7.70	K10 – K3
Δ4.4	30/55	5.60	K9 – K8
Δ4.6	30/55	3.00	K8 – K7
Δ5.1	25/40	1.60	K4 – K6
Δ6.1	30/55	3.65	K1 – K10
Δ7.1	30/55	4.00	K10 – K9
Δ9.1	30/50	4.00	K3 – K8
Δ9.5	30/55	2.20	Δ1.4 – K3
Δ10.2	25/50	4.05	K6 – K7
Δ13.1	25/40	3.40	Δ9.1 – Δ10.2
Δ (κενού)	20/112	2.30	άνοιγμα δυτ. πλευράς
E.Z.	40/22	4.00	Π1/Π2
E.Z.	25/15	1.35	K3 – K4/K6
E.Z.	50/32	2.60	Π7 (οριζ.)
E.Z.	50/32	1.90	Π12 (κατακ.)
E.Z.	95/15	–	μετώπη K23–K25

ΠΛΑΚΕΣ

Πλάκα	h (cm)	Στάθμη	Πλάκα	h (cm)	Στάθμη
Π1	22	+3,65	Π9	15	+3,65
Π2	22	+3,65	Π10	15	+3,65
Π3	18	+3,65	Π11	20	+3,65
Π4	18	+3,65	Π12	32	+3,65
Π5	22	+3,65	Π14	20	+3,65
Π6	15	+3,65	Π (εξώστης δυτ.)	20	+3,85
Π7	32	+3,65	Π (μετώπη) ×2	15	+2,71
Π8	24	+3,65			

ΣΗΜΕΙΩΣΕΙΣ

1. Όλες οι διαστάσεις σε μέτρα (m). Διατομές υποστυλωμάτων/δοκών σε cm (b/h). Πάχη πλακών h σε cm.
2. L = καθαρό μήκος δοκού μεταξύ παρειών στηρίξεων. Οι αλυσίδες διαστάσεων περιμετρικά δίνουν: παρειές στοιχείων (1η σειρά), αποστάσεις αξόνων υποστυλωμάτων (2η σειρά), συνολικά (3η σειρά).
3. Το σχέδιο είναι γεωμετρική/κατασκευαστική εκδοχή του εγκεκριμένου ξυλοτύπου Σ3 (Γ. Κόγιας, 02/2024, κλ. 1:50) χωρίς οπλισμούς. Όλες οι διαστάσεις προέκυψαν από τη διανυσματική γεωμετρία του Σ3 και ελέγχθηκαν έναντι των αναγραφόμενων διαστάσεων του μελετητή.
4. Οπλισμοί, αγκυρώσεις και οι τομές 1-1, 2-2, 3-3 των διακοσμητικών μετωπών (κλ. 1:20): βλ. εγκεκριμένο σχέδιο Σ3. Σε περίπτωση διαφοράς υπερισχύει το εγκεκριμένο σχέδιο και ο μελετητής.
5. Στάθμες: πλάκα οροφής ισογείου +3,65 · εξώστης δυτικής πλευράς +3,85 · διακοσμητική μετώπη K23–K25 +2,71 · φυτευτό τοιχείο δυτικής πλευράς +3,43 έως +4,55 (μπλε).
6. Το διαγραμμισμένο τοιχείο επί της Δ10.2 (κάτω από τη σκάλα) κατασκευάζεται έως το ύψος της σκάλας για τη στήριξή της (βλ. Σ3).
7. Η απόσταση 6.01 της μετώπης από το K1 αναγράφεται όπως στο Σ3 (η διανυσματική γεωμετρία δίνει 6.02). Η μετώπη K23–K25 ακολουθεί τη ρυμοτομική γραμμή.

0 1 2 3 4 5 m (1:80)

ΕΡΓΟ	ΘΕΜΑ ΣΧΕΔΙΟΥ	ΒΑΣΗ	ΚΛΙΜΑΚΑ	ΑΡ. ΣΧΕΔΙΟΥ / ΗΜΕΡΟΜΗΝΙΑ
ΑΝΕΓΕΡΣΗ ΠΕΝΤΑΟΡΟΦΟΥ ΚΤΗΡΙΟΥ ΚΑΤΟΙΚΙΩΝ ΜΕ ΥΠΟΓΕΙΟ, ΣΟΦΙΤΑ ΚΑΙ ΔΩΜΑ **ΟΔΟΣ ΚΩΝΣΤΑΝΤΙΝΟΥΠΟΛΕΩΣ 12 & ΑΓΙΑΣ ΒΑΡΒΑΡΑΣ – Ο.Τ. 103-15, ΔΗΜΟΣ ΕΛΛΗΝΙΚΟΥ-ΑΡΓΥΡΟΥΠΟΛΗΣ** ΕΡΓΟΔΟΤΗΣ: ARKAD I.K.E. ΜΕΛΕΤΗΤΗΣ ΣΤΑΤΙΚΩΝ: ΓΙΩΡΓΟΣ ΚΟΓΙΑΣ, ΠΟΛΙΤΙΚΟΣ ΜΗΧΑΝΙΚΟΣ	**ΞΥΛΟΤΥΠΟΣ ΟΡΟΦΗΣ ΙΣΟΓΕΙΟΥ (+3,65)** **ΓΕΩΜΕΤΡΙΑ – ΠΛΗΡΗΣ ΔΙΑΣΤΑΣΙΟΛΟΓΗΣΗ** **(ΧΩΡΙΣ ΟΠΛΙΣΜΟΥΣ)**	Εγκεκριμένο σχέδιο Σ3 Οριστική μελέτη, 02/2024 κλ. 1:50 (Fespa)	**1:80** **A3**	**Σ3 – ΓΕΩΜΕΤΡΙΑ 1:80** **17/09/2026**