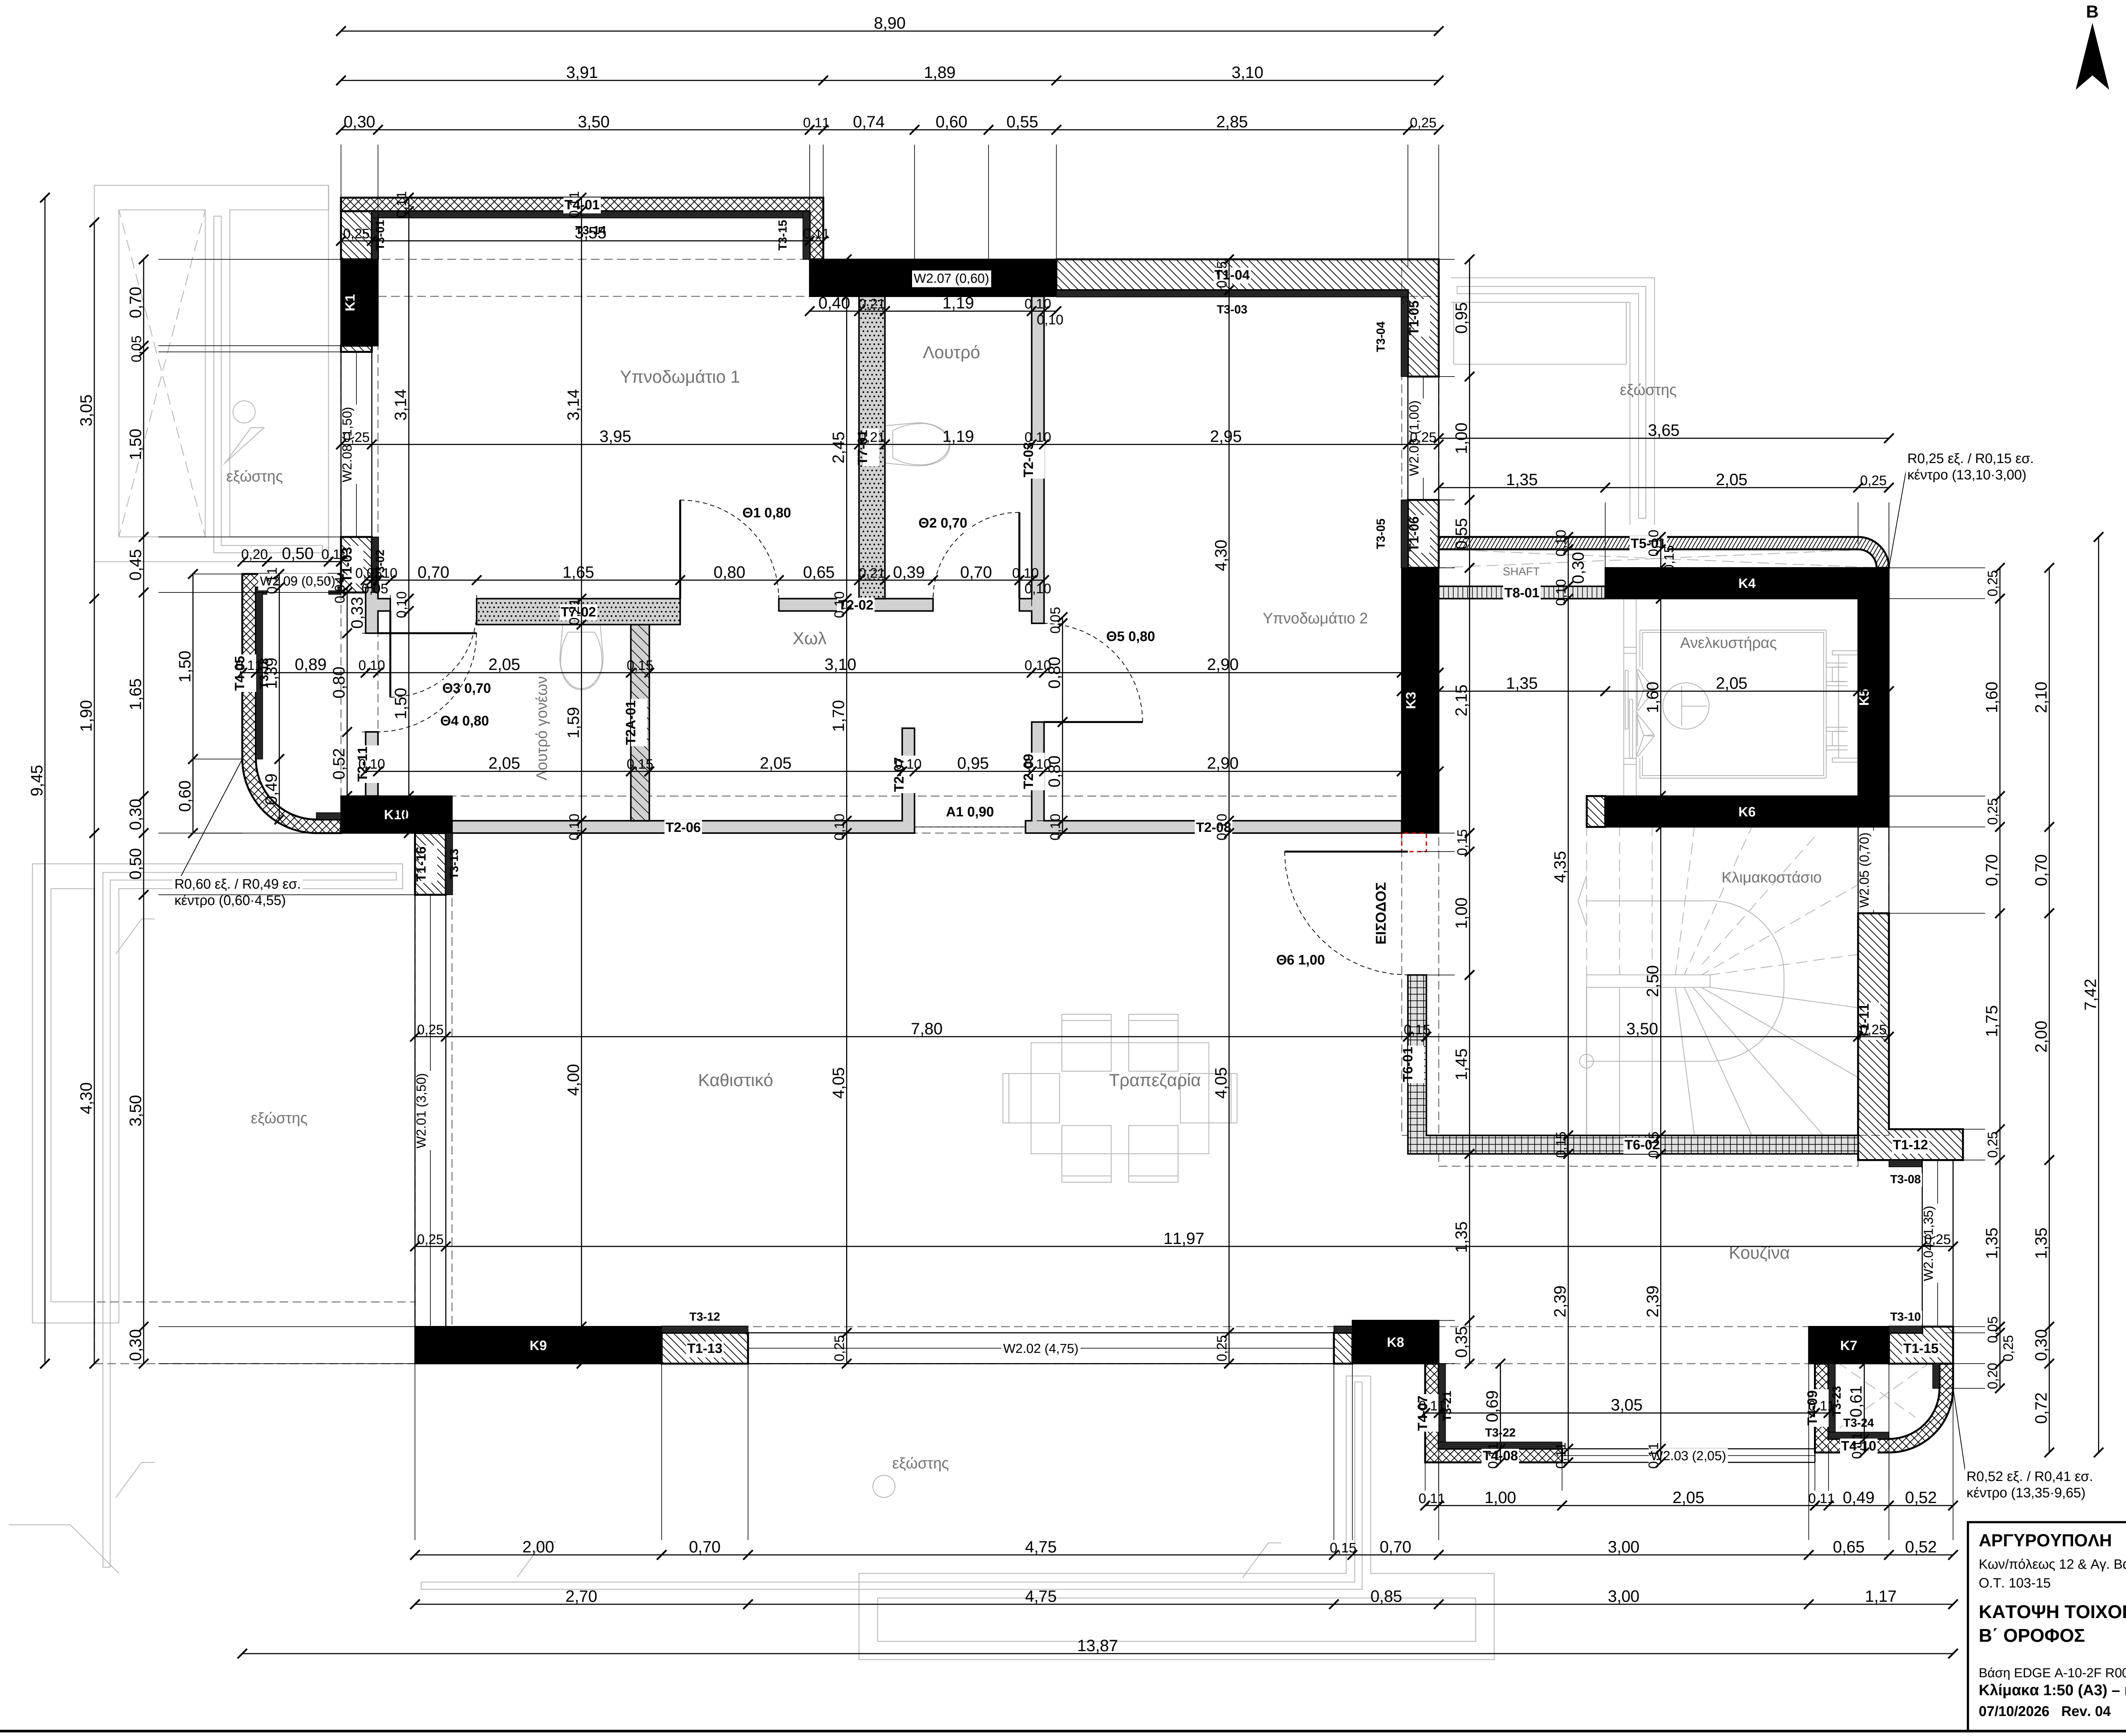
B
8,90
3,91
1,89
3,10
Υπνοδωμάτιο 1
Λουτρό
Υπνοδωμάτιο 2
Χωλ
Λουτρό γονέων
Ανελκυστήρας
Κλιμακοστάσιο
SHAFT
ΕΙΣΟΔΟΣ
Καθιστικό
Τραπεζαρία
Κουζίνα
εξώστης
W2.07 (0,60)
W2.08 (1,50)
W2.09 (0,50)
W2.06 (1,00)
W2.05 (0,70)
W2.01 (3,50)
W2.02 (4,75)
W2.03 (2,05)
W2.04 (1,35)
Θ1 0,80
Θ2 0,70
Θ3 0,70
Θ4 0,80
Θ5 0,80
Θ6 1,00
A1 0,90
K1
K3
K4
K5
K6
K7
K8
K9
K10
T4-01
T1-04
T3-03
T7-02
T2-02
T2-06
T2-08
T6-01
T6-02
T8-01
T5-01
T1-12
T1-13
T1-15
R0,25 εξ. / R0,15 εσ.
κέντρο (13,10·3,00)
R0,60 εξ. / R0,49 εσ.
κέντρο (0,60·4,55)
R0,52 εξ. / R0,41 εσ.
κέντρο (13,35·9,65)
11,97
7,80
13,87
9,45
7,42

ΑΡΓΥΡΟΥΠΟΛΗ
Κων/πόλεως 12 & Αγ. Βαρβάρας
Ο.Τ. 103-15

ΚΑΤΟΨΗ ΤΟΙΧΟΠΟΙΙΩΝ
Β΄ ΟΡΟΦΟΣ

Βάση EDGE A-10-2F R00
Κλίμακα 1:50 (A3) – m
07/10/2026 Rev. 04