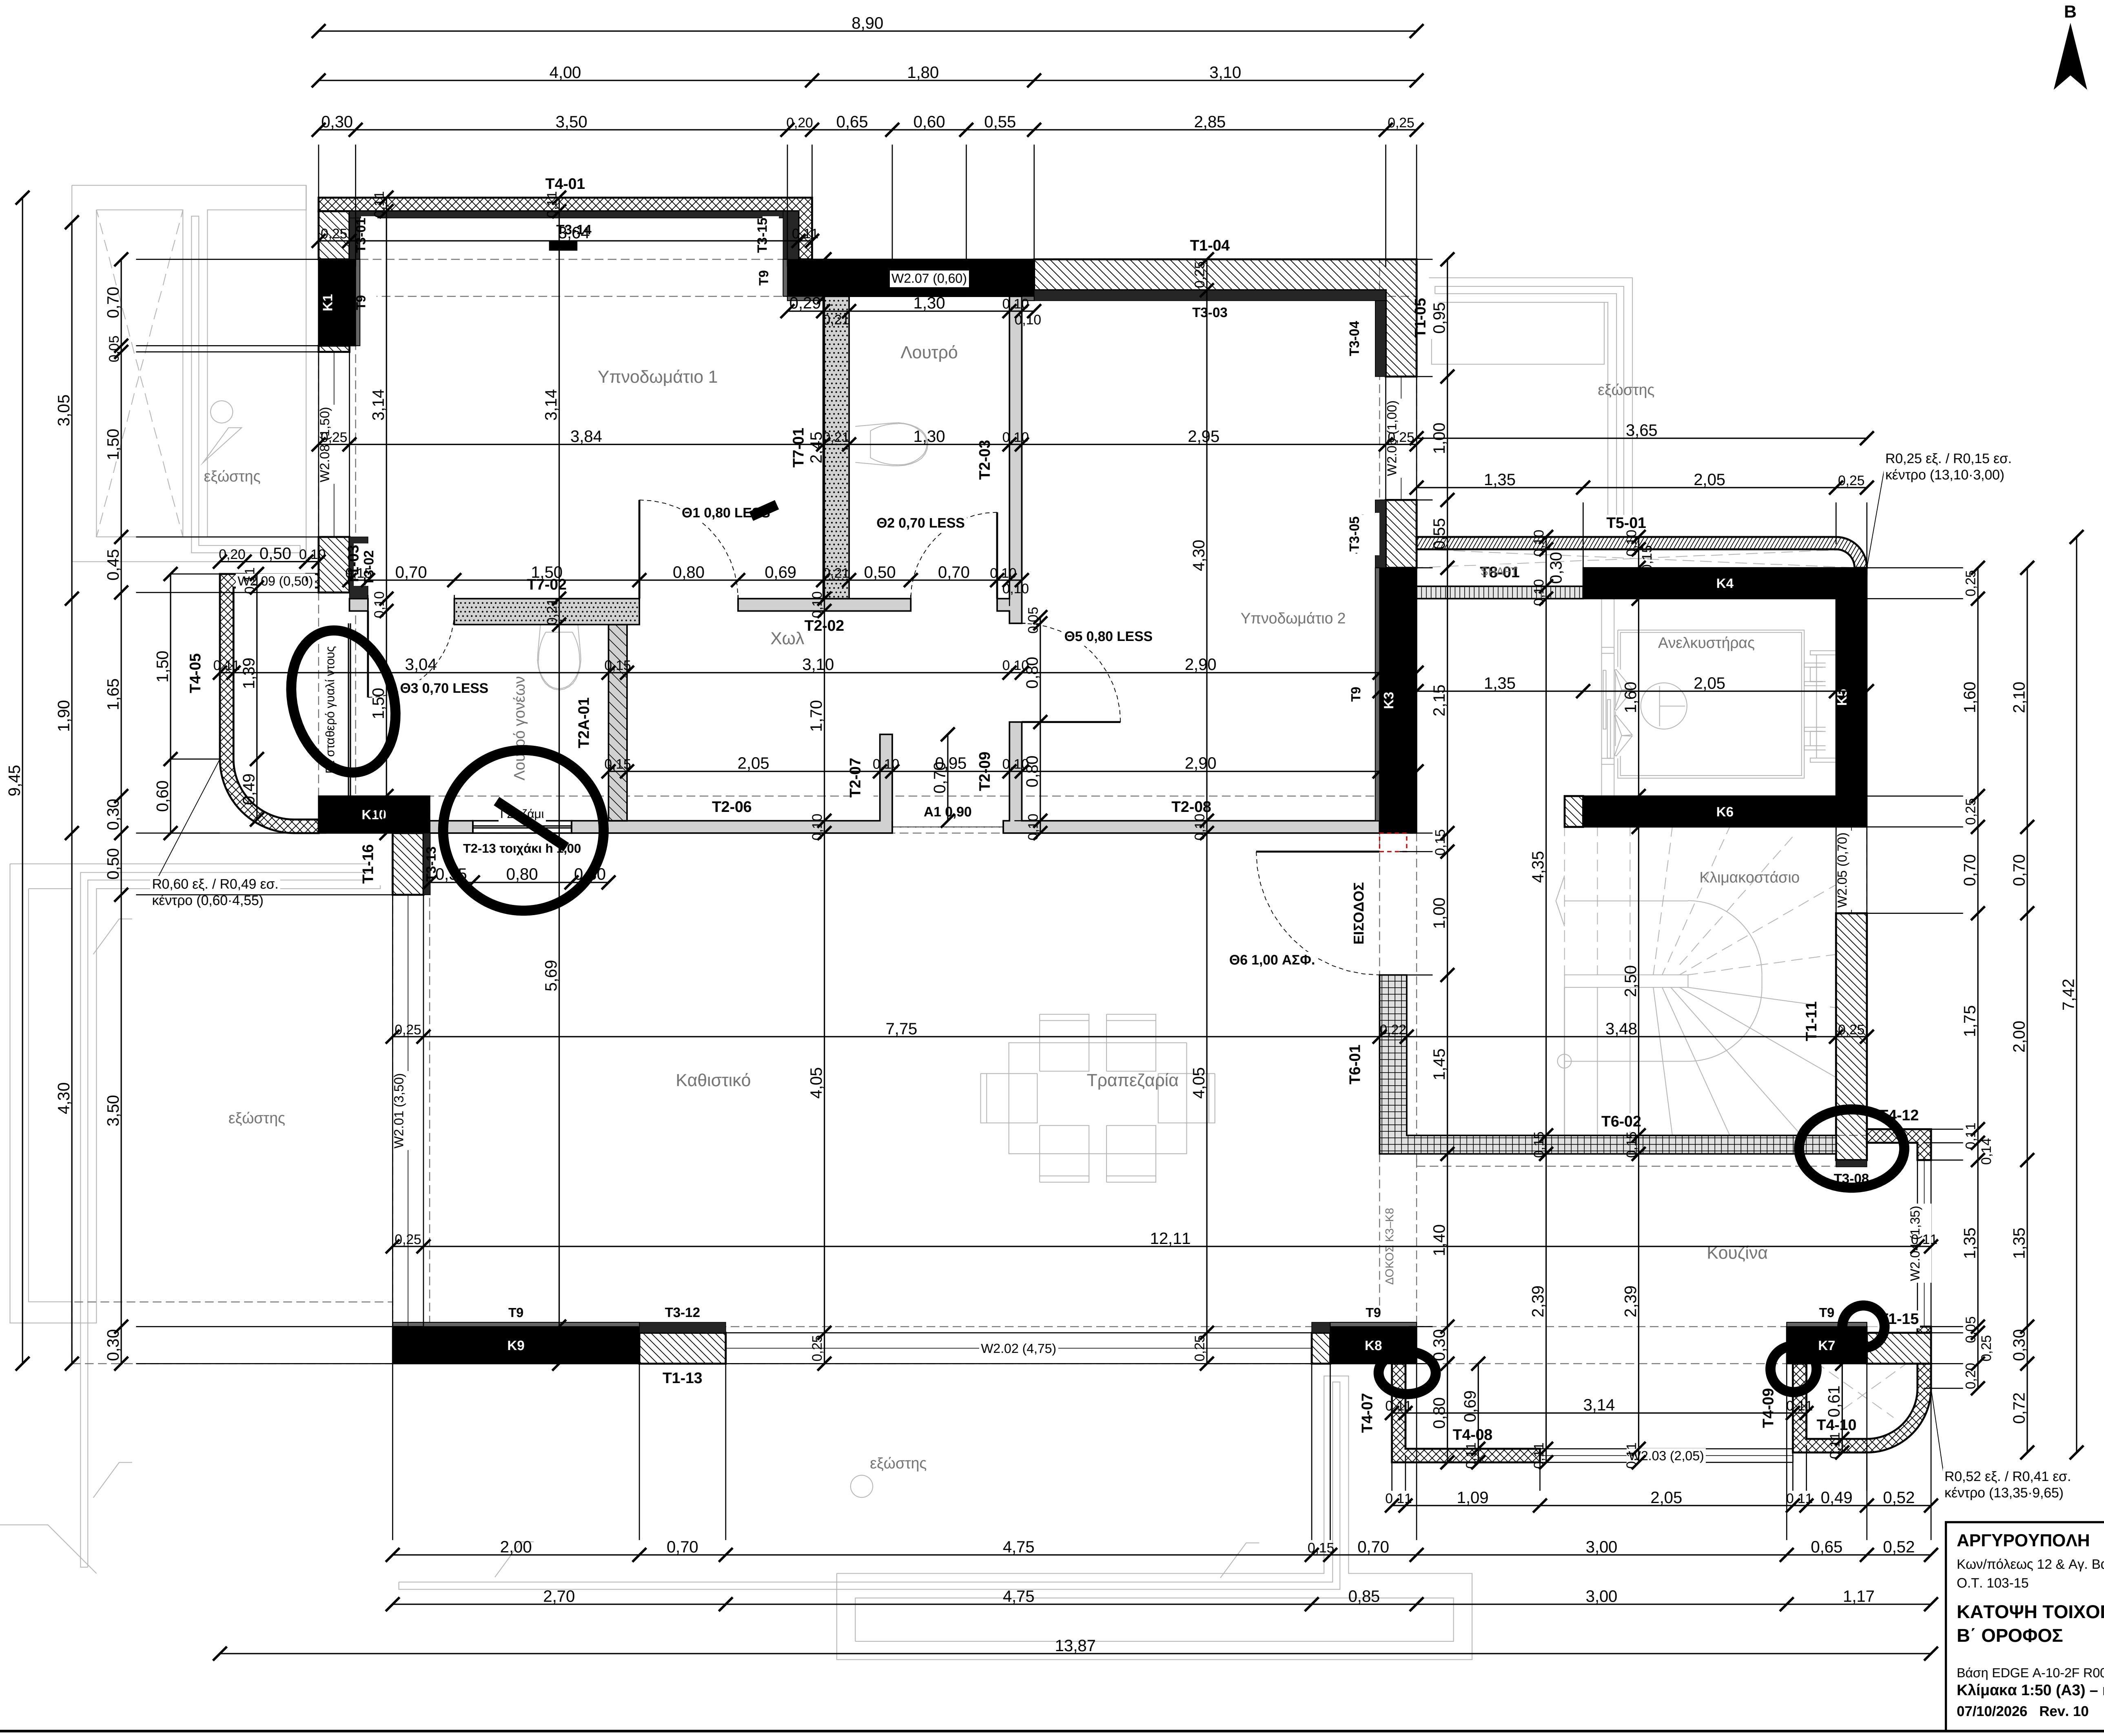

ΚΡΥΦΗ ΠΟΡΤΑ LESS

τομή λαμπά σε τοίχο T2 – 1:5

(σχηματικά κατά Golden Door)

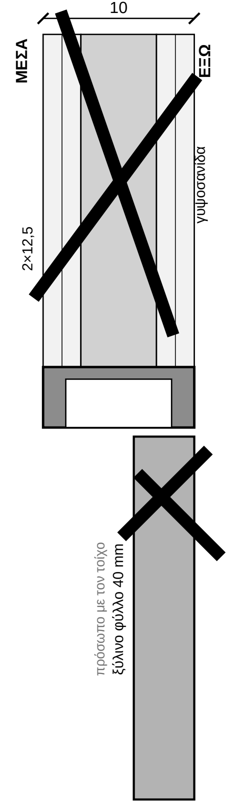

Θ1, Θ2, Θ3, Θ5

κενά κατά κατασκευαστή

ΑΡΓΥΡΟΥΠΟΛΗ
Κων/πόλεως 12 & Αγ. Βαρβάρας
Ο.Τ. 103-15

ΚΑΤΟΨΗ ΤΟΙΧΟΠΟΙΙΩΝ
Β΄ ΟΡΟΦΟΣ

Βάση EDGE A-10-2F R00
Κλίμακα 1:50 (A3) – m
07/10/2026 Rev. 10