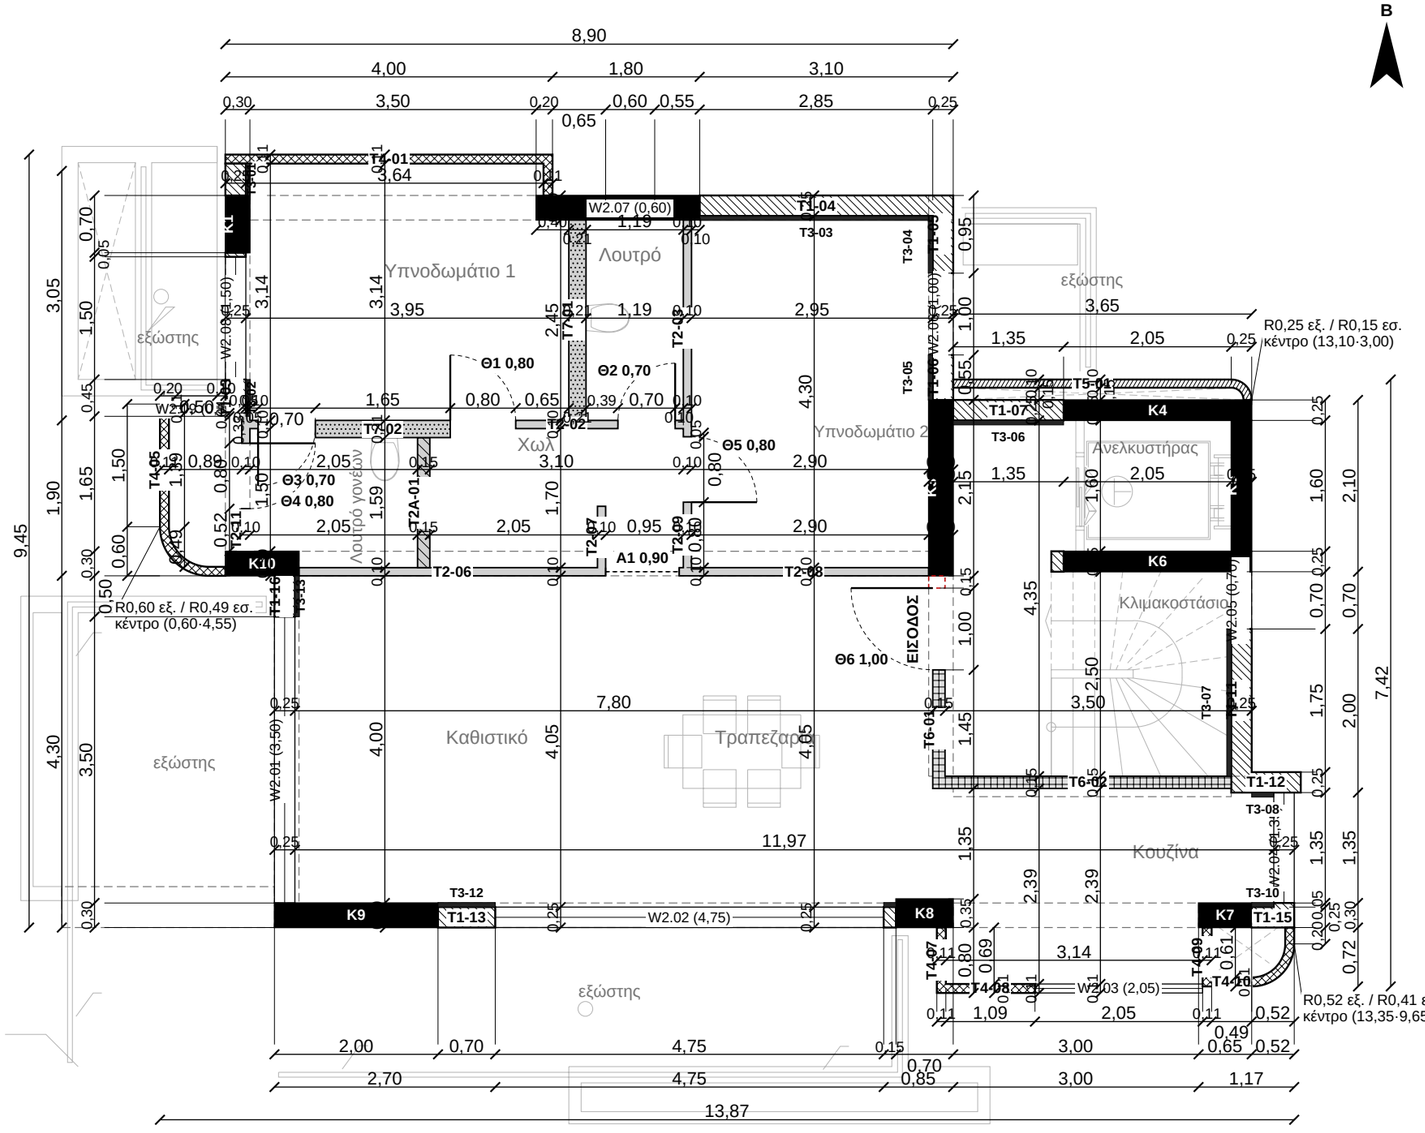


ΥΠΟΜΝΗΜΑ ΤΟΙΧΟΠΟΙΙΩΝ

- T1 – Εξωτερική: τούβλο 25 cm + εσωτερική επένδυση T3 (τελικό 30,5 cm)
- T3 – Επένδυση T1: σκελετός 3 cm + διπλή γυψοσανίδα (5,5 cm)
- T2 – Εσωτερικό χώρισμα: σκελετός 5 cm + διπλή γυψοσανίδα εκατέρωθεν (10 cm)
- T2A – Σκελετός 10 cm + διπλή γυψοσανίδα εκατέρωθεν (15 cm) – μόνο T2A-01
- T4 – ERKER: απλό τούβλο 11 cm
- T5 – Τούβλο 10 cm περιμετρικά πυρήνα (ως αρχιτεκτονικό)
- T6 – Κλιμακοστάσιο: γυψοσανίδα 15 cm (πρόταση σύνθεσης – προς καθορισμό)
- T7 – Τοίχος λεκάνης WC: σκελ. 3 + 2×γυψ. / κενό 10 / σκελ. 3 + 2×γυψ. (21 cm)
- Οπλισμένο σκυρόδεμα K1–K10 (ως έχει, στατικά Κόγια)
- Δοκός οροφής (προβολή άνωθεν, από αρχιτεκτονικό)
- Παράθυρο / πόρτα (φύλλο + τόξο ανοίγματος)
- Στοιχείο προς επιβεβαίωση

Διαστάσεις σε m, μετρημένες σε παρειές τούβλου / σκελετού / σκυροδέματος, χωρίς επιχρίσματα, θερμομόνωση και επενδύσεις. Οι τοίχοι σχεδιάζονται με τα πάχη της προδιαγραφής. Θέσεις τοίχων, ανοιγμάτων και υποστυλωμάτων ακριβώς κατά EDGE A-10-2F. Ποσότητες, τύποι και ανοίγματα: βλ. φύλλο 2.

ΑΡΓΥΡΟΥΠΟΛΗ – ΚΩΝΣΤΑΝΤΙΝΟΥΠΟΛΕΩΣ 12 & ΑΓ. ΒΑΡΒΑΡΑΣ

Ο.Τ. 103-15 – Πενταόροφο κτήριο κατοικιών – INTERKAT Α.Ε. / ARKAD Ι.Κ.Ε.

ΚΑΤΟΨΗ ΤΟΙΧΟΠΟΙΙΩΝ – Β΄ ΟΡΟΦΟΣ

Τύποι τοιχοποιίας, πάχη και θέσεις ανοιγμάτων – φύλλο 2: τύποι & ποσότητες (m²), φύλλο 3: ανοίγματα

Βάση: EDGE Μελέτη Εφαρμογής Α-10-2F R00 (23/07/2026) – στατικά Γ. Κόγιας Σ5/Σ6
Προδιαγραφή τοίχων Γ. Ζαρκαδάς 09/2026 – Rev.02 (πραγματικά πάχη)

Κλίμακα 1:75 (A3) – διαστάσεις σε m 23/09/2026 **Φύλλο 1/3 Rev. 02**

ΚΑΤΟΨΗ ΤΟΙΧΟΠΟΙΙΩΝ – Β΄ ΟΡΟΦΟΣ – ΠΙΝΑΚΕΣ ΤΥΠΩΝ, ΑΝΟΙΓΜΑΤΩΝ & ΠΟΣΟΤΗΤΩΝ (φύλλο 2/3, Rev.02)

ΠΙΝΑΚΑΣ ΤΥΠΩΝ ΤΟΙΧΟΠΟΙΙΑΣ (πάχη σε cm)

Κωδ.	Περιγραφή / θέση	Σύνθεση	Πάχος	EDGE
T1	Εξωτερική τοιχοποιία (περίμετρος, πρόσοψη κλιμακοστασίου)	Τούβλο 25 cm + εσωτερική επένδυση T3	25 (+5,5)	25 / 30
T3	Εσωτερική επένδυση όλων των T1	Σκελετός 3 cm + διπλή γυψοσανίδα 2×12,5 mm (μία πλευρά)	5,5	–
T2	Τυπικά εσωτερικά χωρίσματα	Σκελετός 5 cm + διπλή γυψοσανίδα 2×12,5 mm εκατέρωθεν	10	15
T2A	Μόνο T2A-01 (Λουτρό γονέων / Χωλ, πρώην T2-05)	Σκελετός 10 cm + διπλή γυψοσανίδα εκατέρωθεν	15	15
T4	Τοίχοι ERKER (προεξοχές)	Απλό τούβλο 11 cm	11	15 / 20
T5	Περιμετρικά πυρήνα ανελκυστήρα (ως σχέδιο)	Απλό τούβλο 10 cm	10	10
T6	Κλιμακοστάσιο προς διαμέρισμα (T6-01/02)	Γυψοσανίδα – ΠΡΟΤΑΣΗ: σκελετός 10 + 2×12,5 mm εκατέρωθεν + πετροβάμβακας (προς καθορισμό)	15	20
T7	Τοίχοι λεκανών WC (T7-01/02)	Σκελετός 3 + διπλή γυψοσανίδα + κενό 10 + σκελετός 3 + διπλή γυψοσανίδα	21	15

ΣΥΝΟΨΗ ΠΟΣΟΤΗΤΩΝ ΑΝΑ ΤΥΠΟ – ύψος H = 2,90 m (πλάκα–πλάκα 3,10 − πλάκα 0,20)

Τύπος	Περιγραφή	Μήκος τοίχων m	Ανοίγματα m	Μικτό m²	Αφαίρεση ανοιγμ. m²	ΚΑΘΑΡΟ m²
T1	Τούβλο 25 cm (εξωτερικοί)	11.86	12.80	71.51	27.42	44.09
T3	Επένδυση T1 (σκελ. 3 + 2×γυψ.)	9.92	12.80	65.90	27.42	38.48
T2	Χωρίσματα σκελ. 5 + 2×2 γυψ.	13.34	3.80	49.71	8.36	41.35
T2A	Σκελ. 10 + 2×2 γυψ. (T2A-01)	1.59	0.00	4.61	0.00	4.61
T4	Τούβλο 11 cm (έρκερ)	11.18	2.55	39.81	1.67	38.13
T5	Τούβλο 10 cm (πυρήνας)	3.71	0.00	10.77	0.00	10.77
T6	Κλιμακοστάσιο γυψοσανίδα	4.95	1.00	17.25	2.20	15.05
T7	Τοίχοι WC διπλός σκελετός	4.10	0.00	11.89	0.00	11.89
Σ	ΣΥΝΟΛΟ τοιχοποιίες τούβλου (T1 + T4 + T5)					93.00
Σ	ΣΥΝΟΛΟ κατασκευές γυψοσανίδας (T3 + T2 + T2A + T6 + T7)					111.38

Μικτό = (μήκος τοίχων + πλάτη ανοιγμάτων) × H. Καθαρό = τοίχοι × H + ζώνες πάνω/κάτω από τα ανοίγματα (πρέκια, ποδιές). Δεν αφαιρούνται τα ύψη δοκών κάτω από τις οποίες περνούν τοίχοι (στήλη «Δοκός»: αφαίρεση κατά Σ6 Κόγια, δοκοί 30/40 → −0,20 m, 30/55 → −0,35 m) – ΠΡΟΣ ΕΠΙΒΕΒΑΙΩΣΗ.
T3 = μονόπλευρη επένδυση των T1. Το W2.07 (τοιχίο K2) και το άνοιγμα A1 (έως δοκό) δεν έχουν τοιχοποιία. Οι ποσότητες είναι προμέτρηση από κάτοψη, χωρίς φύρα.

ΥΛΙΚΑ (από καθαρά m²)

Υλικό	Από τύπους	Ποσότητα	Μονάδα
Τούβλο 25 cm (οπτοπλινθοδομή)	T1	44.1	m²
Σκελετός 3 cm (μονός)	T3	38.5	m²
Γυψοσανίδα 12,5 mm (2 στρώσεις × 1 πλευρά)	T3	77.0	m² πλάκας
Σκελετός 5 cm	T2	41.3	m²
Γυψοσανίδα 12,5 mm (2 στρώσεις × 2 πλευρές)	T2, T2A, T6, T7	291.6	m² πλάκας
Σκελετός 10 cm	T2A	4.6	m²
Τούβλο 11 cm (δρομική)	T4	38.1	m²
Τούβλο 10 cm	T5	10.8	m²
Σκελετός 10 cm + πετροβάμβακας (πρόταση)	T6	15.1	m²
Σκελετός 3 cm (2 ανεξάρτητοι)	T7	23.8	m²

ΠΙΝΑΚΑΣ ΤΟΙΧΩΝ – ΜΗΚΗ, ΠΑΧΗ, ΕΜΒΑΔΑ (m² = μήκος × H, χωρίς τις ζώνες ανοιγμάτων)

Κωδ.	Τύπ.	Θέση / περιγραφή	Μήκος m	Πάχος m	Ύψος m	Δοκός	m²
T4-01	T4	Βόρειος τοίχος έρκερ Υπν.1	4,00	0,11	2,90	–	11.60
T4-02	T4	Ανατ. επιστροφή έρκερ Υπν.1 (πάνω από K2)	0,39	0,11	2,90	–	1.13
T4-03	T4	Βόρειος τοίχος δυτ. έρκερ (δυτ. λαμπάς W2.09)	0,20	0,11	2,90	–	0.58
T4-04	T4	Βόρειος τοίχος δυτ. έρκερ (ανατ. λαμπάς W2.09)	0,11	0,10	2,90	–	0.32
T4-05	T4	Δυτικός τοίχος έρκερ λουτρού (ευθύγραμμο τμήμα)	1,39	0,11	2,90	–	4.03
T4-06	T4	Νότια επιστροφή έρκερ λουτρού → K10	0,20	0,11	2,90	–	0.58
T4-07	T4	Δυτικός τοίχος ΝΔ προεξοχής κουζίνας	0,80	0,11	2,90	–	2.32
T4-08	T4	Νότιος τοίχος ΝΔ προεξοχής κουζίνας	1,09	0,11	2,90	–	3.16
T4-09	T4	Δυτικός τοίχος ΝΑ προεξοχής κουζίνας	0,72	0,11	2,90	–	2.09
T4-10	T4	Νότιος τοίχος ΝΑ προεξοχής (ευθύγρ. τμήμα)	0,49	0,11	2,90	–	1.42
T4-11	T4	Ανατ. τοίχος ΝΑ προεξοχής (ευθύγρ. τμήμα)	0,20	0,11	2,90	–	0.58
T1-01	T1	Πεσσός ΒΔ πάνω από K1	0,39	0,25	2,90	–	1.13
T1-02	T1	Λωρίδα K1 → W2.08	0,25	0,05	2,90	ναι	0.72
T1-03	T1	Πεσσός δυτ. Υπν.1 (W2.08 → λουτρό)	0,45	0,25	2,90	ναι	1.31
T1-04	T1	Βόρειος τοίχος Υπν.2 (K2 → πεσσός)	2,85	0,25	2,90	ναι	8.26
T1-05	T1	ΒΑ πεσσός Υπν.2 (→ W2.06)	0,95	0,25	2,90	ναι	2.75
T1-06	T1	Πεσσός W2.06 → K3	0,55	0,25	2,90	–	1.59
T1-07	T1	Βόρειος τοίχος πλατύσκαλου K3 → K4	1,35	0,25	2,90	–	3.92
T1-08	T1	Λαμπάς δυτικά K6 (τούβλο ως σχέδιο)	0,25	0,15	2,90	–	0.72
T1-11	T1	Ανατ. τοίχος κλιμακοστασίου – πρόσοψη (W2.05 → γωνία)	1,75	0,25	2,90	ναι	5.08
T1-12	T1	ΝΑ γωνιακό τμήμα πρόσοψης (κλιμακοστάσιο / κουζίνα)	0,85	0,25	2,90	–	2.46
T1-13	T1	Πεσσός νότιος K9 → W2.02	0,70	0,25	2,90	ναι	2.03
T1-14	T1	Λαμπάς W2.02 → K8	0,25	0,15	2,90	ναι	0.72
T1-15	T1	ΝΑ γωνιακός πεσσός (K7 → προεξοχή), νότιο σκέλος	0,52	0,25	2,90	–	1.51
T1-15β	T1	ΝΑ γωνιακός πεσσός, ανατ. σκέλος (λαμπάς W2.04)	0,25	0,05	2,90	–	0.72
T1-16	T1	Πεσσός K10 → W2.01	0,50	0,25	2,90	ναι	1.45
T5-01	T5	Επένδυση 0,10 βόρεια πυρήνα (K3 → καμπύλη)	3,40	0,10	2,90	–	9.86
T6-01	T6	Δυτ. τοίχος κλιμακοστασίου, ΕΙΣΟΔΟΣ → νότιος (πρώην T1-09)	1,45	0,15	2,90	ναι	4.21
T6-02	T6	Νότιος τοίχος κλιμακοστασίου → κουζίνα (πρώην T1-10)	3,50	0,15	2,90	ναι	10.15

Κωδ.	Τύπ.	Θέση / περιγραφή	Μήκος m	Πάχος m	Ύψος m	Δοκός	m²
T7-01	T7	Υπν.1 / Λουτρό – τοίχος λεκάνης WC (πρώην T2-01)	2,45	0,21	2,90	–	7.11
T7-02	T7	Υπν.1 / Λουτρό γονέων – τοίχος λεκάνης WC (πρώην T2-04)	1,65	0,21	2,90	–	4.78
T2A-01	T2A	Λουτρό γονέων / Χωλ – 15 cm ως σχέδιο (πρώην T2-05)	1,59	0,15	2,90	–	4.61
T2-02	T2	Νότιος τοίχος Λουτρού (μεταξύ Θ1 και Θ2)	1,25	0,10	2,90	–	3.62
T2-03	T2	Λουτρό / Υπν.2	2,65	0,10	2,90	–	7.69
T2-03β	T2	Λαμπάς Θ2 (προεξοχή 0,10)	0,10	0,10	2,90	–	0.29
T2-06	T2	Βόρειος τοίχος Καθιστικού (δυτ. τμήμα)	3,75	0,10	2,90	ναι	10.88
T2-07	T2	Τοίχος ντουλάπας χωλ	0,75	0,10	2,90	–	2.17
T2-08	T2	Βόρειος τοίχος Καθιστικού (ανατ. τμήμα)	3,05	0,10	2,90	ναι	8.85
T2-09	T2	Υπν.2 / Χωλ (νότια Θ5)	0,80	0,10	2,90	–	2.32
T2-10	T2	Λουτρό γονέων / ντους έρκερ (βόρεια Θ4)	0,37	0,10	2,90	ναι	1.07
T2-10β	T2	Λαμπάς Θ3	0,10	0,10	2,90	–	0.29
T2-11	T2	Λουτρό γονέων / ντους έρκερ (νότια Θ4)	0,52	0,10	2,90	ναι	1.51
T4-05κ	T4	Καμπύλη ΝΔ γωνία έρκερ λουτρού (μήκος στον άξονα)	0,856	0,11	2,90	–	2.48
T5-01κ	T5	Καμπύλη ΒΑ γωνία επένδυσης πυρήνα (μήκος στον άξονα)	0,314	0,10	2,90	–	0.91
T4-10κ	T4	Καμπύλη ΝΑ προεξοχή κουζίνας (μήκος στον άξονα)	0,730	0,11	2,90	–	2.12
T3-01	T3	Επένδυση T1-01 – Ανατ. παρειά (Υπν.1)	0,39	0,055	2,90	–	1.13
T3-02	T3	Επένδυση T1-03 – Ανατ. παρειά (Υπν.1)	0,45	0,055	2,90	ναι	1.31
T3-03	T3	Επένδυση T1-04 – Νότια παρειά (Υπν.2)	2,85	0,055	2,90	ναι	8.26
T3-04	T3	Επένδυση T1-05 – Δυτ. παρειά (Υπν.2)	0,645	0,055	2,90	ναι	1.87
T3-05	T3	Επένδυση T1-06 – Δυτ. παρειά (Υπν.2)	0,55	0,055	2,90	–	1.59
T3-06	T3	Επένδυση T1-07 – Νότια παρειά (πλατύσκαλο)	1,35	0,055	2,90	–	3.92
T3-07	T3	Επένδυση T1-11 – Δυτ. παρειά (κλιμακοστάσιο)	1,80	0,055	2,90	ναι	5.22
T3-08	T3	Επένδυση T1-12 – Νότια παρειά (κουζίνα) → λαμπάς W2.04	0,27	0,055	2,90	–	0.78
T3-10	T3	Επένδυση T1-15 – Βόρεια παρειά (κουζίνα)	0,27	0,055	2,90	–	0.78
T3-11	T3	Επένδυση T1-14 – Βόρεια παρειά (καθιστικό)	0,15	0,055	2,90	ναι	0.44
T3-12	T3	Επένδυση T1-13 – Βόρεια παρειά (καθιστικό)	0,70	0,055	2,90	ναι	2.03
T3-13	T3	Επένδυση T1-16 – Ανατ. παρειά (καθιστικό)	0,50	0,055	2,90	ναι	1.45

ΚΑΤΟΨΗ ΤΟΙΧΟΠΟΙΙΩΝ – Β΄ ΟΡΟΦΟΣ – ΠΙΝΑΚΑΣ ΑΝΟΙΓΜΑΤΩΝ & ΛΕΠΤΟΜΕΡΕΙΕΣ ΤΥΠΩΝ (φύλλο 3/3, Rev.02)

ΑΝΟΙΓΜΑΤΑ: πλάτη, ποδιές / ύψη, θέσεις λαμπάδων (m από ΒΔ γωνία), φορά πορτών


Κωδ.	Είδος	Πλάτος	Ποδιά / Ύψος	Θέση (λαμπάδες)	Φορά / παρατήρηση
W2.01	παράθυρο	3,50	0,00 / 2,40	y 5,65 → 9,15, τοίχος x 1,40–1,65	ανοιγόμενο/σταθερό κατά πίνακα κουφωμάτων A-50
W2.02	παράθυρο	4,75	0,00 / 2,40	x 4,10 → 8,85, τοίχος y 9,20–9,45	ανοιγόμενο/σταθερό κατά πίνακα κουφωμάτων A-50
W2.03	παράθυρο	2,05	1,00 / 1,50	x 10,70 → 12,75, τοίχος y 10,14–10,25	ανοιγόμενο/σταθερό κατά πίνακα κουφωμάτων A-50
W2.04	παράθυρο	1,35	1,00 / 1,50	y 7,80 → 9,15, τοίχος x 13,62–13,87	ανοιγόμενο/σταθερό κατά πίνακα κουφωμάτων A-50
W2.05	παράθυρο	0,70	0,15 / 1,50	y 5,10 → 5,80, τοίχος x 13,10–13,35	ανοιγόμενο/σταθερό κατά πίνακα κουφωμάτων A-50
W2.06	παράθυρο	1,00	0,00 / 2,40	y 1,45 → 2,45, τοίχος x 9,45–9,70	ανοιγόμενο/σταθερό κατά πίνακα κουφωμάτων A-50
W2.07	παράθυρο	0,60	1,50 / 2,40	x 5,45 → 6,05, τοίχος y 0,50–0,80	άνοιγμα σε τοιχίο K2 – βλ. στατικά
W2.08	παράθυρο	1,50	0,00 / 2,40	y 1,25 → 2,75, τοίχος x 0,80–1,05	ανοιγόμενο/σταθερό κατά πίνακα κουφωμάτων A-50
W2.09	παράθυρο	0,50	1,10 / 2,40	x 0,20 → 0,70, τοίχος y 3,05–3,16	ανοιγόμενο/σταθερό κατά πίνακα κουφωμάτων A-50
Θ1	πόρτα	0,80	– / 2,20	x 3,55 → 4,35, τοίχος y 3,25–3,35	Υπνοδωμάτιο 1 – μεντεσές δυτικά, ανοίγει προς Υπν.1 (βόρεια)
Θ2	πόρτα	0,70	– / 2,20	x 5,60 → 6,30, τοίχος y 3,25–3,35	Λουτρό – μεντεσές ανατολικά, ανοίγει προς λουτρό (βόρεια)
Θ3	πόρτα	0,70	– / 2,20	x 1,20 → 1,90, τοίχος y 3,25–3,35	Λουτρό γονέων – μεντεσές δυτικά, ανοίγει προς λουτρό (νότια)
Θ4	πόρτα	0,80	– / 2,20	y 3,53 → 4,33, τοίχος x 1,00–1,10	Ντους έρκερ – μεντεσές βόρεια, ανοίγει προς λουτρό (ανατολικά)
Θ5	πόρτα	0,80	– / 2,20	y 3,45 → 4,25, τοίχος x 6,40–6,50	Υπνοδωμάτιο 2 – μεντεσές νότια, ανοίγει προς Υπν.2 (ανατολικά)
Θ6	πόρτα	1,00	– / 2,20	y 5,30 → 6,30, τοίχος x 9,45–9,60	ΕΙΣΟΔΟΣ – μεντεσές βόρεια, ανοίγει προς Καθιστικό (δυτικά)
A1	άνοιγμα	0,90	– / –	x 5,45 → 6,35, τοίχος y 5,05–5,15	Άνοιγμα χωλ → Καθιστικό, χωρίς πόρτα

ΖΩΝΕΣ ΤΟΙΧΟΠΟΙΙΑΣ ΠΑΝΩ / ΚΑΤΩ ΑΠΟ ΤΑ ΑΝΟΙΓΜΑΤΑ (πρέκια, ποδιές) – προστίθενται στα καθαρά m²

Κωδ.	Πλάτος m	Ύψος ανοίγμ. m	Ζώνη = πλάτος × (H − ύψος) m²	Σε τύπο	Παρατήρηση
W2.01	3,50	2,40	1.75	T1 + T3	
W2.02	4,75	2,40	2.38	T1 + T3	
W2.03	2,05	0,50	4.92	T4	
W2.04	1,35	0,50	3.24	T1 + T3	
W2.05	0,70	1,35	1.08	T1 + T3	
W2.06	1,00	2,40	0.50	T1 + T3	
W2.07	0,60	0,90	0.00	–	άνοιγμα σε τοιχίο K2 – χωρίς τοιχοποιία
W2.08	1,50	2,40	0.75	T1 + T3	
W2.09	0,50	1,30	0.80	T4	
Θ1	0,80	2,20	0.56	T2	
Θ2	0,70	2,20	0.49	T2	
Θ3	0,70	2,20	0.49	T2	
Θ4	0,80	2,20	0.56	T2	
Θ5	0,80	2,20	0.56	T2	
Θ6	1,00	2,20	0.70	T6	πρέκι ΕΙΣΟΔΟΥ σε γυψοσανίδα T6 (ΠΡΟΣ ΕΠΙΒΕΒΑΙΩΣΗ)
A1	0,90	2,90	0.00	–	άνοιγμα έως δοκό – χωρίς πρέκι (ΠΡΟΣ ΕΠΙΒΕΒΑΙΩΣΗ)


ΛΕΠΤΟΜΕΡΕΙΕΣ ΤΥΠΩΝ ΤΟΙΧΟΠΟΙΙΑΣ – οριζόντιες τομές, κλίμακα 1:5 (πάχη σε cm)

T1 + T3 Εξωτερικός τοίχος με εσωτερική επένδυση

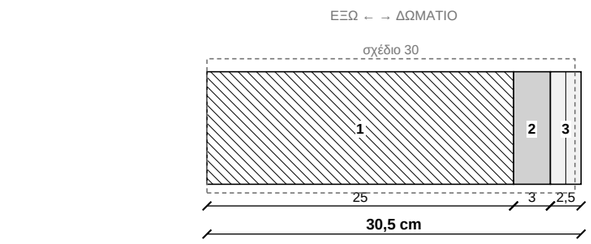


1 τούβλο 25 cm (+εξωτ. επίχρισμα/μόνωση)
2 σκελετός 3 cm
3 διπλή γυψοσανίδα 2×12,5 mm
διακεκ.: πεσσοί αρχιτεκτονικού 30 (εξωτ. παρειά σταθερή)

T2 Τυπικό εσωτερικό χώρισμα

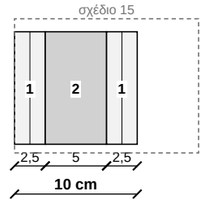


1 διπλή γυψοσανίδα 2×12,5 mm
2 σκελετός 5 cm
διακεκ.: πάχος αρχιτεκτονικού 15

T2A Μόνο T2A-01 (πρώην T2-05)

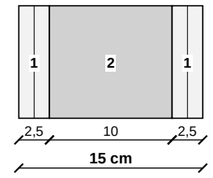


1 διπλή γυψοσανίδα 2×12,5 mm
2 σκελετός 10 cm
παρειές όπως το αρχιτεκτονικό

T4 Τοίχος ERKER

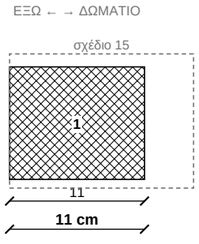


1 απλό τούβλο 11 cm (+επιχρίσματα)
διακεκ.: πάχος αρχιτεκτονικού 15/20
(εξωτερική παρειά σταθερή)

T6 Κλιμακοστάσιο – γυψοσανίδα (ΠΡΟΤΑΣΗ)

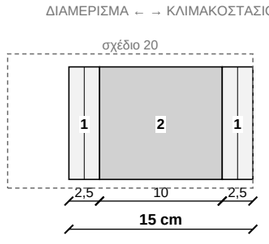

1 διπλή γυψοσανίδα 2×12,5 mm
2 σκελετός 10 cm + πετροβάμβακας
διακεκ.: πάχος αρχιτεκτονικού 20 (παρειά κλιμ/σίου σταθερή)

T7 Τοίχος λεκάνης WC

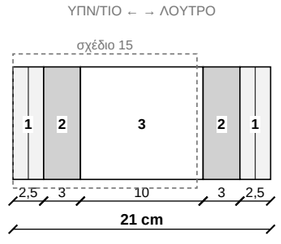

1 διπλή γυψοσανίδα 2×12,5 mm
2 σκελετός 3 cm 3 κενό 10 cm
διακεκ.: πάχος αρχιτεκτονικού 15 (+6 cm προς λουτρό)

ΑΡΓΥΡΟΥΠΟΛΗ – ΚΩΝ/ΠΟΛΕΩΣ 12 & ΑΓ. ΒΑΡΒΑΡΑΣ
ΚΑΤΟΨΗ ΤΟΙΧΟΠΟΙΙΩΝ – Β΄ ΟΡΟΦΟΣ – ανοίγματα / λεπτομέρειες
Βάση: EDGE A-10-2F R00 23/07/2026 – INTERKAT / ARKAD

23/09/2026 Rev. 02 Φύλλο 3/3