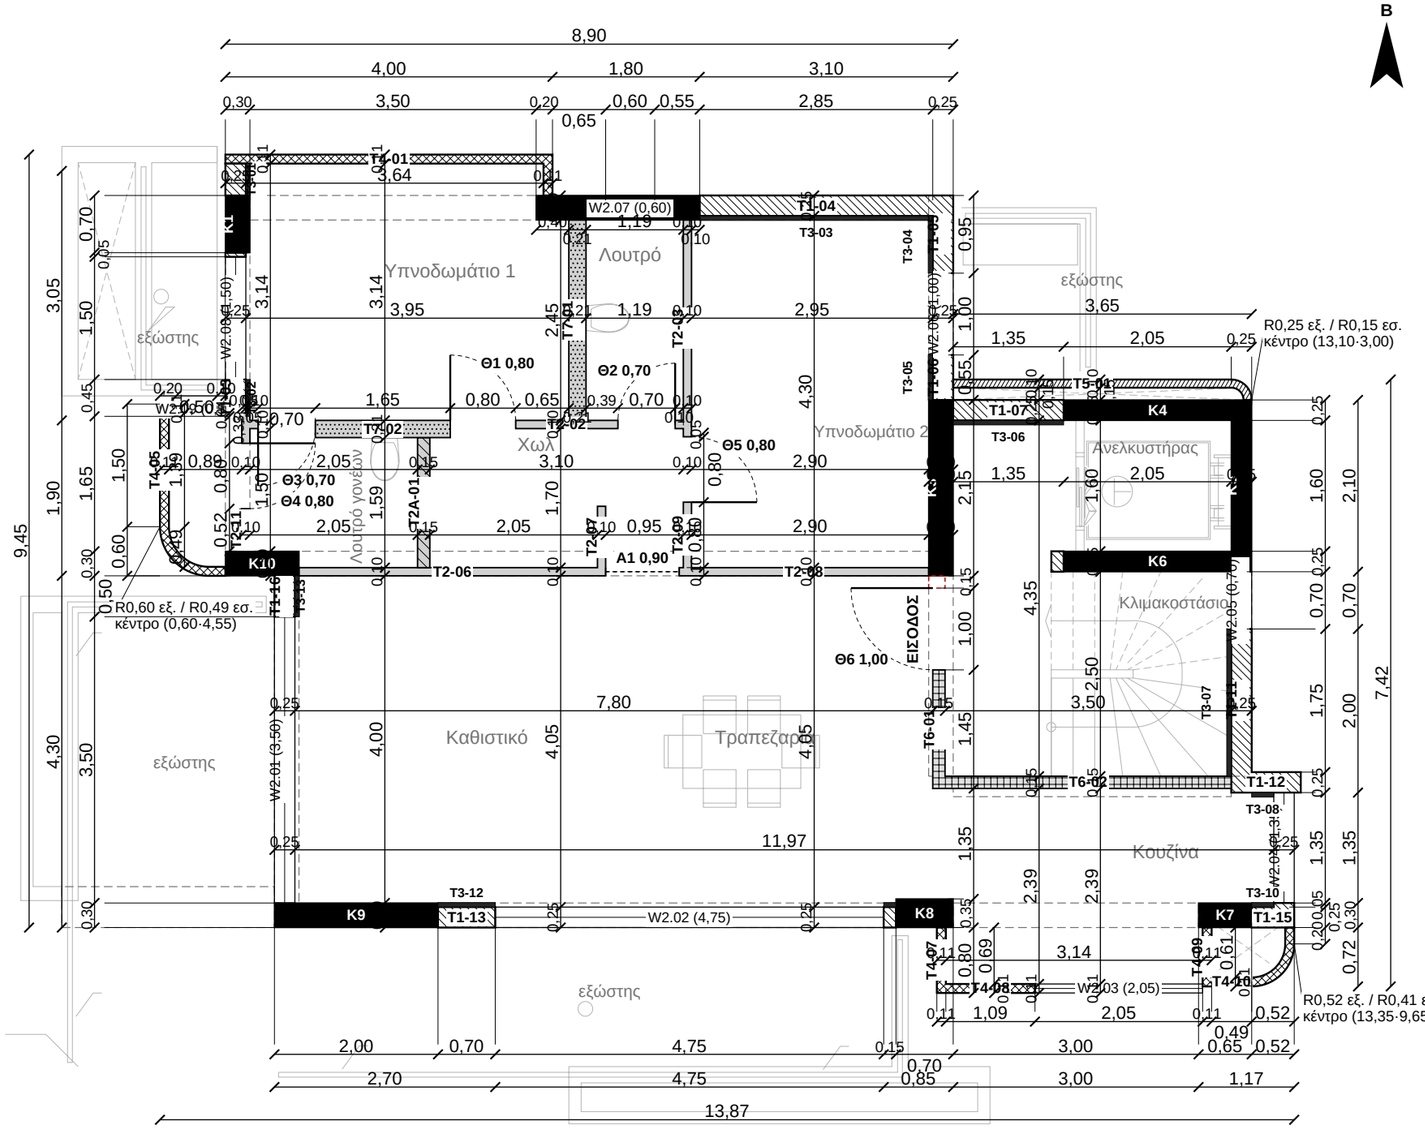


ΥΠΟΜΝΗΜΑ ΤΟΙΧΟΠΟΙΙΩΝ

- T1 – Εξωτερική: τούβλο 25 cm + εσωτερική επένδυση T3 (τελικό 30,5 cm)
- T3 – Επένδυση T1: σκελετός 3 cm + διπλή γυψοσανίδα (5,5 cm)
- T2 – Εσωτερικό χώρισμα: σκελετός 5 cm + διπλή γυψοσανίδα εκατέρωθεν (10 cm)
- T2A – Σκελετός 10 cm + διπλή γυψοσανίδα εκατέρωθεν (15 cm) – μόνο T2A-01
- T4 – ERKER: απλό τούβλο 11 cm
- T5 – Τούβλο 10 cm περιμετρικά πυρήνα (ως αρχιτεκτονικό)
- T6 – Κλιμακοστάσιο: γυψοσανίδα 15 cm (πρόταση σύνθεσης – προς καθορισμό)
- T7 – Τοίχος λεκάνης WC: σκελ. 3 + 2×γυψ. / κενό 10 / σκελ. 3 + 2×γυψ. (21 cm)
- Οπλισμένο σκυρόδεμα K1–K10 (ως έχει, στατικά Κόγια)
- Δοκός οροφής (προβολή άνωθεν, από αρχιτεκτονικό)
- Παράθυρο / πόρτα (φύλλο + τόξο ανοίγματος)
- Στοιχείο προς επιβεβαίωση

Διαστάσεις σε m, μετρημένες σε παρειές τούβλου / σκελετού / σκυροδέματος, χωρίς επιχρίσματα, θερμομόνωση και επενδύσεις. Οι τοίχοι σχεδιάζονται με τα πάχη της προδιαγραφής. Θέσεις τοίχων, ανοιγμάτων και υποστυλωμάτων ακριβώς κατά EDGE A-10-2F. Ποσότητες, τύποι και ανοίγματα: βλ. φύλλο 2.

ΑΡΓΥΡΟΥΠΟΛΗ – ΚΩΝΣΤΑΝΤΙΝΟΥΠΟΛΕΩΣ 12 & ΑΓ. ΒΑΡΒΑΡΑΣ

Ο.Τ. 103-15 – Πενταόροφο κτήριο κατοικιών – INTERKAT Α.Ε. / ARKAD Ι.Κ.Ε.

ΚΑΤΟΨΗ ΤΟΙΧΟΠΟΙΙΩΝ – Β΄ ΟΡΟΦΟΣ

Τύποι τοιχοποιίας, πάχη και θέσεις ανοιγμάτων – φύλλο 2: τύποι & ποσότητες (m²), φύλλο 3: ανοίγματα

Βάση: EDGE Μελέτη Εφαρμογής Α-10-2F R00 (23/07/2026) – στατικά Γ. Κόγιας Σ5/Σ6
Προδιαγραφή τοίχων Γ. Ζαρκαδάς 09/2026 – Rev.02 (πραγματικά πάχη)

Κλίμακα 1:75 (A3) – διαστάσεις σε m 23/09/2026 **Φύλλο 1/3 Rev. 02**