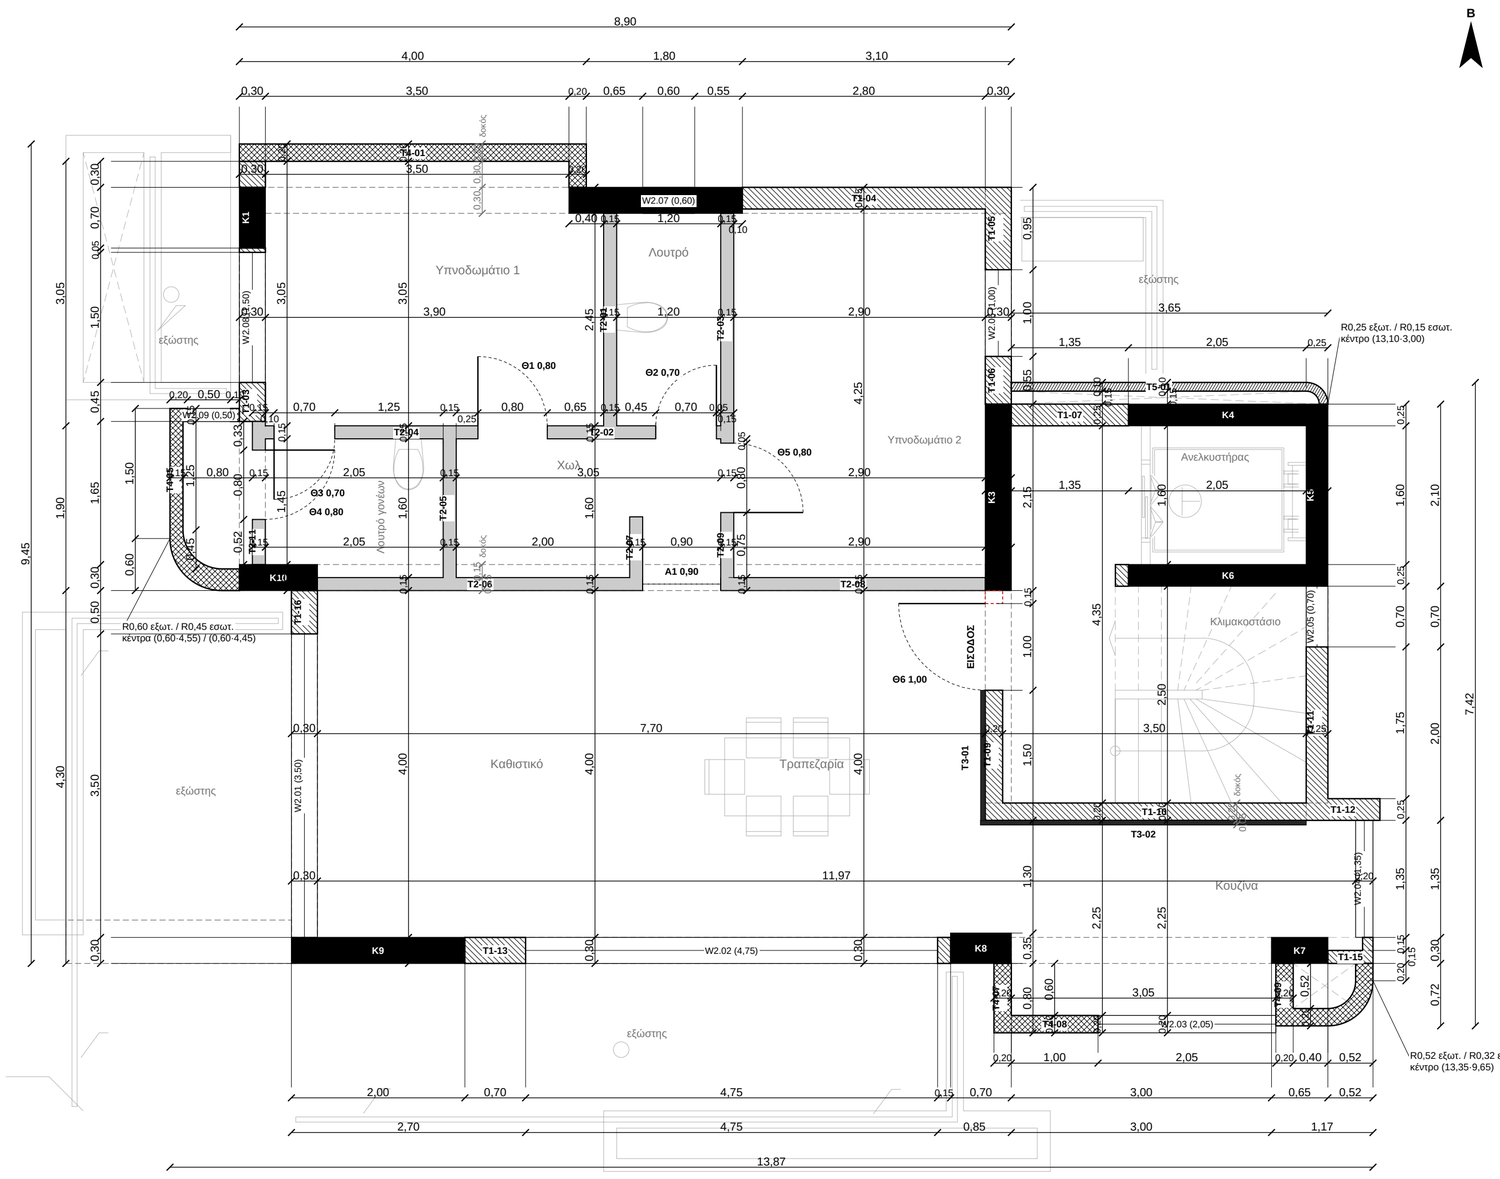


ΥΠΟΜΝΗΜΑ ΤΟΙΧΟΠΟΙΙΩΝ

- T1 – ΤΟΥΒΛΟ 25 cm
- T2 – ΣΚΕΛΕΤΟΣ 7,5 cm + ΔΙΠΛΗ ΓΥΨΟΣΑΝΙΔΑ ΕΚΑΤΕΡΩΘΕΝ (12,5 cm)
- T3 – ΣΚΕΛΕΤΟΣ 3 cm + ΔΙΠΛΗ ΓΥΨΟΣΑΝΙΔΑ (5,5 cm)
- T4 – ERKER – ΤΟΥΒΛΟ 11 cm
- T5 – ΤΟΥΒΛΟ 10 cm (ως σχέδιο, περιμετρικά πυρήνα)
- ΟΠΛΙΣΜΕΝΟ ΣΚΥΡΟΔΕΜΑ K1–K10 (ως έχει, στατικά Κόγια)
- ΔΟΚΟΣ ΟΡΟΦΗΣ (προβολή άνωθεν, από αρχιτεκτονικό)
- ΠΑΡΑΘΥΡΟ / ΠΟΡΤΑ (φύλλο + τόξο ανοίγματος)
- ΣΤΟΙΧΕΙΟ ΠΡΟΣ ΕΠΙΒΕΒΑΙΩΣΗ

ΠΙΝΑΚΑΣ ΤΥΠΩΝ ΤΟΙΧΟΠΟΙΙΑΣ

Κωδ.	Περιγραφή	Υλικά	Πάχος σκελ./τούβλου	Γυψοσανίδα	Τελικό πάχος	Στο σχέδιο EDGE / παρατήρηση
T1	Εξωτερική τοιχοποιία (και τοίχοι προς κλιμακοστάσιο)	Οπτοπλινθοδομή, τούβλο 25 cm, επιχρίσματα εκατέρωθεν	25 cm	–	25 cm (+επιχρ.)	Σχεδιάζεται 20 / 25 / 30 cm + εξωτ. θερμομόνωση – ΠΡΟΣ ΕΠΙΒΕΒΑΙΩΣΗ (βλ. σημ. 2)
T2	Εσωτερικά χωρίσματα	Μεταλλικός σκελετός 7,5 cm + διπλή γυψοσανίδα 2×12,5 mm σε κάθε πλευρά	7,5 cm	2×12,5 mm ανά πλευρά (2,5 cm)	12,5 cm	Σχεδιάζεται 15 cm. Χάραξη στον άξονα του σχεδιασμένου τοίχου (−1,25 cm ανά παρειά)
T3	Επένδυση εσωτερικής τοιχοποιίας από τούβλο	Μεταλλικός σκελετός 3 cm + διπλή γυψοσανίδα 2×12,5 mm (μία πλευρά)	3 cm	2×12,5 mm (2,5 cm)	5,5 cm	Στην πλευρά διαμερίσματος των τοίχων T1-09, T1-10 (προς κλιμακοστάσιο)
T4	Τοιχοποιία ERKER (προεξοχές εκτός αξόνων δοκών)	Οπτοπλινθοδομή, απλό τούβλο 11 cm, επιχρίσματα	11 cm	–	11 cm (+επιχρ.)	Σχεδιάζεται 15 cm (δυτ. έρκερ) / 20 cm (βόρειο, κουζίνα) – ΠΡΟΣ ΕΠΙΒΕΒΑΙΩΣΗ (βλ. σημ. 3)
T5	Τοίχος 10 cm περιμετρικά πυρήνα ανελκυστήρα (εκτός Σ.Δ.)	Απλό τούβλο 10 cm, ως αρχιτεκτονικό	10 cm	–	10 cm	Εκτός προδιαγραφής T1–T4 – ΠΡΟΣ ΕΠΙΒΕΒΑΙΩΣΗ τύπου/πάχους

ΠΙΝΑΚΑΣ ΑΝΟΙΓΜΑΤΩΝ (πλάτη / θέσεις / φορά)

Κωδ.	Είδος	Πλάτος	Ποδιά / Ύψος	Θέση (λαμπάδες)	Φορά / παρατήρηση
W2.01	παράθυρο	3,50	0,00 / 2,40	y 5,65 → 9,15, τοίχος x 1,40–1,70	ανοιγόμενο/σταθερό κατά πίνακα κουφωμάτων A-50
W2.02	παράθυρο	4,75	0,00 / 2,40	x 4,10 → 8,85, τοίχος y 9,15–9,45	ανοιγόμενο/σταθερό κατά πίνακα κουφωμάτων A-50
W2.03	παράθυρο	2,05	1,00 / 1,50	x 10,70 → 12,75, τοίχος y 10,05–10,25	ανοιγόμενο/σταθερό κατά πίνακα κουφωμάτων A-50
W2.04	παράθυρο	1,35	1,00 / 1,50	y 7,80 → 9,15, τοίχος x 13,67–13,87	ανοιγόμενο/σταθερό κατά πίνακα κουφωμάτων A-50
W2.05	παράθυρο	0,70	0,15 / 1,50	y 5,10 → 5,80, τοίχος x 13,10–13,35	ανοιγόμενο/σταθερό κατά πίνακα κουφωμάτων A-50
W2.06	παράθυρο	1,00	0,00 / 2,40	y 1,45 → 2,45, τοίχος x 9,40–9,70	ανοιγόμενο/σταθερό κατά πίνακα κουφωμάτων A-50
W2.07	παράθυρο	0,60	1,50 / 2,40	x 5,45 → 6,05, τοίχος y 0,50–0,80	άνοιγμα σε τοιχίο K2 – βλ. στατικά
W2.08	παράθυρο	1,50	0,00 / 2,40	y 1,25 → 2,75, τοίχος x 0,80–1,10	ανοιγόμενο/σταθερό κατά πίνακα κουφωμάτων A-50
W2.09	παράθυρο	0,50	1,10 / 2,40	x 0,20 → 0,70, τοίχος y 3,05–3,20	ανοιγόμενο/σταθερό κατά πίνακα κουφωμάτων A-50
Θ1	πόρτα	0,80	– / 2,20	y 3,55 → 4,35, τοίχος y 3,25–3,40	Υπνοδωμάτιο 1 – μεντεσές δυτικά, ανοίγει προς Υπν.1 (βόρεια)
Θ2	πόρτα	0,70	– / 2,20	x 5,60 → 6,30, τοίχος y 3,25–3,40	Λουτρό – μεντεσές ανατολικά, ανοίγει προς λουτρό (βόρεια)
Θ3	πόρτα	0,70	– / 2,20	x 1,20 → 1,90, τοίχος y 3,25–3,40	Λουτρό γονέων – μεντεσές δυτικά, ανοίγει προς λουτρό (νότια)
Θ4	πόρτα	0,80	– / 2,20	y 3,53 → 4,33, τοίχος x 0,95–1,10	Ντους έρκερ – μεντεσές βόρεια, ανοίγει προς λουτρό (ανατολικά)
Θ5	πόρτα	0,80	– / 2,20	y 3,45 → 4,25, τοίχος x 6,35–6,50	Υπνοδωμάτιο 2 – μεντεσές νότια, ανοίγει προς Υπν.2 (ανατολικά)
Θ6	πόρτα	1,00	– / 2,20	y 5,30 → 6,30, τοίχος x 9,40–9,60	ΕΙΣΟΔΟΣ – μεντεσές βόρεια, ανοίγει προς Καθιστικό (δυτικά)
A1	άνοιγμα	0,90	– / –	x 5,45 → 6,35, τοίχος y 5,00–5,15	Άνοιγμα χωλ → Καθιστικό, χωρίς πόρτα

ΣΗΜΕΙΩΣΕΙΣ

1. Όλες οι διαστάσεις σε μέτρα (m), όπως το αρχιτεκτονικό, μετρημένες σε παρειές τούβλου / σκυροδέματος ΧΩΡΙΣ επιχρίσματα και θερμομόνωση. Αρχή συντεταγμένων (0,00·0,00) = εξωτερική (βόρεια) παρειά τοίχου T4-01 και εξωτερική (δυτική) παρειά τοίχου T4-05.

2. T1: η προδιαγραφή ορίζει τούβλο 25 cm. Στο αρχιτεκτονικό A-10-2F οι εξωτερικοί τοίχοι σχεδιάζονται 20 cm (T1-09/10, βόρειος Υπν.1), 25 cm (T1-04, T1-07, T1-11) και 30 cm (πεσσοί), με εξωτερική θερμομόνωση ώστε το σύνολο να είναι ≈30 cm. Οι διαστάσεις του σχεδίου κρατούν τις σχεδιασμένες παρειές. Αν χτιστεί τούβλο 25 σε θέση 20 cm, μετακινείται η εσωτερική παρειά κατά 5 cm ή αλλάζει το πάχος μόνωσης – ΠΡΟΣ ΕΠΙΒΕΒΑΙΩΣΗ με EDGE πριν τη χάραξη.

3. T4: ως έρκερ ελήφθησαν οι τοίχοι έξω από τους άξονες των δοκών: βόρεια προεξοχή Υπν.1 (0,50 m πρόβολος από K1/K2), δυτικός κόλπος λουτρού με καμπύλη, δύο νότιες προεξοχές κουζίνας. Σχεδιάζονται 15 και 20 cm, η προδιαγραφή λέει 11 cm – ΠΡΟΣ ΕΠΙΒΕΒΑΙΩΣΗ. Οι εξωτερικές παρειές (γραμμές χάραξης) κρατούν τις θέσεις του σχεδίου.

4. T2: τελικό πάχος 12,5 cm (7,5 + 2×2,5). Στο σχέδιο τα χωρίσματα σχεδιάζονται 0,15. Χάραξη: ο άξονας του T2 ταυτίζεται με τον άξονα του σχεδιασμένου τοίχου 0,15 (διαφορά 1,25 cm ανά παρειά). Ο βόρειος τοίχος καθιστικού (T2-06/08) ευθυγραμμίζεται με τη νότια παρειά της δοκού (y=5,15).

5. T3: επένδυση 5,5 cm στην πλευρά διαμερίσματος των τοίχων προς κλιμακοστάσιο (T1-09 δυτική παρειά, T1-10 νότια παρειά). Οι παρειές του σκυροδέματος (K3, πυρήνας) δεν επενδύονται – επιχρίσματα κατά αρχιτεκτονικό.

6. Οι δύο νότιες προεξοχές κουζίνας δεν είναι στην ίδια γραμμή: νότια παρειά ΝΔ προεξοχής y=10,25, ΝΑ προεξοχής y=10,17 (διαφορά 8 cm, ως σχέδιο) – ΠΡΟΣ ΕΠΙΒΕΒΑΙΩΣΗ. Το στοιχείο 0,15 κάτω από K3 (y 5,15–5,30, δίπλα στην ΕΙΣΟΔΟ) δεν έχει διαγράμμιση τοιχοποίας στο αρχιτεκτονικό – ΠΡΟΣ ΕΠΙΒΕΒΑΙΩΣΗ.

7. Υποστυλώματα K1–K10 όπως σχεδιάζονται στο A-10-2F (ταυτίζονται με Σ3/Σ5 Κόγια). Το K8 σχεδιάζεται 0,70×0,35 (στατικά 70/30). Καμία μετακίνηση φέροντος στοιχείου. Το W2.07 (0,60) είναι άνοιγμα μέσα στο τοιχίο K2 – αφορά τα στατικά, όχι την τοιχοποιία.

8. Πόρτες: φορά ανοίγματος όπως το τόξο στην κάτοψη (μεντεσές στην αρχή του φύλλου). Ύψη ανοιγμάτων πορτών 2,20. Κουφώματα κατά πίνακα A-50. Οι μετρήσεις επιβεβαιώνονται στο εργοτάξιο (σημ. 1 A-10-2F) – κάθε απόκλιση > 2 cm αναφέρεται πριν τη χάραξη.

ΠΙΝΑΚΑΣ ΤΟΙΧΩΝ (χάραξη: συντεταγμένες παρειών από την αρχή 0,00·0,00 – βλ. σημ. 1)

Κωδ.	Τύπ.	Θέση / περιγραφή	Από x ; y	Έως x ; y	Μήκος	Πάχος
T4-01	T4	Βόρειος τοίχος έρκερ Υπν.1	0,80 ; 0,00	4,80 ; 0,20	4,00	0,20
T4-02	T4	Ανατ. επιστροφή έρκερ Υπν.1 (πάνω από K2)	4,60 ; 0,20	4,80 ; 0,50	0,30	0,20
T4-03	T4	Βόρειος τοίχος δυτ. έρκερ (δυτ. λαμπάς W2.09)	0,00 ; 3,05	0,20 ; 3,20	0,20	0,15
T4-04	T4	Βόρειος τοίχος δυτ. έρκερ (ανατ. λαμπάς W2.09)	0,70 ; 3,05	0,80 ; 3,20	0,15	0,10
T4-05	T4	Δυτικός τοίχος έρκερ λουτρού (ευθύγραμμο τμήμα)	0,00 ; 3,20	0,15 ; 4,55	1,35	0,15
T4-06	T4	Νότια επιστροφή έρκερ λουτρού → K10	0,60 ; 4,90	0,80 ; 5,15	0,25	0,20
T4-07	T4	Δυτικός τοίχος ΝΔ προεξοχής κουζίνας	9,50 ; 9,45	9,70 ; 10,25	0,80	0,20
T4-08	T4	Νότιος τοίχος ΝΔ προεξοχής κουζίνας	9,70 ; 10,05	10,70 ; 10,25	1,00	0,20
T4-09	T4	Δυτικός τοίχος ΝΑ προεξοχής κουζίνας	12,75 ; 9,45	12,95 ; 10,17	0,72	0,20
T4-10	T4	Νότιος τοίχος ΝΑ προεξοχής (ευθύγρ. τμήμα)	12,95 ; 9,97	13,35 ; 10,17	0,40	0,20
T4-11	T4	Ανατ. τοίχος ΝΑ προεξοχής (ευθύγρ. τμήμα)	13,67 ; 9,45	13,87 ; 9,65	0,20	0,20
T1-01	T1	Πεσσός ΒΔ πάνω από K1	0,80 ; 0,20	1,10 ; 0,50	0,30	0,30
T1-02	T1	Λωρίδα K1 → W2.08	0,80 ; 1,20	1,10 ; 1,25	0,30	0,05
T1-03	T1	Πεσσός δυτ. Υπν.1 (W2.08 → λουτρό)	0,80 ; 2,75	1,10 ; 3,20	0,45	0,30
T1-04	T1	Βόρειος τοίχος Υπν.2 (K2 → πεσσός)	6,60 ; 0,50	9,40 ; 0,75	2,80	0,25
T1-05	T1	ΒΑ πεσσός Υπν.2 (→ W2.06)	9,40 ; 0,50	9,70 ; 1,45	0,95	0,30
T1-06	T1	Πεσσός W2.06 → K3	9,40 ; 2,45	9,70 ; 3,00	0,55	0,30
T1-07	T1	Βόρειος τοίχος πλατύσκαλου K3 → K4	9,70 ; 3,00	11,05 ; 3,25	1,35	0,25
T1-08	T1	Λαμπάς δυτικά K6	10,90 ; 4,85	11,05 ; 5,10	0,25	0,15
T1-09	T1	Δυτ. τοίχος κλιμακοστασίου (ΕΙΣΟΔΟΣ → νότιος)	9,40 ; 6,30	9,60 ; 7,80	1,50	0,20
T1-10	T1	Νότιος τοίχος κλιμακοστασίου (→ κουζίνα)	9,60 ; 7,60	13,10 ; 7,80	3,50	0,20
T1-11	T1	Ανατ. τοίχος κλιμακοστασίου (W2.05 → γωνία)	13,10 ; 5,80	13,35 ; 7,55	1,75	0,25
T1-12	T1	ΝΑ γωνιακό τμήμα κλιμακοστασίου	13,10 ; 7,55	13,95 ; 7,80	0,85	0,25
T1-13	T1	Πεσσός νότιος K9 → W2.02	3,40 ; 9,15	4,10 ; 9,45	0,70	0,30

Κωδ.	Τύπ.	Θέση / περιγραφή	Από x ; y	Έως x ; y	Μήκος	Πάχος
T1-14	T1	Λαμπάς W2.02 → K8	8,85 ; 9,15	9,00 ; 9,45	0,30	0,15
T1-15	T1	ΝΑ γωνιακός πεσσός (K7 → προεξοχή), νότιο τμήμα	13,35 ; 9,30	13,87 ; 9,45	0,52	0,15
T1-15β	T1	ΝΑ γωνιακός πεσσός, βόρειο τμήμα 0,12 (λαμπάς W2.04)	13,75 ; 9,15	13,87 ; 9,30	0,15	0,12
T1-16	T1	Πεσσός K10 → W2.01	1,40 ; 5,15	1,70 ; 5,65	0,50	0,30
T5-01	T5	Επένδυση 0,10 βόρεια πυρήνα (K3 → καμπύλη)	9,70 ; 2,75	13,10 ; 2,85	3,40	0,10
T2-01	T2	Υπν.1 / Λουτρό	5,00 ; 0,80	5,15 ; 3,25	2,45	0,15
T2-02	T2	Νότιος τοίχος Λουτρού (μεταξύ Θ1 και Θ2)	4,35 ; 3,25	5,60 ; 3,40	1,25	0,15
T2-03	T2	Λουτρό / Υπν.2	6,35 ; 0,80	6,50 ; 3,45	2,65	0,15
T2-03β	T2	Λαμπάς Θ2 (προεξοχή 0,05)	6,30 ; 3,25	6,35 ; 3,40	0,15	0,05
T2-04	T2	Υπν.1 / Λουτρό γονέων (Θ3 → Θ1)	1,90 ; 3,25	3,55 ; 3,40	1,65	0,15
T2-05	T2	Λουτρό γονέων / Χωλ	3,15 ; 3,40	3,30 ; 5,00	1,60	0,15
T2-06	T2	Βόρειος τοίχος Καθιστικού (δυτ. τμήμα)	1,70 ; 5,00	5,45 ; 5,15	3,75	0,15
T2-07	T2	Τοίχος ντουλάπας χωλ	5,30 ; 4,30	5,45 ; 5,00	0,70	0,15
T2-08	T2	Βόρειος τοίχος Καθιστικού (ανατ. τμήμα)	6,35 ; 5,00	9,40 ; 5,15	3,05	0,15
T2-09	T2	Υπν.2 / Χωλ (νότια Θ5)	6,35 ; 4,25	6,50 ; 5,00	0,75	0,15
T2-10	T2	Λουτρό γονέων / ντους έρκερ (βόρεια Θ4)	0,95 ; 3,20	1,10 ; 3,53	0,33	0,15
T2-10β	T2	Λαμπάς Θ3	1,10 ; 3,25	1,20 ; 3,40	0,15	0,10
T2-11	T2	Λουτρό γονέων / ντους έρκερ (νότια Θ4)	0,95 ; 4,33	1,10 ; 4,85	0,52	0,15
T4-05κ	T4	Καμπύλη ΝΔ γωνία έρκερ λουτρού (μήκος εξωτ. τόξου)	κ. 0,60 ; 4,55	R 0,60 / 0,45	0,94	0,15
T5-01κ	T5	Καμπύλη ΒΑ γωνία επένδυσης πυρήνα (μήκος εξωτ. τόξου)	κ. 13,10 ; 3,00	R 0,25 / 0,15	0,39	0,10
T4-10κ	T4	Καμπύλη ΝΑ προεξοχή κουζίνας (μήκος εξωτ. τόξου)	κ. 13,35 ; 9,65	R 0,52 / 0,32	0,82	0,20
T3-01	T3	Επένδυση δυτ. τοίχου κλιμακοστασίου (πλευρά Καθιστικού)	9,35 ; 6,30	9,40 ; 7,86	1,56	0,055
T3-02	T3	Επένδυση νότιου τοίχου κλιμακοστασίου (πλευρά Κουζίνας)	9,35 ; 7,80	13,10 ; 7,86	3,75	0,055

Σύνολα μήκους ανά τύπο (m): T1 = 16,72 T2 = 19,00 T3 = 5,31 T4 = 11,13 T5 = 3,79 (μήκη σε παρειές, χωρίς αφαίρεση ανοιγμάτων)

ΑΡΓΥΡΟΥΠΟΛΗ – ΚΩΝΣΤΑΝΤΙΝΟΥΠΟΛΕΩΣ 12 & ΑΓ. ΒΑΡΒΑΡΑΣ (Ο.Τ. 103-15)

Πενταόροφο κτήριο κατοικιών με υπόγειο, σοφίτα και δώμα – INTERKAT A.E. / ARKAD I.K.E.

ΣΧΕΔΙΟ ΧΑΡΑΞΗΣ ΤΟΙΧΟΠΟΙΙΩΝ – ΚΑΤΟΨΗ Β΄ ΟΡΟΦΟΥ

Φύλλο 1/1: κάτοψη 1:50 με πλήρη διαστασιολόγηση, υπόμνημα, πίνακες τύπων / ανοιγμάτων / τοίχων, σημειώσεις

Βάση: EDGE, Μελέτη Εφαρμογής A-10-2F «Κάτοψη Β΄ ορόφου» R00, 23/07/2026, 1:50 – γεωμετρία διανυσματικά από το PDF

Προδιαγραφή τοίχων T1–T4: Γ. Ζαρκαδάς (09/2026). Οι θέσεις ΠΡΟΣ ΕΠΙΒΕΒΑΙΩΣΗ επιβεβαιώνονται από EDGE πριν τη χάραξη.

Κλίμακα 1:50 (A2) – διαστάσεις σε m Ημερομηνία 21/09/2026 **Φύλλο 1/1 Rev. 00**