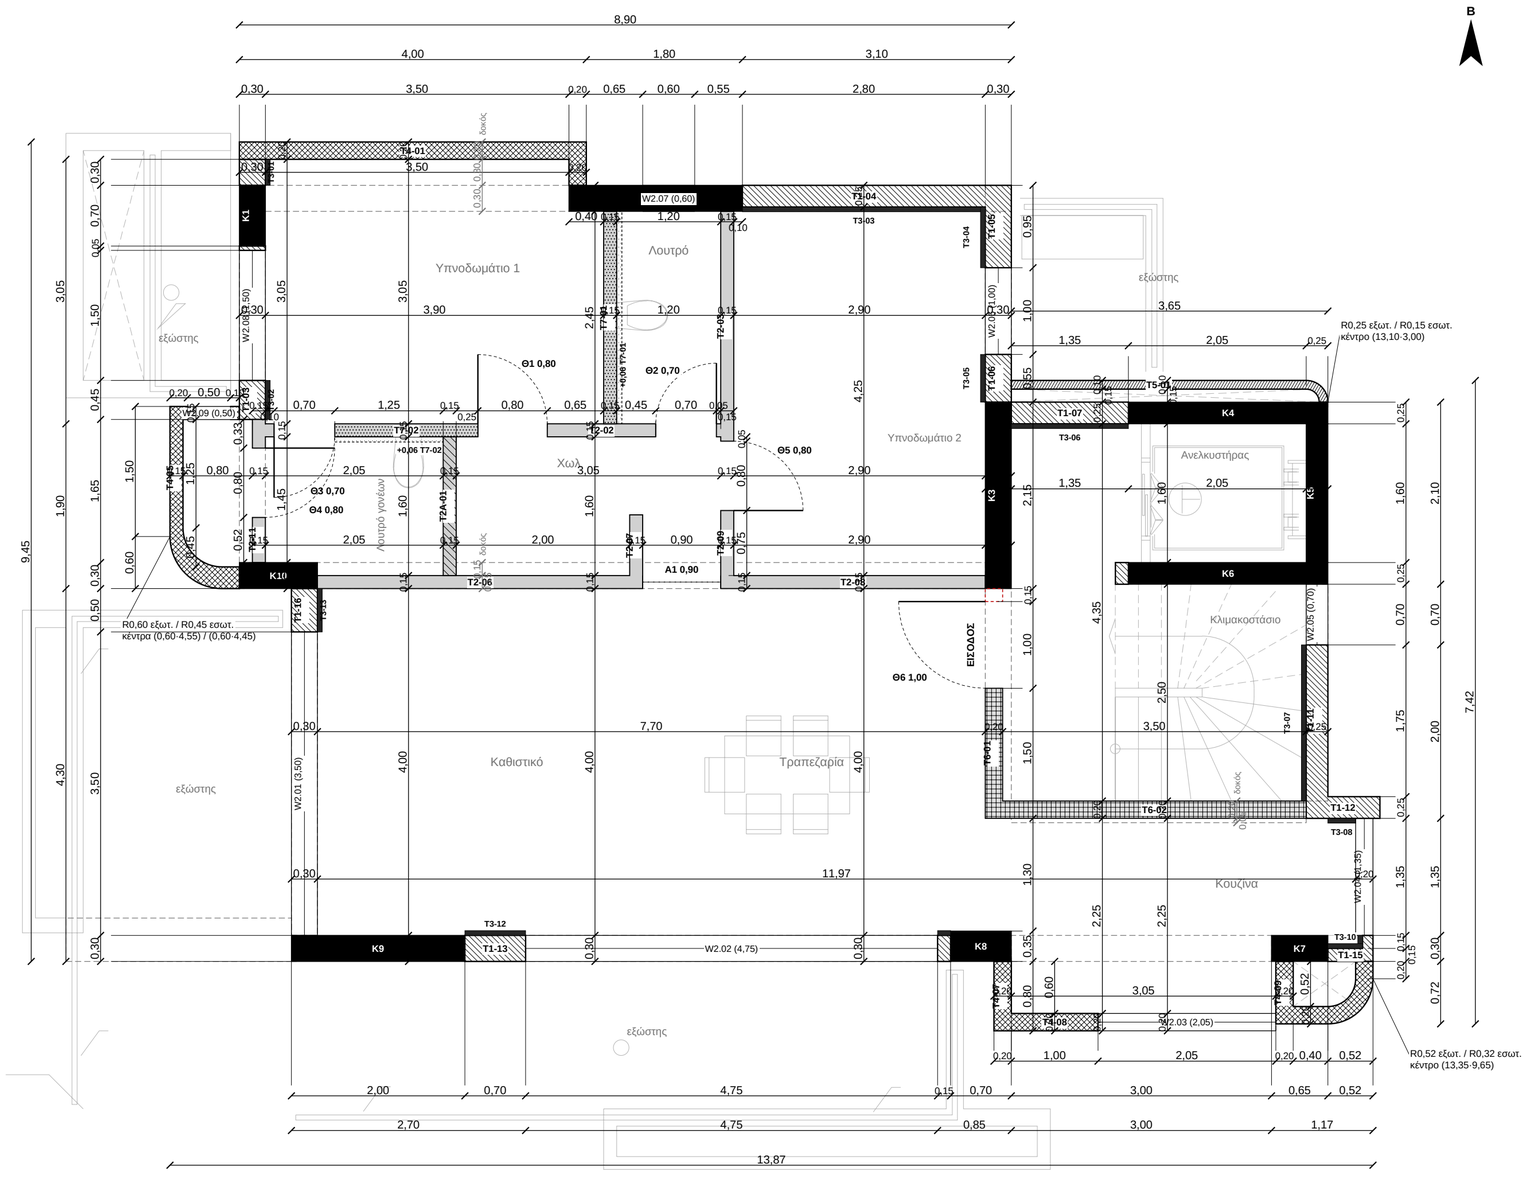


ΥΠΟΜΝΗΜΑ ΤΟΙΧΟΠΟΙΙΩΝ

- T1 – ΕΞΩΤΕΡΙΚΗ: ΤΟΥΒΛΟ 25 cm + ΕΣΩΤ. ΕΠΕΝΔΥΣΗ Τ3 (30,5 cm)
- T3 – ΕΠΕΝΔΥΣΗ Τ1: ΣΚΕΛΕΤΟΣ 3 cm + ΔΙΠΛΗ ΓΥΨΟΣΑΝΙΔΑ (5,5 cm)
- T2 – ΕΣΩΤΕΡΙΚΟ: ΣΚΕΛΕΤΟΣ 5 cm + ΔΙΠΛΗ ΓΥΨΟΣΑΝΙΔΑ ΕΚΑΤΕΡΩΘΕΝ (10 cm)
- T2A – ΣΚΕΛΕΤΟΣ 10 cm + ΔΙΠΛΗ ΓΥΨΟΣΑΝΙΔΑ ΕΚΑΤΕΡΩΘΕΝ (15 cm) – μόνο T2A-01
- T4 – ERKER – ΑΠΛΟ ΤΟΥΒΛΟ 11 cm
- T5 – ΤΟΥΒΛΟ 10 cm (ως σχέδιο, περιμετρικά πυρήνα)
- T6 – ΚΛΙΜΑΚΟΣΤΑΣΙΟ: ΓΥΨΟΣΑΝΙΔΑ (σύνθεση προς καθορισμό, σχεδ. 20 cm)
- T7 – ΤΟΙΧΟΣ WC: ΣΚΕΛ. 3 + 2×ΓΥΨ. + ΚΕΝΟ 10 + ΣΚΕΛ. 3 + 2×ΓΥΨ. (21 cm)
- T7 – ΠΡΟΣΘΕΤΟ ΠΑΧΟΣ +6 cm ΠΡΟΣ ΛΟΥΤΡΟ (21 αντί 15) – ΠΡΟΣ ΕΠΙΒΕΒΑΙΩΣΗ
- ΟΠΛΙΣΜΕΝΟ ΣΚΥΡΟΔΕΜΑ K1–K10 (ως έχει, στατικά Κόγια)
- ΔΟΚΟΣ ΟΡΟΦΗΣ (προβολή άνωθεν, από αρχιτεκτονικό)
- ΠΑΡΑΘΥΡΟ / ΠΟΡΤΑ (φύλλο + τόξο ανοίγματος)
- ΣΤΟΙΧΕΙΟ ΠΡΟΣ ΕΠΙΒΕΒΑΙΩΣΗ

ΠΙΝΑΚΑΣ ΤΥΠΩΝ ΤΟΙΧΟΠΟΙΙΑΣ (Rev.01)

Κωδ.	Περιγραφή / θέση	Υλικά – σύνθεση	Σκελετός / τούβλο	Γυψοσανίδα	Τελικό πάχος	Στο σχέδιο EDGE / παρατήρηση
T1	Εξωτερική τοιχοποιία (περίμετρος κτηρίου, πρόσοψη κλιμακοστασίου)	Οπτοπλινθοδομή, τούβλο 25 cm + εσωτερική επένδυση Τ3 (σκελετός 3 cm + διπλή γυψοσανίδα)	25 cm	εσωτ. 2×12,5 mm (μέσω Τ3)	25 + 5,5 = 30,5 cm (+εξωτ. επιχρ./μόνωση)	Σχεδιάζεται 25 cm (T1-04/07/08/11/12) και 30 cm (πεσσοί σε ευθυγράμμιση με υποστυλώματα) + εξωτ. μόνωση – ΠΡΟΣ ΕΠΙΒΕΒΑΙΩΣΗ (σημ. 2)
T3	Εσωτερική επένδυση όλων των T1 (λωρίδες T3-01…T3-13)	Μεταλλικός σκελετός 3 cm + διπλή γυψοσανίδα 2×12,5 mm (μία πλευρά)	3 cm	2×12,5 mm (2,5 cm)	5,5 cm	Στην παρειά δωματίου κάθε T1. Συνέχεια μπροστά από υποστυλώματα και στους T4: ΠΡΟΣ ΕΠΙΒΕΒΑΙΩΣΗ (σημ. 2)
T2	Τυπικά εσωτερικά χωρίσματα	Μεταλλικός σκελετός 5 cm + διπλή γυψοσανίδα 2×12,5 mm σε κάθε πλευρά	5 cm	2×12,5 mm ανά πλευρά (2,5 cm)	10 cm	Σχεδιάζεται 15 cm. Χάραξη στον άξονα του σχεδιασμένου τοίχου (−2,5 cm ανά παρειά) (σημ. 4)
T2A	Μόνο T2A-01: Λουτρό γονέων / Χωλ (πρώην T2-05)	Μεταλλικός σκελετός 10 cm + διπλή γυψοσανίδα 2×12,5 mm σε κάθε πλευρά	10 cm	2×12,5 mm ανά πλευρά (2,5 cm)	15 cm	Παρειές ακριβώς ως σχέδιο (x 3,15 / 3,30) – δεν τροποποιείται
T4	Τοιχοποιία ERKER (προεξοχές εκτός αξόνων δοκών)	Οπτοπλινθοδομή, απλό τούβλο 11 cm, επιχρίσματα	11 cm	–	11 cm (+επιχρ.)	Σχεδιάζεται 15 cm (δυτ. έρκερ) / 20 cm (βόρειο, κουζίνα) – ΠΡΟΣ ΕΠΙΒΕΒΑΙΩΣΗ (σημ. 3)
T5	Τοίχος 10 cm περιμετρικά πυρήνα ανελκυστήρα (ως σχέδιο)	Απλό τούβλο 10 cm, ως αρχιτεκτονικό	10 cm	–	10 cm	Εκτός προδιαγραφής – ΠΡΟΣ ΕΠΙΒΕΒΑΙΩΣΗ τύπου/πάχους
T6	Τοίχοι κλιμακοστασίου προς διαμέρισμα: T6-01 (πρώην T1-09), T6-02 (πρώην T1-10)	Γυψοσανίδα – πρόταση: σκελετός 10 cm + διπλή γυψοσανίδα 2×12,5 mm εκατέρωθεν + πετροβάμβακας (πυράντοχη διάταξη)	10 cm (πρόταση)	2×12,5 mm ανά πλευρά	15 cm (πρόταση) – σχεδ. 20 cm	Σύνθεση & πυραντίσταση ΠΡΟΣ ΚΑΘΟΡΙΣΜΟ. Παρειά προς κλιμακοστάσιο στη σχεδιασμένη θέση (x 9,60 / y 7,60) (σημ. 6)
T7	Τοίχοι λεκανών WC: T7-01 (πρώην T2-01), T7-02 (πρώην T2-04)	Σκελετός 3 cm + διπλή γυψοσανίδα + κενό 10 cm + σκελετός 3 cm + διπλή γυψοσανίδα	3 + 10 (κενό) + 3 cm	2×12,5 mm ανά πλευρά (2,5 cm)	21 cm	Σχεδιάζεται 15 cm → +6 cm προς το λουτρό (διακεκομμένη λωρίδα), παρειά Υπν.1 σταθερή – ΠΡΟΣ ΕΠΙΒΕΒΑΙΩΣΗ (σημ. 5)

ΣΗΜΕΙΩΣΕΙΣ

1. Όλες οι διαστάσεις σε μέτρα (m), όπως το αρχιτεκτονικό, μετρημένες σε παρειές τούβλου / σκυροδέματος ΧΩΡΙΣ επιχρίσματα, θερμομόνωση και επενδύσεις γυψοσανίδας. Αρχή συντεταγμένων (0,00·0,00) = εξωτερική (βόρεια) παρειά τοίχου T4-01 και εξωτερική (δυτική) παρειά τοίχου T4-05. Η γεωμετρία, οι θέσεις και οι διαστάσεις της κάτοψης παραμένουν ακριβώς όπως στο A-10-2F και στη Rev.00.

2. T1: τούβλο 25 cm με εσωτερική επένδυση Τ3 (σκελετός 3 cm + διπλή γυψοσανίδα = 5,5 cm) σε ΟΛΕΣ τις εσωτερικές παρειές (λωρίδες T3-01…T3-13, μισύρες στην κάτοψη). Στα A-10-2F οι τοίχοι T1 σχεδιάζονται 25 cm (T1-04, T1-07, T1-08, T1-11, T1-12) και 30 cm οι πεσσοί σε ευθυγράμμιση με τα υποστυλώματα (T1-01/02/03/05/06/13/14/15/16), με εξωτερική θερμομόνωση. Οι διαστάσεις κρατούν τις σχεδιασμένες παρειές· στους πεσσούς 0,30 με τούβλο 25 μένουν 5 cm για μόνωση/επίχρισμα – ποια παρειά (εξωτερική ή εσωτερική) κρατείται: ΠΡΟΣ ΕΠΙΒΕΒΑΙΩΣΗ με EDGE. Η επένδυση Τ3 σχεδιάζεται μόνο στο τούβλο· η συνέχειά της μπροστά από τα υποστυλώματα της περιμέτρου (K1, K2, K3, K7, K8, K9, K10) και στους τοίχους έρκερ Τ4 είναι ΠΡΟΣ ΕΠΙΒΕΒΑΙΩΣΗ.

3. T4 (έρκερ, απλό τούβλο 11 cm – αμετάβλητο): βόρεια προεξοχή Υπν.1 (0,50 m πρόβολος από K1/K2), δυτικός κόλπος λουτρού με καμπύλη, δύο νότιες προεξοχές κουζίνας. Σχεδιάζονται 15 και 20 cm – ΠΡΟΣ ΕΠΙΒΕΒΑΙΩΣΗ. Οι εξωτερικές παρειές (γραμμές χάραξης) κρατούν τις θέσεις του σχεδίου.

4. T2: τελικό πάχος 10 cm (σκελετός 5 + 2×2,5). Στο σχέδιο τα χωρίσματα σχεδιάζονται 0,15· χάραξη: ο άξονας του T2 ταυτίζεται με τον άξονα του σχεδιασμένου τοίχου (−2,5 cm ανά παρειά). Εξαίρεση: ο T2A-01 (πρώην T2-05, Λουτρό γονέων / Χωλ) παραμένει 15 cm με τις σχεδιασμένες παρειές x 3,15 / 3,30. Ο βόρειος τοίχος καθιστικού (T2-06/08) ευθυγραμμίζεται με τη νότια παρειά της δοκού (y=5,15).

5. T7 (τοίχοι που εφάπτονται σε λεκάνες WC): T7-01 (πρώην T2-01, λεκάνη Λουτρού στην ανατ. παρειά, y=1,70–2,30) και T7-02 (πρώην T2-04, λεκάνη Λουτρού γονέων στη νότια παρειά, άξονας x=2,75). Σύνθεση 2,5 + 3 + 10 + 3 + 2,5 = 21 cm έναντι 15 σχεδιασμένων: η παρειά προς Υπν.1 κρατείται στη σχεδιασμένη θέση (x 5,00 / y 3,25) και το επιπλέον πάχος 6 cm μπαίνει προς το λουτρό (διακεκομμένη λωρίδα: 5,15→5,21 και 3,40→3,46) – ΠΡΟΣ ΕΠΙΒΕΒΑΙΩΣΗ. Το τμήμα του T7-02 προς το χωλ (x 3,30–3,55) παραμένει 15.

6. T6 (κλιμακοστάσιο): οι τοίχοι T6-01 (πρώην T1-09) και T6-02 (πρώην T1-10) κατασκευάζονται από γυψοσανίδα αντί τούβλου, ως ξεχωριστός τύπος. Σύνθεση/πυραντίσταση προς καθορισμό (πρόταση: σκελετός 10 cm + 2×12,5 mm εκατέρωθεν + πετροβάμβακας, τελικό 15 cm). Χάραξη: η παρειά προς το κλιμακοστάσιο μένει στη σχεδιασμένη θέση (x=9,60 / y=7,60) ώστε να μη μεταβληθεί το πλάτος 3,50 του κλιμακοστασίου. Ο ανατολικός τοίχος T1-11/12 είναι πρόσοψη και παραμένει T1 με επένδυση T3-07 προς το κλιμακοστάσιο – ΠΡΟΣ ΕΠΙΒΕΒΑΙΩΣΗ.

7. Οι δύο νότιες προεξοχές κουζίνας δεν είναι στην ίδια γραμμή: νότια παρειά ΝΔ προεξοχής y=10,25, ΝΑ προεξοχής y=10,17 (διαφορά 8 cm, ως σχέδιο) – ΠΡΟΣ ΕΠΙΒΕΒΑΙΩΣΗ. Το στοιχείο 0,15 κάτω από K3 (y 5,15–5,30, δίπλα στην ΕΙΣΟΔΟ) δεν έχει διαγράμμιση τοιχοποίας στο αρχιτεκτονικό – ΠΡΟΣ ΕΠΙΒΕΒΑΙΩΣΗ.

8. Υποστυλώματα K1–K10 όπως σχεδιάζονται στο A-10-2F (ταυτίζονται με Σ3/Σ5 Κόγια). Το K8 σχεδιάζεται 0,70×0,35 (στατικά 70/30). Καμία μετακίνηση φέροντος στοιχείου. Το W2.07 (0,60) είναι άνοιγμα μέσα στο τοιχίο K2 – αφορά τα στατικά, όχι την τοιχοποιία.

9. Πόρτες: φορά ανοίγματος όπως το τόξο στην κάτοψη (μεντεσές στην αρχή του φύλλου), ύψη 2,20. Κουφώματα κατά πίνακα A-50. Οι μετρήσεις επιβεβαιώνονται στο εργοτάξιο – κάθε απόκλιση > 2 cm αναφέρεται πριν τη χάραξη. Rev.01 (21/09/2026): αναθεώρηση προδιαγραφών τοίχων – T1 με εσωτερική επένδυση T3, T2 με σκελετό 5 cm, νέοι τύποι T2A, T6, T7· οι κωδικοί T1-09, T1-10, T2-01, T2-04, T2-05 της Rev.00 αντικαθίστανται (βλ. «πρώην»).

ΠΙΝΑΚΑΣ ΑΝΟΙΓΜΑΤΩΝ (πλάτη / θέσεις / φορά)

Κωδ.	Είδος	Πλάτος	Ποδιά / Ύψος	Θέση (λαμπάδες)	Φορά / παρατήρηση
W2.01	παράθυρο	3,50	0,00 / 2,40	y 5,65 → 9,15, τοίχος x 1,40–1,70	ανοιγόμενο/σταθερό κατά πίνακα κουφωμάτων A-50
W2.02	παράθυρο	4,75	0,00 / 2,40	x 4,10 → 8,85, τοίχος y 9,15–9,45	ανοιγόμενο/σταθερό κατά πίνακα κουφωμάτων A-50
W2.03	παράθυρο	2,05	1,00 / 1,50	x 10,70 → 12,75, τοίχος y 10,05–10,25	ανοιγόμενο/σταθερό κατά πίνακα κουφωμάτων A-50
W2.04	παράθυρο	1,35	1,00 / 1,50	y 7,80 → 9,15, τοίχος x 13,67–13,87	ανοιγόμενο/σταθερό κατά πίνακα κουφωμάτων A-50
W2.05	παράθυρο	0,70	0,15 / 1,50	y 5,10 → 5,80, τοίχος x 13,10–13,35	ανοιγόμενο/σταθερό κατά πίνακα κουφωμάτων A-50
W2.06	παράθυρο	1,00	0,00 / 2,40	y 1,45 → 2,45, τοίχος x 9,40–9,70	ανοιγόμενο/σταθερό κατά πίνακα κουφωμάτων A-50
W2.07	παράθυρο	0,60	1,50 / 2,40	x 5,45 → 6,05, τοίχος y 0,50–0,80	άνοιγμα σε τοιχίο K2 – βλ. στατικά
W2.08	παράθυρο	1,50	0,00 / 2,40	y 1,25 → 2,75, τοίχος x 0,80–1,10	ανοιγόμενο/σταθερό κατά πίνακα κουφωμάτων A-50
W2.09	παράθυρο	0,50	1,10 / 2,40	x 0,20 → 0,70, τοίχος y 3,05–3,20	ανοιγόμενο/σταθερό κατά πίνακα κουφωμάτων A-50
Θ1	πόρτα	0,80	– / 2,20	x 3,55 → 4,35, τοίχος y 3,25–3,40	Υπνοδωμάτιο 1 – μεντεσές δυτικά, ανοίγει προς Υπν.1 (βόρεια)
Θ2	πόρτα	0,70	– / 2,20	x 5,60 → 6,30, τοίχος y 3,25–3,40	Λουτρό – μεντεσές ανατολικά, ανοίγει προς λουτρό (βόρεια)
Θ3	πόρτα	0,70	– / 2,20	x 1,20 → 1,90, τοίχος y 3,25–3,40	Λουτρό γονέων – μεντεσές δυτικά, ανοίγει προς λουτρό (νότια)
Θ4	πόρτα	0,80	– / 2,20	y 3,53 → 4,33, τοίχος x 0,95–1,10	Ντους έρκερ – μεντεσές βόρεια, ανοίγει προς λουτρό (ανατολικά)
Θ5	πόρτα	0,80	– / 2,20	y 3,45 → 4,25, τοίχος x 6,35–6,50	Υπνοδωμάτιο 2 – μεντεσές νότια, ανοίγει προς Υπν.2 (ανατολικά)
Θ6	πόρτα	1,00	– / 2,20	y 5,30 → 6,30, τοίχος x 9,40–9,60	ΕΙΣΟΔΟΣ – μεντεσές βόρεια, ανοίγει προς Καθιστικό (δυτικά)
Α1	άνοιγμα	0,90	– / –	x 5,45 → 6,35, τοίχος y 5,00–5,15	Άνοιγμα χωλ → Καθιστικό, χωρίς πόρτα

ΑΡΓΥΡΟΥΠΟΛΗ – ΚΩΝΣΤΑΝΤΙΝΟΥΠΟΛΕΩΣ 12 & ΑΓ. ΒΑΡΒΑΡΑΣ (Ο.Τ. 103-15)
Πενταόροφο κτήριο κατοικιών με υπόγειο, σοφίτα και δώμα – INTERKAT A.E. / ARKAD I.K.E.

ΣΧΕΔΙΟ ΧΑΡΑΞΗΣ ΤΟΙΧΟΠΟΙΙΩΝ – ΚΑΤΟΨΗ Β΄ ΟΡΟΦΟΥ

Φύλλο 1/2: κάτοψη 1:50 με πλήρη διαστασιολόγηση, υπόμνημα, πίνακας τύπων, πίνακας ανοιγμάτων, σημειώσεις. Φύλλο 2/2: πίνακας τοίχων.

Βάση: EDGE, Μελέτη Εφαρμογής Α-10-2F «Κάτοψη Β΄ ορόφου» R00, 23/07/2026, 1:50 – γεωμετρία διανυσματικά από το PDF
Προδιαγραφή τοίχων: Γ. Ζαρκαδάς 09/2026, διορθώσεις 21/09/2026 (Rev.01). Οι θέσεις ΠΡΟΣ ΕΠΙΒΕΒΑΙΩΣΗ επιβεβαιώνονται από EDGE πριν τη χάραξη.

Κλίμακα 1:50 (A2) – διαστάσεις σε m Ημερομηνία 21/09/2026 **Φύλλο 1/2 Rev. 01**

ΣΧΕΔΙΟ ΧΑΡΑΞΗΣ ΤΟΙΧΟΠΟΙΙΩΝ – ΚΑΤΟΨΗ Β΄ ΟΡΟΦΟΥ – ΠΙΝΑΚΑΣ ΤΟΙΧΩΝ (φύλλο 2/2, Rev.01)

Συντεταγμένες παρειών (m) από την αρχή 0,00·0,00 (βλ. σημ. 1 φύλλου 1). Οι λωρίδες Τ3 δίνονται με τις παρειές τους (πάχος 0,055). Κωδικοί «πρώην» = κωδικοί της Rev.00.


Κωδ.	Τύπ.	Θέση / περιγραφή	Από x ; y	Έως x ; y	Μήκος	Πάχος
T4-01	T4	Βόρειος τοίχος έρκερ Υπν.1	0,80 ; 0,00	4,80 ; 0,20	4,00	0,20
T4-02	T4	Ανατ. επιστροφή έρκερ Υπν.1 (πάνω από Κ2)	4,60 ; 0,20	4,80 ; 0,50	0,30	0,20
T4-03	T4	Βόρειος τοίχος δυτ. έρκερ (δυτ. λαμπάς W2.09)	0,00 ; 3,05	0,20 ; 3,20	0,20	0,15
T4-04	T4	Βόρειος τοίχος δυτ. έρκερ (ανατ. λαμπάς W2.09)	0,70 ; 3,05	0,80 ; 3,20	0,15	0,10
T4-05	T4	Δυτικός τοίχος έρκερ λουτρού (ευθύγραμμο τμήμα)	0,00 ; 3,20	0,15 ; 4,55	1,35	0,15
T4-06	T4	Νότια επιστροφή έρκερ λουτρού → Κ10	0,60 ; 4,90	0,80 ; 5,15	0,25	0,20
T4-07	T4	Δυτικός τοίχος ΝΔ προεξοχής κουζίνας	9,50 ; 9,45	9,70 ; 10,25	0,80	0,20
T4-08	T4	Νότιος τοίχος ΝΔ προεξοχής κουζίνας	9,70 ; 10,05	10,70 ; 10,25	1,00	0,20
T4-09	T4	Δυτικός τοίχος ΝΑ προεξοχής κουζίνας	12,75 ; 9,45	12,95 ; 10,17	0,72	0,20
T4-10	T4	Νότιος τοίχος ΝΑ προεξοχής (ευθύγρ. τμήμα)	12,95 ; 9,97	13,35 ; 10,17	0,40	0,20
T4-11	T4	Ανατ. τοίχος ΝΑ προεξοχής (ευθύγρ. τμήμα)	13,67 ; 9,45	13,87 ; 9,65	0,20	0,20
T1-01	T1	Πεσσός ΒΔ πάνω από Κ1	0,80 ; 0,20	1,10 ; 0,50	0,30	0,30
T1-02	T1	Λωρίδα Κ1 → W2.08	0,80 ; 1,20	1,10 ; 1,25	0,30	0,05
T1-03	T1	Πεσσός δυτ. Υπν.1 (W2.08 → λουτρό)	0,80 ; 2,75	1,10 ; 3,20	0,45	0,30
T1-04	T1	Βόρειος τοίχος Υπν.2 (Κ2 → πεσσός)	6,60 ; 0,50	9,40 ; 0,75	2,80	0,25
T1-05	T1	ΒΑ πεσσός Υπν.2 (→ W2.06)	9,40 ; 0,50	9,70 ; 1,45	0,95	0,30
T1-06	T1	Πεσσός W2.06 → Κ3	9,40 ; 2,45	9,70 ; 3,00	0,55	0,30
T1-07	T1	Βόρειος τοίχος πλατύσκαλου Κ3 → Κ4	9,70 ; 3,00	11,05 ; 3,25	1,35	0,25
T1-08	T1	Λαμπάς δυτικά Κ6 (τούβλο ως σχέδιο)	10,90 ; 4,85	11,05 ; 5,10	0,25	0,15
T1-11	T1	Ανατ. τοίχος κλιμακοστασίου – πρόσοψη (W2.05 → γωνία)	13,10 ; 5,80	13,35 ; 7,55	1,75	0,25
T1-12	T1	ΝΑ γωνιακό τμήμα πρόσοψης (κλιμακοστάσιο / κουζίνα)	13,10 ; 7,55	13,95 ; 7,80	0,85	0,25
T1-13	T1	Πεσσός νότιος Κ9 → W2.02	3,40 ; 9,15	4,10 ; 9,45	0,70	0,30
T1-14	T1	Λαμπάς W2.02 → Κ8	8,85 ; 9,15	9,00 ; 9,45	0,30	0,15
T1-15	T1	ΝΑ γωνιακός πεσσός (Κ7 → προεξοχή), νότιο τμήμα	13,35 ; 9,30	13,87 ; 9,45	0,52	0,15
T1-15β	T1	ΝΑ γωνιακός πεσσός, βόρειο τμήμα 0,12 (λαμπάς W2.04)	13,75 ; 9,15	13,87 ; 9,30	0,15	0,12
T1-16	T1	Πεσσός Κ10 → W2.01	1,40 ; 5,15	1,70 ; 5,65	0,50	0,30
T5-01	T5	Επένδυση 0,10 βόρεια πυρήνα (Κ3 → καμπύλη)	9,70 ; 2,75	13,10 ; 2,85	3,40	0,10
T6-01	T6	Δυτ. τοίχος κλιμακοστασίου, ΕΙΣΟΔΟΣ → νότιος (πρώην T1-09)	9,40 ; 6,30	9,60 ; 7,80	1,50	0,20
T6-02	T6	Νότιος τοίχος κλιμακοστασίου → κουζίνα (πρώην T1-10)	9,60 ; 7,60	13,10 ; 7,80	3,50	0,20

Κωδ.	Τύπ.	Θέση / περιγραφή	Από x ; y	Έως x ; y	Μήκος	Πάχος
T7-01	T7	Υπν.1 / Λουτρό – τοίχος λεκάνης WC (πρώην T2-01)	5,00 ; 0,80	5,15 ; 3,25	2,45	0,15
T7-02	T7	Υπν.1 / Λουτρό γονέων – τοίχος λεκάνης WC (πρώην T2-04)	1,90 ; 3,25	3,55 ; 3,40	1,65	0,15
T2A-01	T2A	Λουτρό γονέων / Χωλ – τελικό 15 cm ως σχέδιο (πρώην T2-05)	3,15 ; 3,40	3,30 ; 5,00	1,60	0,15
T2-02	T2	Νότιος τοίχος Λουτρού (μεταξύ Θ1 και Θ2)	4,35 ; 3,25	5,60 ; 3,40	1,25	0,15
T2-03	T2	Λουτρό / Υπν.2	6,35 ; 0,80	6,50 ; 3,45	2,65	0,15
T2-03β	T2	Λαμπάς Θ2 (προεξοχή 0,05)	6,30 ; 3,25	6,35 ; 3,40	0,15	0,05
T2-06	T2	Βόρειος τοίχος Καθιστικού (δυτ. τμήμα)	1,70 ; 5,00	5,45 ; 5,15	3,75	0,15
T2-07	T2	Τοίχος ντουλάπας χωλ	5,30 ; 4,30	5,45 ; 5,00	0,70	0,15
T2-08	T2	Βόρειος τοίχος Καθιστικού (ανατ. τμήμα)	6,35 ; 5,00	9,40 ; 5,15	3,05	0,15
T2-09	T2	Υπν.2 / Χωλ (νότια Θ5)	6,35 ; 4,25	6,50 ; 5,00	0,75	0,15
T2-10	T2	Λουτρό γονέων / ντους έρκερ (βόρεια Θ4)	0,95 ; 3,20	1,10 ; 3,53	0,33	0,15
T2-10β	T2	Λαμπάς Θ3	1,10 ; 3,25	1,20 ; 3,40	0,15	0,10
T2-11	T2	Λουτρό γονέων / ντους έρκερ (νότια Θ4)	0,95 ; 4,33	1,10 ; 4,85	0,52	0,15
T4-05κ	T4	Καμπύλη ΝΔ γωνία έρκερ λουτρού (μήκος εξωτ. τόξου)	κ. 0,60 ; 4,55	R 0,60 / 0,45	0,94	0,15
T5-01κ	T5	Καμπύλη ΒΑ γωνία επένδυσης πυρήνα (μήκος εξωτ. τόξου)	κ. 13,10 ; 3,00	R 0,25 / 0,15	0,39	0,10
T4-10κ	T4	Καμπύλη ΝΑ προεξοχή κουζίνας (μήκος εξωτ. τόξου)	κ. 13,35 ; 9,65	R 0,52 / 0,32	0,82	0,20
T3-01	T3	Επένδυση T1-01 – Ανατ. παρειά (Υπν.1)	1,10 ; 0,20	1,16 ; 0,50	0,30	0,055
T3-02	T3	Επένδυση T1-03 – Ανατ. παρειά (Υπν.1)	1,10 ; 2,75	1,16 ; 3,20	0,45	0,055
T3-03	T3	Επένδυση T1-04 – Νότια παρειά (Υπν.2)	6,60 ; 0,75	9,40 ; 0,81	2,80	0,055
T3-04	T3	Επένδυση T1-05 – Δυτ. παρειά (Υπν.2)	9,35 ; 0,75	9,40 ; 1,45	0,70	0,055
T3-05	T3	Επένδυση T1-06 – Δυτ. παρειά (Υπν.2)	9,35 ; 2,45	9,40 ; 3,00	0,55	0,055
T3-06	T3	Επένδυση T1-07 – Νότια παρειά (πλατύσκαλο)	9,70 ; 3,25	11,05 ; 3,31	1,35	0,055
T3-07	T3	Επένδυση T1-11 – Δυτ. παρειά (κλιμακοστάσιο)	13,04 ; 5,80	13,10 ; 7,60	1,80	0,055
T3-08	T3	Επένδυση T1-12 – Νότια παρειά (κουζίνα) → λαμπάς W2.04	13,35 ; 7,80	13,67 ; 7,86	0,32	0,055
T3-09	T3	Επένδυση T1-15β – Δυτ. παρειά (κουζίνα)	13,70 ; 9,15	13,75 ; 9,30	0,15	0,055
T3-10	T3	Επένδυση T1-15 – Βόρεια παρειά (κουζίνα)	13,35 ; 9,24	13,75 ; 9,30	0,40	0,055
T3-11	T3	Επένδυση T1-14 – Βόρεια παρειά (καθιστικό)	8,85 ; 9,10	9,00 ; 9,15	0,15	0,055
T3-12	T3	Επένδυση T1-13 – Βόρεια παρειά (καθιστικό)	3,40 ; 9,10	4,10 ; 9,15	0,70	0,055
T3-13	T3	Επένδυση T1-16 – Ανατ. παρειά (καθιστικό)	1,70 ; 5,15	1,75 ; 5,65	0,50	0,055

Σύνολα μήκους ανά τύπο (m): T1 = 11,72 T3 = 10,17 T2 = 13,30 T2A = 1,60 T4 = 11,13 T5 = 3,79 T6 = 5,00 T7 = 4,10 (μήκη σε παρειές, χωρίς αφαίρεση ανοιγμάτων· T3 = μήκη επένδυσης)


ΛΕΠΤΟΜΕΡΕΙΕΣ ΤΥΠΩΝ ΤΟΙΧΟΠΟΙΙΑΣ – οριζόντιες τομές, κλίμακα 1:5 (πάχη σε cm)

T1 + T3 Εξωτερικός τοίχος με εσωτερική επένδυση

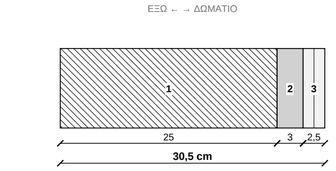


1 τούβλο 25 cm (+εξωτ. επίχρισμα/μόνωση)
2 σκελετός 3 cm
3 διπλή γυψοσανίδα 2×12,5 mm

T2 Τυπικό εσωτερικό χώρισμα

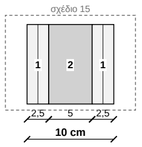


1 διπλή γυψοσανίδα 2×12,5 mm
2 σκελετός 5 cm
διακεκ.: σχεδιασμένος τοίχος 15 – κοινός άξονας

T2A Μόνο T2A-01 (πρώην T2-05)

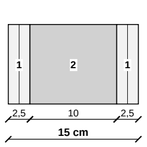


1 διπλή γυψοσανίδα 2×12,5 mm
2 σκελετός 10 cm
παρειές = σχεδιασμένες (x 3,15 / 3,30)

T4 Τοίχος ERKER

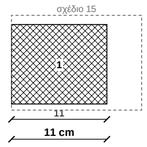


1 απλό τούβλο 11 cm (+επιχρίσματα)
διακεκ.: σχεδιασμένο πάχος 15/20 –
θέση παρειάς ΠΡΟΣ ΕΠΙΒΕΒΑΙΩΣΗ

T6 Κλιμακοστάσιο – γυψοσανίδα (ΠΡΟΤΑΣΗ)

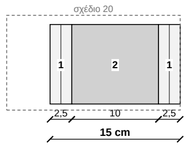

1 διπλή γυψοσανίδα 2×12,5 mm
2 σκελετός 10 cm + πετροβάμβακας
διακεκ.: σχεδιασμένο 20 – παρειά κλιμ/σίου σταθερή

T7 Τοίχος λεκάνης WC

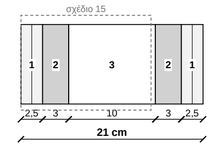

1 διπλή γυψοσανίδα 2×12,5 mm
2 σκελετός 3 cm 3 κενό 10 cm
διακεκ.: σχεδιασμένο 15 – +6 προς λουτρό

ΑΡΓΥΡΟΥΠΟΛΗ – ΚΩΝΣΤΑΝΤΙΝΟΥΠΟΛΕΩΣ 12 & ΑΓ. ΒΑΡΒΑΡΑΣ (Ο.Τ. 103-15)
Πενταόροφο κτήριο κατοικιών με υπόγειο, σοφίτα και δώμα – INTERKAT A.E. / ARKAD I.K.E.

ΣΧΕΔΙΟ ΧΑΡΑΞΗΣ ΤΟΙΧΟΠΟΙΙΩΝ – ΚΑΤΟΨΗ Β΄ ΟΡΟΦΟΥ

Φύλλο 2/2: πίνακας τοίχων (συντεταγμένες, μήκη, πάχη, σύνολα ανά τύπο).

Βάση: EDGE, Μελέτη Εφαρμογής Α-10-2F «Κάτοψη Β΄ ορόφου» R00, 23/07/2026, 1:50 – γεωμετρία διανυσματικά από το PDF
Προδιαγραφή τοίχων: Γ. Ζαρκαδάς 09/2026, διορθώσεις 21/09/2026 (Rev.01). Οι θέσεις ΠΡΟΣ ΕΠΙΒΕΒΑΙΩΣΗ επιβεβαιώνονται από EDGE πριν τη χάραξη.

Κλίμακα 1:50 (A2) – διαστάσεις σε m Ημερομηνία 21/09/2026 **Φύλλο 2/2 Rev. 01**