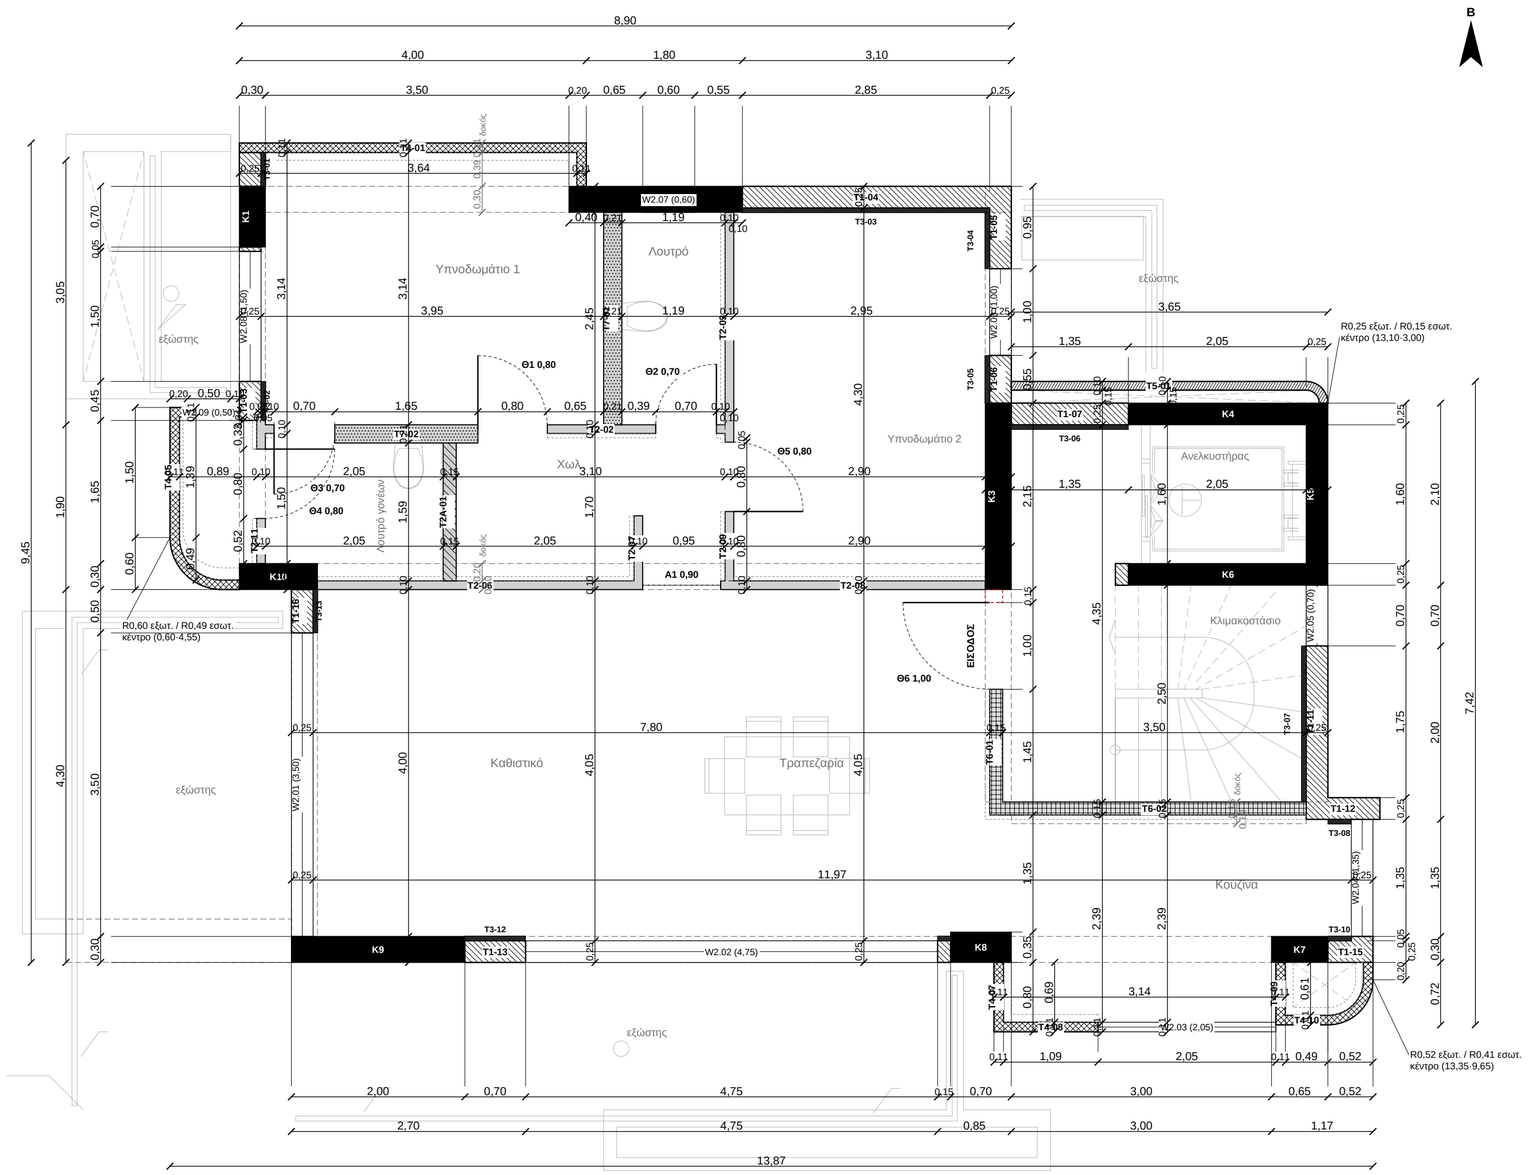


ΠΙΝΑΚΑΣ ΑΝΟΙΓΜΑΤΩΝ (πλάτη / θέσεις / φορά)

Κωδ.	Είδος	Πλάτος	Ποδιά / Ύψος	Θέση (λαμπάδες)	Φορά / παρατήρηση
W2.01	παράθυρο	3,50	0,00 / 2,40	y 5,65 → 9,15, τοίχος x 1,40–1,65	ανοιγόμενο/σταθερό κατά πίνακα κουφωμάτων A-50
W2.02	παράθυρο	4,75	0,00 / 2,40	x 4,10 → 8,85, τοίχος y 9,20–9,45	ανοιγόμενο/σταθερό κατά πίνακα κουφωμάτων A-50
W2.03	παράθυρο	2,05	1,00 / 1,50	x 10,70 → 12,75, τοίχος y 10,14–10,25	ανοιγόμενο/σταθερό κατά πίνακα κουφωμάτων A-50
W2.04	παράθυρο	1,35	1,00 / 1,50	y 7,80 → 9,15, τοίχος x 13,62–13,87	ανοιγόμενο/σταθερό κατά πίνακα κουφωμάτων A-50
W2.05	παράθυρο	0,70	0,15 / 1,50	y 5,10 → 5,80, τοίχος x 13,10–13,35	ανοιγόμενο/σταθερό κατά πίνακα κουφωμάτων A-50
W2.06	παράθυρο	1,00	0,00 / 2,40	y 1,45 → 2,45, τοίχος x 9,45–9,70	ανοιγόμενο/σταθερό κατά πίνακα κουφωμάτων A-50
W2.07	παράθυρο	0,60	1,50 / 2,40	x 5,45 → 6,05, τοίχος y 0,50–0,80	άνοιγμα σε τοιχίο K2 – βλ. στατικά
W2.08	παράθυρο	1,50	0,00 / 2,40	y 1,25 → 2,75, τοίχος x 0,80–1,05	ανοιγόμενο/σταθερό κατά πίνακα κουφωμάτων A-50
W2.09	παράθυρο	0,50	1,10 / 2,40	x 0,20 → 0,70, τοίχος y 3,05–3,16	ανοιγόμενο/σταθερό κατά πίνακα κουφωμάτων A-50
Θ1	πόρτα	0,80	– / 2,20	x 3,55 → 4,35, τοίχος y 3,25–3,35	Υπνοδωμάτιο 1 – μεντεσές δυτικά, ανοίγει προς Υπν.1 (βόρεια)
Θ2	πόρτα	0,70	– / 2,20	x 5,60 → 6,30, τοίχος y 3,25–3,35	Λουτρό – μεντεσές ανατολικά, ανοίγει προς λουτρό (βόρεια)
Θ3	πόρτα	0,70	– / 2,20	x 1,20 → 1,90, τοίχος y 3,25–3,35	Λουτρό γονέων – μεντεσές δυτικά, ανοίγει προς λουτρό (νότια)
Θ4	πόρτα	0,80	– / 2,20	y 3,53 → 4,33, τοίχος x 1,00–1,10	Ντους έρκερ – μεντεσές βόρεια, ανοίγει προς λουτρό (ανατολικά)
Θ5	πόρτα	0,80	– / 2,20	y 3,45 → 4,25, τοίχος x 6,40–6,50	Υπνοδωμάτιο 2 – μεντεσές νότια, ανοίγει προς Υπν.2 (ανατολικά)
Θ6	πόρτα	1,00	– / 2,20	y 5,30 → 6,30, τοίχος x 9,45–9,60	ΕΙΣΟΔΟΣ – μεντεσές βόρεια, ανοίγει προς Καθιστικό (δυτικά)
A1	άνοιγμα	0,90	– / –	x 5,45 → 6,35, τοίχος y 5,05–5,15	Άνοιγμα χωλ → Καθιστικό, χωρίς πόρτα

ΥΠΟΜΝΗΜΑ ΤΟΙΧΟΠΟΙΙΩΝ

- T1 – ΕΞΩΤΕΡΙΚΗ: ΤΟΥΒΛΟ 25 cm + ΕΣΩΤ. ΕΠΕΝΔΥΣΗ T3 (30,5 cm)
- T3 – ΕΠΕΝΔΥΣΗ T1: ΣΚΕΛΕΤΟΣ 3 cm + ΔΙΠΛΗ ΓΥΨΟΣΑΝΙΔΑ (5,5 cm)
- T2 – ΕΣΩΤΕΡΙΚΟ: ΣΚΕΛΕΤΟΣ 5 cm + ΔΙΠΛΗ ΓΥΨΟΣΑΝΙΔΑ ΕΚΑΤΕΡΩΘΕΝ (10 cm)
- T2A – ΣΚΕΛΕΤΟΣ 10 cm + ΔΙΠΛΗ ΓΥΨΟΣΑΝΙΔΑ ΕΚΑΤΕΡΩΘΕΝ (15 cm) – μόνο T2A-01
- T4 – ERKER – ΑΠΛΟ ΤΟΥΒΛΟ 11 cm
- T5 – ΤΟΥΒΛΟ 10 cm (ως σχέδιο, περιμετρικά πυρήνα)
- T6 – ΚΛΙΜΑΚΟΣΤΑΣΙΟ: ΓΥΨΟΣΑΝΙΔΑ 15 cm (ΠΡΟΤΑΣΗ – σύνθεση προς καθορισμό)
- T7 – ΤΟΙΧΟΣ WC: ΣΚΕΛ. 3 + 2×ΓΥΨ. + ΚΕΝΟ 10 + ΣΚΕΛ. 3 + 2×ΓΥΨ. (21 cm)
- ΠΑΡΕΙΑ ΑΡΧΙΤΕΚΤΟΝΙΚΟΥ Α-10-2F ΟΠΟΥ ΔΙΑΦΕΡΕΙ ΑΠΟ ΤΟ ΝΕΟ ΠΑΧΟΣ (μόνο για αναφορά)
- ΟΠΛΙΣΜΕΝΟ ΣΚΥΡΟΔΕΜΑ K1–K10 (ως έχει, στατικά Κόγια)
- ΔΟΚΟΣ ΟΡΟΦΗΣ (προβολή άνωθεν, από αρχιτεκτονικό)
- ΠΑΡΑΘΥΡΟ / ΠΟΡΤΑ (φύλλο + τόξο ανοίγματος)
- ΣΤΟΙΧΕΙΟ ΠΡΟΣ ΕΠΙΒΕΒΑΙΩΣΗ

ΠΙΝΑΚΑΣ ΤΥΠΩΝ ΤΟΙΧΟΠΟΙΙΑΣ (Rev.02)

Κωδ.	Περιγραφή / θέση	Υλικά – σύνθεση	Σκελετός / τούβλο	Γυψοσανίδα	Τελικό πάχος	Στο σχέδιο EDGE / παρατήρηση
T1	Εξωτερική τοιχοποιία (περίμετρος κτηρίου, πρόσοψη κλιμακοστασίου)	Οπτοπλινθοδομή, τούβλο 25 cm + εσωτερική επένδυση T3 (σκελετός 3 cm + διπλή γυψοσανίδα)	25 cm	εσωτ. 2×12,5 mm (μέσω T3)	25 + 5,5 = 30,5 cm (+εξωτ. επιχρ./μόνωση)	Σχεδιάζεται 25 cm· οι πεσσοί στη γραμμή υποστυλωμάτων· σταθερή η εξωτερική παρειά, εσωτερική 5 cm πίσω από την παρειά της κολώνας (καλύπτεται από T3) (σημ. 2)
T3	Εσωτερική επένδυση όλων των T1 (λωρίδες T3-01…T3-13)	Μεταλλικός σκελετός 3 cm + διπλή γυψοσανίδα 2×12,5 mm (μία πλευρά)	3 cm	2×12,5 mm (2,5 cm)	5,5 cm	Στην παρειά δωματίου κάθε T1 (σχεδιάζεται 0,055). Συνέχεια μπροστά από υποστυλώματα και στους T4: ΠΡΟΣ ΕΠΙΒΕΒΑΙΩΣΗ (σημ. 2)
T2	Τυπικά εσωτερικά χωρίσματα	Μεταλλικός σκελετός 5 cm + διπλή γυψοσανίδα 2×12,5 mm σε κάθε πλευρά	5 cm	2×12,5 mm ανά πλευρά (2,5 cm)	10 cm	Σχεδιάζεται 10 cm (EDGE 0,15)· σταθερή η παρειά του πίνακα τοίχων, η άλλη μετακινείται 5 cm (γκρι διακεκομμένη = αρχική) (σημ. 4)
T2A	Μόνο T2A-01: Λουτρό γονέων / Χωλ (πρώην T2-05)	Μεταλλικός σκελετός 10 cm + διπλή γυψοσανίδα 2×12,5 mm σε κάθε πλευρά	10 cm	2×12,5 mm ανά πλευρά (2,5 cm)	15 cm	Παρειές ακριβώς ως σχέδιο (x 3,15 / 3,30) – δεν τροποποιείται
T4	Τοιχοποιία ERKER (προεξοχές εκτός αξόνων δοκών)	Οπτοπλινθοδομή, απλό τούβλο 11 cm, επιχρίσματα	11 cm	–	11 cm (+επιχρ.)	Σχεδιάζεται 11 cm με σταθερή την εξωτερική παρειά (EDGE 0,15 / 0,20 – γκρι διακεκομμένη = αρχική εσωτερική παρειά) (σημ. 3)
T5	Τοίχος 10 cm περιμετρικά πυρήνα ανελκυστήρα (ως σχέδιο)	Απλό τούβλο 10 cm, ως αρχιτεκτονικό	10 cm	–	10 cm	Εκτός προδιαγραφής – ΠΡΟΣ ΕΠΙΒΕΒΑΙΩΣΗ τύπου/πάχους
T6	Τοίχοι κλιμακοστασίου προς διαμέρισμα: T6-01 (πρώην T1-09), T6-02 (πρώην T1-10)	Γυψοσανίδα – πρόταση: σκελετός 10 cm + διπλή γυψοσανίδα 2×12,5 mm εκατέρωθεν + πετροβάμβακας (πυράντοχη διάταξη)	10 cm (πρόταση)	2×12,5 mm ανά πλευρά	15 cm (πρόταση)	Σχεδιάζεται 15 cm (πρόταση) με σταθερή την παρειά προς κλιμακοστάσιο (x 9,60 / y 7,60)· σύνθεση & πυραντίσταση ΠΡΟΣ ΚΑΘΟΡΙΣΜΟ (σημ. 6)
T7	Τοίχοι λεκανών WC: T7-01 (πρώην T2-01), T7-02 (πρώην T2-04)	Σκελετός 3 cm + διπλή γυψοσανίδα + κενό 10 cm + σκελετός 3 cm + διπλή γυψοσανίδα	3 + 10 (κενό) + 3 cm	2×12,5 mm ανά πλευρά (2,5 cm)	21 cm	Σχεδιάζεται 21 cm: σταθερή η παρειά προς Υπν.1 (x 5,00 / y 3,25), +6 cm προς το λουτρό (EDGE 0,15) – ΠΡΟΣ ΕΠΙΒΕΒΑΙΩΣΗ (σημ. 5)

ΣΗΜΕΙΩΣΕΙΣ

1. Όλες οι διαστάσεις σε μέτρα (m), σε παρειές τούβλου / σκελετού γυψοσανίδας / σκυροδέματος ΧΩΡΙΣ επιχρίσματα και θερμομόνωση. Οι τοίχοι σχεδιάζονται με τα ΠΡΑΓΜΑΤΙΚΑ πάχη της προδιαγραφής (T1 0,25 – T2 0,10 – T2A 0,15 – T3 0,055 – T4 0,11 – T6 0,15 πρόταση – T7 0,21), όχι με τα πάχη του αρχιτεκτονικού. Θέσεις τοίχων, ανοιγμάτων και υποστυλωμάτων από το A-10-2F: όπου το νέο πάχος διαφέρει από το σχεδιασμένο, μένει σταθερή η «σταθερή παρειά» του πίνακα τοίχων και μετακινείται η άλλη· η αρχική παρειά του A-10-2F φαίνεται με γκρι διακεκομμένη γραμμή. Αρχή συντεταγμένων (0,00·0,00) = εξωτερική (βόρεια) παρειά T4-01 και εξωτερική (δυτική) παρειά T4-05.

2. T1: τούβλο 25 cm με εσωτερική επένδυση T3 (σκελετός 3 cm + διπλή γυψοσανίδα = 5,5 cm) σε ΟΛΕΣ τις εσωτερικές παρειές (λωρίδες T3-01…T3-13, μισόρες στην κάτοψη). Σταθερή η εξωτερική παρειά (γραμμή πρόσοψης / εξωτερική παρειά υποστυλωμάτων). Στους πεσσούς που το A-10-2F σχεδιάζει 0,30 (T1-01/02/03/05/06/13/14/15/16) η εσωτερική παρειά του τούβλου μένει 5 cm πίσω από την παρειά της κολώνας και η T3 (5,5) την καλύπτει (τελικό 30,5 ≈ κολώνα 30). Η επένδυση T3 σχεδιάζεται μόνο στο τούβλο· η συνέχειά της μπροστά από τα υποστυλώματα της περιμέτρου (K1, K2, K3, K7, K8, K9, K10) και στους τοίχους έρκερ T4: ΠΡΟΣ ΕΠΙΒΕΒΑΙΩΣΗ.

3. T4 (έρκερ, απλό τούβλο 11 cm): βόρεια προεξοχή Υπν.1, δυτικός κόλπος λουτρού με καμπύλη (R0,60 εξωτ. / R0,49 εσωτ.), δύο νότιες προεξοχές κουζίνας (R0,52 / R0,41). Σταθερές οι εξωτερικές παρειές (γραμμές χάραξης στην πλάκα)· οι εσωτερικές παρειές μετακινούνται προς τα έξω κατά 4 cm (σχέδιο 0,15) ή 9 cm (σχέδιο 0,20).

4. T2: σκελετός 5 + 2×2,5 = 10 cm (A-10-2F 0,15). Σταθερή παρειά ανά τοίχο (πίνακας τοίχων): T2-02 προς λουτρό (y 3,25)· T2-03/09 προς Υπν.2 (x 6,50)· T2-06/08 προς καθιστικό (y 5,15, ευθυγράμμιση με νότια παρειά δοκού)· T2-07 προς χωλ (x 5,45, άνοιγμα A1 0,90)· T2-10/11 προς λουτρό (x 1,10). T2A-01 (πρώην T2-05): 15 cm, παρειές ως σχέδιο x 3,15 / 3,30. Θέσεις λαμπάδων πορτών αμετάβλητες.

5. T7 (τοίχοι που εφάπτονται σε λεκάνες WC, 2,5+3+10+3+2,5 = 21 cm): T7-01 (πρώην T2-01, λεκάνη Λουτρού στην ανατ. παρειά, y=1,70–2,30) και T7-02 (πρώην T2-04, λεκάνη Λουτρού γονέων στη νότια παρειά, άξονας x=2,75). Σταθερή η παρειά προς Υπν.1 (x 5,00 / y 3,25), το επιπλέον πάχος μπαίνει προς το λουτρό: παρειές λουτρού x 5,21 και y 3,46 (Λουτρό 1,19 πλάτος, Λουτρό γονέων 1,59 βάθος) – ΠΡΟΣ ΕΠΙΒΕΒΑΙΩΣΗ. Το τμήμα του T7-02 προς το χωλ (x 3,30–3,55) σχεδιάζεται επίσης 0,21.

6. T6 (κλιμακοστάσιο): T6-01 (πρώην T1-09) και T6-02 (πρώην T1-10) από γυψοσανίδα, ξεχωριστός τύπος. Σχεδιάζονται 15 cm (ΠΡΟΤΑΣΗ: σκελετός 10 cm + 2×12,5 mm εκατέρωθεν + πετροβάμβακας) με σταθερή την παρειά προς το κλιμακοστάσιο (x 9,60 / y 7,60) ώστε να μη μεταβληθεί το πλάτος 3,50· η παρειά διαμερίσματος μένει 5 cm πίσω από την παρειά K3 (x 9,45) και η κουζίνα κερδίζει 5 cm (y 7,75). Σύνθεση/πυραντίσταση ΠΡΟΣ ΚΑΘΟΡΙΣΜΟ. Ο ανατολικός τοίχος T1-11/12 είναι πρόσοψη και παραμένει T1 με T3-07 προς το κλιμακοστάσιο.

7. Οι δύο νότιες προεξοχές κουζίνας δεν είναι στην ίδια γραμμή: νότια παρειά ΝΔ προεξοχής y=10,25, ΝΑ προεξοχής y=10,17 (διαφορά 8 cm, ως A-10-2F) – ΠΡΟΣ ΕΠΙΒΕΒΑΙΩΣΗ. Το στοιχείο 0,15 κάτω από K3 (y 5,15–5,30, δίπλα στην ΕΙΣΟΔΟ) δεν έχει διαγράμμιση τοιχοποιίας στο αρχιτεκτονικό – ΠΡΟΣ ΕΠΙΒΕΒΑΙΩΣΗ.

8. Υποστυλώματα K1–K10 όπως σχεδιάζονται στο A-10-2F (ταυτίζονται με Σ3/Σ5 Κόγια). Το K8 σχεδιάζεται 0,70×0,35 (στατικά 70/30). Καμία μετακίνηση φέροντος στοιχείου. Το W2.07 (0,60) είναι άνοιγμα μέσα στο τοιχίο K2 – αφορά τα στατικά, όχι την τοιχοποιία.

9. Πόρτες: φορά ανοίγματος όπως το τόξο στην κάτοψη (μεντεσές στην αρχή του φύλλου), ύψη 2,20. Κουφώματα κατά πίνακα A-50 (τα κουφώματα σχεδιάζονται μέσα στο νέο πάχος τοίχου). Οι μετρήσεις επιβεβαιώνονται στο εργοτάξιο – κάθε απόκλιση > 2 cm αναφέρεται πριν τη χάραξη. Rev.02 (22/09/2026): όλοι οι τοίχοι με τα πάχη προδιαγραφής και ενημερωμένες διαστάσεις. Rev.01: νέοι τύποι T2A, T6, T7, T3 σε όλους τους T1· οι κωδικοί T1-09, T1-10, T2-01, T2-04, T2-05 της Rev.00 αντικαθίστανται (βλ. «πρώην»).

ΑΡΓΥΡΟΥΠΟΛΗ – ΚΩΝΣΤΑΝΤΙΝΟΥΠΟΛΕΩΣ 12 & ΑΓ. ΒΑΡΒΑΡΑΣ (Ο.Τ. 103-15)

Πενταόροφο κτήριο κατοικιών με υπόγειο, σοφίτα και δώμα – INTERKAT A.E. / ARKAD I.K.E.

ΣΧΕΔΙΟ ΧΑΡΑΞΗΣ ΤΟΙΧΟΠΟΙΙΩΝ – ΚΑΤΟΨΗ Β΄ ΟΡΟΦΟΥ

Φύλλο 1/2: κάτοψη 1:50 με πλήρη διαστασιολόγηση, υπόμνημα, πίνακας τύπων, πίνακας ανοιγμάτων, σημειώσεις. Φύλλο 2/2: πίνακας τοίχων.

Βάση: EDGE, Μελέτη Εφαρμογής Α-10-2F «Κάτοψη Β΄ ορόφου» R00, 23/07/2026, 1:50 – γεωμετρία διανυσματικά από το PDF

Προδιαγραφή τοίχων: Γ. Ζαρκαδάς 09/2026 (Rev.01 21/09, Rev.02 22/09: πραγματικά πάχη στο σχέδιο). Οι θέσεις ΠΡΟΣ ΕΠΙΒΕΒΑΙΩΣΗ επιβεβαιώνονται από EDGE πριν τη χάραξη.

Κλίμακα 1:50 (A2) – διαστάσεις σε m Ημερομηνία 22/09/2026 **Φύλλο 1/2 Rev. 02**

ΣΧΕΔΙΟ ΧΑΡΑΞΗΣ ΤΟΙΧΟΠΟΙΙΩΝ – ΚΑΤΟΨΗ Β΄ ΟΡΟΦΟΥ – ΠΙΝΑΚΑΣ ΤΟΙΧΩΝ (φύλλο 2/2, Rev.02)

Συντεταγμένες παρειών (m) από την αρχή 0,00·0,00 (βλ. σημ. 1 φύλλου 1). Πάχη = πάχη προδιαγραφής· στήλη EDGE = πάχος στο A-10-2F· «σταθερή παρειά» = η παρειά που δεν μετακινείται. Κωδικοί «πρώην» = Rev.00.


Κωδ.	Τύπ.	Θέση / περιγραφή	Από x ; y	Έως x ; y	Μήκος	Πάχος	EDGE	Σταθερή παρειά
T4-01	T4	Βόρειος τοίχος έρκερ Υπν.1	0,80 ; 0,00	4,80 ; 0,11	4,00	0,11	0,20	εξωτ. (y 0,00)
T4-02	T4	Ανατ. επιστροφή έρκερ Υπν.1 (πάνω από Κ2)	4,69 ; 0,11	4,80 ; 0,50	0,39	0,11	0,20	εξωτ. (x 4,80)
T4-03	T4	Βόρειος τοίχος δυτ. έρκερ (δυτ. λαμπάς W2.09)	0,00 ; 3,05	0,20 ; 3,16	0,20	0,11	0,15	εξωτ. (y 3,05)
T4-04	T4	Βόρειος τοίχος δυτ. έρκερ (ανατ. λαμπάς W2.09)	0,70 ; 3,05	0,80 ; 3,16	0,11	0,10	0,15	εξωτ. (y 3,05)
T4-05	T4	Δυτικός τοίχος έρκερ λουτρού (ευθύγραμμο τμήμα)	0,00 ; 3,16	0,11 ; 4,55	1,39	0,11	0,15	εξωτ. (x 0,00)
T4-06	T4	Νότια επιστροφή έρκερ λουτρού → Κ10	0,60 ; 5,04	0,80 ; 5,15	0,20	0,11	0,25	εξωτ. (y 5,15)
T4-07	T4	Δυτικός τοίχος ΝΔ προεξοχής κουζίνας	9,50 ; 9,45	9,61 ; 10,25	0,80	0,11	0,20	εξωτ. (x 9,50)
T4-08	T4	Νότιος τοίχος ΝΔ προεξοχής κουζίνας	9,61 ; 10,14	10,70 ; 10,25	1,09	0,11	0,20	εξωτ. (y 10,25)
T4-09	T4	Δυτικός τοίχος ΝΑ προεξοχής κουζίνας	12,75 ; 9,45	12,86 ; 10,17	0,72	0,11	0,20	εξωτ. (x 12,75)
T4-10	T4	Νότιος τοίχος ΝΑ προεξοχής (ευθύγρ. τμήμα)	12,86 ; 10,06	13,35 ; 10,17	0,49	0,11	0,20	εξωτ. (y 10,17)
T4-11	T4	Ανατ. τοίχος ΝΑ προεξοχής (ευθύγρ. τμήμα)	13,76 ; 9,45	13,87 ; 9,65	0,20	0,11	0,20	εξωτ. (x 13,87)
T1-01	T1	Πεσσός ΒΔ πάνω από Κ1	0,80 ; 0,11	1,05 ; 0,50	0,39	0,25	0,30	εξωτ. (x 0,80)
T1-02	T1	Λωρίδα Κ1 → W2.08	0,80 ; 1,20	1,05 ; 1,25	0,25	0,05	0,30	εξωτ. (x 0,80)
T1-03	T1	Πεσσός δυτ. Υπν.1 (W2.08 → λουτρό)	0,80 ; 2,75	1,05 ; 3,20	0,45	0,25	0,30	εξωτ. (x 0,80)
T1-04	T1	Βόρειος τοίχος Υπν.2 (Κ2 → πεσσός)	6,60 ; 0,50	9,45 ; 0,75	2,85	0,25	0,25	ίδια (0,25)
T1-05	T1	ΒΑ πεσσός Υπν.2 (→ W2.06)	9,45 ; 0,50	9,70 ; 1,45	0,95	0,25	0,30	εξωτ. (x 9,70)
T1-06	T1	Πεσσός W2.06 → Κ3	9,45 ; 2,45	9,70 ; 3,00	0,55	0,25	0,30	εξωτ. (x 9,70)
T1-07	T1	Βόρειος τοίχος πλατύσκαλου Κ3 → Κ4	9,70 ; 3,00	11,05 ; 3,25	1,35	0,25	0,25	ίδια (0,25)
T1-08	T1	Λαμπάς δυτικά Κ6 (τούβλο ως σχέδιο)	10,90 ; 4,85	11,05 ; 5,10	0,25	0,15	0,25	ίδια (0,25)
T1-11	T1	Ανατ. τοίχος κλιμακοστασίου – πρόσοψη (W2.05 → γωνία)	13,10 ; 5,80	13,35 ; 7,55	1,75	0,25	0,25	ίδια (0,25)
T1-12	T1	ΝΑ γωνιακό τμήμα πρόσοψης (κλιμακοστάσιο / κουζίνα)	13,10 ; 7,55	13,95 ; 7,80	0,85	0,25	0,25	ίδια (0,25)
T1-13	T1	Πεσσός νότιος Κ9 → W2.02	3,40 ; 9,20	4,10 ; 9,45	0,70	0,25	0,30	εξωτ. (y 9,45)
T1-14	T1	Λαμπάς W2.02 → Κ8	8,85 ; 9,20	9,00 ; 9,45	0,25	0,15	0,30	εξωτ. (y 9,45)
T1-15	T1	ΝΑ γωνιακός πεσσός (Κ7 → προεξοχή), νότιο σκέλος	13,35 ; 9,20	13,87 ; 9,45	0,52	0,25	0,30	εξωτ. (y 9,45)
T1-15β	T1	ΝΑ γωνιακός πεσσός, ανατ. σκέλος (λαμπάς W2.04)	13,62 ; 9,15	13,87 ; 9,20	0,25	0,05	0,20	εξωτ. (x 13,87)
T1-16	T1	Πεσσός Κ10 → W2.01	1,40 ; 5,15	1,65 ; 5,65	0,50	0,25	0,30	εξωτ. (x 1,40)
T5-01	T5	Επένδυση 0,10 βόρεια πυρήνα (Κ3 → καμπύλη)	9,70 ; 2,75	13,10 ; 2,85	3,40	0,10	0,10	ίδια (0,10)
T6-01	T6	Δυτ. τοίχος κλιμακοστασίου, ΕΙΣΟΔΟΣ → νότιος (πρώην T1-09)	9,45 ; 6,30	9,60 ; 7,75	1,45	0,15	0,20	κλιμ/σιο (x 9,60)
T6-02	T6	Νότιος τοίχος κλιμακοστασίου → κουζίνα (πρώην T1-10)	9,60 ; 7,60	13,10 ; 7,75	3,50	0,15	0,20	κλιμ/σιο (y 7,60)

Κωδ.	Τύπ.	Θέση / περιγραφή	Από x ; y	Έως x ; y	Μήκος	Πάχος	EDGE	Σταθερή παρειά
T7-01	T7	Υπν.1 / Λουτρό – τοίχος λεκάνης WC (πρώην T2-01)	5,00 ; 0,80	5,21 ; 3,25	2,45	0,21	0,15	Υπν.1 (x 5,00)
T7-02	T7	Υπν.1 / Λουτρό γονέων – τοίχος λεκάνης WC (πρώην T2-04)	1,90 ; 3,25	3,55 ; 3,46	1,65	0,21	0,15	Υπν.1 (y 3,25)
T2A-01	T2A	Λουτρό γονέων / Χωλ – 15 cm ως σχέδιο (πρώην T2-05)	3,15 ; 3,46	3,30 ; 5,05	1,59	0,15	0,15	ίδια (0,15)
T2-02	T2	Νότιος τοίχος Λουτρού (μεταξύ Θ1 και Θ2)	4,35 ; 3,25	5,60 ; 3,35	1,25	0,10	0,15	λουτρό (y 3,25)
T2-03	T2	Λουτρό / Υπν.2	6,40 ; 0,80	6,50 ; 3,45	2,65	0,10	0,15	Υπν.2 (x 6,50)
T2-03β	T2	Λαμπάς Θ2 (προεξοχή 0,10)	6,30 ; 3,25	6,40 ; 3,35	0,10	0,10	0,15	λαμπάς Θ2 (x 6,30)
T2-06	T2	Βόρειος τοίχος Καθιστικού (δυτ. τμήμα)	1,70 ; 5,05	5,45 ; 5,15	3,75	0,10	0,15	καθιστικό (y 5,15)
T2-07	T2	Τοίχος ντουλάπας χωλ	5,35 ; 4,30	5,45 ; 5,05	0,75	0,10	0,15	χωλ (x 5,45)
T2-08	T2	Βόρειος τοίχος Καθιστικού (ανατ. τμήμα)	6,35 ; 5,05	9,40 ; 5,15	3,05	0,10	0,15	καθιστικό (y 5,15)
T2-09	T2	Υπν.2 / Χωλ (νότια Θ5)	6,40 ; 4,25	6,50 ; 5,05	0,80	0,10	0,15	Υπν.2 (x 6,50)
T2-10	T2	Λουτρό γονέων / ντους έρκερ (βόρεια Θ4)	1,00 ; 3,16	1,10 ; 3,53	0,37	0,10	0,15	λουτρό (x 1,10)
T2-10β	T2	Λαμπάς Θ3	1,10 ; 3,25	1,20 ; 3,35	0,10	0,10	0,15	λουτρό (y 3,25)
T2-11	T2	Λουτρό γονέων / ντους έρκερ (νότια Θ4)	1,00 ; 4,33	1,10 ; 4,85	0,52	0,10	0,15	λουτρό (x 1,10)
T4-05κ	T4	Καμπύλη ΝΔ γωνία έρκερ λουτρού (μήκος εξωτ. τόξου)	κ. 0,60 ; 4,55	R 0,60 / 0,49	0,942	0,11	0,15	εξωτ. ακτίνα
T5-01κ	T5	Καμπύλη ΒΑ γωνία επένδυσης πυρήνα (μήκος εξωτ. τόξου)	κ. 13,10 ; 3,00	R 0,25 / 0,15	0,393	0,10	0,10	εξωτ. ακτίνα
T4-10κ	T4	Καμπύλη ΝΑ προεξοχή κουζίνας (μήκος εξωτ. τόξου)	κ. 13,35 ; 9,65	R 0,52 / 0,41	0,817	0,11	0,20	εξωτ. ακτίνα
T3-01	T3	Επένδυση T1-01 – Ανατ. παρειά (Υπν.1)	1,05 ; 0,11	1,105 ; 0,50	0,39	0,055	–	παρειά τούβλου
T3-02	T3	Επένδυση T1-03 – Ανατ. παρειά (Υπν.1)	1,05 ; 2,75	1,105 ; 3,20	0,45	0,055	–	παρειά τούβλου
T3-03	T3	Επένδυση T1-04 – Νότια παρειά (Υπν.2)	6,60 ; 0,75	9,45 ; 0,805	2,85	0,055	–	παρειά τούβλου
T3-04	T3	Επένδυση T1-05 – Δυτ. παρειά (Υπν.2)	9,395 ; 0,805	9,45 ; 1,45	0,645	0,055	–	παρειά τούβλου
T3-05	T3	Επένδυση T1-06 – Δυτ. παρειά (Υπν.2)	9,395 ; 2,45	9,45 ; 3,00	0,55	0,055	–	παρειά τούβλου
T3-06	T3	Επένδυση T1-07 – Νότια παρειά (πλατύσκαλο)	9,70 ; 3,25	11,05 ; 3,305	1,35	0,055	–	παρειά τούβλου
T3-07	T3	Επένδυση T1-11 – Δυτ. παρειά (κλιμακοστάσιο)	13,045 ; 5,80	13,10 ; 7,60	1,80	0,055	–	παρειά τούβλου
T3-08	T3	Επένδυση T1-12 – Νότια παρειά (κουζίνα) → λαμπάς W2.04	13,35 ; 7,80	13,62 ; 7,855	0,27	0,055	–	παρειά τούβλου
T3-10	T3	Επένδυση T1-15 – Βόρεια παρειά (κουζίνα)	13,35 ; 9,145	13,62 ; 9,20	0,27	0,055	–	παρειά τούβλου
T3-11	T3	Επένδυση T1-14 – Βόρεια παρειά (καθιστικό)	8,85 ; 9,145	9,00 ; 9,20	0,15	0,055	–	παρειά τούβλου
T3-12	T3	Επένδυση T1-13 – Βόρεια παρειά (καθιστικό)	3,40 ; 9,145	4,10 ; 9,20	0,70	0,055	–	παρειά τούβλου
T3-13	T3	Επένδυση T1-16 – Ανατ. παρειά (καθιστικό)	1,65 ; 5,15	1,705 ; 5,65	0,50	0,055	–	παρειά τούβλου

Σύνολα μήκους ανά τύπο (m): T1 = 11,86 T3 = 9,925 T2 = 13,34 T2A = 1,59 T4 = 11,349 T5 = 3,793 T6 = 4,95 T7 = 4,10 (μήκη σε παρειές, χωρίς αφαίρεση ανοιγμάτων· T3 = μήκη επένδυσης)


ΛΕΠΤΟΜΕΡΕΙΕΣ ΤΥΠΩΝ ΤΟΙΧΟΠΟΙΙΑΣ – οριζόντιες τομές, κλίμακα 1:5 (πάχη σε cm)

T1 + T3 Εξωτερικός τοίχος με εσωτερική επένδυση

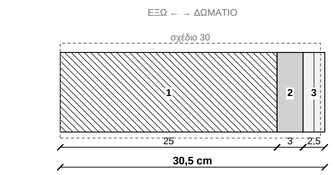


1 τούβλο 25 cm (+εξωτ. επίχρισμα/μόνωση)
2 σκελετός 3 cm
3 διπλή γυψοσανίδα 2×12,5 mm
διακεκ.: πεσσοί σχεδίου 30 – εξωτ. παρειά σταθερή

T2 Τυπικό εσωτερικό χώρισμα

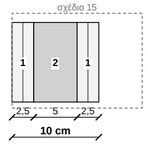


1 διπλή γυψοσανίδα 2×12,5 mm
2 σκελετός 5 cm
διακεκ.: σχεδιασμένο 15 – σταθερή παρειά κατά πίνακα τοίχων

T2A Μόνο T2A-01 (πρώην T2-05)

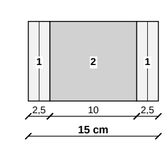


1 διπλή γυψοσανίδα 2×12,5 mm
2 σκελετός 10 cm
παρειές = σχεδιασμένες (x 3,15 / 3,30)

T4 Τοίχος ERKER

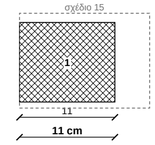


1 απλό τούβλο 11 cm (+επιχρίσματα)
διακεκ.: σχεδιασμένο πάχος 15/20 –
εξωτερική παρειά σταθερή

T6 Κλιμακοστάσιο – γυψοσανίδα (ΠΡΟΤΑΣΗ)

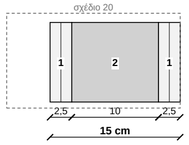

1 διπλή γυψοσανίδα 2×12,5 mm
2 σκελετός 10 cm + πετροβάμβακας
διακεκ.: σχεδιασμένο 20 – παρειά κλιμ/σίου σταθερή

T7 Τοίχος λεκάνης WC

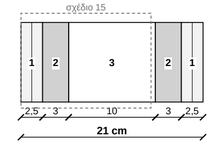

1 διπλή γυψοσανίδα 2×12,5 mm
2 σκελετός 3 cm 3 κενό 10 cm
διακεκ.: σχεδιασμένο 15 – παρειά Υπν.1 σταθερή, +6 προς λουτρό

ΑΡΓΥΡΟΥΠΟΛΗ – ΚΩΝΣΤΑΝΤΙΝΟΥΠΟΛΕΩΣ 12 & ΑΓ. ΒΑΡΒΑΡΑΣ (Ο.Τ. 103-15)
Πενταόροφο κτήριο κατοικιών με υπόγειο, σοφίτα και δώμα – INTERKAT A.E. / ARKAD I.K.E.

ΣΧΕΔΙΟ ΧΑΡΑΞΗΣ ΤΟΙΧΟΠΟΙΙΩΝ – ΚΑΤΟΨΗ Β΄ ΟΡΟΦΟΥ

Φύλλο 2/2: πίνακας τοίχων (συντεταγμένες, μήκη, πάχη, σύνολα ανά τύπο).

Βάση: EDGE, Μελέτη Εφαρμογής Α-10-2F «Κάτοψη Β΄ ορόφου» R00, 23/07/2026, 1:50 – γεωμετρία διανυσματικά από το PDF
Προδιαγραφή τοίχων: Γ. Ζαρκαδάς 09/2026 (Rev.01 21/09, Rev.02 22/09: πραγματικά πάχη στο σχέδιο). Οι θέσεις ΠΡΟΣ ΕΠΙΒΕΒΑΙΩΣΗ επιβεβαιώνονται από EDGE πριν τη χάραξη.

Κλίμακα 1:50 (A2) – διαστάσεις σε m | Ημερομηνία 22/09/2026 | **Φύλλο 2/2 Rev. 02**