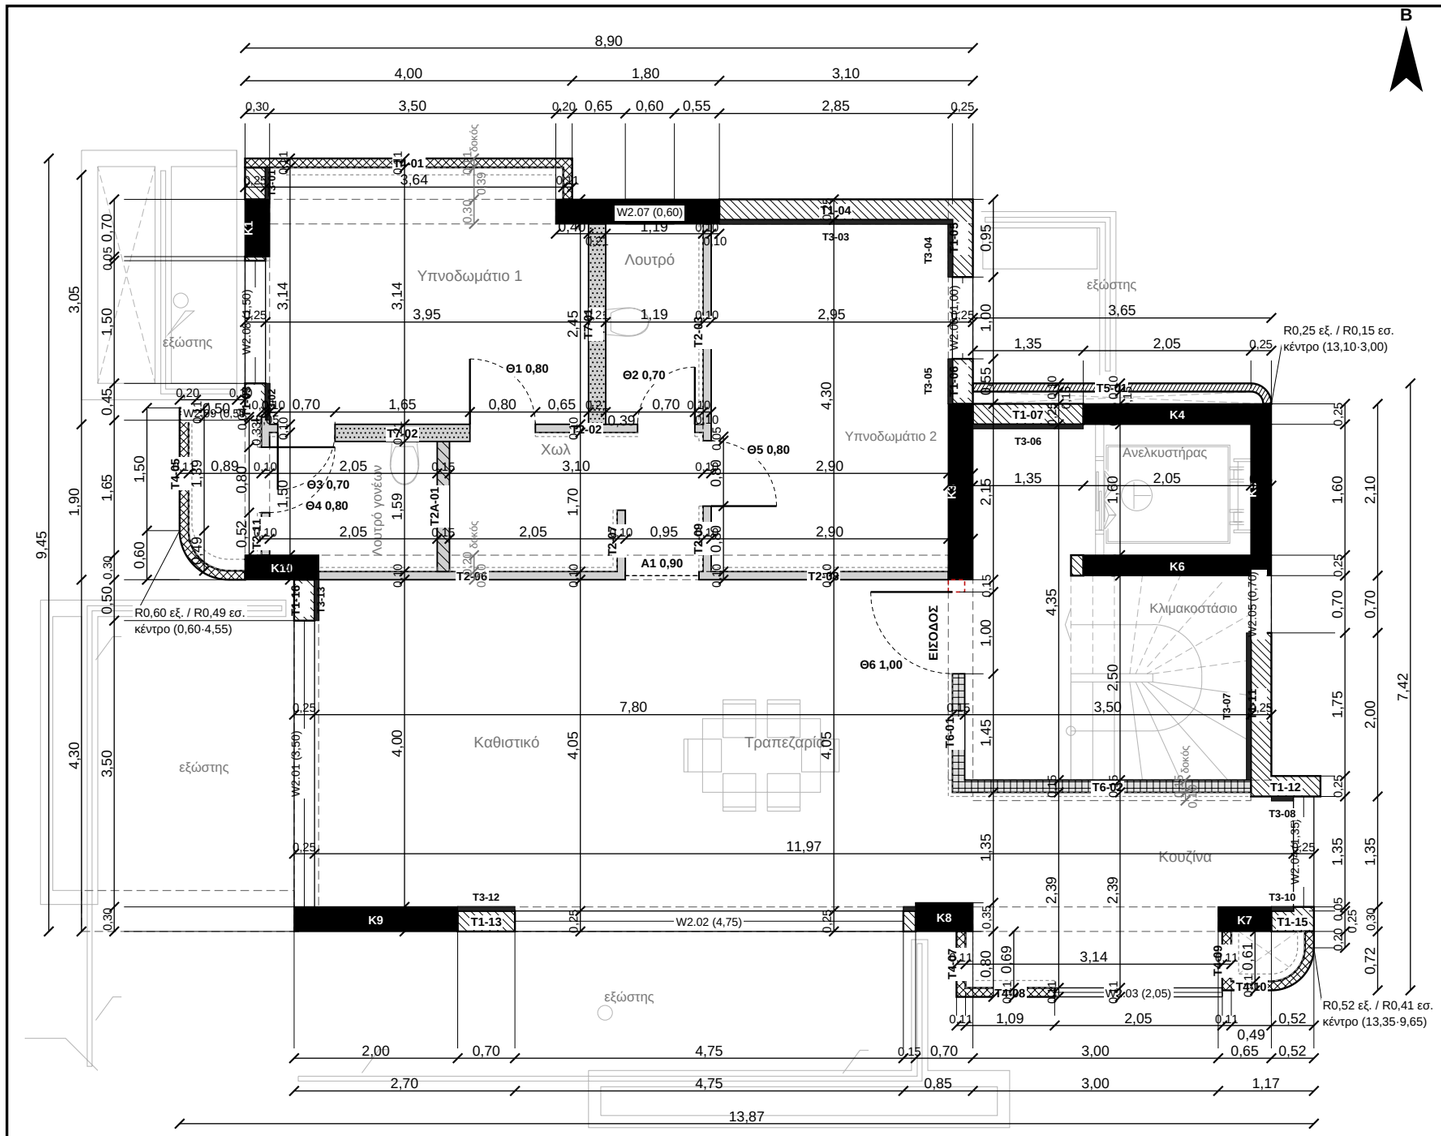


ΥΠΟΜΝΗΜΑ

- T1 – τούβλο 25 cm + εσωτ. επένδυση T3 (30,5)
- T3 – επένδυση: σκελ. 3 + 2 γυψοσ. = 5,5 cm
- T2 – σκελ. 5 + 2×2 γυψοσ. = 10 cm
- T2A – σκελ. 10 + 2×2 γυψοσ. = 15 cm (μόνο T2A-01)
- T4 – ERKER απλό τούβλο 11 cm
- T5 – τούβλο 10 cm (ως σχέδιο)
- T6 – κλιμακοστάσιο: γυψοσανίδα 15 cm (πρόταση)
- T7 – τοίχος WC: 3+2γ / κενό 10 / 3+2γ = 21 cm
- Παρειά αρχιτεκτονικού όπου διαφέρει (αναφορά)
- Οπλ. σκυρόδεμα K1–K10
- Δοκός οροφής (προβολή)
- Παράθυρο / πόρτα
- Προς επιβεβαίωση

Διαστάσεις σε m, σε παρειές τούβλου/σκελετού/μπετόν με τα νέα πάχη, χωρίς επιχρίσματα και μόνωση. Αρχή 0,00·0,00 = ΒΔ γωνία (βόρεια παρειά T4-01 / δυτική παρειά T4-05).

ΠΙΝΑΚΑΣ ΤΥΠΩΝ ΤΟΙΧΟΠΟΙΙΑΣ (πάχη σε cm)

Κωδ.	Περιγραφή / θέση	Σύνθεση	Πάχος	EDGE
T1	Εξωτερική τοιχοποιία (περίμετρος, πρόσοψη κλιμακοστασίου)	Τούβλο 25 cm + εσωτερική επένδυση T3	25 (+5,5)	25 / 30
T3	Εσωτερική επένδυση όλων των T1	Σκελετός 3 cm + διπλή γυψοσανίδα 2×12,5 mm (μία πλευρά)	5,5	–
T2	Τυπικά εσωτερικά χωρίσματα	Σκελετός 5 cm + διπλή γυψοσανίδα 2×12,5 mm εκατέρωθεν	10	15
T2A	Μόνο T2A-01 (Λουτρό γονέων / Χωλ, πρώην T2-05)	Σκελετός 10 cm + διπλή γυψοσανίδα εκατέρωθεν	15	15
T4	Τοίχοι ERKER (προεξοχές)	Απλό τούβλο 11 cm	11	15 / 20
T5	Περιμετρικά πυρήνα ανελκυστήρα (ως σχέδιο)	Απλό τούβλο 10 cm	10	10
T6	Κλιμακοστάσιο προς διαμέρισμα (T6-01/02)	Γυψοσανίδα – ΠΡΟΤΑΣΗ: σκελετός 10 + 2×12,5 mm εκατέρωθεν + πετροβάμβακας (προς καθορισμό)	15	20
T7	Τοίχοι λεκανών WC (T7-01/02)	Σκελετός 3 + διπλή γυψοσανίδα + κενό 10 + σκελετός 3 + διπλή γυψοσανίδα	21	15

Στήλη EDGE = πάχος στο αρχιτεκτονικό A-10-2F. Όπου διαφέρει, η αρχική παρειά φαίνεται με γκρι διακεκομμένη γραμμή. Θέσεις ΠΡΟΣ ΕΠΙΒΕΒΑΙΩΣΗ: βλ. Rev.02 A2 1:50 (σημ. 1–9).

ΠΙΝΑΚΑΣ ΑΝΟΙΓΜΑΤΩΝ (πλάτη / θέσεις / φορά)

Κωδ.	Είδος	Πλάτος	Ποδιά / Ύψος	Θέση (λαμπάδες)	Φορά / παρατήρηση
W2.01	παράθυρο	3,50	0,00 / 2,40	y 5,65 → 9,15, τοίχος x 1,40–1,65	ανοιγόμενο/σταθερό κατά πίνακα κουφωμάτων A-50
W2.02	παράθυρο	4,75	0,00 / 2,40	x 4,10 → 8,85, τοίχος y 9,20–9,45	ανοιγόμενο/σταθερό κατά πίνακα κουφωμάτων A-50
W2.03	παράθυρο	2,05	1,00 / 1,50	x 10,70 → 12,75, τοίχος y 10,14–10,25	ανοιγόμενο/σταθερό κατά πίνακα κουφωμάτων A-50
W2.04	παράθυρο	1,35	1,00 / 1,50	y 7,80 → 9,15, τοίχος x 13,62–13,87	ανοιγόμενο/σταθερό κατά πίνακα κουφωμάτων A-50
W2.05	παράθυρο	0,70	0,15 / 1,50	y 5,10 → 5,80, τοίχος x 13,10–13,35	ανοιγόμενο/σταθερό κατά πίνακα κουφωμάτων A-50
W2.06	παράθυρο	1,00	0,00 / 2,40	y 1,45 → 2,45, τοίχος x 9,45–9,70	ανοιγόμενο/σταθερό κατά πίνακα κουφωμάτων A-50
W2.07	παράθυρο	0,60	1,50 / 2,40	x 5,45 → 6,05, τοίχος y 0,50–0,80	άνοιγμα σε τοιχίο K2 – βλ. στατικά
W2.08	παράθυρο	1,50	0,00 / 2,40	y 1,25 → 2,75, τοίχος x 0,80–1,05	ανοιγόμενο/σταθερό κατά πίνακα κουφωμάτων A-50
W2.09	παράθυρο	0,50	1,10 / 2,40	x 0,20 → 0,70, τοίχος y 3,05–3,16	ανοιγόμενο/σταθερό κατά πίνακα κουφωμάτων A-50
Θ1	πόρτα	0,80	– / 2,20	x 3,55 → 4,35, τοίχος y 3,25–3,35	Υπνοδωμάτιο 1 – μεντεσές δυτικά, ανοίγει προς Υπν.1 (βόρεια)
Θ2	πόρτα	0,70	– / 2,20	x 5,60 → 6,30, τοίχος y 3,25–3,35	Λουτρό – μεντεσές ανατολικά, ανοίγει προς λουτρό (βόρεια)
Θ3	πόρτα	0,70	– / 2,20	x 1,20 → 1,90, τοίχος y 3,25–3,35	Λουτρό γονέων – μεντεσές δυτικά, ανοίγει προς λουτρό (νότια)
Θ4	πόρτα	0,80	– / 2,20	y 3,53 → 4,33, τοίχος x 1,00–1,10	Ντους έρκερ – μεντεσές βόρεια, ανοίγει προς λουτρό (ανατολικά)
Θ5	πόρτα	0,80	– / 2,20	y 3,45 → 4,25, τοίχος x 6,40–6,50	Υπνοδωμάτιο 2 – μεντεσές νότια, ανοίγει προς Υπν.2 (ανατολικά)
Θ6	πόρτα	1,00	– / 2,20	y 5,30 → 6,30, τοίχος x 9,45–9,60	ΕΙΣΟΔΟΣ – μεντεσές βόρεια, ανοίγει προς Καθιστικό (δυτικά)
A1	άνοιγμα	0,90	– / –	x 5,45 → 6,35, τοίχος y 5,05–5,15	Άνοιγμα χωλ → Καθιστικό, χωρίς πόρτα

ΑΡΓΥΡΟΥΠΟΛΗ
Κων/πόλεως 12 & Αγ. Βαρβάρας
Ο.Τ. 103-15

ΣΧΕΔΙΟ ΧΑΡΑΞΗΣ ΤΟΙΧΟΠΟΙΙΩΝ
ΚΑΤΟΨΗ Β΄ ΟΡΟΦΟΥ

Βάση: EDGE A-10-2F
R00 – 23/07/2026
INTERKAT A.E. / ARKAD I.K.E.

Κλίμακα 1:75 (A3)
23/09/2026
Rev. 02 – πραγματικά πάχη
Φύλλο 1/2

ΣΧΕΔΙΟ ΧΑΡΑΞΗΣ ΤΟΙΧΟΠΟΙΙΩΝ – ΚΑΤΟΨΗ Β΄ ΟΡΟΦΟΥ – ΠΙΝΑΚΑΣ ΤΟΙΧΩΝ & ΛΕΠΤΟΜΕΡΕΙΕΣ ΤΥΠΩΝ (φύλλο 2/2, Rev.02)

Συντεταγμένες παρειών (m) από την αρχή 0,00·0,00 (ΒΔ γωνία). Πάχη = πάχη προδιαγραφής· στήλη EDGE = πάχος στο A-10-2F· «σταθερή παρειά» = η παρειά που δεν μετακινείται. Κωδικοί «πρώην» = Rev.00.


Κωδ.	Τύπ.	Θέση / περιγραφή	Από x ; y	Έως x ; y	Μήκος	Πάχος	EDGE	Σταθερή παρειά
T4-01	T4	Βόρειος τοίχος έρκερ Υπν.1	0,80 ; 0,00	4,80 ; 0,11	4,00	0,11	0,20	εξωτ. (y 0,00)
T4-02	T4	Ανατ. επιστροφή έρκερ Υπν.1 (πάνω από K2)	4,69 ; 0,11	4,80 ; 0,50	0,39	0,11	0,20	εξωτ. (x 4,80)
T4-03	T4	Βόρειος τοίχος δυτ. έρκερ (δυτ. λαμπάς W2.09)	0,00 ; 3,05	0,20 ; 3,16	0,20	0,11	0,15	εξωτ. (y 3,05)
T4-04	T4	Βόρειος τοίχος δυτ. έρκερ (ανατ. λαμπάς W2.09)	0,70 ; 3,05	0,80 ; 3,16	0,11	0,10	0,15	εξωτ. (y 3,05)
T4-05	T4	Δυτικός τοίχος έρκερ λουτρού (ευθύγραμμο τμήμα)	0,00 ; 3,16	0,11 ; 4,55	1,39	0,11	0,15	εξωτ. (x 0,00)
T4-06	T4	Νότια επιστροφή έρκερ λουτρού → K10	0,60 ; 5,04	0,80 ; 5,15	0,20	0,11	0,25	εξωτ. (y 5,15)
T4-07	T4	Δυτικός τοίχος ΝΔ προεξοχής κουζίνας	9,50 ; 9,45	9,61 ; 10,25	0,80	0,11	0,20	εξωτ. (x 9,50)
T4-08	T4	Νότιος τοίχος ΝΔ προεξοχής κουζίνας	9,61 ; 10,14	10,70 ; 10,25	1,09	0,11	0,20	εξωτ. (y 10,25)
T4-09	T4	Δυτικός τοίχος ΝΑ προεξοχής κουζίνας	12,75 ; 9,45	12,86 ; 10,17	0,72	0,11	0,20	εξωτ. (x 12,75)
T4-10	T4	Νότιος τοίχος ΝΑ προεξοχής (ευθύγρ. τμήμα)	12,86 ; 10,06	13,35 ; 10,17	0,49	0,11	0,20	εξωτ. (y 10,17)
T4-11	T4	Ανατ. τοίχος ΝΑ προεξοχής (ευθύγρ. τμήμα)	13,76 ; 9,45	13,87 ; 9,65	0,20	0,11	0,20	εξωτ. (x 13,87)
T1-01	T1	Πεσσός ΒΔ πάνω από K1	0,80 ; 0,11	1,05 ; 0,50	0,39	0,25	0,30	εξωτ. (x 0,80)
T1-02	T1	Λωρίδα K1 → W2.08	0,80 ; 1,20	1,05 ; 1,25	0,25	0,05	0,30	εξωτ. (x 0,80)
T1-03	T1	Πεσσός δυτ. Υπν.1 (W2.08 → λουτρό)	0,80 ; 2,75	1,05 ; 3,20	0,45	0,25	0,30	εξωτ. (x 0,80)
T1-04	T1	Βόρειος τοίχος Υπν.2 (K2 → πεσσός)	6,60 ; 0,50	9,45 ; 0,75	2,85	0,25	0,25	ίδια (0,25)
T1-05	T1	ΒΑ πεσσός Υπν.2 (→ W2.06)	9,45 ; 0,50	9,70 ; 1,45	0,95	0,25	0,30	εξωτ. (x 9,70)
T1-06	T1	Πεσσός W2.06 → K3	9,45 ; 2,45	9,70 ; 3,00	0,55	0,25	0,30	εξωτ. (x 9,70)
T1-07	T1	Βόρειος τοίχος πλατύσκαλου K3 → K4	9,70 ; 3,00	11,05 ; 3,25	1,35	0,25	0,25	ίδια (0,25)
T1-08	T1	Λαμπάς δυτικά K6 (τούβλο ως σχέδιο)	10,90 ; 4,85	11,05 ; 5,10	0,25	0,15	0,25	ίδια (0,25)
T1-11	T1	Ανατ. τοίχος κλιμακοστασίου – πρόσοψη (W2.05 → γωνία)	13,10 ; 5,80	13,35 ; 7,55	1,75	0,25	0,25	ίδια (0,25)
T1-12	T1	ΝΑ γωνιακό τμήμα πρόσοψης (κλιμακοστάσιο / κουζίνα)	13,10 ; 7,55	13,95 ; 7,80	0,85	0,25	0,25	ίδια (0,25)
T1-13	T1	Πεσσός νότιος K9 → W2.02	3,40 ; 9,20	4,10 ; 9,45	0,70	0,25	0,30	εξωτ. (y 9,45)
T1-14	T1	Λαμπάς W2.02 → K8	8,85 ; 9,20	9,00 ; 9,45	0,25	0,15	0,30	εξωτ. (y 9,45)
T1-15	T1	ΝΑ γωνιακός πεσσός (K7 → προεξοχή), νότιο σκέλος	13,35 ; 9,20	13,87 ; 9,45	0,52	0,25	0,30	εξωτ. (y 9,45)
T1-15β	T1	ΝΑ γωνιακός πεσσός, ανατ. σκέλος (λαμπάς W2.04)	13,62 ; 9,15	13,87 ; 9,20	0,25	0,05	0,20	εξωτ. (x 13,87)
T1-16	T1	Πεσσός K10 → W2.01	1,40 ; 5,15	1,65 ; 5,65	0,50	0,25	0,30	εξωτ. (x 1,40)
T5-01	T5	Επένδυση 0,10 βόρεια πυρήνα (K3 → καμπύλη)	9,70 ; 2,75	13,10 ; 2,85	3,40	0,10	0,10	ίδια (0,10)
T6-01	T6	Δυτ. τοίχος κλιμακοστασίου, ΕΙΣΟΔΟΣ → νότιος (πρώην T1-09)	9,45 ; 6,30	9,60 ; 7,75	1,45	0,15	0,20	κλιμ/σιο (x 9,60)
T6-02	T6	Νότιος τοίχος κλιμακοστασίου → κουζίνα (πρώην T1-10)	9,60 ; 7,60	13,10 ; 7,75	3,50	0,15	0,20	κλιμ/σιο (y 7,60)

Κωδ.	Τύπ.	Θέση / περιγραφή	Από x ; y	Έως x ; y	Μήκος	Πάχος	EDGE	Σταθερή παρειά
T7-01	T7	Υπν.1 / Λουτρό – τοίχος λεκάνης WC (πρώην T2-01)	5,00 ; 0,80	5,21 ; 3,25	2,45	0,21	0,15	Υπν.1 (x 5,00)
T7-02	T7	Υπν.1 / Λουτρό γονέων – τοίχος λεκάνης WC (πρώην T2-04)	1,90 ; 3,25	3,55 ; 3,46	1,65	0,21	0,15	Υπν.1 (y 3,25)
T2A-01	T2A	Λουτρό γονέων / Χωλ – 15 cm ως σχέδιο (πρώην T2-05)	3,15 ; 3,46	3,30 ; 5,05	1,59	0,15	0,15	ίδια (0,15)
T2-02	T2	Νότιος τοίχος Λουτρού (μεταξύ Θ1 και Θ2)	4,35 ; 3,25	5,60 ; 3,35	1,25	0,10	0,15	λουτρό (y 3,25)
T2-03	T2	Λουτρό / Υπν.2	6,40 ; 0,80	6,50 ; 3,45	2,65	0,10	0,15	Υπν.2 (x 6,50)
T2-03β	T2	Λαμπάς Θ2 (προεξοχή 0,10)	6,30 ; 3,25	6,40 ; 3,35	0,10	0,10	0,15	λαμπάς Θ2 (x 6,30)
T2-06	T2	Βόρειος τοίχος Καθιστικού (δυτ. τμήμα)	1,70 ; 5,05	5,45 ; 5,15	3,75	0,10	0,15	καθιστικό (y 5,15)
T2-07	T2	Τοίχος ντουλάπας χωλ	5,35 ; 4,30	5,45 ; 5,05	0,75	0,10	0,15	χωλ (x 5,45)
T2-08	T2	Βόρειος τοίχος Καθιστικού (ανατ. τμήμα)	6,35 ; 5,05	9,40 ; 5,15	3,05	0,10	0,15	καθιστικό (y 5,15)
T2-09	T2	Υπν.2 / Χωλ (νότια Θ5)	6,40 ; 4,25	6,50 ; 5,05	0,80	0,10	0,15	Υπν.2 (x 6,50)
T2-10	T2	Λουτρό γονέων / ντους έρκερ (βόρεια Θ4)	1,00 ; 3,16	1,10 ; 3,53	0,37	0,10	0,15	λουτρό (x 1,10)
T2-10β	T2	Λαμπάς Θ3	1,10 ; 3,25	1,20 ; 3,35	0,10	0,10	0,15	λουτρό (y 3,25)
T2-11	T2	Λουτρό γονέων / ντους έρκερ (νότια Θ4)	1,00 ; 4,33	1,10 ; 4,85	0,52	0,10	0,15	λουτρό (x 1,10)
T4-05κ	T4	Καμπύλη ΝΔ γωνία έρκερ λουτρού (μήκος εξωτ. τόξου)	κ. 0,60 ; 4,55	R 0,60 / 0,49	0,942	0,11	0,15	εξωτ. ακτίνα
T5-01κ	T5	Καμπύλη ΒΑ γωνία επένδυσης πυρήνα (μήκος εξωτ. τόξου)	κ. 13,10 ; 3,00	R 0,25 / 0,15	0,393	0,10	0,10	εξωτ. ακτίνα
T4-10κ	T4	Καμπύλη ΝΑ προεξοχή κουζίνας (μήκος εξωτ. τόξου)	κ. 13,35 ; 9,65	R 0,52 / 0,41	0,817	0,11	0,20	εξωτ. ακτίνα
T3-01	T3	Επένδυση T1-01 – Ανατ. παρειά (Υπν.1)	1,05 ; 0,11	1,105 ; 0,50	0,39	0,055	–	παρειά τούβλου
T3-02	T3	Επένδυση T1-03 – Ανατ. παρειά (Υπν.1)	1,05 ; 2,75	1,105 ; 3,20	0,45	0,055	–	παρειά τούβλου
T3-03	T3	Επένδυση T1-04 – Νότια παρειά (Υπν.2)	6,60 ; 0,75	9,45 ; 0,805	2,85	0,055	–	παρειά τούβλου
T3-04	T3	Επένδυση T1-05 – Δυτ. παρειά (Υπν.2)	9,395 ; 0,805	9,45 ; 1,45	0,645	0,055	–	παρειά τούβλου
T3-05	T3	Επένδυση T1-06 – Δυτ. παρειά (Υπν.2)	9,395 ; 2,45	9,45 ; 3,00	0,55	0,055	–	παρειά τούβλου
T3-06	T3	Επένδυση T1-07 – Νότια παρειά (πλατύσκαλο)	9,70 ; 3,25	11,05 ; 3,305	1,35	0,055	–	παρειά τούβλου
T3-07	T3	Επένδυση T1-11 – Δυτ. παρειά (κλιμακοστάσιο)	13,045 ; 5,80	13,10 ; 7,60	1,80	0,055	–	παρειά τούβλου
T3-08	T3	Επένδυση T1-12 – Νότια παρειά (κουζίνα) → λαμπάς W2.04	13,35 ; 7,80	13,62 ; 7,855	0,27	0,055	–	παρειά τούβλου
T3-10	T3	Επένδυση T1-15 – Βόρεια παρειά (κουζίνα)	13,35 ; 9,145	13,62 ; 9,20	0,27	0,055	–	παρειά τούβλου
T3-11	T3	Επένδυση T1-14 – Βόρεια παρειά (καθιστικό)	8,85 ; 9,145	9,00 ; 9,20	0,15	0,055	–	παρειά τούβλου
T3-12	T3	Επένδυση T1-13 – Βόρεια παρειά (καθιστικό)	3,40 ; 9,145	4,10 ; 9,20	0,70	0,055	–	παρειά τούβλου
T3-13	T3	Επένδυση T1-16 – Ανατ. παρειά (καθιστικό)	1,65 ; 5,15	1,705 ; 5,65	0,50	0,055	–	παρειά τούβλου

Σύνολα μήκους ανά τύπο (m): T1 = 11,86 T3 = 9,925 T2 = 13,34 T2A = 1,59 T4 = 11,349 T5 = 3,793 T6 = 4,95 T7 = 4,10 (μήκη σε παρειές, χωρίς αφαίρεση ανοιγμάτων· T3 = μήκη επένδυσης)


ΛΕΠΤΟΜΕΡΕΙΕΣ ΤΥΠΩΝ ΤΟΙΧΟΠΟΙΙΑΣ – οριζόντιες τομές, κλίμακα 1:5 (πάχη σε cm)

T1 + T3 Εξωτερικός τοίχος με εσωτερική επένδυση

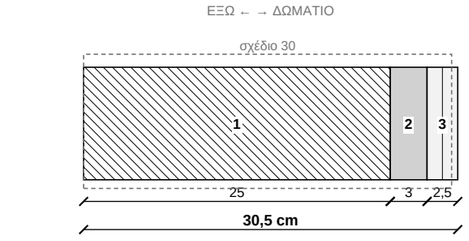


1 τούβλο 25 cm (+εξωτ. επίχρισμα/μόνωση)
2 σκελετός 3 cm
3 διπλή γυψοσανίδα 2×12,5 mm
διακεκ.: πεσσοί σχεδίου 30 – εξωτ. παρειά σταθερή

T2 Τυπικό εσωτερικό χώρισμα

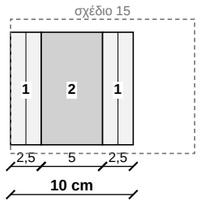


1 διπλή γυψοσανίδα 2×12,5 mm
2 σκελετός 5 cm
διακεκ.: σχεδιασμένο 15 – σταθερή παρειά κατά πίνακα τοίχων

T2A Μόνο T2A-01 (πρώην T2-05)

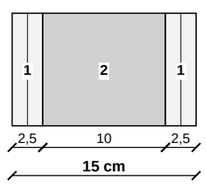


1 διπλή γυψοσανίδα 2×12,5 mm
2 σκελετός 10 cm
παρειές = σχεδιασμένες (x 3,15 / 3,30)

T4 Τοίχος ERKER

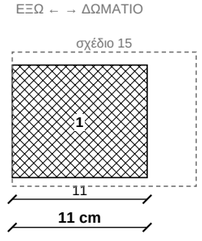


1 απλό τούβλο 11 cm (+επιχρίσματα)
διακεκ.: σχεδιασμένο πάχος 15/20 –
εξωτερική παρειά σταθερή

T6 Κλιμακοστάσιο – γυψοσανίδα (ΠΡΟΤΑΣΗ)

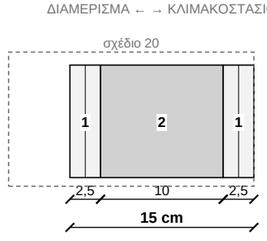

1 διπλή γυψοσανίδα 2×12,5 mm
2 σκελετός 10 cm + πετροβάμβακας
διακεκ.: σχεδιασμένο 20 – παρειά κλιμ/σίου σταθερή

T7 Τοίχος λεκάνης WC

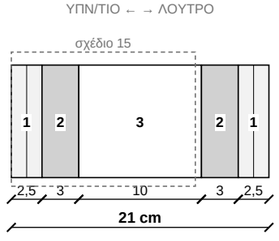

1 διπλή γυψοσανίδα 2×12,5 mm
2 σκελετός 3 cm 3 κενό 10 cm
διακεκ.: σχεδιασμένο 15 – παρειά Υπν.1 σταθερή, +6 προς λουτρό

ΑΡΓΥΡΟΥΠΟΛΗ – ΚΩΝ/ΠΟΛΕΩΣ 12 & ΑΓ. ΒΑΡΒΑΡΑΣ
ΧΑΡΑΞΗ ΤΟΙΧΟΠΟΙΙΩΝ – Β΄ ΟΡΟΦΟΣ – πίνακας τοίχων
Βάση: EDGE A-10-2F R00 23/07/2026 – INTERKAT / ARKAD

23/09/2026 Rev. 02 Φύλλο 2/2