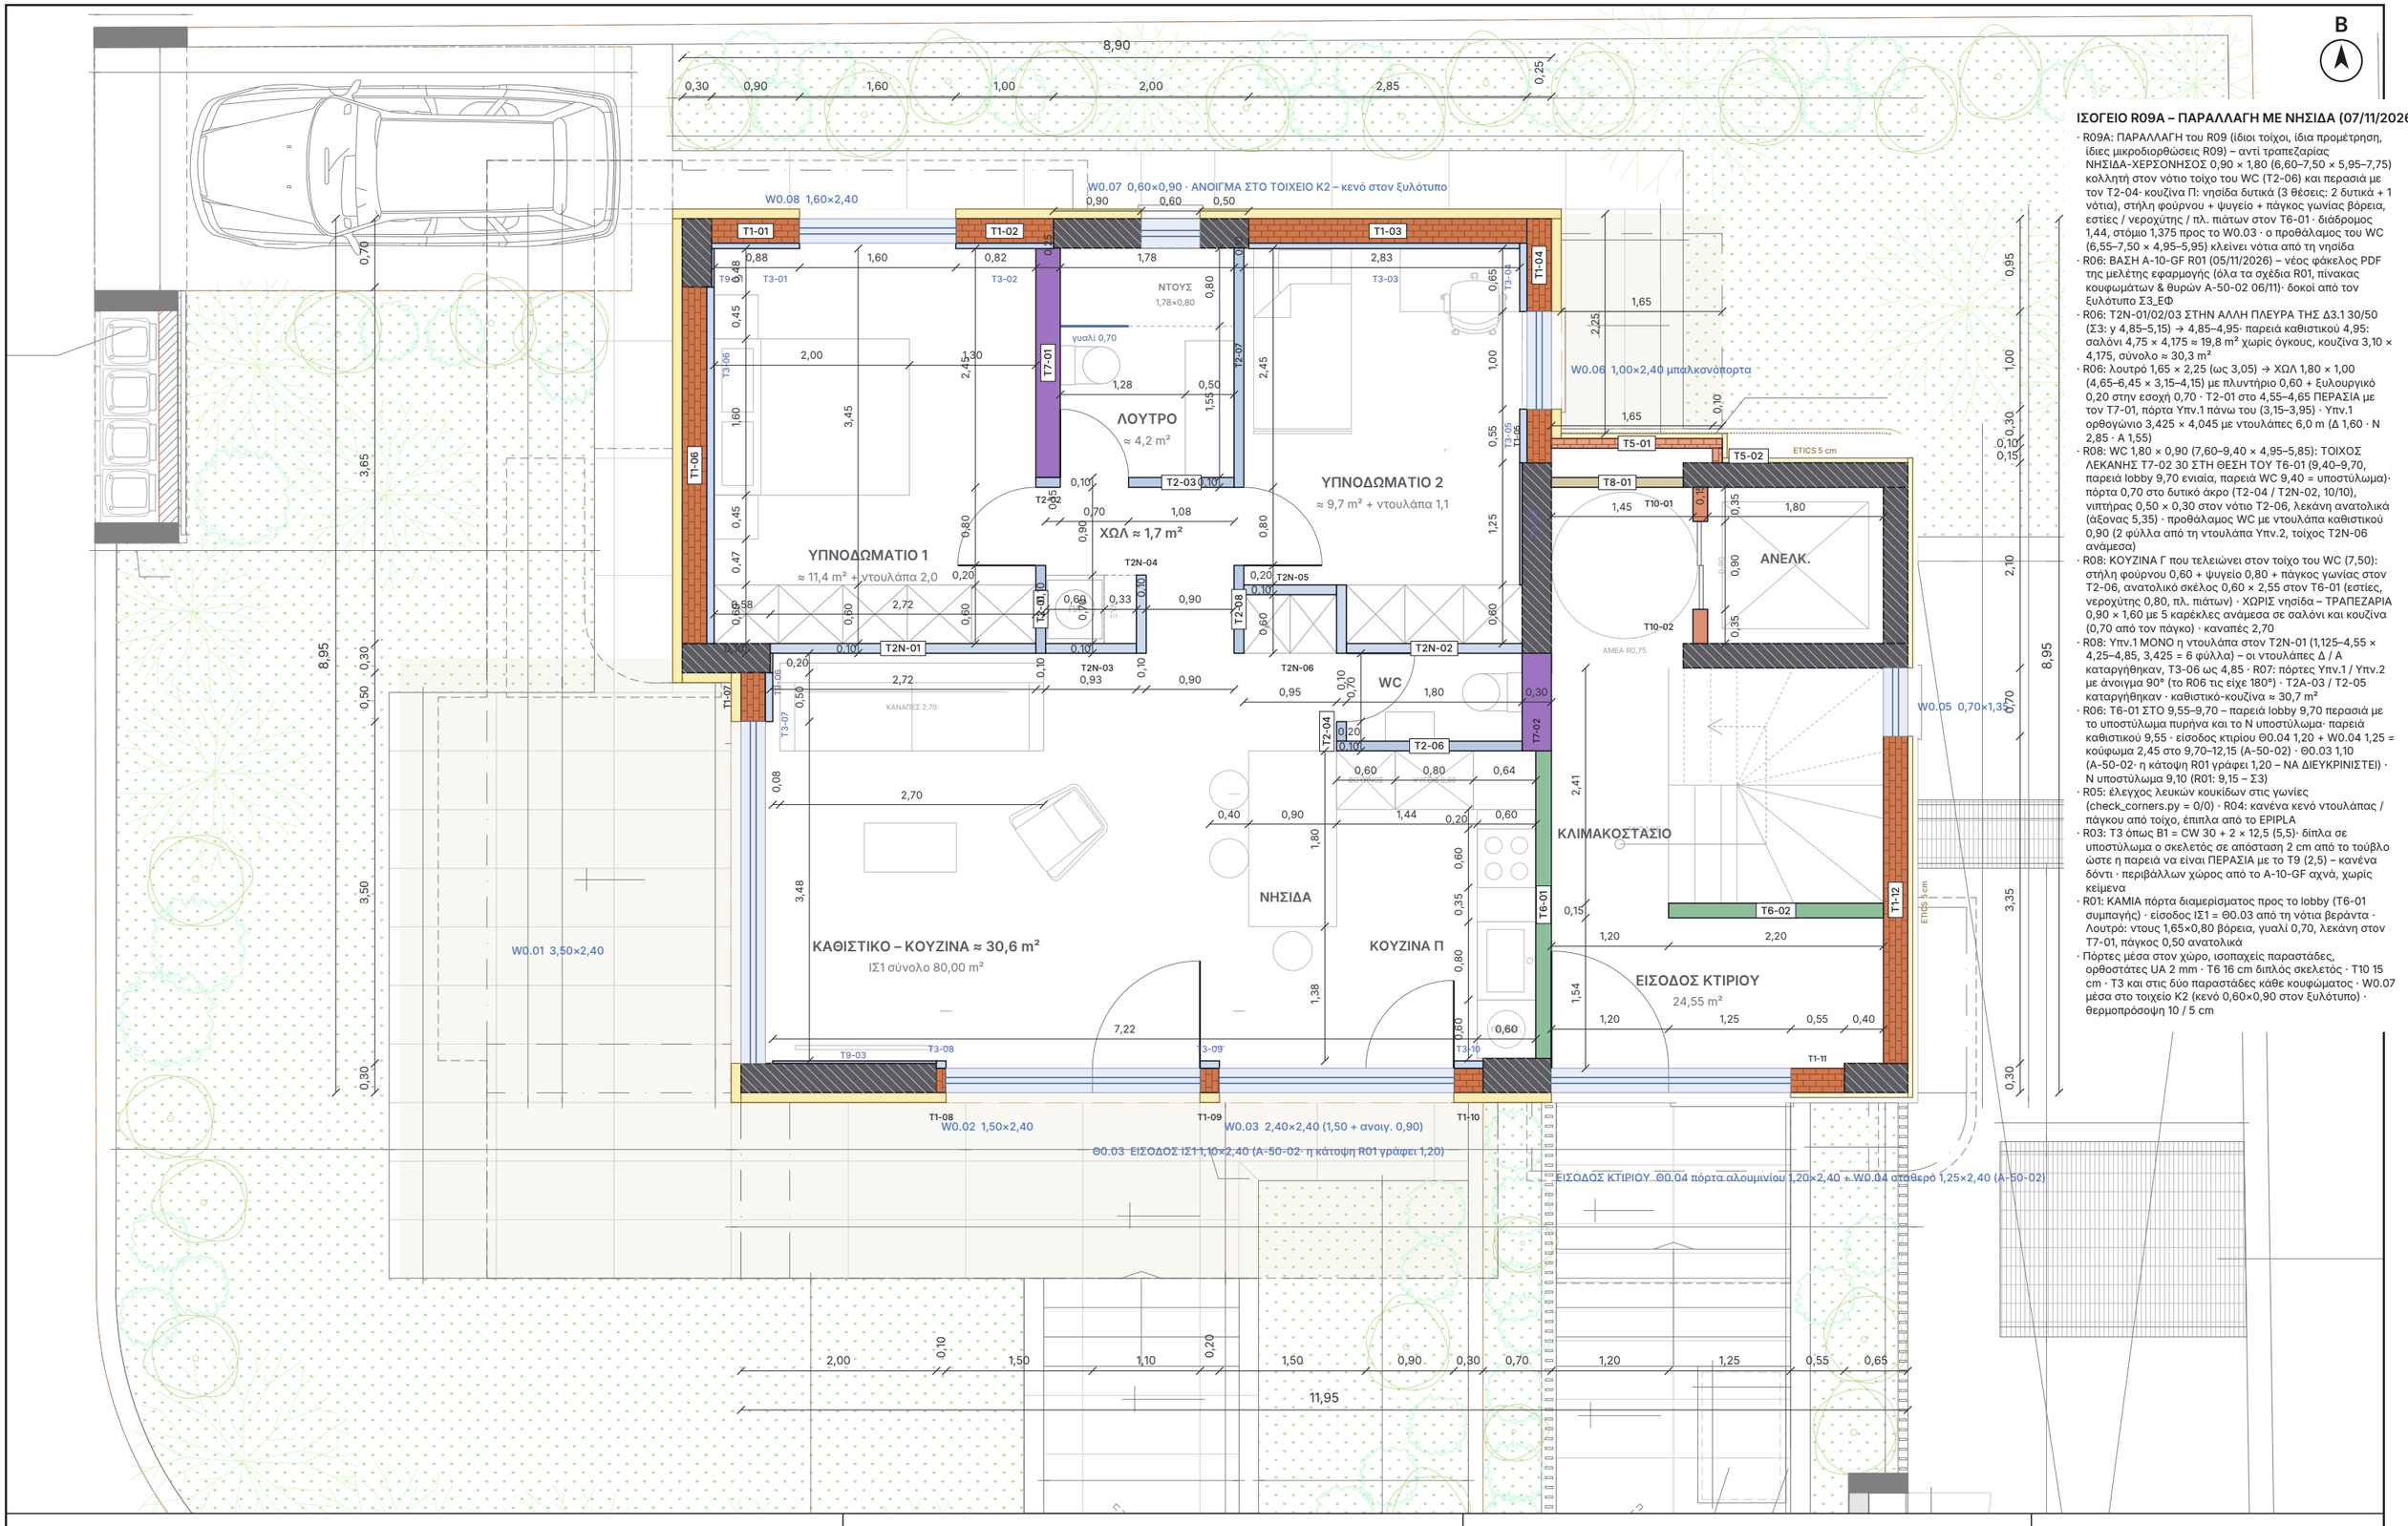


ΙΣΟΓΕΙΟ R09A – ΠΑΡΑΛΛΑΓΗ ΜΕ ΝΗΣΙΔΑ (07/11/2026)

- R09A: ΠΑΡΑΛΛΑΓΗ του R09 (ίδιοι τοίχοι, ίδια προμέτρηση, ίδιες μικροδιορθώσεις R09) – αντί τραπεζαρίας ΝΗΣΙΔΑ-ΧΕΡΣΟΝΗΣΟΣ 0,90 × 1,80 (6,60–7,50 × 5,95–7,75) κολλητή στον νότιο τοίχο του WC (T2-06) και περασιά με τον T2-04· κουζίνα Π: νησίδα δυτικά (3 θέσεις: 2 δυτικά + 1 νότια), στήλη φούρνου + ψυγείο + πάγκος γωνίας βόρεια, εστίες / νεροχύτης / πλ. πιάτων στον T6-01 · διάδρομος 1,44, στόμιο 1,375 προς το W0.03 · ο προθάλαμος του WC (6,55–7,50 × 4,95–5,95) κλείνει νότια από τη νησίδα
- R06: ΒΑΣΗ A-10-GF R01 (05/11/2026) – νέος φάκελος PDF της μελέτης εφαρμογής (όλα τα σχέδια R01, πίνακας κουφωμάτων & θυρών A-50-02 06/11)· δοκοί από τον ξυλότυπο Σ3_ΕΦ
- R06: T2N-01/02/03 ΣΤΗΝ ΑΛΛΗ ΠΛΕΥΡΑ ΤΗΣ Δ3.1 30/50 (Σ3: y 4,85–5,15) → 4,85–4,95· παρειά καθιστικού 4,95: σαλόνι 4,75 × 4,175 ≈ 19,8 m² χωρίς όγκους, κουζίνα 3,10 × 4,175, σύνολο ≈ 30,3 m²
- R06: λουτρό 1,65 × 2,25 (ως 3,05) → ΧΩΛ 1,80 × 1,00 (4,65–6,45 × 3,15–4,15) με πλυντήριο 0,60 + ξυλουργικό 0,20 στην εσοχή 0,70 · T2-01 στο 4,55–4,65 ΠΕΡΑΣΙΑ με τον T7-01, πόρτα Υπν.1 πάνω του (3,15–3,95) · Υπν.1 ορθογώνιο 3,425 × 4,045 με ντουλάπες 6,0 m (Δ 1,60 · N 2,85 · A 1,55)
- R08: WC 1,80 × 0,90 (7,60–9,40 × 4,95–5,85): ΤΟΙΧΟΣ ΛΕΚΑΝΗΣ T7-02 30 ΣΤΗ ΘΕΣΗ ΤΟΥ T6-01 (9,40–9,70, παρειά lobby 9,70 ενιαία, παρειά WC 9,40 = υποστύλωμα)· πόρτα 0,70 στο δυτικό άκρο (T2-04 / T2N-02, 10/10), νιπτήρας 0,50 × 0,30 στον νότιο T2-06, λεκάνη ανατολικά (άξονας 5,35) · προθάλαμος WC με ντουλάπα καθιστικού 0,90 (2 φύλλα από τη ντουλάπα Υπν.2, τοίχος T2N-06 ανάμεσα)
- R08: ΚΟΥΖΙΝΑ Γ που τελειώνει στον τοίχο του WC (7,50): στήλη φούρνου 0,60 + ψυγείο 0,80 + πάγκος γωνίας στον T2-06, ανατολικό σκέλος 0,60 × 2,55 στον T6-01 (εστίες, νεροχύτης 0,80, πλ. πιάτων) · ΧΩΡΙΣ νησίδα – ΤΡΑΠΕΖΑΡΙΑ 0,90 × 1,60 με 5 καρέκλες ανάμεσα σε σαλόνι και κουζίνα (0,70 από τον πάγκο) · καναπές 2,70
- R08: Υπν.1 ΜΟΝΟ η ντουλάπα στον T2N-01 (1,125–4,55 × 4,25–4,85, 3,425 = 6 φύλλα) – οι ντουλάπες Δ / Α καταργήθηκαν, T3-06 ως 4,85 · R07: πόρτες Υπν.1 / Υπν.2 με άνοιγμα 90° (το R06 τις είχε 180°) · T2A-03 / T2-05 καταργήθηκαν · καθιστικό-κουζίνα ≈ 30,7 m²
- R06: T6-01 ΣΤΟ 9,55–9,70 – παρειά lobby 9,70 περασιά με το υποστύλωμα πυρήνα και το N υποστύλωμα· παρειά καθιστικού 9,55 · είσοδος κτιρίου Θ0.04 1,20 + W0.04 1,25 = κούφωμα 2,45 στο 9,70–12,15 (A-50-02) · Θ0.03 1,10 (A-50-02· η κάτοψη R01 γράφει 1,20 – ΝΑ ΔΙΕΥΚΡΙΝΙΣΤΕΙ) · N υποστύλωμα 9,10 (R01: 9,15 – Σ3)
- R05: έλεγχος λευκών κουκίδων στις γωνίες (check_corners.py = 0/0) · R04: κανένα κενό ντουλάπας / πάγκου από τοίχο, έπιπλα από το EPIPLA
- R03: T3 όπως B1 = CW 30 + 2 × 12,5 (5,5)· δίπλα σε υποστύλωμα ο σκελετός σε απόσταση 2 cm από το τούβλο ώστε η παρειά να είναι ΠΕΡΑΣΙΑ με το T9 (2,5) – κανένα δόντι · περιβάλλων χώρος από το A-10-GF αχνά, χωρίς κείμενα
- R01: ΚΑΜΙΑ πόρτα διαμερίσματος προς το lobby (T6-01 συμπαγής) · είσοδος ΙΣ1 = Θ0.03 από τη νότια βεράντα · Λουτρό: ντους 1,65×0,80 βόρεια, γυαλί 0,70, λεκάνη στον T7-01, πάγκος 0,50 ανατολικά
- Πόρτες μέσα στον χώρο, ισοπαχείς παραστάδες, ορθοστάτες UA 2 mm · T6 16 cm διπλός σκελετός · T10 15 cm · T3 και στις δύο παραστάδες κάθε κουφώματος · W0.07 μέσα στο τοιχείο K2 (κενό 0,60×0,90 στον ξυλότυπο) · θερμοπρόσοψη 10 / 5 cm

ΕΡΓΟ

ΠΕΝΤΑΟΡΟΦΟ ΚΤΗΡΙΟ ΚΑΤΟΙΚΙΩΝ – ΑΡΓΥΡΟΥΠΟΛΗ
Κωνσταντινουπόλεως 12 & Αγ. Βαρβάρας · Ο.Τ. 103-15
Εργοδότης: INTERKAT Α.Ε. · Κατασκευή: ARKAD Ι.Κ.Ε.

ΘΕΜΑ ΣΧΕΔΙΟΥ

ΚΑΤΟΨΗ ΤΟΙΧΟΠΟΙΙΩΝ – ΙΣΟΓΕΙΟΥ
Είδη τοιχοποιιών · διαστάσεις χάραξης · κουφώματα · εξώστες
ΙΣΟΓΕΙΟ – ΙΣ1

ΒΑΣΗ


Βάση: A-10-GF R01 (05/11/2026, Drive) · Σ3_ΕΦ · κανόνες B1 R20

ΑΡ. ΣΧΕΔΙΟΥ

T-01
Κλίμακα 1:60 · A3
07/11/2026 · R09A

T1 Εξωτερική οπτοπλινθοδομή 1:4

πάχος 25 cm

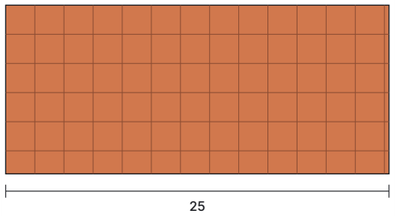

θερμομονωτικό τούβλο κάθετων οπών 25 cm · θερμοπρόσοψη 10 cm έξω · επένδυση T3 μέσα όπου σημειώνεται




Τοίχοι: T1-01, T1-02, T1-03, T1-04, T1-05, T1-06, T1-07, T1-08, T1-09, T1-10, T1-11, T1-12


Μήκος 15,10 m · επιφάνεια ≈ 45,3 m²

T5 Οπτοπλινθοδομή πυρήνα 1:4

πάχος 10 cm

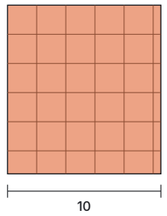

θερμομονωτικό τούβλο κάθετων οπών 10 cm · γύρω από τον πυρήνα (ανελκυστήρας – ηλεκτροστάσιο)

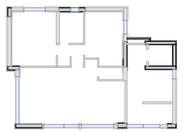


Τοίχοι: T5-01, T5-02


Μήκος 1,90 m · επιφάνεια ≈ 5,7 m²

T10 Μέτωπο ανελκυστήρα 1:4

πάχος 15 cm

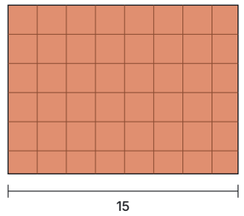

θερμομονωτικό τούβλο κάθετων οπών 15 cm · μέτωπο φρεατίου εκατέρωθεν της πόρτας 0,90 · στην ΕΣΩΤΕΡΙΚΗ παρειά της δοκού μετώπου του φρεατίου (Δ5.1 25/40 στον Σ3, x 11,05–11,30) → x 11,15–11,30, σε όλους τους ορόφους (R21 / ισόγειο R09, Γιάννης 07/11) · θέση πόρτας προς επιβεβαίωση από τον προμηθευτή

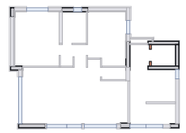


Τοίχοι: T10-01, T10-02


Μήκος 0,70 m · επιφάνεια ≈ 2,1 m²

T3 Επένδυση τοίχου 1:4

πάχος 5,5 cm

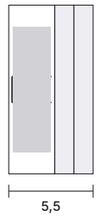

σκελετός 30 · 2 × γυψοσανίδα 12,5 · στις εσωτερικές παρειές των T1 – ΟΧΙ όπου πλακάκι ή ντουλάπα, ΟΧΙ στα έρκερ

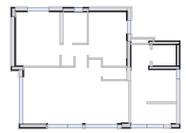


Τοίχοι: T3-01, T3-02, T3-03, T3-04, T3-05, T3-06, T3-07, T3-08, T3-09, T3-10


Μήκος 10,68 m · επιφάνεια ≈ 32,0 m²

T9 Επένδυση υποστυλώματος 1:4

πάχος 2,5 cm

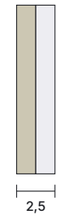

κόλλα + 1 × γυψοσανίδα 12,5 (ένα φύλλο) · στις παρειές υποστυλωμάτων μέσα στα διαμερίσματα – ΟΧΙ όπου πλακάκι ή ντουλάπα

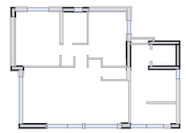


Τοίχοι: T9-01, T9-02, T9-03, T9-06

Μήκος 3,52 m · επιφάνεια ≈ 10,6 m²

T2 Χώρισμα γυψοσανίδας 1:4

πάχος 10 cm

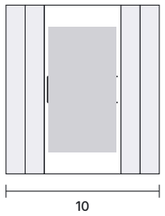

2 × γυψοσανίδα 12,5 · σκελετός CW 50 · 2 × γυψοσανίδα 12,5 · εσωτερικά χωρίσματα · ανθυγρή γυψοσανίδα στην πλευρά των λουτρών · ανοίγματα πορτών με ορθοστάτες UA 50 (2 mm)




Τοίχοι: T2-07, T2-08, T2-01, T2-02, T2-03, T2-04, T2-06


Μήκος 7,68 m · επιφάνεια ≈ 23,0 m²

T2N Χώρισμα γυψ. – πλευρά ντουλάπας 1:4

πάχος 8,75 cm

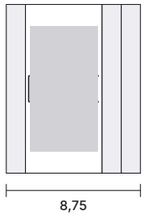

1 × γυψοσανίδα 12,5 (πλευρά ντουλάπας) · σκελετός CW 50 · 2 × γυψοσανίδα 12,5 · όπου η μία παρειά βλέπει σε ντουλάπα: ένα φύλλο αρκεί (κανόνας R15)

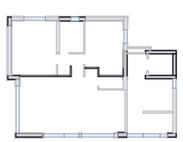


Τοίχοι: T2N-01, T2N-02, T2N-05, T2N-06, T2N-03, T2N-04


Μήκος 7,90 m · επιφάνεια ≈ 23,7 m²

T7 Τοίχος λεκάνης WC 1:4

πάχος 25 cm

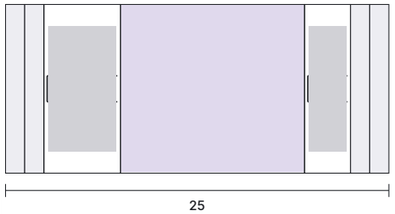

2 × γυψοσανίδα 12,5 · σκελετός CW 50 · κενό 12 cm (καζανάκι γυψοσανίδας στον σκελετό + κατακόρυφη στήλη Ø110, έξοδος Ø90) · σκελετός CW 30 · 2 × γυψοσανίδα 12,5 · ΟΛΟΙ οι τοίχοι λεκανών · ανθυγρή προς το λουτρό · στην πλευρά ντουλάπας 1 φύλλο · ανοίγματα πορτών με ορθοστάτες UA 50 (2 mm)

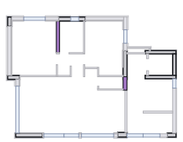


Τοίχοι: T7-01, T7-02


Μήκος 3,35 m · επιφάνεια ≈ 10,0 m²

T6 Τοίχος κλιμακοστασίου – διπλός σκελετός 1:4

πάχος 16 cm

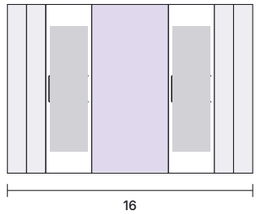

2 × γυψοσανίδα 12,5 πυράντοχη · σκελετός CW 30 · κενό 5 cm · σκελετός CW 30 · 2 × γυψοσανίδα 12,5 πυράντοχη = 16 cm (R09, Γιάννης) · προς lobby / κλιμακοστάσιο (T6-01) και μέτωπο σκάλας (T6-02) · χωρίς πόρτα

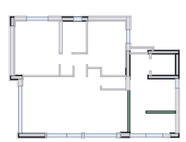


Τοίχοι: T6-01, T6-02


Μήκος 5,35 m · επιφάνεια ≈ 16,0 m²

T8 Τοίχος shaft 1:4

πάχος 10 cm

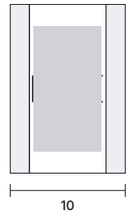

πλαίσιο + ανοιγόμενα φύλλα γυψοσανίδας · μέτωπο shaft ηλεκτρολογικών

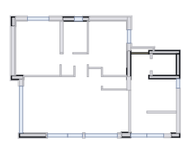

Τοίχοι: T8-01

Μήκος 1,35 m · επιφάνεια ≈ 4,1 m²

Επιφάνειες ενδεικτικές: μήκος × ύψος 3,00 m (τελικό δάπεδο – πλάκα) – οι τοίχοι ορίζονται μεταξύ ανοιγμάτων, χωρίς αφαίρεση κασών. T3 = επένδυση στην εσωτερική παρειά των T1 · T9 = περίμετρος υποστυλώματος × ύψος. R15: T2N = 1 φύλλο στην πλευρά ντουλάπας (T2N-01, T2N-02) · T7-01 1 φύλλο προς Υπν.1.

ΕΡΓΟ

ΠΕΝΤΑΟΡΟΦΟ ΚΤΗΡΙΟ ΚΑΤΟΙΚΙΩΝ – ΑΡΓΥΡΟΥΠΟΛΗ
Κωνσταντινουπόλεως 12 & Αγ. Βαρβάρας · Ο.Τ. 103-15
Εργοδότης: INTERKAT Α.Ε. · Κατασκευή: ARKAD Ι.Κ.Ε.

ΘΕΜΑ ΣΧΕΔΙΟΥ

ΕΙΔΗ ΤΟΙΧΟΠΟΙΙΩΝ – ΙΣΟΓΕΙΟΥ
Είδη τοιχοποιιών · ΙΣΟΓΕΙΟ – ΙΣ1
τομές 1:4 · μήκη – εμβαδά ανά είδος

ΒΑΣΗ

Βάση: κάτοψη τοιχοποιιών T-01 · κάτοψη A-10-GF

ΑΡ. ΣΧΕΔΙΟΥ

T-02
Κλίμακα 1:4 · A3
07/11/2026 · R09A

ΠΡΟΜΕΤΡΗΣΗ ΤΟΙΧΟΠΟΙΙΩΝ – ΙΣΟΓΕΙΟ – ΙΣ1

τετραγωνικά ανά τυπολογία τοίχου · Η = 3,00 m (τελικό δάπεδο – κάτω παρειά πλάκας) · μήκη στον άξονα, χωρίς αφαίρεση κουφωμάτων · R09A

	Τύπος	Περιγραφή	Πάχος cm	Τοίχοι	Μήκος m	Επιφάνεια m²
ΤΟΥΒΛΑ						
	T1	Εξωτερική οπτοπλινθοδομή	25	12	15,10	**45,3**
	T5	Οπτοπλινθοδομή πυρήνα	10	2	1,90	**5,7**
	T10	Μέτωπο ανελκυστήρα	15	2	0,70	**2,1**
	Σύνολο τουβλα					**53,1 m²**
ΧΩΡΙΣΜΑΤΑ ΓΥΨΟΣΑΝΙΔΑΣ						
	T2	Χώρισμα γυψοσανίδας	10	7	7,68	**23,0**
	T2N	Χώρισμα γυψ. – πλευρά ντουλάπας	8,8	6	7,90	**23,7**
	T7	Τοίχος λεκάνης WC	25	2	3,35	**10,0**
	T6	Τοίχος κλιμακοστασίου – διπλός σκελετός	16	2	5,35	**16,0**
	T8	Τοίχος shaft	10	1	1,35	**4,1**
	Σύνολο χωρισματα γυψοσανιδας					**76,9 m²**
ΕΠΕΝΔΥΣΕΙΣ						
	T3	Επένδυση τοίχου	5,5	10	10,68	**32,0**
	T9	Επένδυση υποστυλώματος	2,5	4	3,52	**10,6**
	Σύνολο επενδυσεις					**42,6 m²**
	ΣΥΝΟΛΟ ΤΟΙΧΟΠΟΙΙΩΝ ΙΣ1					**172,6 m²**

ΘΕΡΜΟΠΡΟΣΟΨΗ (ETICS)

10 cm στις όψεις των διαμερισμάτων · 5 cm στο κλιμακοστάσιο / πυρήνα · ύψος 3,20 m (με τη μετώπη πλάκας) · καθαρά = όψη − κουφώματα + λαμπάδες/ανώφλια

Ζώνη	Μήκος όψης m	Μικτά m²	Κουφώματα m²	Λαμπάδες m²	Καθαρά m²
ETICS 10 cm – διαμερίσματα	29,40	94,1	−27,2	+5,9	**72,8**
ETICS 5 cm – κλιμακοστάσιο / πυρήνας	14,15	45,3	−6,8	+2,0	**40,5**
Σύνολο ETICS					**113,3 m²**

ΣΗΜΕΙΩΣΕΙΣ ΚΑΤΟΨΗΣ

• ΠΑΡΑΛΛΑΓΗ R09A – ΝΗΣΙΔΑ ΚΟΛΛΗΤΗ ΣΤΟ WC (Γιάννης 07/11: «κάνε μου και ένα σχέδιο με νησίδα η οποία θα κολλάει στον τοίχο του WC»): ίδιοι τοίχοι με το R09 (η προμέτρηση T-03 δεν αλλάζει). Η νησίδα-χερσόνησος 0,90 × 1,80 (6,60–7,50 × 5,95–7,75) ξεκινά από τον νότιο τοίχο του WC (T2-06, παρειά 5,95) και η ανατολική της παρειά (7,50) είναι περασιά με τον δυτικό τοίχο του WC (T2-04) – δυτικά της ο προθάλαμος του WC (6,55–7,50 × 4,95–5,95) μένει κλειστός νότια, ανοιχτός προς το καθιστικό. Κουζίνα Π: δυτικό σκέλος η νησίδα (3 θέσεις: 2 δυτικά στο 6,20–6,60, 1 στο νότιο άκρο), βόρειο σκέλος στον T2-06 στήλη φούρνου 0,60 (7,50–8,10) + ψυγείο 0,80 (8,10–8,90) + πάγκος γωνίας 0,65, ανατολικό σκέλος 0,60 × 2,55 στον T6-01 (παρειά 9,54· εστίες 6,75–7,35, νεροχύτης 7,70–8,50, πλ. πιάτων 8,50–9,10). Διάδρομος εργασίας 1,44 (7,50–8,94), στόμιο της Π προς νότο 1,375 (7,75–9,125) μπροστά στο W0.03. Χωρίς ξεχωριστή τραπεζαρία – η νησίδα είναι και η τραπεζαρία.

• Θέσεις τοίχων και ανοιγμάτων κατά την κάτοψη ισογείου A-10-GF R01 (EDGE, μελέτη εφαρμογής 05/11/2026, φάκελος PDF στο Drive του έργου) με τους κανόνες του B1 R20 και τις αλλαγές R01–R09 του Γιάννη. Διαστάσεις στο τούβλο / μπετό και στις παρειές της γυψοσανίδας, χωρίς τη θερμοπρόσοψη. Υποστυλώματα / τοιχεία από το A-10-GF, δοκοί από τον ξυλότυπο Σ3_ΕΦ (Δ3.1 30/50 στο y 4,85–5,15 · Δ5.1 25/40 μέτωπο φρεατίου 11,05–11,30)· το R01 δείχνει το N υποστύλωμα στο 9,15–9,45 – εδώ 9,10 όπως B1, να επιβεβαιωθεί.

• Τ3 ΠΕΡΑΣΙΑ (R03, όπως B1): T3 = σκελετός CW 30 + 2 × γυψοσανίδα 12,5 (5,5 cm). Τα υποστυλώματα (30) προεξέχουν 5 cm από την εσωτερική παρειά του τούβλου (25) και παίρνουν κολλητή γυψοσανίδα T9 2,5 cm· όπου η T3 συνεχίζει δίπλα σε υποστύλωμα, ο σκελετός CW 30 στήνεται σε απόσταση 2 cm από το τούβλο ώστε η παρειά της γυψοσανίδας να είναι στο ίδιο επίπεδο με το T9: T3-06 (παρειά 1,125 = T9-01), T3-04/T3-05 (9,375 = T9-02), T3-08/09/10 (9,125 = T9-03). Αλλού η T3 κολλητά στο τούβλο: B 0,805 · Δ καθιστικού 1,705. Όπου πλακάκι, ντουλάπα ή πάγκος: χωρίς T3 / T9 (γυμνό τούβλο / μπετό).

• WC 1,80 × 0,90 ΚΟΛΛΗΤΑ ΣΤΟ ΚΛΙΜΑΚΟΣΤΑΣΙΟ (R08): WC 7,60–9,40 × 4,95–5,85 (1,62 m²), η μακριά πλευρά στον βόρειο τοίχο. ΤΟΙΧΟΣ ΛΕΚΑΝΗΣ T7-02 (30, 9,40–9,70 × 4,95–5,95) ΣΤΗ ΘΕΣΗ ΤΟΥ T6-01: παρειά lobby 9,70 ενιαία, παρειά WC 9,40 = παρειά του υποστυλώματος πυρήνα (κανένα δόντι), 2 γυψ. + CW 50 (καζανάκι, στήλη Ø110) + κενό + CW 30 + 2 γυψ. προς το κλιμακοστάσιο· ο T6-01 συνεχίζει από 5,95 ως 9,10. Λεκάνη προς δύση στον άξονα y 5,35, 1,09 ελεύθερα μπροστά της. Βόρειος τοίχος ο T2N-02 (πλάτη της ντουλάπας Υπν.2 – προς το WC ανθυγρή διπλή), δυτικός ο T2-04 (10, 7,50–7,60 × 5,65–5,85) με την πόρτα 0,70 στο y 4,95–5,65 (παραστάδες 10/10, μεντεσές βόρεια 4,95, διπλώνει στον βόρειο τοίχο), νότιος ο T2-06 (10, 7,50–9,40 × 5,85–5,95) με τον νιπτήρα 0,50 × 0,30 (8,00–8,50) έξω από το τόξο. Μπροστά στην πόρτα ο προθάλαμος 6,55–7,50 × 4,95–5,95 (ανοιχτός στο καθιστικό) με τη ντουλάπα καθιστικού στον βόρειο τοίχο του.

• ΒΟΡΕΙΑ ΖΩΝΗ (R09 – Γιάννης 07/11: «το λουτρό μεγαλώνει κατά 13 πόντους προς το Υπν.1 · το χωλ από 1,00 να γίνει 0,90 και να μεγαλώσει το μπάνιο πάλι · οι T2A να γίνουν T2 · η πόρτα στο λουτρό και η πόρτα στο Υπν.1 να ανοίγουν από την άλλη»): ΛΟΥΤΡΟ 1,78 × 2,35 (4,67–6,45 × 0,80–3,15 ≈ 4,2 m²): T7-01 στο 4,42–4,67 (παρειά Υπν.1 4,42), νότιος τοίχος T2-02 / T2-03 στο 3,15–3,25· ντους 1,78 × 0,80 βόρεια με γυαλί 0,70 στο y 1,60, λεκάνη στον T7-01 (y 2,00), πάγκος 0,50 ανατολικά 1,75–3,15 (1,40), πόρτα 0,70 στο 4,67–5,37 με ΜΕΝΤΕΣΕ ΔΥΤΙΚΑ (4,67) – το φύλλο διπλώνει στον T7-01 ως το 2,45, πάνω από τη λεκάνη (1,80–2,20). ΧΩΛ 1,93 × 0,90 (4,52–6,45 × 3,25–4,15 ≈ 1,7 m²): δυτικά πόρτα Υπν.1 (y 3,25–4,05, στον T2-01 4,42–4,52) με ΜΕΝΤΕΣΕ ΝΟΤΙΑ (4,05) – φύλλο στο y 4,05, 0,20 από τη ντουλάπα· βόρεια πόρτα λουτρού (4,67–5,37)· ανατολικά πόρτα Υπν.2 (y 3,25–4,05, στους T2-07 / T2-08 10 cm – τα T2A 15 καταργήθηκαν, παρειά χωλ 6,45 σταθερή, Υπν.2 από 6,55)· νότια εσοχή 0,70 (y 4,15–4,85): πλυντήριο 0,60 (4,52–5,12) + ξυλουργικό ράφια 0,33 (5,12–5,45, κανένα κενό), T2N-04 επιστροφή 5,45–5,55, άνοιγμα προς καθιστικό 5,55–6,45 (0,90, παραστάδες 10/10, διάδρομος 0,80 ως την παρειά 4,95). Τοίχοι που βλέπουν σε ντουλάπα / πλυντήριο: 1 φύλλο (T2N-01…04).

• T6-01 ΔΙΠΛΟΣ ΣΚΕΛΕΤΟΣ 16 cm ΣΤΟ 9,54–9,70 (R09 – Γιάννης: «τον T6-01 κάντον 3άρι σκελετό διπλή, κενό 5 πόντους, 3άρι σκελετό διπλή»): 2 × γυψοσανίδα 12,5 πυράντοχη + σκελετός CW 30 + κενό 5 cm + σκελετός CW 30 + 2 × γυψοσανίδα 12,5 πυράντοχη = 16 cm (δύο ανεξάρτητοι σκελετοί, χωρίς CW 100 / πετροβάμβακα). Σταθερή η παρειά του lobby 9,70 – μία ευθεία από το φρεάτιο ως την είσοδο, περασιά με το υποστύλωμα πυρήνα και το N υποστύλωμα (R06)· παρειά καθιστικού 9,54 (πάγκος κουζίνας 8,94–9,54). Ο ίδιος τύπος στο μέτωπο της σκάλας T6-02. Συμπαγής, ΧΩΡΙΣ πόρτα προς το lobby.

• Υπν.1 (R08/R09 – Γιάννης: «μόνο η ντουλάπα στον τοίχο T2N-01 · το κρεβάτι να μπει σωστά»): ορθογώνιο 1,125–4,42 × 0,805–4,85 (3,295 × 4,045 ≈ 13,3 m² μικτά, ≈ 11,4 m² ελεύθερα + ντουλάπα 2,0 m²). ΜΟΝΗ ΝΤΟΥΛΑΠΑ 0,60 στον T2N-01: 1,125–4,42 × 4,25–4,85 (3,295 = 5 φύλλα 0,66 ή 6 × 0,55), από την T3-06 ως τον T2-01, πλάτη ο T2N-01 (1,70–4,42, 1 φύλλο προς τη ντουλάπα) και το γυμνό Δ υποστύλωμα (1,125–1,70, παρειά 4,85). Ο T2-01 (4,42–4,52 × 4,05–4,95) περασιά με τον T7-01 (παρειά Υπν.1 4,42 ενιαία)· πάνω του η πόρτα 0,80 από το χωλ (y 3,25–4,05, βόρεια παραστάδα ο T2-02, ΜΕΝΤΕΣΕΣ ΝΟΤΙΑ 4,05, ανοίγει 90° μέσα στο δωμάτιο – φύλλο στο y 4,05, 3,62–4,42, 0,20 από το μέτωπο της ντουλάπας). ΚΡΕΒΑΤΙ 1,60 × 2,00 με κεφαλάρι στη δυτική επένδυση (στον βόρειο τοίχο είναι το W0.08 1,60×2,40), ΚΕΝΤΡΑΡΙΣΜΕΝΟ ανάμεσα στον βόρειο τοίχο και το μέτωπο της ντουλάπας: y 1,73–3,33, κομοδίνα 0,45 × 0,45 εκατέρωθεν (1,28–1,73 / 3,33–3,78)· 0,92 ελεύθερα ως τη ντουλάπα, 1,30 ανάμεσα στα πόδια του κρεβατιού (3,125) και τον T7-01.

• Υπν.2 (6,55–9,375 × 0,805–4,25 ≈ 9,7 m² – R09: δυτικός τοίχος T2-07 / T2-08 10 cm στο 6,45–6,55 αντί T2A 15): ντουλάπα 7,60–9,40 × 4,25–4,85 (1,80, 3 φύλλα)· τα δυτικά φύλλα της (R07 – Γιάννης: «ένα-δύο φύλλα ντουλάπας του Υπν.2 να γυρίσει προς το σαλόνι · χώρισέ τες με τοίχο») γίνονται ΝΤΟΥΛΑΠΑ ΚΑΘΙΣΤΙΚΟΥ 0,95 × 0,60 (6,55–7,50 × 4,35–4,95, 2 φύλλα 0,475 προς το καθιστικό, μέτωπο 4,95 περασιά με τον T2N-02) με πλάτη τον T2N-05 (6,55–7,50 × 4,25–4,35, 1 φύλλο προς τη ντουλάπα, διπλή προς το Υπν.2) και τον ΤΟΙΧΟ T2N-06 (7,50–7,60 × 4,25–4,95, περασιά με τον T2-04 του WC) ανάμεσα στις δύο ντουλάπες. ΠΟΡΤΕΣ ΔΩΜΑΤΙΩΝ πάντα με άνοιγμα 90° (το φύλλο κάθετο στον τοίχο της πόρτας): Υπν.2 0,80 από το χωλ στο y 3,25–4,05 (T2-07 / T2-08), μεντεσές νότια 4,05, φύλλο στο y 4,05 (6,55–7,35) 0,20 από τον T2N-05· Υπν.1 0,80 στον T2-01 (y 3,25–4,05), R09: μεντεσές νότια 4,05, φύλλο στο y 4,05 (3,62–4,42). W0.06 1,00×2,40 μπαλκονόπορτα προς τη ΒΑ βεράντα. T9-02 στο υποστύλωμα πυρήνα 3,00–4,25 περασιά με την T3-05. W0.07 0,60×0,90 μέσα στο τοιχείο K2 (x 5,50–6,10): κενό στον ξυλότυπο από τώρα (ποδιά +1,50).


• ΚΑΘΙΣΤΙΚΟ: δυτικός τοίχος T1-07 1,40–1,65 + T3-07 με παρειά 1,725 (R09 – Γιάννης: «ο T3-07 δεν συνεχίζει περασιά στην κολόνα»: ο σκελετός σε απόσταση από το τούβλο ώστε η παρειά να είναι περασιά με το T9-06 2,5 στην ανατολική παρειά του Δ υποστυλώματος 1,70 × 4,95–5,15 – μία ευθεία από τον T2N-01 ως το W0.01)· T3-10 στον νότιο τοίχο από την παραστάδα του W0.03 ως το N υποστύλωμα (8,70–9,00, R09 – «ο T3-10 γιατί σταματάει;»)· W0.01 3,50×2,40 στο 5,65–9,15· T9-03 στο ΝΔ τοιχείο (παρειά 9,125) περασιά με T3-08 / T3-09. Καναπές, πολυθρόνα (0,45 δυτικότερα), τραπεζάκι, έπιπλο TV από το EPIPLA.

• ΠΥΡΗΝΑΣ (R09 – Γιάννης 07/11): T5-01 10 cm ΟΠΩΣ ΣΤΟΝ B1 («παντού ίδιος θα είναι αυτός»): 9,70–11,45 × 2,75–2,85 ως την άκρη της ΒΑ βεράντας + επιστροφή T5-02 11,35–11,45 × 2,85–3,00 στο τοιχείο του φρεατίου· ανατολικά του 11,45 εξωτερικός τοίχος είναι το ίδιο το τοιχείο 25 του φρεατίου (3,00–3,25) με θερμοπρόσοψη 5 cm στο 2,95–3,00. Shaft Η/Μ εκτός Σ.Δ. στο y 2,85–3,15 × 9,70–11,05 (βάθος 0,30 όπως B1). ΑΝΕΛΚΥΣΤΗΡΑΣ: στον Σ3 η δοκός μετώπου Δ5.1 25/40 κάθεται στο x 11,05–11,30 (εσωτερική παρειά = καθαρή παρειά φρεατίου 11,30)· T10-01 / T10-02 ΤΟΥΒΛΟ 15 cm ΣΤΗΝ ΕΣΩΤΕΡΙΚΗ ΠΑΡΕΙΑ ΤΗΣ ΔΟΚΟΥ (x 11,15–11,30, 0,35 το καθένα, πόρτα 0,90 στο y 3,60–4,50) σε ΟΛΟΥΣ τους ορόφους (B1 → R21)· τα άκρα των τοιχείων του φρεατίου (11,05) προεξέχουν 0,10 στο lobby. Θέση / πλάτος πόρτας προς επιβεβαίωση από τον προμηθευτή. ΜΕΤΩΠΟ ΣΚΑΛΑΣ T6-02 (16, 10,90–13,10 × 7,51–7,66 – «να μπουν τοίχοι για να ορίσουν τη σκάλα»): όπως ο T6-02 του B1, ορίζει το κάτω σκέλος της σκάλας (y 6,30–7,51) προς την είσοδο· το πλατύσκαλο 9,70–10,90 μένει ανοιχτό προς το lobby (δίοδος 1,20) και τον ανελκυστήρα. Κύκλος ΑΜΕΑ R0,75 στο 9,70–11,20. Σκάλα 16 ριχτιών όπως B1 / A-10-GF. ΕΙΣΟΔΟΣ ΚΤΙΡΙΟΥ (A-50-02): ενιαίο κούφωμα αλουμινίου 2,45 στο 9,70–12,15 = πόρτα Θ0.04 1,20×2,40 (9,70–10,90, μεντεσές δυτικά, ανοίγει μέσα) + σταθερό W0.04 1,25×2,40. Καμία πόρτα διαμερίσματος προς το lobby.

• ΚΟΥΦΩΜΑΤΑ (A-50-02 + A-10-GF R01): W0.08 1,60×2,40 (2,00–3,60) · W0.07 0,60×0,90 (ποδιά 1,50) · W0.06 1,00×2,40 (1,45–2,45) · W0.01 3,50×2,40 δίφυλλο επάλληλο (5,65–9,15) · W0.02 1,45 σταθερό (3,50–5,00) · Θ0.03 πόρτα ΙΣ1 1,10×2,40 (5,00–6,10 – ο πίνακας 110, η ετικέτα της κάτοψης R01 1,20: ΝΑ ΔΙΕΥΚΡΙΝΙΣΤΕΙ) · W0.03 2,40 = 1,50 σταθερό + 0,90 ανοιγοανακλινόμενο (6,30–8,70) · Θ0.04 1,20 + W0.04 1,25 · W0.05 0,70×1,35. Πεσσοί 0,10 (3,40–3,50), 0,20, 0,30 όπως ο αρχιτέκτονας – ΠΡΟΣ ΑΠΟΦΑΣΗ αν ο 0,10 ενσωματωθεί στο κούφωμα. Τ3 και στις δύο παραστάδες.

• ΘΕΡΜΟΠΡΟΣΟΨΗ: 10 cm στο διαμέρισμα, 5 cm στον πυρήνα / είσοδο κτιρίου (T5-01, φρεάτιο, T1-12, T1-11). ΥΨΟΣ ισογείου 3,00 (πλάκα οροφής +3,65 κατά Σ3) – επιφάνειες T-03 με H = 3,00.

ΕΡΓΟ	ΘΕΜΑ ΣΧΕΔΙΟΥ	ΒΑΣΗ	ΑΡ. ΣΧΕΔΙΟΥ
ΠΕΝΤΑΟΡΟΦΟ ΚΤΗΡΙΟ ΚΑΤΟΙΚΙΩΝ – ΑΡΓΥΡΟΥΠΟΛΗ Κωνσταντινουπόλεως 12 & Αγ. Βαρβάρας · Ο.Τ. 103-15 Εργοδότης: INTERKAT Α.Ε. · Κατασκευή: ARKAD Ι.Κ.Ε.	**ΠΡΟΜΕΤΡΗΣΗ ΤΟΙΧΟΠΟΙΙΩΝ – ΙΣΟΓΕΙΟΥ** Τετραγωνικά ανά τυπολογία τοίχου · θερμοπρόσοψη 10 / 5 cm ΙΣΟΓΕΙΟ – ΙΣ1	Βάση: κάτοψη τοιχοποιιών T-01 · είδη T-02	**T-03** — · A3 07/11/2026 · R09A

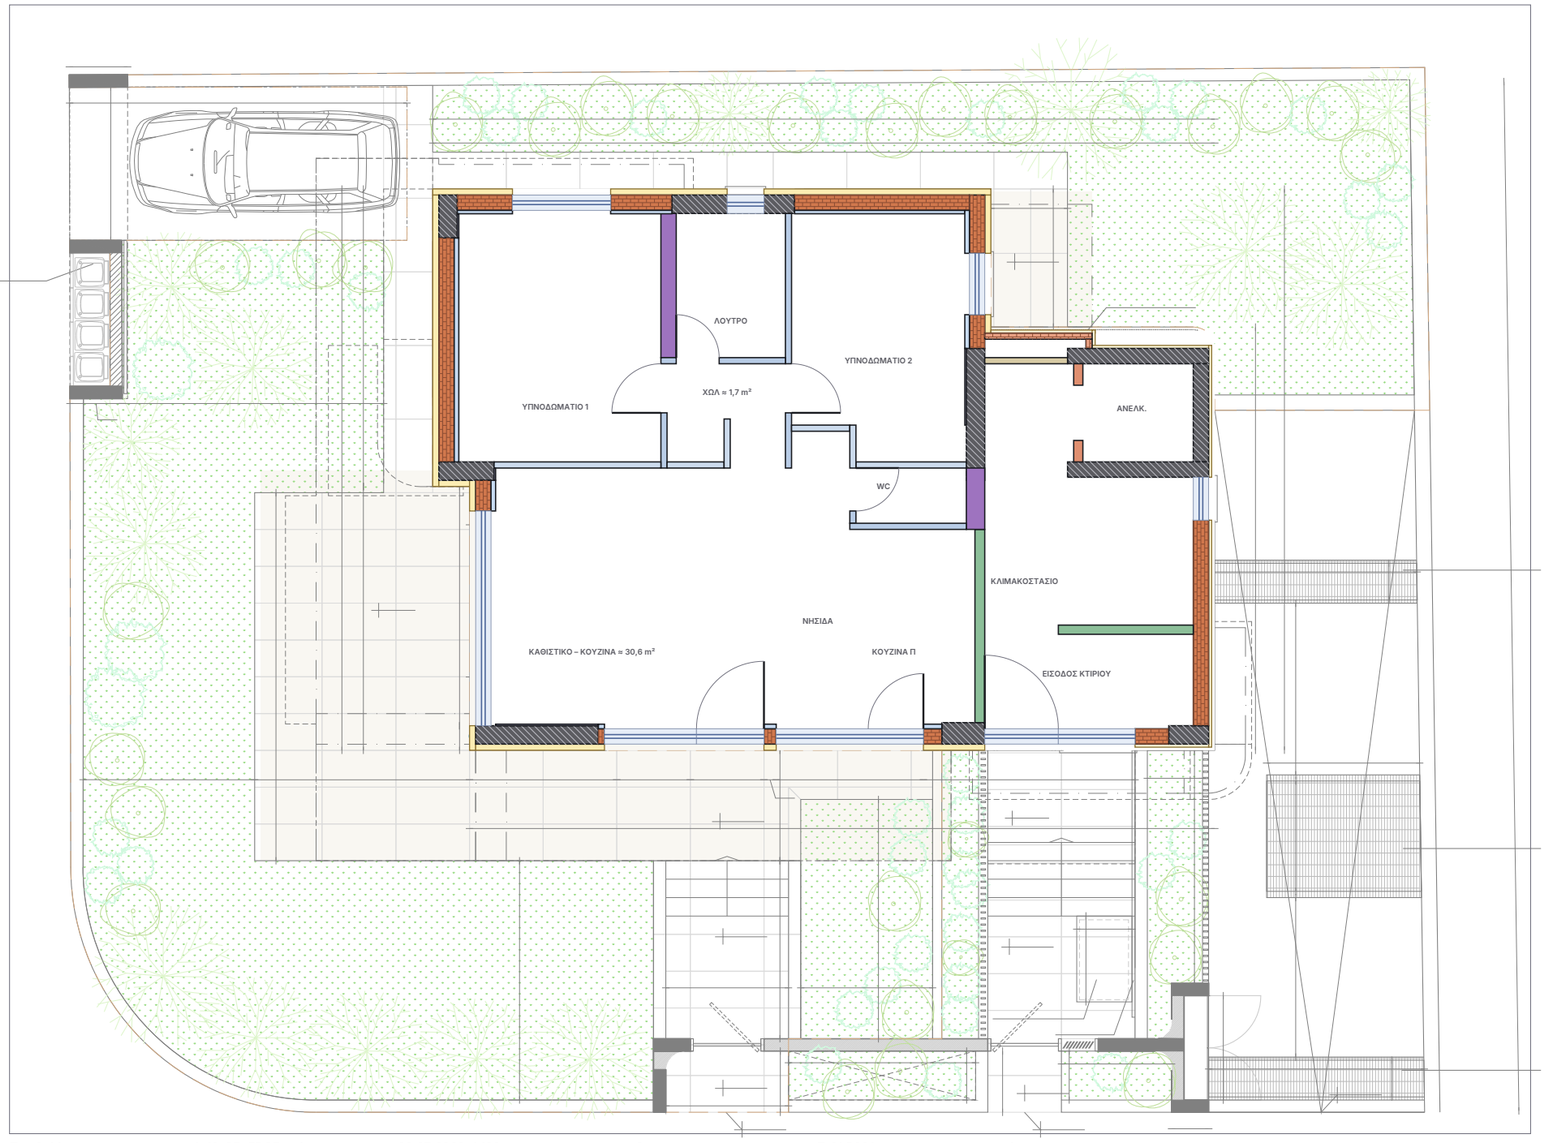

Περιβάλλων χώρος: γεωμετρία A-10-GF (EDGE, μελέτη εφαρμογής 23/07/2026) 1:100, αχνά, χωρίς κείμενα / διαστάσεις · τοιχοποιίες από το T-01 R09A · συντεταγμένες μοντέλου σε m

B

ΠΕΡΙΒΑΛΛΩΝ ΧΩΡΟΣ ΙΣΟΓΕΙΟΥ – όπως τον έχει ο αρχιτέκτονας (A-10-GF)

Το φύλλο δείχνει το οικόπεδο ολόκληρο με τον κήπο, τις βεράντες, τις εισόδους και τη ράμπα όπως τα έχει ο αρχιτέκτονας στο A-10-GF (μόνο η γεωμετρία, χωρίς τα κείμενά του), για να φαίνεται πώς δένουν οι τοιχοποιίες του ισογείου με τον περιβάλλοντα χώρο. Δεν είναι σχέδιο κατασκευής κήπου: για διαστάσεις, στάθμες και φυτεύσεις ισχύουν τα A-10-GF / A-14-GF και η μελέτη περιβάλλοντος χώρου.

ΚΗΠΟΣ ΙΣ1
Χώρος αποκλειστικής χρήσης ΙΣ1 κατοικίας 182,08 m² (σημεία 1…23 του A-10-GF): δυτικά και νότια του κτιρίου, βεράντα ισογείου δυτικά +0,40 (κλίση 1 %) και νότια +0,45 με σκαλιά 1–4 προς −0,30 · προβολές εξώστη / έρκερ με διακεκομμένη.

ΕΙΣΟΔΟΣ ΙΣ1
Από τη νότια περίφραξη: πύλη Θ 1,00/2,20 (x ≈ 5,2–6,2), σκαλιά −0,30 → +0,45, βεράντα, πόρτα Θ0.03 1,10×2,40 (5,00–6,10).

ΣΤΑΘΜΕΥΣΗ
Θ.Σ.Ι.1 13,75 m² στη ΒΔ γωνία του οικοπέδου (θέση στάθμευσης ισογείου), πλάτος 2,50 · μήκος 5,50.

ΦΥΤΕΜΕΝΟΙ ΧΩΡΟΙ
Φ.Χ.1 37,69 m² (βόρεια) · Φ.Χ.2 68,46 (νοτιοδυτικά) · Φ.Χ.3 8,39 · Φ.Χ.4 2,82 · Φ.Χ.5 3,76 · Φ.Χ.6 1,42 · Φ.Χ.7 2,44 m².

ΕΙΣΟΔΟΣ ΚΤΙΡΙΟΥ
Νότια: πύλη πεζών Θ 1,00/2,20 (x ≈ 9,85–10,85) στο −0,45, σκάλα 5 ριχτιών 2,40 (x 9,75–12,15) ως το πλατύσκαλο +0,45 (9,50–12,95 × 9,45–10,25), αναδιπλούμενη πλατφόρμα αναβατορίου ΑΜΕΑ 0,90×1,40 με οδηγό x 8,85–9,75, πόρτα αλουμινίου 1,00×2,40 + σταθερό W0.04 1,20 στο lobby (24,55 m²).

ΒΑ ΒΕΡΑΝΤΑ
Βεράντα ισογείου +0,45, 9,80–11,45 × 0,45–2,70, από την μπαλκονόπορτα W0.06 του Υπν.2 · ανατολικά της φυτεμένος χώρος.

ΟΧΗΜΑΤΑ / ΥΠΟΣΤΑΘΜΟΣ
Ράμπα Ι.Χ. κλίσης 16,12 % στη ΝΑ γωνία (είσοδος – έξοδος οχημάτων, −0,55), μετρητές ΔΕΔΔΗΕ, εσχάρες υποσταθμού: εξαερισμού Ι-Κ-Λ-Μ 3,40×0,60 = 2,04 m² (ανατολικά του lobby) και Ρ-Σ-Τ-Υ 3,52×0,60 = 2,11 m², καταπακτής Ν-Ξ-Ο-Π 2,80×1,80 = 5,02 m² (βλ. A-30-01).

ΕΡΓΟ	ΘΕΜΑ ΣΧΕΔΙΟΥ	ΒΑΣΗ	ΑΡ. ΣΧΕΔΙΟΥ
ΠΕΝΤΑΟΡΟΦΟ ΚΤΗΡΙΟ ΚΑΤΟΙΚΙΩΝ – ΑΡΓΥΡΟΥΠΟΛΗ Κωνσταντινουπόλεως 12 & Αγ. Βαρβάρας · Ο.Τ. 103-15 Εργοδότης: INTERKAT Α.Ε. · Κατασκευή: ARKAD Ι.Κ.Ε.	**ΠΕΡΙΒΑΛΛΩΝ ΧΩΡΟΣ – ΙΣΟΓΕΙΟ** Κήπος ΙΣ1 · βεράντες · είσοδοι · ράμπα κατά A-10-GF ΙΣΟΓΕΙΟ – ΙΣ1	Βάση: γεωμετρία περιβάλλοντος χώρου A-10-GF · τοιχοποιίες T-01	**T-04** **Κλίμακα 1:100 · A3** 07/11/2026 · R09A