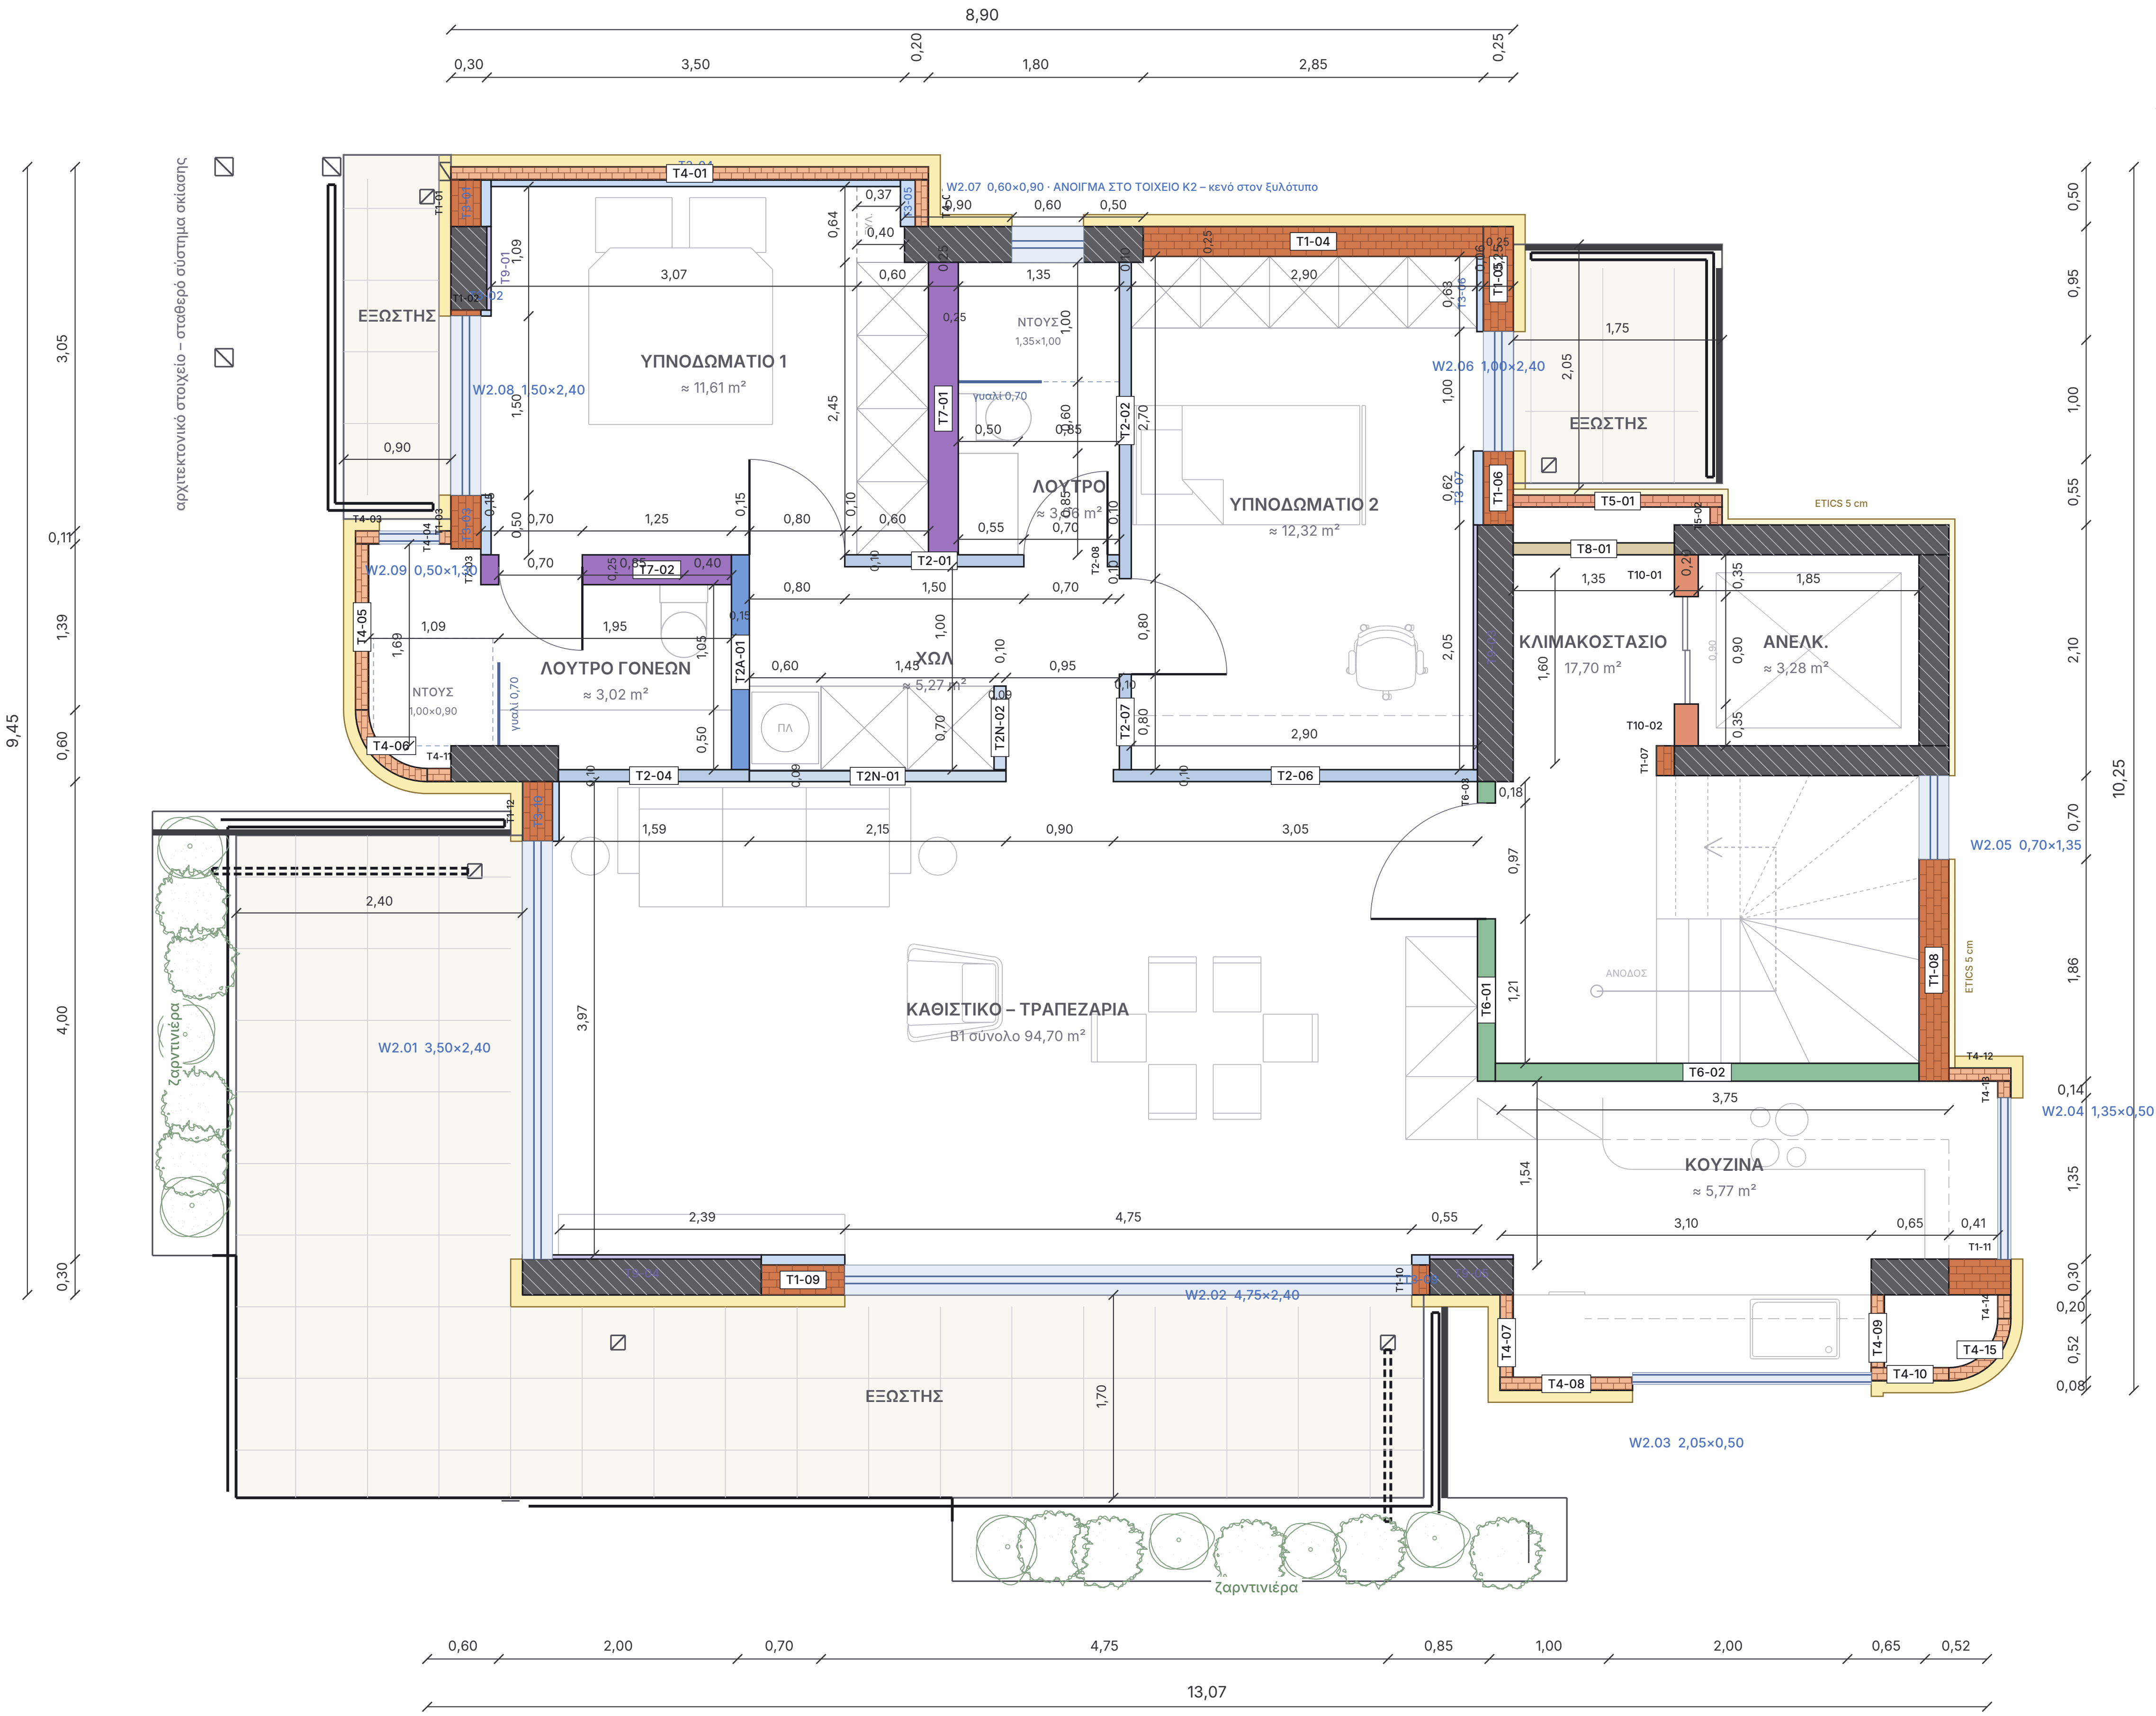

ΑΛΛΑΓΕΣ R15 – R18 (05/11/2026)

- · Ντουλάπες χωνευτές: δωματίων 0,60 · πλυντηρίου 0,70
- · Τ1-05 ως 1,38 (+0,03 περιθώριο) · Τ3-06 μένει (ισοπαχείς λαμπάδες) · W2.06 → 1,38–2,38
- · Υπν.1: χωρίς κουτί – ξυλουργικό συνέχεια ντουλάπας ως τον β. τοίχο
- · Τ2-05 → Τ2Ν-02 (1 φύλλο προς ντουλάπα) · διάδρομος χωλ 1,00
- · Λουτρά: πάγκος 0,50 · λεκάνη · γυάλινο διαχωριστικό 0,70 · ντους 0,70–1,00
- · Αλουμίνια στη μέση του τοίχου: Τ3 και στις δύο παραστάδες
- · Πόρτες: ανοίγουν μέσα στον χώρο (Υπν.1, λουτρά, Υπν.2)
- · W2.07 μέσα στο τοιχείο Κ2: κενό 0,60×0,90 στον ξυλότυπο (ποδιά +1,50)
- · Θερμοπρόσοψη: 10 cm διαμερίσματα · 5 cm κλιμακοστάσιο / πυρήνας
- · Τ6 15 cm · μέτωπο ανελκυστήρα Τ10 20 cm, πόρτα 0,90 · εξώστης Υπν.2 ως 2,70
- · Πόρτες σε γυψοσανίδα: ορθοστάτες UA 2 mm (Knauf) · είσοδος UA 100
- · Τ7-02: ισοπαχείς παραστάδες – λουτρό γονέων σε 25 (Τ7-03), πόρτα Υπν.1 3,30–4,10 σε 10 cm
- · R18: λουτρό +10 cm (Τ7-01 4,80–5,05) · ντους 1,35×1,00, γυαλί στο 1,00 · Τ9-02 καταργήθηκε (ξυλουργικό βάθους 0,40) · Τ6-02 από 9,55
- · Αλυσίδες διαστάσεων μέσα στους χώρους

ΕΡΓΟ	ΘΕΜΑ ΣΧΕΔΙΟΥ	ΒΑΣΗ	ΑΡ. ΣΧΕΔΙΟΥ
ΠΕΝΤΑΟΡΟΦΟ ΚΤΗΡΙΟ ΚΑΤΟΙΚΙΩΝ – ΑΡΓΥΡΟΥΠΟΛΗ Κωνσταντινουπόλεως 12 & Αγ. Βαρβάρας · Ο.Τ. 103-15 Εργοδότης: INTERKAT Α.Ε. · Κατασκευή: ARKAD Ι.Κ.Ε.	**ΚΑΤΟΨΗ ΤΟΙΧΟΠΟΙΙΩΝ – Β΄ ΟΡΟΦΟΣ** Είδη τοιχοποιιών · διαστάσεις χάραξης · κουφώματα · εξώστες Β΄ ΟΡΟΦΟΣ – Β1	Βάση: κάτοψη Α-10-2F (μελέτη εφαρμογής) · ξυλότυποι Σ · R14 + αλλαγές 05/11	**T-01** **Κλίμακα 1:60 · A3** 05/11/2026 · R18

🟧 **T1** Εξωτερική οπτοπλινθοδομή 1:4

πάχος 25 cm

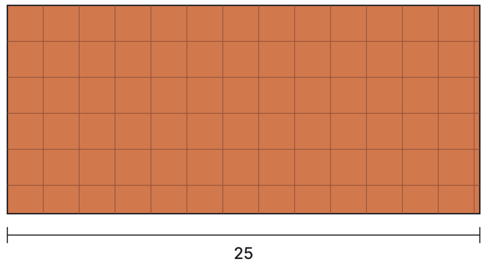

θερμομονωτικό τούβλο κάθετων οπών 25 cm · θερμοπρόσοψη 10 cm έξω · επένδυση T3 μέσα όπου σημειώνεται

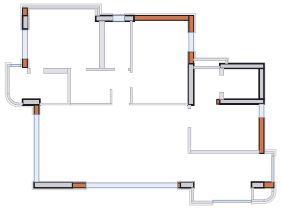

Τοίχοι: T1-01, T1-02, T1-03, T1-04, T1-05, T1-06, T1-07, T1-08, T1-09, T1-10, T1-11, T1-12

Μήκος 9,52 m · επιφάνεια ≈ 27,6 m²

🟧 **T4** Έρκερ – απλή οπτοπλινθοδομή 1:4

πάχος 11 cm

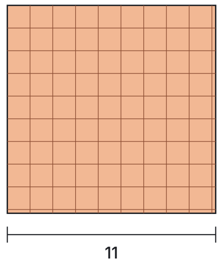

απλό τούβλο 6οπο 9 × 12 × 19 δρομικό ≈ 11 cm · σταθερή η εξωτερική παρειά · θερμοπρόσοψη 10 cm έξω

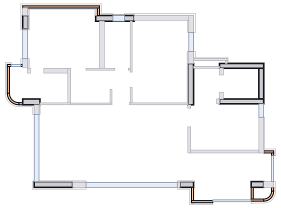

Τοίχοι: T4-01, T4-02, T4-03, T4-04, T4-05, T4-06, T4-07, T4-08, T4-09, T4-10, T4-11, T4-12, T4-13, T4-14, T4-15

Μήκος 12,02 m · επιφάνεια ≈ 34,8 m²

🟧 **T5** Οπτοπλινθοδομή πυρήνα 1:4

πάχος 10 cm

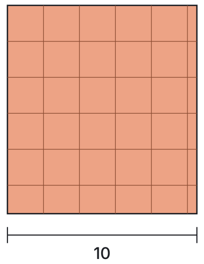

θερμομονωτικό τούβλο κάθετων οπών 10 cm · γύρω από τον πυρήνα (ανελκυστήρας – ηλεκτροστάσιο)

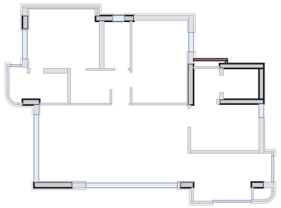

Τοίχοι: T5-01, T5-02

Μήκος 1,90 m · επιφάνεια ≈ 5,5 m²

🟧 **T10** Μέτωπο ανελκυστήρα 1:4

πάχος 20 cm

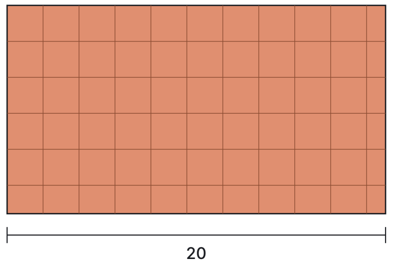

θερμομονωτικό τούβλο κάθετων οπών 20 cm (ή 2 × 10 δρομικά) · μέτωπο φρεατίου εκατέρωθεν της πόρτας 0,90 · ισοπαχές ώστε να κάθεται σωστά η κάσα της πόρτας ορόφου · πάχος / θέση πόρτας προς επιβεβαίωση από τον προμηθευτή

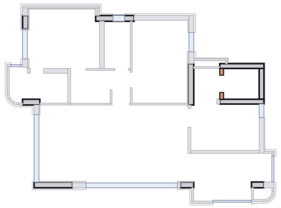

Τοίχοι: T10-01, T10-02

Μήκος 0,70 m · επιφάνεια ≈ 2,0 m²

🟦 **T3** Επένδυση τοίχου 1:4

πάχος 5,5 cm

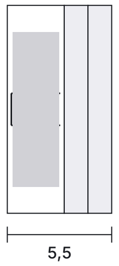

σκελετός 30 · 2 × γυψοσανίδα 12,5 · στις εσωτερικές παρειές των T1 – ΟΧΙ όπου πλακάκι ή ντουλάπα, ΟΧΙ στα έρκερ

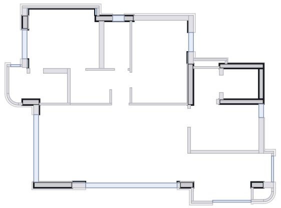

Τοίχοι: T3-01, T3-02, T3-03, T3-04, T3-05, T3-06, T3-07, T3-08, T3-09, T3-10

Μήκος 7,40 m · επιφάνεια ≈ 21,4 m²

🟪 **T9** Επένδυση υποστυλώματος 1:4

πάχος 2,5 cm

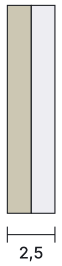

κόλλα + 1 × γυψοσανίδα 12,5 (ένα φύλλο) · στις παρειές υποστυλωμάτων μέσα στα διαμερίσματα – ΟΧΙ όπου πλακάκι ή ντουλάπα

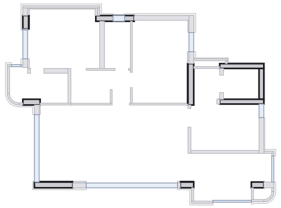

Τοίχοι: T9-01, T9-03, T9-04, T9-05

Μήκος 5,45 m · επιφάνεια ≈ 15,8 m²

🟦 **T2** Χώρισμα γυψοσανίδας 1:4

πάχος 10 cm

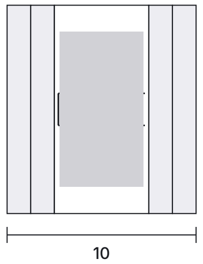

2 × γυψοσανίδα 12,5 · σκελετός CW 50 · 2 × γυψοσανίδα 12,5 · εσωτερικά χωρίσματα · ανθυγρή γυψοσανίδα στην πλευρά των λουτρών · ανοίγματα πορτών με ορθοστάτες UA 50 (2 mm)

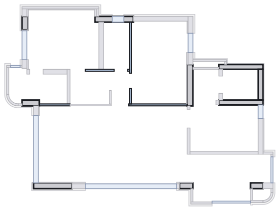

Τοίχοι: T2-01, T2-02, T2-04, T2-06, T2-07, T2-08

Μήκος 9,70 m · επιφάνεια ≈ 28,1 m²

🟦 **T2N** Χώρισμα γυψ. – πλευρά ντουλάπας 1:4

πάχος 8,75 cm

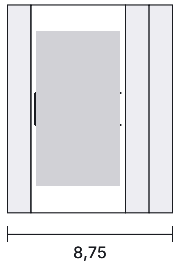

1 × γυψοσανίδα 12,5 (πλευρά ντουλάπας) · σκελετός CW 50 · 2 × γυψοσανίδα 12,5 · όπου η μία παρειά βλέπει σε ντουλάπα: ένα φύλλο αρκεί (κανόνας R15)

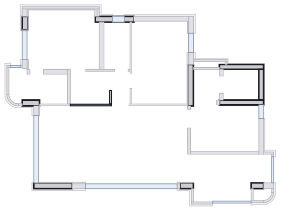

Τοίχοι: T2N-01, T2N-02

Μήκος 2,85 m · επιφάνεια ≈ 8,3 m²

🟦 **T2A** Χώρισμα γυψοσανίδας 15 1:4

πάχος 15 cm

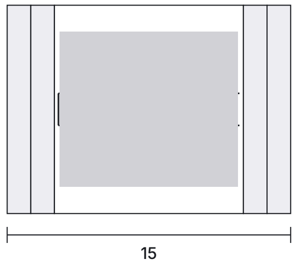

2 × γυψοσανίδα 12,5 · σκελετός CW 100 + πετροβάμβακας · 2 × γυψοσανίδα 12,5 · λουτρό γονέων / χωλ · υπνοδωμάτια · ανοίγματα πορτών με ορθοστάτες UA 100 (2 mm)

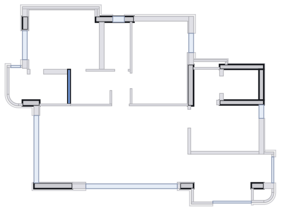

Τοίχοι: T2A-01

Μήκος 1,80 m · επιφάνεια ≈ 5,2 m²

🟪 **T7** Τοίχος λεκάνης WC 1:4

πάχος 25 cm

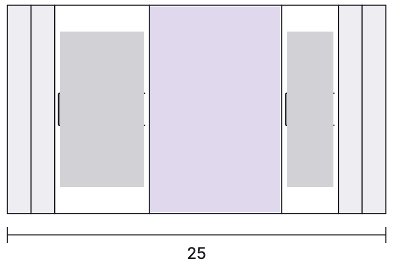

2 × γυψοσανίδα 12,5 · σκελετός CW 50 · κενό 12 cm (καζανάκι γυψοσανίδας στον σκελετό + κατακόρυφη στήλη Ø110, έξοδος Ø90) · σκελετός CW 30 · 2 × γυψοσανίδα 12,5 · ΟΛΟΙ οι τοίχοι λεκανών · ανθυγρή προς το λουτρό · στην πλευρά ντουλάπας 1 φύλλο · ανοίγματα πορτών με ορθοστάτες UA 50 (2 mm)

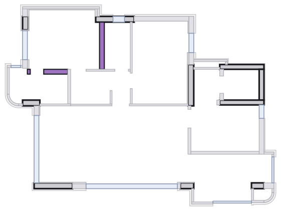

Τοίχοι: T7-01, T7-02, T7-03

Μήκος 3,95 m · επιφάνεια ≈ 11,5 m²

🟩 **T6** Τοίχος κλιμακοστασίου 1:4

πάχος 15 cm

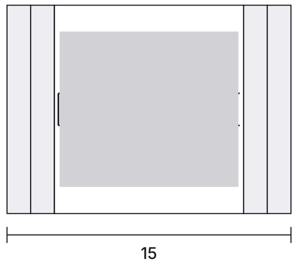

2 × γυψοσανίδα 12,5 πυράντοχη · σκελετός CW 100 + πετροβάμβακας · 2 × γυψοσανίδα 12,5 πυράντοχη · προς κοινόχρηστους χώρους · 15 cm · άνοιγμα πόρτας εισόδου (ασφαλείας) με ορθοστάτες UA 100 (2 mm) κατά Knauf

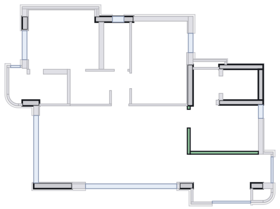

Τοίχοι: T6-01, T6-02, T6-03

Μήκος 5,09 m · επιφάνεια ≈ 14,8 m²

🟨 **T8** Τοίχος shaft 1:4

πάχος 10 cm

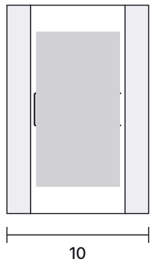

πλαίσιο + ανοιγόμενα φύλλα γυψοσανίδας · μέτωπο shaft ηλεκτρολογικών

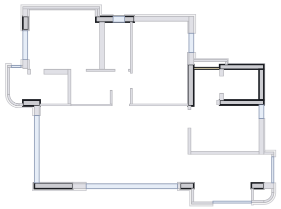

Τοίχοι: T8-01

Μήκος 1,35 m · επιφάνεια ≈ 3,9 m²

Επιφάνειες ενδεικτικές: μήκος × ύψος 2,90 m (τελικό δάπεδο – πλάκα) – οι τοίχοι ορίζονται μεταξύ ανοιγμάτων, χωρίς αφαίρεση κασών. T3 = επένδυση στην εσωτερική παρειά των T1 · T9 = περίμετρος υποστυλώματος × ύψος. R15: T2N = 1 φύλλο στην πλευρά ντουλάπας (T2N-01, T2N-02) · T7-01 1 φύλλο προς Υπν.1.

ΕΡΓΟ
ΠΕΝΤΑΟΡΟΦΟ ΚΤΗΡΙΟ ΚΑΤΟΙΚΙΩΝ – ΑΡΓΥΡΟΥΠΟΛΗ
Κωνσταντινουπόλεως 12 & Αγ. Βαρβάρας · Ο.Τ. 103-15
Εργοδότης: INTERKAT A.E. · Κατασκευή: ARKAD I.K.E.

ΘΕΜΑ ΣΧΕΔΙΟΥ
ΕΙΔΗ ΤΟΙΧΟΠΟΙΙΩΝ – Β΄ ΟΡΟΦΟΣ
Είδη τοιχοποιιών · Β΄ ΟΡΟΦΟΣ – Β1
τομές 1:4 · μήκη – εμβαδά ανά είδος

ΒΑΣΗ
Βάση: κάτοψη τοιχοποιιών Τ-01 · κάτοψη Α-10-2F

ΑΡ. ΣΧΕΔΙΟΥ
Τ-02
Κλίμακα 1:4 · Α3
05/11/2026 · R18

ΠΡΟΜΕΤΡΗΣΗ ΤΟΙΧΟΠΟΙΙΩΝ – Β΄ ΟΡΟΦΟΣ – Β1

τετραγωνικά ανά τυπολογία τοίχου · H = 2,90 m (τελικό δάπεδο – κάτω παρειά πλάκας) · μήκη στον άξονα, χωρίς αφαίρεση κουφωμάτων · R18

	Τύπος	Περιγραφή	Πάχος cm	Τοίχοι	Μήκος m	Επιφάνεια m²
ΤΟΥΒΛΑ						
🟧	**T1**	Εξωτερική οπτοπλινθοδομή	25	12	9,52	**27,6**
🟧	**T4**	Έρκερ – απλή οπτοπλινθοδομή	11	15	12,02	**34,8**
🟧	**T5**	Οπτοπλινθοδομή πυρήνα	10	2	1,90	**5,5**
🟧	**T10**	Μέτωπο ανελκυστήρα	20	2	0,70	**2,0**
	Σύνολο τουβλα					**70,0 m²**
ΧΩΡΙΣΜΑΤΑ ΓΥΨΟΣΑΝΙΔΑΣ						
🟦	**T2**	Χώρισμα γυψοσανίδας	10	6	9,70	**28,1**
🟦	**T2N**	Χώρισμα γυψ. – πλευρά ντουλάπας	8,8	2	2,85	**8,3**
🟦	**T2A**	Χώρισμα γυψοσανίδας 15	15	1	1,80	**5,2**
🟪	**T7**	Τοίχος λεκάνης WC	25	3	3,95	**11,5**
🟩	**T6**	Τοίχος κλιμακοστασίου	15	3	5,09	**14,8**
🟨	**T8**	Τοίχος shaft	10	1	1,35	**3,9**
	Σύνολο χωρισματα γυψοσανιδας					**71,7 m²**
ΕΠΕΝΔΥΣΕΙΣ						
🟦	**T3**	Επένδυση τοίχου	5,5	10	7,40	**21,4**
🟪	**T9**	Επένδυση υποστυλώματος	2,5	4	5,45	**15,8**
	Σύνολο επενδυσεις					**37,3 m²**
	ΣΥΝΟΛΟ ΤΟΙΧΟΠΟΙΙΩΝ Β1					**179,0 m²**

ΘΕΡΜΟΠΡΟΣΟΨΗ (ETICS)

10 cm στις όψεις των διαμερισμάτων · 5 cm στο κλιμακοστάσιο / πυρήνα · ύψος 3,10 m (με τη μετώπη πλάκας) · καθαρά = όψη − κουφώματα + λαμπάδες/ανώφλια

Ζώνη	Μήκος όψης m	Μικτά m²	Κουφώματα m²	Λαμπάδες m²	Καθαρά m²
ETICS 10 cm – διαμερίσματα	39,72	123,1	−28,7	+6,2	**100,6**
ETICS 5 cm – κλιμακοστάσιο / πυρήνας	8,50	26,4	−0,9	+0,5	**25,9**
Σύνολο ETICS					**126,5 m²**

ΣΗΜΕΙΩΣΕΙΣ ΚΑΤΟΨΗΣ

- Θέσεις τοίχων και ανοιγμάτων όπως η κάτοψη A-10-2F (Rev.11). Διαστάσεις στο τούβλο / μπετό, χωρίς τη θερμοπρόσοψη (κίτρινη λωρίδα 10 cm).
- ΝΤΟΥΛΑΠΕΣ ΧΩΝΕΥΤΕΣ (R15/R16): δωματίων βάθος 0,60 · πλυντηρίου 0,70. Οι τοίχοι / πεσσοί που τις πλαισιώνουν έχουν ακριβώς το βάθος της ντουλάπας (T2N-02 0,70)· μόνο στον T1-05 περιθώριο +0,03 (ως 1,38). Πίσω και δίπλα σε ντουλάπα καμία επένδυση T3 / T9, ΕΚΤΟΣ παραστάδων κουφωμάτων.
- ΚΟΥΦΩΜΑΤΑ ΑΛΟΥΜΙΝΙΟΥ (R16): τοποθετούνται στη μέση του τοίχου· οι λαμπάδες πρέπει να είναι ισοπαχείς και από τις δύο πλευρές → επένδυση γυψοσανίδας T3 και στις δύο παραστάδες κάθε κουφώματος (T3-06 στον T1-05 μένει, δίπλα στη ντουλάπα).
- T1-05: κόπηκε στο 1,38 (ντουλάπα Υπν.2 0,60 + 0,03). Το W2.06 (1,00×2,40) μετατοπίζεται 7 cm βόρεια: 1,38–2,38 (εγκρίθηκε από τον ιδιοκτήτη 05/11 – να ενημερωθεί ο αρχιτέκτονας).
- Υπν.1 (R18): λουτρό +10 cm → T7-01 στο 4,80–5,05, ντουλάπα 0,60 στο x 4,20–4,80 (y 0,80–3,25) ανάμεσα στον T2-01 και την K2· 10 cm πεσσός μεταξύ κάσας (4,10) και μετώπου ντουλάπας. Το κενό προς τον βόρειο τοίχο ΔΕΝ κτίζεται: ξυλουργικό που συνεχίζει τη ντουλάπα (βιβλιοθήκη / κομοδίνο), βάθος 0,40 (4,20 → γυμνό τοιχείο K2 στο 4,60, y 0,50–0,80) και 0,365 (→ T3-05, y 0,165–0,50), πλάτος 0,635. Ο T9-02 (κολλητή γυψοσανίδα K2) ΚΑΤΑΡΓΗΘΗΚΕ – κρύβεται από το ξυλουργικό. Πόρτα 3,30–4,10.
- ΤΟΙΧΟΙ ΠΟΥ ΒΛΕΠΟΥΝ ΣΕ ΝΤΟΥΛΑΠΑ: 1 φύλλο γυψοσανίδας στην πλευρά της ντουλάπας (T2N-01, T2N-02 · T7-01 πλευρά Υπν.1).
- ΛΟΥΤΡΑ: σχεδιάζονται μόνο πάγκος νιπτήρα βάθους 0,50, λεκάνη και ένα γυάλινο διαχωριστικό ντους 0,70. Το γυαλί μπαίνει ώστε το ντους να φτάνει το 1,00 (R18). Λουτρό (καθαρό 1,35 × 2,45 μετά το +10 cm): ντους βόρεια 1,35×1,00 (y 0,80–1,80), γυαλί 0,70 στο y 1,80 από τον T7-01, λεκάνη στον T7-01 (y 2,10), πάγκος 5,05–5,55 × 2,40–3,25. Λουτρό γονέων: ντους 1,00×0,90 στη δυτική εσοχή (W2.09), γυαλί 0,70 στο x 1,20 από τον νότιο τοίχο.
- ΤΟΙΧΟΙ ΛΕΚΑΝΗΣ T7: 2 γυψ. + CW 50 (καζανάκι γυψοσανίδας) + κενό 12 + CW 30 + 2 γυψ. = 25 cm. T7-01 (R18): x 4,80–5,05, παρειά λουτρού 5,05 (λουτρό +10 cm προς Υπν.1). T7-02: σταθερή η παρειά του Υπν.1, μήκος 1,90–3,15 (ως την παρειά του λουτρού).
- ΟΠΟΥ ΠΛΑΚΑΚΙ Ή ΝΤΟΥΛΑΠΑ: χωρίς γυψοσανίδα σε τούβλο / μπετό. Επενδύσεις T3 / T9 σε ενιαίο επίπεδο, χωρίς δόντια.
- W2.07 (λουτρό, 0,60×0,90, ποδιά +1,50 από Τ.Δ.): το παράθυρο βρίσκεται ΜΕΣΑ στο τοιχείο K2 (x 5,50–6,10). Το κενό 0,60 × 0,90 κρατιέται ΑΠΟ ΤΩΡΑ στον ξυλότυπο του τοιχείου (στάθμες +1,50 ... +2,40 από το τελικό δάπεδο Β΄, δηλ. ≈ +8,40 ... +9,30). Να ενημερωθεί ο στατικός (Κόγιας) για την οπή στο τοιχείο.
- ΠΟΡΤΕΣ (R16/R17): ανοίγουν μέσα στον χώρο που εξυπηρετούν. Υπν.1 μεντεσές δυτικά στη γωνία (3,30), λουτρό μεντεσές ανατολικά (6,30), λουτρό γονέων μεντεσές ανατολικά (1,90) ώστε να μένει ελεύθερη η είσοδος του ντους, Υπν.2 μεντεσές νότια (4,25). ΙΣΟΠΑΧΕΙΣ ΠΑΡΑΣΤΑΔΕΣ σε κάθε πόρτα (R17): λουτρό γονέων 1,20–1,90 σε T7 25 cm και από τις δύο πλευρές (T7-03 1,05–1,20 + T7-02 1,90–3,15) · Υπν.1 3,30–4,10 σε τοίχο 10 cm (T2A-01 ως το 3,25 δυτικά, T2-01 ανατολικά).
- T6-02 ξεκινά από την παρειά του T6-01 (x 9,55) – κλειστή γωνία (R18). T5-01 κόβεται στην άκρη του εξώστη (x 11,45) με επιστροφή T5-02 στο τοιχείο του ασανσέρ. Υποστυλώματα (σκούρο γκρι) κατά Σ5. Εξώστες από την κάτοψη A-10-2F.
- ΑΝΕΛΚΥΣΤΗΡΑΣ (R17): μέτωπο φρεατίου T10-01 / T10-02 (τούβλο 20 cm, x 11,05–11,25) εκατέρωθεν της πόρτας ορόφου 0,90 (y 3,60–4,50), περασιά με τα άκρα των τοιχείων (25 cm) προς το κλιμακοστάσιο. Καθαρό φρεάτιο 1,85 × 1,60. Θέση / πλάτος πόρτας και καθαρές διαστάσεις ΠΡΟΣ ΕΠΙΒΕΒΑΙΩΣΗ από τον προμηθευτή του ανελκυστήρα πριν το κτίσιμο. T6-01 / T6-03 σε 15 cm (x 9,40–9,55).
- ΑΝΟΙΓΜΑΤΑ ΠΟΡΤΩΝ ΣΕ ΓΥΨΟΣΑΝΙΔΑ (Knauf): ύψος τοίχου 2,90 > 2,60 → σε ΚΑΘΕ πόρτα οι παραστάδες από ορθοστάτες UA 2 mm (UA 50 στα T2 / T2N / T7, UA 100 στα T2A / T6) με γωνιακά στηρίγματα Knauf πάνω-κάτω (2 βύσματα το καθένα), πρέκι από UA / CW και αρμοί γυψοσανίδας ≥ 15 cm από την παραστάδα. Όρια φύλλου: UA 50 ≤ 50 kg · UA 75 ≤ 75 kg · UA 100 ≤ 100 kg. Πόρτα εισόδου (ασφαλείας, ~80–100 kg): UA 100 στον T6 (15 cm) + ψευτόκασα του προμηθευτή βιδωτή στα UA· αν το φύλλο > 100 kg, διπλό UA (κουτί).
- ΘΕΡΜΟΠΡΟΣΟΨΗ: 10 cm στις όψεις των διαμερισμάτων (κίτρινη λωρίδα) · 5 cm στο κλιμακοστάσιο / πυρήνα (T5-01, T5-02, τοιχείο ανελκυστήρα, T1-08 – ανοιχτή κίτρινη λωρίδα). Οι διαστάσεις της κάτοψης είναι χωρίς τη θερμοπρόσοψη.

ΕΡΓΟ

ΠΕΝΤΑΟΡΟΦΟ ΚΤΗΡΙΟ ΚΑΤΟΙΚΙΩΝ – ΑΡΓΥΡΟΥΠΟΛΗ
Κωνσταντινουπόλεως 12 & Αγ. Βαρβάρας · Ο.Τ. 103-15
Εργοδότης: INTERKAT A.E. · Κατασκευή: ARKAD I.K.E.

ΘΕΜΑ ΣΧΕΔΙΟΥ

ΠΡΟΜΕΤΡΗΣΗ ΤΟΙΧΟΠΟΙΙΩΝ – Β΄ ΟΡΟΦΟΣ
Τετραγωνικά ανά τυπολογία τοίχου · θερμοπρόσοψη 10 / 5 cm
Β΄ ΟΡΟΦΟΣ – Β1

ΒΑΣΗ

Βάση: κάτοψη τοιχοποιιών T-01 · είδη T-02

ΑΡ. ΣΧΕΔΙΟΥ

T-03
— · A3
05/11/2026 · R18