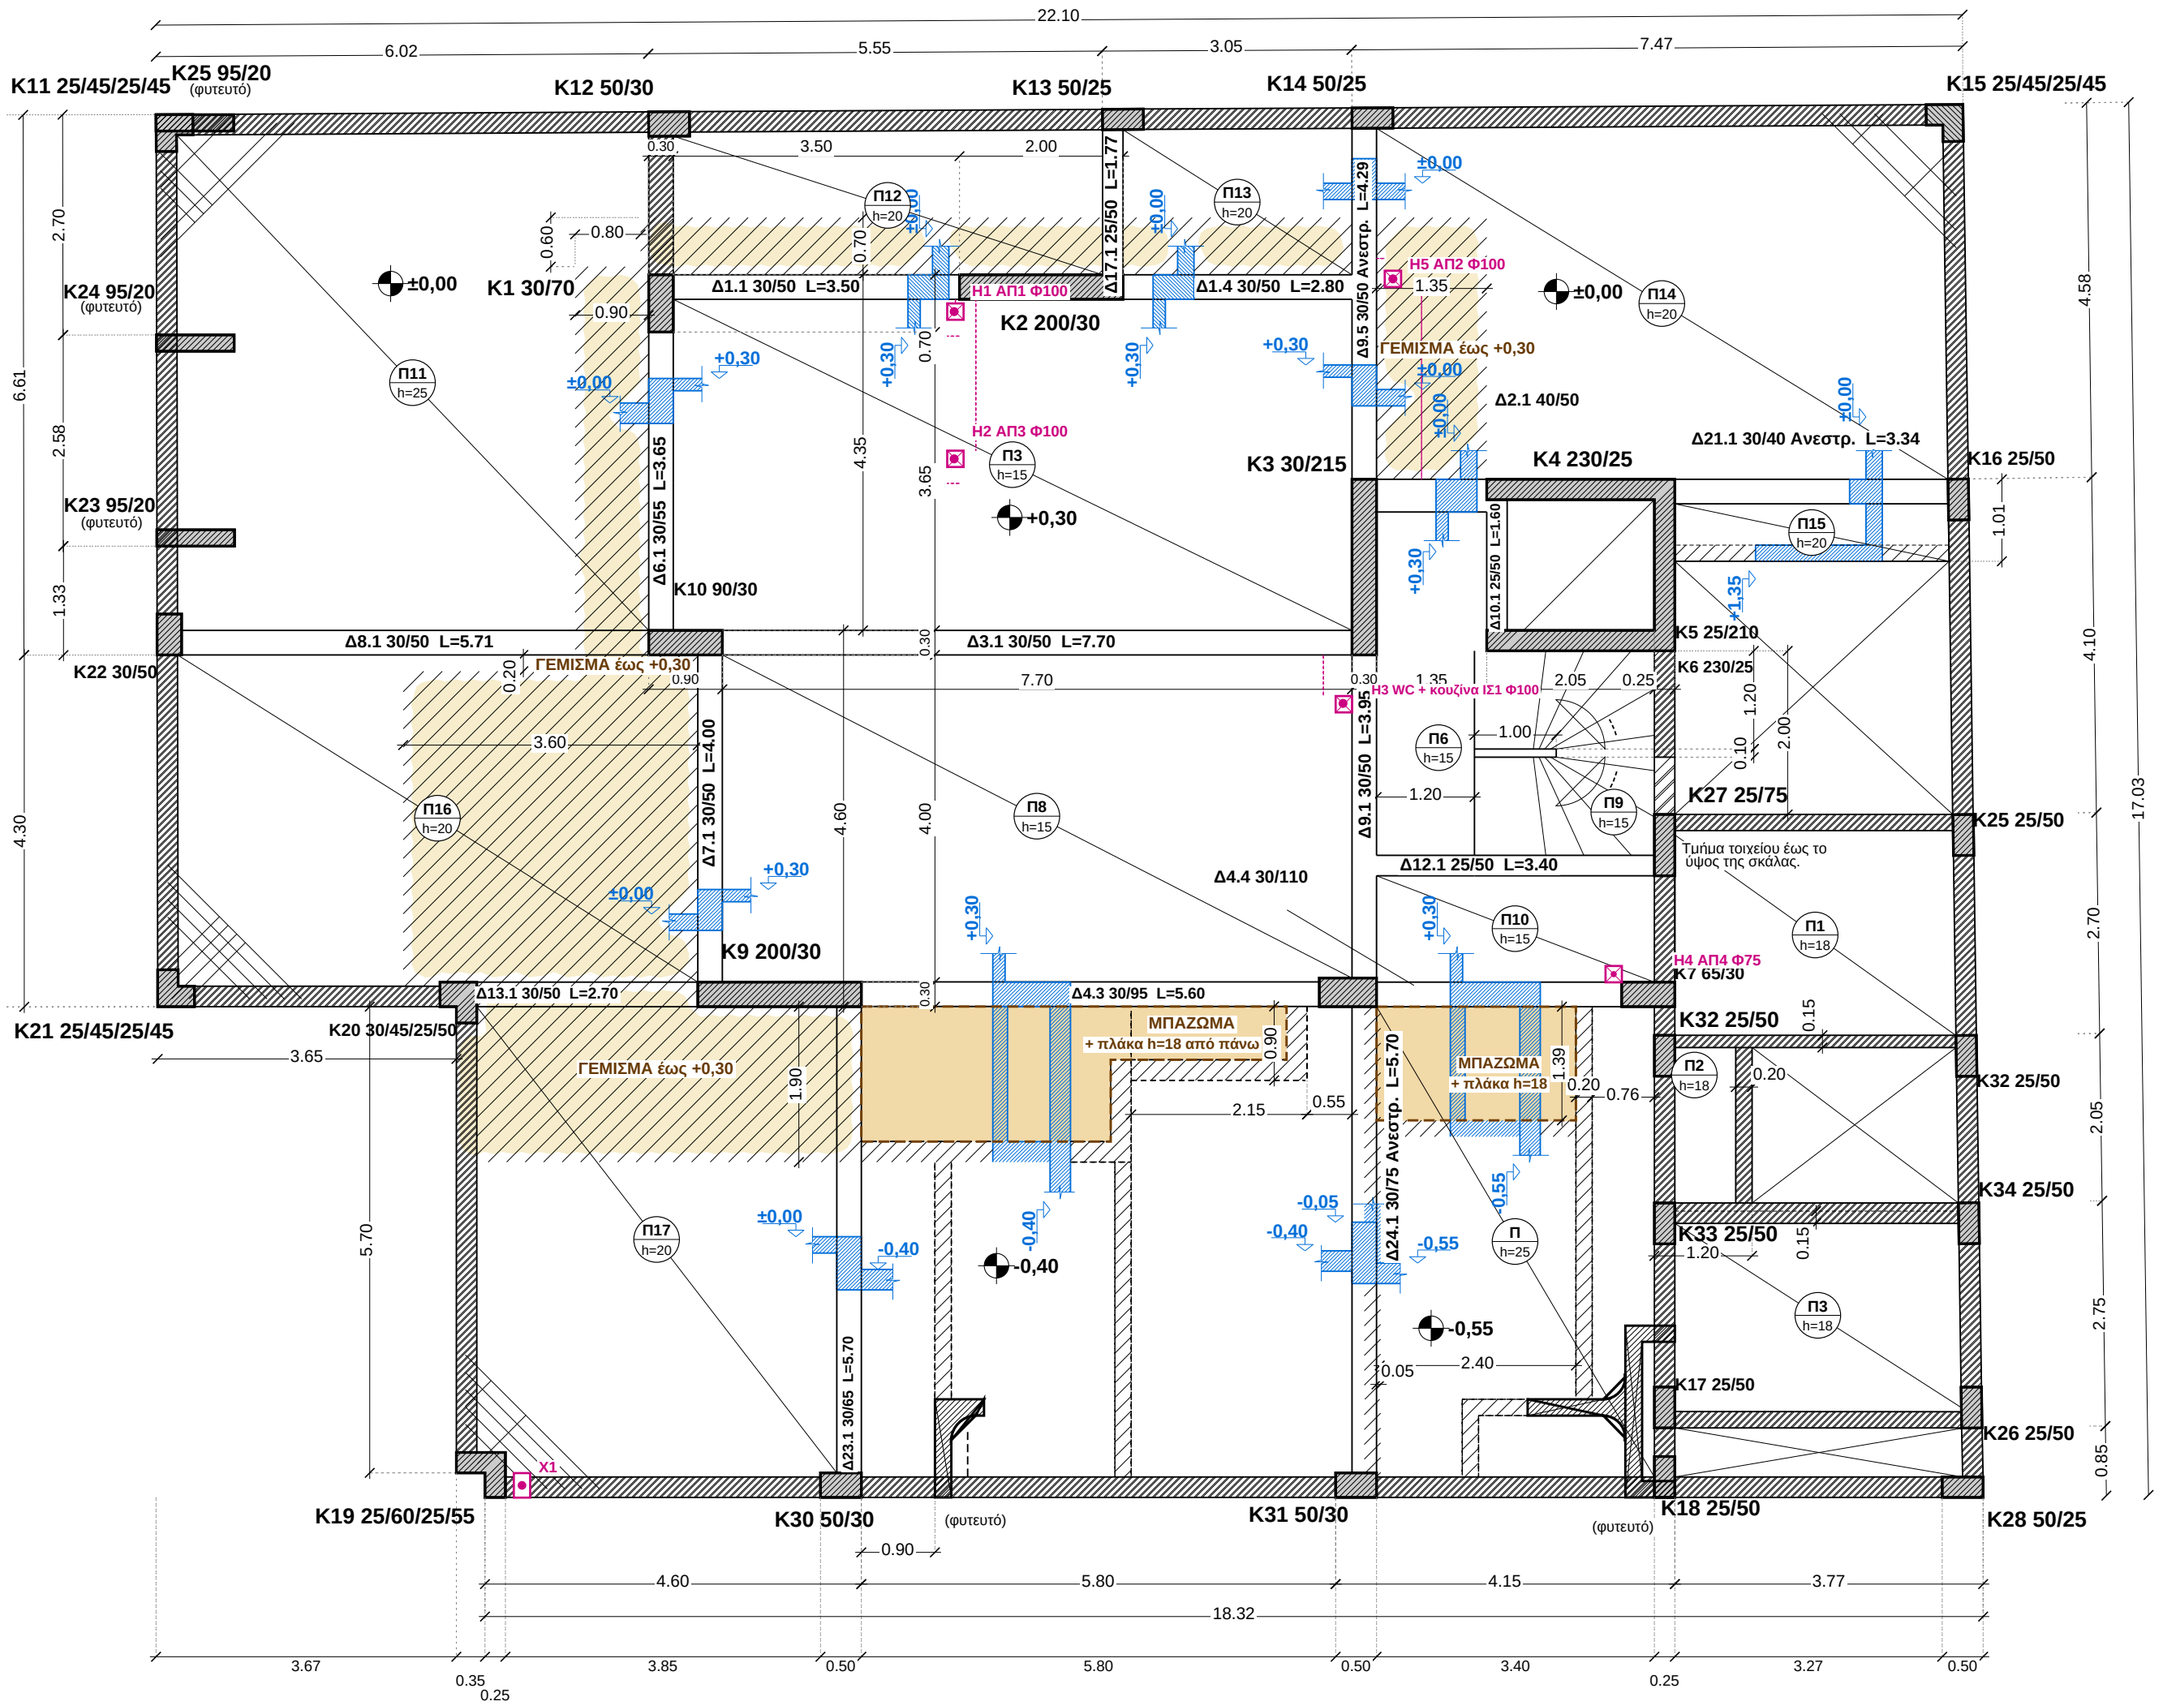


ΚΩΝΣΤΑΝΤΙΝΟΥΠΟΛΕΩΣ 12 & ΑΓ. ΒΑΡΒΑΡΑΣ, ΑΡΓΥΡΟΥΠΟΛΗ – ARKAD I.K.E.
Ξυλότυπος εργοταξίου – χωρίς οπλισμούς

ΞΥΛΟΤΥΠΟΣ ΟΡΟΦΗΣ ΥΠΟΓΕΙΟΥ

Σ2

ΣΤΑΘΜΗ ΑΝΩ ΠΛΑΚΑΣ
±0,00 / +0,30
ΚΛΙΜΑΚΑ 1:75
A3 · 100 %
0 1 2 m

K1 30/70	υποστύλωμα / τοιχείο (cm)
Δ1.1 30/40	δοκός: πλάτος / ύψος (το ύψος μαζί με την πλάκα)
L=3.50	καθαρό μήκος δοκού, παρειά με παρειά
Π3 h=15	πλάκα – πάχος (cm)
+0,30	στάθμη άνω μπετού (m)
μπλε	τομές επί τόπου / φυτευτά και οι στάθμες τους
	γέμισμα έως τη στάθμη +0,30 (πλάκα ±0,00)
	ΜΠΑΖΩΜΑ («φελιζόλ» του μελετητή) κάτω από πλάκα
☒	οπή πλάκας 20 × 20 (αποχέτευση / υδρορροή)

Διαστάσεις σε m, από γωνία / παρειά κολόνας σε γωνία κολόνας. Οι αλυσίδες παρειών μετρήθηκαν από τη γεωμετρία του σχεδίου, οι υπόλοιπες είναι του μελετητή.

ΟΠΕΣ ΠΛΑΚΑΣ – ΚΟΥΤΙ 20 × 20
Θέση σε cm ως την ΑΚΜΗ του κουτιού, από παρειές σκυροδέματος.

- **Η1** **ΑΠ1 Φ100** — δυτ. ακμή 15 δυτ. της Δ παρ. Κ2 · 5 νότια της Ν παρ. Κ2
- **Η2** **ΑΠ3 Φ100** — δυτ. ακμή 15 δυτ. της Δ παρ. Κ2 · 1,85 m νότια της Ν παρ. Κ2
- **Η3** **WC + κουζίνα ΙΣ1 Φ100** — κολλητά στη Δ παρ. Δ9.1 · 50 νότια της Ν παρ. Κ3
- **Η4** **ΑΠ4 Φ75** — ανατ. ακμή στην ευθεία της Δ παρ. Κ7 · κολλητά στη Β παρ. δοκού Κ8–Κ7
- **Η5** **ΑΠ2 Φ100** — 10 ανατ. της Α παρ. Δ9.5 · 2,35 m βόρ. της Β παρ. Κ3
- **Χ1** Έξοδος συλλεκτήρα Φ125: χιτώνιο Ø200 στο ΝΟΤΙΟ ΤΟΙΧΕΙΟ του υπογείου (όχι στην πλάκα) · άξονας 50 cm ανατ. της εσωτ. παρειάς του δυτικού τοιχείου · άντυγα −0,86

Τεύχος αποχετεύσεων R19, φύλλο ΑΠ-11. Καμία οπή σε δοκό, καμία αναμονή σε στηθαίο.

ΣΗΜΕΙΩΣΕΙΣ

· Β και Α πλευρά λοξές (όριο οικοπέδου): ισχύουν οι διαστάσεις του μελετητή κατά μήκος τους.

Βάση: Σ2_ΕΦ.pdf – ξυλότυπος οροφής υπογείου, Γ. Κόγιας (Drive 19/10/2026).
Οπλισμοί ΜΟΝΟ από το σχέδιο του μελετητή.

Έκδοση R02 – 10/11/2026