

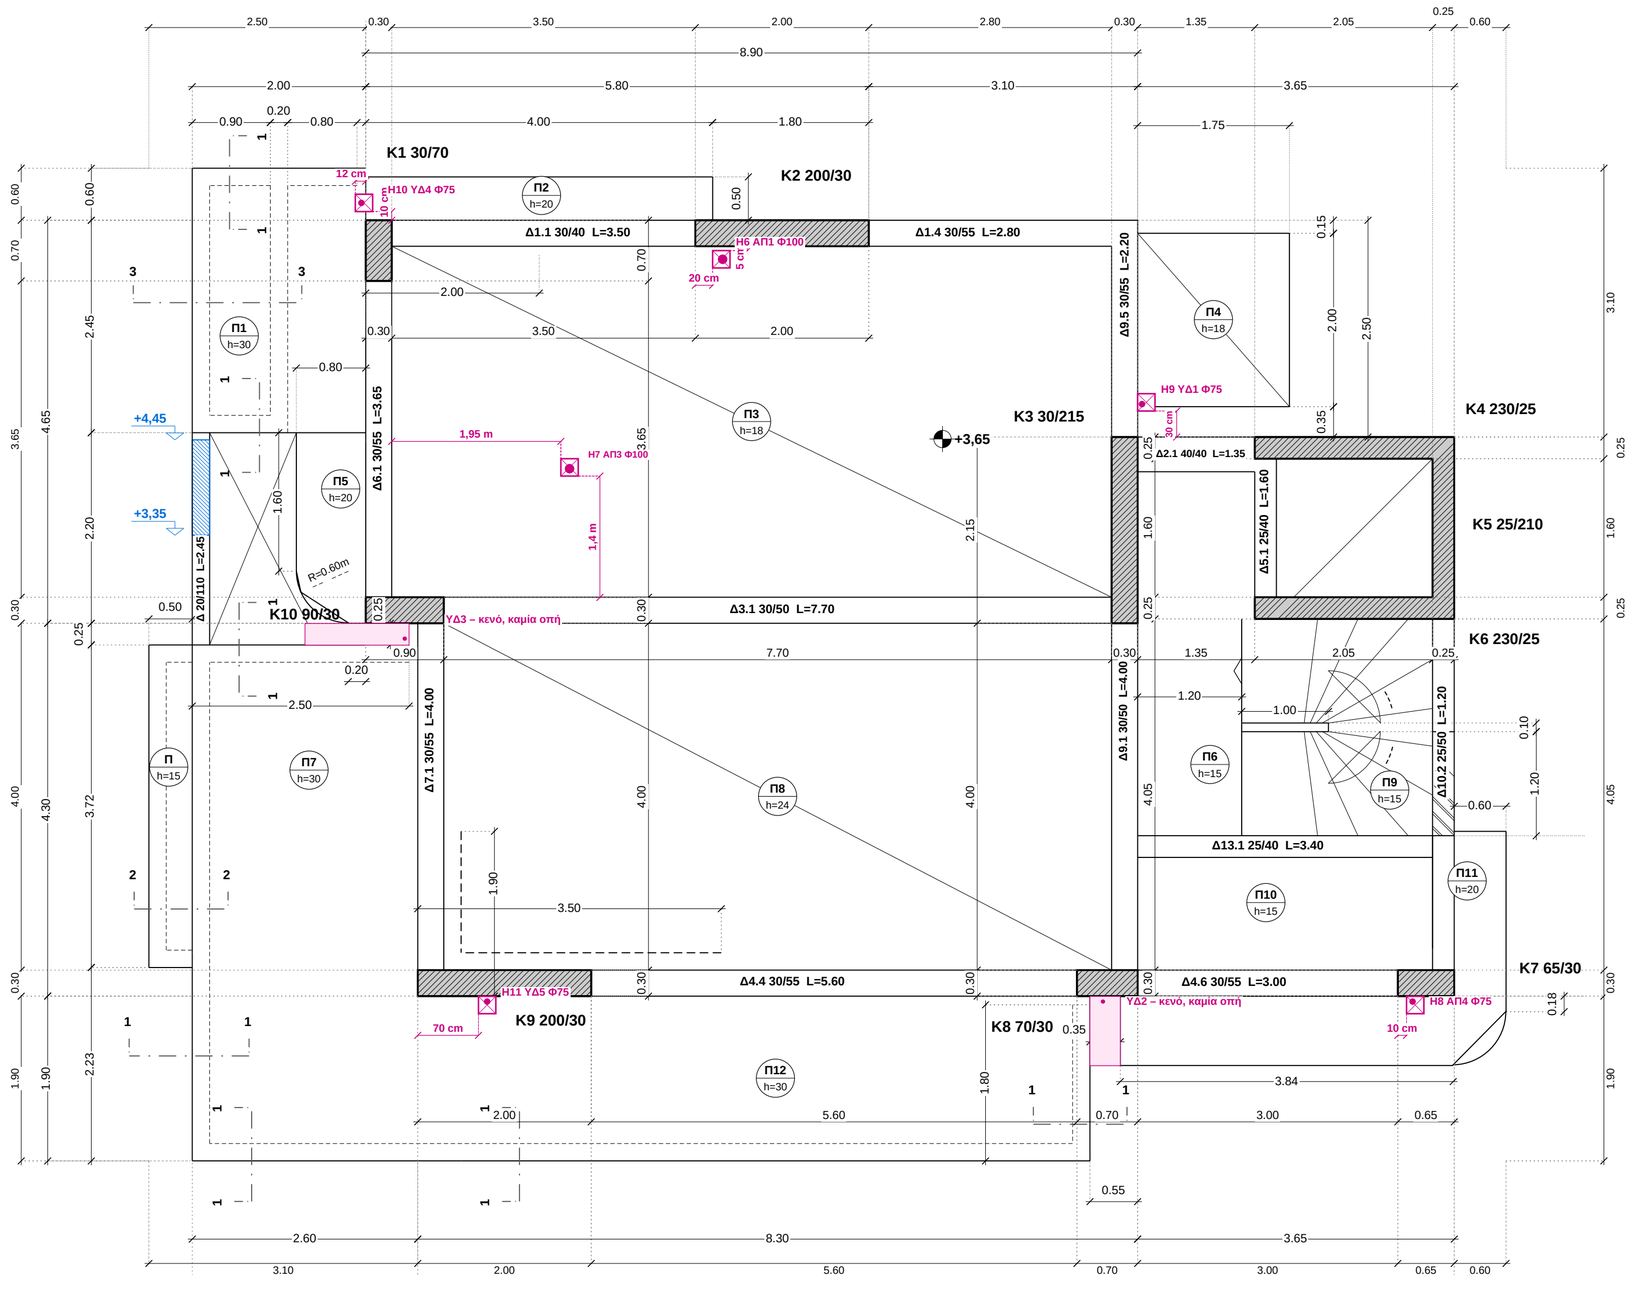


ΤΟΜΕΣ ΜΕΤΩΠΩΝ
(σκαρίφημα χωρίς κλίμακα)


ΤΟΜΗ 1-1

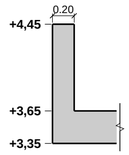

ΤΟΜΗ 2-2

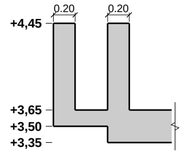

ΤΟΜΗ 3-3

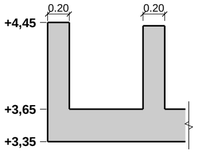

ΚΩΝΣΤΑΝΤΙΝΟΥΠΟΛΕΩΣ 12 & ΑΓ. ΒΑΡΒΑΡΑΣ, ΑΡΓΥΡΟΥΠΟΛΗ – ARKAD Ι.Κ.Ε.
Ξυλότυπος εργοταξίου – χωρίς οπλισμούς

ΞΥΛΟΤΥΠΟΣ ΟΡΟΦΗΣ ΙΣΟΓΕΙΟΥ — Σ3

ΣΤΑΘΜΗ ΑΝΩ ΠΛΑΚΑΣ
+3,65
ΚΛΙΜΑΚΑ 1:50 — A2 · 100 %

0 1 2 m

K1 30/70	υποστύλωμα / τοιχείο (cm)
Δ1.1 30/40	δοκός: πλάτος / ύψος (το ύψος μαζί με την πλάκα)
L=3.50	καθαρό μήκος δοκού, παρειά με παρειά
Π3 h=15	πλάκα – πάχος (cm)
+0,30	στάθμη άνω μπετού (m)
μπλε	τομές επί τόπου / φυτευτά και οι στάθμες τους
☒	οπή πλάκας 20 × 20 (αποχέτευση / υδρορροή)

Διαστάσεις σε m, από γωνία / παρειά κολόνας σε γωνία κολόνας. Οι αλυσίδες παρειών μετρήθηκαν από τη γεωμετρία του σχεδίου, οι υπόλοιπες είναι του μελετητή.

ΠΑΤΟΙ ΚΑΛΟΥΠΙΩΝ	στάθμη
Πλάκα h=15	**+3,50**
Πλάκα h=18	**+3,47**
Πλάκα h=20	**+3,45**
Πλάκα h=24	**+3,41**
Πλάκα h=30	**+3,35**
Δοκός ύψους 40	**+3,25**
Δοκός ύψους 50	**+3,15**
Δοκός ύψους 55	**+3,10**

Υπολογισμένα (στάθμη – ύψος)· όχι για ανεστραμμένες δοκούς / φυτευτά.

ΟΠΕΣ ΠΛΑΚΑΣ – ΚΟΥΤΙ 20 × 20
Θέση σε cm ως την ΑΚΜΗ του κουτιού, από παρειές σκυροδέματος.

H6 **ΑΠ1 Φ100**
20 ανατ. της Δ παρ. K2 · 5 νότια της N παρ. K2

H7 **ΑΠ3 Φ100**
1,95 m ανατ. της A παρ. Δ6.1 · 1,4 m βόρ. της B παρ. Δ3.1

H8 **ΑΠ4 Φ75**
10 ανατ. της Δ παρ. K7 · κολλητά στη N παρ. K7

H9 **ΥΔ1 Φ75**
κολλητά στη A παρ. Δ9.5 · 30 βόρ. της B παρ. K3

H10 **ΥΔ4 Φ75**
δυτ. ακμή 12 δυτ. της Δ παρ. K1 · 10 βόρ. της B παρ. K1

H11 **ΥΔ5 Φ75**
70 ανατ. της Δ παρ. K9 · κολλητά στη N παρ. K9

ΥΔ2 κενό 35 cm νότια της K8 – ΚΑΜΙΑ οπή

ΥΔ3 κενό 25 cm δυτικά της K10 – ΚΑΜΙΑ οπή

Τεύχος αποχετεύσεων R19, φύλλο ΑΠ-12.
Καμία οπή σε δοκό, καμία αναμονή σε στηθαίο.

ΣΗΜΕΙΩΣΕΙΣ

· Πρόβολοι: υποδοχή σιφωνιού και υδρορροή ΠΡΙΝ το μπετό, να μην κοπεί οπλισμός (μελετητής).

· Διαγραμμισμένο τοιχείο δίπλα στη σκάλα (0,60): έως το ύψος της σκάλας (μελετητής).

· Φυτευτά K23–K25 και τοιχεία εισόδου: φύλλο Σ3α.

Βάση: Σ3_ΕΦ.pdf – ξυλότυπος οροφής ισογείου, Γ. Κόγιας (Drive 19/10/2026).
Οπλισμοί ΜΟΝΟ από το σχέδιο του μελετητή.

Έκδοση R03 – 10/11/2026