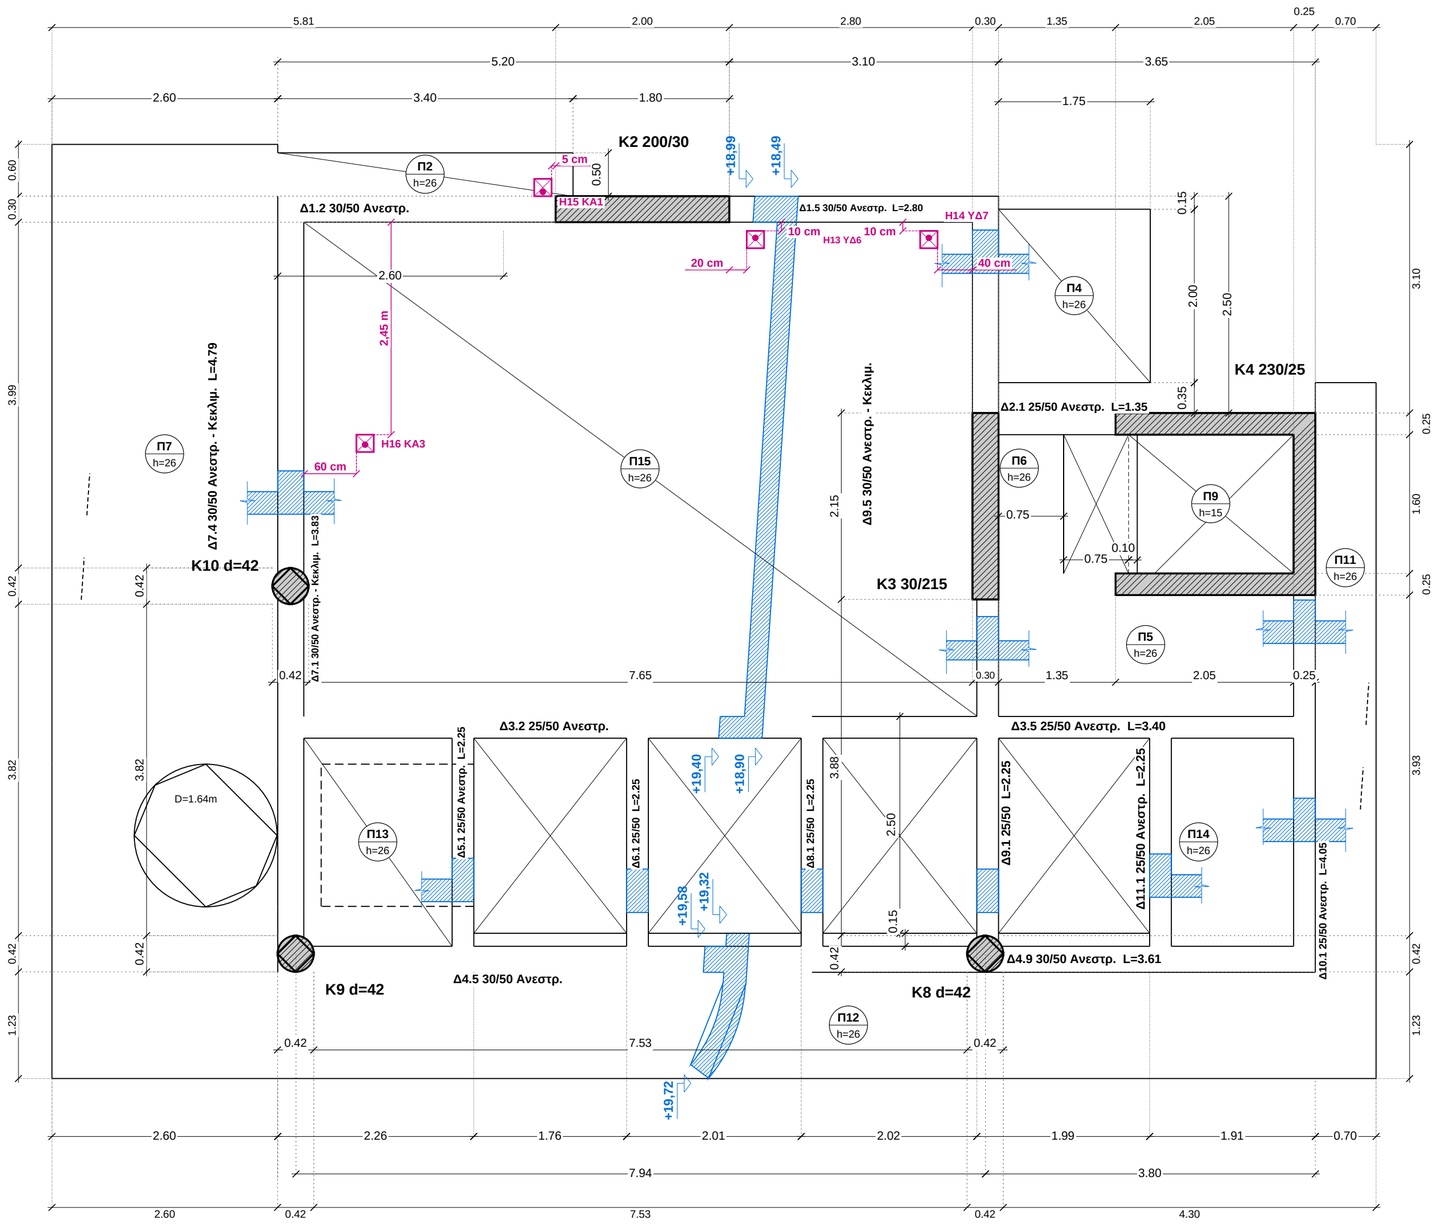


ΚΩΝΣΤΑΝΤΙΝΟΥΠΟΛΕΩΣ 12 & ΑΓ. ΒΑΡΒΑΡΑΣ, ΑΡΓΥΡΟΥΠΟΛΗ – ARKAD Ι.Κ.Ε.
Ξυλότυπος εργοταξίου – χωρίς οπλισμούς

ΞΥΛΟΤΥΠΟΣ ΣΟΦΙΤΑΣ (ΣΤΕΓΗ) Σ8

ΣΤΑΘΜΗ ΑΝΩ ΠΛΑΚΑΣ
+18,49 έως +19,72
ΚΛΙΜΑΚΑ 1:50 A2 · 100 %

0 1 2 m

Κ1 30/70	υποστύλωμα / τοιχείο (cm)
Δ1.1 30/40	δοκός: πλάτος / ύψος (το ύψος μαζί με την πλάκα)
L=3.50	καθαρό μήκος δοκού, παρειά με παρειά
Π3 h=15	πλάκα – πάχος (cm)
+0,30	στάθμη άνω μπετού (m)
μπλε	τομές επί τόπου / φυτευτά και οι στάθμες τους
☒	οπή πλάκας 20 × 20 (αποχέτευση / υδρορροή)

Διαστάσεις σε m, από γωνία / παρειά κολόνας σε γωνία κολόνας. Οι αλυσίδες παρειών μετρήθηκαν από τη γεωμετρία του σχεδίου, οι υπόλοιπες είναι του μελετητή.

ΟΠΕΣ ΠΛΑΚΑΣ – ΚΟΥΤΙ 20 × 20 · SHAFT
Θέση σε cm ως την ΑΚΜΗ του κουτιού, από παρειές σκυροδέματος.

H13 ΥΔ6 – σιφώνι στέγης Φ75
20 ανατ. της Α παρ. Κ2 · 10 νότια της Ν παρ. Δ1.5

H14 ΥΔ7 – σιφώνι στέγης Φ75
40 δυτ. της Δ παρ. Δ9.5 · 10 νότια της Ν παρ. Δ1.5

H15 ΚΑ1 – αερισμός ΑΠ1 Φ75
5 δυτ. της Δ παρ. Κ2 · κολλητά στη Β παρ. Δ1.2

H16 ΚΑ3 – αερισμός ΑΠ3 Φ75
60 ανατ. της Α παρ. Δ7.4 · 2,45 m νότια της Ν παρ. Δ1.2

Τεύχος αποχετεύσεων R22, φύλλο ΑΠ-17.
Καμία οπή σε δοκό, καμία αναμονή σε στηθαίο.

ΣΗΜΕΙΩΣΕΙΣ

· Πρόβολοι: υποδοχή σιφωνιού και υδρορροή ΠΡΙΝ το μπετό, να μην κοπεί οπλισμός (μελετητής).
· Στέγη κεκλιμένη: στάθμες (μπλε) στις τομές επί τόπου. «Ανεστρ.» = ανεστραμμένη δοκός.

Βάση: Σ8.pdf – ξυλότυπος σοφίτας, Γ. Κόγιας (οριστική μελέτη 02/2026, Drive 06/11/2026).
Οπλισμοί ΜΟΝΟ από το σχέδιο του μελετητή.

Έκδοση R04 – 11/11/2026