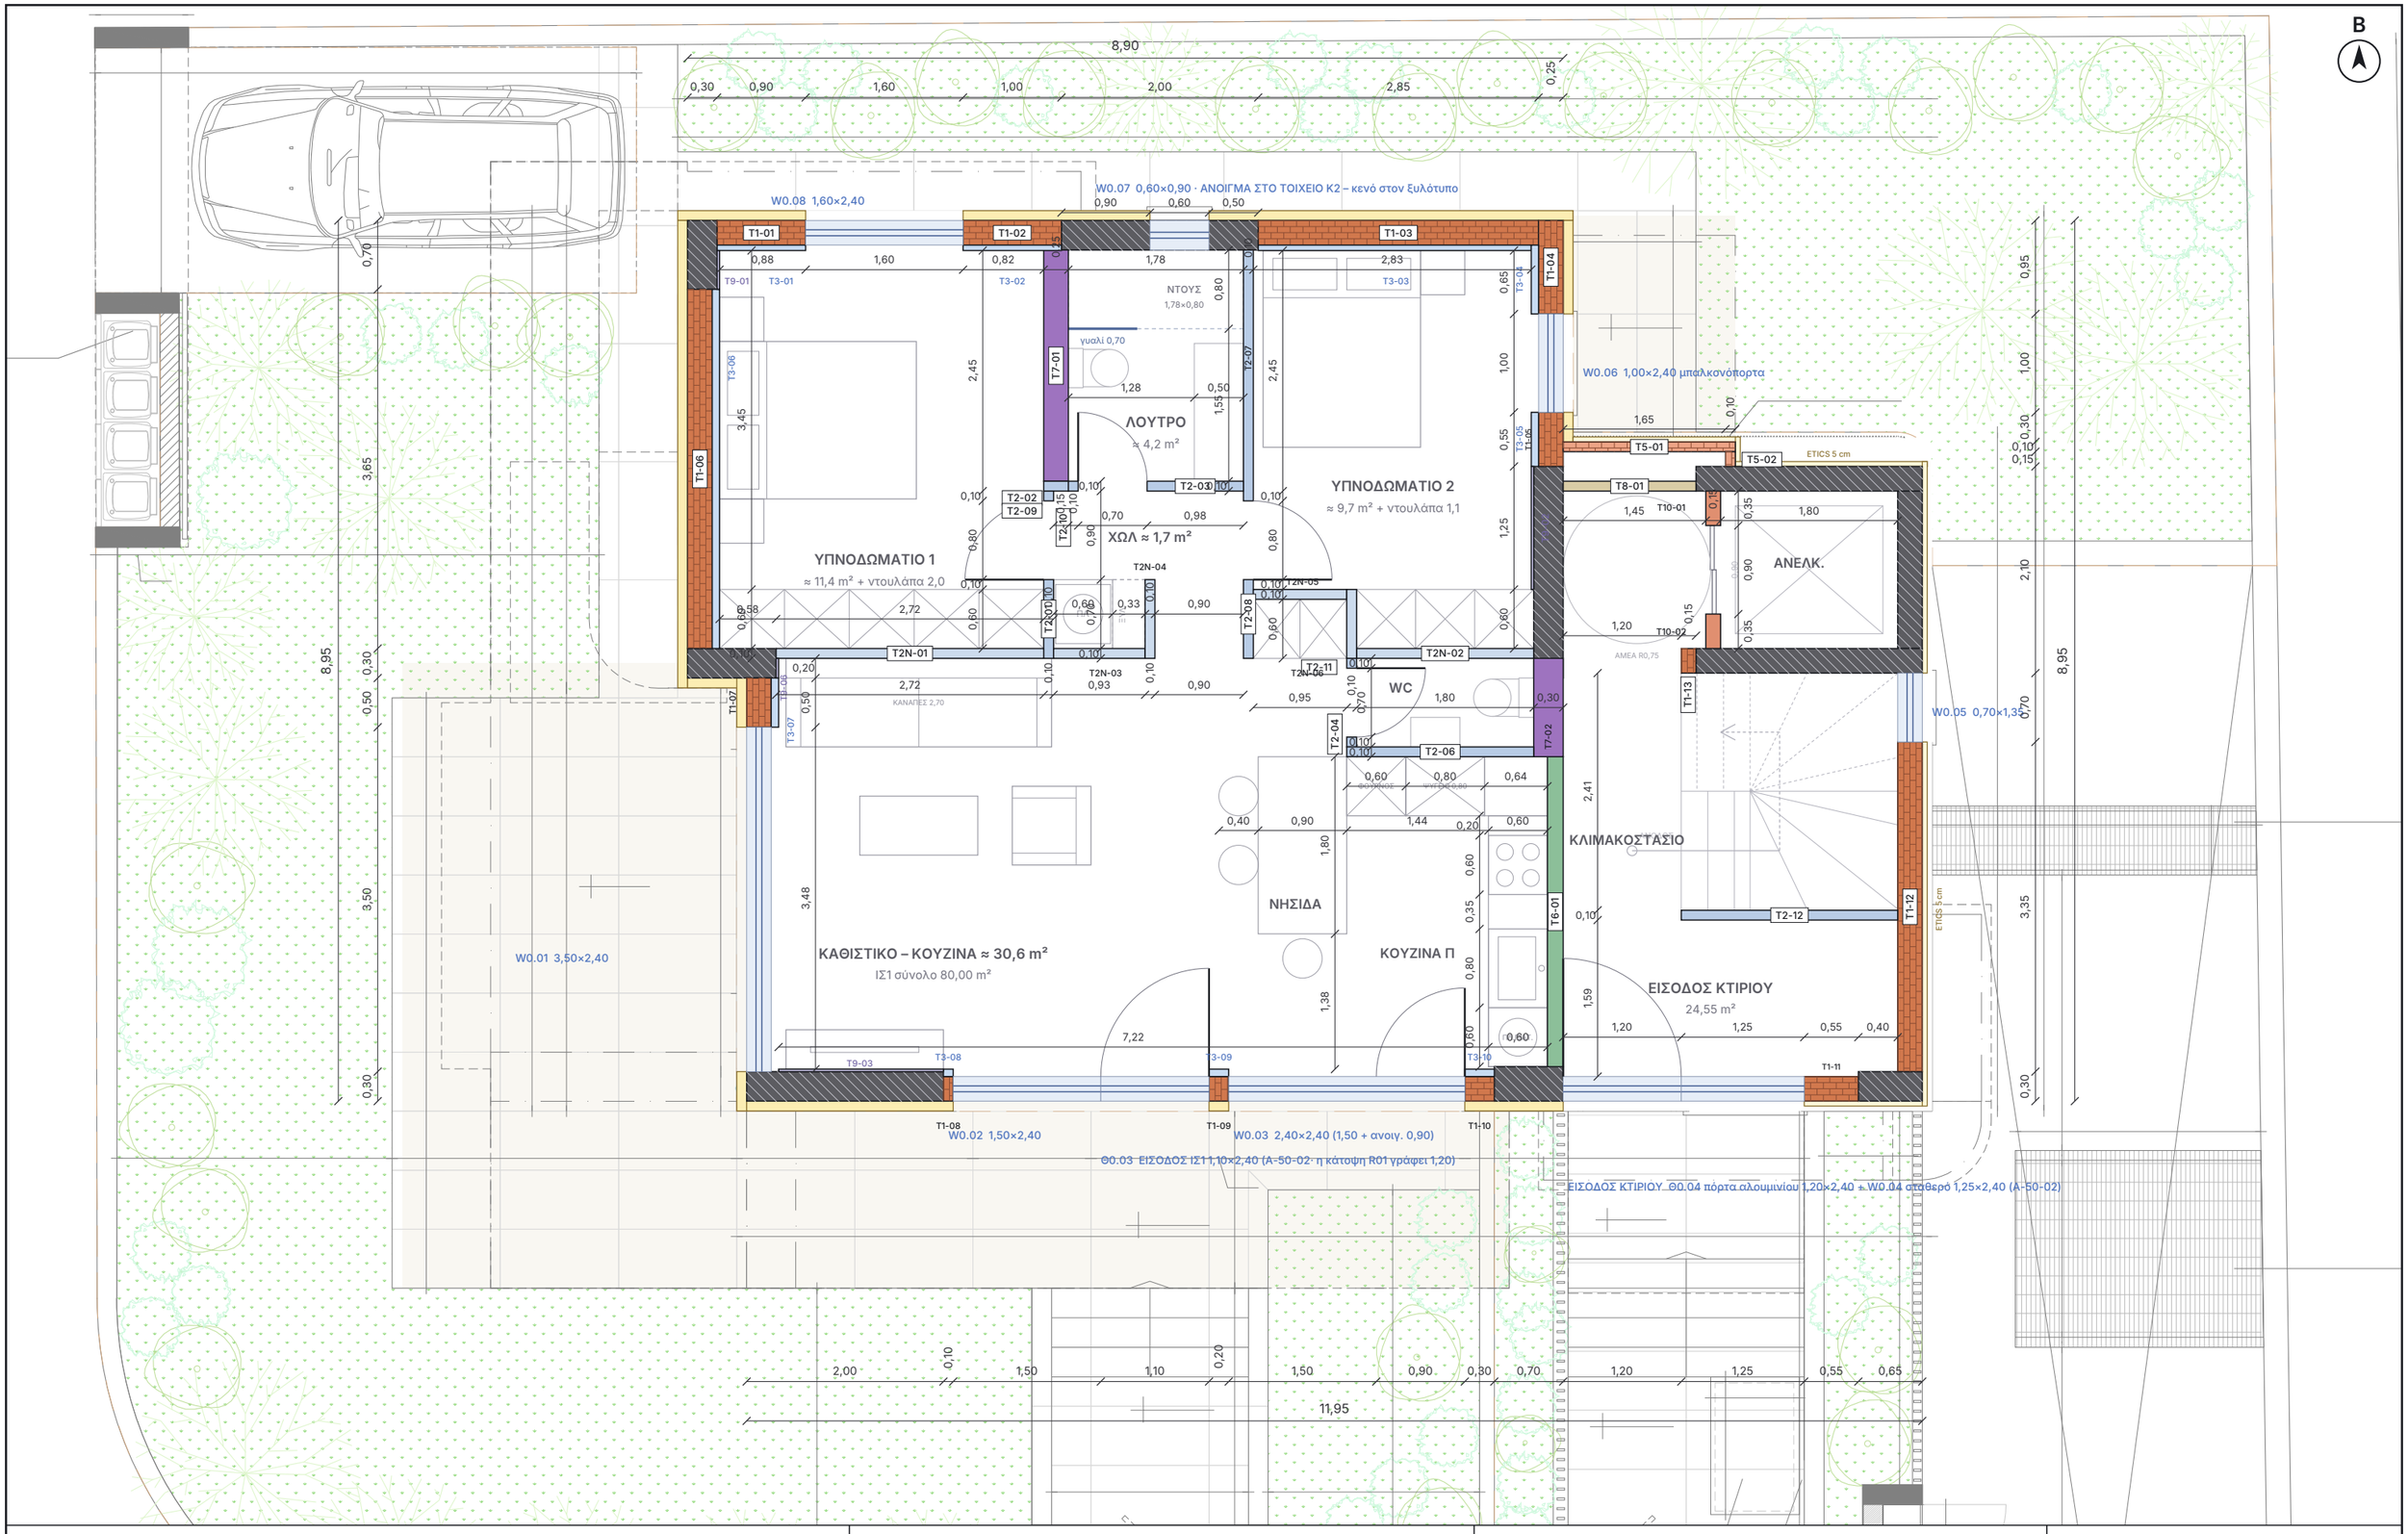


ΕΡΓΟ

ΠΕΝΤΑΟΡΟΦΟ ΚΤΗΡΙΟ ΚΑΤΟΙΚΙΩΝ – ΑΡΓΥΡΟΥΠΟΛΗ
Κωνσταντινουπόλεως 12 & Αγ. Βαρβάρας · Ο.Τ. 103-15
Εργοδότης: INTERKAT Α.Ε. · Κατασκευή: ARKAD Ι.Κ.Ε.

ΘΕΜΑ ΣΧΕΔΙΟΥ

ΚΑΤΟΨΗ ΤΟΙΧΟΠΟΙΙΩΝ – ΙΣΟΓΕΙΟΥ

Είδη τοιχοποιιών · διαστάσεις χάραξης · κουφώματα · εξώστες
ΙΣΟΓΕΙΟ – ΙΣ1

ΒΑΣΗ

Βάση: A-10-GF R01 (05/11/2026, Drive) · Σ3_ΕΦ · κανόνες B1 R20

ΑΡ. ΣΧΕΔΙΟΥ


T-01

Κλίμακα 1:60 · A3
07/11/2026 · R12


T1 Εξωτερική οπτοπλινθοδομή

1:4

πάχος 25 cm

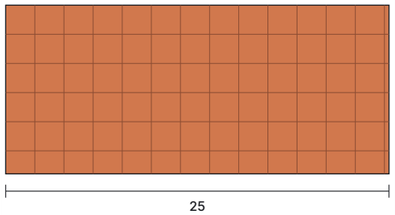

θερμομονωτικό τούβλο κάθετων οπών 25 cm · θερμοπρόσοψη 10 cm έξω · επένδυση T3 μέσα όπου σημειώνεται

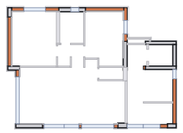


Τοίχοι: T1-01, T1-02, T1-03, T1-04, T1-05, T1-06, T1-07, T1-08, T1-09, T1-10, T1-11, T1-12, T1-13

Μήκος 15,35 m · επιφάνεια ≈ 46,0 m²


T5 Οπτοπλινθοδομή πυρήνα

1:4

πάχος 10 cm

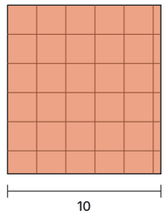

θερμομονωτικό τούβλο κάθετων οπών 10 cm · γύρω από τον πυρήνα (ανελκυστήρας – ηλεκτροστάσιο)

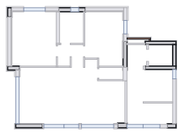


Τοίχοι: T5-01, T5-02

Μήκος 1,90 m · επιφάνεια ≈ 5,7 m²


T10 Μέτωπο ανελκυστήρα

1:4

πάχος 15 cm

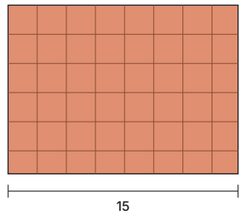

θερμομονωτικό τούβλο κάθετων οπών 15 cm · μέτωπο φρεατίου εκατέρωθεν της πόρτας 0,90 · στην ΕΣΩΤΕΡΙΚΗ παρειά της δοκού μετώπου του φρεατίου (Δ5.1 25/40 στον Σ3, x 11,05–11,30) → x 11,15–11,30, σε όλους τους ορόφους (R21 / ισόγειο R09, Γιάννης 07/11) · θέση πόρτας προς επιβεβαίωση από τον προμηθευτή

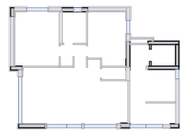


Τοίχοι: T10-01, T10-02

Μήκος 0,70 m · επιφάνεια ≈ 2,1 m²

T3 Επένδυση τοίχου

1:4

πάχος 5,5 cm

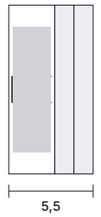

σκελετός 30 · 2 × γυψοσανίδα 12,5 · στις εσωτερικές παρειές των T1 – ΟΧΙ όπου πλακάκι ή ντουλάπα, ΟΧΙ στα έρκερ




Τοίχοι: T3-01, T3-02, T3-03, T3-04, T3-05, T3-06, T3-07, T3-08, T3-09, T3-10

Μήκος 10,68 m · επιφάνεια ≈ 32,0 m²


T9 Επένδυση υποστυλώματος

1:4

πάχος 2,5 cm

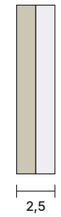

κόλλα + 1 × γυψοσανίδα 12,5 (ένα φύλλο) · στις παρειές υποστυλωμάτων μέσα στα διαμερίσματα – ΟΧΙ όπου πλακάκι ή ντουλάπα

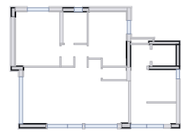


Τοίχοι: T9-01, T9-02, T9-03, T9-06

Μήκος 3,52 m · επιφάνεια ≈ 10,6 m²


T2 Χώρισμα γυψοσανίδας

1:4

πάχος 10 cm

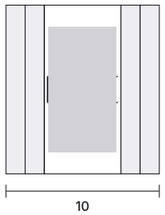

2 × γυψοσανίδα 12,5 · σκελετός CW 50 · 2 × γυψοσανίδα 12,5 · εσωτερικά χωρίσματα · ανθυγρή γυψοσανίδα στην πλευρά των λουτρών · ανοίγματα πορτών με ορθοστάτες UA 50 (2 mm)

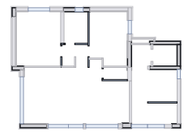


Τοίχοι: T2-12, T2-07, T2-08, T2-01, T2-02, T2-03, T2-04, T2-06, T2-09, T2-10, T2-11

Μήκος 9,88 m · επιφάνεια ≈ 29,6 m²


T2N Χώρισμα γυψ. – πλευρά ντουλάπας

1:4

πάχος 8,75 cm

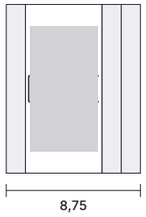

1 × γυψοσανίδα 12,5 (πλευρά ντουλάπας) · σκελετός CW 50 · 2 × γυψοσανίδα 12,5 · όπου η μία παρειά βλέπει σε ντουλάπα: ένα φύλλο αρκεί (κανόνας R15)

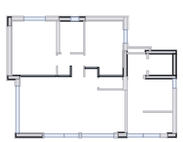


Τοίχοι: T2N-01, T2N-02, T2N-05, T2N-06, T2N-03, T2N-04

Μήκος 7,90 m · επιφάνεια ≈ 23,7 m²


T7 Τοίχος λεκάνης WC

1:4

πάχος 25 cm

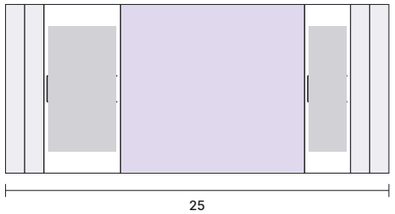

2 × γυψοσανίδα 12,5 · σκελετός CW 50 · κενό 12 cm (καζανάκι γυψοσανίδας στον σκελετό + κατακόρυφη στήλη Ø110, έξοδος Ø90) · σκελετός CW 30 · 2 × γυψοσανίδα 12,5 · ΟΛΟΙ οι τοίχοι λεκανών · ανθυγρή προς το λουτρό · στην πλευρά ντουλάπας 1 φύλλο · ανοίγματα πορτών με ορθοστάτες UA 50 (2 mm)

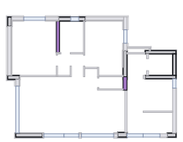


Τοίχοι: T7-01, T7-02

Μήκος 3,35 m · επιφάνεια ≈ 10,0 m²


T6 Τοίχος κλιμακοστασίου – διπλός σκελετός

1:4

πάχος 16 cm

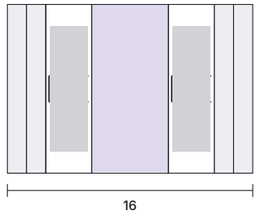

2 × γυψοσανίδα 12,5 πυράντοχη · σκελετός CW 30 · κενό 5 cm · σκελετός CW 30 · 2 × γυψοσανίδα 12,5 πυράντοχη = 16 cm · ισόγειο: T6-01 προς το lobby (R09, Γιάννης) · χωρίς πόρτα

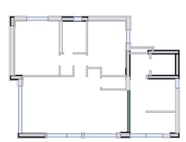


Τοίχοι: T6-01

Μήκος 3,15 m · επιφάνεια ≈ 9,4 m²


T8 Τοίχος shaft

1:4

πάχος 10 cm

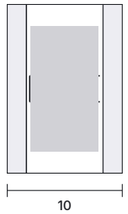

πλαίσιο + ανοιγόμενα φύλλα γυψοσανίδας · μέτωπο shaft ηλεκτρολογικών

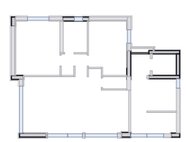

Τοίχοι: T8-01

Μήκος 1,35 m · επιφάνεια ≈ 4,1 m²

Επιφάνειες ενδεικτικές: μήκος × ύψος 3,00 m (τελικό δάπεδο – πλάκα) – οι τοίχοι ορίζονται μεταξύ ανοιγμάτων, χωρίς αφαίρεση κασών. T3 = επένδυση στην εσωτερική παρειά των T1 · T9 = περίμετρος υποστυλώματος × ύψος. R15: T2N = 1 φύλλο στην πλευρά ντουλάπας (T2N-01, T2N-02) · T7-01 1 φύλλο προς Υπν.1.

ΕΡΓΟ

ΠΕΝΤΑΟΡΟΦΟ ΚΤΗΡΙΟ ΚΑΤΟΙΚΙΩΝ – ΑΡΓΥΡΟΥΠΟΛΗ
Κωνσταντινουπόλεως 12 & Αγ. Βαρβάρας · Ο.Τ. 103-15
Εργοδότης: INTERKAT Α.Ε. · Κατασκευή: ARKAD Ι.Κ.Ε.

ΘΕΜΑ ΣΧΕΔΙΟΥ

ΕΙΔΗ ΤΟΙΧΟΠΟΙΙΩΝ – ΙΣΟΓΕΙΟΥ
Είδη τοιχοποιιών · ΙΣΟΓΕΙΟ – ΙΣ1
τομές 1:4 · μήκη – εμβαδά ανά είδος

ΒΑΣΗ

Βάση: κάτοψη τοιχοποιιών T-01 · κάτοψη A-10-GF

ΑΡ. ΣΧΕΔΙΟΥ

T-02
Κλίμακα 1:4 · A3
07/11/2026 · R12




ΕΡΓΟ	ΘΕΜΑ ΣΧΕΔΙΟΥ	ΒΑΣΗ	ΑΡ. ΣΧΕΔΙΟΥ
ΠΕΝΤΑΟΡΟΦΟ ΚΤΗΡΙΟ ΚΑΤΟΙΚΙΩΝ – ΑΡΓΥΡΟΥΠΟΛΗ Κωνσταντινουπόλεως 12 & Αγ. Βαρβάρας · Ο.Τ. 103-15 Εργοδότης: INTERKAT Α.Ε. · Κατασκευή: ARKAD Ι.Κ.Ε.	**ΚΑΤΟΨΗ ΤΟΙΧΟΠΟΙΙΩΝ – Β΄ ΟΡΟΦΟΣ** Είδη τοιχοποιιών · διαστάσεις χάραξης · κουφώματα · εξώστες Β΄ ΟΡΟΦΟΣ – Β1	Βάση: κάτοψη Α-10-2F (μελέτη εφαρμογής) · ξυλότυποι Σ · R14 + αλλαγές 05/11	**Τ-03** **Κλίμακα 1:60 · Α3** 07/11/2026 · R23


T1 Εξωτερική οπτοπλινθοδομή

1:4

πάχος 25 cm

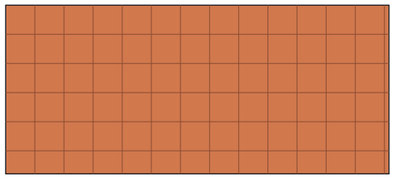

θερμομονωτικό τούβλο κάθετων οπών 25 cm · θερμοπρόσοψη 10 cm έξω · επένδυση Τ3 μέσα όπου σημειώνεται

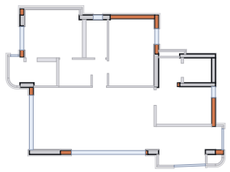


Τοίχοι: T1-01, T1-02, T1-03, T1-04, T1-05, T1-06, T1-07, T1-08, T1-09, T1-10, T1-11, T1-12

Μήκος 9,52 m · επιφάνεια ≈ 27,6 m²


T4 Έρκερ – απλή οπτοπλινθοδομή

1:4

πάχος 11 cm

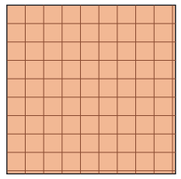

απλό τούβλο 6οπο 9 × 12 × 19 δρομικό ≈ 11 cm · σταθερή η εξωτερική παρειά · θερμοπρόσοψη 10 cm έξω

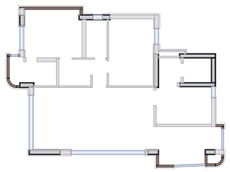


Τοίχοι: T4-01, T4-02, T4-03, T4-04, T4-05, T4-06, T4-07, T4-08, T4-09, T4-10, T4-11, T4-12, T4-13, T4-14, T4-15

Μήκος 12,02 m · επιφάνεια ≈ 34,8 m²


T5 Οπτοπλινθοδομή πυρήνα

1:4

πάχος 10 cm

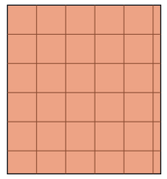

θερμομονωτικό τούβλο κάθετων οπών 10 cm · γύρω από τον πυρήνα (ανελκυστήρας – ηλεκτροστάσιο)

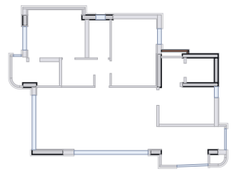


Τοίχοι: T5-01, T5-02

Μήκος 1,90 m · επιφάνεια ≈ 5,5 m²


T10 Μέτωπο ανελκυστήρα

1:4

πάχος 15 cm

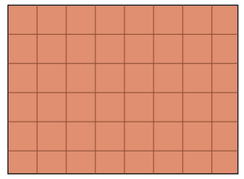

θερμομονωτικό τούβλο κάθετων οπών 15 cm · μέτωπο φρεατίου εκατέρωθεν της πόρτας 0,90 · στην ΕΣΩΤΕΡΙΚΗ παρειά της δοκού μετώπου του φρεατίου (Δ5.1 25/40 στον Σ3, x 11,05–11,30) → x 11,15–11,30, σε όλους τους ορόφους (R21 / ισόγειο R09, Γιάννης 07/11) · θέση πόρτας προς επιβεβαίωση από τον προμηθευτή

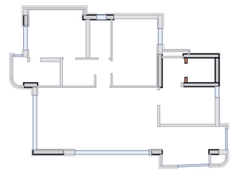


Τοίχοι: T10-01, T10-02

Μήκος 0,70 m · επιφάνεια ≈ 2,0 m²


T3 Επένδυση τοίχου

1:4

πάχος 5,5 cm

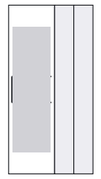

σκελετός 30 · 2 × γυψοσανίδα 12,5 · στις εσωτερικές παρειές των Τ1 – ΟΧΙ όπου πλακάκι ή ντουλάπα, ΟΧΙ στα έρκερ

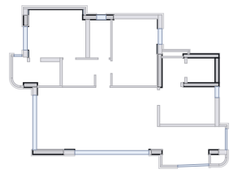

Τοίχοι: T3-01, T3-02, T3-03, T3-04, T3-05, T3-06, T3-07, T3-08, T3-09, T3-10

Μήκος 7,43 m · επιφάνεια ≈ 21,5 m²


T9 Επένδυση υποστυλώματος

1:4

πάχος 2,5 cm



κόλλα + 1 × γυψοσανίδα 12,5 (ένα φύλλο) · στις παρειές υποστυλωμάτων μέσα στα διαμερίσματα – ΟΧΙ όπου πλακάκι ή ντουλάπα

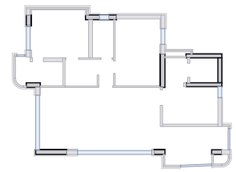


Τοίχοι: T9-01, T9-03, T9-04, T9-05

Μήκος 5,45 m · επιφάνεια ≈ 15,8 m²


T2 Χώρισμα γυψοσανίδας

1:4

πάχος 10 cm

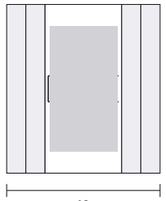

2 × γυψοσανίδα 12,5 · σκελετός CW 50 · 2 × γυψοσανίδα 12,5 · εσωτερικά χωρίσματα · ανθυγρή γυψοσανίδα στην πλευρά των λουτρών · ανοίγματα πορτών με ορθοστάτες UA 50 (2 mm)

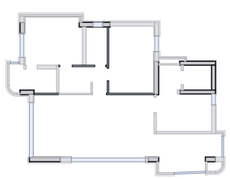


Τοίχοι: T2-01, T2-02, T2-04, T2-06, T2-07, T2-08, T2-09

Μήκος 9,75 m · επιφάνεια ≈ 28,3 m²


T2N Χώρισμα γυψ. – πλευρά ντουλάπας

1:4

πάχος 8,75 cm

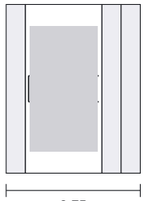

1 × γυψοσανίδα 12,5 (πλευρά ντουλάπας) · σκελετός CW 50 · 2 × γυψοσανίδα 12,5 · όπου η μία παρειά βλέπει σε ντουλάπα: ένα φύλλο αρκεί (κανόνας R15)

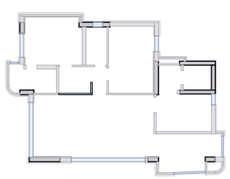


Τοίχοι: T2N-01, T2N-02

Μήκος 2,85 m · επιφάνεια ≈ 8,3 m²


T2A Χώρισμα γυψοσανίδας 15

1:4

πάχος 15 cm

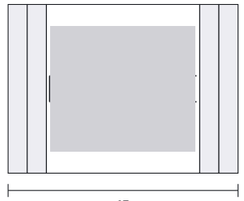

2 × γυψοσανίδα 12,5 · σκελετός CW 100 + πετροβάμβακας · 2 × γυψοσανίδα 12,5 · λουτρό γονέων / χωλ · υπνοδωμάτια · ανοίγματα πορτών με ορθοστάτες UA 100 (2 mm)

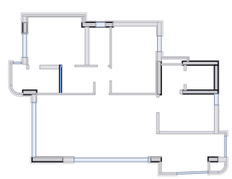


Τοίχοι: T2A-01

Μήκος 1,80 m · επιφάνεια ≈ 5,2 m²


T7 Τοίχος λεκάνης WC

1:4

πάχος 25 cm

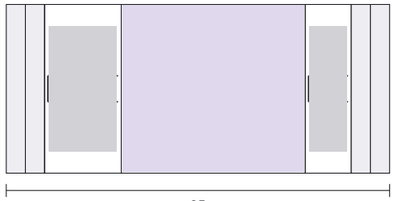

2 × γυψοσανίδα 12,5 · σκελετός CW 50 · κενό 12 cm (καζανάκι γυψοσανίδας στον σκελετό + κατακόρυφη στήλη Ø110, έξοδος Ø90) · σκελετός CW 30 · 2 × γυψοσανίδα 12,5 · ΟΛΟΙ οι τοίχοι λεκανών · ανθυγρή προς το λουτρό · στην πλευρά ντουλάπας 1 φύλλο · ανοίγματα πορτών με ορθοστάτες UA 50 (2 mm)

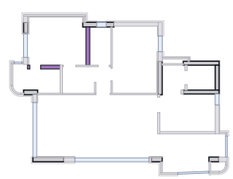


Τοίχοι: T7-01, T7-02, T7-03

Μήκος 3,95 m · επιφάνεια ≈ 11,5 m²


T6A Τοίχος κλιμακοστασίου 15

1:4

πάχος 15 cm

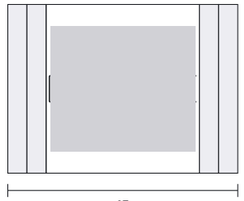

2 × γυψοσανίδα 12,5 πυράντοχη · σκελετός CW 100 + πετροβάμβακας · 2 × γυψοσανίδα 12,5 πυράντοχη = 15 cm · Β1: διαμέρισμα προς κλιμακοστάσιο (Τ6Α-01 / Τ6Α-03 με την πόρτα εισόδου – ορθοστάτες UA 100 + ψευτόκασα) και μέτωπο σκάλας Τ6Α-02 · (ως R21 ονομαζόταν Τ6)

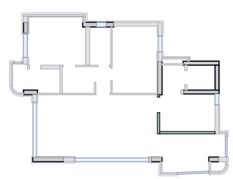


Τοίχοι: T6A-01, T6A-02, T6A-03

Μήκος 5,06 m · επιφάνεια ≈ 14,7 m²


T8 Τοίχος shaft

1:4

πάχος 10 cm

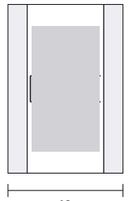

πλαίσιο + ανοιγόμενα φύλλα γυψοσανίδας · μέτωπο shaft ηλεκτρολογικών

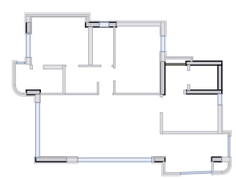

Τοίχοι: T8-01

Μήκος 1,35 m · επιφάνεια ≈ 3,9 m²

Επιφάνειες ενδεικτικές: μήκος × ύψος 2,90 m (τελικό δάπεδο – πλάκα) – οι τοίχοι ορίζονται μεταξύ ανοιγμάτων, χωρίς αφαίρεση κασών. Τ3 = επένδυση στην εσωτερική παρειά των Τ1 · Τ9 = περίμετρος υποστυλώματος × ύψος. R15: Τ2Ν = 1 φύλλο στην πλευρά ντουλάπας (Τ2Ν-01, Τ2Ν-02) · Τ7-01 1 φύλλο προς Υπν.1.

ΕΡΓΟ

ΠΕΝΤΑΟΡΟΦΟ ΚΤΗΡΙΟ ΚΑΤΟΙΚΙΩΝ – ΑΡΓΥΡΟΥΠΟΛΗ
Κωνσταντινουπόλεως 12 & Αγ. Βαρβάρας · Ο.Τ. 103-15
Εργοδότης: INTERKAT Α.Ε. · Κατασκευή: ARKAD Ι.Κ.Ε.

ΘΕΜΑ ΣΧΕΔΙΟΥ

ΕΙΔΗ ΤΟΙΧΟΠΟΙΙΩΝ – Β΄ ΟΡΟΦΟΣ
Είδη τοιχοποιιών · Β΄ ΟΡΟΦΟΣ – Β1
τομές 1:4 · μήκη – εμβαδά ανά είδος

ΒΑΣΗ

Βάση: κάτοψη τοιχοποιιών Τ-01 · κάτοψη Α-10-2F

ΑΡ. ΣΧΕΔΙΟΥ

Τ-04
Κλίμακα 1:4 · Α3
07/11/2026 · R23

ΠΡΟΜΕΤΡΗΣΗ ΤΟΙΧΟΠΟΙΙΩΝ – ΤΕΤΡΑΓΩΝΙΚΑ ΑΝΑ ΤΥΠΟΛΟΓΙΑ ΚΑΙ ΑΝΑ ΟΡΟΦΟ

ΙΣΟΓΕΙΟ – ΙΣ1 · R12

H = 3,00 m · μήκη στον άξονα, χωρίς αφαίρεση κουφωμάτων · υπέρθυρα πορτών στο είδος του τοίχου

	Τύπος	Περιγραφή	Πάχος cm	Τοίχοι	Μήκος m	m²
ΤΟΥΒΛΑ						
	T1	Εξωτερική οπτοπλινθοδομή	25	13	15,35	**46,0**
	T5	Οπτοπλινθοδομή πυρήνα	10	2	1,90	**5,7**
	T10	Μέτωπο ανελκυστήρα	15	2	0,70	**2,1**
	Σύνολο τουβλα					**53,9 m²**
ΧΩΡΙΣΜΑΤΑ ΓΥΨΟΣΑΝΙΔΑΣ						
	T2	Χώρισμα γυψοσανίδας	10	11	9,88	**29,6**
	T2N	Χώρισμα γυψ. – πλευρά ντουλάπας	8,8	6	7,90	**23,7**
	T7	Τοίχος λεκάνης WC	25	2	3,35	**10,0**
	T6	Τοίχος κλιμακοστασίου – διπλός σκελετό…	16	1	3,15	**9,4**
	T8	Τοίχος shaft	10	1	1,35	**4,1**
	Σύνολο χωρισματα γυψοσανιδας					**76,9 m²**
ΕΠΕΝΔΥΣΕΙΣ						
	T3	Επένδυση τοίχου	5,5	10	10,68	**32,0**
	T9	Επένδυση υποστυλώματος	2,5	4	3,52	**10,6**
	Σύνολο επενδυσεις					**42,6 m²**
	ΣΥΝΟΛΟ ΤΟΙΧΟΠΟΙΙΩΝ ΙΣ1					**173,3 m²**

ΘΕΡΜΟΠΡΟΣΟΨΗ (ETICS) – ΙΣΟΓΕΙΟΥ

10 cm όψεις διαμερίσματος · 5 cm κλιμακοστάσιο / πυρήνας · ύψος 3,20 m (με τη μετώπη πλάκας) · καθαρά = όψη – κουφώματα + λαμπάδες

Ζώνη	Μήκος m	Μικτά m²	Κουφώματα	Λαμπάδες	Καθαρά m²
ETICS 10 cm – διαμέρισμα	29,40	94,1	−27,2	+5,9	**72,8**
ETICS 5 cm – κλιμακοστάσιο / πυρήνας	14,15	45,3	−6,8	+2,0	**40,5**
Σύνολο ETICS ΙΣ1					**113,3 m²**

Β΄ ΟΡΟΦΟΣ – Β1 · R23

H = 2,90 m · μήκη στον άξονα, χωρίς αφαίρεση κουφωμάτων · υπέρθυρα πορτών στο είδος του τοίχου

	Τύπος	Περιγραφή	Πάχος cm	Τοίχοι	Μήκος m	m²
ΤΟΥΒΛΑ						
	T1	Εξωτερική οπτοπλινθοδομή	25	12	9,52	**27,6**
	T4	Έρκερ – απλή οπτοπλινθοδομή	11	15	12,02	**34,8**
	T5	Οπτοπλινθοδομή πυρήνα	10	2	1,90	**5,5**
	T10	Μέτωπο ανελκυστήρα	15	2	0,70	**2,0**
	Σύνολο τουβλα					**70,0 m²**
ΧΩΡΙΣΜΑΤΑ ΓΥΨΟΣΑΝΙΔΑΣ						
	T2	Χώρισμα γυψοσανίδας	10	7	9,75	**28,3**
	T2N	Χώρισμα γυψ. – πλευρά ντουλάπας	8,8	2	2,85	**8,3**
	T2A	Χώρισμα γυψοσανίδας 15	15	1	1,80	**5,2**
	T7	Τοίχος λεκάνης WC	25	3	3,95	**11,5**
	T6A	Τοίχος κλιμακοστασίου 15	15	3	5,06	**14,7**
	T8	Τοίχος shaft	10	1	1,35	**3,9**
	Σύνολο χωρισματα γυψοσανιδας					**71,8 m²**
ΕΠΕΝΔΥΣΕΙΣ						
	T3	Επένδυση τοίχου	5,5	10	7,43	**21,5**
	T9	Επένδυση υποστυλώματος	2,5	4	5,45	**15,8**
	Σύνολο επενδυσεις					**37,4 m²**
	ΣΥΝΟΛΟ ΤΟΙΧΟΠΟΙΙΩΝ Β1					**179,1 m²**

ΘΕΡΜΟΠΡΟΣΟΨΗ (ETICS) – Β΄ ΟΡΟΦΟΥ

10 cm όψεις διαμερίσματος · 5 cm κλιμακοστάσιο / πυρήνας · ύψος 3,10 m (με τη μετώπη πλάκας) · καθαρά = όψη – κουφώματα + λαμπάδες

Ζώνη	Μήκος m	Μικτά m²	Κουφώματα	Λαμπάδες	Καθαρά m²
ETICS 10 cm – διαμέρισμα	39,72	123,1	−28,7	+6,2	**100,6**
ETICS 5 cm – κλιμακοστάσιο / πυρήνας	8,50	26,4	−0,9	+0,5	**25,9**
Σύνολο ETICS Β1					**126,5 m²**

ΣΥΝΟΛΑ ΤΕΥΧΟΥΣ

ΙΣ1: τοιχοποιίες 173,3 m² · ETICS 113,3 m² **Β1: τοιχοποιίες 179,1 m² · ETICS 126,5 m²**

ΟΛΟΙ ΟΙ ΟΡΟΦΟΙ ΤΟΥ ΤΕΥΧΟΥΣ: τοιχοποιίες 352,5 m² · ETICS 239,8 m²

ΕΡΓΟ	ΘΕΜΑ ΣΧΕΔΙΟΥ	ΒΑΣΗ	ΑΡ. ΣΧΕΔΙΟΥ
ΠΕΝΤΑΟΡΟΦΟ ΚΤΗΡΙΟ ΚΑΤΟΙΚΙΩΝ – ΑΡΓΥΡΟΥΠΟΛΗ Κωνσταντινουπόλεως 12 & Αγ. Βαρβάρας · Ο.Τ. 103-15 Εργοδότης: INTERKAT Α.Ε. · Κατασκευή: ARKAD Ι.Κ.Ε.	**ΠΡΟΜΕΤΡΗΣΗ ΤΟΙΧΟΠΟΙΙΩΝ – ΙΣΟΓΕΙΟ & Β΄ ΟΡΟΦΟΣ** Τετραγωνικά ανά τυπολογία τοίχου, χωριστά ανά όροφο θερμοπρόσοψη 10 / 5 cm	Βάση: κατόψεις τοιχοποιιών Τ-01 / Τ-03 · είδη Τ-02 / Τ-04	**Τ-05** — · A3 07/11/2026 · ΙΣ R12 · Β1 R23