
ΟΡΟΦΗ ΥΠΟΓΕΙΟΥ – ΣΥΛΛΕΚΤΗΡΑΣ ΛΥΜΑΤΩΝ

Κλίμακα 1:80

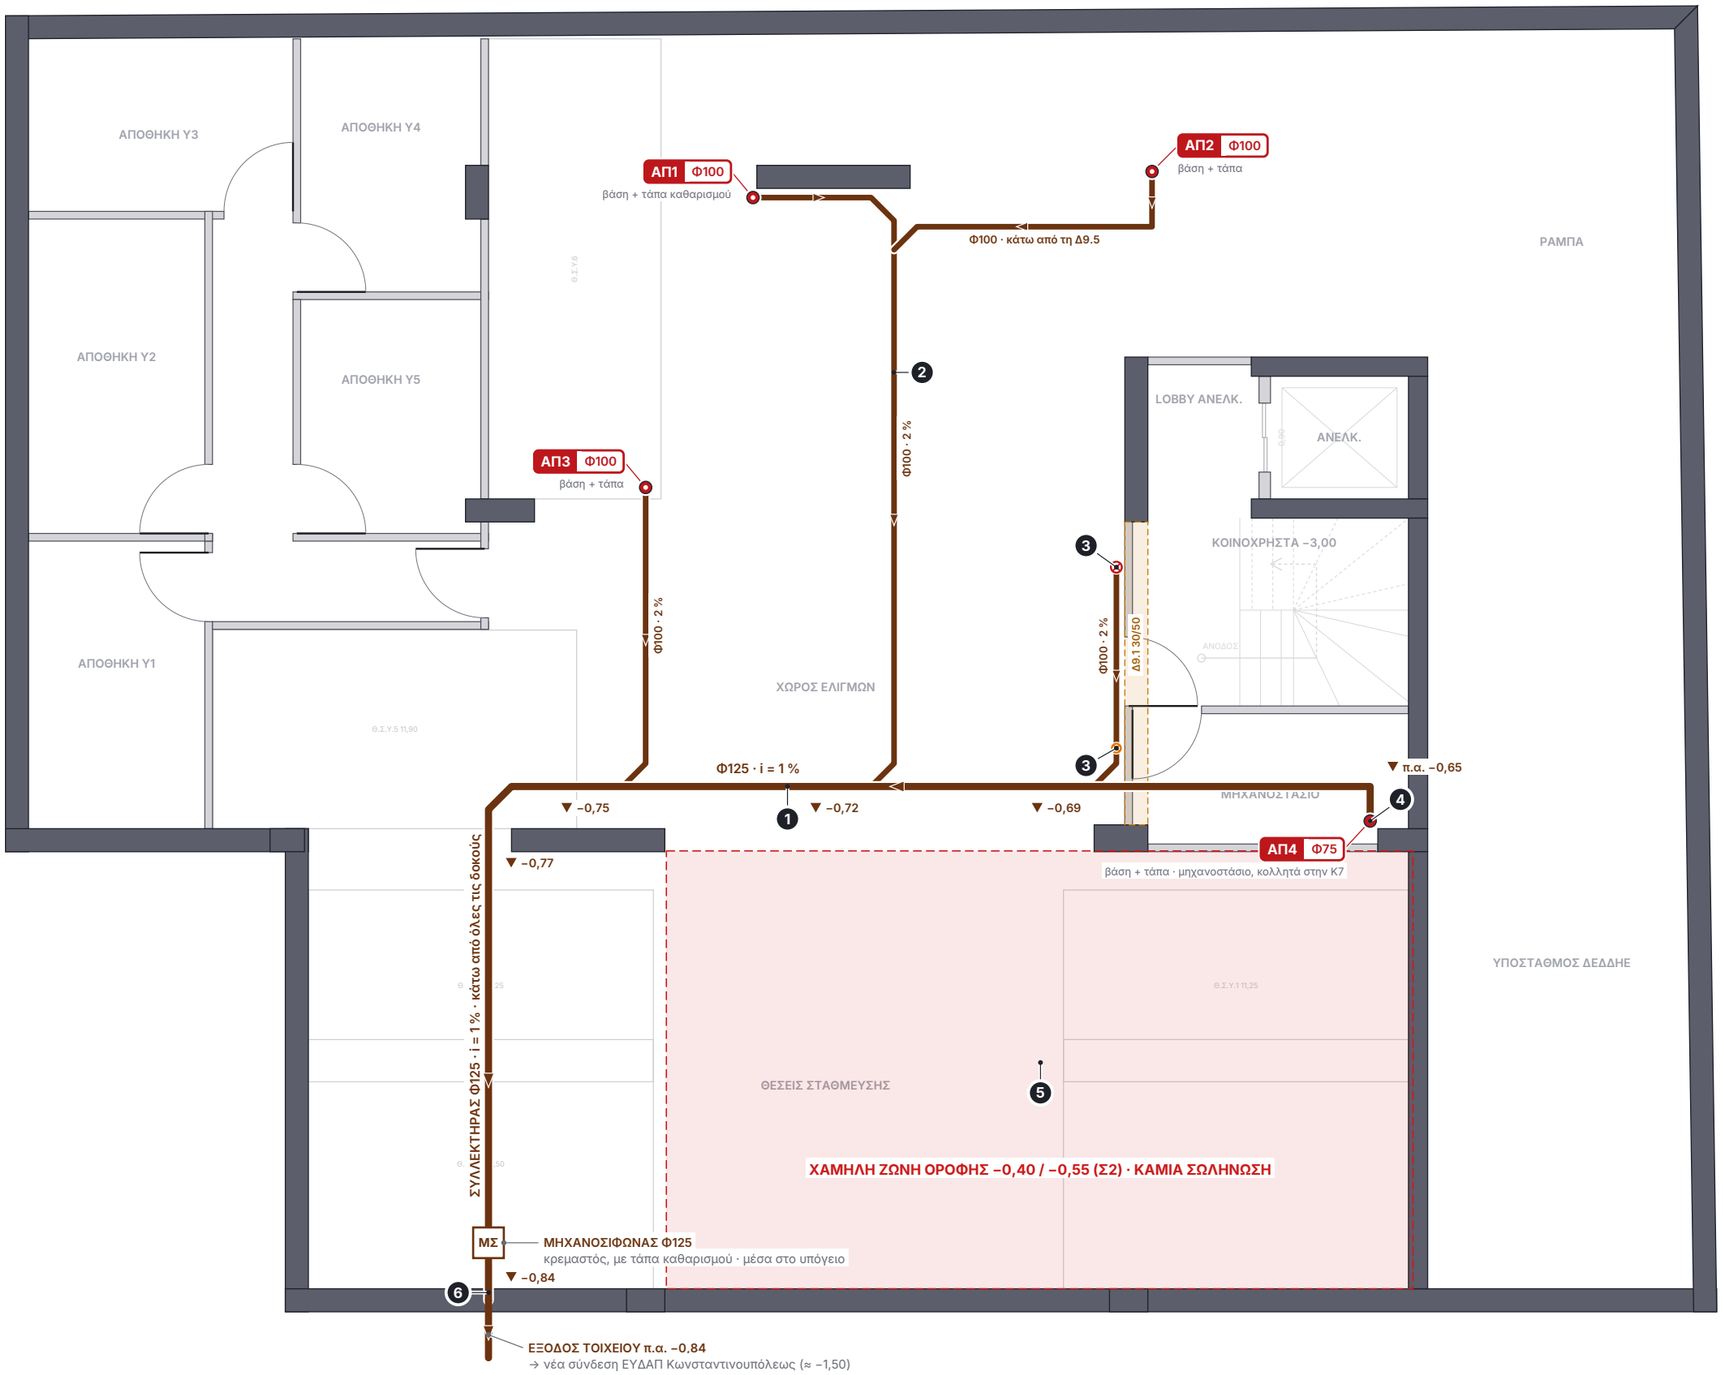

ΥΠΟΜΝΗΜΑ

- Συλλεκτήρας / κλάδοι υπογείου, κρεμαστοί κάτω από τις δοκούς
- Κατακόρυφη στήλη λυμάτων ΑΠ
- Πτώση στον κάτω όροφο
- Δοκός (ξυλότυποι Σ2–Σ7) – ΚΑΜΙΑ οπή
- Χαμηλή ζώνη οροφής υπογείου – καμία σωλήνωση
- 1 Αριθμημένη σημείωση – βλ. ΣΗΜΕΙΩΣΕΙΣ

ΣΗΜΕΙΩΣΕΙΣ

1. **Συλλεκτήρας Φ125, i = 1 %, 18,8 m:** κεφαλή ΑΠ4 π.α. −0,65 → έξοδος ΝΔ −0,84. Κρεμαστός κάτω από ΟΛΕΣ τις δοκούς του Σ2 – καμία διάτρηση.
2. **Κλάδος ΑΠ1 + ΑΠ2 (x 6,39):** η ΑΠ1 φέρνει και το λουτρό ΙΣ1. Η ΑΠ2 (σοφίτα) περνά κάτω από τη Δ9.5 και μπαίνει με 45°.
3. **WC + κουζίνα ΙΣ1 (x 9,29):** πτώση WC από το κούτελο 9,29 / 5,74 και πτώση νεροχύτη 9,29 / 8,10 σε ΕΝΑΝ κλάδο, 5 cm δυτικά της Δ9.1.
4. **Βάση ΑΠ4:** 12,60 / 9,05 μέσα στο μηχανοστάσιο, κολλητά στην Κ7 (πλάκα Π10, βόρεια της δοκού Κ8–Κ7).
5. **Χαμηλές ζώνες −0,40 / −0,55:** καμία σωλήνωση. Ο υποσταθμός ΔΕΔΔΗΕ δεν αγγίζεται.
6. **Μηχανοσίφωνας Φ125** πριν από την έξοδο, επισκέψιμος. Όλες οι συμβολές με 45°· τάπα καθαρισμού σε κάθε βάση στήλης και στην κεφαλή.


ΑΝΟΙΚΤΑ

- Βάθος σύνδεσης ΕΥΔΑΠ (≈ −1,50) – να επιβεβαιωθεί επί τόπου.
- Καθαρό ύψος 2,16 κάτω από τον συλλεκτήρα στις Θ.Σ.Υ. 3/4 (ΑΠ-10, αρ. 5).

ΕΡΓΟ	ΘΕΜΑ ΣΧΕΔΙΟΥ	ΒΑΣΗ	ΑΡ. ΣΧΕΔΙΟΥ
ΠΕΝΤΑΟΡΟΦΟ ΚΤΗΡΙΟ ΚΑΤΟΙΚΙΩΝ – ΑΡΓΥΡΟΥΠΟΛΗ Κωνσταντινουπόλεως 12 & Αγ. Βαρβάρας · Ο.Τ. 103-15 Εργοδότης: INTERKAT A.E. · Κατασκευή: ARKAD I.K.E.	**ΥΠΟΓΕΙΟ – ΣΥΛΛΕΚΤΗΡΑΣ ΛΥΜΑΤΩΝ** R16 · λύματα · ακάθαρτα · αερισμοί · όμβρια Οροφή υπογείου · συλλεκτήρας κάτω από τις δοκούς · έξοδος −0,84	Σ2 εφαρμογής · τοιχοποιίες υπογείου R05	**ΑΠ-01** **Κλίμακα 1:80 · A3** 10/11/2026 · R16

ΚΑΤΟΨΗ ΙΣΟΓΕΙΟΥ – ΑΠΟΧΕΤΕΥΣΗ & ΟΜΒΡΙΑ

Κλίμακα 1:60

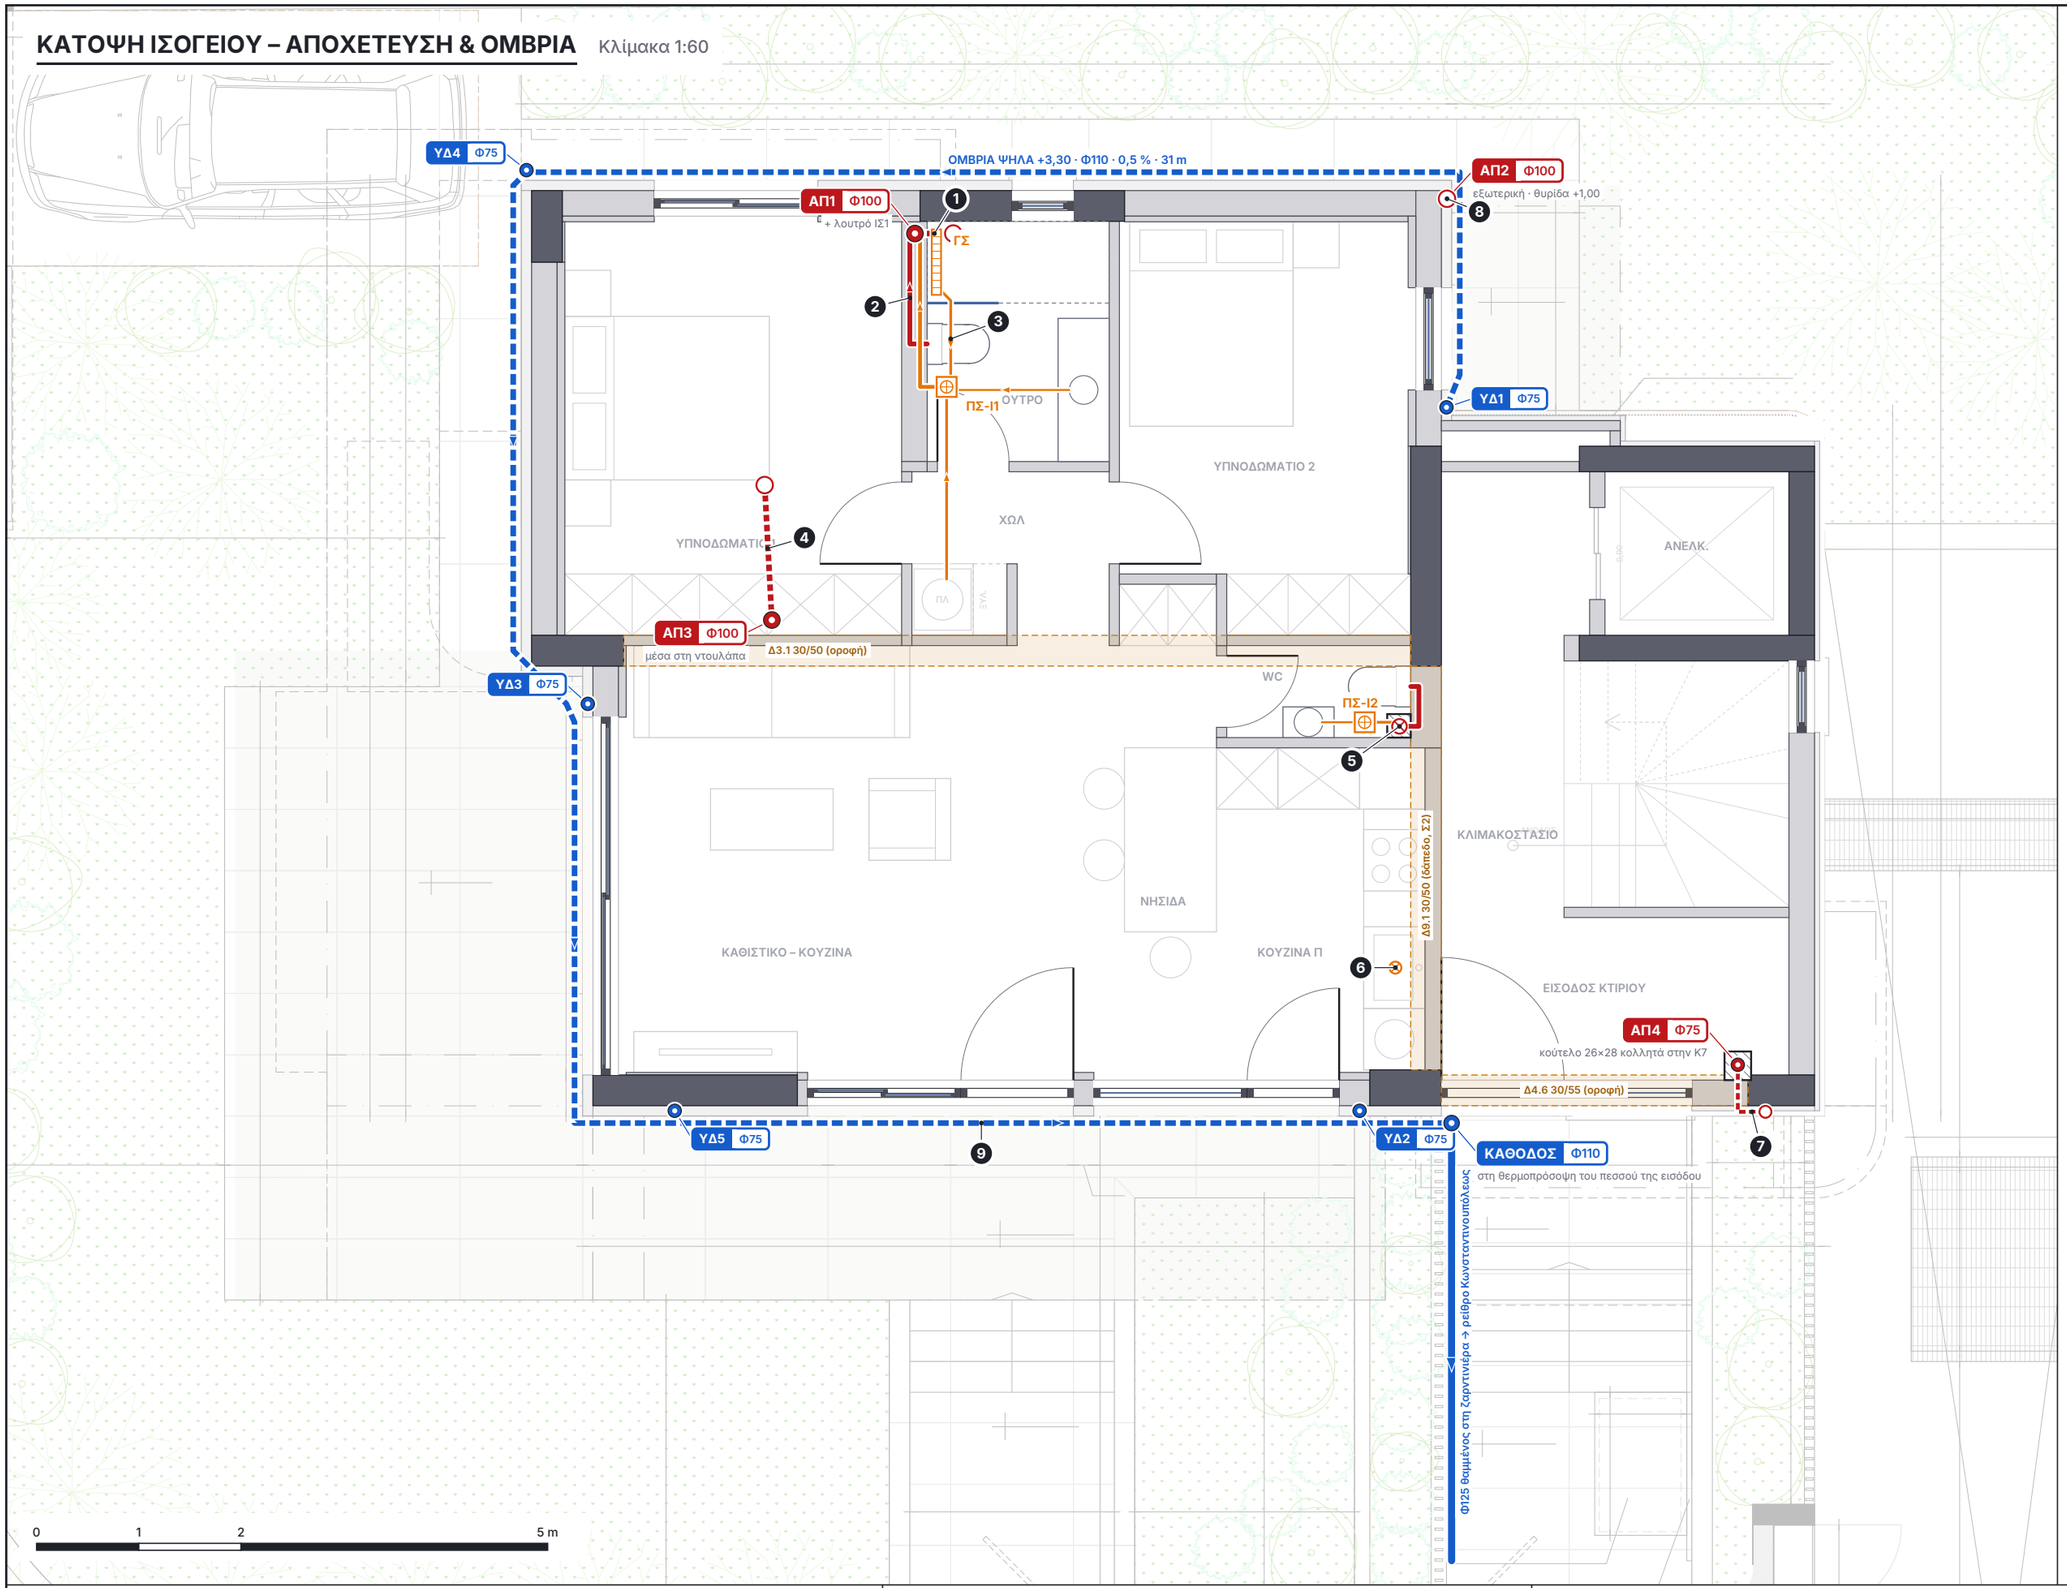

ΥΠΟΜΝΗΜΑ

- Λύματα: λεκάνη Φ90 · στήλη / αγωγός Φ100
- Ακάθαρτα: Φ40 νιπτήρας · Φ50 ντους, νεροχύτης, πλυντήριο · Φ75 έξοδος πατοσίφωνου
- Αγωγός στην οροφή του ορόφου (μετατόπιση στήλης 2×45°)
- Συλλεκτήρας ομβρίων ΨΗΛΑ +3,30 (οροφή προβόλων Α΄)
- Όμβρια: συλλεκτήρας / αγωγός
- Κατακόρυφη στήλη λυμάτων ΑΠ
- Στήλη που περνά / σταματά (χωρίς σύνδεση στον όροφο)
- Πτώση στον κάτω όροφο
- Πατοσίφωνο ΠΣ (σιφώνι δαπέδου με σχάρα)
- Γραμμικό σιφώνι ντους ΓΣ → πατοσίφωνο
- Κούτελο (κλειστό κανάλι γύρω από αγωγό)
- Υδρορροή ΥΔ Φ75 μέσα στη θερμοπρόσοψη
- Δοκός (ξυλότυποι Σ2–Σ7) – ΚΑΜΙΑ οπή


ΣΗΜΕΙΩΣΕΙΣ

1. **ΑΠ1:** μετατόπιση 2×45° στην οροφή του λουτρού → κατεβαίνει μέσα στον Τ7-01 του ισογείου (4,55 / 0,92).
2. **Λουτρό → ΑΠ1:** λεκάνη Φ90 μέσα στον Τ7-01. Σύνδεση ≈ 0,6 m πάνω από τον συλλεκτήρα → βάση με 2×45° και ευθύ 25 cm.
3. **Γραμμικό σιφώνι → πατοσίφωνο ΠΣ-Ι1** (Φ50). Νιπτήρας Φ40 και πλυντήριο Φ50 επίσης στο ΠΣ-Ι1. ΠΣ-Ι1 → ΑΠ1 Φ75 μέσα στον τοίχο.
4. **ΑΠ3:** 2×45° στην οροφή του Υπν.1 (1,3 m) → μέσα στη ντουλάπα (ανοικτό 1).
5. **WC:** λεκάνη Φ90 μέσα στον Τ7-02 → ΚΟΥΤΕΛΟ 23×23 δίπλα στη λεκάνη, πτώση Φ100 μέσα από πλάκα. Κάτω από τον τοίχο είναι η Δ9.1 – καμία οπή σε δοκό. Νιπτήρας → ΠΣ-Ι2 → κούτελο.
6. **Νεροχύτης:** Φ50 → πτώση Φ75. Στο υπόγειο ενώνεται με το WC.
7. **ΑΠ4 Φ75:** κατεβαίνει κολλητά στην Κ7, 0,3 m δυτικά μέσα από το τούβλο Τ1-11 (κάτω από τη Δ4.6) → ΚΟΥΤΕΛΟ 26×28 στη γωνία της Κ7 → μηχανοστάσιο.
8. **ΑΠ2 Φ100 εξωτερική** (σοφίτα): θυρίδα καθαρισμού +1,00, περνά κάτω από το γέμισμα +0,30 στο υπόγειο.
9. **Όμβρια:** ΥΔ1–ΥΔ5 → συλλεκτήρας ψηλά +3,30 → κάθοδος Φ110 στον πεσσό της εισόδου → Φ125 θαμμένος → ρείθρο.

ΕΡΓΟ	ΘΕΜΑ ΣΧΕΔΙΟΥ	ΒΑΣΗ	ΑΡ. ΣΧΕΔΙΟΥ
ΠΕΝΤΑΟΡΟΦΟ ΚΤΗΡΙΟ ΚΑΤΟΙΚΙΩΝ – ΑΡΓΥΡΟΥΠΟΛΗ Κωνσταντινουπόλεως 12 & Αγ. Βαρβάρας · Ο.Τ. 103-15 Εργοδότης: INTERKAT Α.Ε. · Κατασκευή: ARKAD Ι.Κ.Ε.	**ΙΣΟΓΕΙΟ – ΑΠΟΧΕΤΕΥΣΗ & ΟΜΒΡΙΑ** R16 · λύματα · ακάθαρτα · αερισμοί · όμβρια Λουτρό στην ΑΠ1 · κούτελα WC / ΑΠ4 · όμβρια ψηλά · λεπτομέρειες στο ΑΠ-06	Σ2 / Σ3 εφαρμογής · τοιχοποιίες ισογείου R13	**ΑΠ-02** **Κλίμακα 1:60 · A3** 10/11/2026 · R16

ΚΑΤΟΨΗ Α΄ · Β΄ · Γ΄ ΟΡΟΦΟΥ (ΤΥΠΙΚΟΣ) – ΑΠΟΧΕΤΕΥΣΗ & ΥΔΡΟΡΡΟΕΣ

Κλίμακα 1:60

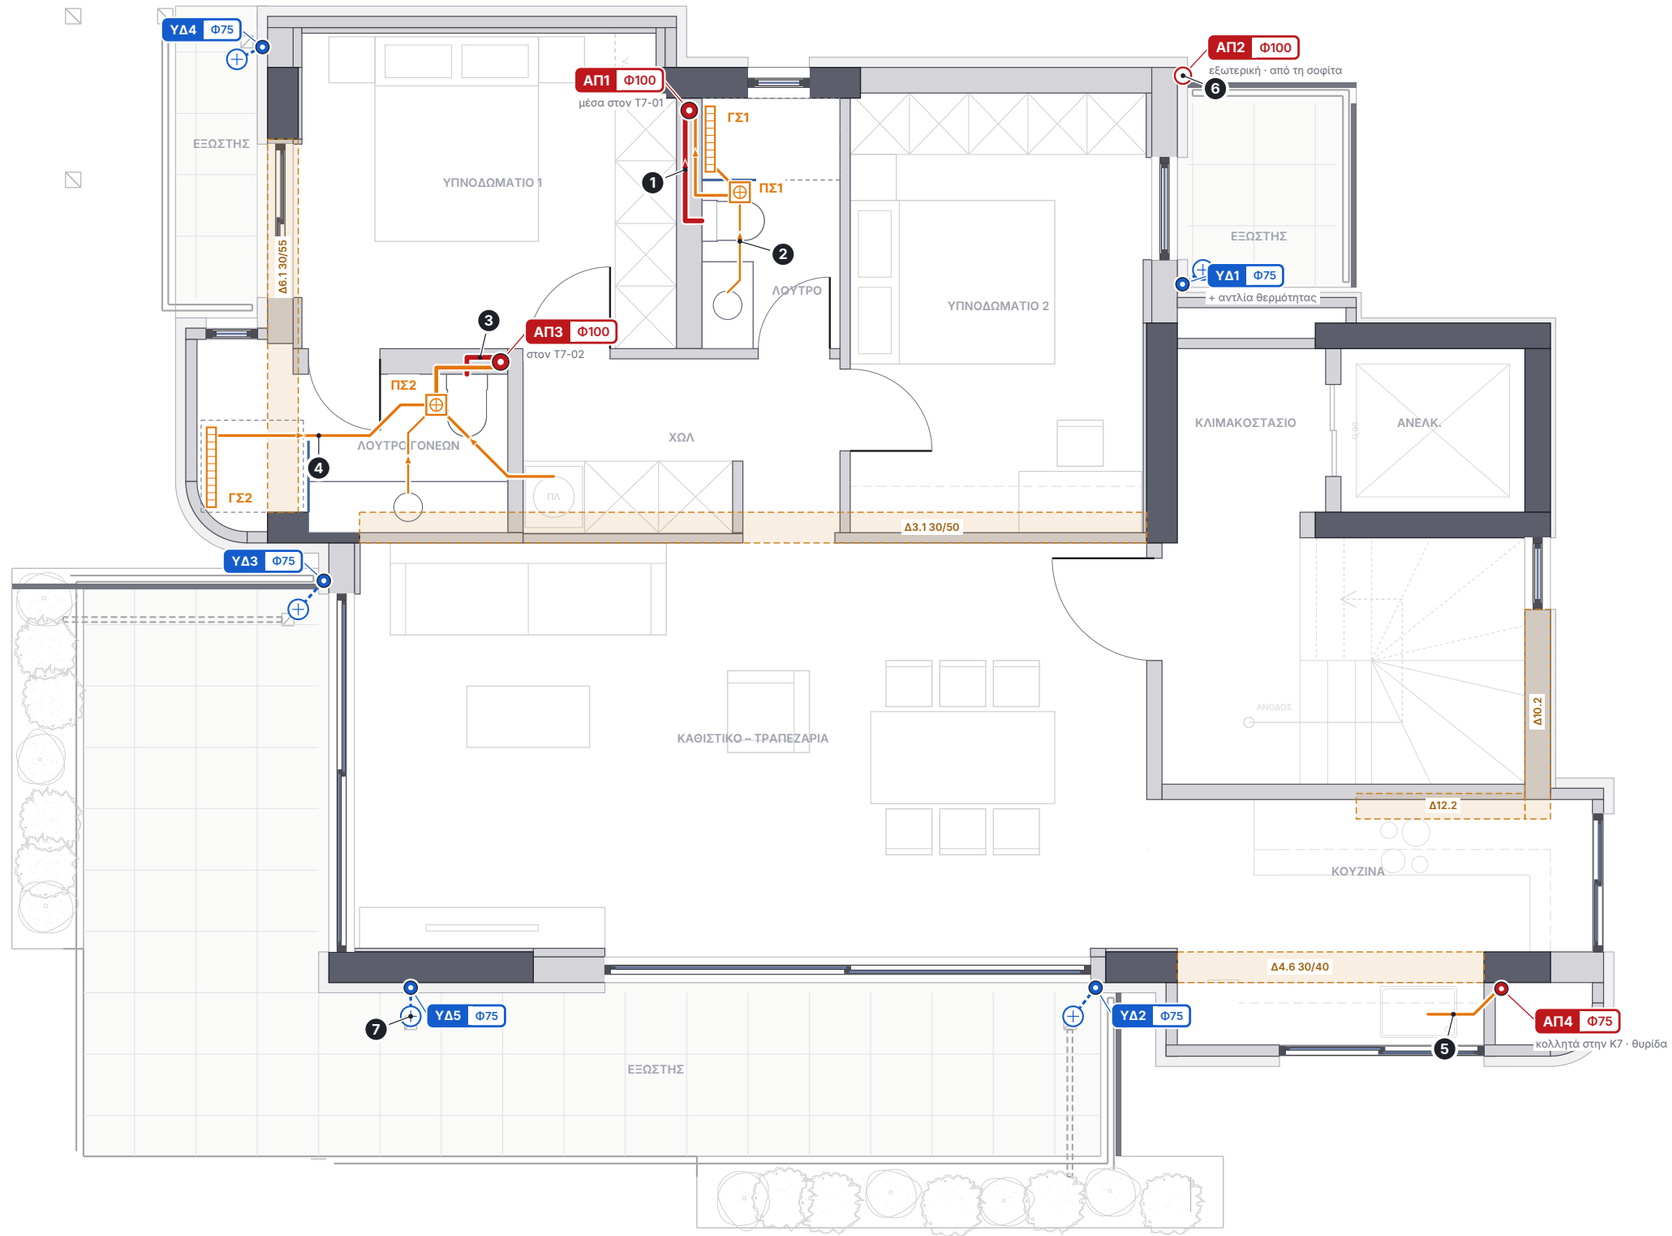

ΥΠΟΜΝΗΜΑ

- Λύματα: λεκάνη Φ90 · στήλη / αγωγός Φ100
- Ακάθαρτα: Φ40 νιπτήρας · Φ50 ντους, νεροχύτης, πλυντήριο · Φ75 έξοδος πατοσίφωνου
- Κατακόρυφη στήλη λυμάτων ΑΠ
- Στήλη που περνά / σταματά (χωρίς σύνδεση στον όροφο)
- Πατοσίφωνο ΠΣ (σιφώνι δαπέδου με σχάρα)
- Γραμμικό σιφώνι ντους ΓΣ → πατοσίφωνο
- Υδρορροή ΥΔ Φ75 μέσα στη θερμοπρόσοψη
- Σιφώνι ομβρίων εξώστη, πλευρική έξοδος
- Δοκός (ξυλότυποι Σ2–Σ7) – ΚΑΜΙΑ οπή


ΣΗΜΕΙΩΣΕΙΣ

1. **Λουτρό → ΑΠ1:** λεκάνη κρεμαστή, Φ90 μέσα στον τοίχο λεκάνης Τ7-01 (+0,22).
2. **Γραμμικό ΓΣ1 → πατοσίφωνο ΠΣ1** (Φ50). Νιπτήρας Φ40 → ΠΣ1. ΠΣ1 → ΑΠ1 Φ50 μέσα στον Τ7-01 (+ συμπυκνώματα Α/C).
3. **Λουτρό γονέων → ΑΠ3:** λεκάνη Φ90 δεξιά, μέσα στον Τ7-02.
4. **Γραμμικό ΓΣ2 → πατοσίφωνο ΠΣ2** (Φ50, 2,2 m). Νιπτήρας Φ40 και πλυντήριο Φ50 (μέσα από τον Τ2Α-01) → ΠΣ2. ΠΣ2 → ΑΠ3 Φ75.
5. **Κουζίνα:** νεροχύτης Φ50 στο δάπεδο → μέσα από τον Τ4-09 → ΑΠ4 Φ75 κολλητά στη νότια παρειά της Κ7 (θυρίδα).
6. **ΑΠ2 Φ100 εξωτερική** στη θερμοπρόσοψη: περνά χωρίς σύνδεση (παίρνει λουτρό + WC σοφίτας).
7. **Υδρορροές ΥΔ1–ΥΔ5 Φ75** μέσα στη θερμοπρόσοψη (αναμονή Ø125 στην πλάκα). Σιφώνια εξωστών με πλευρική έξοδο.

ΕΡΓΟ **ΠΕΝΤΑΟΡΟΦΟ ΚΤΗΡΙΟ ΚΑΤΟΙΚΙΩΝ – ΑΡΓΥΡΟΥΠΟΛΗ** Κωνσταντινουπόλεως 12 & Αγ. Βαρβάρας · Ο.Τ. 103-15 Εργοδότης: INTERKAT Α.Ε. · Κατασκευή: ARKAD Ι.Κ.Ε.	ΘΕΜΑ ΣΧΕΔΙΟΥ **Α΄·Β΄·Γ΄ ΟΡΟΦΟΣ – ΑΠΟΧΕΤΕΥΣΗ** R16 · λύματα · ακάθαρτα · αερισμοί · όμβρια Τυπικός όροφος (Β1) · λεπτομέρειες στο ΑΠ-07	ΒΑΣΗ Σ4 / Σ5 · τοιχοποιίες τυπικού R25	ΑΡ. ΣΧΕΔΙΟΥ **ΑΠ-03** **Κλίμακα 1:60 · Α3** 10/11/2026 · R16

ΚΑΤΟΨΗ Δ΄ ΟΡΟΦΟΥ – ΑΠΟΧΕΤΕΥΣΗ & ΥΔΡΟΡΡΟΕΣ

Κλίμακα 1:60

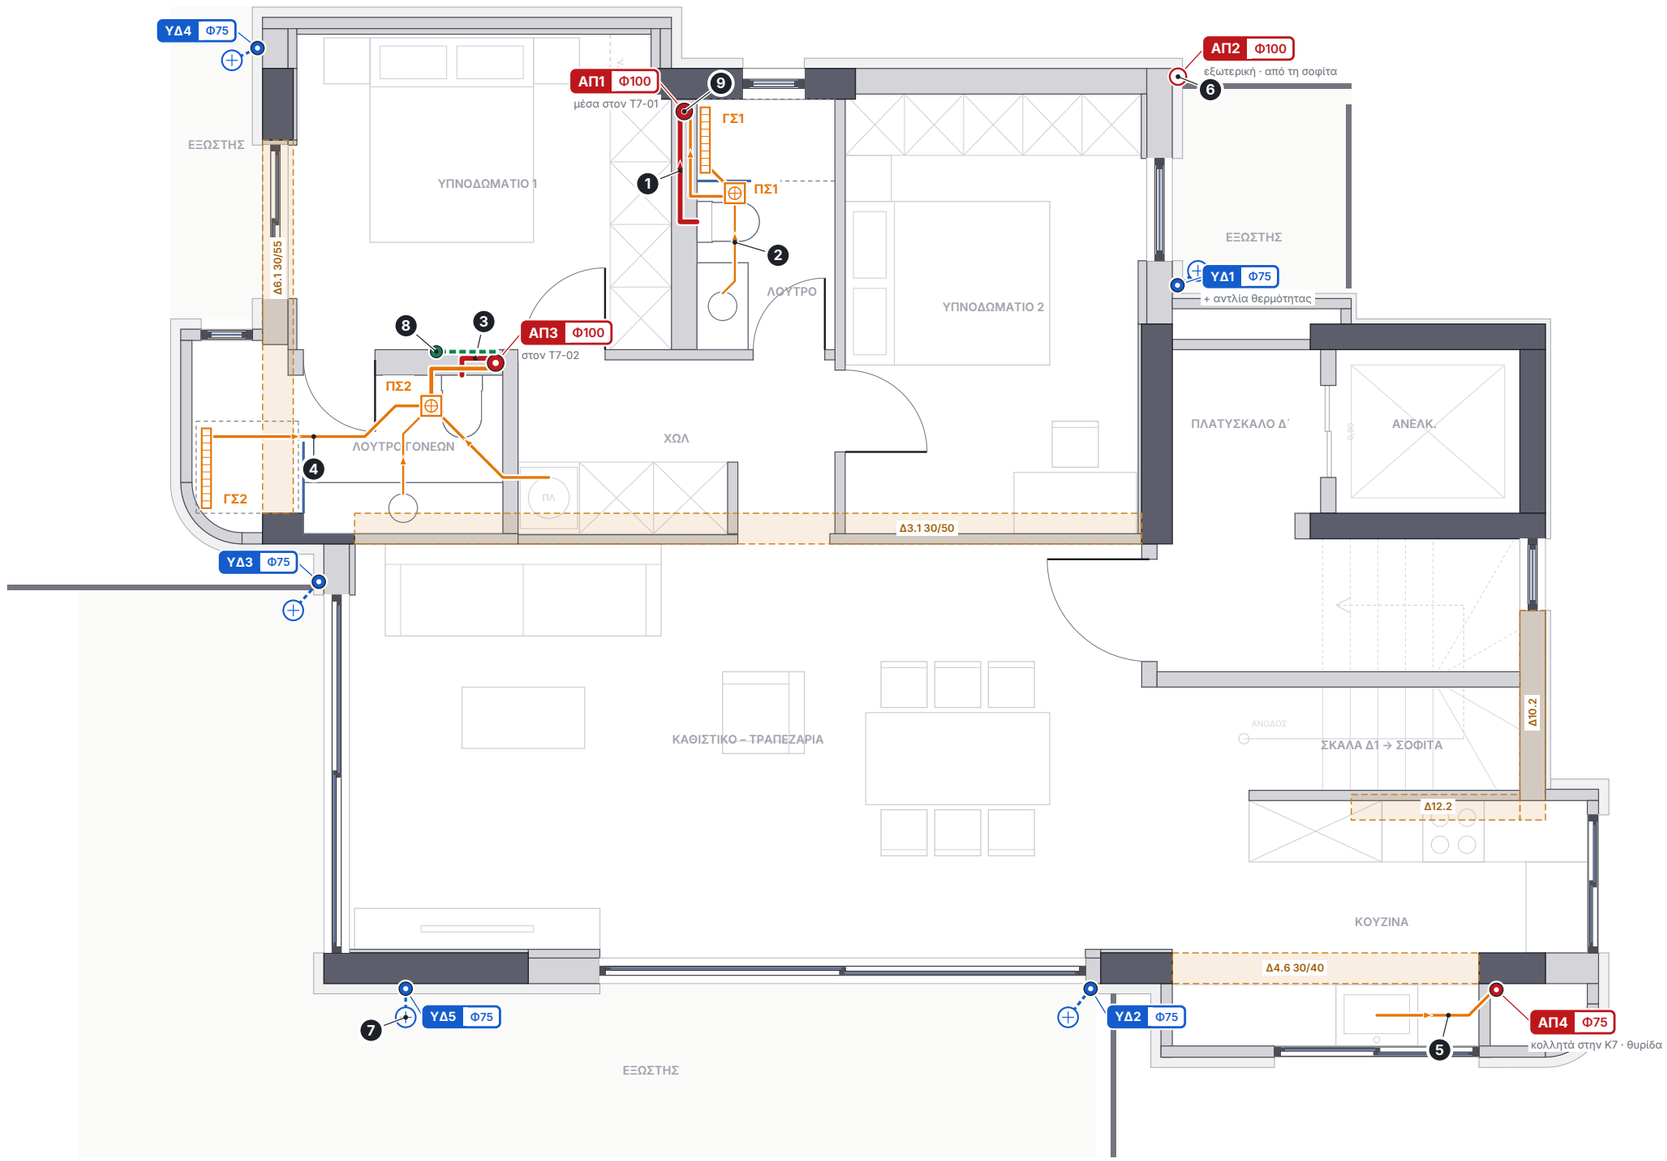

0 1 2 5 m

B

ΥΠΟΜΝΗΜΑ

- Λύματα: λεκάνη Φ90 · στήλη / αγωγός Φ100
- Ακάθαρτα: Φ40 νιπτήρας · Φ50 ντους, νεροχύτης, πλυντήριο · Φ75 έξοδος πατοσίφωνου
- Κατακόρυφη στήλη λυμάτων ΑΠ
- Στήλη που περνά / σταματά (χωρίς σύνδεση στον όροφο)
- Πατοσίφωνο ΠΣ (σιφώνι δαπέδου με σχάρα)
- Γραμμικό σιφώνι ντους ΓΣ → πατοσίφωνο
- Υδρορροή ΥΔ Φ75 μέσα στη θερμοπρόσοψη
- Σιφώνι ομβρίων εξώστη, πλευρική έξοδος
- Δοκός (ξυλότυποι Σ2–Σ7) – ΚΑΜΙΑ οπή
- Αερισμός ΚΑ Φ75 (βγαίνει έξω και ανεβαίνει στη θερμοπρόσοψη)


ΣΗΜΕΙΩΣΕΙΣ

1. **Λουτρό → ΑΠ1:** λεκάνη κρεμαστή, Φ90 μέσα στον τοίχο λεκάνης Τ7-01 (+0,22).
2. **Γραμμικό ΓΣ1 → πατοσίφωνο ΠΣ1** (Φ50). Νιπτήρας Φ40 → ΠΣ1. ΠΣ1 → ΑΠ1 Φ50 μέσα στον Τ7-01 (+ συμπυκνώματα Α/C).
3. **Λουτρό γονέων → ΑΠ3:** λεκάνη Φ90 δεξιά, μέσα στον Τ7-02.
4. **Γραμμικό ΓΣ2 → πατοσίφωνο ΠΣ2** (Φ50, 2,2 m). Νιπτήρας Φ40 και πλυντήριο Φ50 (μέσα από τον Τ2Α-01) → ΠΣ2. ΠΣ2 → ΑΠ3 Φ75.
5. **Κουζίνα:** νεροχύτης Φ50 στο δάπεδο → μέσα από τον Τ4-09 → ΑΠ4 Φ75 κολλητά στη νότια παρειά της Κ7 (θυρίδα).
6. **ΑΠ2 Φ100 εξωτερική** στη θερμοπρόσοψη: περνά χωρίς σύνδεση (παίρνει λουτρό + WC σοφίτας).
7. **Υδρορροές ΥΔ1–ΥΔ5 Φ75** μέσα στη θερμοπρόσοψη (αναμονή Ø125 στην πλάκα). Σιφώνια εξωστών με πλευρική έξοδο.
8. **ΚΑ3:** ο αερισμός της ΑΠ3 φεύγει 0,6 m στην οροφή του Δ΄ (μέσα στον Τ7-02) ως τον δυτικό τοίχο της σοφίτας και ανεβαίνει στη θερμοπρόσοψη.
9. **ΑΠ1:** τελευταία σύνδεση. Ο αερισμός ΚΑ1 συνεχίζει στο γέμισμα του δαπέδου της σοφίτας (ΑΠ-05).

ΕΡΓΟ	ΘΕΜΑ ΣΧΕΔΙΟΥ	ΒΑΣΗ	ΑΡ. ΣΧΕΔΙΟΥ
ΠΕΝΤΑΟΡΟΦΟ ΚΤΗΡΙΟ ΚΑΤΟΙΚΙΩΝ – ΑΡΓΥΡΟΥΠΟΛΗ Κωνσταντινουπόλεως 12 & Αγ. Βαρβάρας · Ο.Τ. 103-15 Εργοδότης: INTERKAT Α.Ε. · Κατασκευή: ARKAD Ι.Κ.Ε.	**Δ΄ ΟΡΟΦΟΣ – ΑΠΟΧΕΤΕΥΣΗ** R16 · λύματα · ακάθαρτα · αερισμοί · όμβρια Δ1 κάτω επίπεδο · λουτρά όπως ο τυπικός (ΑΠ-07)	Σ7 · τοιχοποιίες Δ΄ R04	**ΑΠ-04** **Κλίμακα 1:60 · Α3** 10/11/2026 · R16

ΚΑΤΟΨΗ ΣΟΦΙΤΑΣ – ΑΠΟΧΕΤΕΥΣΗ & ΑΕΡΙΣΜΟΙ

Κλίμακα 1:60

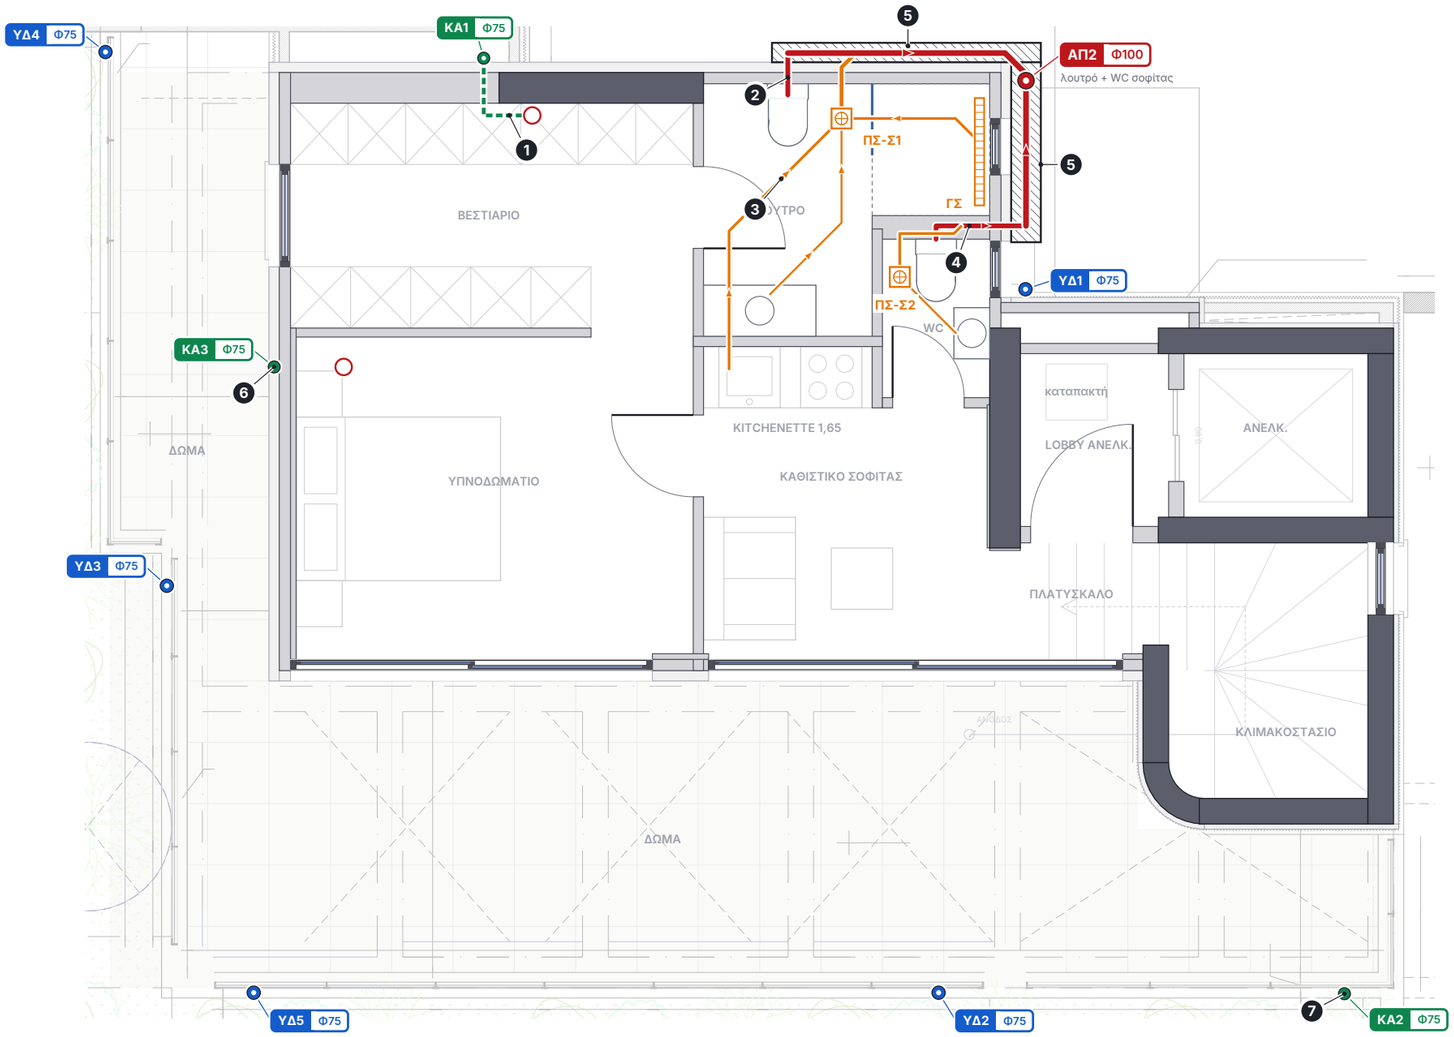

ΥΠΟΜΝΗΜΑ

- Λύματα: λεκάνη Φ90 · στήλη / αγωγός Φ100
- Ακάθαρτα: Φ40 νιπτήρας · Φ50 ντους, νεροχύτης, πλυντήριο · Φ75 έξοδος πατοσίφωνου
- Αερισμός ΚΑ Φ75 (βγαίνει έξω και ανεβαίνει στη θερμοπρόσοψη)
- Κατακόρυφη στήλη λυμάτων ΑΠ
- Στήλη που περνά / σταματά (χωρίς σύνδεση στον όροφο)
- Πατοσίφωνο ΠΣ (σιφώνι δαπέδου με σχάρα)
- Γραμμικό σιφώνι ντους ΓΣ → πατοσίφωνο
- Κούτελο (κλειστό κανάλι γύρω από αγωγό)
- Άνοδος αερισμού στη θερμοπρόσοψη
- Υδρορροή ΥΔ Φ75 μέσα στη θερμοπρόσοψη

ΣΗΜΕΙΩΣΕΙΣ

1. **ΑΠ1:** δεν ανεβαίνει στη σοφίτα. Ο αερισμός ΚΑ1 Φ75 φεύγει μέσα στο γέμισμα του δαπέδου, βγαίνει έξω δυτικά του Κ2 και ανεβαίνει στη θερμοπρόσοψη ως τη στέγη.
2. **Λουτρό:** δική του έξοδος από τον βόρειο τοίχο – λεκάνη Φ90 ίσια έξω.
3. **Γραμμικό ντους → πατοσίφωνο ΠΣ-Σ1** (Φ50). Νιπτήρας Φ40 και KITCHENETTE Φ50 (2,8 m μέσα στο γέμισμα) επίσης στο ΠΣ-Σ1. ΠΣ-Σ1 → έξω Φ75.
4. **WC:** δική του έξοδος από τον ανατολικό τοίχο – λεκάνη Φ90 μέσα στον Τ7Α-02. Νιπτήρας Φ40 → ΠΣ-Σ2 → Φ50 στον ίδιο τοίχο.
5. **Εξωτερικοί Φ100 σε ΚΟΥΤΕΛΟ** θερμοπρόσοψης 20×20 στη στάθμη της πλάκας +16,05: βόρεια όψη 2,3 m, ανατολική 1,4 m, κλίση 2 %. Ενώνονται έξω στη ΒΑ γωνία → ΑΠ2 Φ100.
6. **ΚΑ3:** αερισμός της ΑΠ3 στη θερμοπρόσοψη του δυτικού τοίχου.
7. **ΚΑ2:** αερισμός της ΑΠ4 (κολλητά στην Κ7) – 1,3 m στο δώμα ως τον καμπύλο τοίχο του κλιμακοστασίου → στέγη.
8. **Υδρορροές:** ΥΔ2–ΥΔ5 από τα σιφώνια των δωμάτων +16,05 · ΥΔ1 από τη στέγη.


ΓΕΜΙΣΜΑ ΔΑΠΕΔΟΥ ΣΟΦΙΤΑΣ 20 cm

- Πλάκα +16,05 → τελικό δάπεδο +16,25 = 20 cm (κάτοψη Α-10-S και τομή Α-30-ΒΒ της μελέτης εφαρμογής). Το δώμα είναι +16,20.
- Μέσα στα 20 cm χωράνε ο ΚΑ1 Φ75 και η kitchenette Φ50 με 2 % (πτώση 6 cm), κάτω από την ενδοδαπέδια.
- Η kitchenette έχει δικό της σιφώνι· το ΠΣ-Σ1 με ξεβιδωτή σχάρα για καθαρισμό (λίπη).


ΕΡΓΟ	ΘΕΜΑ ΣΧΕΔΙΟΥ	ΒΑΣΗ	ΑΡ. ΣΧΕΔΙΟΥ
ΠΕΝΤΑΟΡΟΦΟ ΚΤΗΡΙΟ ΚΑΤΟΙΚΙΩΝ – ΑΡΓΥΡΟΥΠΟΛΗ Κωνσταντινουπόλεως 12 & Αγ. Βαρβάρας · Ο.Τ. 103-15 Εργοδότης: INTERKAT Α.Ε. · Κατασκευή: ARKAD Ι.Κ.Ε.	**ΣΟΦΙΤΑ – ΑΠΟΧΕΤΕΥΣΗ & ΑΕΡΙΣΜΟΙ** R16 · λύματα · ακάθαρτα · αερισμοί · όμβρια Δ1 πάνω επίπεδο · έξοδοι λουτρού / WC · κούτελα · λεπτομέρεια στο ΑΠ-08	Α-10-S · Α-30-ΒΒ · Σ7 / Σ8 · τοιχοποιίες σοφίτας R04	**ΑΠ-05** **Κλίμακα 1:60 · Α3** 10/11/2026 · R16

ΙΣΟΓΕΙΟ – ΛΕΠΤΟΜΕΡΕΙΕΣ ΥΓΡΩΝ ΧΩΡΩΝ


Κλίμακα 1:25

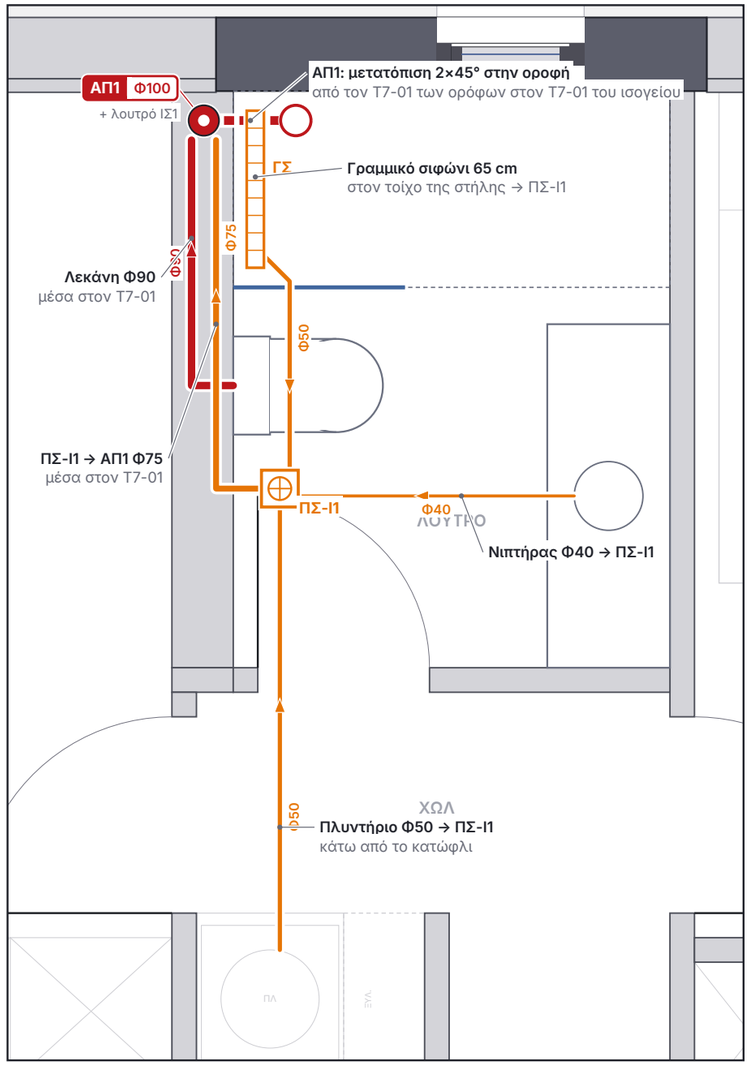

1 **ΛΟΥΤΡΟ ΙΣΟΓΕΙΟΥ → ΑΠ1** Κλίμακα 1:25

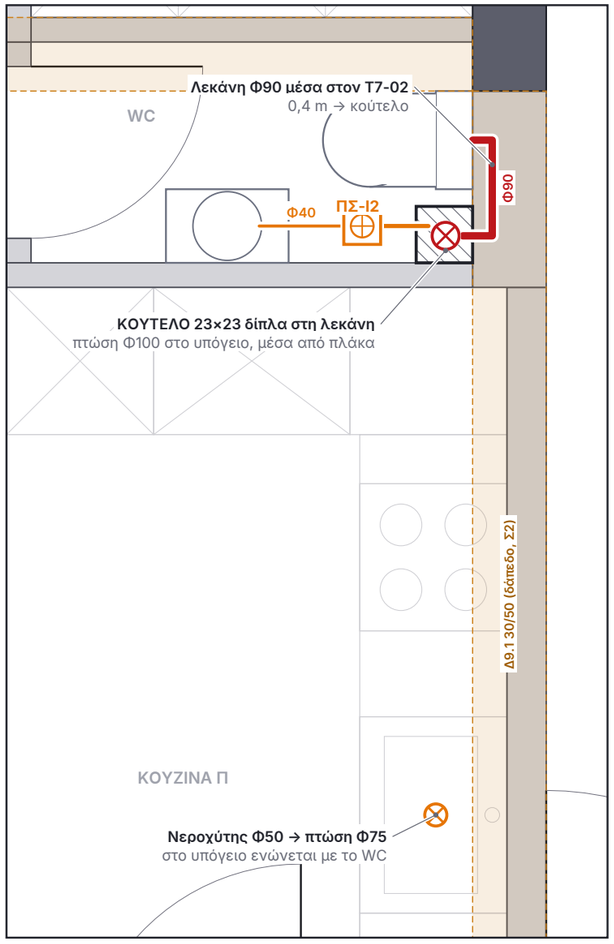

2 **WC + ΚΟΥΖΙΝΑ ΙΣΟΓΕΙΟΥ – ΚΟΥΤΕΛΟ** Κλίμακα 1:25

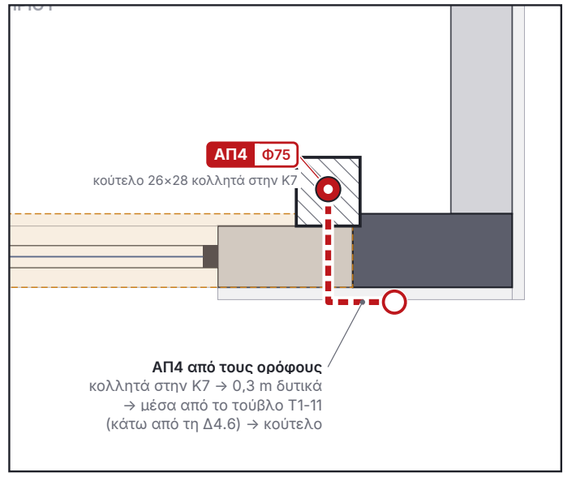

3 **ΑΠ4 ΣΤΗΝ Κ7 – ΚΟΥΤΕΛΟ** Κλίμακα 1:25

ΥΠΟΜΝΗΜΑ

- Λύματα: λεκάνη Φ90 · στήλη / αγωγός Φ100
- Ακάθαρτα: Φ40 νιπτήρας · Φ50 ντους, νεροχύτης, πλυντήριο · Φ75 έξοδος πατοσίφωνου
- Αγωγός στην οροφή του ορόφου (μετατόπιση στήλης 2×45°)
- Κατακόρυφη στήλη λυμάτων ΑΠ
- Στήλη που περνά / σταματά (χωρίς σύνδεση στον όροφο)
- Πτώση στον κάτω όροφο
- Πατοσίφωνο ΠΣ (σιφώνι δαπέδου με σχάρα)
- Γραμμικό σιφώνι ντους ΓΣ → πατοσίφωνο
- Κούτελο (κλειστό κανάλι γύρω από αγωγό)
- Δοκός (ξυλότυποι Σ2–Σ7) – ΚΑΜΙΑ οπή

ΓΕΝΙΚΑ


- Κλίσεις: Φ40–Φ50 2 % · Φ75–Φ100 2 % (ελάχιστη 1 %). Όλα τα οριζόντια μέσα στο γέμισμα του δαπέδου ή μέσα στους τοίχους λεκάνης – τίποτα σε οροφή διαμερίσματος εκτός από τις μετατοπίσεις του ισογείου.
- Κάθε γραμμικό σιφώνι ντους αποχετεύει στο πατοσίφωνο του χώρου· στο ίδιο πατοσίφωνο ο νιπτήρας (και πλυντήριο / kitchenette όπου υπάρχει).
- Έξοδος πατοσίφωνου Φ75 όπου μπαίνει πλυντήριο ή kitchenette (ΠΣ2, ΠΣ-Ι1, ΠΣ-Σ1), αλλιώς Φ50.
- ΚΑΜΙΑ οπή σε δοκό. Διελεύσεις πλακών με χιτώνιο + πυροφραγή. Δοκιμή στεγανότητας πριν από το γέμισμα.
- Σωλήνες U-PVC 6 atm (αερισμοί 4 atm) – ηχομονωτικοί στις ΑΠ1 / ΑΠ3 αν εγκριθεί (ΑΠ-10, αρ. 6).

Β


ΕΡΓΟ	ΘΕΜΑ ΣΧΕΔΙΟΥ	ΒΑΣΗ	ΑΡ. ΣΧΕΔΙΟΥ
ΠΕΝΤΑΟΡΟΦΟ ΚΤΗΡΙΟ ΚΑΤΟΙΚΙΩΝ – ΑΡΓΥΡΟΥΠΟΛΗ Κωνσταντινουπόλεως 12 & Αγ. Βαρβάρας · Ο.Τ. 103-15 Εργοδότης: INTERKAT Α.Ε. · Κατασκευή: ARKAD Ι.Κ.Ε.	**ΙΣΟΓΕΙΟ – ΛΕΠΤΟΜΕΡΕΙΕΣ ΥΓΡΩΝ ΧΩΡΩΝ** R16 · λύματα · ακάθαρτα · αερισμοί · όμβρια Λουτρό · WC / κουζίνα · ΑΠ4 στην Κ7	ΑΠ-02 · τοιχοποιίες ισογείου R13	**ΑΠ-06** **Κλίμακα 1:25 · Α3** 10/11/2026 · R16

Α΄ · Β΄ · Γ΄ · Δ΄ ΟΡΟΦΟΣ – ΛΕΠΤΟΜΕΡΕΙΕΣ ΥΓΡΩΝ ΧΩΡΩΝ


Κλίμακα 1:25

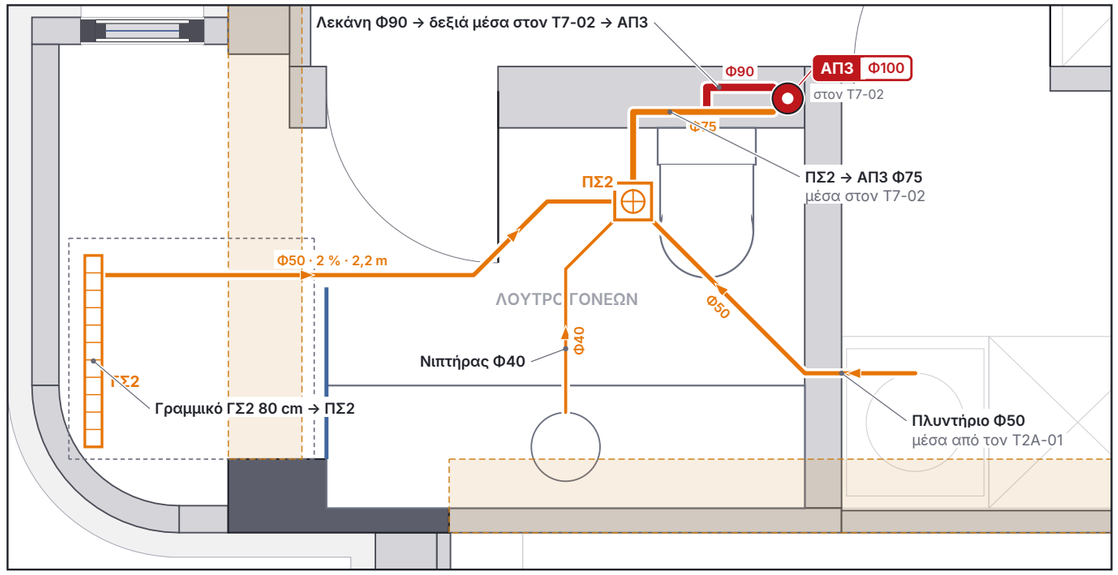

1 **ΛΟΥΤΡΟ ΓΟΝΕΩΝ → ΑΠ3** Κλίμακα 1:25

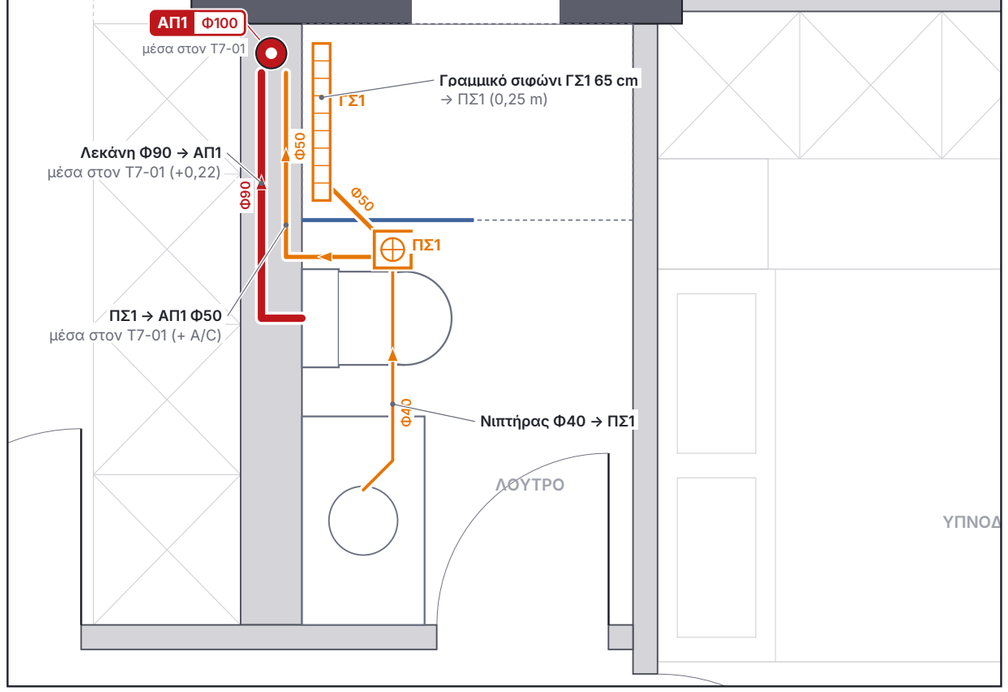

2 **ΛΟΥΤΡΟ → ΑΠ1** Κλίμακα 1:25

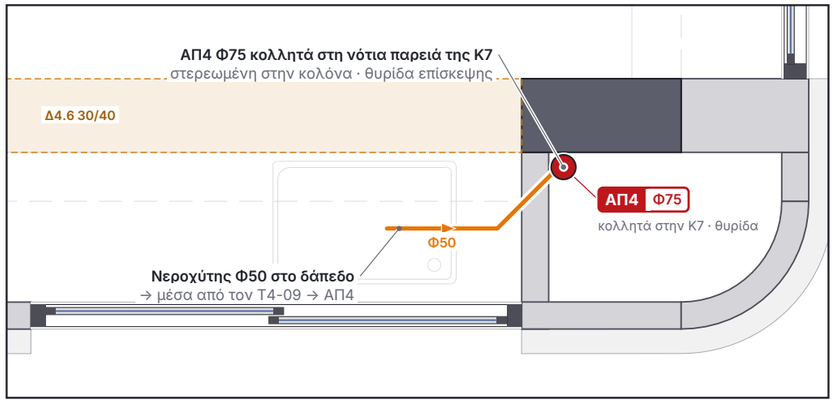

3 **ΚΟΥΖΙΝΑ → ΑΠ4 ΚΟΛΛΗΤΑ ΣΤΗΝ Κ7** Κλίμακα 1:25

ΥΠΟΜΝΗΜΑ

- Λύματα: λεκάνη Φ90 · στήλη / αγωγός Φ100
- Ακάθαρτα: Φ40 νιπτήρας · Φ50 ντους, νεροχύτης, πλυντήριο · Φ75 έξοδος πατοσίφωνου
- Κατακόρυφη στήλη λυμάτων ΑΠ
- Στήλη που περνά / σταματά (χωρίς σύνδεση στον όροφο)
- Πατοσίφωνο ΠΣ (σιφώνι δαπέδου με σχάρα)
- Γραμμικό σιφώνι ντους ΓΣ → πατοσίφωνο
- Υδρορροή ΥΔ Φ75 μέσα στη θερμοπρόσοψη
- Σιφώνι ομβρίων εξώστη, πλευρική έξοδος
- Δοκός (ξυλότυποι Σ2–Σ7) – ΚΑΜΙΑ οπή

ΓΕΝΙΚΑ


- Κλίσεις: Φ40–Φ50 2 % · Φ75–Φ100 2 % (ελάχιστη 1 %). Όλα τα οριζόντια μέσα στο γέμισμα του δαπέδου ή μέσα στους τοίχους λεκάνης – τίποτα σε οροφή διαμερίσματος εκτός από τις μετατοπίσεις του ισογείου.
- Κάθε γραμμικό σιφώνι ντους αποχετεύει στο πατοσίφωνο του χώρου· στο ίδιο πατοσίφωνο ο νιπτήρας (και πλυντήριο / kitchenette όπου υπάρχει).
- Έξοδος πατοσίφωνου Φ75 όπου μπαίνει πλυντήριο ή kitchenette (ΠΣ2, ΠΣ-Ι1, ΠΣ-Σ1), αλλιώς Φ50.
- ΚΑΜΙΑ οπή σε δοκό. Διελεύσεις πλακών με χιτώνιο + πυροφραγή. Δοκιμή στεγανότητας πριν από το γέμισμα.
- Σωλήνες U-PVC 6 atm (αερισμοί 4 atm) – ηχομονωτικοί στις ΑΠ1 / ΑΠ3 αν εγκριθεί (ΑΠ-10, αρ. 6).

B

ΕΡΓΟ	ΘΕΜΑ ΣΧΕΔΙΟΥ	ΒΑΣΗ	ΑΡ. ΣΧΕΔΙΟΥ
ΠΕΝΤΑΟΡΟΦΟ ΚΤΗΡΙΟ ΚΑΤΟΙΚΙΩΝ – ΑΡΓΥΡΟΥΠΟΛΗ Κωνσταντινουπόλεως 12 & Αγ. Βαρβάρας · Ο.Τ. 103-15 Εργοδότης: INTERKAT Α.Ε. · Κατασκευή: ARKAD Ι.Κ.Ε.	**Α΄·Β΄·Γ΄·Δ΄ – ΛΕΠΤΟΜΕΡΕΙΕΣ ΥΓΡΩΝ ΧΩΡΩΝ** R16 · λύματα · ακάθαρτα · αερισμοί · όμβρια Λουτρό γονέων · λουτρό · κουζίνα (ίδια και στον Δ΄)	ΑΠ-03 / ΑΠ-04 · τοιχοποιίες τυπικού R25	**ΑΠ-07** **Κλίμακα 1:25 · Α3** 10/11/2026 · R16

ΣΟΦΙΤΑ – ΛΕΠΤΟΜΕΡΕΙΑ ΥΓΡΩΝ ΧΩΡΩΝ

Κλίμακα 1:20

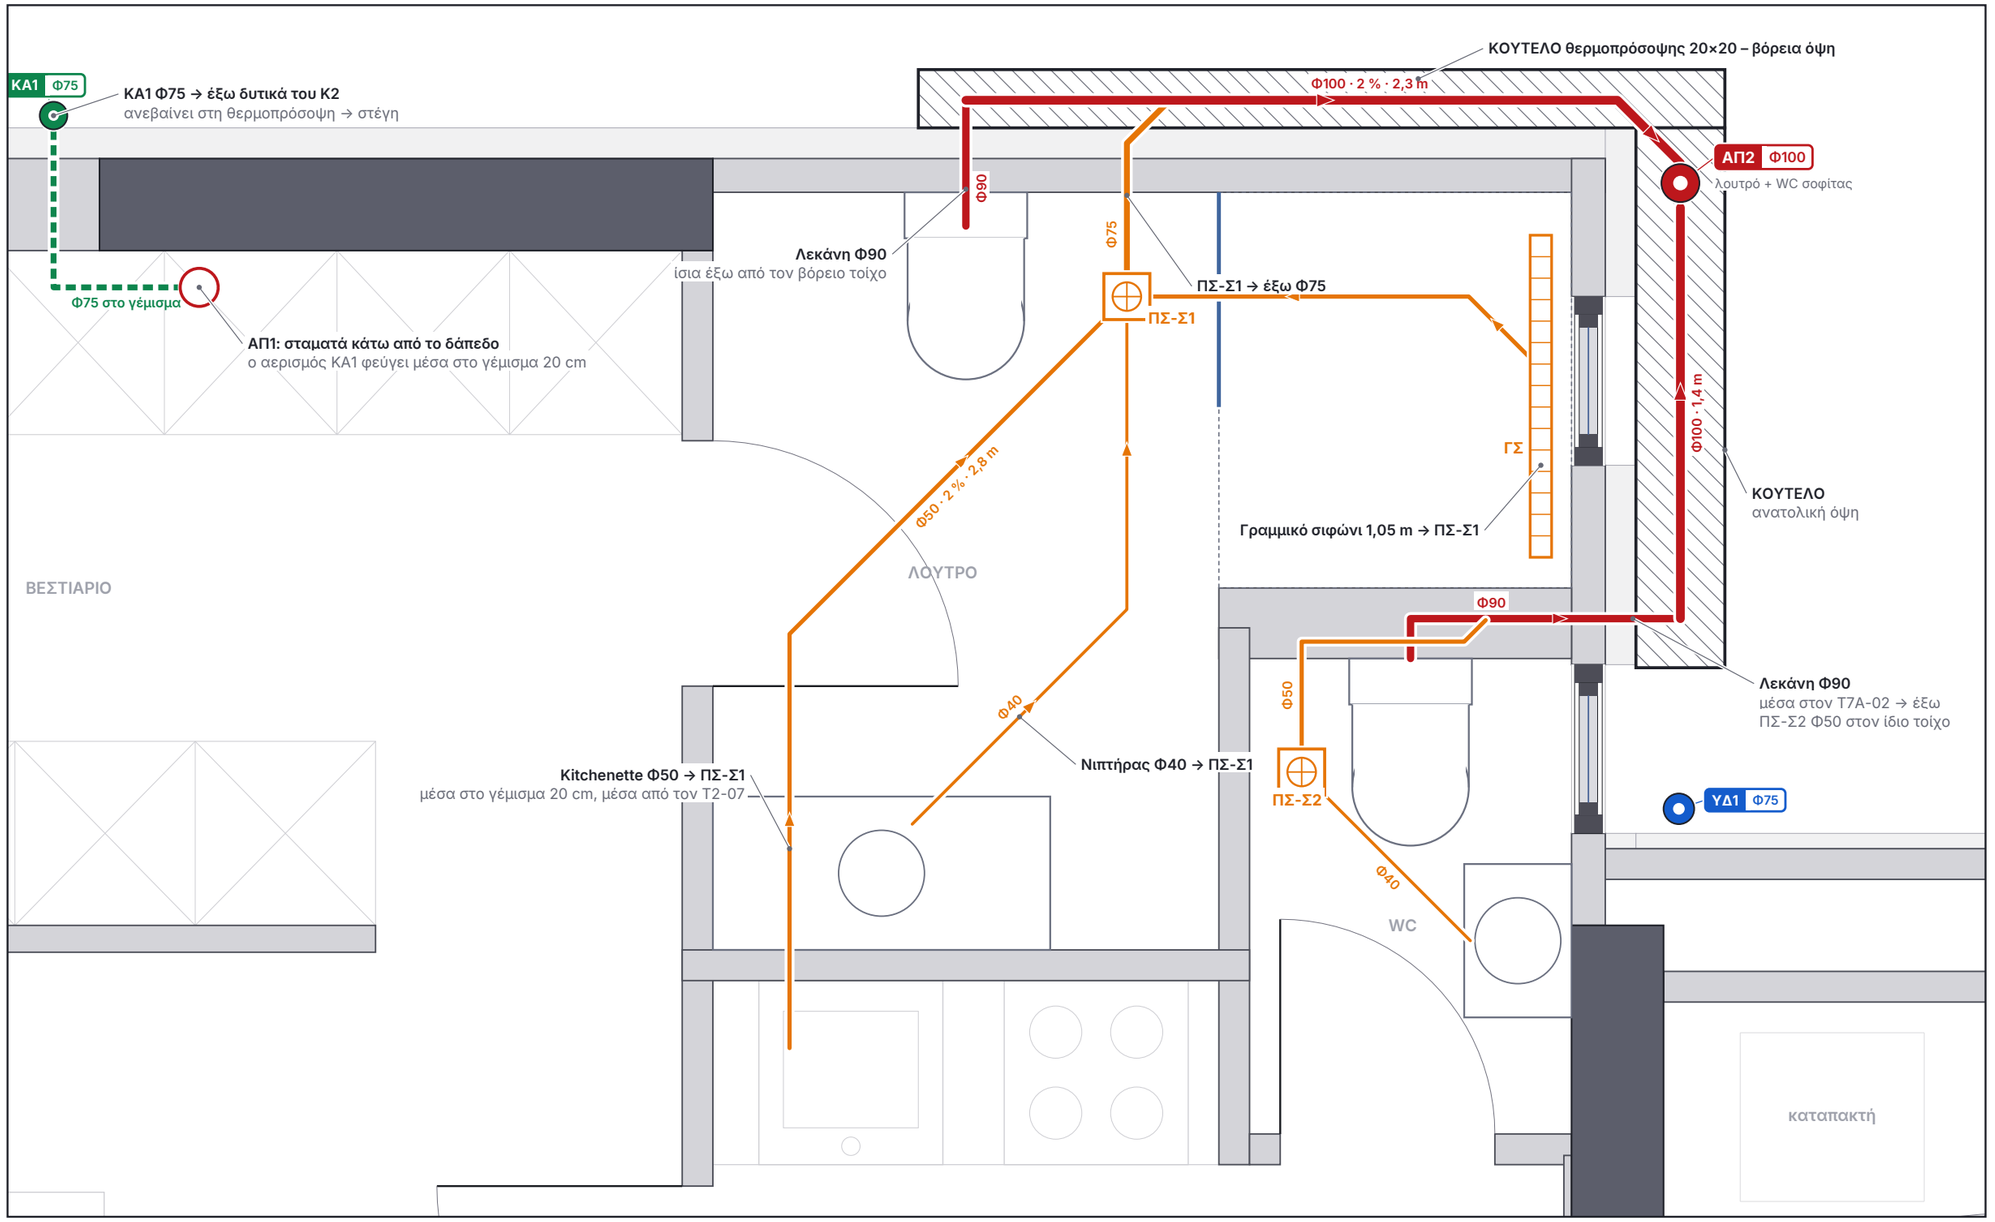

1 **ΛΟΥΤΡΟ · WC · ΚΙΤCHENETTE ΣΟΦΙΤΑΣ – ΕΞΟΔΟΙ & ΚΟΥΤΕΛΑ → ΑΠ2** Κλίμακα 1:20

ΥΠΟΜΝΗΜΑ

- Λύματα: λεκάνη Φ90 · στήλη / αγωγός Φ100
- Ακάθαρτα: Φ40 νιπτήρας · Φ50 ντους, νεροχύτης, πλυντήριο · Φ75 έξοδος πατοσίφωνου
- Αερισμός ΚΑ Φ75 (βγαίνει έξω και ανεβαίνει στη θερμοπρόσοψη)
- Κατακόρυφη στήλη λυμάτων ΑΠ
- Στήλη που περνά / σταματά (χωρίς σύνδεση στον όροφο)
- Πατοσίφωνο ΠΣ (σιφώνι δαπέδου με σχάρα)
- Γραμμικό σιφώνι ντους ΓΣ → πατοσίφωνο
- Κούτελο (κλειστό κανάλι γύρω από αγωγό)
- Άνοδος αερισμού στη θερμοπρόσοψη

ΓΕΝΙΚΑ

- Κλίσεις: Φ40–Φ50 2 % · Φ75–Φ100 2 % (ελάχιστη 1 %). Όλα τα οριζόντια μέσα στο γέμισμα του δαπέδου ή μέσα στους τοίχους λεκάνης – τίποτα σε οροφή διαμερίσματος εκτός από τις μετατοπίσεις του ισογείου.
- Κάθε γραμμικό σιφώνι ντους αποχετεύει στο πατοσίφωνο του χώρου· στο ίδιο πατοσίφωνο ο νιπτήρας (και πλυντήριο / kitchenette όπου υπάρχει).
- Έξοδος πατοσίφωνου Φ75 όπου μπαίνει πλυντήριο ή kitchenette (ΠΣ2, ΠΣ-Ι1, ΠΣ-Σ1), αλλιώς Φ50.
- ΚΑΜΙΑ οπή σε δοκό. Διελεύσεις πλακών με χιτώνιο + πυροφραγή. Δοκιμή στεγανότητας πριν από το γέμισμα.
- Σωλήνες U-PVC 6 atm (αερισμοί 4 atm) – ηχομονωτικοί στις ΑΠ1 / ΑΠ3 αν εγκριθεί (ΑΠ-10, αρ. 6).

ΓΕΜΙΣΜΑ ΔΑΠΕΔΟΥ ΣΟΦΙΤΑΣ 20 cm


- Πλάκα +16,05 → τελικό δάπεδο +16,25 = 20 cm (κάτοψη Α-10-S και τομή Α-30-ΒΒ της μελέτης εφαρμογής). Το δώμα είναι +16,20.
- Μέσα στα 20 cm χωράνε ο ΚΑ1 Φ75 και η kitchenette Φ50 με 2 % (πτώση 6 cm), κάτω από την ενδοδαπέδια.
- Η kitchenette έχει δικό της σιφώνι· το ΠΣ-Σ1 με ξεβιδωτή σχάρα για καθαρισμό (λίπη).

B

ΕΡΓΟ	ΘΕΜΑ ΣΧΕΔΙΟΥ	ΒΑΣΗ	ΑΡ. ΣΧΕΔΙΟΥ
ΠΕΝΤΑΟΡΟΦΟ ΚΤΗΡΙΟ ΚΑΤΟΙΚΙΩΝ – ΑΡΓΥΡΟΥΠΟΛΗ Κωνσταντινουπόλεως 12 & Αγ. Βαρβάρας · Ο.Τ. 103-15 Εργοδότης: INTERKAT Α.Ε. · Κατασκευή: ARKAD Ι.Κ.Ε.	**ΣΟΦΙΤΑ – ΛΕΠΤΟΜΕΡΕΙΑ ΥΓΡΩΝ ΧΩΡΩΝ** R16 · λύματα · ακάθαρτα · αερισμοί · όμβρια Λουτρό · WC · kitchenette · εξωτερικοί Φ100 σε κούτελο	ΑΠ-05 · Α-10-S · Α-30-ΒΒ · τοιχοποιίες σοφίτας R04	**ΑΠ-08** **Κλίμακα 1:20 · Α3** 10/11/2026 · R16

ΚΑΤΑΚΟΡΥΦΟ ΔΙΑΓΡΑΜΜΑ ΑΠΟΧΕΤΕΥΣΗΣ & ΟΜΒΡΙΩΝ

Χωρίς κλίμακα

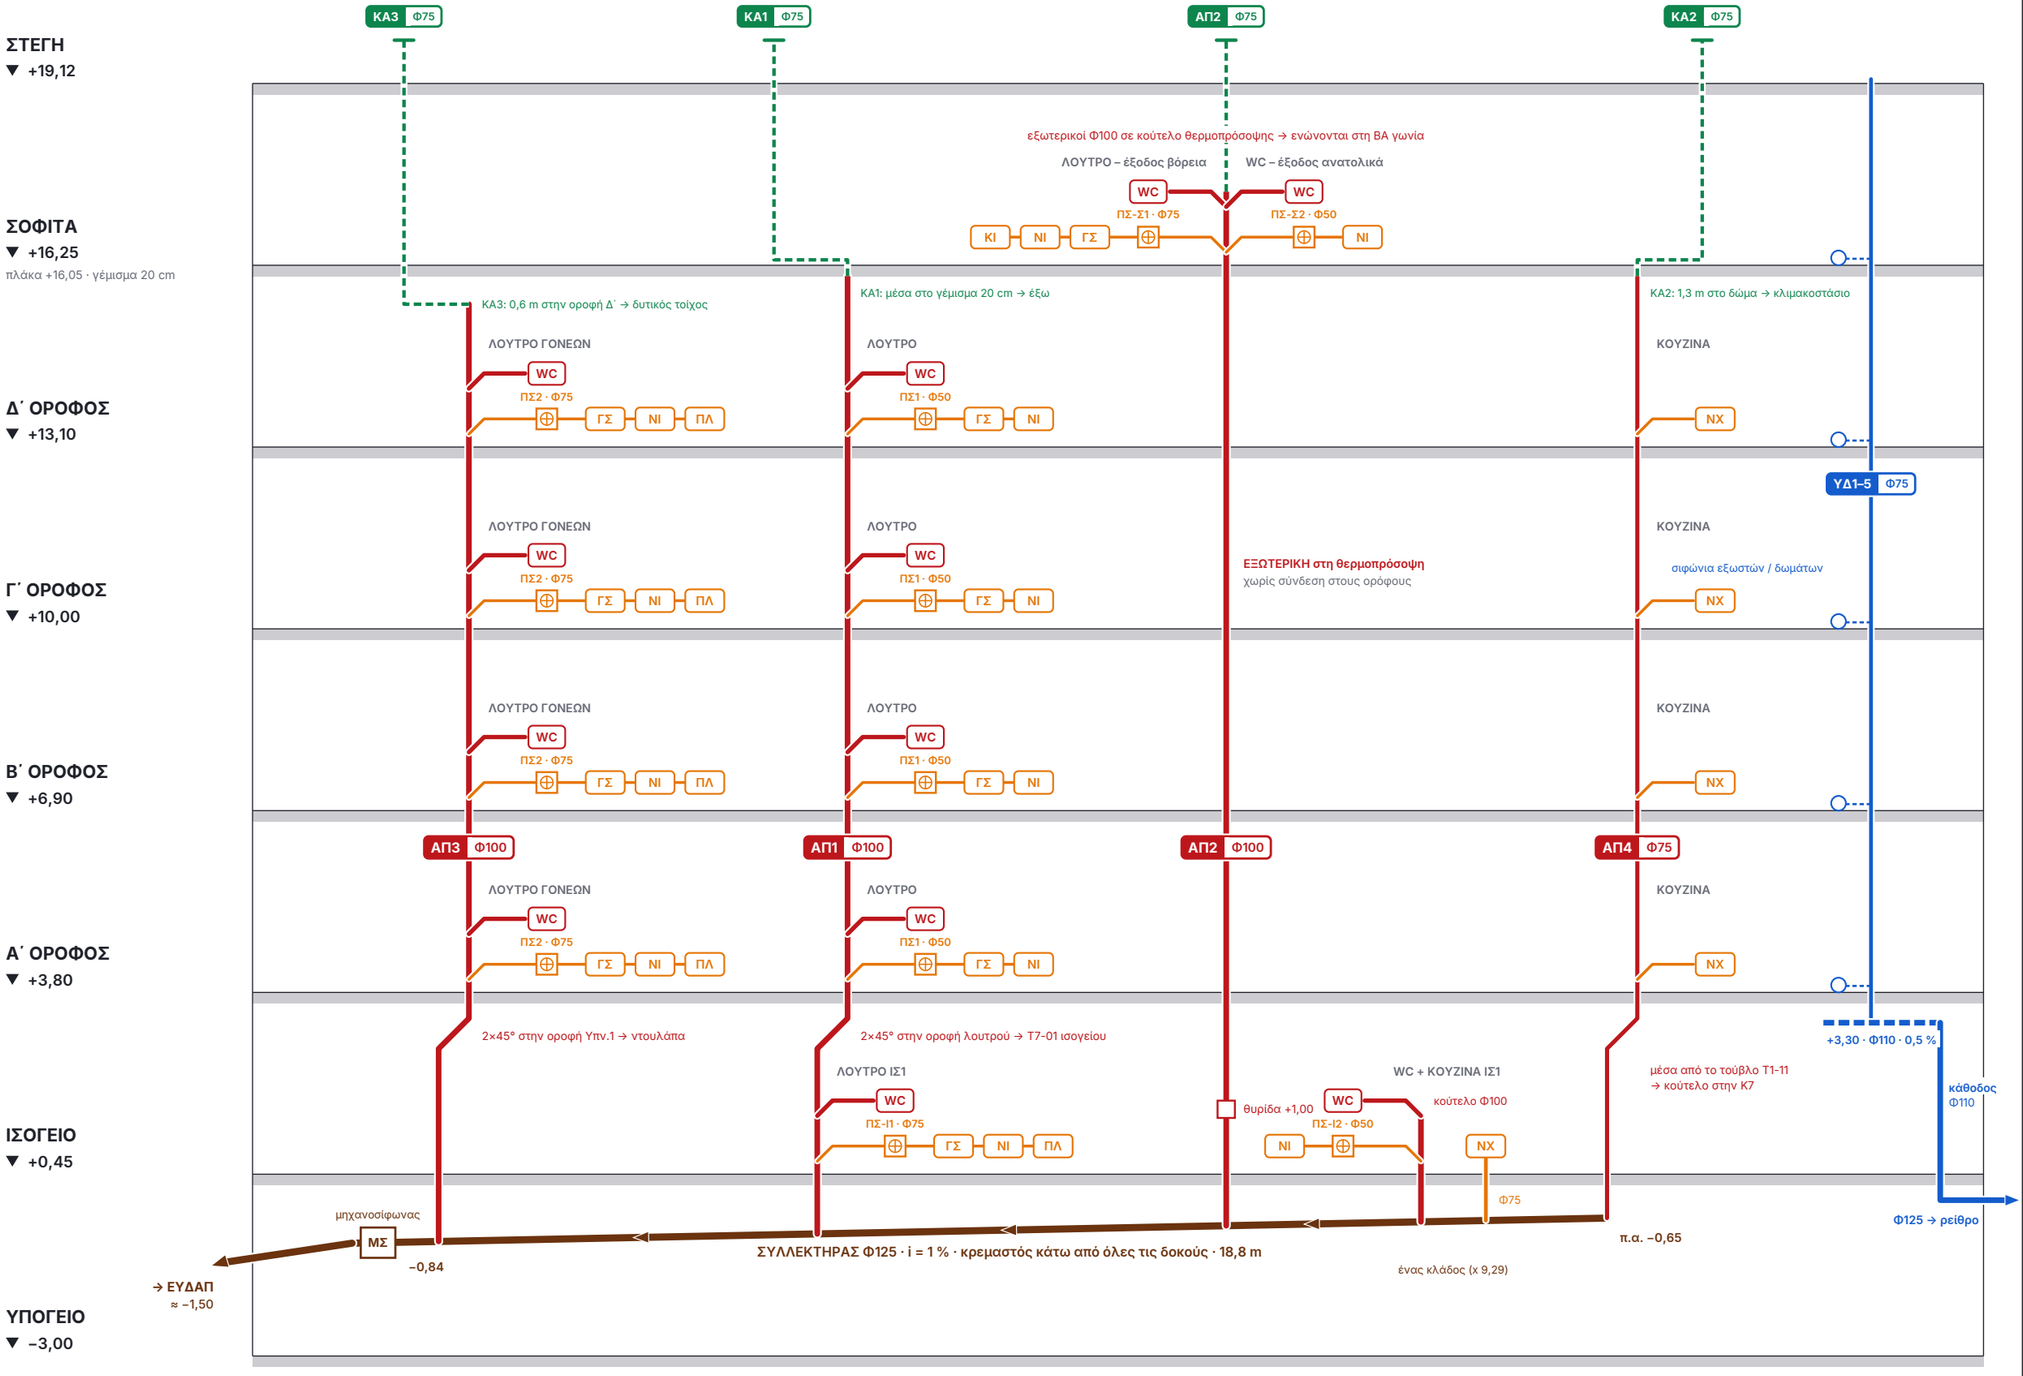

ΥΠΟΜΝΗΜΑ

- Λύματα: λεκάνη Φ90 · στήλη / αγωγός Φ100
- Ακάθαρτα: Φ40 νιπτήρας · Φ50 ντους, νεροχύτης, πλυντήριο · Φ75 έξοδος πατοσίφωνου
- Αερισμός ΚΑ Φ75 (βγαίνει έξω και ανεβαίνει στη θερμοπρόσοψη)
- Όμβρια: συλλεκτήρας / αγωγός
- Συλλεκτήρας ομβρίων ΨΗΛΑ +3,30 (οροφή προβόλων Α΄)
- Συλλεκτήρας / κλάδοι υπογείου, κρεμαστοί κάτω από τις δοκούς
- Πατοσίφωνο ΠΣ (σιφώνι δαπέδου με σχάρα)

ΣΥΝΤΟΜΟΓΡΑΦΙΕΣ

- **WC** λεκάνη κρεμαστή – Φ90 μέσα στον τοίχο λεκάνης
- **ΓΣ** γραμμικό σιφώνι ντους – Φ50 → πατοσίφωνο
- **ΝΙ** νιπτήρας – Φ40 → πατοσίφωνο
- **ΠΛ** πλυντήριο ρούχων – Φ50 → πατοσίφωνο
- **ΚΙ** kitchenette σοφίτας – Φ50 → πατοσίφωνο ΠΣ-Σ1
- **ΝΧ** νεροχύτης κουζίνας (+ πλυντήριο πιάτων) – Φ50
- **ΠΣ** πατοσίφωνο · δίπλα η διατομή εξόδου
- **ΚΑ** αερισμός στήλης Φ75 ως πάνω από τη στέγη

ΣΗΜΕΙΩΣΕΙΣ

- Στάθμες τελικού δαπέδου. Σοφίτα: πλάκα +16,05, γέμισμα 20 cm (A-10-S, A-30-ΒΒ).
- ΑΠ1 / ΑΠ3 Φ100 εσωτερικές μέσα στους τοίχους λεκάνης · ΑΠ2 Φ100 εξωτερική · ΑΠ4 Φ75 κολλητά στην Κ7.
- Ισόγειο: ΑΠ1 / ΑΠ3 με μετατόπιση 2×45° στην οροφή · ΑΠ4 μέσα από το τούβλο Τ1-11 στο κούτελο · WC και κουζίνα ΙΣ1 με δικές τους πτώσεις.
- Όλοι οι αερισμοί βγαίνουν έξω και καταλήγουν πάνω από τη στέγη – κανένας σε οροφή χώρου.
- Συλλεκτήρας υπογείου κάτω από όλες τις δοκούς – καμία οπή σε δοκό.

B

ΕΡΓΟ	ΘΕΜΑ ΣΧΕΔΙΟΥ	ΒΑΣΗ	ΑΡ. ΣΧΕΔΙΟΥ
ΠΕΝΤΑΟΡΟΦΟ ΚΤΗΡΙΟ ΚΑΤΟΙΚΙΩΝ – ΑΡΓΥΡΟΥΠΟΛΗ Κωνσταντινουπόλεως 12 & Αγ. Βαρβάρας · Ο.Τ. 103-15 Εργοδότης: INTERKAT Α.Ε. · Κατασκευή: ARKAD Ι.Κ.Ε.	**ΚΑΤΑΚΟΡΥΦΟ ΔΙΑΓΡΑΜΜΑ** R16 · λύματα · ακάθαρτα · αερισμοί · όμβρια Στήλες ΑΠ1–ΑΠ4 · αερισμοί · συλλεκτήρας · όμβρια	ΑΠ-01 … ΑΠ-05	**ΑΠ-09** **Χωρίς κλίμακα · Α3** 10/11/2026 · R16

ΑΛΛΑΓΕΣ R15 → R16 (σχόλια Γιάννη 10/11/2026 στο R15)

Στοιχείο	R15	R16	Λόγος / έλεγχος
Γραμμικό ντους ισογείου	Φ50 κατευθείαν στην ΑΠ1	γραμμικό → πατοσίφωνο ΠΣ-Ι1 → ΑΠ1 Φ75 μέσα στον Τ7-01	«τα γραμμικά σιφώνια πάνε στο πατοσίφωνο»
Kitchenette σοφίτας	Φ50 κατευθείαν στην έξοδο του λουτρού	Φ50 μέσα στο γέμισμα (2,8 m, 2 %) → πατοσίφωνο ΠΣ-Σ1 → έξω Φ75	«όπως και η kitchenette στη σοφίτα» · δικό της σιφώνι, ΠΣ-Σ1 με ξεβιδωτή σχάρα
Γέμισμα δαπέδου σοφίτας	15 cm (τελικό +16,20)	20 cm: πλάκα +16,05 → τελικό +16,25	Α-10-S και τομή Α-30-ΒΒ. Η τομή Α-30-ΑΑ / Α-90-01 γράφει ακόμη +16,20 – να το διορθώσει ο αρχιτέκτονας
ΚΑ1 (αερισμός ΑΠ1)	Φ75 ή Φ63; (ανοικτό 10)	Φ75 μέσα στο γέμισμα 20 cm	χωράει κάτω από την ενδοδαπέδια – το ανοικτό 10 κλείνει
Εξωτερικοί Φ100 σοφίτας	πρόταση για κούτελο (ανοικτό 11)	ΚΟΥΤΕΛΑ θερμοπρόσοψης 20×20: βόρεια όψη 2,3 m, ανατολική 1,4 m	«ναι, για τις Φ100 κάνουμε κούτελα»
ΑΠ4	θέση οπής προς επιβεβαίωση (ανοικτό 9)	οριστική: 12,87 / 9,51 κολλητά στην Κ7 · ισόγειο κούτελο 12,60 / 9,05	«η ΑΠ4 όπως την έκανες είναι εντάξει»
Πατοσίφωνα ΠΣ1, ΠΣ2, ΠΣ-Ι2, ΠΣ-Σ2	σχεδιασμένα κάτω από τη λεκάνη	δίπλα στη λεκάνη (μετακίνηση 5–25 cm)	σχεδιαστική διόρθωση: η σχάρα πρέπει να μένει ελεύθερη
Έξοδοι πατοσίφωνων	Φ50–Φ75 χωρίς διάκριση	Φ75 όπου μπαίνει πλυντήριο / kitchenette (ΠΣ2, ΠΣ-Ι1, ΠΣ-Σ1), Φ50 αλλού	3 υποδοχείς στο ίδιο πατοσίφωνο
Σχέδια	6 φύλλα, ένα στιλ για όλα	10 φύλλα: κατόψεις 1:60 με αριθμημένες σημειώσεις, λεπτομέρειες 1:25 / 1:20, κατακόρυφο διάγραμμα	«πιο ωραίο σχέδιο, να φαίνεται πιο επαγγελματικό»

ΑΝΟΙΚΤΑ – απάντησε με τον αριθμό (π.χ. «1 κουτί, 3 ΟΚ, 8 Φ90»)

No	Θέμα	Πρόταση	Ερώτηση
1	ΑΠ3 στο ισόγειο	Αντί για μετατόπιση 1,3 m στην οροφή του Υπν.1, κουτί 20×20 στη θέση 3,08 / 3,38 μέσα στη γωνία ντουλάπας–τοίχου του ισογείου.	Μετατόπιση ή κουτί;
3	Ντους γονέων	Το ΠΣ2 πάει δίπλα στο γυαλί (1,25 / 4,30): γραμμικό → ΠΣ2 0,9 m αντί 2,2 m.	ΟΚ;
4	Κλίση ομβρίων +3,30	31 m με 0,5 % είναι οριακό για φύλλα. Πρόταση 1 % (πτώση 0,31 m) ή δεύτερη κάθοδος στη ΒΔ γωνία.	Ποιο;
5	Ύψος υπογείου	Ο συλλεκτήρας αφήνει 2,16 πάνω από τις Θ.Σ.Υ. 3/4. Πρόταση: ο νότιος κλάδος κολλητά στο δυτικό τοιχείο (x −1,10).	ΟΚ;
6	Ηχομόνωση στηλών	ΑΠ1 και ΑΠ3 περνούν δίπλα σε υπνοδωμάτια: ηχομονωτικός σωλήνας PP τριών στρώσεων αντί U-PVC.	ΟΚ;
7	Υδρορροές στη θερμοπρόσοψη	Φ75 μέσα σε ETICS 10 cm αφήνει 2,5 cm μόνωση: τοπικά ETICS 12 cm ή υδρορροή Φ63.	Ποιο;
8	ΑΠ4 κουζίνες	Φ75 επαρκεί για 4 κουζίνες. Πρόταση Φ90 για τα λίπη, ίδια θέση κολλητά στην Κ7.	Φ75 ή Φ90;

ΕΚΛΕΙΣΑΝ ΣΤΟ R16: 9 (θέση ΑΠ4 – εντάξει) · 10 (ΚΑ1 Φ75 στο γέμισμα 20 cm) · 11 (κούτελα για τους εξωτερικούς Φ100 – ναι). Το 2 είχε κλείσει στο R15.