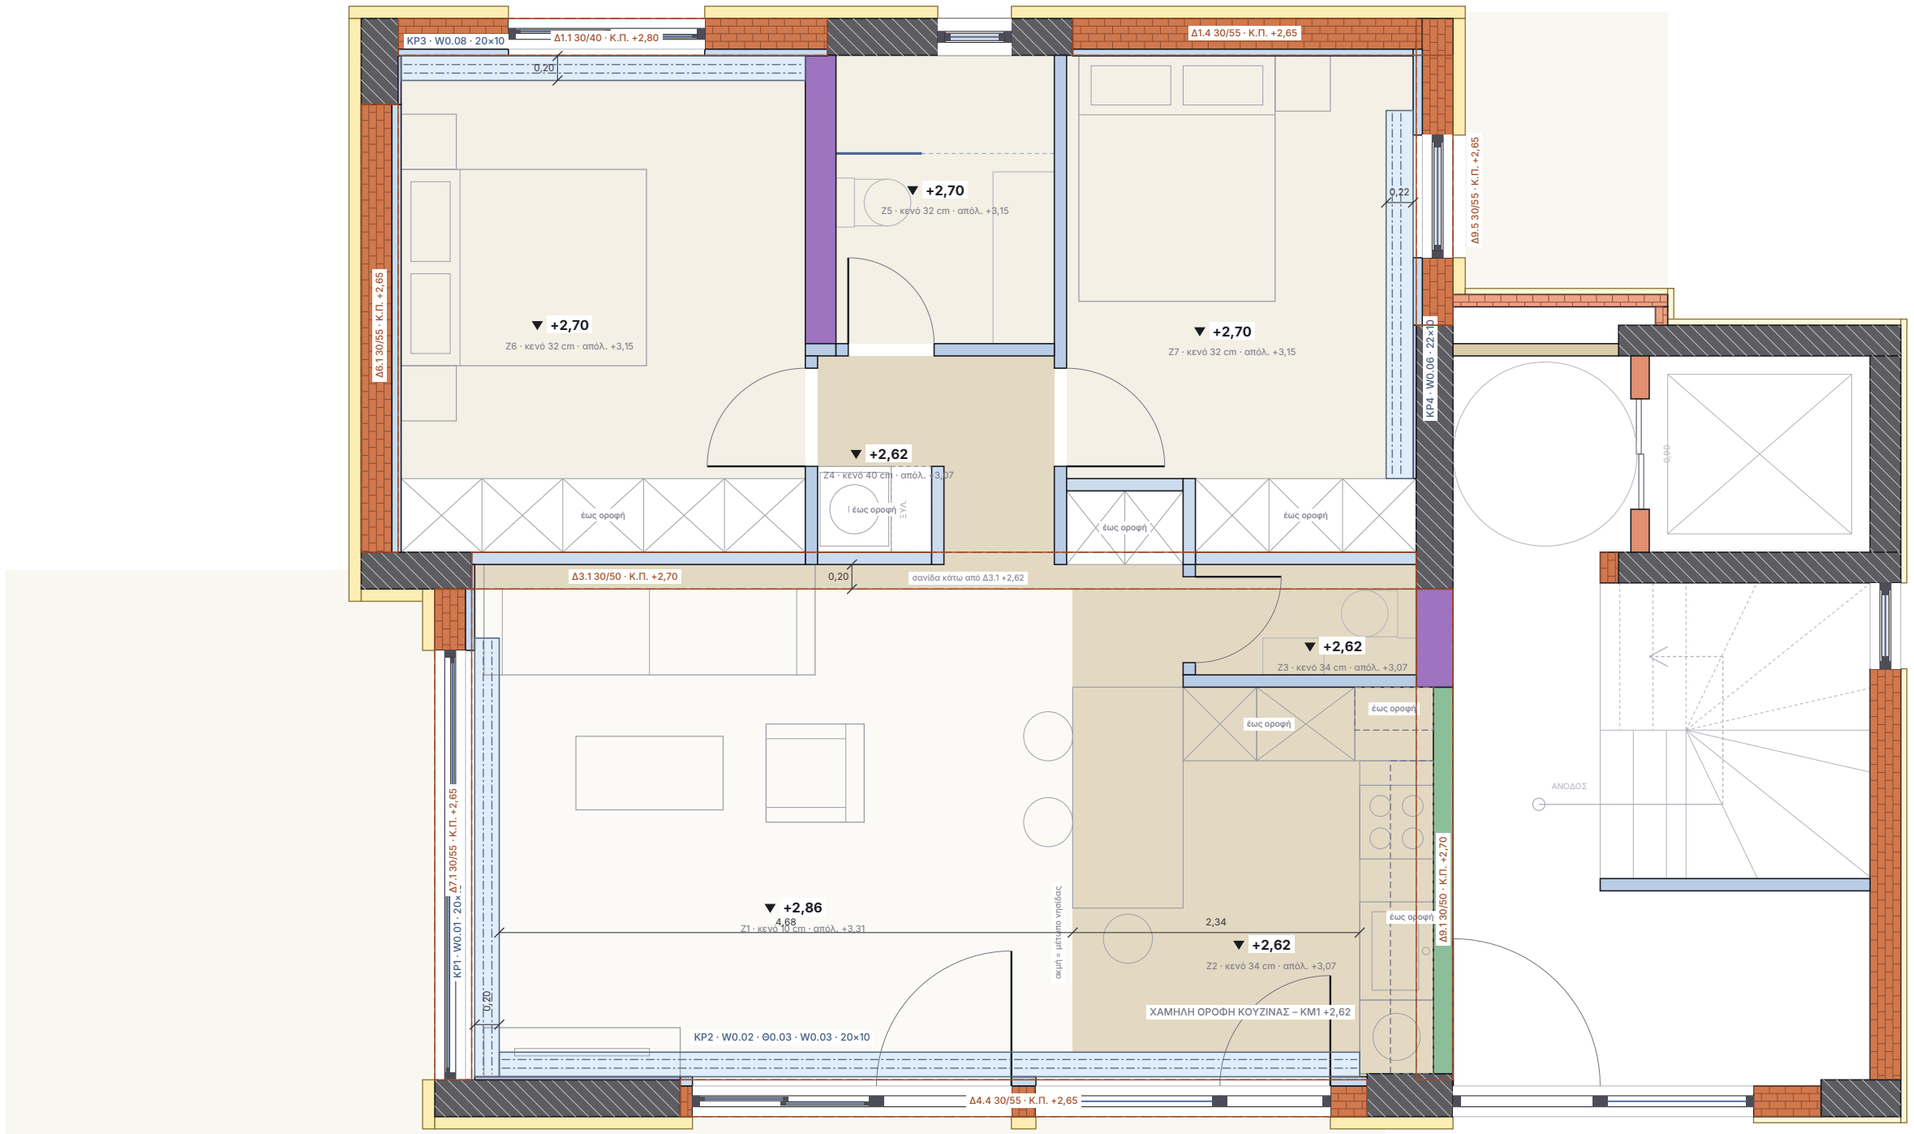


ΣΗΜΕΙΩΣΕΙΣ

Στάθμες από το τελικό δάπεδο του ισογείου – Τ.Δ. θεωρήθηκε +0,45 στο σύστημα του Σ3 (Α1): πάνω παρειά πλάκας +3,20 · κάτω παρειά Π3 h18 +3,02 · Π8 h24 +2,96 · δοκοί 50 +2,70 · 55 +2,65 · 40 +2,80. Σε κάθε στάθμη και η απόλυτη (Σ3).

R02 (ιδιοκτήτης 07/11: «του σαλονιού τη χαμηλή οροφή κάτω από την κουζίνα και το μηχάνημα εκεί»): χαμηλή οροφή +2,62 ΜΟΝΟ πάνω από την κουζίνα (νησίδα, στήλες, πάγκος, προθάλαμος WC), ακμή στο μέτωπο της νησίδας x 6,60 σε όλο το βάθος. Το καθιστικό ελεύθερο +2,86.

Η Δ3.1 προεξέχει 0,20 στο καθιστικό (4,95–5,15) → σανίδα +2,62 ίδια με χωλ / κουζίνα: στο πέρασμα από το χωλ μία μόνο αλλαγή (+2,62 → +2,86) στη γραμμή της δοκού. Λουτρό / υπνοδωμάτια +2,70 περασιά με τη Δ3.1.


Κουρτινόθηκες ΚΡ1–ΚΡ4: 20 × 10 cm (ΚΡ4 22 cm για τη μπαλκονόπορτα W0.06)· η ΚΡ2 συνεχής σε όλο τον νότιο τοίχο (W0.02 · Θ0.03 · W0.03).

Πάνω από το Υπν.1: λουτρό γονέων Α΄ (Α2).

ΥΠΟΜΝΗΜΑ

- +2,86 καθιστικό = 10 cm κάτω από την Π8 h24 (spot σώμα ≤ 75 mm)
- +2,70 περασιά με δοκό 50: υπνοδωμάτια · λουτρό (κενό 32 cm)
- +2,62 χαμηλή οροφή κουζίνας (ΚΜ1) · σανίδα Δ3.1 · χωλ · WC (8 cm κάτω από τις δοκούς 50)
- ΚΡ εσοχή κουρτίνας ανοιχτή ως την πλάκα · 2 οδηγοί
- δοκός (Σ3) · Κ.Π. = κάτω παρειά από Τ.Δ.

ΕΡΓΟ	ΘΕΜΑ ΣΧΕΔΙΟΥ	ΒΑΣΗ	ΑΡ. ΣΧΕΔΙΟΥ
ΠΕΝΤΑΟΡΟΦΟ ΚΤΗΡΙΟ ΚΑΤΟΙΚΙΩΝ – ΑΡΓΥΡΟΥΠΟΛΗ Κωνσταντινουπόλεως 12 & Αγ. Βαρβάρας · Ο.Τ. 103-15 Εργοδότης: INTERKAT Α.Ε. · Κατασκευή: ARKAD Ι.Κ.Ε.	**ΑΝΟΨΗ – ΣΤΑΘΜΕΣ · ΔΟΚΟΙ · ΚΟΥΡΤΙΝΕΣ** Στάθμες ψευδοροφής · χαμηλή οροφή κουζίνας · δοκοί Σ3 · κουρτίνες ΙΣΟΓΕΙΟ – ΙΣ1 (Τ.Δ. θεωρήθηκε +0,45 στο σύστημα του Σ3)	Βάση: τοιχοποιίες ισογείου R13 · ξυλότυπος Σ3 (+3,65) · ανόψη Β1 R13	**ΑΝ-01** **Κλίμακα 1:50 · Α3** 07/11/2026 · R02

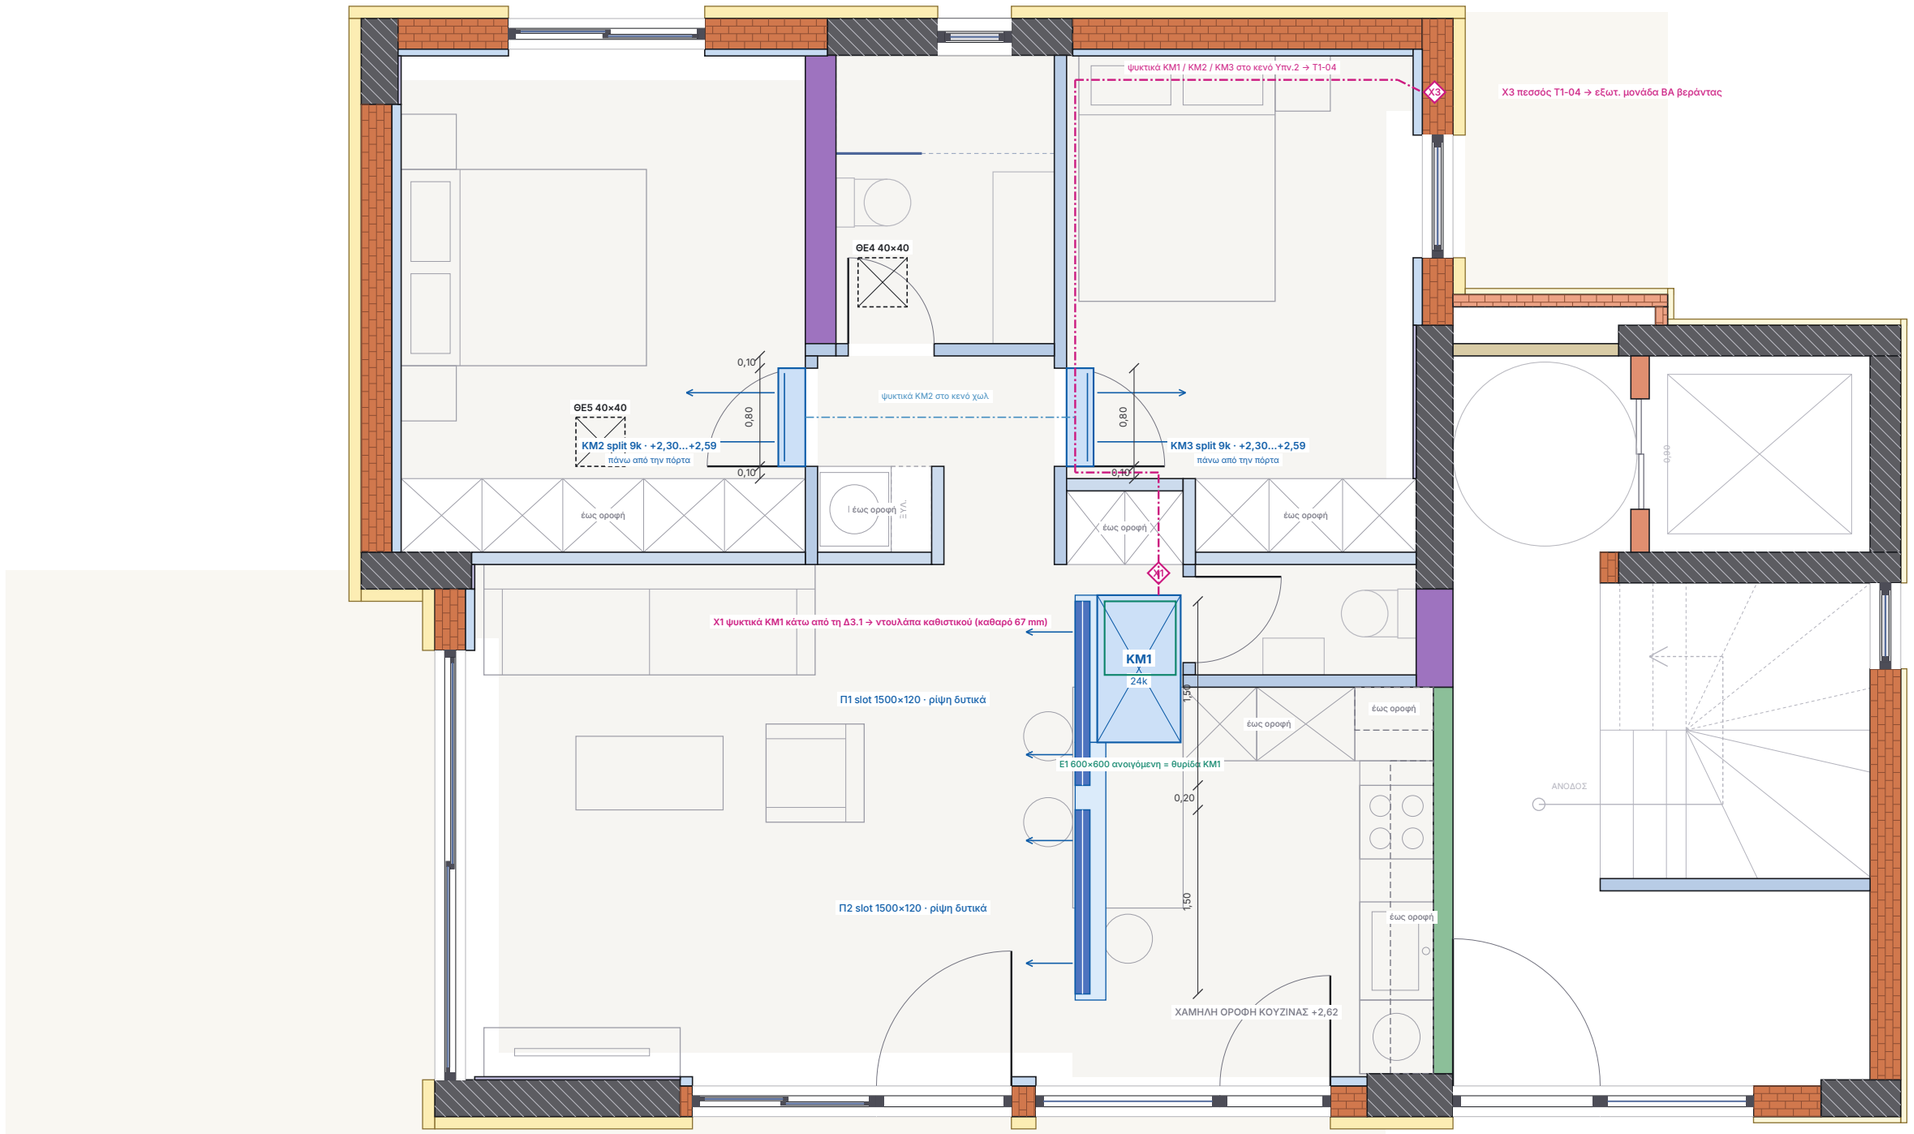

ΣΗΜΕΙΩΣΕΙΣ

R02 – ΚΜ1 ΣΤΗ ΧΑΜΗΛΗ ΟΡΟΦΗ ΤΗΣ ΚΟΥΖΙΝΑΣ (ιδιοκτήτης 07/11): ζώνη +2,62 κάτω από την Π8 +2,96 = 34 cm → ΚΜ1 245 + 10 + 40 = 295 → περιθώριο 45 mm. Η μονάδα πάνω από τον προθάλαμο WC / το βόρειο άκρο της νησίδας (όχι πάνω από εστίες ή στήλες)· Ε1 600×600 με φίλτρο ανοιγόμενη = θυρίδα.

Προσαγωγή: κιβώτιο-plenum στο δυτικό πλάι της μονάδας + κανάλι 250×200 κατά μήκος της ακμής → Π1 / Π2 slot 1,50 στην ακμή x 6,60 με ρίψη ΔΥΤΙΚΑ σε όλο το καθιστικό (4,7 m)· ρυθμίστε τις σχισμές οριζόντια (Coanda) ώστε ο αέρας να μην πέφτει στις θέσεις της νησίδας.

Ψυκτικά ΚΜ1: βόρεια κάτω από τη Δ3.1 μέσα από το επάνω μέρος της ντουλάπας καθιστικού (καθαρό 2,70 – 2,62 – 12,5 = 67 mm → χωράει και μόνωση 13 mm) → Τ2Ν-05 → κενό Υπν.2 → Τ1-04 → εξωτερική μονάδα στη ΒΑ βεράντα. Καμία οπή σε δοκό.

R02 – ΥΠΝΟΔΩΜΑΤΙΑ ΜΕ SPLIT (ιδιοκτήτης: «στα δωμάτια δεν θα βάζουμε καναλάτο, θα βάζουμε split σε ένα σημείο που θα βρεις»): ΚΜ2 / ΚΜ3 9k ψηλά ΠΑΝΩ ΑΠΟ ΤΗΝ ΠΟΡΤΑ κάθε δωματίου (τοίχος χωλ, +2,30…+2,59 – 11 cm από την οροφή +2,70, 5 cm πάνω από την κάσα 2,25).

Γιατί εκεί: ο αέρας ρίχνεται κατά μήκος του δωματίου ΔΙΓΩΝΑ από το κρεβάτι (Υπν.1 κεφαλάρι δυτικά → ρίψη δυτικά 0,42 νότια του κρεβατιού · Υπν.2 κεφαλάρι βόρεια → ρίψη ανατολικά 0,95 νότια από τα πόδια) – όχι στο πρόσωπο· τα ψυκτικά μπαίνουν κατευθείαν στο κενό χωλ / Υπν.2 όπου ήδη περνά η ΚΜ1· τα συμπυκνώματα κατεβαίνουν με φυσική ροή μέσα στον γυψότοιχο στη στήλη Τ7-01 / στο σιφώνι του λουτρού.

Στήριξη split σε γυψότοιχο: ενίσχυση (OSB 18 ή UA) στο υπέρθυρο.

ΥΠΟΜΝΗΜΑ

- ΚΜ1 καναλάτη μονάδα (slim ≤ 245 mm)
- ΚΜ2 / ΚΜ3 split τοίχου (σώμα στον τοίχο, βέλη = ρίψη)
- αεραγωγός / plenum προσαγωγής (μονωμένος, στο κενό)
- Π1 / Π2 γραμμικό slot οροφής 2 σχισμών στην ακμή της χαμήλωσης κουζίνας
- Ε στόμιο / κιβώτιο επιστροφής με φίλτρο
- ΘΕ θυρίδα επίσκεψης (αφανής, βαφόμενη)
- Χ κατέβασμα / έξοδος σωληνώσεων – καμία οπή σε σκυρόδεμα

ΕΡΓΟ	ΘΕΜΑ ΣΧΕΔΙΟΥ	ΒΑΣΗ	ΑΡ. ΣΧΕΔΙΟΥ
ΠΕΝΤΑΟΡΟΦΟ ΚΤΗΡΙΟ ΚΑΤΟΙΚΙΩΝ – ΑΡΓΥΡΟΥΠΟΛΗ Κωνσταντινουπόλεως 12 & Αγ. Βαρβάρας · Ο.Τ. 103-15 Εργοδότης: INTERKAT Α.Ε. · Κατασκευή: ARKAD Ι.Κ.Ε.	**ΑΝΟΨΗ – ΚΛΙΜΑΤΙΣΜΟΣ · ΘΥΡΙΔΕΣ** Καναλάτη ΚΜ1 στη χαμηλή οροφή κουζίνας · split υπνοδωματίων · ψυκτικά ΙΣΟΓΕΙΟ – ΙΣ1 (Τ.Δ. θεωρήθηκε +0,45 στο σύστημα του Σ3)	Βάση: τοιχοποιίες ισογείου R13 · ξυλότυπος Σ3 (+3,65) · ανόψη Β1 R13	**ΑΝ-02** **Κλίμακα 1:50 · Α3** 07/11/2026 · R02

B



ΣΗΜΕΙΩΣΕΙΣ

Κατανομή: Υπν. 2 × 2 spots · λουτρό 3 (IP65 στο ντους) · WC 1 · χωλ 2 · κουζίνα 2 στον άξονα του διαδρόμου νησίδα – πάγκος + LED4 κάτω από τα επάνω ντουλάπια · καθιστικό ΚΘ1–ΚΘ7. Σύνολο 22 spots + 2 κρεμαστά + LED4.

R02 καθιστικό (ιδιοκτήτης: «το κρεμαστό σε λάθος θέση – σκέψου και σπορτ»): ΚΡΕΜ0 στο ΚΕΝΤΡΟ του τραπεζιού σαλονιού (3,15 · 6,65 – ήταν 3,60 · 7,70, ανάμεσα σε τραπεζάκι και TV)· ΚΡΕΜ1 στο κέντρο της νησίδας (7,05 · 6,85), πίσω από τα slot (ρίψη δυτικά – δεν κουνιέται).

Spots καθιστικού ΚΘ1–ΚΘ7 (πρόταση, κύκλωμα λ με dimmer): περιμετρικά στις τζαμαρίες W0.01 / W0.02, 0,525 από τις κουρτινόθηκες, ανά 1,20 – φωτίζουν κουρτίνες, τοίχο TV και την είσοδο Θ0.03 (το ΚΘ7 στη χαμηλή οροφή της κουζίνας).

Πυρανίχνευση (προδ. 4): καθιστικό, Υπν.1, Υπν.2, χωλ (άξονας 0,90 – ΑΚ4 1,03 από το split ΚΜ2), κουζίνα θερμοδιαφορικός· ≥ 0,50 από τοίχους / φωτιστικά, ≥ 1,00 από slot / split· λουτρό / WC χωρίς ανιχνευτή καπνού.

Οπή spot Ø 75–80 ανάμεσα στα προφίλ CD (όχι πάνω τους)· όπου πέφτει σε προφίλ, μετατόπιση του προφίλ – όχι του spot.

ΥΠΟΜΝΗΜΑ

- χωνευτό spot LED 7–9 W, 2700 K, CRI ≥ 90, UGR < 19, σώμα ≤ 75 mm
- χωνευτό spot IP44 (λουτρά)
- χωνευτό spot IP65 (πάνω από ντους)
- split τοίχου (για συντονισμό – βλ. φύλλο κλιματισμού)
- ΚΡΕΜ παροχή οροφής (κουτί + ενίσχυση ανάρτησης)
- ΑΚ ανιχνευτής καπνού (ΕΠ104 · EN 54-7)
- ΑΘ θερμοδιαφορικός ανιχνευτής (κουζίνα · EN 54-5)
- ακτίνα 0,50 m γύρω από ανιχνευτή – κανένας τοίχος / φωτιστικό μέσα
- LED4 κρυφό γραμμικό 3000 K κάτω από τα επάνω ντουλάπια κουζίνας

ΕΡΓΟ

ΠΕΝΤΑΟΡΟΦΟ ΚΤΗΡΙΟ ΚΑΤΟΙΚΙΩΝ – ΑΡΓΥΡΟΥΠΟΛΗ
Κωνσταντινουπόλεως 12 & Αγ. Βαρβάρας · Ο.Τ. 103-15
Εργοδότης: INTERKAT Α.Ε. · Κατασκευή: ARKAD Ι.Κ.Ε.

ΘΕΜΑ ΣΧΕΔΙΟΥ

ΑΝΟΨΗ – ΦΩΤΙΣΜΟΣ · ΠΥΡΑΝΙΧΝΕΥΣΗ
Χωνευτά spots · κρεμαστά · LED κουζίνας · ανιχνευτές
ΙΣΟΓΕΙΟ – ΙΣ1 (Τ.Δ. θεωρήθηκε +0,45 στο σύστημα του Σ3)

ΒΑΣΗ

Βάση: τοιχοποιίες ισογείου R13 · ξυλότυπος Σ3 (+3,65) · ανόψη Β1 R13

ΑΡ. ΣΧΕΔΙΟΥ

AN-03
Κλίμακα 1:50 · A3
07/11/2026 · R02

ΣΥΜΜΟΡΦΩΣΗ ΜΕ ΤΙΣ ΠΡΟΔΙΑΓΡΑΦΕΣ (ιδιοκτήτης 07/11/2026)

1 Κλιματισμός	Καναλάτη ΚΜ1 24k στη χαμηλή οροφή της κουζίνας (ιδιοκτήτης 07/11) με slot Π1 / Π2 στην ακμή → καθιστικό · split τοίχου ΚΜ2 / ΚΜ3 στα υπνοδωμάτια (ιδιοκτήτης – ΕΓΚΕΚΡ.) · χώρος 34 cm (περιθώριο 45 mm) · θυρίδα = Ε1 · ψυκτικά ΚΜ1 κάτω από τη Δ3.1 με 67 mm.
2 Κουρτίνες	ΚΡ1–ΚΡ4 σε όλα τα ανοίγματα καθιστικού / υπνοδωματίων, 20 (22) × 10 cm, ανοιχτές ως την πλάκα, δίπλα στις δοκούς όψης.
3 Φωτισμός	22 χωνευτά spots (υπνοδωμάτια, λουτρό, WC, χωλ, κουζίνα, καθιστικό ΚΘ1–ΚΘ7) + LED4 · ΚΡΕΜ0 στο κέντρο του τραπεζιού σαλονιού · ΚΡΕΜ1 στο κέντρο της νησίδας · κανένα spot κάτω από μονάδα / αεραγωγό / σε θυρίδα / πάνω από ντουλάπι.
4 Πυρανίχνευση	ΑΚ1–ΑΚ4 καπνού + Αθ5 θερμοδιαφορικός κουζίνας · ≥ 0,50 / 0,50 / 1,00 (χωλ 0,90: στον άξονα).
5 Κατασκευή	Βασική 10 cm κάτω από την πλάκα στο καθιστικό · καταβίβαση μόνο για την καναλάτη (κουζίνα +2,62) και την κάλυψη των δοκών (σανίδα Δ3.1 +2,62 – εξαίρεση) · υπνοδωμάτια / λουτρό +2,70 περασιά · κανένα δόντι.
6 Γενική αρχή	3 στάθμες· στον ενιαίο χώρο καθιστικού – κουζίνας μία ευθεία στο μέτωπο της νησίδας και η γραμμή της Δ3.1.

ΕΓΚΕΚΡΙΜΕΝΑ / ΑΠΟΦΑΣΕΙΣ ΙΔΙΟΚΤΗΤΗ (07/11/2026)

- Χαμηλή οροφή του σαλονιού πάνω από την κουζίνα, με το μηχάνημα εκεί (R02).
- Υπνοδωμάτια με split τοίχου αντί καναλάτου (R02).
- Μονάδα ΚΜ1 slim ≤ 245 mm ως παραδοχή μέχρι την επιλογή μοντέλου (όπως Β1).

ΑΛΛΑΓΕΣ R01 → R02 (ιδιοκτήτης 07/11/2026)

- Χαμηλή οροφή ΠΑΝΩ ΑΠΟ ΤΗΝ ΚΟΥΖΙΝΑ με το μηχάνημα εκεί (ιδιοκτήτης 07/11): +2,62 στο 6,60–9,54 × 4,95–9,125 (νησίδα, στήλες, πάγκος, προθάλαμος WC), ακμή στο μέτωπο της νησίδας x 6,60 σε όλο το βάθος. ΚΜ1 24k πάνω από τον προθάλαμο / το βόρειο άκρο της νησίδας, slot Π1 / Π2 1,50 στην ακμή με ρίψη ΔΥΤΙΚΑ στο καθιστικό, Ε1 600×600 ανοιγόμενη = θυρίδα. Καταργήθηκε η ζώνη σε Γ κατά μήκος του καναπέ.
- Καθιστικό ελεύθερο +2,86· η Δ3.1 που προεξέχει 0,20 με σανίδα +2,62 (= χωλ / κουζίνα → μία μόνο αλλαγή στάθμης στο πέρασμα από το χωλ). Ψυκτικά ΚΜ1 κάτω από τη Δ3.1 μέσα από τη ντουλάπα καθιστικού (καθαρό 67 mm) → κενό Υπν.2 → Τ1-04.
- Υπνοδωμάτια με split τοίχου (ιδιοκτήτης: «στα δωμάτια split»): ΚΜ2 / ΚΜ3 9k πάνω από την πόρτα κάθε δωματίου (+2,30…+2,59), ρίψη δίπλα από το κρεβάτι· ψυκτικά στο κενό χωλ / Υπν.2 · συμπυκνώματα με ροή στα σιφώνια του λουτρού. Καταργήθηκαν οι καναλάτες, Π3 / Π4, Ε2 / Ε3, αεραγωγοί.
- Καθιστικό (ιδιοκτήτης: «κρεμαστό σε λάθος θέση – σκέψου και σποτ»): ΚΡΕΜ0 στο κέντρο του τραπεζιού σαλονιού (3,15 · 6,65 – ήταν 3,60 · 7,70) · ΚΡΕΜ1 στο κέντρο της νησίδας (7,05 · 6,85 – ήταν 0,30 νοτιότερα) · 7 spots ΚΘ1–ΚΘ7 περιμετρικά στις τζαμαρίες (κύκλωμα λ)· το spot εισόδου Ε1 καταργήθηκε (η είσοδος Θ0.03 φωτίζεται από τα ΚΘ5 / ΚΘ6). Χ1 → 4,90 και ΑΚ4 → 5,45 (≥ 1,00 από το split ΚΜ2). Σύνολο 22 spots.

ΠΡΟΗΓΟΥΜΕΝΗ ΑΝΑΘΕΩΡΗΣΗ

- R01: καθιστικό +2,86 με ζώνη ΚΜ1 / κουζίνας +2,62 σε Γ κατά μήκος του βόρειου τοίχου · καναλάτες ΚΜ2 / ΚΜ3 με slot στα υπνοδωμάτια · καθιστικό χωρίς spots.

ΑΝΟΙΚΤΑ ΣΗΜΕΙΑ


- Α1 [ΑΠΟΦΑΣΗ] Τ.Δ. ισογείου στο σύστημα του Σ3: θεωρήθηκε +0,45 (Α-10-GF «ΙΣ1 +0,45») → πλάκα +3,20 από Τ.Δ., καθαρό ύψος καθιστικού 2,86 / υπνοδωματίων 2,70 / κουζίνας 2,62. Αν διαφέρει, αλλάζουν μόνο οι αριθμοί – επιβεβαίωση (τομή Α-30 ή στατικός).
- Α2 [ΣΥΝΤΟΝΙΣΜΟΣ] Το λουτρό γονέων του Α΄ είναι πάνω από το Υπν.1: η στήλη λεκάνης (x ≈ 2,75 · y ≈ 3,37) πέφτει μέσα στο δωμάτιο → εκτροπή στο κενό 32 cm ως τη ντουλάπα (y 4,25–4,85) και κατέβασμα μέσα σε αυτή· ΘΕ5 για καθαρισμό – οριστικά στις αποχετεύσεις.
- Α3 [ΑΠΟΦΑΣΗ] Spots καθιστικού ΚΘ1–ΚΘ7 = πρόταση (κύκλωμα λ με dimmer) – μπορούν να αφαιρεθούν χωρίς άλλη αλλαγή.
- Α4 [ΑΠΟΦΑΣΗ] Επάνω ντουλάπια κουζίνας στον Τ6-01 και στη γωνία ως την οροφή +2,62, με LED4 από κάτω – όπως Β1.
- Α5 [ΑΠΟΦΑΣΗ] Τα split ΚΜ2 / ΚΜ3 είναι ΠΑΝΩ ΑΠΟ ΤΙΣ ΠΟΡΤΕΣ → πόρτες υπνοδωματίων ύψους ≤ 2,20 (κάσα +2,25). Με πόρτες 2,40 πάνε πάνω από τα κεφαλάρια (Υπν.1 δυτικός τοίχος / Υπν.2 βόρειος) με ψυκτικά στο κενό του δωματίου.
- Α6 [ΜΟΝΤΕΛΟ] ΚΜ1 24k slim ≤ 245 mm (θέση ηλεκτρικού κουτιού προς την Ε1) · split ≤ 290 × 800 mm · μελέτη ψύξης ισογείου.
- Α7 [ΣΤΑΤΙΚΟΣ] Δοκοί / πλάκες από το παράγωγο σχέδιο γεωμετρίας του Σ3 (εγκεκριμένο 02/2024)· το Σ3_ΕΦ (Κόγιας) να ελεγχθεί πριν τη σκυροδέτηση – κρίσιμα: Π8 h24, Δ3.1 30/50 στο 4,85–5,15, Δ9.1 30/50.

ΕΛΕΓΧΟΣ ΣΥΓΚΡΟΥΣΕΩΝ & ΣΤΑΘΜΩΝ – 66 έλεγχοι · ΟΚ 64 · ΟΡΙΑΚΟ 0 · ΕΓΚΕΚΡ. 2 · ΑΠΟΚΛΙΣΗ 0

Αυτόματος έλεγχος από το μοντέλο (code/anopseis/checks.py): στάθμες ↔ δοκοί · κενό μονάδων · θυρίδες · spots ↔ ζώνες / θυρίδες / μονάδες / αεραγωγοί / κουρτινόθηκες · ανιχνευτές ↔ τοίχοι / φωτιστικά / στόμια · κουρτινόθηκες ↔ κουφώματα / δοκοί.

ΚΩΔ.	ΚΑΤΑΣΤ.	ΣΤΟΙΧΕΙΟ	ΜΕΤΡΗΣΗ
ΣΤ01	ΟΚ	Z2 ΚΟΥΖΙΝΑ – ΧΑΜΗΛΗ ΟΡΟΦΗ ΚΜ1 ↔ Δ3.1 30/50 (Κ.Π. +2.70)	οροφή +2.62 · κρυμμένη 8 cm
ΣΤ02	ΟΚ	Z2 ΚΟΥΖΙΝΑ – ΧΑΜΗΛΗ ΟΡΟΦΗ ΚΜ1 ↔ Δ9.1 30/50 (Κ.Π. +2.70)	οροφή +2.62 · κρυμμένη 8 cm
ΣΤ03	ΟΚ	Z3 WC ↔ Δ3.1 30/50 (Κ.Π. +2.70)	οροφή +2.62 · κρυμμένη 8 cm
ΣΤ04	ΟΚ	Z4 ΧΩΛ ↔ Δ3.1 30/50 (Κ.Π. +2.70)	οροφή +2.62 · κρυμμένη 8 cm
ΣΤ05	ΟΚ	Z8 ΣΑΝΙΔΑ ΚΑΤΩ ΑΠΟ Δ3.1 (καθιστικό) ↔ Δ3.1 30/50 (Κ.Π. +2.7…	οροφή +2.62 · κρυμμένη 8 cm
ΚΛ-ΚΜ1	ΟΚ	ΚΜ1 24.000 Btu/h – καθιστικό – κουζίνα	κενό 340 mm · περιθώριο +45 mm
ΘΕ-ΚΜ1	ΟΚ	ΚΜ1 – πρόσβαση συντήρησης	Ε1
ΚΛ-ΚΜ2	ΟΚ	ΚΜ2 split τοίχου 9.000 Btu/h – Υπνοδωμάτιο 1 (πάνω από την πό…	οροφή +2,70 · μονάδα +2,30…+2,59 · πάνω…
ΚΡ-ΚΜ2	ΟΚ	ΚΜ2 – ρίψη δυτικά, νότια του κρεβατιού	ο άξονας της ρίψης περνά 0,42 νότια του κ…
ΨΣ-ΚΜ2	ΟΚ	ΚΜ2 – ψυκτικά / συμπυκνώματα	ψυκτικά από πίσω στο κενό χωλ (+2,62) → …
ΚΛ-ΚΜ3	ΟΚ	ΚΜ3 split τοίχου 9.000 Btu/h – Υπνοδωμάτιο 2 (πάνω από την πό…	οροφή +2,70 · μονάδα +2,30…+2,59 · πάνω…
ΚΡ-ΚΜ3	ΟΚ	ΚΜ3 – ρίψη ανατολικά, νότια από τα πόδια του κρεβατιού	κεφαλάρι βόρεια (6,65–8,25 × 0,805–2,805…
ΨΣ-ΚΜ3	ΟΚ	ΚΜ3 – ψυκτικά / συμπυκνώματα	ψυκτικά από πίσω κατευθείαν στο κενό Υπν…
ΨΥ-ΚΜ1	ΟΚ	Όδευση ψυκτικών ΚΜ1 κουζίνα → ντουλάπα καθιστικού → Υπν.2…	ελάχιστο 280 mm
ΨΥ-ΚΜ2	ΟΚ	Όδευση ψυκτικών split ΚΜ2 Υπν.1 → κενό χωλ → Υπν.2	ελάχιστο 280 mm
ΨΥ-ΔΟΚ	ΟΚ	Διέλευση ψυκτικών ΚΜ1 κάτω από τη Δ3.1 (x ≈ 7.30, ντουλάπα κ…	καθαρό 67.5 mm · περιθώριο +25.6 mm
ΚΔ-ΚΜ1	ΟΚ	Καθιστικό – κουζίνα (ενιαίος χώρος)	ΚΜ1 καναλάτη στη χαμηλή οροφή της κουζ…
ΚΔ-ΚΜ2	ΕΓΚΕΚΡ.	Υπνοδωμάτιο 1	ΚΜ2 split τοίχου (ιδιοκτήτης 07/11: «στα δ…
ΚΔ-ΚΜ3	ΕΓΚΕΚΡ.	Υπνοδωμάτιο 2	ΚΜ3 split τοίχου (ιδιοκτήτης 07/11: «στα δ…
ΣΤ-Π1	ΟΚ	Π1 slot οροφής 1500×120 · 2 σχισμές	μέσα
ΣΤ-Π2	ΟΚ	Π2 slot οροφής 1500×120 · 2 σχισμές	μέσα
SP-Y1	ΟΚ	Y1 spot (1.800 · 1.750) – ΥΠΝΟΔΩΜΑΤΙΟ 1	κενό 307 mm · άκρη 0.67
SP-Y2	ΟΚ	Y2 spot (3.200 · 1.750) – ΥΠΝΟΔΩΜΑΤΙΟ 1	κενό 307 mm · άκρη 0.74
SP-Y3	ΟΚ	Y3 spot (1.800 · 3.300) – ΥΠΝΟΔΩΜΑΤΙΟ 1	κενό 307 mm · άκρη 0.67
SP-Y4	ΟΚ	Y4 spot (3.200 · 3.300) – ΥΠΝΟΔΩΜΑΤΙΟ 1	κενό 307 mm · άκρη 0.95
SP-Y5	ΟΚ	Y5 spot (7.200 · 1.750) – ΥΠΝΟΔΩΜΑΤΙΟ 2	κενό 307 mm · άκρη 0.65
SP-Y6	ΟΚ	Y6 spot (8.600 · 1.750) – ΥΠΝΟΔΩΜΑΤΙΟ 2	κενό 307 mm · άκρη 0.55
SP-Y7	ΟΚ	Y7 spot (7.200 · 3.300) – ΥΠΝΟΔΩΜΑΤΙΟ 2	κενό 307 mm · άκρη 0.65
SP-Y8	ΟΚ	Y8 spot (8.600 · 3.300) – ΥΠΝΟΔΩΜΑΤΙΟ 2	κενό 307 mm · άκρη 0.55
SP-Λ1	ΟΚ	Λ1 spot IP65 (5.560 · 1.200) – ΛΟΥΤΡΟ	κενό 307 mm · άκρη 0.40
SP-Λ2	ΟΚ	Λ2 spot IP44 (5.450 · 2.150) – ΛΟΥΤΡΟ	κενό 307 mm · άκρη 0.78
SP-Λ3	ΟΚ	Λ3 spot IP44 (5.450 · 2.850) – ΛΟΥΤΡΟ	κενό 307 mm · άκρη 0.30
SP-Λ4	ΟΚ	Λ4 spot IP44 (8.400 · 5.300) – WC	κενό 327 mm · άκρη 0.35
SP-X1	ΟΚ	X1 spot (4.900 · 3.700) – ΧΩΛ	κενό 387 mm · άκρη 0.38
SP-X2	ΟΚ	X2 spot (6.000 · 4.600) – ΧΩΛ	κενό 387 mm · άκρη 0.35
SP-M1	ΟΚ	M1 spot (8.220 · 7.000) – ΚΟΥΖΙΝΑ – ΧΑΜΗΛΗ ΟΡΟΦΗ ΚΜ1	κενό 327 mm · άκρη 1.05
SP-M2	ΟΚ	M2 spot (8.220 · 8.400) – ΚΟΥΖΙΝΑ – ΧΑΜΗΛΗ ΟΡΟΦΗ ΚΜ1	κενό 327 mm · άκρη 0.72
SP-ΚΘ1	ΟΚ	ΚΘ1 spot (2.450 · 6.000) – ΚΑΘΙΣΤΙΚΟ	κενό 88 mm · άκρη 0.53
SP-ΚΘ2	ΟΚ	ΚΘ2 spot (2.450 · 7.200) – ΚΑΘΙΣΤΙΚΟ	κενό 88 mm · άκρη 0.53
SP-ΚΘ3	ΟΚ	ΚΘ3 spot (2.450 · 8.400) – ΚΑΘΙΣΤΙΚΟ	κενό 88 mm · άκρη 0.53
SP-ΚΘ4	ΟΚ	ΚΘ4 spot (3.650 · 8.400) – ΚΑΘΙΣΤΙΚΟ	κενό 88 mm · άκρη 0.53
SP-ΚΘ5	ΟΚ	ΚΘ5 spot (4.850 · 8.400) – ΚΑΘΙΣΤΙΚΟ	κενό 88 mm · άκρη 0.53
SP-ΚΘ6	ΟΚ	ΚΘ6 spot (6.050 · 8.400) – ΚΑΘΙΣΤΙΚΟ	κενό 88 mm · άκρη 0.53
SP-ΚΘ7	ΟΚ	ΚΘ7 spot (7.250 · 8.400) – ΚΟΥΖΙΝΑ – ΧΑΜΗΛΗ ΟΡΟΦΗ ΚΜ1	κενό 327 mm · άκρη 0.65
SP-ΚΑΘ	ΟΚ	Καθιστικό	ΚΘ1–ΚΘ7 περιμετρικά (κύκλωμα λ, dimmer)…
ΚΜΣ-ΚΡΕΜ0	ΟΚ	ΚΡΕΜ0 κρεμαστό – τραπέζι σαλονιού	κέντρο (3.15 · 6.65) · Π1 3.47
ΚΜΣ-ΚΡΕΜ1	ΟΚ	ΚΡΕΜ1 κρεμαστό – νησίδα	κέντρο (7.05 · 6.85) · κανένα στόμιο δεν ρί…
ΠΥ-ΑΚ1	ΟΚ	ΑΚ1 καπνού (5.30 · 7.70) – καθιστικό	τοίχος 1.30 · ΚΘ5 0.83 · Π2 1.32
ΠΥ-ΑΚ2	ΟΚ	ΑΚ2 καπνού (2.50 · 2.52) – Υπνοδωμάτιο 1	τοίχος 1.37 · Υ1 1.04 · ΚΜ2 1.89
ΠΥ-ΑΚ3	ΟΚ	ΑΚ3 καπνού (7.90 · 2.52) – Υπνοδωμάτιο 2	τοίχος 1.35 · Υ6 1.04 · ΚΜ3 1.40
ΠΥ-ΑΚ4	ΟΚ	ΑΚ4 καπνού (5.45 · 3.70) – χωλ – άξονας διαδρόμου 0,90 (≥ 1,00…	τοίχος 0.45 (διάδρομος 0,90 – άξονας) · Χ1…
ΠΥ-Αθ5	ΟΚ	Αθ5 θερμοδιαφορικός (8.22 · 7.70) – κουζίνα – θερμοδιαφορικός…	τοίχος 0.97 · Μ1 0.70 · Π2 1.48
ΠΥ-ΧΩΡ	ΟΚ	Κάλυψη χώρων	καθιστικό · κουζίνα (θερμικός) · Υπν.1 · Υπν…
ΘΕ-ΘΕ4	ΟΚ	ΘΕ4 40×40 – λουτρό: επίσκεψη αποχετεύσεων λουτρού Α΄	ελεύθερη
ΘΕ-ΘΕ5	ΟΚ	ΘΕ5 40×40 – Υπν.1: καθαριστήριο αποχέτευσης λουτρού γονέων …	ελεύθερη
KP-KP1	ΟΚ	KP1 W0.01 – καθιστικό – Δ · 20 × 10 cm · οδηγοί 7 / 14 cm	πλήρης · βάθος 10 cm
KP-KP2	ΟΚ	KP2 W0.02 · Θ0.03 · W0.03 – καθιστικό – Ν · 20 × 10 cm · οδηγοί 7…	πλήρης · βάθος 10 cm
KP-KP3	ΟΚ	KP3 W0.08 – Υπν.1 – Β · 20 × 10 cm · οδηγοί 7 / 14 cm	πλήρης · βάθος 32 cm
KP-KP4	ΟΚ	KP4 W0.06 – Υπν.2 – Α · 22 × 10 cm · οδηγοί 10 / 17 cm (μπαλκον…	πλήρης · βάθος 32 cm
KP-W0.07	ΟΚ	W0.07	δεν απαιτείται – λουτρό (στο τοιχείο Κ2)
KP-W0.05	ΟΚ	W0.05	δεν απαιτείται – κλιμακοστάσιο (εκτός διαμ…
ΣΘ-Ζ1	ΟΚ	Ζ1 +2,86 ↔ Ζ2 +2,62	χαμηλή οροφή κουζίνας / ΚΜ1 – μία ευθεία…
ΣΘ-Ζ1	ΟΚ	Ζ1 +2,86 ↔ Ζ8 +2,62	σανίδα κάτω από τη Δ3.1 που προεξέχει 0,2…
ΣΘ-Ζ8	ΟΚ	Ζ8 / Ζ4 / Ζ2 / Ζ3 +2,62	ίδια στάθμη – κανένα σκαλοπάτι στο πέρασ…
ΣΘ-Ζ4	ΟΚ	Ζ4 +2,62 ↔ Ζ5 / Ζ6 / Ζ7 +2,70	χωλ ↔ λουτρό / υπνοδωμάτια – μόνο σε πό…
ΣΘ-ΣΥΝ	ΟΚ	Στάθμες στο διαμέρισμα	+2.62 · +2.70 · +2.86 (καθιστικό +2,86 = 10 …

B

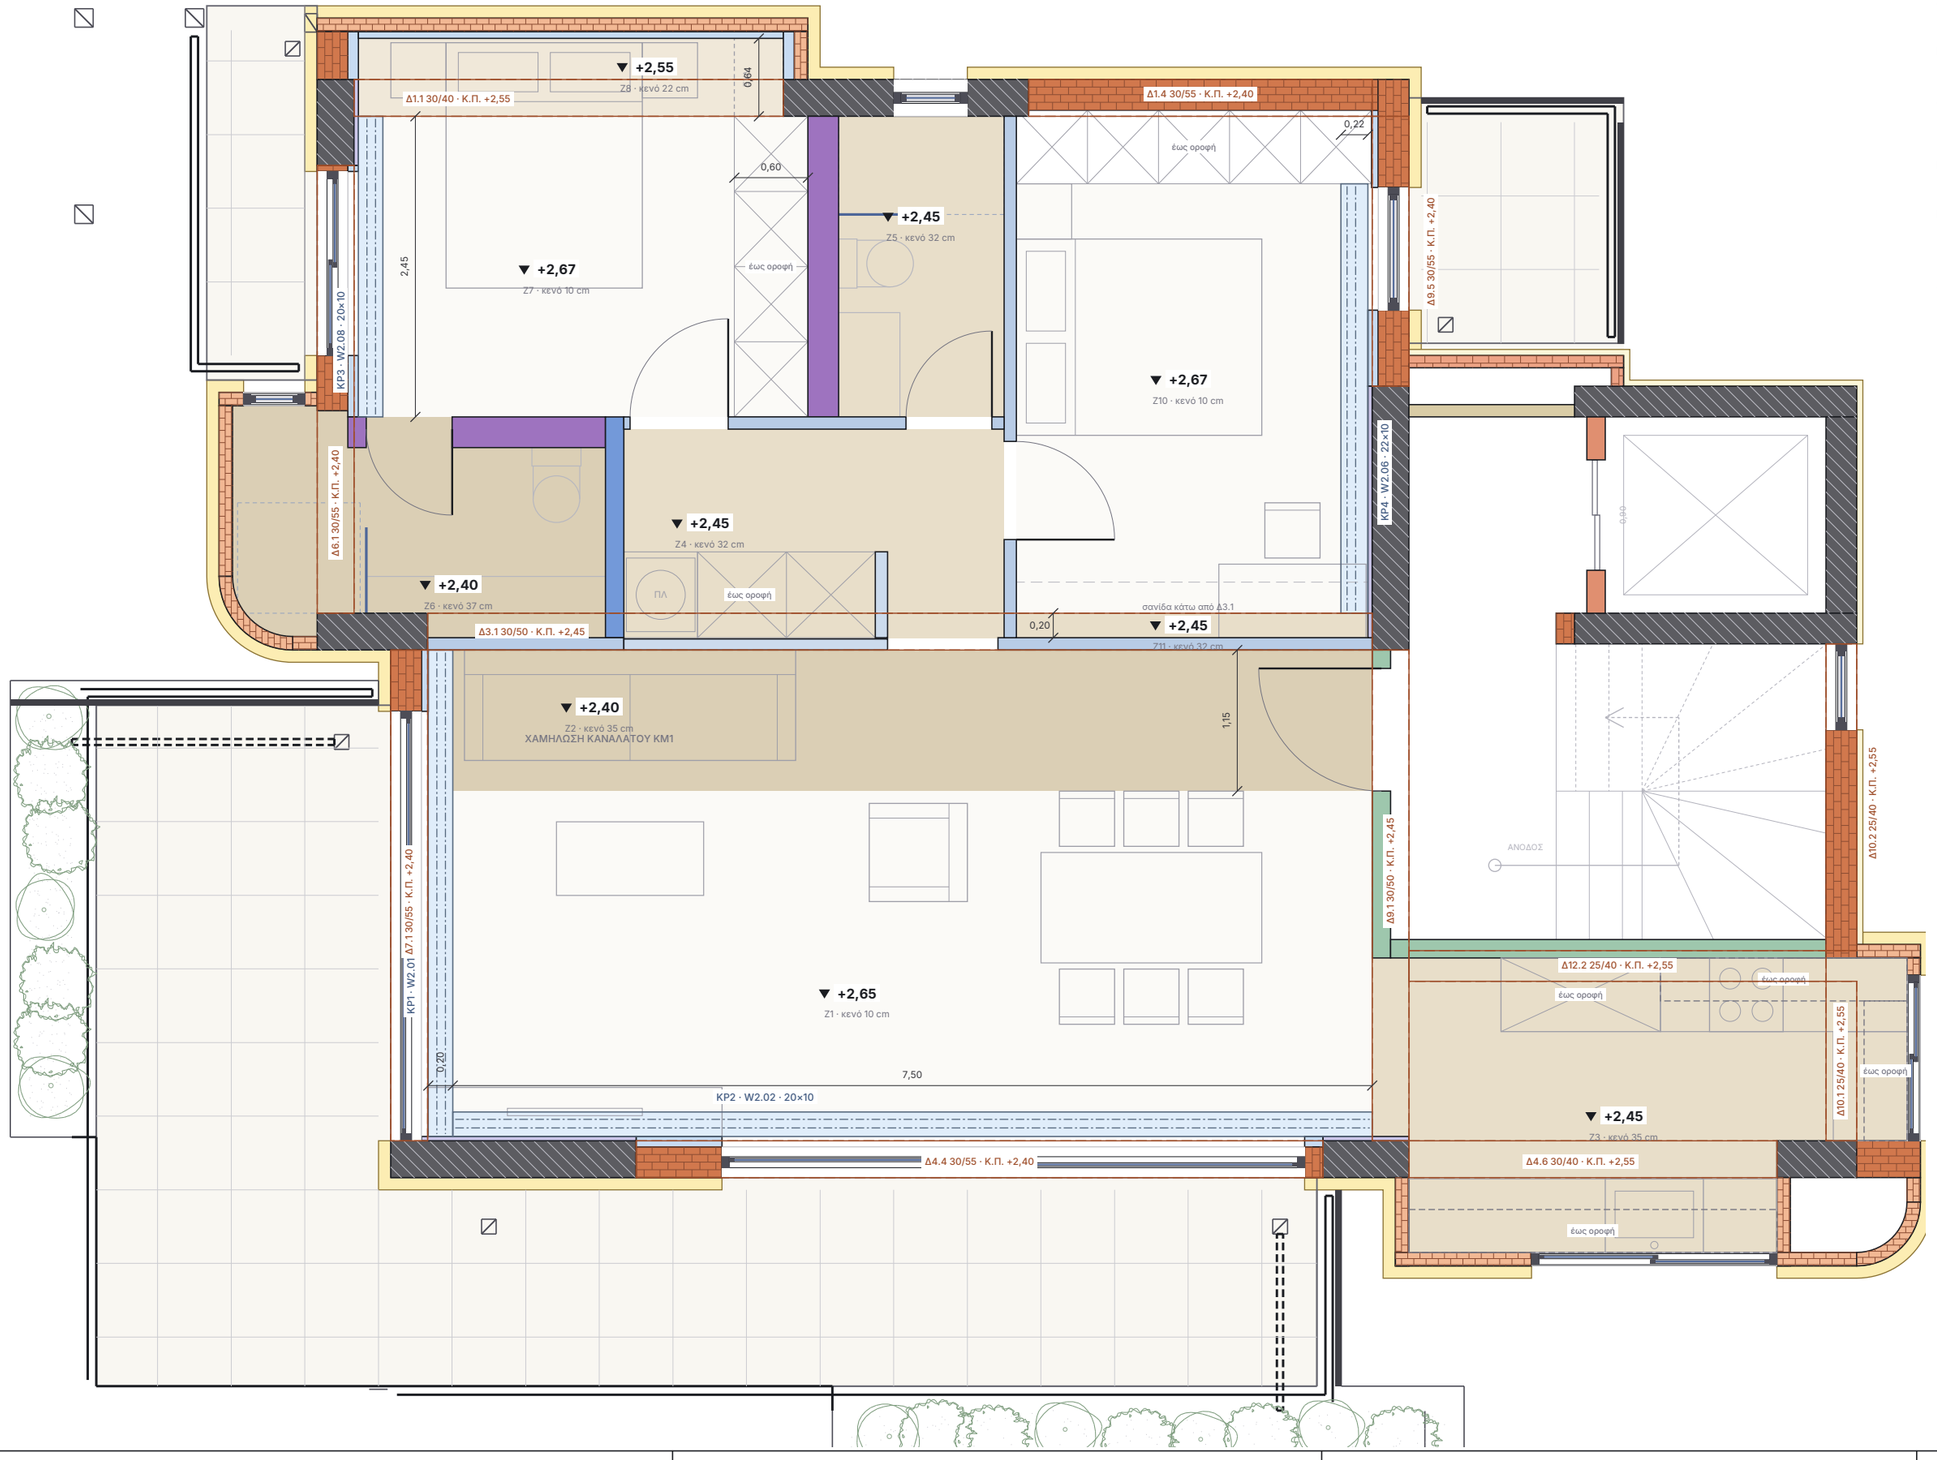

ΣΗΜΕΙΩΣΕΙΣ

Στάθμες από το τελικό δάπεδο του ορόφου (Β΄ +6,90). Πάνω παρειά πλάκας +2,95· κάτω παρειά Π3 h18 +2,77 · Π8 h20 +2,75 · Π10 h15 +2,80.

Κανόνας: πουθενά ψευδοροφή κάτω από κάτω παρειά δοκού· όπου «περασιά» η γυψοσανίδα στη δοκό προσθέτει ≈ 1,5 cm.

Αλλαγές στάθμης ΜΟΝΟ: χαμήλωση ΚΜ1 · γραμμή δοκού Δ9.1 (καθιστικό → κουζίνα) · γραμμή Δ1.1 (κεφαλάρι) · σανίδα κάτω από Δ3.1 στο Υπν.2. R13: χωρίς κουτί ντουλάπας Υπν.1 (καμία καναλάτη στα υπνοδωμάτια).


Κουρτινόθηκες: 20 × 10 cm (ΚΡ4 22 cm για το ανοιγοανακλινόμενο W2.06), σε όλο το μήκος του τοίχου, δίπλα (όχι κάτω) από τις δοκούς όψης.

R12: ΜΟΝΟ η χαμήλωση της ΚΜ1 −5 cm → +2,40 (κενό 35 cm): η Δ3.1 κρύβεται 5 cm και τα ψυκτικά της ΚΜ1 περνούν από κάτω της προς τη ντουλάπα του χωλ (ιδιοκτήτης 07/11). Το καθιστικό μένει +2,65. Στο άνοιγμα χωλ – καθιστικού: χωλ +2,45 (περασιά Δ3.1) / χαμήλωση +2,40.

ΥΠΟΜΝΗΜΑ

- +2,65 / +2,67 βασική = 10 cm κάτω από την πλάκα (spot σώμα ≤ 75 mm)
- +2,55 περασιά με δοκό 40 (κεφαλάρι Υπν.1)
- +2,45 περασιά με δοκό 50: χωλ · λουτρό · κουζίνα
- +2,40 χαμήλωση ΚΜ1 (5 cm κάτω από Δ3.1 – ψυκτικά) · λουτρό γονέων (περασιά Δ6.1)
- ΚΡ εσοχή κουρτίνας ανοιχτή ως την πλάκα · 2 οδηγοί
- δοκός (Σ5) · Κ.Π. = κάτω παρειά από Τ.Δ.

ΕΡΓΟ	ΘΕΜΑ ΣΧΕΔΙΟΥ	ΒΑΣΗ	ΑΡ. ΣΧΕΔΙΟΥ
ΠΕΝΤΑΟΡΟΦΟ ΚΤΗΡΙΟ ΚΑΤΟΙΚΙΩΝ – ΑΡΓΥΡΟΥΠΟΛΗ Κωνσταντινουπόλεως 12 & Αγ. Βαρβάρας · Ο.Τ. 103-15 Εργοδότης: INTERKAT Α.Ε. · Κατασκευή: ARKAD Ι.Κ.Ε.	**ΑΝΟΨΗ – ΣΤΑΘΜΕΣ · ΔΟΚΟΙ · ΚΟΥΡΤΙΝΕΣ** Στάθμες ψευδοροφής · δοκοί Σ5 · εσοχές κουρτινών Α΄ · Β΄ · Γ΄ ΟΡΟΦΟΣ – Β1 (τυπικός όροφος)	Βάση: τοιχοποιίες Β1 R25 · ξυλότυπος Σ5 (+9,85) · ανόψη R10	**ΑΝ-05** **Κλίμακα 1:50 · Α3** 07/11/2026 · R13

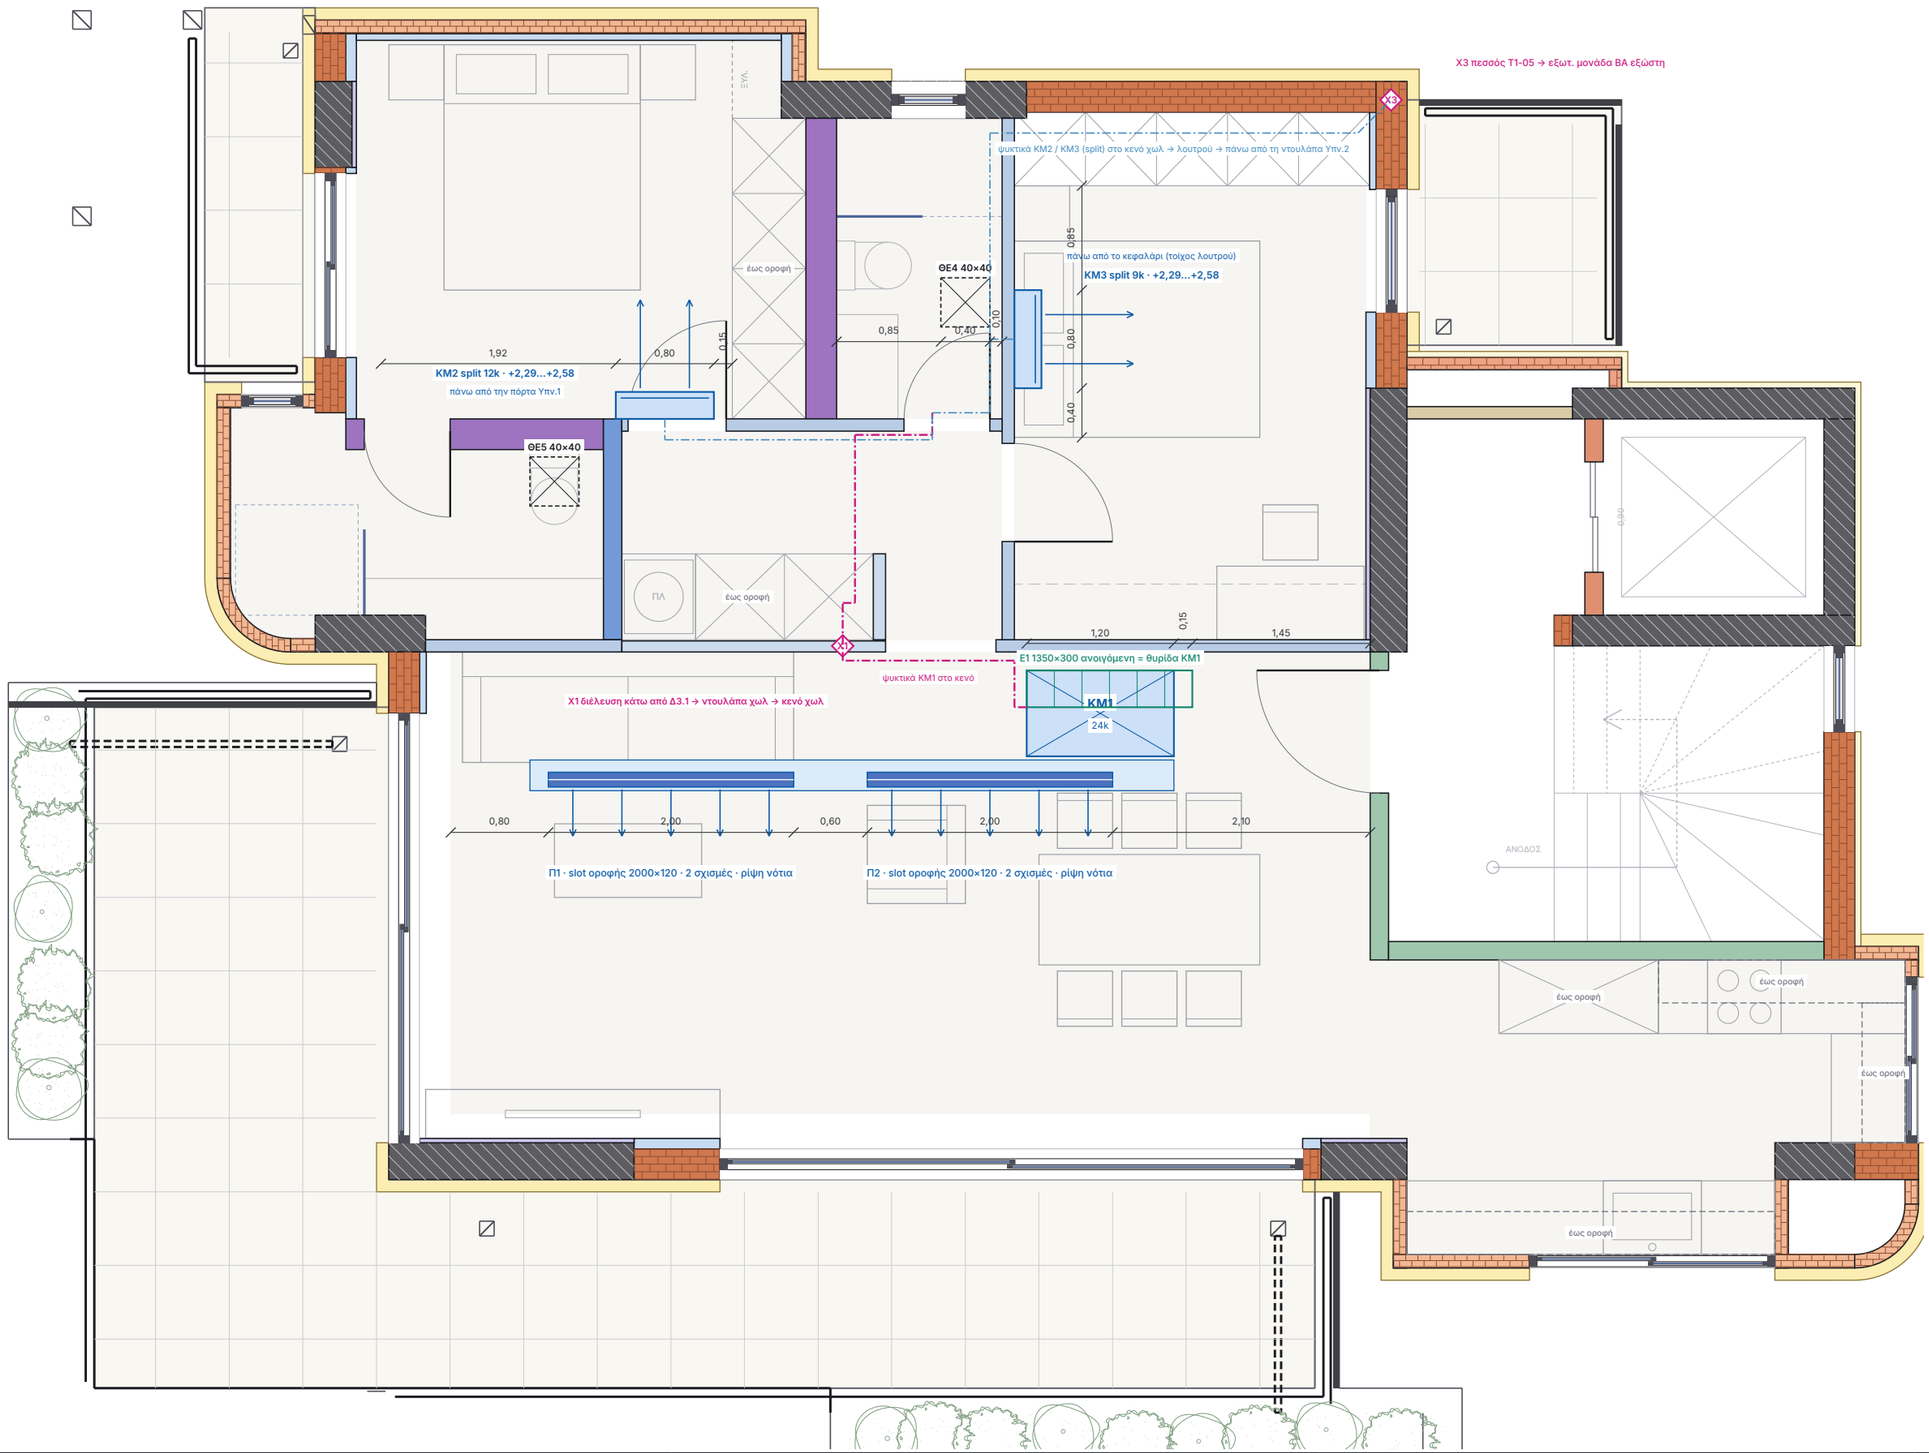

ΣΗΜΕΙΩΣΕΙΣ

Χώρος ΚΜ1 (προδ. 1): χαμήλωση +2,40 κάτω από Π8 +2,75 = 35 cm → 245 + 10 + 40 = 295 → περιθώριο 55 mm. Πρόσβαση από την ανοιγόμενη Ε1.

R13 – ΥΠΟΔΩΜΑΤΙΑ ΜΕ SPLIT (ιδιοκτήτης 07/11: «στα δωμάτια δεν θα βάζουμε καναλάτο, θα βάζουμε split σε ένα σημείο που θα βρεις»). Κανόνας θέσης: ψηλά σε εσωτερικό τοίχο, ρίψη κατά μήκος του δωματίου που δεν πέφτει στο προσκέφαλο, ψυκτικά κατευθείαν στο κενό χωλ / λουτρού.

ΚΜ2 12k Υπν.1: ΠΑΝΩ ΑΠΟ ΤΗΝ ΠΟΡΤΑ (3,25–4,05 · +2,29…+2,58, 9 cm από την οροφή +2,67, 4 cm πάνω από την κάσα 2,25). Το κεφαλάρι είναι στο έρκερ (εξωτερικός τοίχος, LED3, Δ1.1 – χωρίς κενό για ψυκτικά) → ο αέρας ρίχνεται βόρεια δίπλα από την ανατολική πλευρά του κρεβατιού.

ΚΜ3 9k Υπν.2: ΠΑΝΩ ΑΠΟ ΤΟ ΚΕΦΑΛΑΡΙ στον τοίχο λουτρού Τ2-02 (2,20–3,00 · +2,29…+2,58), ρίψη ανατολικά προς τα πόδια και το W2.06.

Ψυκτικά split: από πίσω από τη μονάδα μέσα στον γυψότοιχο / υπέρθυρο ως το κενό χωλ (+2,45) / λουτρού → μαζί με την ΚΜ1 → πάνω από τη ντουλάπα Υπν.2 → πεσσός Τ1-05 → εξωτερική μονάδα ΒΑ εξώστη. Συμπυκνώματα με φυσική ροή μέσα στον γυψότοιχο στα σιφώνια των λουτρών (ΚΜ2 → Τ2Α-01 / λουτρό γονέων · ΚΜ3 → Τ2-02 / λουτρό) – χωρίς αντλία.

Ψυκτικά ΚΜ1 (R12, ιδιοκτήτης: «μέσω οροφής και ντουλάπας χωλ»): Χ1 κάτω από τη Δ3.1 μέσα από τον Τ2Ν-01 στη ντουλάπα χωλ (x ≈ 5,10) → κενό χωλ → λουτρό → Τ1-05. ΟΡΙΑΚΟ: καθαρό 37,5 mm → αερίου 5/8″ με μόνωση 9 mm χωράει, 13 mm όχι. Καμία οπή σε δοκό.

Στήριξη split σε γυψότοιχο: ενίσχυση (OSB 18 ή UA) πίσω από τη βάση της μονάδας / στο υπέρθυρο.

ΥΠΟΜΝΗΜΑ

- ΚΜ1 καναλάτη μονάδα (slim ≤ 245 mm)
- ΚΜ2 / ΚΜ3 split τοίχου (σώμα στον τοίχο, βέλη = ρίψη)
- αεραγωγός / plenum προσαγωγής (μονωμένος, στο κενό)
- Π1 / Π2 γραμμικό slot οροφής 2 σχισμών, ρυθμιζόμενη ρίψη
- Ε στόμιο / κιβώτιο επιστροφής με φίλτρο
- ΘΕ θυρίδα επίσκεψης (αφανής, βαφόμενη)
- Χ κατέβασμα / έξοδος σωληνώσεων – καμία οπή σε σκυρόδεμα

ΕΡΓΟ	ΘΕΜΑ ΣΧΕΔΙΟΥ	ΒΑΣΗ	ΑΡ. ΣΧΕΔΙΟΥ
ΠΕΝΤΑΟΡΟΦΟ ΚΤΗΡΙΟ ΚΑΤΟΙΚΙΩΝ – ΑΡΓΥΡΟΥΠΟΛΗ Κωνσταντινουπόλεως 12 & Αγ. Βαρβάρας · Ο.Τ. 103-15 Εργοδότης: INTERKAT Α.Ε. · Κατασκευή: ARKAD Ι.Κ.Ε.	**ΑΝΟΨΗ – ΚΛΙΜΑΤΙΣΜΟΣ · ΘΥΡΙΔΕΣ** Καναλάτη ΚΜ1 · split υπνοδωματίων · slot · θυρίδα · ψυκτικά Α΄ · Β΄ · Γ΄ ΟΡΟΦΟΣ – Β1 (τυπικός όροφος)	Βάση: τοιχοποιίες Β1 R25 · ξυλότυπος Σ5 (+9,85) · ανόψη R10	**ΑΝ-06** **Κλίμακα 1:50 · Α3** 07/11/2026 · R13



ΣΗΜΕΙΩΣΕΙΣ

Κατανομή: Υπν. 2 × 2 spots · λουτρά 3 (IP65 στο ντους) · κουζίνα 3 στον άξονα του διαδρόμου + LED κάτω από τα ντουλάπια · χωλ / είσοδος στον άξονα της διαδρομής · καθιστικό Κθ1–Κθ7. Σύνολο 28 spots + 2 κρεμαστά + LED3 + LED4.

R13 καθιστικό (ιδιοκτήτης: «το κρεμαστό του σαλονιού σε λάθος θέση – σκέψου μήπως βάλουμε και σποτ»): ΚΡΕΜ0 στο ΚΕΝΤΡΟ του τραπεζιού σαλονιού (3,35 · 6,85 – ήταν 4,30 · 7,575, ανάμεσα σε τραπεζάκι και TV), 0,60 από το slot Π1· ΚΡΕΜ1 στο κέντρο της τραπεζαρίας.

Spots καθιστικού Κθ1–Κθ7 (πρόταση, κύκλωμα λ με dimmer): περιμετρικά στις δύο τζαμαρίες, 0,55 από τις κουρτινόθηκες ΚΡ1 / ΚΡ2, ανά 1,20 – φωτίζουν κουρτίνες και τοίχο TV χωρίς θάμβωση στον καναπέ· το κέντρο μένει στο κρεμαστό.

Πυρανίχνευση (προδ. 4): σε κάθε κύριο χώρο και στο χωλ· ≥ 0,50 από τοίχους / δοκούς / φωτιστικά, ≥ 1,00 από στόμια προσαγωγής και split· λουτρά χωρίς ανιχνευτή καπνού (υδρατμοί). R13: ΑΚ2 (2,70 · 2,00) · ΑΚ3 (7,83 · 3,85).

Κουζίνα (R12): επάνω ντουλάπια περασιά με την οροφή με LED4 από κάτω για τον πάγκο· Μ1–Μ3 γενικός φωτισμός στον άξονα (y 8,86)· ΑΘ5 1,4 m από τις εστίες.

Οπή spot Ø 75–80 ανάμεσα στα προφίλ CD (όχι πάνω τους)· όπου πέφτει σε προφίλ, μετατόπιση του προφίλ – όχι του spot.

ΥΠΟΜΝΗΜΑ

- χωνευτό spot LED 7–9 W, 2700 K, CRI ≥ 90, UGR < 19, σώμα ≤ 75 mm
- χωνευτό spot IP44 (λουτρά)
- χωνευτό spot IP65 (πάνω από ντους)
- split τοίχου (για συντονισμό – βλ. φύλλο κλιματισμού)
- ΚΡΕΜ παροχή οροφής (κουτί + ενίσχυση ανάρτησης)
- ΑΚ ανιχνευτής καπνού (ΕΠ104 · EN 54-7)
- ΑΘ θερμοδιαφορικός ανιχνευτής (κουζίνα · EN 54-5)
- ακτίνα 0,50 m γύρω από ανιχνευτή – κανένας τοίχος / φωτιστικό μέσα
- LED κρυφό γραμμικό 3000 K – LED3 κεφαλάρι · LED4 κάτω από τα ντουλάπια κουζίνας

ΕΡΓΟ

ΠΕΝΤΑΟΡΟΦΟ ΚΤΗΡΙΟ ΚΑΤΟΙΚΙΩΝ – ΑΡΓΥΡΟΥΠΟΛΗ
Κωνσταντινουπόλεως 12 & Αγ. Βαρβάρας · Ο.Τ. 103-15
Εργοδότης: INTERKAT Α.Ε. · Κατασκευή: ARKAD Ι.Κ.Ε.

ΘΕΜΑ ΣΧΕΔΙΟΥ

ΑΝΟΨΗ – ΦΩΤΙΣΜΟΣ · ΠΥΡΑΝΙΧΝΕΥΣΗ
Χωνευτά spots · παροχές · κρυφό LED · ανιχνευτές
Α΄ · Β΄ · Γ΄ ΟΡΟΦΟΣ – Β1 (τυπικός όροφος)

ΒΑΣΗ

Βάση: τοιχοποιίες Β1 R25 · ξυλότυπος Σ5 (+9,85) · ανόψη R10

ΑΡ. ΣΧΕΔΙΟΥ

ΑΝ-07
Κλίμακα 1:50 · Α3
07/11/2026 · R13

ΣΥΜΜΟΡΦΩΣΗ ΜΕ ΤΙΣ ΠΡΟΔΙΑΓΡΑΦΕΣ (ιδιοκτήτης 07/11/2026)

1 Κλιματισμός	Καναλάτη ΚΜ1 24k στο καθιστικό / κουζίνα (κουζίνα από την ΚΜ1 – ΕΓΚΕΚΡ.) με slot Π1/Π2 · υπνοδωμάτια με split τοίχου ΚΜ2 / ΚΜ3 (ιδιοκτήτης 07/11 – ΕΓΚΕΚΡ.) · χώρος 35 cm (περιθώριο 55 mm) · θυρίδα Ε1 · ψυκτικά ΚΜ1 κάτω από τη Δ3.1 (οριακό 3,6 mm).
2 Κουρτίνες	ΚΡ1–ΚΡ4 σε όλα τα ανοίγματα καθιστικού / υπνοδωματίων, 20 (22) × 10 cm, 2 οδηγοί, ανοιχτές ως την πλάκα, δίπλα στις δοκούς όψης.
3 Φωτισμός	28 χωνευτά spots σε όλους τους χώρους (καθιστικό ΚΘ1–ΚΘ7 περιμετρικά – R13) + ΚΡΕΜ0 στο κέντρο του τραπεζιού σαλονιού + ΚΡΕΜ1 τραπεζαρίας + LED3 / LED4 · IP44/IP65 στα λουτρά · κανένα spot κάτω από μονάδα / αεραγωγό / σε θυρίδα / πάνω από ντουλάπι.
4 Πυρανίχνευση	ΑΚ1–ΑΚ4 καπνού + ΑΘ5 θερμοδιαφορικός κουζίνας · όλοι ≥ 0,50 από τοίχους / δοκούς / φωτιστικά και ≥ 1,00 από στόμια / split.
5 Κατασκευή	Βασική 10 cm κάτω από την πλάκα · μεγαλύτερη καταβίβαση μόνο στην καναλάτη ΚΜ1 (+2,40) · χωλ / λουτρό / κουζίνα περασιά με τις δοκούς (+2,45) · μία σανίδα κάτω από τη Δ3.1 στο Υπν.2 (εξαίρεση) · κανένα δόντι.
6 Γενική αρχή	5 στάθμες σε όλο το διαμέρισμα, κάθε αλλαγή πάνω σε γραμμή δοκού· τα υπνοδωμάτια ενιαία +2,67 χωρίς κουτιά (R13).

ΕΓΚΕΚΡΙΜΕΝΑ / ΑΠΟΦΑΣΕΙΣ ΙΔΙΟΚΤΗΤΗ (07/11/2026)

· Υπνοδωμάτια με split τοίχου αντί καναλάτου (R13: «στα δωμάτια δεν θα βάζουμε καναλάτο, θα βάζουμε split»).
· Κουζίνα χωρίς δική της καναλάτη – καλύπτεται από την ΚΜ1 24k.
· Μονάδα ΚΜ1 slim ≤ 245 mm ως παραδοχή μέχρι την επιλογή μοντέλου.
· Η απόφαση R02 «καθιστικό χωρίς spots» αναθεωρείται (R13: «σκέψου μήπως βάλουμε και σποτ») – τα ΚΘ1–ΚΘ7 είναι πρόταση (Α6).

ΑΛΛΑΓΕΣ R12 → R13 (ιδιοκτήτης 07/11/2026)

· Υπνοδωμάτια με split τοίχου αντί καναλάτου (ιδιοκτήτης 07/11: «στα δωμάτια δεν θα βάζουμε καναλάτο, θα βάζουμε split σε ένα σημείο που θα βρεις»). ΚΜ2 12k Υπν.1 ΠΑΝΩ ΑΠΟ ΤΗΝ ΠΟΡΤΑ (3,25–4,05, +2,29…+2,58), ρίψη βόρεια δίπλα από το κρεβάτι – το κεφαλάρι είναι στο έρκερ (εξωτ. τοίχος, LED3, Δ1.1)· ΚΜ3 9k Υπν.2 ΠΑΝΩ ΑΠΟ ΤΟ ΚΕΦΑΛΑΡΙ στον τοίχο λουτρού Τ2-02 (2,20–3,00), ρίψη ανατολικά προς τα πόδια. Ψυκτικά κατευθείαν στο κενό χωλ / λουτρού (μαζί με την ΚΜ1 → Τ1-05) · συμπυκνώματα με φυσική ροή στα σιφώνια των λουτρών.
· Καταργήθηκαν: καναλάτες ΚΜ2 / ΚΜ3 στο χωλ, Π3 / Π4, Ε2 / Ε3, θυρίδες ΘΕ2 / ΘΕ3, αεραγωγοί, το κουτί ντουλάπας Ζ9 (η ντουλάπα Υπν.1 πάει ως την οροφή +2,67). Το χωλ μένει +2,45 (περασιά Δ3.1 – κενό για τα ψυκτικά).
· Καθιστικό (ιδιοκτήτης: «το κρεμαστό του σαλονιού σε λάθος θέση – σκέψου μήπως βάλουμε και σποτ χωνευτά»): ΚΡΕΜ0 στο κέντρο του τραπεζιού σαλονιού (3,35 · 6,85 – ήταν 4,30 · 7,575, έξω από τη σύνθεση), 0,60 από το slot Π1· 7 χωνευτά spots ΚΘ1–ΚΘ7 περιμετρικά στις τζαμαρίες (0,55 από τις κουρτινόθηκες, ανά 1,20) σε κύκλωμα λ με dimmer. ΚΡΕΜ1 στο κέντρο της τραπεζαρίας (όπως ήταν). Σύνολο 28 spots.
· ΑΚ2 → (2,70 · 2,00) για ≥ 1,00 από το split ΚΜ2 · ΑΚ3 → (7,83 · 3,85) εκτός της ρίψης της ΚΜ3.

ΠΡΟΗΓΟΥΜΕΝΗ ΑΝΑΘΕΩΡΗΣΗ

· R12: χαμήλωση ΚΜ1 +2,40 με τα ψυκτικά κάτω από τη Δ3.1 στη ντουλάπα χωλ · χωρίς Wi-Fi · κουζίνα με επάνω ντουλάπια περασιά και LED4.

ΑΝΟΙΚΤΑ ΣΗΜΕΙΑ

· Α1 [ΚΑΤΑΣΚΕΥΗ] Διέλευση ψυκτικών ΚΜ1 κάτω από τη Δ3.1: καθαρό ύψος 2,45 – 2,40 – γυψοσανίδα 12,5 = 37,5 mm. Χωράει σωλήνας αερίου 5/8″ με μόνωση 9 mm (Ø ≈ 34) – με μόνωση 13 mm (Ø ≈ 42) ΟΧΙ. Στο σημείο διέλευσης χωρίς περιμετρικό UD, οι σωλήνες δίπλα-δίπλα (όχι ο ένας πάνω στον άλλο)· στη ντουλάπα χωλ επάνω καπάκι ≤ +2,40 στα νότια 0,25 (κάτω από τη δοκό). Αν ο ψυκτικός θέλει 13 mm: χαμήλωση στο +2,38.
· Α2 [ΜΟΝΤΕΛΟ] ΚΜ1: ύψος ≤ 245 mm και θέση ηλεκτρικού κουτιού / αντλίας – αν δεν φτάνονται από την ανοιγόμενη Ε1 (300 mm), προστίθεται θυρίδα 40×40 στο ανατολικό άκρο. Split ΚΜ2 / ΚΜ3: ύψος ≤ 290, πλάτος ≤ 800 mm.
· Α5 [ΑΠΟΦΑΣΗ] Το split ΚΜ2 μπαίνει ΠΑΝΩ ΑΠΟ ΤΗΝ ΠΟΡΤΑ του Υπν.1 → πόρτα ύψους ≤ 2,20 (κάσα +2,25). Αν μπουν πόρτες 2,40, η ΚΜ2 πάει πάνω από το κεφαλάρι στο έρκερ και το LED3 καταργείται.
· Α6 [ΑΠΟΦΑΣΗ] Spots καθιστικού ΚΘ1–ΚΘ7 = πρόταση (η απόφαση R02 ήταν «χωρίς spots»)· σε δικό τους κύκλωμα λ με dimmer – μπορούν να αφαιρεθούν χωρίς άλλη αλλαγή.
· Α3 [ΣΤΑΤΙΚΟΣ] Διατομή Δ10.1 (χωρίς ετικέτα στον Σ5 – θεωρήθηκε 25/40). Δεν επηρεάζει τη στάθμη της κουζίνας (+2,45 ≤ 2,55).
· Α4 [ΕΠΙ ΤΟΠΟΥ] Μέτρηση πλακών / δοκών μετά το ξεκαλούπωμα κάθε ορόφου (Α΄ Σ4 · Β΄ Σ5 · Γ΄ Σ6) πριν τη χάραξη – η ανόψη θεωρεί ίδιους δοκούς στους τρεις τυπικούς ορόφους· οι Σ4 / Σ6 να ελεγχθούν.

ΕΛΕΓΧΟΣ ΣΥΓΚΡΟΥΣΕΩΝ & ΣΤΑΘΜΩΝ – 80 έλεγχοι · ΟΚ 76 · ΟΡΙΑΚΟ 1 · ΕΓΚΕΚΡ. 3 · ΑΠΟΚΛΙΣΗ 0

Αυτόματος έλεγχος από το μοντέλο (code/anopseis/checks.py): στάθμες ↔ δοκοί · κενό μονάδων · θυρίδες · spots ↔ ζώνες / θυρίδες / μονάδες / αεραγωγοί / κουρτινόθηκες · ανιχνευτές ↔ τοίχοι / φωτιστικά / στόμια · κουρτινόθηκες ↔ κουφώματα / δοκοί.

ΚΩΔ.	ΚΑΤΑΣΤ.	ΣΤΟΙΧΕΙΟ	ΜΕΤΡΗΣΗ
ΣΤ01	ΟΚ	Ζ3 ΚΟΥΖΙΝΑ ↔ Δ9.1 30/50 (Κ.Π. +2.45)	οροφή +2.45 · περασιά
ΣΤ02	ΟΚ	Ζ3 ΚΟΥΖΙΝΑ ↔ Δ4.6 30/40 (Κ.Π. +2.55)	οροφή +2.45 · κρυμμένη 10 cm
ΣΤ03	ΟΚ	Ζ3 ΚΟΥΖΙΝΑ ↔ Δ12.2 25/40 (Κ.Π. +2.55)	οροφή +2.45 · κρυμμένη 10 cm
ΣΤ04	ΟΚ	Ζ3 ΚΟΥΖΙΝΑ ↔ Δ10.1 25/40 (Κ.Π. +2.55)	οροφή +2.45 · κρυμμένη 10 cm
ΣΤ05	ΟΚ	Ζ4 ΧΩΛ ↔ Δ3.1 30/50 (Κ.Π. +2.45)	οροφή +2.45 · περασιά
ΣΤ06	ΟΚ	Ζ6 ΛΟΥΤΡΟ ΓΟΝΕΩΝ ↔ Δ6.1 30/55 (Κ.Π. +2.40)	οροφή +2.40 · περασιά
ΣΤ07	ΟΚ	Ζ6 ΛΟΥΤΡΟ ΓΟΝΕΩΝ ↔ Δ3.1 30/50 (Κ.Π. +2.45)	οροφή +2.40 · κρυμμένη 5 cm
ΣΤ08	ΟΚ	Ζ8 ΚΕΦΑΛΑΡΙ ΥΠΝ.1 (έρκερ) ↔ Δ1.1 30/40 (Κ.Π. +2.55)	οροφή +2.55 · περασιά
ΣΤ09	ΟΚ	Ζ11 ΣΑΝΙΔΑ ΚΑΤΩ ΑΠΟ Δ3.1 (Υπν.2) ↔ Δ3.1 30/50 (Κ.Π. +2.45)	οροφή +2.45 · περασιά
ΚΛ-ΚΜ1	ΟΚ	ΚΜ1 24.000 Btu/h – καθιστικό – τραπεζαρία – κουζίνα	κενό 350 mm · περιθώριο +55 mm
ΘΕ-ΚΜ1	ΟΚ	ΚΜ1 – πρόσβαση συντήρησης	Ε1
ΚΛ-ΚΜ2	ΟΚ	ΚΜ2 split τοίχου 12.000 Btu/h – Υπνοδωμάτιο 1 (πάνω από την πό…	οροφή +2,67 · μονάδα +2,29…+2,58 · πάν…
ΚΡ-ΚΜ2	ΟΚ	ΚΜ2 – ρίψη βόρεια κατά μήκος της ανατολικής πλευράς του κρε…	το κεφαλάρι είναι στο έρκερ (εξωτ. τοίχος …
ΨΣ-ΚΜ2	ΟΚ	ΚΜ2 – ψυκτικά / συμπυκνώματα	ψυκτικά από πίσω μέσα στο υπέρθυρο στο κ…
ΚΛ-ΚΜ3	ΟΚ	ΚΜ3 split τοίχου 9.000 Btu/h – Υπνοδωμάτιο 2 (πάνω από το κεφ…	οροφή +2,67 · μονάδα +2,29…+2,58 · πάνω…
ΚΡ-ΚΜ3	ΟΚ	ΚΜ3 – ρίψη ανατολικά κατά μήκος του κρεβατιού	πάνω από το κεφαλάρι – ο αέρας πέφτει π…
ΨΣ-ΚΜ3	ΟΚ	ΚΜ3 – ψυκτικά / συμπυκνώματα	ψυκτικά από πίσω στο κενό λουτρού → πάν…
ΨΥ-ΚΜ1	ΟΚ	Όδευση ψυκτικών ΚΜ1 χαμήλωση → ντουλάπα χωλ → κενό χωλ…	ελάχιστο 280 mm
ΨΥ-ΚΜ2	ΟΚ	Όδευση ψυκτικών split ΚΜ2 / ΚΜ3 κενό χωλ → λουτρό → Τ1-05	ελάχιστο 280 mm
ΨΥ-ΔΟΚ	ΟΡΙΑΚΟ	Διέλευση ψυκτικών ΚΜ1 κάτω από τη Δ3.1 (x ≈ 5.10, Τ2Ν-01 → ντο…	καθαρό 37.5 mm · περιθώριο +3.6 mm
ΚΔ-ΚΜ1	ΟΚ	Καθιστικό – τραπεζαρία	ΚΜ1 καναλάτη
ΚΔ-ΚΜ2	ΕΓΚΕΚΡ.	Υπνοδωμάτιο 1	ΚΜ2 split τοίχου (ιδιοκτήτης 07/11: «στα δ…
ΚΔ-ΚΜ3	ΕΓΚΕΚΡ.	Υπνοδωμάτιο 2	ΚΜ3 split τοίχου (ιδιοκτήτης 07/11: «στα δ…
ΚΔ-ΚΟΥΖ	ΕΓΚΕΚΡ.	Κουζίνα	από την ΚΜ1 (ανοιχτή στο καθιστικό)
ΣΤ-Π1	ΟΚ	Π1 slot οροφής 2000×120 · 2 σχισμές	μέσα
ΣΤ-Π2	ΟΚ	Π2 slot οροφής 2000×120 · 2 σχισμές	μέσα
SP-Υ1	ΟΚ	Υ1 spot (1.765 · 1.550) – ΥΠΝΟΔΩΜΑΤΙΟ 1	κενό 88 mm · άκρη 0.63
SP-Υ2	ΟΚ	Υ2 spot (3.770 · 1.550) – ΥΠΝΟΔΩΜΑΤΙΟ 1	κενό 88 mm · άκρη 0.75
SP-Υ3	ΟΚ	Υ3 spot (1.765 · 2.650) – ΥΠΝΟΔΩΜΑΤΙΟ 1	κενό 88 mm · άκρη 0.60
SP-Υ4	ΟΚ	Υ4 spot (3.770 · 2.650) – ΥΠΝΟΔΩΜΑΤΙΟ 1	κενό 88 mm · άκρη 0.60
SP-Υ5	ΟΚ	Υ5 spot (7.130 · 1.850) – ΥΠΝΟΔΩΜΑΤΙΟ 2	κενό 88 mm · άκρη 0.50
SP-Υ6	ΟΚ	Υ6 spot (8.530 · 1.850) – ΥΠΝΟΔΩΜΑΤΙΟ 2	κενό 88 mm · άκρη 0.50
SP-Υ7	ΟΚ	Υ7 spot (7.130 · 4.250) – ΥΠΝΟΔΩΜΑΤΙΟ 2	κενό 88 mm · άκρη 0.60
SP-Υ8	ΟΚ	Υ8 spot (8.530 · 4.250) – ΥΠΝΟΔΩΜΑΤΙΟ 2	κενό 88 mm · άκρη 0.60
SP-Λ1	ΟΚ	Λ1 spot IP65 (5.600 · 1.250) – ΛΟΥΤΡΟ	κενό 307 mm · άκρη 0.45
SP-Λ2	ΟΚ	Λ2 spot IP44 (5.600 · 2.050) – ΛΟΥΤΡΟ	κενό 307 mm · άκρη 0.55
SP-Λ3	ΟΚ	Λ3 spot IP44 (5.600 · 2.850) – ΛΟΥΤΡΟ	κενό 307 mm · άκρη 0.40
SP-Λ4	ΟΚ	Λ4 spot IP65 (0.470 · 4.150) – ΛΟΥΤΡΟ ΓΟΝΕΩΝ	κενό 358 mm · άκρη 0.36
SP-Λ5	ΟΚ	Λ5 spot IP44 (1.600 · 4.150) – ΛΟΥΤΡΟ ΓΟΝΕΩΝ	κενό 358 mm · άκρη 0.70
SP-Λ6	ΟΚ	Λ6 spot IP44 (2.500 · 4.150) – ΛΟΥΤΡΟ ΓΟΝΕΩΝ	κενό 358 mm · άκρη 0.65
SP-Χ1	ΟΚ	Χ1 spot (3.650 · 3.850) – ΧΩΛ	κενό 307 mm · άκρη 0.35
SP-Χ2	ΟΚ	Χ2 spot (5.925 · 4.700) – ΧΩΛ	κενό 307 mm · άκρη 0.35
SP-Ε1	ΟΚ	Ε1 spot (8.800 · 5.500) – ΧΑΜΗΛΩΣΗ ΚΑΝΑΛΑΤΟΥ / ΕΙΣΟΔΟΣ	κενό 338 mm · άκρη 0.35
SP-Ε2	ΟΚ	Ε2 spot (8.800 · 6.050) – ΧΑΜΗΛΩΣΗ ΚΑΝΑΛΑΤΟΥ / ΕΙΣΟΔΟΣ	κενό 338 mm · άκρη 0.25
SP-Μ1	ΟΚ	Μ1 spot (10.280 · 8.860) – ΚΟΥΖΙΝΑ	κενό 337 mm · άκρη 0.63
SP-Μ2	ΟΚ	Μ2 spot (11.430 · 8.860) – ΚΟΥΖΙΝΑ	κενό 337 mm · άκρη 1.20
SP-Μ3	ΟΚ	Μ3 spot (12.580 · 8.860) – ΚΟΥΖΙΝΑ	κενό 337 mm · άκρη 0.31
SP-ΚΘ1	ΟΚ	ΚΘ1 spot (2.450 · 7.200) – ΚΑΘΙΣΤΙΚΟ – ΤΡΑΠΕΖΑΡΙΑ	κενό 88 mm · άκρη 0.55
SP-ΚΘ2	ΟΚ	ΚΘ2 spot (2.450 · 8.360) – ΚΑΘΙΣΤΙΚΟ – ΤΡΑΠΕΖΑΡΙΑ	κενό 88 mm · άκρη 0.55
SP-ΚΘ3	ΟΚ	ΚΘ3 spot (3.650 · 8.360) – ΚΑΘΙΣΤΙΚΟ – ΤΡΑΠΕΖΑΡΙΑ	κενό 88 mm · άκρη 0.55
SP-ΚΘ4	ΟΚ	ΚΘ4 spot (4.850 · 8.360) – ΚΑΘΙΣΤΙΚΟ – ΤΡΑΠΕΖΑΡΙΑ	κενό 88 mm · άκρη 0.55
SP-ΚΘ5	ΟΚ	ΚΘ5 spot (6.050 · 8.360) – ΚΑΘΙΣΤΙΚΟ – ΤΡΑΠΕΖΑΡΙΑ	κενό 88 mm · άκρη 0.55
SP-ΚΘ6	ΟΚ	ΚΘ6 spot (7.250 · 8.360) – ΚΑΘΙΣΤΙΚΟ – ΤΡΑΠΕΖΑΡΙΑ	κενό 88 mm · άκρη 0.55
SP-ΚΘ7	ΟΚ	ΚΘ7 spot (8.450 · 8.360) – ΚΑΘΙΣΤΙΚΟ – ΤΡΑΠΕΖΑΡΙΑ	κενό 88 mm · άκρη 0.55
SP-ΚΑΘ	ΟΚ	Καθιστικό – τραπεζαρία	ΚΘ1–ΚΘ7 περιμετρικά (κύκλωμα λ, dimmer)…
ΚΜΣ-ΚΡΕΜ0	ΟΚ	ΚΡΕΜ0 κρεμαστό – τραπέζι σαλονιού	κέντρο (3.35 · 6.85) · Π1 0.60
ΚΜΣ-ΚΡΕΜ1	ΟΚ	ΚΡΕΜ1 κρεμαστό – τραπεζαρία	κέντρο (7.60 · 7.25) · Π2 1.04
ΠΥ-ΑΚ1	ΟΚ	ΑΚ1 καπνού (8.24 · 7.17) – καθιστικό – τραπεζαρία (R05: 0,55 από…	τοίχος 0.87 · ΚΡΕΜ1 0.64 · Π2 1.32
ΠΥ-ΑΚ2	ΟΚ	ΑΚ2 καπνού (2.70 · 2.00) – Υπνοδωμάτιο 1 (R13: ≥ 1,00 από το spli…	τοίχος 1.20 · Υ1 1.04 · ΚΜ2 1.17
ΠΥ-ΑΚ3	ΟΚ	ΑΚ3 καπνού (7.83 · 3.85) – Υπνοδωμάτιο 2 (R13: εκτός ρίψης ΚΜ…	τοίχος 1.00 · Υ8 0.81 · ΚΜ3 1.40
ΠΥ-ΑΚ4	ΟΚ	ΑΚ4 καπνού (5.21 · 3.85) – χωλ – άξονας διαδρόμου 1,00	τοίχος 0.50 · Λ3 1.07 · ΚΜ2 1.31
ΠΥ-ΑΘ5	ΟΚ	ΑΘ5 θερμοδιαφορικός (10.86 · 8.86) – κουζίνα – θερμοδιαφορικό…	τοίχος 0.60 · Μ2 0.57 · Π2 4.41
ΠΥ-ΧΩΡ	ΟΚ	Κάλυψη χώρων	καθιστικό · Υπν.1 · Υπν.2 · χωλ · κουζίνα (θ…
ΘΕ-ΘΕ4	ΟΚ	ΘΕ4 40×40 – λουτρό: ψυκτικά ΚΜ3 / αποχέτευση άνω ορόφου · …	ελεύθερη
ΘΕ-ΘΕ5	ΟΚ	ΘΕ5 40×40 – λουτρό γονέων: αποχέτευση άνω ορόφου (θέση κατ…	ελεύθερη
ΚΡ-ΚΡ1	ΟΚ	ΚΡ1 W2.01 – καθιστικό – Δ · 20 × 10 cm · οδηγοί 7 / 14 cm	πλήρης · βάθος 10 cm
ΚΡ-ΚΡ2	ΟΚ	ΚΡ2 W2.02 – καθιστικό – Ν · 20 × 10 cm · οδηγοί 7 / 14 cm	πλήρης · βάθος 10 cm
ΚΡ-ΚΡ3	ΟΚ	ΚΡ3 W2.08 – Υπν.1 – Δ · 20 × 10 cm · οδηγοί 7 / 14 cm	πλήρης · βάθος 10 cm
ΚΡ-ΚΡ4	ΟΚ	ΚΡ4 W2.06 – Υπν.2 – Α · 22 × 10 cm · οδηγοί 10 / 17 cm (ανοιγοα…	πλήρης · βάθος 10 cm
ΚΡ-W2.03	ΟΚ	W2.03	δεν απαιτείται – κουζίνα – πάνω από τον ν…
ΚΡ-W2.04	ΟΚ	W2.04	δεν απαιτείται – κουζίνα – έρκερ, πάνω από…
ΚΡ-W2.05	ΟΚ	W2.05	δεν απαιτείται – κλιμακοστάσιο (εκτός διαμ…
ΚΡ-W2.07	ΟΚ	W2.07	δεν απαιτείται – λουτρό (στο τοιχείο Κ2)
ΚΡ-W2.09	ΟΚ	W2.09	δεν απαιτείται – λουτρό γονέων (ντους)
ΣΘ-Ζ1	ΟΚ	Ζ1 +2,65 ↔ Ζ2 +2,40	χαμήλωση καναλάτου ΚΜ1 (προδ. 1/5)
ΣΘ-Ζ4	ΟΚ	Ζ4 +2,45 ↔ Ζ2 +2,40	στη γραμμή της Δ3.1 (άνοιγμα χωλ – καθιστι…
ΣΘ-Ζ1	ΟΚ	Ζ1 +2,65 ↔ Ζ3 +2,45	στη γραμμή της δοκού Δ9.1 (περασιά)
ΣΘ-Ζ7	ΟΚ	Ζ7 +2,67 ↔ Ζ8 +2,55	στη γραμμή της δοκού Δ1.1 (κεφαλάρι έρκε…
ΣΘ-Ζ10	ΟΚ	Ζ10 +2,67 ↔ Ζ11 +2,45	σανίδα κάτω από τη Δ3.1 (εξαίρεση προδ. …
ΣΘ-ΣΥΝ	ΟΚ	Στάθμες στο διαμέρισμα	+2.40 · +2.45 · +2.55 · +2.65 · +2.67 (χαμήλ…

B

ΕΡΓΟ

ΠΕΝΤΑΟΡΟΦΟ ΚΤΗΡΙΟ ΚΑΤΟΙΚΙΩΝ – ΑΡΓΥΡΟΥΠΟΛΗ
Κωνσταντινουπόλεως 12 & Αγ. Βαρβάρας · Ο.Τ. 103-15
Εργοδότης: INTERKAT Α.Ε. · Κατασκευή: ARKAD Ι.Κ.Ε.

ΘΕΜΑ ΣΧΕΔΙΟΥ


ΑΝΟΨΗ – ΕΛΕΓΧΟΣ ΠΡΟΔΙΑΓΡΑΦΩΝ
Συμμόρφωση · έλεγχος συγκρούσεων · αλλαγές R13 · ανοικτά σημεία
Α΄ · Β΄ · Γ΄ ΟΡΟΦΟΣ – Β1 (τυπικός όροφος)

ΒΑΣΗ

Βάση: τοιχοποιίες Β1 R25 · ξυλότυπος Σ5 (+9,85) · ανόψη R10

ΑΡ. ΣΧΕΔΙΟΥ

ΑΝ-08
—
07/11/2026 · R13

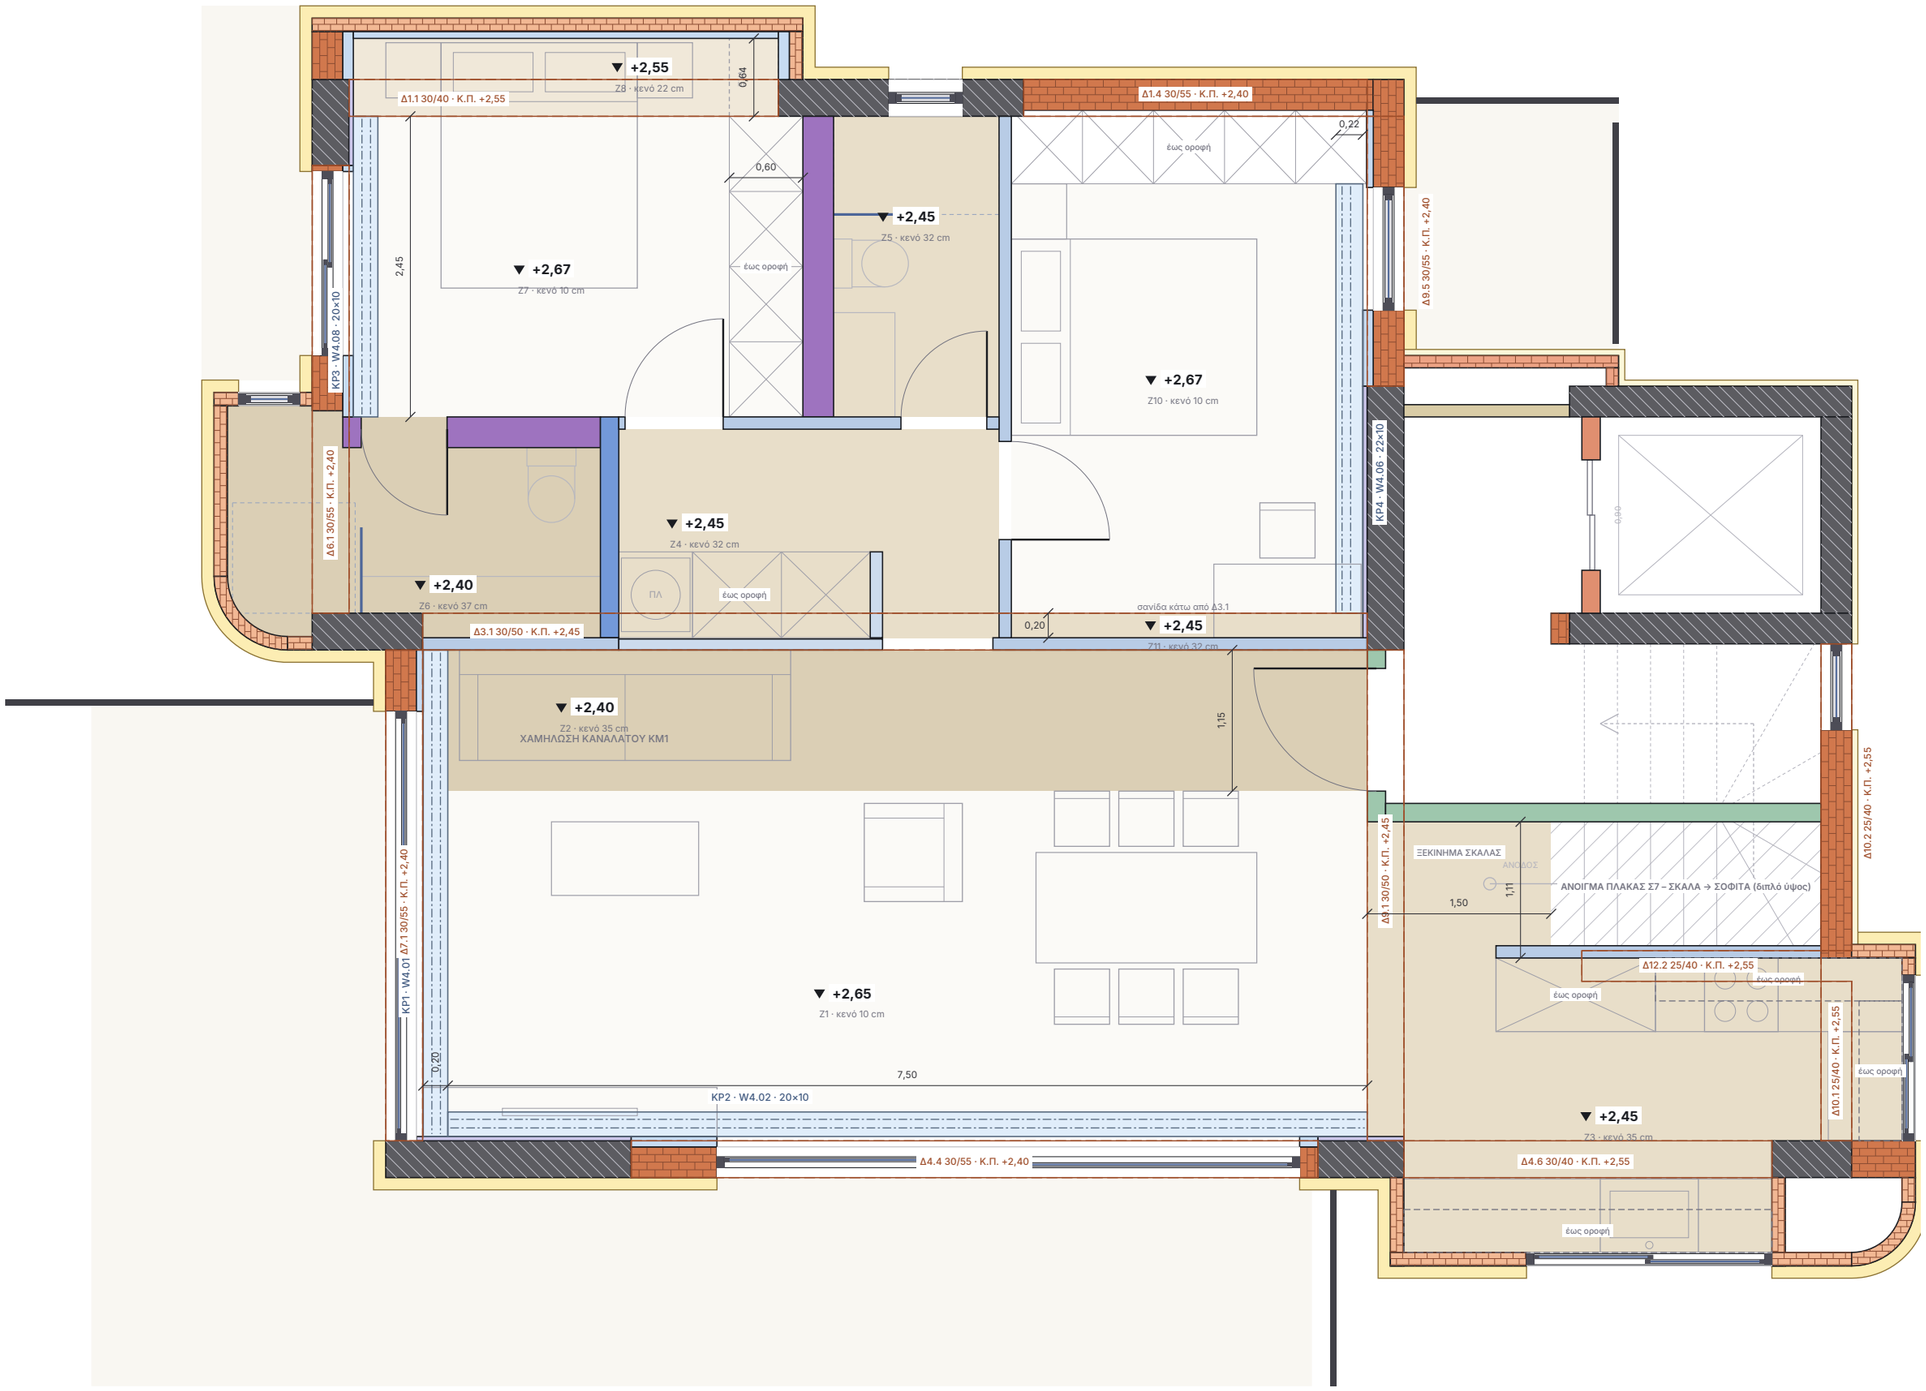

ΣΗΜΕΙΩΣΕΙΣ

Στάθμες από το τελικό δάπεδο του Δ΄ (+13,10). Πάνω παρειά πλάκας Σ7 +2,95 (+16,05)· κάτω παρειά Π3 h18 +2,77 · Π8 h20 +2,75 · Π10 h15 +2,80 (όπως Σ5 – Α4).

Ίδιο διαμέρισμα με το Β1: ίδιες στάθμες R13 (καθιστικό +2,65 · χαμήλωση ΚΜ1 +2,40 · κουζίνα / χωλ / λουτρό +2,45 · λουτρό γονέων +2,40 · υπνοδωμάτια +2,67 χωρίς κουτιά).

Ξεκίνημα ιδιωτικής σκάλας 9,40–10,90: +2,45 ενιαίο με την κουζίνα, περασιά με τη Δ9.1. Στο 10,90 τελειώνει η ψευδοροφή στο άνοιγμα της πλάκας (γωνιόκρανο) – βλ. Α3.


Κουρτινόθηκες ΚΡ1–ΚΡ4: 20 × 10 cm (ΚΡ4 22), όπως Β1.

Πάνω από το Υπν.2: λουτρό / WC σοφίτας (Α5) · πάνω από καθιστικό / κουζίνα / Υπν.1: δώμα (Α6).

ΥΠΟΜΝΗΜΑ

- +2,65 / +2,67 βασική = 10 cm κάτω από την πλάκα (spot σώμα ≤ 75 mm)
- +2,55 περασιά με δοκό 40 (κεφαλάρι Υπν.1)
- +2,45 περασιά με δοκό 50: χωλ · λουτρό · κουζίνα · ξεκίνημα σκάλας
- +2,40 χαμήλωση ΚΜ1 (5 cm κάτω από Δ3.1 – ψυκτικά) · λουτρό γονέων (περασιά Δ6.1)
- ΚΡ εσοχή κουρτίνας ανοιχτή ως την πλάκα · 2 οδηγοί
- δοκός (Σ7) · Κ.Π. = κάτω παρειά από Τ.Δ.

ΕΡΓΟ	ΘΕΜΑ ΣΧΕΔΙΟΥ	ΒΑΣΗ	ΑΡ. ΣΧΕΔΙΟΥ
ΠΕΝΤΑΟΡΟΦΟ ΚΤΗΡΙΟ ΚΑΤΟΙΚΙΩΝ – ΑΡΓΥΡΟΥΠΟΛΗ Κωνσταντινουπόλεως 12 & Αγ. Βαρβάρας · Ο.Τ. 103-15 Εργοδότης: INTERKAT Α.Ε. · Κατασκευή: ARKAD Ι.Κ.Ε.	**ΑΝΟΨΗ – ΣΤΑΘΜΕΣ · ΔΟΚΟΙ · ΚΟΥΡΤΙΝΕΣ** Στάθμες ψευδοροφής · δοκοί Σ7 · εσοχές κουρτινών · ξεκίνημα σκάλας Δ΄ ΟΡΟΦΟΣ – Δ1 κάτω επίπεδο (μεζονέτα)	Βάση: τοιχοποιίες Δ΄ R04 · ξυλότυπος Σ7_ΕΦ (+16,05) · ανόψη Β1 R13	**ΑΝ-09** **Κλίμακα 1:50 · Α3** 07/11/2026 · R02

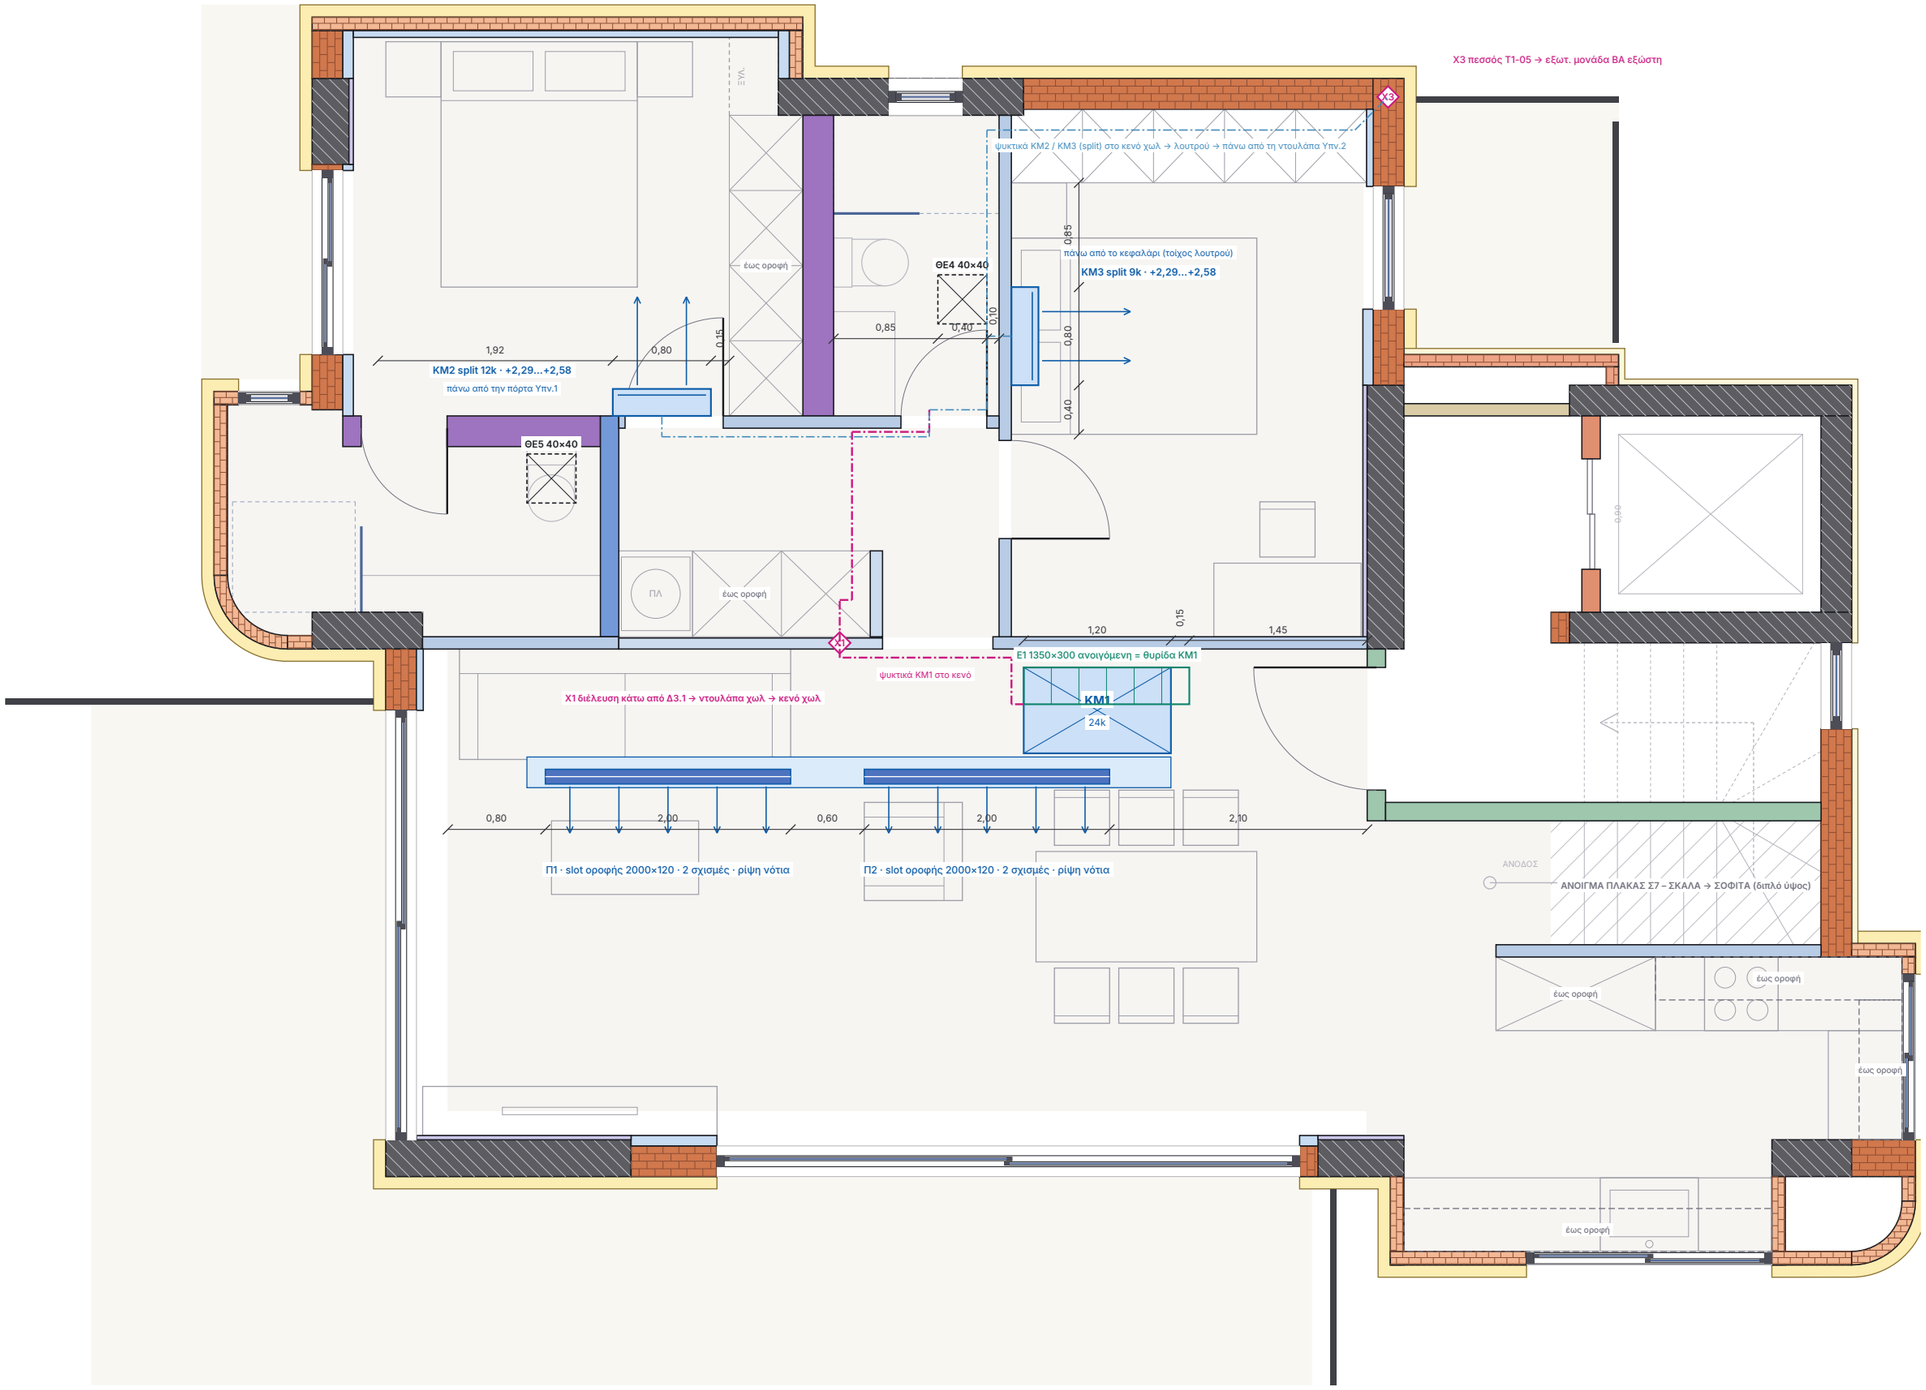

ΣΗΜΕΙΩΣΕΙΣ

Χώρος ΚΜ1 (προδ. 1): χαμήλωση +2,40 κάτω από Π8 +2,75 = 35 cm → 245 + 10 + 40 = 295 → περιθώριο 55 mm. Πρόσβαση από την ανοιγόμενη Ε1.

R13 – ΥΠΝΟΔΩΜΑΤΙΑ ΜΕ SPLIT (ιδιοκτήτης 07/11: «στα δωμάτια δεν θα βάζουμε καναλάτο, θα βάζουμε split σε ένα σημείο που θα βρεις»). Κανόνας θέσης: ψηλά σε εσωτερικό τοίχο, ρίψη κατά μήκος του δωματίου που δεν πέφτει στο προσκέφαλο, ψυκτικά κατευθείαν στο κενό χωλ / λουτρού.

ΚΜ2 12k Υπν.1: ΠΑΝΩ ΑΠΟ ΤΗΝ ΠΟΡΤΑ (3,25–4,05 · +2,29…+2,58, 9 cm από την οροφή +2,67, 4 cm πάνω από την κάσα 2,25). Το κεφαλάρι είναι στο έρκερ (εξωτερικός τοίχος, LED3, Δ1.1 – χωρίς κενό για ψυκτικά) → ο αέρας ρίχνεται βόρεια δίπλα από την ανατολική πλευρά του κρεβατιού.

ΚΜ3 9k Υπν.2: ΠΑΝΩ ΑΠΟ ΤΟ ΚΕΦΑΛΑΡΙ στον τοίχο λουτρού Τ2-02 (2,20–3,00 · +2,29…+2,58), ρίψη ανατολικά προς τα πόδια και το W2.06.

Ψυκτικά split: από πίσω από τη μονάδα μέσα στον γυψότοιχο / υπέρθυρο ως το κενό χωλ (+2,45) / λουτρού → μαζί με την ΚΜ1 → πάνω από τη ντουλάπα Υπν.2 → πεσσός Τ1-05 → εξωτερική μονάδα ΒΑ εξώστη. Συμπυκνώματα με φυσική ροή μέσα στον γυψότοιχο στα σιφώνια των λουτρών (ΚΜ2 → Τ2Α-01 / λουτρό γονέων · ΚΜ3 → Τ2-02 / λουτρό) – χωρίς αντλία.

Ψυκτικά ΚΜ1 (R12, ιδιοκτήτης: «μέσω οροφής και ντουλάπας χωλ»): Χ1 κάτω από τη Δ3.1 μέσα από τον Τ2Ν-01 στη ντουλάπα χωλ (x ≈ 5,10) → κενό χωλ → λουτρό → Τ1-05. ΟΡΙΑΚΟ: καθαρό 37,5 mm → αερίου 5/8″ με μόνωση 9 mm χωράει, 13 mm όχι. Καμία οπή σε δοκό.

Στήριξη split σε γυψότοιχο: ενίσχυση (OSB 18 ή UA) πίσω από τη βάση της μονάδας / στο υπέρθυρο.

Εξωτερική μονάδα στον ΒΑ εξώστη του Δ΄ (όπως Β1)· συμπυκνώματα με αντλία → σιφώνι / υδρορροή εξώστη (επιβεβαίωση υδραυλικού).

ΥΠΟΜΝΗΜΑ

- ΚΜ1 καναλάτη μονάδα (slim ≤ 245 mm)
- ΚΜ2 / ΚΜ3 split τοίχου (σώμα στον τοίχο, βέλη = ρίψη)
- αεραγωγός / plenum προσαγωγής (μονωμένος, στο κενό)
- Π1 / Π2 γραμμικό slot οροφής 2 σχισμών, ρυθμιζόμενη ρίψη
- Ε στόμιο / κιβώτιο επιστροφής με φίλτρο
- ΘΕ θυρίδα επίσκεψης (αφανής, βαφόμενη)
- Χ κατέβασμα / έξοδος σωληνώσεων – καμία οπή σε σκυρόδεμα

ΕΡΓΟ	ΘΕΜΑ ΣΧΕΔΙΟΥ	ΒΑΣΗ	ΑΡ. ΣΧΕΔΙΟΥ
ΠΕΝΤΑΟΡΟΦΟ ΚΤΗΡΙΟ ΚΑΤΟΙΚΙΩΝ – ΑΡΓΥΡΟΥΠΟΛΗ Κωνσταντινουπόλεως 12 & Αγ. Βαρβάρας · Ο.Τ. 103-15 Εργοδότης: INTERKAT Α.Ε. · Κατασκευή: ARKAD Ι.Κ.Ε.	**ΑΝΟΨΗ – ΚΛΙΜΑΤΙΣΜΟΣ · ΘΥΡΙΔΕΣ** Καναλάτη ΚΜ1 · split υπνοδωματίων · slot · θυρίδα · ψυκτικά Δ΄ ΟΡΟΦΟΣ – Δ1 κάτω επίπεδο (μεζονέτα)	Βάση: τοιχοποιίες Δ΄ R04 · ξυλότυπος Σ7_ΕΦ (+16,05) · ανόψη Β1 R13	**ΑΝ-10** **Κλίμακα 1:50 · Α3** 07/11/2026 · R02



ΣΗΜΕΙΩΣΕΙΣ

Κατανομή όπως Β1 R13: Υπν. 2 × 2 spots · λουτρά 3 (IP65 στο ντους) · κουζίνα 3 γενικός + LED4 κάτω από τα ντουλάπια · χωλ / είσοδος · καθιστικό ΚΘ1–ΚΘ7 περιμετρικά + ΚΡΕΜ0 στο κέντρο του τραπεζιού σαλονιού · + ΣΚ1 στο ξεκίνημα της σκάλας. Σύνολο 29 spots + 2 κρεμαστά + LED3 + LED4.

Σκάλα προς σοφίτα: φωτιστικά τοίχου / σκαλοπατιών (ηλεκτρολογικά) – ανιχνευτής καπνού στο πλατύσκαλο της σοφίτας (ανόψη σοφίτας).

Πυρανίχνευση (προδ. 4): σε κάθε κύριο χώρο και στο χωλ· ≥ 0,50 από τοίχους / δοκούς / φωτιστικά, ≥ 1,00 από στόμια προσαγωγής / split· λουτρά χωρίς ανιχνευτή καπνού.

Οπή spot Ø 75–80 ανάμεσα στα προφίλ CD (όχι πάνω τους)· όπου πέφτει σε προφίλ, μετατόπιση του προφίλ – όχι του spot.

ΥΠΟΜΝΗΜΑ

- χωνευτό spot LED 7–9 W, 2700 K, CRI ≥ 90, UGR < 19, σώμα ≤ 75 mm
- χωνευτό spot IP44 (λουτρά)
- χωνευτό spot IP65 (πάνω από ντους)
- split τοίχου (για συντονισμό – βλ. φύλλο κλιματισμού)
- ΚΡΕΜ παροχή οροφής (κουτί + ενίσχυση ανάρτησης)
- ΑΚ ανιχνευτής καπνού (ΕΠ04 · EN 54-7)
- ΑΘ θερμοδιαφορικός ανιχνευτής (κουζίνα · EN 54-5)
- ακτίνα 0,50 m γύρω από ανιχνευτή – κανένας τοίχος / φωτιστικό μέσα
- LED κρυφό γραμμικό 3000 K – LED3 κεφαλάρι · LED4 κάτω από τα ντουλάπια κουζίνας

ΕΡΓΟ	ΘΕΜΑ ΣΧΕΔΙΟΥ	ΒΑΣΗ	ΑΡ. ΣΧΕΔΙΟΥ
ΠΕΝΤΑΟΡΟΦΟ ΚΤΗΡΙΟ ΚΑΤΟΙΚΙΩΝ – ΑΡΓΥΡΟΥΠΟΛΗ Κωνσταντινουπόλεως 12 & Αγ. Βαρβάρας · Ο.Τ. 103-15 Εργοδότης: INTERKAT Α.Ε. · Κατασκευή: ARKAD Ι.Κ.Ε.	**ΑΝΟΨΗ – ΦΩΤΙΣΜΟΣ · ΠΥΡΑΝΙΧΝΕΥΣΗ** Χωνευτά spots · παροχές · κρυφό LED · ανιχνευτές Δ΄ ΟΡΟΦΟΣ – Δ1 κάτω επίπεδο (μεζονέτα)	Βάση: τοιχοποιίες Δ΄ R04 · ξυλότυπος Σ7_ΕΦ (+16,05) · ανόψη Β1 R13	**ΑΝ-11** **Κλίμακα 1:50 · Α3** 07/11/2026 · R02

ΣΥΜΜΟΡΦΩΣΗ ΜΕ ΤΙΣ ΠΡΟΔΙΑΓΡΑΦΕΣ (ιδιοκτήτης 07/11/2026)

1 Κλιματισμός	Όπως B1 R13: καναλάτη ΚΜ1 24k καθιστικό / κουζίνα (ΕΓΚΕΚΡ.) με slot Π1/Π2 · split τοίχου ΚΜ2 / ΚΜ3 στα υπνοδωμάτια (ιδιοκτήτης 07/11 – ΕΓΚΕΚΡ.) · χώρος 35 cm · θυρίδα Ε1 · ψυκτικά ΚΜ1 κάτω από τη Δ3.1 (οριακό 3,6 mm).
2 Κουρτίνες	ΚΡ1–ΚΡ4 σε όλα τα ανοίγματα καθιστικού / υπνοδωματίων (W4.01, W4.02, W4.08, W4.06), 20 (22) × 10 cm, ανοιχτές ως την πλάκα.
3 Φωτισμός	29 χωνευτά spots (B1 R13 + ΣΚ1 σκάλας) + ΚΡΕΜ0 / ΚΡΕΜ1 + LED3 / LED4 · κανένα spot κάτω από μονάδα / αεραγωγό / σε θυρίδα / πάνω από ντουλάπι · κενό ≥ 88 mm.
4 Πυρανίχνευση	ΑΚ1–ΑΚ4 καπνού + ΑΘ5 θερμοδιαφορικός κουζίνας · σκάλα: ανιχνευτής στο πλατύσκαλο σοφίτας.
5 Κατασκευή	Όπως B1 · το ξεκίνημα της σκάλας ενιαίο με την κουζίνα +2,45 (περασιά Δ9.1) · ακμή στο άνοιγμα της πλάκας με γωνιόκρανο.
6 Γενική αρχή	5 στάθμες, κάθε αλλαγή πάνω σε γραμμή δοκού – όπως B1· υπνοδωμάτια ενιαία +2,67.

ΕΓΚΕΚΡΙΜΕΝΑ / ΑΠΟΦΑΣΕΙΣ ΙΔΙΟΚΤΗΤΗ (07/11/2026)

- Υπνοδωμάτια με split τοίχου αντί καναλάτου (R13: «στα δωμάτια δεν θα βάζουμε καναλάτο, θα βάζουμε split»).
- Κουζίνα χωρίς δική της καναλάτη – καλύπτεται από την ΚΜ1 24k.
- Μονάδα ΚΜ1 slim ≤ 245 mm ως παραδοχή μέχρι την επιλογή μοντέλου.
- Η απόφαση R02 «καθιστικό χωρίς spots» αναθεωρείται (R13: «σκέψου μήπως βάλουμε και spot») – τα ΚΘ1–ΚΘ7 είναι πρόταση (Α6).

ΑΛΛΑΓΕΣ R01 → R02 · ΔΙΑΦΟΡΕΣ ΑΠΟ ΤΟ B1 R13 (07/11/2026)

- R02 = B1 R13 (ιδιοκτήτης 07/11): υπνοδωμάτια με split τοίχου – ΚΜ2 πάνω από την πόρτα Υπν.1, ΚΜ3 πάνω από το κεφαλάρι Υπν.2 (τοίχος λουτρού), ψυκτικά στο κενό χωλ / λουτρού → Τ1-05 · καταργήθηκαν καναλάτες ΚΜ2 / ΚΜ3, Π3 / Π4, ΘΕ2 / ΘΕ3, κουτί ντουλάπας Υπν.1 · ΚΡΕΜ0 στο κέντρο του τραπεζιού σαλονιού + ΚΘ1–ΚΘ7 περιμετρικά στις τζαμαρίες.
- Διαφορές από το B1 (από το R01): χωμλώση ΚΜ1 +2,40, ψυκτικά κάτω από τη Δ3.1 στη ντουλάπα χωλ, κουζίνα με επάνω ντουλάπια και LED4, χωρίς Wi-Fi – όπως B1.
- Ξεκίνημα ιδιωτικής σκάλας 9,40–10,90 × 6,55–7,66 στη στάθμη της κουζίνας +2,45 (περασιά με τη Δ9.1 – η γραμμή της δοκού χωρίζει καθιστικό +2,65 και κουζίνα / σκάλα +2,45)· ανατολικά του 10,90 το άνοιγμα της πλάκας Σ7 (χωρίς ψευδοροφή, ακμή με γωνιόκρανο). Spot ΣΚ1 στο κέντρο του πλατύσκαλου.
- Δ12.2 του Σ7 από x 11,15 (στο B1 από 9,70) – κρυμμένη πάνω από την κουζίνα +2,45.

ΠΡΟΗΓΟΥΜΕΝΗ ΑΝΑΘΕΩΡΗΣΗ

- R01: = B1 R12 (καναλάτες σε όλα τα δωμάτια, καθιστικό χωρίς spots) + ξεκίνημα σκάλας.

ΑΝΟΙΚΤΑ ΣΗΜΕΙΑ


- Α1 [ΚΑΤΑΣΚΕΥΗ] Διέλευση ψυκτικών ΚΜ1 κάτω από τη Δ3.1 όπως B1: καθαρό 37,5 mm → αερίου 5/8'' με μόνωση 9 mm χωράει, με 13 mm όχι (τότε χαμήλωση +2,38).
- Α2 [ΜΟΝΤΕΛΟ] ΚΜ1 ≤ 245 mm (θέση ηλεκτρικού κουτιού) · split ΚΜ2 / ΚΜ3 ≤ 290 × 800 mm – όπως B1.
- Α7 [ΑΠΟΦΑΣΗ] Όπως B1 Α5 / Α6: πόρτα Υπν.1 ≤ 2,20 (το split ΚΜ2 είναι πάνω από την πόρτα) · spots καθιστικού ΚΘ1–ΚΘ7 = πρόταση.
- Α3 [ΣΤΑΤΙΚΟΣ] Δοκός / ακμή πλάκας Σ7 στο x 10,90–11,15 (κάτω από το Δ τοιχείο του κλιμακοστασίου της σοφίτας): η ψευδοροφή +2,45 του ξεκινήματος της σκάλας τελειώνει εκεί – η κάτω παρειά της δοκού πρέπει να είναι ≥ +2,45 (διατομή ≤ 50 cm).
- Α4 [ΣΤΑΤΙΚΟΣ] Δοκοί Σ7_ΕΦ στη ζώνη του διαμερίσματος: θεωρήθηκαν ίδιοι με τον Σ5 (ο έλεγχος της 07/11 έγινε μόνο στη ζώνη της σκάλας) – επιβεβαίωση πριν τη σκυροδέτηση του Σ7· και μέτρηση μετά το ξεκαλούπωμα.
- Α5 [ΑΠΟΦΑΣΗ] Λουτρό / WC σοφίτας πάνω από το Υπν.2 (και τη ντουλάπα του): η ανόψη κρατά το Υπν.2 +2,67 (κενό 10 cm) θεωρώντας ότι τα οριζόντια της αποχέτευσης μπαίνουν στην επίστρωση της σοφίτας (15 cm) και οι στήλες κατεβαίνουν μέσα στη ντουλάπα Υπν.2 (έως οροφή). Αν ο υδραυλικός τις φέρει από κάτω → χαμήλωση Υπν.2 στο +2,45 (κενό 32 cm, περασιά Δ3.1) – να αποφασιστεί στις αποχετεύσεις.
- Α6 [ΣΥΝΤΟΝΙΣΜΟΣ] Δώμα πάνω από καθιστικό / κουζίνα / Υπν.1: οι υδρορροές του δώματος κατεβαίνουν κατακόρυφα στις όψεις / εξώστες – καμία οριζόντια όδευση στο κενό 10 cm του καθιστικού. Κουτιά οροφής και σωληνώσεις ανιχνευτών μέσα στην ψευδοροφή (όχι στη μόνωση δώματος).

ΕΛΕΓΧΟΣ ΣΥΓΚΡΟΥΣΕΩΝ & ΣΤΑΘΜΩΝ – 81 έλεγχοι · ΟΚ 77 · ΟΡΙΑΚΟ 1 · ΕΓΚΕΚΡ. 3 · ΑΠΟΚΛΙΣΗ 0

Αυτόματος έλεγχος από το μοντέλο (code/anopseis/checks.py): στάθμες ↔ δοκοί · κενό μονάδων · θυρίδες · spots ↔ ζώνες / θυρίδες / μονάδες / αεραγωγοί / κουρτινόθηκες · ανιχνευτές ↔ τοίχοι / φωτιστικά / στόμια · κουρτινόθηκες ↔ κουφώματα / δοκοί.

ΚΩΔ.	ΚΑΤΑΣΤ.	ΣΤΟΙΧΕΙΟ	ΜΕΤΡΗΣΗ
ΣΤ01	ΟΚ	Z3 ΚΟΥΖΙΝΑ – ΞΕΚΙΝΗΜΑ ΣΚΑΛΑΣ ↔ Δ9.1 30/50 (Κ.Π. +2.45)	οροφή +2.45 · περασιά
ΣΤ02	ΟΚ	Z3 ΚΟΥΖΙΝΑ – ΞΕΚΙΝΗΜΑ ΣΚΑΛΑΣ ↔ Δ4.6 30/40 (Κ.Π. +2.55)	οροφή +2.45 · κρυμμένη 10 cm
ΣΤ03	ΟΚ	Z3 ΚΟΥΖΙΝΑ – ΞΕΚΙΝΗΜΑ ΣΚΑΛΑΣ ↔ Δ12.2 25/40 (Κ.Π. +2.55)	οροφή +2.45 · κρυμμένη 10 cm
ΣΤ04	ΟΚ	Z3 ΚΟΥΖΙΝΑ – ΞΕΚΙΝΗΜΑ ΣΚΑΛΑΣ ↔ Δ10.1 25/40 (Κ.Π. +2.55)	οροφή +2.45 · κρυμμένη 10 cm
ΣΤ05	ΟΚ	Z4 ΧΩΛ ↔ Δ3.1 30/50 (Κ.Π. +2.45)	οροφή +2.45 · περασιά
ΣΤ06	ΟΚ	Z6 ΛΟΥΤΡΟ ΓΟΝΕΩΝ ↔ Δ6.1 30/55 (Κ.Π. +2.40)	οροφή +2.40 · περασιά
ΣΤ07	ΟΚ	Z6 ΛΟΥΤΡΟ ΓΟΝΕΩΝ ↔ Δ3.1 30/50 (Κ.Π. +2.45)	οροφή +2.40 · κρυμμένη 5 cm
ΣΤ08	ΟΚ	Z8 ΚΕΦΑΛΑΡΙ ΥΠΝ.1 (έρκερ) ↔ Δ1.1 30/40 (Κ.Π. +2.55)	οροφή +2.55 · περασιά
ΣΤ09	ΟΚ	Z11 ΣΑΝΙΔΑ ΚΑΤΩ ΑΠΟ Δ3.1 (Υπν.2) ↔ Δ3.1 30/50 (Κ.Π. +2.45)	οροφή +2.45 · περασιά
ΚΛ-ΚΜ1	ΟΚ	ΚΜ1 24.000 Btu/h – καθιστικό – τραπεζαρία – κουζίνα	κενό 350 mm · περιθώριο +55 mm
ΘΕ-ΚΜ1	ΟΚ	ΚΜ1 – πρόσβαση συντήρησης	Ε1
ΚΛ-ΚΜ2	ΟΚ	ΚΜ2 split τοίχου 12.000 Btu/h – Υπνοδωμάτιο 1 (πάνω από την πό…	οροφή +2,67 · μονάδα +2,29…+2,58 · πάν…
ΚΡ-ΚΜ2	ΟΚ	ΚΜ2 – ρίψη βόρεια κατά μήκος της ανατολικής πλευράς του κρε…	το κεφαλάρι είναι στο έρκερ (εξωτ. τοίχος …
ΨΣ-ΚΜ2	ΟΚ	ΚΜ2 – ψυκτικά / συμπυκνώματα	ψυκτικά από πίσω μέσα στο υπέρθυρο στο κ…
ΚΛ-ΚΜ3	ΟΚ	ΚΜ3 split τοίχου 9.000 Btu/h – Υπνοδωμάτιο 2 (πάνω από το κεφ…	οροφή +2,67 · μονάδα +2,29…+2,58 · πάνω…
ΚΡ-ΚΜ3	ΟΚ	ΚΜ3 – ρίψη ανατολικά κατά μήκος του κρεβατιού	πάνω από το κεφαλάρι – ο αέρας πέφτει π…
ΨΣ-ΚΜ3	ΟΚ	ΚΜ3 – ψυκτικά / συμπυκνώματα	ψυκτικά από πίσω στο κενό λουτρού → πάν…
ΨΥ-ΚΜ1	ΟΚ	Όδευση ψυκτικών ΚΜ1 χαμήλωση → ντουλάπα χωλ → κενό χωλ…	ελάχιστο 280 mm
ΨΥ-ΚΜ2	ΟΚ	Όδευση ψυκτικών split ΚΜ2 / ΚΜ3 κενό χωλ → λουτρό → Τ1-05	ελάχιστο 280 mm
ΨΥ-ΔΟΚ	ΟΡΙΑΚΟ	Διέλευση ψυκτικών ΚΜ1 κάτω από τη Δ3.1 (x ≈ 5.10, T2N-01 → ντο…	καθαρό 37.5 mm · περιθώριο +3.6 mm
ΚΔ-ΚΜ1	ΟΚ	Καθιστικό – τραπεζαρία	ΚΜ1 καναλάτη
ΚΔ-ΚΜ2	ΕΓΚΕΚΡ.	Υπνοδωμάτιο 1	ΚΜ2 split τοίχου (ιδιοκτήτης 07/11: «στα δ…
ΚΔ-ΚΜ3	ΕΓΚΕΚΡ.	Υπνοδωμάτιο 2	ΚΜ3 split τοίχου (ιδιοκτήτης 07/11: «στα δ…
ΚΔ-ΚΟΥΖ	ΕΓΚΕΚΡ.	Κουζίνα	από την ΚΜ1 (ανοιχτή στο καθιστικό)
ΣΤ-Π1	ΟΚ	Π1 slot οροφής 2000×120 · 2 σχισμές	μέσα
ΣΤ-Π2	ΟΚ	Π2 slot οροφής 2000×120 · 2 σχισμές	μέσα
SP-Υ1	ΟΚ	Υ1 spot (1.765 · 1.550) – ΥΠΝΟΔΩΜΑΤΙΟ 1	κενό 88 mm · άκρη 0.63
SP-Υ2	ΟΚ	Υ2 spot (3.770 · 1.550) – ΥΠΝΟΔΩΜΑΤΙΟ 1	κενό 88 mm · άκρη 0.75
SP-Υ3	ΟΚ	Υ3 spot (1.765 · 2.650) – ΥΠΝΟΔΩΜΑΤΙΟ 1	κενό 88 mm · άκρη 0.60
SP-Υ4	ΟΚ	Υ4 spot (3.770 · 2.650) – ΥΠΝΟΔΩΜΑΤΙΟ 1	κενό 88 mm · άκρη 0.60
SP-Υ5	ΟΚ	Υ5 spot (7.130 · 1.850) – ΥΠΝΟΔΩΜΑΤΙΟ 2	κενό 88 mm · άκρη 0.50
SP-Υ6	ΟΚ	Υ6 spot (8.530 · 1.850) – ΥΠΝΟΔΩΜΑΤΙΟ 2	κενό 88 mm · άκρη 0.50
SP-Υ7	ΟΚ	Υ7 spot (7.130 · 4.250) – ΥΠΝΟΔΩΜΑΤΙΟ 2	κενό 88 mm · άκρη 0.60
SP-Υ8	ΟΚ	Υ8 spot (8.530 · 4.250) – ΥΠΝΟΔΩΜΑΤΙΟ 2	κενό 88 mm · άκρη 0.60
SP-Λ1	ΟΚ	Λ1 spot IP65 (5.600 · 1.250) – ΛΟΥΤΡΟ	κενό 307 mm · άκρη 0.45
SP-Λ2	ΟΚ	Λ2 spot IP44 (5.600 · 2.050) – ΛΟΥΤΡΟ	κενό 307 mm · άκρη 0.55
SP-Λ3	ΟΚ	Λ3 spot IP44 (5.600 · 2.850) – ΛΟΥΤΡΟ	κενό 307 mm · άκρη 0.40
SP-Λ4	ΟΚ	Λ4 spot IP65 (0.470 · 4.150) – ΛΟΥΤΡΟ ΓΟΝΕΩΝ	κενό 358 mm · άκρη 0.36
SP-Λ5	ΟΚ	Λ5 spot IP44 (1.600 · 4.150) – ΛΟΥΤΡΟ ΓΟΝΕΩΝ	κενό 358 mm · άκρη 0.70
SP-Λ6	ΟΚ	Λ6 spot IP44 (2.500 · 4.150) – ΛΟΥΤΡΟ ΓΟΝΕΩΝ	κενό 358 mm · άκρη 0.65
SP-X1	ΟΚ	X1 spot (3.650 · 3.850) – ΧΩΛ	κενό 307 mm · άκρη 0.35
SP-X2	ΟΚ	X2 spot (5.925 · 4.700) – ΧΩΛ	κενό 307 mm · άκρη 0.35
SP-Ε1	ΟΚ	Ε1 spot (8.800 · 5.500) – ΧΑΜΗΛΩΣΗ ΚΑΝΑΛΑΤΟΥ / ΕΙΣΟΔΟΣ	κενό 338 mm · άκρη 0.35
SP-Ε2	ΟΚ	Ε2 spot (8.800 · 6.050) – ΧΑΜΗΛΩΣΗ ΚΑΝΑΛΑΤΟΥ / ΕΙΣΟΔΟΣ	κενό 338 mm · άκρη 0.25
SP-Μ1	ΟΚ	Μ1 spot (10.280 · 8.860) – ΚΟΥΖΙΝΑ – ΞΕΚΙΝΗΜΑ ΣΚΑΛΑΣ	κενό 337 mm · άκρη 0.63
SP-Μ2	ΟΚ	Μ2 spot (11.430 · 8.860) – ΚΟΥΖΙΝΑ – ΞΕΚΙΝΗΜΑ ΣΚΑΛΑΣ	κενό 337 mm · άκρη 1.20
SP-Μ3	ΟΚ	Μ3 spot (12.580 · 8.860) – ΚΟΥΖΙΝΑ – ΞΕΚΙΝΗΜΑ ΣΚΑΛΑΣ	κενό 337 mm · άκρη 0.31
SP-ΚΘ1	ΟΚ	ΚΘ1 spot (2.450 · 7.200) – ΚΑΘΙΣΤΙΚΟ – ΤΡΑΠΕΖΑΡΙΑ	κενό 88 mm · άκρη 0.55
SP-ΚΘ2	ΟΚ	ΚΘ2 spot (2.450 · 8.360) – ΚΑΘΙΣΤΙΚΟ – ΤΡΑΠΕΖΑΡΙΑ	κενό 88 mm · άκρη 0.55
SP-ΚΘ3	ΟΚ	ΚΘ3 spot (3.650 · 8.360) – ΚΑΘΙΣΤΙΚΟ – ΤΡΑΠΕΖΑΡΙΑ	κενό 88 mm · άκρη 0.55
SP-ΚΘ4	ΟΚ	ΚΘ4 spot (4.850 · 8.360) – ΚΑΘΙΣΤΙΚΟ – ΤΡΑΠΕΖΑΡΙΑ	κενό 88 mm · άκρη 0.55
SP-ΚΘ5	ΟΚ	ΚΘ5 spot (6.050 · 8.360) – ΚΑΘΙΣΤΙΚΟ – ΤΡΑΠΕΖΑΡΙΑ	κενό 88 mm · άκρη 0.55
SP-ΚΘ6	ΟΚ	ΚΘ6 spot (7.250 · 8.360) – ΚΑΘΙΣΤΙΚΟ – ΤΡΑΠΕΖΑΡΙΑ	κενό 88 mm · άκρη 0.55
SP-ΚΘ7	ΟΚ	ΚΘ7 spot (8.450 · 8.360) – ΚΑΘΙΣΤΙΚΟ – ΤΡΑΠΕΖΑΡΙΑ	κενό 88 mm · άκρη 0.55
SP-ΣΚ1	ΟΚ	ΣΚ1 spot (10.150 · 7.100) – ΚΟΥΖΙΝΑ – ΞΕΚΙΝΗΜΑ ΣΚΑΛΑΣ	κενό 337 mm · άκρη 0.55
SP-ΚΑΘ	ΟΚ	Καθιστικό – τραπεζαρία	ΚΘ1–ΚΘ7 περιμετρικά (κύκλωμα λ, dimmer)…
ΚΜΣ-ΚΡΕΜ0	ΟΚ	ΚΡΕΜ0 κρεμαστό – τραπέζι σαλονιού	κέντρο (3.35 · 6.85) · Π1 0.60
ΚΜΣ-ΚΡΕΜ1	ΟΚ	ΚΡΕΜ1 κρεμαστό – τραπεζαρία	κέντρο (7.60 · 7.25) · Π2 1.04
ΠΥ-ΑΚ1	ΟΚ	ΑΚ1 καπνού (8.24 · 7.17) – καθιστικό – τραπεζαρία (R05: 0,55 από…	τοίχος 0.87 · ΚΡΕΜ1 0.64 · Π2 1.32
ΠΥ-ΑΚ2	ΟΚ	ΑΚ2 καπνού (2.70 · 2.00) – Υπνοδωμάτιο 1 (R13: ≥ 1,00 από το spli…	τοίχος 1.20 · Υ1 1.04 · ΚΜ2 1.17
ΠΥ-ΑΚ3	ΟΚ	ΑΚ3 καπνού (7.83 · 3.85) – Υπνοδωμάτιο 2 (R13: εκτός ρίψης ΚΜ…	τοίχος 1.00 · Υ8 0.81 · ΚΜ3 1.40
ΠΥ-ΑΚ4	ΟΚ	ΑΚ4 καπνού (5.21 · 3.85) – χωλ – άξονας διαδρόμου 1,00	τοίχος 0.50 · Λ3 1.07 · ΚΜ2 1.31
ΠΥ-ΑΘ5	ΟΚ	ΑΘ5 θερμοδιαφορικός (10.86 · 8.86) – κουζίνα – θερμοδιαφορικό…	τοίχος 0.60 · Μ2 0.57 · Π2 4.41
ΠΥ-ΧΩΡ	ΟΚ	Κάλυψη χώρων	καθιστικό · Υπν.1 · Υπν.2 · χωλ · κουζίνα (θε…
ΘΕ-ΘΕ4	ΟΚ	ΘΕ4 40×40 – λουτρό: ψυκτικά ΚΜ3 / αποχέτευση άνω ορόφου · …	ελεύθερη
ΘΕ-ΘΕ5	ΟΚ	ΘΕ5 40×40 – λουτρό γονέων: επίσκεψη κενού (από πάνω δώμα – …	ελεύθερη
KP-KP1	ΟΚ	KP1 W4.01 – καθιστικό – Δ · 20 × 10 cm · οδηγοί 7 / 14 cm	πλήρης · βάθος 10 cm
KP-KP2	ΟΚ	KP2 W4.02 – καθιστικό – Ν · 20 × 10 cm · οδηγοί 7 / 14 cm	πλήρης · βάθος 10 cm
KP-KP3	ΟΚ	KP3 W4.08 – Υπν.1 – Δ · 20 × 10 cm · οδηγοί 7 / 14 cm	πλήρης · βάθος 10 cm
KP-KP4	ΟΚ	KP4 W4.06 – Υπν.2 – Α · 22 × 10 cm · οδηγοί 10 / 17 cm (ανοιγοα…	πλήρης · βάθος 10 cm
KP-W4.03	ΟΚ	W4.03	δεν απαιτείται – κουζίνα – πάνω από τον ν…
KP-W4.04	ΟΚ	W4.04	δεν απαιτείται – κουζίνα – έρκερ, πάνω από…
KP-W4.05	ΟΚ	W4.05	δεν απαιτείται – κλιμακοστάσιο (εκτός διαμ…
KP-W4.07	ΟΚ	W4.07	δεν απαιτείται – λουτρό (στο τοιχείο Κ2)
KP-W4.09	ΟΚ	W4.09	δεν απαιτείται – λουτρό γονέων (ντους)
ΣΘ-Ζ1	ΟΚ	Ζ1 +2,65 ↔ Ζ2 +2,40	χαμήλωση καναλάτου ΚΜ1 (προδ. 1/5)
ΣΘ-Ζ4	ΟΚ	Ζ4 +2,45 ↔ Ζ2 +2,40	στη γραμμή της Δ3.1 (άνοιγμα χωλ – καθιστι…
ΣΘ-Ζ1	ΟΚ	Ζ1 +2,65 ↔ Ζ3 +2,45	στη γραμμή της δοκού Δ9.1 (περασιά) – καθ…
ΣΘ-Ζ7	ΟΚ	Ζ7 +2,67 ↔ Ζ8 +2,55	στη γραμμή της δοκού Δ1.1 (κεφαλάρι έρκε…
ΣΘ-Ζ10	ΟΚ	Ζ10 +2,67 ↔ Ζ11 +2,45	σανίδα κάτω από τη Δ3.1 (εξαίρεση προσ. …
ΣΘ-ΣΥΝ	ΟΚ	Στάθμες στο διαμέρισμα	+2.40 · +2.45 · +2.55 · +2.65 · +2.67 (χαμήλ…

B

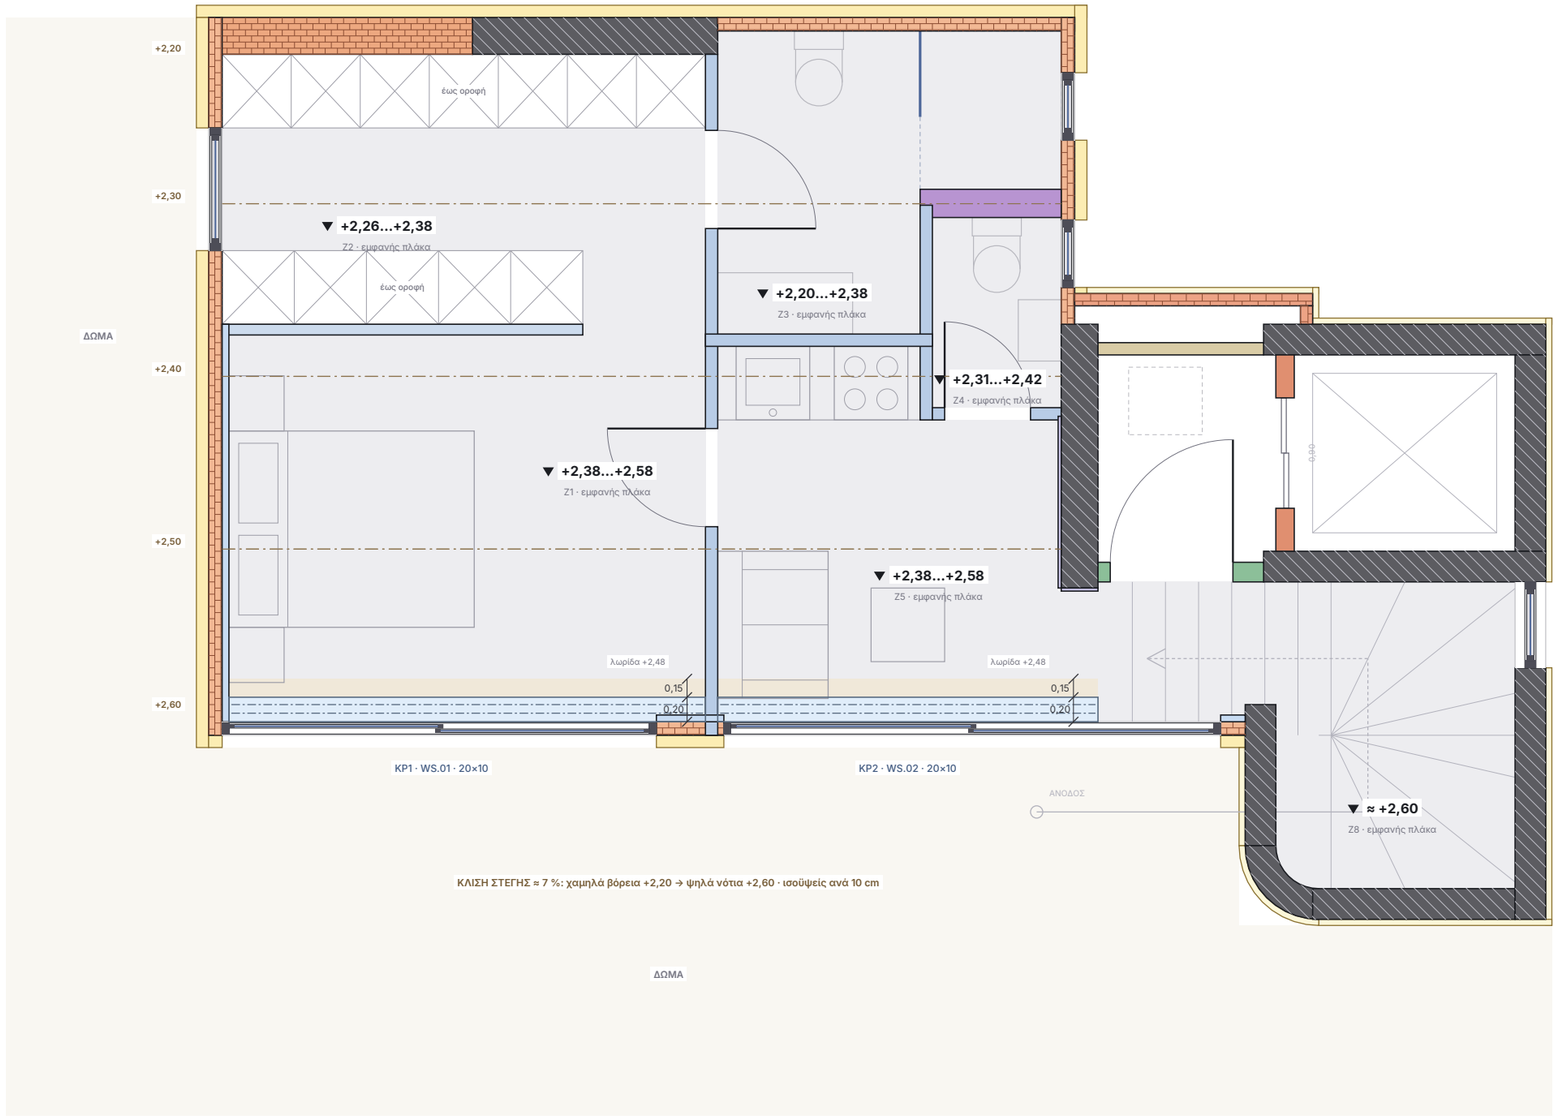

ΣΗΜΕΙΩΣΕΙΣ

Ιδιοκτήτης 07/11: «η οροφή της σοφίτας είναι με κλίση – αρχίζει περίπου από 2,2 και τελειώνει 2,6 · μην την κατεβάσεις γενικά». Η οροφή είναι η κάτω παρειά της κεκλιμένης πλάκας στέγης Σ8 (ανεστραμμένες δοκοί – κανένα δοκάρι μέσα): +2,20 στον βόρειο τοίχο, +2,60 στις νότιες τζαμαρίες, κλίση ≈ 7 % (4°). Οι διακεκομμένες είναι ισοϋψείς ανά 10 cm.

Σ8: κάτω παρειά +18,49 (Δ1.5) → +18,90 (Δ3.2) = 2,29 → 2,70 από το Τ.Δ. +16,20· η ανόψη κρατά τα δυσμενέστερα 2,20 / 2,60 (Α1).

Ύψη ανά χώρο: βεστιάριο 2,26–2,38 · λουτρό 2,20–2,38 · WC 2,31–2,42 · υπνοδωμάτιο / καθιστικό 2,38–2,58.


Καταβιβάσεις ΜΟΝΟ: λωρίδα κουρτίνας 15 cm ΟΡΙΖΟΝΤΙΑ +2,48 + εσοχή 20 × 11 ανοιχτή ως την πλάκα κατά μήκος WS.01 / WS.02 (προδ. 2 – κάτω ακμή 8 cm πάνω από την κάσα 2,40, μετώπη ≈ 10 cm). Λουτρό / WC / βεστιάριο / υπνοδωμάτιο / καθιστικό / σκάλα χωρίς ψευδοροφή.

ΥΠΟΜΝΗΜΑ

- εμφανής κεκλιμένη πλάκα Σ8 +2,20 → +2,60 – χωρίς ψευδοροφή (ισοϋψείς ανά 10 cm)
- +2,48 λωρίδα κουρτίνας (οριζόντια, γυψοσανίδα)
- ΚΡ εσοχή κουρτίνας 20 × 11 ανοιχτή ως την πλάκα · 2 οδηγοί

ΕΡΓΟ	ΘΕΜΑ ΣΧΕΔΙΟΥ	ΒΑΣΗ	ΑΡ. ΣΧΕΔΙΟΥ
ΠΕΝΤΑΟΡΟΦΟ ΚΤΗΡΙΟ ΚΑΤΟΙΚΙΩΝ – ΑΡΓΥΡΟΥΠΟΛΗ Κωνσταντινουπόλεως 12 & Αγ. Βαρβάρας · Ο.Τ. 103-15 Εργοδότης: INTERKAT Α.Ε. · Κατασκευή: ARKAD Ι.Κ.Ε.	**ΑΝΟΨΗ – ΣΤΑΘΜΕΣ · ΔΟΚΟΙ · ΚΟΥΡΤΙΝΕΣ** Εμφανής κεκλιμένη πλάκα Σ8 · ισοϋψείς · κουρτινόθηκες ΣΟΦΙΤΑ – Δ1 πάνω επίπεδο (μεζονέτα)	Βάση: τοιχοποιίες σοφίτας R04 · Σ8 (κεκλιμένη, ανεστρ. δοκοί)	**ΑΝ-13** **Κλίμακα 1:50 · Α3** 07/11/2026 · R02

B

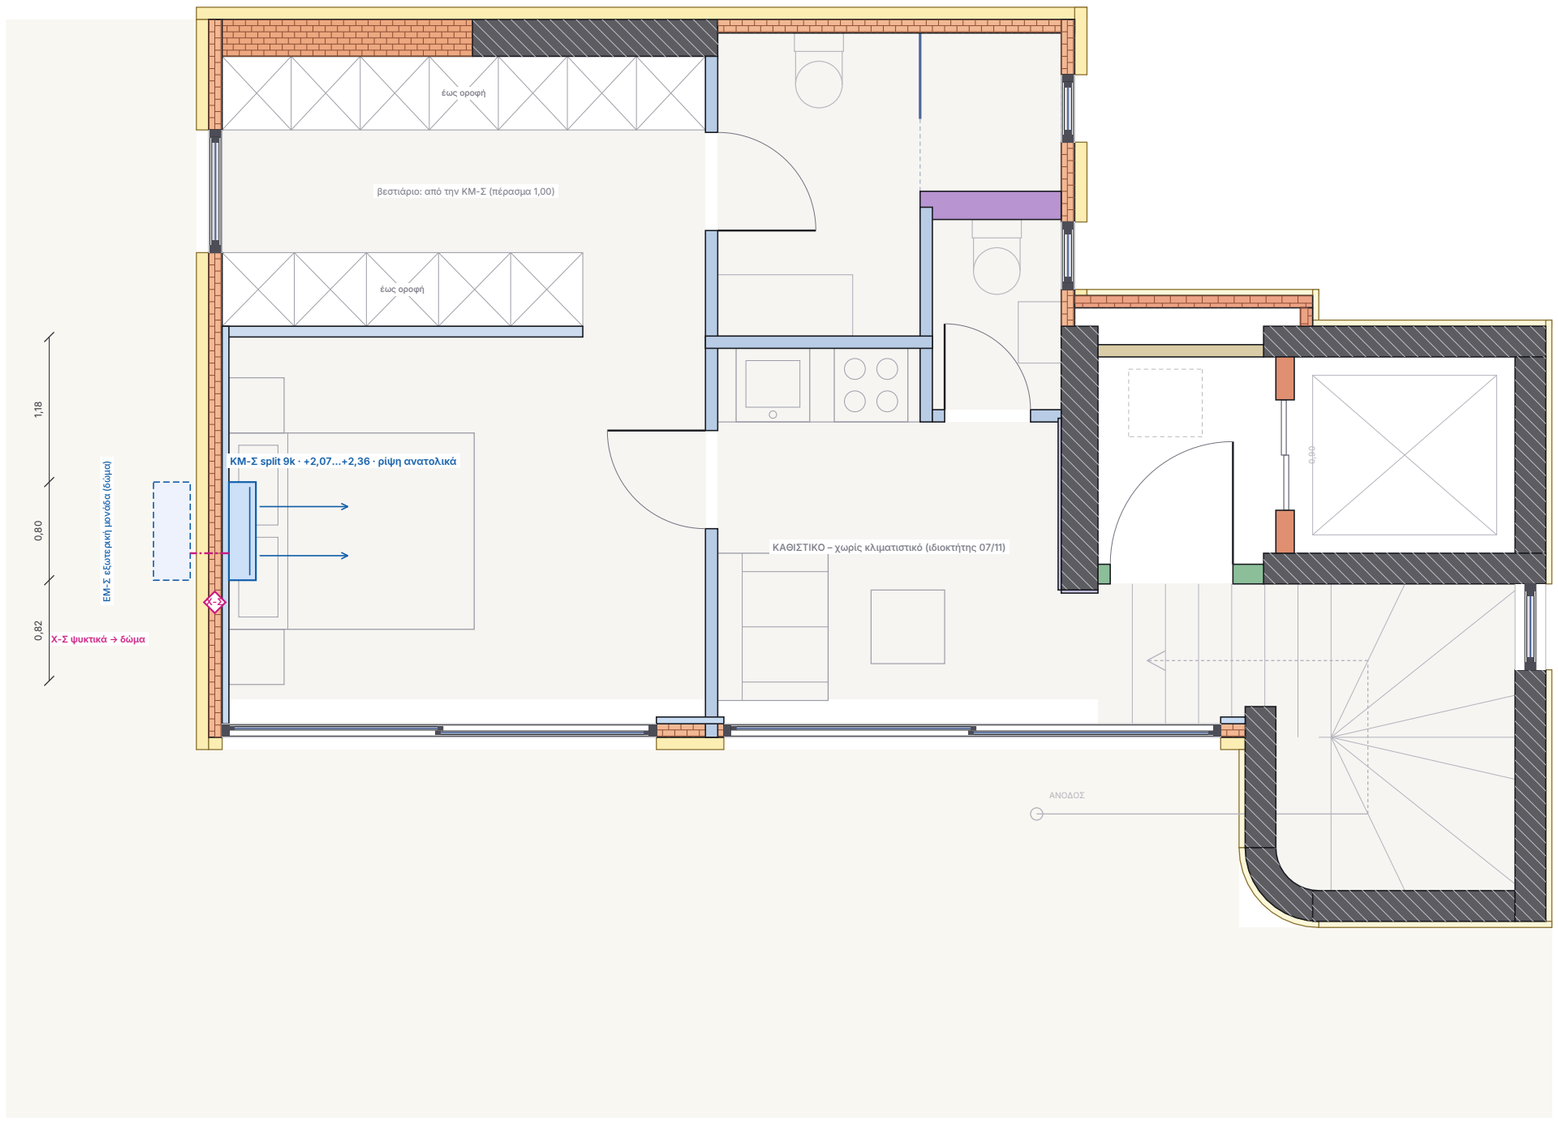

ΣΗΜΕΙΩΣΕΙΣ

Ιδιοκτήτης 07/11: «στα δωμάτια δεν θα βάζουμε καναλάτο, θα βάζουμε split σε ένα σημείο που θα βρεις» · σοφίτα: ένα κλιματιστικό, στο υπνοδωμάτιο.

ΚΜ-Σ split τοίχου 9.000 Btu/h ψηλά στον δυτικό (εξωτερικό) τοίχο ΠΑΝΩ ΑΠΟ ΤΟ ΚΕΦΑΛΑΡΙ, στον άξονα του κρεβατιού (y 4,27–5,07): ο αέρας ρίχνεται ανατολικά κατά μήκος του δωματίου (3,9 m) προς τα πόδια και την πόρτα – όχι στο πρόσωπο.

Ύψη: η κεκλιμένη οροφή στη θέση της μονάδας είναι +2,46…+2,52 → μονάδα +2,07…+2,36 (ύψος ≤ 290 mm), 10 cm από την οροφή στο χαμηλό άκρο· πάνω από το κεφαλάρι (≤ 1,20).

Ψυκτικά + συμπυκνώματα κατευθείαν πίσω από τη μονάδα μέσα από τον Τ4-07 (≈ 1 m) → εξωτερική μονάδα στο δυτικό δώμα (Χ-Σ)· συμπυκνώματα με φυσική ροή στο σιφώνι του δώματος. Καμία σωλήνωση στην οροφή ή στη ντουλάπα.


Απορρίφθηκε ο βόρειος τοίχος (Τ2Ν-01): οροφή μόνο +2,38 εκεί και ψυκτικά 2,4 m πάνω από τη ντουλάπα βεστιαρίου.

Καθιστικό – kitchenette: χωρίς κλιματιστικό (απόφαση ιδιοκτήτη).

ΥΠΟΜΝΗΜΑ

- ΚΜ-Σ split τοίχου (σώμα στον τοίχο, βέλη = ρίψη)
- εξωτερική μονάδα
- Χ κατέβασμα / έξοδος σωληνώσεων – καμία οπή σε σκυρόδεμα

ΕΡΓΟ	ΘΕΜΑ ΣΧΕΔΙΟΥ	ΒΑΣΗ	ΑΡ. ΣΧΕΔΙΟΥ
ΠΕΝΤΑΟΡΟΦΟ ΚΤΗΡΙΟ ΚΑΤΟΙΚΙΩΝ – ΑΡΓΥΡΟΥΠΟΛΗ Κωνσταντινουπόλεως 12 & Αγ. Βαρβάρας · Ο.Τ. 103-15 Εργοδότης: INTERKAT Α.Ε. · Κατασκευή: ARKAD Ι.Κ.Ε.	**ΑΝΟΨΗ – ΚΛΙΜΑΤΙΣΜΟΣ · ΘΥΡΙΔΕΣ** Ένα κλιματιστικό – split τοίχου στο υπνοδωμάτιο · ψυκτικά στο δώμα ΣΟΦΙΤΑ – Δ1 πάνω επίπεδο (μεζονέτα)	Βάση: τοιχοποιίες σοφίτας R04 · Σ8 (κεκλιμένη, ανεστρ. δοκοί)	**ΑΝ-14** **Κλίμακα 1:50 · Α3** 07/11/2026 · R02

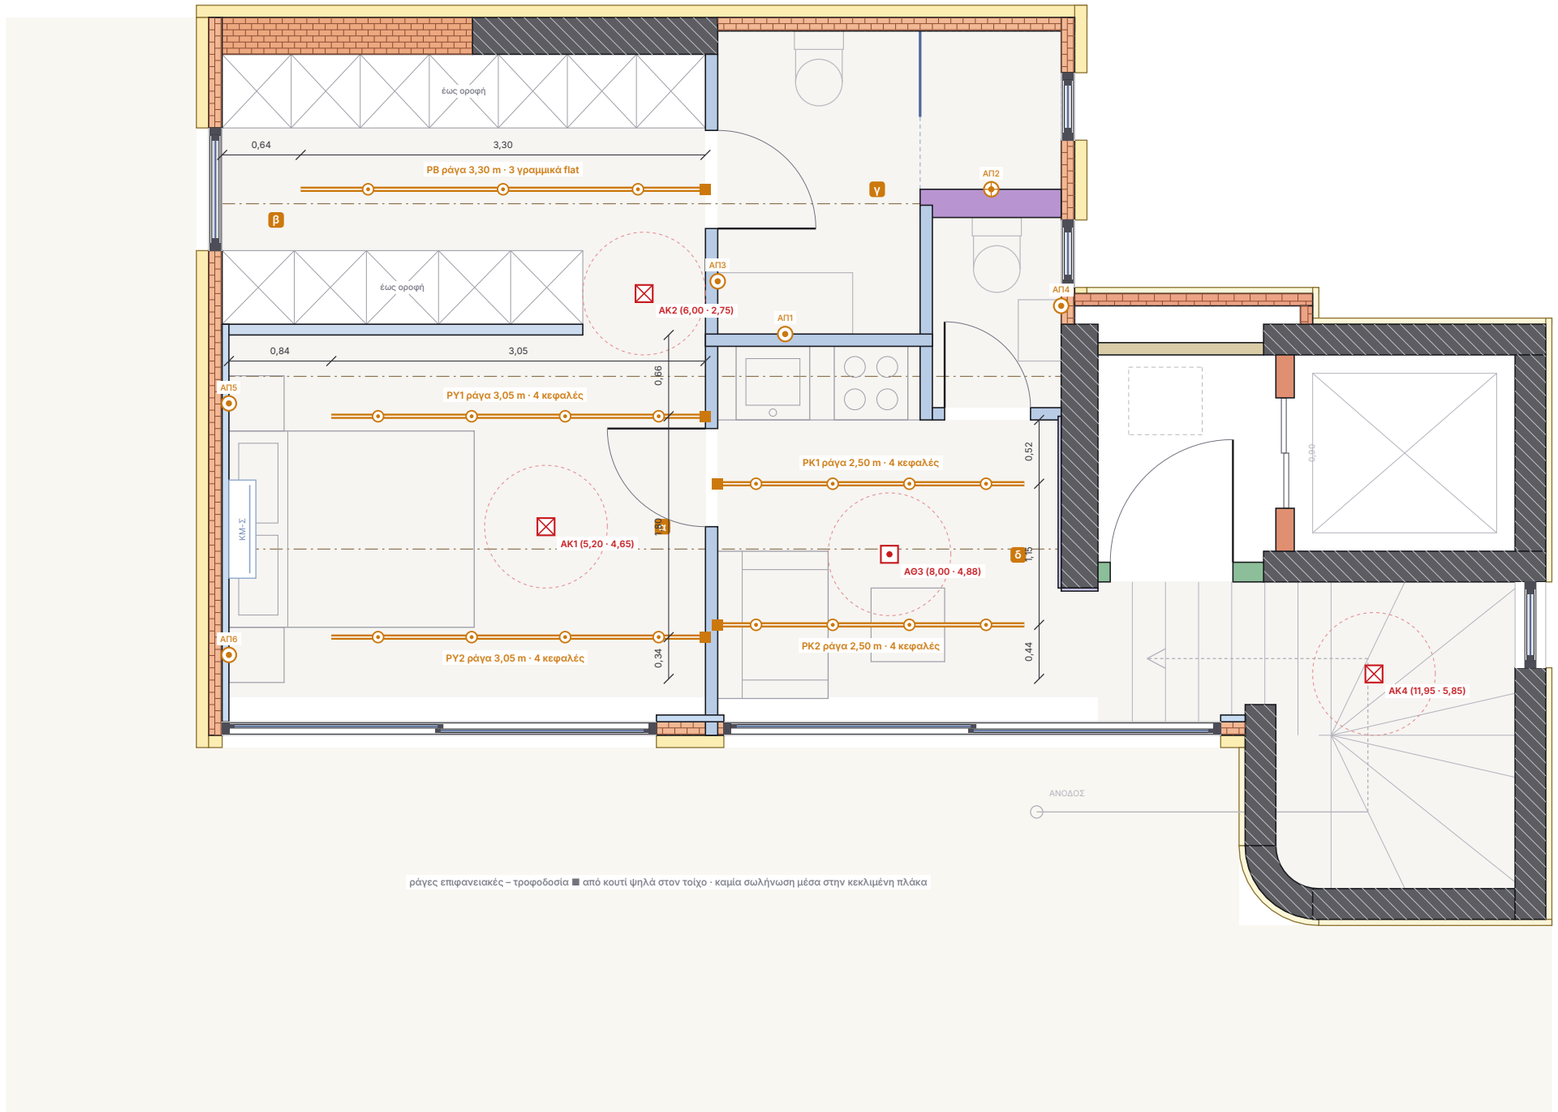

ΣΗΜΕΙΩΣΕΙΣ

Ιδιοκτήτης 07/11: «στη σοφίτα πρέπει να δείξουμε φωτισμό με ράγες – δε γίνεται χωνευτά spot». Ράγες επιφανειακές στην εμφανή πλάκα, ΟΛΕΣ Α–Δ: παράλληλες στις ισοϋψείς, άρα οριζόντιες – το ύψος δεν αλλάζει κατά μήκος τους. Κάθε ράγα ξεκινά από τοίχο (■ τροφοδοσία).

Υπνοδωμάτιο: PY1 / PY2 3,05 m συμμετρικά στον άξονα του κρεβατιού (y 3,75 / 5,55, οροφή +2,42 / +2,55), από τον ανατολικό τοίχο ως 0,84 από το κεφαλάρι – οι κεφαλές στρέφονται σε κρεβάτι, ντουλάπα, κουρτίνα · απλίκες ΑΠ5 / ΑΠ6 πάνω από τα κομοδίνα.

Βεστιάριο: PB 3,30 m στον άξονα του διαδρόμου με γραμμικά flat φωτιστικά (οροφή +2,29), τροφοδοσία από το υπέρθυρο της πόρτας λουτρού.

Καθιστικό – kitchenette: PK1 0,52 μπροστά από τον πάγκο (+2,46) · PK2 πάνω από το σαλόνι (+2,54) · 2,50 m η καθεμία.

Λουτρό / WC (οροφή 2,20–2,42, χωρίς ψευδοροφή): απλίκες ΑΠ1 καθρέπτης IP44 · ΑΠ2 ντους IP65 · ΑΠ3 γενικός IP44 · ΑΠ4 WC IP44.

Πυρανίχνευση: επιφανειακοί ανιχνευτές (Α7)· κλίση 4° < 20° → η οροφή θεωρείται επίπεδη (CEN/TS 54-14)· ≥ 0,50 από τοίχους / ράγες, ≥ 1,00 από το split.

ΥΠΟΜΝΗΜΑ

- ράγα φωτισμού επιφανειακή, λευκή, με κεφαλές spot (■ = τροφοδοσία από τοίχο)
- απλίκα τοίχου (σταυρός = IP65 στο ντους)
- split τοίχου (για συντονισμό – βλ. φύλλο κλιματισμού)
- ΑΚ ανιχνευτής καπνού (ΕΠ04 · EN 54-7)
- ΑΘ θερμοδιαφορικός ανιχνευτής (κουζίνα · EN 54-5)
- ακτίνα 0,50 m γύρω από ανιχνευτή – κανένας τοίχος / φωτιστικό μέσα

ΕΡΓΟ	ΘΕΜΑ ΣΧΕΔΙΟΥ	ΒΑΣΗ	ΑΡ. ΣΧΕΔΙΟΥ
ΠΕΝΤΑΟΡΟΦΟ ΚΤΗΡΙΟ ΚΑΤΟΙΚΙΩΝ – ΑΡΓΥΡΟΥΠΟΛΗ Κωνσταντινουπόλεως 12 & Αγ. Βαρβάρας · Ο.Τ. 103-15 Εργοδότης: INTERKAT Α.Ε. · Κατασκευή: ARKAD Ι.Κ.Ε.	**ΑΝΟΨΗ – ΦΩΤΙΣΜΟΣ · ΠΥΡΑΝΙΧΝΕΥΣΗ** Ράγες φωτισμού · απλίκες · ανιχνευτές ΣΟΦΙΤΑ – Δ1 πάνω επίπεδο (μεζονέτα)	Βάση: τοιχοποιίες σοφίτας R04 · Σ8 (κεκλιμένη, ανεστρ. δοκοί)	**ΑΝ-15** **Κλίμακα 1:50 · Α3** 07/11/2026 · R02

ΣΥΜΜΟΡΦΩΣΗ ΜΕ ΤΙΣ ΠΡΟΔΙΑΓΡΑΦΕΣ (ιδιοκτήτης 07/11/2026)

1 Κλιματισμός	Ένα split τοίχου ΚΜ-Σ 9k στο υπνοδωμάτιο (ιδιοκτήτης: «στα δωμάτια split», «μόνο ένα κλιματιστικό στη σοφίτα») πάνω από το κεφαλάρι, ψυκτικά κατευθείαν στο δώμα · καθιστικό χωρίς κλιματιστικό (ΕΓΚΕΚΡ.).
2 Κουρτίνες	ΚΡ1 (WS.01) / ΚΡ2 (WS.02 – καθιστικό) 20 × 11, ανοιχτές ως την κεκλιμένη πλάκα, με λωρίδα +2,48.
3 Φωτισμός	Χωρίς χωνευτά spots (ιδιοκτήτης) → 5 ράγες οριζόντιες με τροφοδοσία από τοίχο + 6 απλίκες (IP44 / IP65 στα λουτρά).
4 Πυρανίχνευση	ΑΚ1 υπνοδωμάτιο · ΑΚ2 βεστιάριο · ΑΘ3 καθιστικό – kitchenette · ΑΚ4 κορυφή σκάλας – επιφανειακοί.
5 Κατασκευή	Χωρίς γενική καταβίβαση (ιδιοκτήτης) · μόνο λωρίδες κουρτίνας +2,48 · κανένα δοκάρι (Σ8 ανεστραμμένες) · λουτρό / WC χωρίς ψευδοροφή (οροφή 2,20–2,42).
6 Γενική αρχή	Μία οροφή: η κεκλιμένη πλάκα, καθαρή· οι ράγες ακολουθούν τις ισοϋψείς (οριζόντιες), οι λωρίδες κουρτίνας στη γραμμή της τζαμαρίας.

ΕΓΚΕΚΡΙΜΕΝΕΣ ΑΠΟΚΛΙΣΕΙΣ (ιδιοκτήτης 07/11/2026)

· Σοφίτα: μόνο ένα κλιματιστικό, στο υπνοδωμάτιο – split τοίχου (ιδιοκτήτη 07/11).

· Σοφίτα: χωρίς γενική καταβίβαση της κεκλιμένης οροφής – χωρίς χωνευτά spots, φωτισμός με ράγες (ιδιοκτήτης 07/11).

ΑΛΛΑΓΕΣ R01 → R02 (ιδιοκτήτης 07/11/2026)

· Κεκλιμένη οροφή (ιδιοκτήτης: «η οροφή της σοφίτας είναι με κλίση, αρχίζει περίπου από 2,2 και τελειώνει 2,6»): εμφανής κεκλιμένη πλάκα Σ8, χαμηλά στον βόρειο τοίχο +2,20 → ψηλά στις νότιες τζαμαρίες +2,60 (≈ 7 % / 4°)· ισοϋψείς ανά 10 cm. Ο Σ8 δίνει 2,29 → 2,70 (Α1).

· Φωτισμός με ράγες (ιδιοκτήτης: «δε γίνεται χωνευτά spot»): καταργήθηκαν τα 14 spots και τα κουτιά στον Σ8. 5 επιφανειακές ράγες Α–Δ, οριζόντιες (παράλληλες στις ισοϋψείς), τροφοδοσία από τοίχο: ΡΥ1 / ΡΥ2 υπνοδωμάτιο · ΡΒ βεστιάριο · ΡΚ1 / ΡΚ2 καθιστικό + 6 απλίκες (κομοδίνα, λουτρό IP44 / ντους IP65, WC).

· Λουτρό / WC χωρίς ψευδοροφή: η οροφή εκεί είναι 2,20–2,42 – καταβίβαση για χωνευτά θα έριχνε το ύψος κάτω από 2,20.

· Κλιματισμός (ιδιοκτήτης: «στα δωμάτια split»): ΚΜ-Σ 9k split ψηλά στον δυτικό εξωτερικό τοίχο ΠΑΝΩ ΑΠΟ ΤΟ ΚΕΦΑΛΑΡΙ (+2,07…+2,36, οροφή εκεί +2,46), ρίψη ανατολικά προς τα πόδια· ψυκτικά / συμπυκνώματα κατευθείαν στον τοίχο → εξωτερική μονάδα στο δυτικό δώμα. Καταργήθηκαν η κρυφή καναλάτη στη ντουλάπα βεστιαρίου, το slot Π-Σ και η επιστροφή Ε-Σ.

· Λωρίδες κουρτίνας +2,48 (ήταν +2,55): με την κλίση η πλάκα στις τζαμαρίες είναι +2,59 → εσοχή 11 cm, κάτω ακμή 8 cm πάνω από την κάσα 2,40.

ΠΡΟΗΓΟΥΜΕΝΗ ΑΝΑΘΕΩΡΗΣΗ

· R01: εμφανής πλάκα θεωρημένη επίπεδη +2,65 · 14 χωνευτά spots σε κουτιά σκυροδέματος · λουτρό / WC +2,55 · ΚΜ-Σ κρυφή καναλάτη στη ντουλάπα βεστιαρίου με slot τοίχου.

ΑΝΟΙΚΤΑ ΣΗΜΕΙΑ

· Α1 [ΕΠΙ ΤΟΠΟΥ] Κλίση στέγης: ο Σ8 δίνει κάτω παρειά +18,49 (Δ1.5, βόρεια) → +18,90 (Δ3.2, νότια) = 2,29 → 2,70 από το Τ.Δ. +16,20· ο ιδιοκτήτης ≈ 2,20 → 2,60. Η ανόψη κρατά τα δυσμενέστερα (2,20 / 2,60) – μέτρηση μετά το ξεκαλούπωμα και επιβεβαίωση του τελικού δαπέδου.

· Α2 [ΑΠΟΦΑΣΗ] Πόρτες σοφίτας ύψους ≤ 2,10: η οροφή στο βεστιάριο / λουτρό είναι 2,26–2,38 και οι ράγες ΡΒ / ΡΚ1 τροφοδοτούνται από το υπέρθυρο της πόρτας λουτρού / υπνοδωματίου (≥ 10 cm τοίχος πάνω από την κάσα).

· Α3 [ΜΟΝΤΕΛΟ] Ράγες: επιφανειακό σύστημα λευκό (μονοφασικό 230 V ή μαγνητικό 48 V) με κεφαλές 7–10 W 2700 K, στο βεστιάριο γραμμικά flat (οροφή +2,29)· τροφοδοσία στο άκρο από κουτί ψηλά στον τοίχο – καμία σωλήνωση μέσα στην πλάκα.

· Α4 [ΣΥΝΤΟΝΙΣΜΟΣ] ΚΜ-Σ: split ύψους ≤ 290 mm, πλάτους ≤ 800 · εξωτερική μονάδα στο δυτικό δώμα (Σύσταση ΟΙ: δικαίωμα τοποθέτησης)· συμπυκνώματα με φυσική ροή στο σιφώνι του δώματος.

· Α5 [ΑΠΟΦΑΣΗ] Κουρτίνες: λωρίδα +2,48 με εσοχή (πρόταση – καθαρή γραμμή όπως στους ορόφους) ή επιφανειακή ράγα κουρτίνας στην πλάκα.

· Α6 [ΣΥΝΤΟΝΙΣΜΟΣ] Αποχετεύσεις λουτρού / WC σοφίτας στην επίστρωση (15 cm) – όχι στην οροφή του Δ΄ (βλ. Δ΄ Α5).

· Α7 [ΚΑΤΑΣΚΕΥΗ] Ανιχνευτές επιφανειακοί: καλώδιο σε λεπτό κανάλι βαμμένο από τον τοίχο ή ασύρματοι διασυνδεδεμένοι (μπαταρία 10 ετών).

· Α8 [ΕΠΙ ΤΟΠΟΥ] Πλάκα πάνω από την ιδιωτική σκάλα (ανατολικά της Δ9.5): κλίση / στάθμη δεν φαίνεται στον Σ8 – μέτρηση.

ΕΛΕΓΧΟΣ ΣΥΓΚΡΟΥΣΕΩΝ & ΣΤΑΘΜΩΝ – 39 έλεγχοι · ΟΚ 36 · ΟΡΙΑΚΟ 0 · ΕΓΚΕΚΡ. 3 · ΑΠΟΚΛΙΣΗ 0

B

Αυτόματος έλεγχος από το μοντέλο (code/anopseis/checks.py): στάθμες ↔ δοκοί · κενό μονάδων · θυρίδες · spots ↔ ζώνες / θυρίδες / μονάδες / αεραγωγοί / κουρτινόθηκες · ανιχνευτές ↔ τοίχοι / φωτιστικά / στόμια · κουρτινόθηκες ↔ κουφώματα / δοκοί.

ΚΩΔ.	ΚΑΤΑΣΤ.	ΣΤΟΙΧΕΙΟ	ΜΕΤΡΗΣΗ
ΣΤ-Ζ1	ΟΚ	Ζ1 ΥΠΝΟΔΩΜΑΤΙΟ – εμφανής πλάκα +2,38…+2,58	Σ8 κεκλιμένη (ανεστραμμένες δοκοί): +2,2…
ΣΤ-Ζ2	ΟΚ	Ζ2 ΒΕΣΤΙΑΡΙΟ – εμφανής πλάκα +2,26…+2,38	Σ8 κεκλιμένη (ανεστραμμένες δοκοί): +2,2…
ΣΤ-Ζ3	ΟΚ	Ζ3 ΛΟΥΤΡΟ – εμφανής πλάκα +2,20…+2,38	Σ8 κεκλιμένη (ανεστραμμένες δοκοί): +2,2…
ΣΤ-Ζ4	ΟΚ	Ζ4 WC – εμφανής πλάκα +2,31…+2,42	Σ8 κεκλιμένη (ανεστραμμένες δοκοί): +2,2…
ΣΤ-Ζ5	ΟΚ	Ζ5 ΚΑΘΙΣΤΙΚΟ – KITCHENETTE – εμφανής πλάκα +2,38…+2,58	Σ8 κεκλιμένη (ανεστραμμένες δοκοί): +2,2…
ΣΤ-Ζ8	ΟΚ	Ζ8 ΚΛΙΜΑΚΟΣΤΑΣΙΟ Δ1 – εμφανής πλάκα ≈ +2,60	πλάκα Σ8 πάνω από την ιδιωτική σκάλα (δ…
ΚΛ-ΚΜ-Σ	ΟΚ	ΚΜ-Σ split τοίχου 9.000 Btu/h – Υπνοδωμάτιο σοφίτας (δυτικός το…	οροφή +2,46 · μονάδα +2,07…+2,36 · πάν…
ΚΡ-ΚΜ-Σ	ΟΚ	ΚΜ-Σ – ρίψη ανατολικά κατά μήκος του κρεβατιού	πάνω από το κεφαλάρι, στον άξονα του κ…
ΨΣ-ΚΜ-Σ	ΟΚ	ΚΜ-Σ – ψυκτικά / συμπυκνώματα	κατευθείαν πίσω από τη μονάδα μέσα από τ…
ΚΔ-ΥΠΝ	ΕΓΚΕΚΡ.	Υπνοδωμάτιο σοφίτας	ΚΜ-Σ split τοίχου πάνω από το κεφαλάρι (…
ΚΔ-ΒΕΣΤ	ΟΚ	Βεστιάριο	από την ΚΜ-Σ (ανοιχτό στο υπνοδωμάτιο …
ΚΔ-ΚΑΘ	ΕΓΚΕΚΡ.	Καθιστικό – kitchenette σοφίτας	χωρίς κλιματιστικό – ιδιοκτήτης 07/11: «μό…
SP-OPO	ΕΓΚΕΚΡ.	Εμφανής κεκλιμένη πλάκα Σ8	δεν γίνονται (ιδιοκτήτης 07/11) → ράγες + α…
ΡΓ-ΡΥ1	ΟΚ	ΡΥ1 ράγα – υπνοδωμάτιο – βόρεια του κρεβατιού	μήκος 3.05 · οροφή +2,42 · κεφαλές ≈ +2,3…
ΡΓ-ΡΥ2	ΟΚ	ΡΥ2 ράγα – υπνοδωμάτιο – νότια του κρεβατιού	μήκος 3.05 · οροφή +2,55 · κεφαλές ≈ +2,4…
ΡΓ-ΡΒ	ΟΚ	ΡΒ ράγα – βεστιάριο – άξονας διαδρόμου (γραμμικά flat)	μήκος 3.30 · οροφή +2,29 · κεφαλές ≈ +2,…
ΡΓ-ΡΚ1	ΟΚ	ΡΚ1 ράγα – καθιστικό – μπροστά από την kitchenette	μήκος 2.50 · οροφή +2,46 · κεφαλές ≈ +2,…
ΡΓ-ΡΚ2	ΟΚ	ΡΚ2 ράγα – καθιστικό – πάνω από το σαλόνι	μήκος 2.50 · οροφή +2,54 · κεφαλές ≈ +2,4…
ΑΠ-ΑΠ1	ΟΚ	ΑΠ1 απλίκα IP44 – λουτρό – πάνω από τον καθρέπτη	τοίχος 0.00
ΑΠ-ΑΠ2	ΟΚ	ΑΠ2 απλίκα IP65 – ντους	μέσα στο ντους
ΑΠ-ΑΠ3	ΟΚ	ΑΠ3 απλίκα IP44 – λουτρό – γενικός	τοίχος 0.00
ΑΠ-ΑΠ4	ΟΚ	ΑΠ4 απλίκα IP44 – WC – πάνω από τον νιπτήρα	τοίχος 0.00
ΑΠ-ΑΠ5	ΟΚ	ΑΠ5 απλίκα τοίχου – κομοδίνο Β	τοίχος 0.00
ΑΠ-ΑΠ6	ΟΚ	ΑΠ6 απλίκα τοίχου – κομοδίνο Ν	τοίχος 0.00
ΠΥ-ΑΚ1	ΟΚ	ΑΚ1 καπνού (5.20 · 4.65) – υπνοδωμάτιο (ανάμεσα στις ράγες)	τοίχος 1.24 · ΡΥ2 0.90 · ΚΜ-Σ 2.37
ΠΥ-ΑΚ2	ΟΚ	ΑΚ2 καπνού (6.00 · 2.75) – βεστιάριο – άξονας περάσματος 1,00	τοίχος 0.50 (διάδρομος 1,00 – άξονας) · ΡΒ …
ΠΥ-ΑΘ3	ΟΚ	ΑΘ3 θερμοδιαφορικός (8.00 · 4.88) – καθιστικό – kitchenette (θε…	τοίχος 1.01 · ΡΚ1 0.58 · ΚΜ-Σ 5.17
ΠΥ-ΑΚ4	ΟΚ	ΑΚ4 καπνού (11.95 · 5.85) – κορυφή ιδιωτικής σκάλας (καλύπτει κ…	τοίχος 0.75 · ΡΚ2 2.88 · ΚΜ-Σ 9.15
ΠΥ-ΧΩΡ	ΟΚ	Κάλυψη χώρων	υπνοδωμάτιο · βεστιάριο · καθιστικό (θερμι…
ΚΡ-ΚΡ1	ΟΚ	ΚΡ1 WS.01 – υπνοδωμάτιο – Ν · 20 × 10 cm · οδηγοί 7 / 14 cm	πλήρης · βάθος 11 cm
ΚΡ-ΚΡ2	ΟΚ	ΚΡ2 WS.02 – καθιστικό – Ν · 20 × 10 cm · οδηγοί 7 / 14 cm	πλήρης · βάθος 11 cm
ΚΡ-WS.06	ΟΚ	WS.06	δεν απαιτείται – βεστιάριο – ανάμεσα σε ντ…
ΚΡ-WS.02-Α	ΟΚ	WS.02-Α	δεν απαιτείται – ανατολικό 1,00 της τζαμα…
ΚΡ-WS.03	ΟΚ	WS.03	δεν απαιτείται – κλιμακοστάσιο (εκτός διαμ…
ΚΡ-WS.04	ΟΚ	WS.04	δεν απαιτείται – WC (ποδιά 1,50)
ΚΡ-WS.05	ΟΚ	WS.05	δεν απαιτείται – ντους (ποδιά 1,50)
ΣΘ-Ζ1	ΟΚ	Ζ1 ↔ Ζ6 +2,48	λωρίδα κουρτινόθηκης ΚΡ1 κατά μήκος του…
ΣΘ-Ζ5	ΟΚ	Ζ5 ↔ Ζ7 +2,48	λωρίδα κουρτινόθηκης ΚΡ2 κατά μήκος του…
ΣΘ-ΣΥΝ	ΟΚ	Στάθμες στο διαμέρισμα	+2.48 · +2.60 (εμφανής κεκλιμένη πλάκα +…