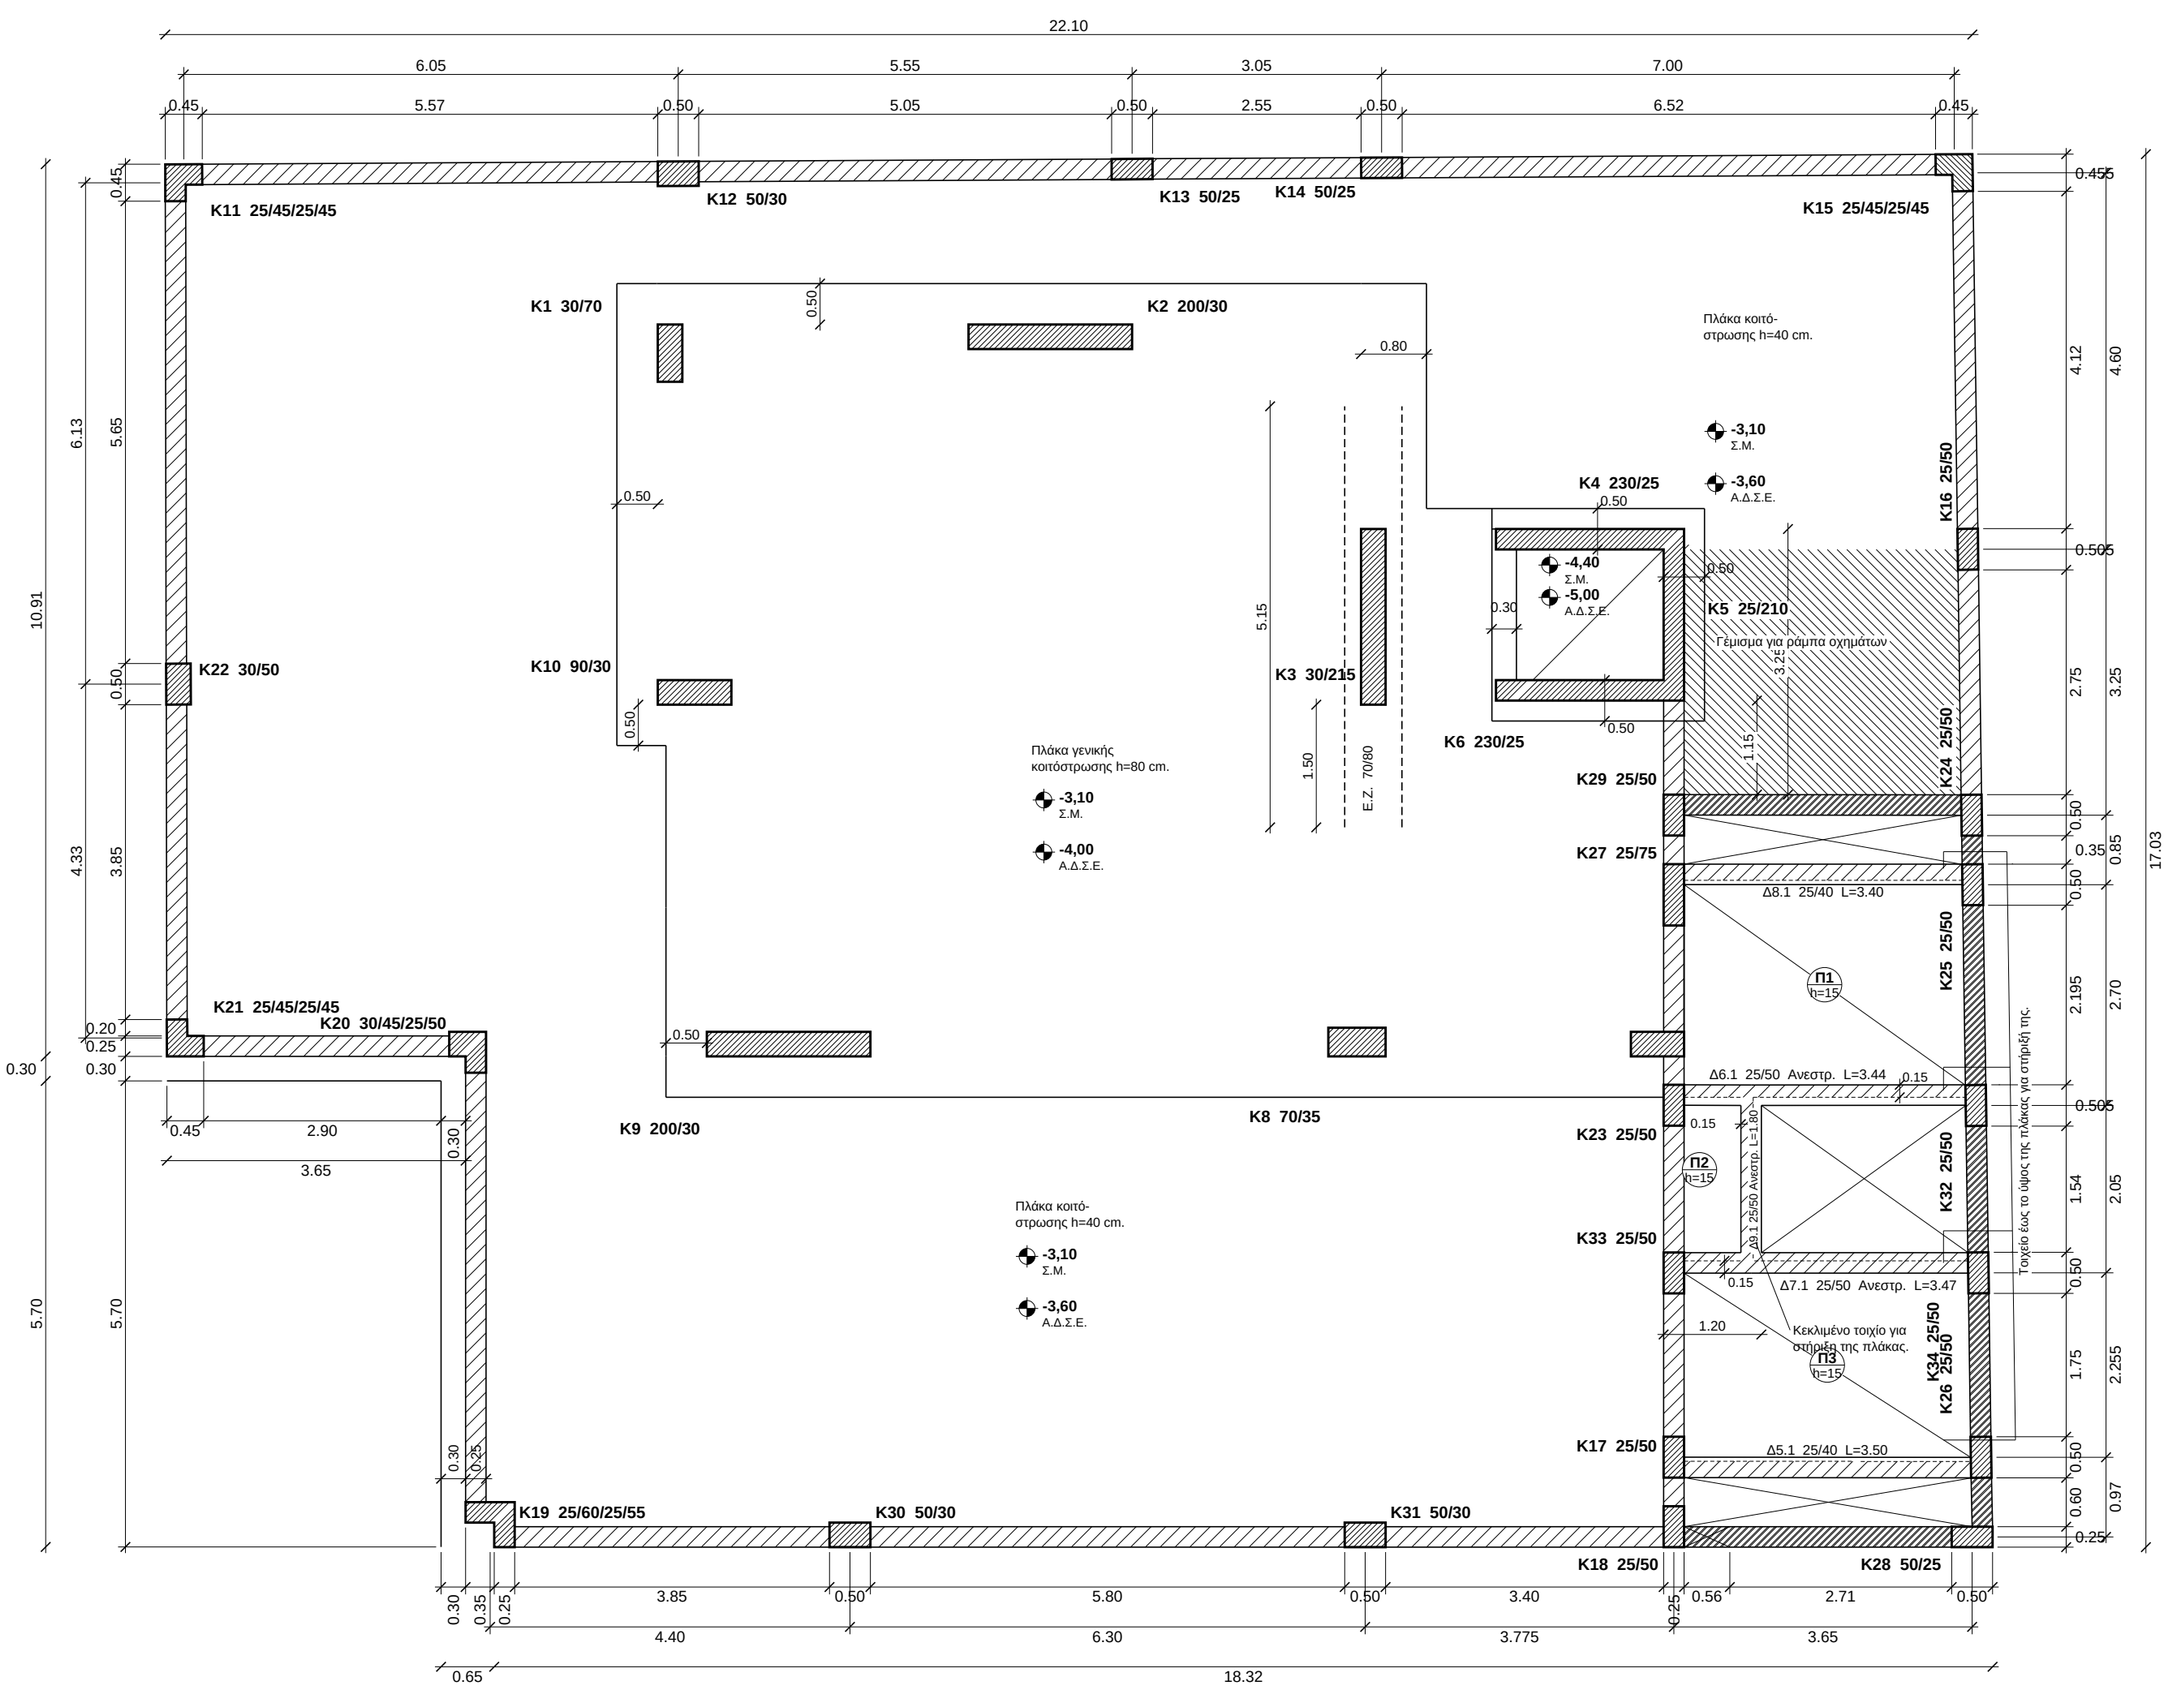


ΕΡΓΟ

ΑΝΕΓΕΡΣΗ ΠΕΝΤΑΟΡΟΦΟΥ ΚΤΗΡΙΟΥ ΚΑΤΟΙΚΙΩΝ ΜΕ ΥΠΟΓΕΙΟ, ΣΟΦΙΤΑ ΚΑΙ ΔΩΜΑ

ΘΕΣΗ

ΚΩΝΣΤΑΝΤΙΝΟΥΠΟΛΕΩΣ 12 &
ΑΓΙΑΣ ΒΑΡΒΑΡΑΣ – Ο.Τ. 103-15
ΔΗΜΟΣ ΕΛΛΗΝΙΚΟΥ-ΑΡΓΥΡΟΥΠΟΛΗΣ

ΕΡΓΟΔΟΤΗΣ

ARKAD I.K.E.

ΜΕΛΕΤΗΤΗΣ ΣΤΑΤΙΚΩΝ

ΓΙΩΡΓΟΣ ΚΟΓΙΑΣ
ΠΟΛΙΤΙΚΟΣ ΜΗΧΑΝΙΚΟΣ

ΘΕΜΑ ΣΧΕΔΙΟΥ

ΞΥΛΟΤΥΠΟΣ ΘΕΜΕΛΙΩΣΗΣ (-4,00 / -3,60)
ΓΕΩΜΕΤΡΙΑ – ΠΛΗΡΗΣ ΔΙΑΣΤΑΣΙΟΛΟΓΗΣΗ (ΧΩΡΙΣ ΟΠΛΙΣΜΟΥΣ)

ΒΑΣΗ

Εγκεκριμένο σχέδιο Σ1
Οριστική μελέτη, 02/2024
κλ. 1:50 (Fespa)

ΚΛΙΜΑΚΑ


1:75 (A3)

ΑΡ. ΣΧΕΔΙΟΥ / ΗΜΕΡΟΜΗΝΙΑ

Σ1 – ΓΕΩΜΕΤΡΙΑ 1:75 (1/2)
21/09/2026

Διαστάσεις σε m · b/h σε cm
h πλάκας σε cm
L = καθαρό μήκος δοκού μεταξύ παρειών στηρίξεων
Ανεστρ. = ανεστραμμένη δοκός
Σ.Μ. / Α.Δ.Σ.Ε.: στάθμες κατά Σ1
Οπλισμοί κατά Σ1

0 1 2
m (1:75)

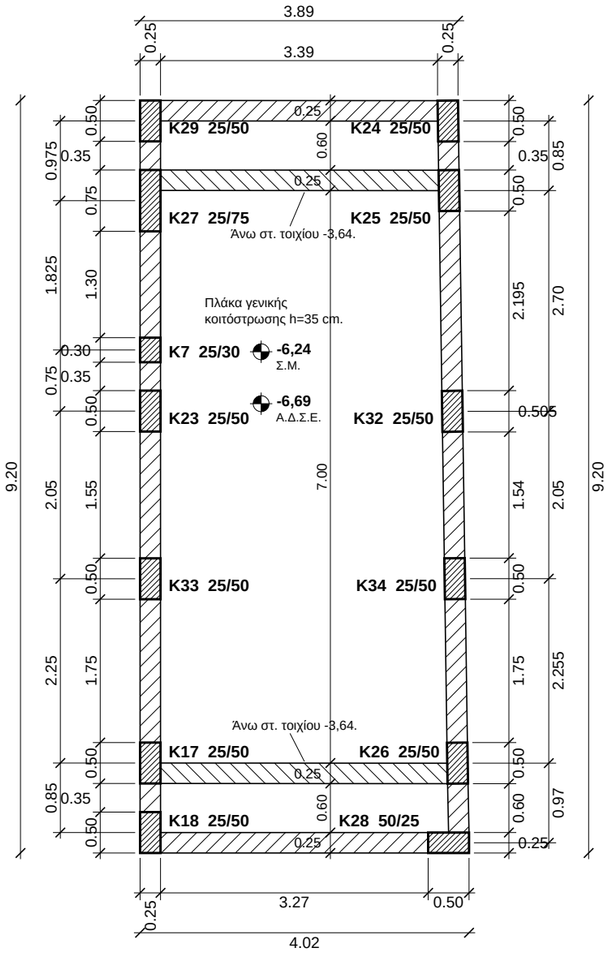

ΞΥΛΟΤΥΠΟΣ ΘΕΜΕΛΙΩΣΗΣ ΥΠΟΣΤΑΘΜΟΥ (-6,69)

ΕΡΓΟ

ΑΝΕΓΕΡΣΗ ΠΕΝΤΑΟΡΟΦΟΥ ΚΤΗΡΙΟΥ ΚΑΤΟΙΚΙΩΝ ΜΕ ΥΠΟΓΕΙΟ, ΣΟΦΙΤΑ ΚΑΙ ΔΩΜΑ

ΘΕΣΗ

ΚΩΝΣΤΑΝΤΙΝΟΥΠΟΛΕΩΣ 12 &
ΑΓΙΑΣ ΒΑΡΒΑΡΑΣ – Ο.Τ. 103-15
ΔΗΜΟΣ ΕΛΛΗΝΙΚΟΥ-ΑΡΓΥΡΟΥΠΟΛΗΣ

ΕΡΓΟΔΟΤΗΣ

ARKAD I.K.E.

ΜΕΛΕΤΗΤΗΣ ΣΤΑΤΙΚΩΝ

ΓΙΩΡΓΟΣ ΚΟΓΙΑΣ
ΠΟΛΙΤΙΚΟΣ ΜΗΧΑΝΙΚΟΣ

ΘΕΜΑ ΣΧΕΔΙΟΥ

ΞΥΛΟΤΥΠΟΣ ΘΕΜΕΛΙΩΣΗΣ ΥΠΟΣΤΑΘΜΟΥ (-6,69) ΓΕΩΜΕΤΡΙΑ – ΠΛΗΡΗΣ ΔΙΑΣΤΑΣΙΟΛΟΓΗΣΗ (ΧΩΡΙΣ ΟΠΛΙΣΜΟΥΣ)

ΒΑΣΗ

Εγκεκριμένο σχέδιο Σ1
Οριστική μελέτη, 02/2024
κλ. 1:50 (Fespa)

ΚΛΙΜΑΚΑ

1:75 (A3)

ΑΡ. ΣΧΕΔΙΟΥ / ΗΜΕΡΟΜΗΝΙΑ

Σ1 – ΓΕΩΜΕΤΡΙΑ 1:75 (2/2)
21/09/2026

Διαστάσεις σε m · b/h σε cm
Σ.Μ. / Α.Δ.Σ.Ε.: στάθμες κατά Σ1
Οπλισμοί κατά Σ1

0 1 2
m (1:75)