
ΑΛΛΑΓΕΣ R15 / R16 (05/11/2026)

· Ντουλάπες χωνευτές: δωματίων 0,60 · πλυντηρίου 0,70
· T1-05 ως 1,38 (+0,03 περιθώριο) · T3-06 μένει (ισοπαχείς λαμπάδες) · W2.06 → 1,38–2,38
· Υπν.1: χωρίς κουτί – ξυλουργικό συνέχεια ντουλάπας ως τον β. τοίχο
· T2-05 → T2N-02 (1 φύλλο προς ντουλάπα) · διάδρομος χωλ 1,00
· Λουτρά: πάγκος 0,50 · λεκάνη · γυάλινο διαχωριστικό 0,70 · ντους 0,70–1,00
· Αλουμίνια στη μέση του τοίχου: T3 και στις δύο παραστάδες
· Πόρτες: ανοίγουν μέσα στον χώρο (Υπν.1, λουτρά, Υπν.2)
· Αλυσίδες διαστάσεων μέσα στους χώρους · φύλλο χάραξης T-01A

B

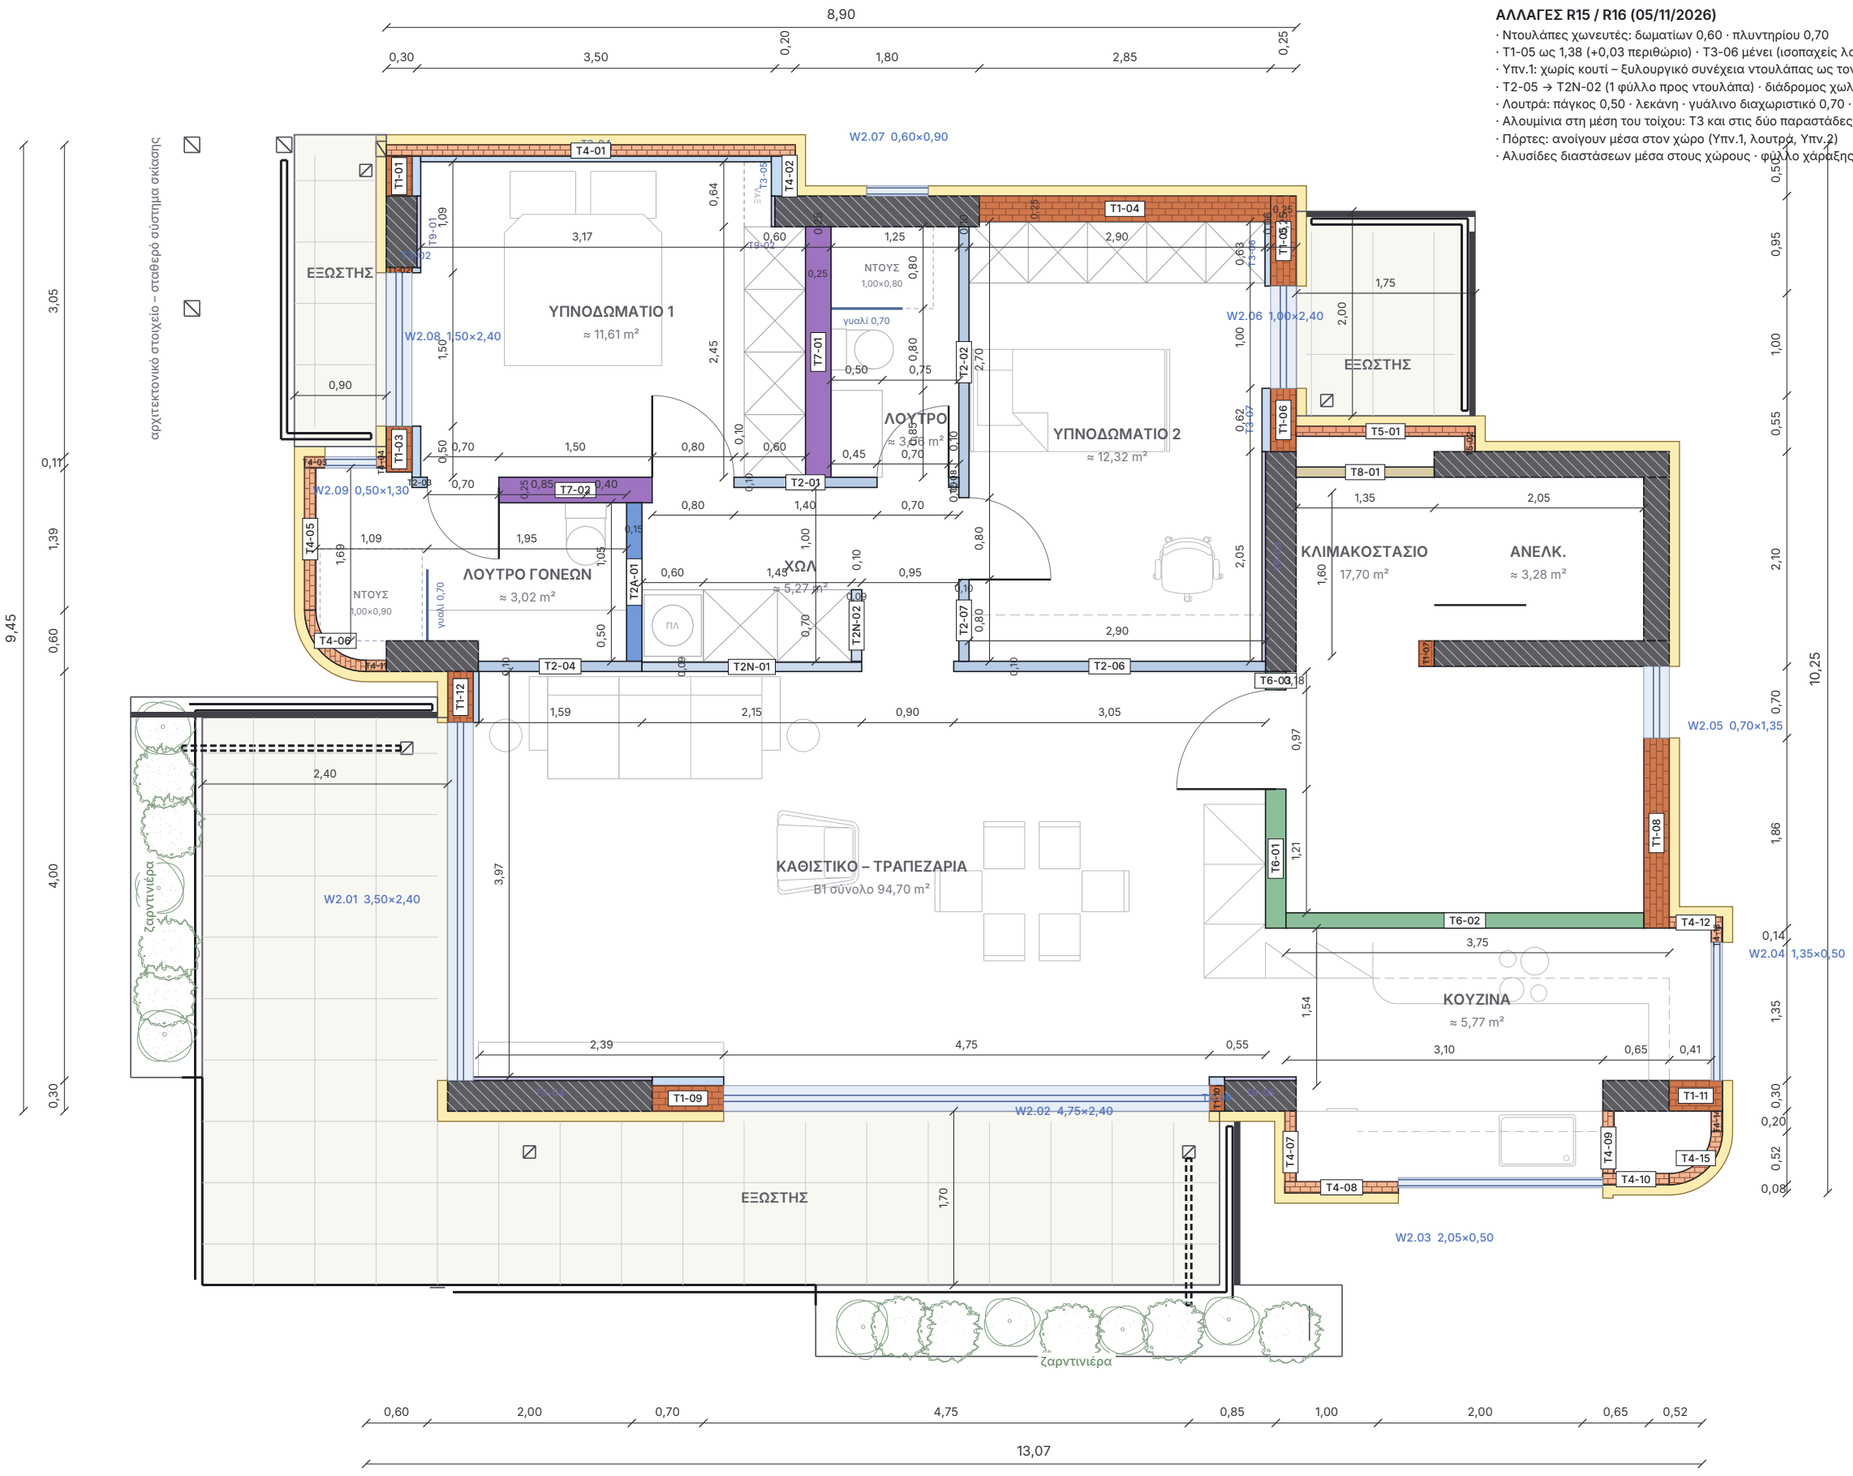

ΕΡΓΟ **ΠΕΝΤΑΟΡΟΦΟ ΚΤΗΡΙΟ ΚΑΤΟΙΚΙΩΝ – ΑΡΓΥΡΟΥΠΟΛΗ** Κωνσταντινουπόλεως 12 & Αγ. Βαρβάρας · Ο.Τ. 103-15 Εργοδότης: INTERKAT Α.Ε. · Κατασκευή: ARKAD Ι.Κ.Ε.	ΘΕΜΑ ΣΧΕΔΙΟΥ **ΚΑΤΟΨΗ ΤΟΙΧΟΠΟΙΙΩΝ – Β΄ ΟΡΟΦΟΣ** Είδη τοιχοποιιών · διαστάσεις χάραξης · κουφώματα · εξώστες Β΄ ΟΡΟΦΟΣ – Β1	ΒΑΣΗ Βάση: κάτοψη Α-10-2F (μελέτη εφαρμογής) · ξυλότυποι Σ · R14 + αλλαγές 05/11	ΑΡ. ΣΧΕΔΙΟΥ **T-01** **Κλίμακα 1:60 · Α3** 05/11/2026 · R16

ΣΥΝΤΕΤΑΓΜΕΝΕΣ ΠΑΡΕΙΩΝ ΤΟΙΧΩΝ (m)

x από την εξωτ. Δ παρειά Τ4-05 (→ ανατολή) · y από την εξωτ. Β παρειά Τ4-01 (→ νότο) · χωρίς θερμοπρόσοψη επενδύσεις Τ3 / Τ9 δεν χαράσσονται: ακολουθούν τον τοίχο / την κολόνα που ντύνουν

Τοίχος	πάχ.	x από	x έως	y από	y έως	μήκος
T1-01	25	0,80	1,05	0,11	0,50	0,39
T1-02	25	0,80	1,05	1,20	1,25	0,25
T1-03	25	0,80	1,05	2,75	3,20	0,45
T1-04	25	6,60	9,45	0,50	0,75	2,85
T1-05	25	9,45	9,70	0,50	1,38	0,88
T1-06	25	9,45	9,70	2,38	3,00	0,62
T1-07	25	10,90	11,05	4,85	5,10	0,25
T1-08	25	13,10	13,35	5,80	7,66	1,86
T1-09	25	3,40	4,10	9,20	9,45	0,70
T1-10	25	8,85	9,00	9,20	9,45	0,25
T1-11	25	13,35	13,87	9,15	9,45	0,52
T1-12	25	1,40	1,65	5,15	5,65	0,50
T4-01	11	0,80	4,80	-0,00	0,11	4,00
T4-02	11	4,69	4,80	0,11	0,50	0,39
T4-03	11	-0,00	0,20	3,05	3,16	0,20
T4-04	11	0,70	0,80	3,05	3,16	0,11
T4-05	11	-0,00	0,11	3,16	4,55	1,39
T4-06	11	-0,00	0,60	4,55	5,15	0,86*
T4-07	11	9,59	9,70	9,45	10,25	0,80
T4-08	11	9,59	10,70	10,14	10,25	1,11
T4-09	11	12,70	12,81	9,45	10,17	0,72
T4-10	11	12,70	13,35	10,06	10,17	0,65
T4-11	11	0,60	0,80	5,04	5,15	0,20
T4-12	11	13,35	13,87	7,55	7,66	0,52
T4-13	11	13,76	13,87	7,66	7,80	0,14
T4-14	11	13,76	13,87	9,45	9,65	0,20
T4-15	11	13,35	13,87	9,65	10,17	0,73*
T5-01	10	9,70	11,45	2,75	2,85	1,75
T5-02	10	11,35	11,45	2,85	3,00	0,15
T2-01	10	4,20	5,60	3,25	3,35	1,40
T2-02	10	6,40	6,50	0,80	3,45	2,65
T2-03	10	1,05	1,20	3,25	3,35	0,15
T2-04	10	1,70	3,30	5,05	5,15	1,60
T2-06	10	6,35	9,40	5,05	5,15	3,05
T2-07	10	6,40	6,50	4,25	5,05	0,80
T2-08	10	6,30	6,40	3,25	3,35	0,10
T2N-01	8,8	3,30	5,45	5,06	5,15	2,15
T2N-02	8,8	5,35	5,45	4,35	5,05	0,70
T2A-01	15	3,15	3,30	3,50	5,05	1,55
T7-01	25	4,90	5,15	0,80	3,25	2,45
T7-02	25	1,90	3,40	3,25	3,50	1,50
T6-01	15	9,40	9,60	6,30	7,66	1,36
T6-02	15	9,60	13,10	7,51	7,66	3,50
T6-03	15	9,40	9,60	5,15	5,33	0,20
T8-01	10	9,70	11,05	3,15	3,25	1,35

* καμπύλο τμήμα (έρκερ): μήκος στον μέσο άξονα του τόξου · Τ6-01: δύο τμήματα (πόρτα εισόδου 5,33–6,30)
Οι αλυσίδες της κάτοψης δίνουν, σε κάθε γραμμή τοίχου, τα άκρα των τοίχων και τις παρειές των υποστυλωμάτων ώστε η χάραξη να γίνεται με μετροταινία από τα μπετά. Ανοχή ±1 cm.

ΕΡΓΟ

ΠΕΝΤΑΟΡΟΦΟ ΚΤΗΡΙΟ ΚΑΤΟΙΚΙΩΝ – ΑΡΓΥΡΟΥΠΟΛΗ
Κωνσταντινουπόλεως 12 & Αγ. Βαρβάρας · Ο.Τ. 103-15
Εργοδότης: INTERKAT Α.Ε. · Κατασκευή: ARKAD Ι.Κ.Ε.

ΘΕΜΑ ΣΧΕΔΙΟΥ

ΧΑΡΑΞΗ ΤΟΙΧΟΠΟΙΙΩΝ – Β΄ ΟΡΟΦΟΣ
Αλυσίδες κατά μήκος κάθε γραμμής τοίχου · συντεταγμένες παρειών
Β΄ ΟΡΟΦΟΣ – Β1 · χωρίς έπιπλα

ΒΑΣΗ

Βάση: κάτοψη τοιχοποιιών Τ-01 · ξυλότυποι Σ (υποστυλώματα)


ΑΡ. ΣΧΕΔΙΟΥ

Τ-01Α
Κλίμακα 1:60 · Α3
05/11/2026 · R16


T1 Εξωτερική οπτοπλινθοδομή

1:4

πάχος 25 cm

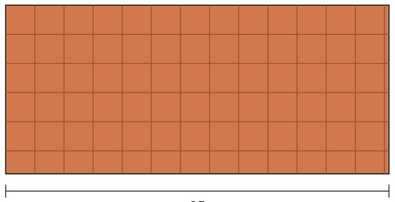

θερμομονωτικό τούβλο κάθετων οπών 25 cm · θερμοπρόσοψη 10 cm έξω · επένδυση Τ3 μέσα όπου σημειώνεται

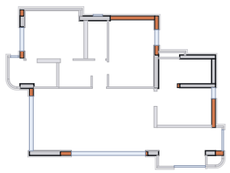


Τοίχοι: Τ1-01, Τ1-02, Τ1-03, Τ1-04, Τ1-05, Τ1-06, Τ1-07, Τ1-08, Τ1-09, Τ1-10, Τ1-11, Τ1-12

Μήκος 9,52 m · επιφάνεια ≈ 27,6 m²


T4 Έρκερ – απλή οπτοπλινθοδομή

1:4

πάχος 11 cm

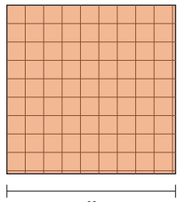

απλό τούβλο 6οπο 9 × 12 × 19 δρομικό ≈ 11 cm · σταθερή η εξωτερική παρειά · θερμοπρόσοψη 10 cm έξω

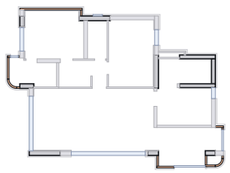


Τοίχοι: Τ4-01, Τ4-02, Τ4-03, Τ4-04, Τ4-05, Τ4-06, Τ4-07, Τ4-08, Τ4-09, Τ4-10, Τ4-11, Τ4-12, Τ4-13, Τ4-14, Τ4-15

Μήκος 12,02 m · επιφάνεια ≈ 34,8 m²


T5 Οπτοπλινθοδομή πυρήνα

1:4

πάχος 10 cm

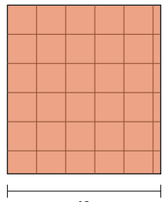

θερμομονωτικό τούβλο κάθετων οπών 10 cm · γύρω από τον πυρήνα (ανελκυστήρας – ηλεκτροστάσιο)

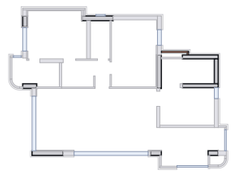


Τοίχοι: Τ5-01, Τ5-02

Μήκος 1,90 m · επιφάνεια ≈ 5,5 m²


T3 Επένδυση τοίχου

1:4

πάχος 5,5 cm

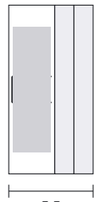

σκελετός 30 · 2 × γυψοσανίδα 12,5 · στις εσωτερικές παρειές των Τ1 – ΟΧΙ όπου πλακάκι ή ντουλάπα, ΟΧΙ στα έρκερ

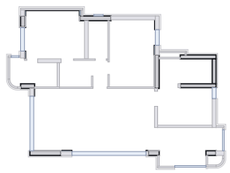

Τοίχοι: Τ3-01, Τ3-02, Τ3-03, Τ3-04, Τ3-05, Τ3-06, Τ3-07, Τ3-08, Τ3-09, Τ3-10

Μήκος 7,40 m · επιφάνεια ≈ 21,4 m²


T9 Επένδυση υποστυλώματος

1:4

πάχος 2,5 cm



κόλλα + 1 × γυψοσανίδα 12,5 (ένα φύλλο) · στις παρειές υποστυλωμάτων μέσα στα διαμερίσματα – ΟΧΙ όπου πλακάκι ή ντουλάπα

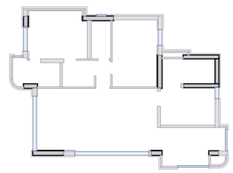


Τοίχοι: Τ9-01, Τ9-02, Τ9-03, Τ9-04, Τ9-05

Μήκος 5,75 m · επιφάνεια ≈ 16,7 m²


T2 Χώρισμα γυψοσανίδας

1:4

πάχος 10 cm

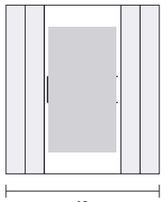

2 × γυψοσανίδα 12,5 · σκελετός CW 50 · 2 × γυψοσανίδα 12,5 · εσωτερικά χωρίσματα · ανθυγρή γυψοσανίδα στην πλευρά των λουτρών

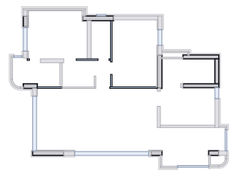


Τοίχοι: Τ2-01, Τ2-02, Τ2-03, Τ2-04, Τ2-06, Τ2-07, Τ2-08

Μήκος 9,75 m · επιφάνεια ≈ 28,3 m²


T2N Χώρισμα γυψ. – πλευρά ντουλάπας

1:4

πάχος 8,75 cm

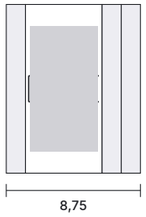

1 × γυψοσανίδα 12,5 (πλευρά ντουλάπας) · σκελετός CW 50 · 2 × γυψοσανίδα 12,5 · όπου η μία παρειά βλέπει σε ντουλάπα: ένα φύλλο αρκεί (κανόνας R15)

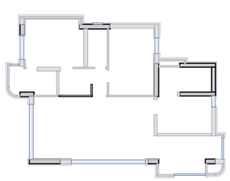


Τοίχοι: Τ2N-01, Τ2N-02

Μήκος 2,85 m · επιφάνεια ≈ 8,3 m²


T2A Χώρισμα γυψοσανίδας 15

1:4

πάχος 15 cm

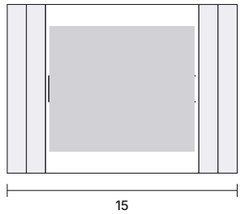

2 × γυψοσανίδα 12,5 · σκελετός CW 100 + πετροβάμβακας · 2 × γυψοσανίδα 12,5 · λουτρό γονέων / χωλ · υπνοδωμάτια

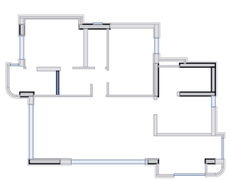


Τοίχοι: Τ2Α-01

Μήκος 1,55 m · επιφάνεια ≈ 4,5 m²


T7 Τοίχος λεκάνης WC

1:4

πάχος 25 cm

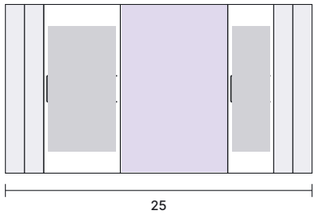

2 × γυψοσανίδα 12,5 · σκελετός CW 50 · κενό 12 cm (καζανάκι γυψοσανίδας στον σκελετό + κατακόρυφη στήλη Ø110, έξοδος Ø90) · σκελετός CW 30 · 2 × γυψοσανίδα 12,5 · ΟΛΟΙ οι τοίχοι λεκανών · ανθυγρή προς το λουτρό · στην πλευρά ντουλάπας 1 φύλλο

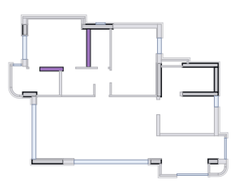


Τοίχοι: Τ7-01, Τ7-02

Μήκος 3,95 m · επιφάνεια ≈ 11,5 m²


T6 Τοίχος κλιμακοστασίου

1:4

πάχος 15 cm

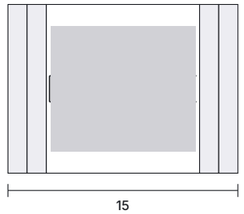

2 × γυψοσανίδα 12,5 πυράντοχη · σκελετός CW 100 + πετροβάμβακας · 2 × γυψοσανίδα 12,5 πυράντοχη · προς κοινόχρηστους χώρους · Τ6-01 (πόρτα εισόδου) μένει όπως η κάτοψη

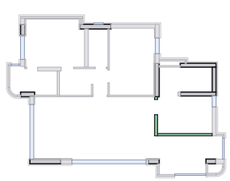


Τοίχοι: Τ6-01, Τ6-02, Τ6-03

Μήκος 5,06 m · επιφάνεια ≈ 14,7 m²


T8 Τοίχος shaft

1:4

πάχος 10 cm

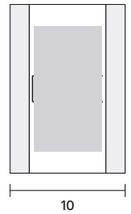

πλαίσιο + ανοιγόμενα φύλλα γυψοσανίδας · μέτωπο shaft ηλεκτρολογικών

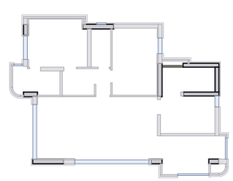

Τοίχοι: Τ8-01

Μήκος 1,35 m · επιφάνεια ≈ 3,9 m²

Επιφάνειες ενδεικτικές: μήκος × ύψος 2,90 m (τελικό δάπεδο – πλάκα) – οι τοίχοι ορίζονται μεταξύ ανοιγμάτων, χωρίς αφαίρεση κασών. Τ3 = επένδυση στην εσωτερική παρειά των Τ1 · Τ9 = περίμετρος υποστυλώματος × ύψος. R15: Τ2N = 1 φύλλο στην πλευρά ντουλάπας (Τ2N-01, Τ2N-02) · Τ7-01 1 φύλλο προς Υπν.1.

ΕΡΓΟ

ΠΕΝΤΑΟΡΟΦΟ ΚΤΗΡΙΟ ΚΑΤΟΙΚΙΩΝ – ΑΡΓΥΡΟΥΠΟΛΗ
Κωνσταντινουπόλεως 12 & Αγ. Βαρβάρας · Ο.Τ. 103-15
Εργοδότης: INTERKAT Α.Ε. · Κατασκευή: ARKAD Ι.Κ.Ε.

ΘΕΜΑ ΣΧΕΔΙΟΥ

ΕΙΔΗ ΤΟΙΧΟΠΟΙΙΩΝ – Β΄ ΟΡΟΦΟΣ
Είδη τοιχοποιιών · Β΄ ΟΡΟΦΟΣ – Β1
τομές 1:4 · μήκη – εμβαδά ανά είδος

ΒΑΣΗ

Βάση: κάτοψη τοιχοποιιών Τ-01 · κάτοψη Α-10-2F

ΑΡ. ΣΧΕΔΙΟΥ

Τ-02
Κλίμακα 1:4 · Α3
05/11/2026 · R16

ΠΡΟΜΕΤΡΗΣΗ ΥΛΙΚΩΝ ΤΟΙΧΟΠΟΙΙΩΝ – Β΄ ΟΡΟΦΟΣ – Β1

από την κάτοψη Τ-01 · Η = 2,90 m (δάπεδο πλάκας – κάτω παρειά πλάκας) · μήκη στον άξονα κάθε τοίχου, χωρίς αφαίρεση κουφωμάτων (οι τοίχοι ορίζονται μεταξύ ανοιγμάτων) · R15

Είδος	Περιγραφή	Τοίχοι	Μήκος m	Επιφ. m²	Γυψοσ. κοινή m²	Γυψοσ. ανθυγρή m²	Γυψοσ. πυράντ. m²	Σκελετός CW m	Οδηγός UW m	Πετροβάμβ. m²	Θερμοτούβλα τεμ.	Κονίαμα m³	Κόλλα kg
T1	Εξωτερική οπτοπλινθοδομή · 25 cm T1-01, T1-02, T1-03, T1-04, T1-05, T1-06, T1-07, T1-08, T1-09, T1-10, T1-11, T1-12	12	9,52	27,61	–	–	–	–	–	–	461	0,41	–
T4	Έρκερ – απλή οπτοπλινθοδομή · 11 cm T4-01, T4-02, T4-03, T4-04, T4-05, T4-06, T4-07, T4-08, T4-09, T4-10, T4-11, T4-12, T4-13, T4-14, T4-15	15	12,02	34,85	–	–	–	–	–	–	1.342	0,69	–
T5	Οπτοπλινθοδομή πυρήνα · 10 cm T5-01, T5-02	2	1,90	5,51	–	–	–	–	–	–	92	0,03	–
T3	Επένδυση τοίχου · 5,5 cm T3-01, T3-02, T3-03, T3-04, T3-05, T3-06, T3-07, T3-08, T3-09, T3-10	10	7,40	21,45	42,9	–	–	81,2	14,8	–	–	–	–
T9	Επένδυση υποστυλώματος · 2,5 cm T9-01, T9-02, T9-03, T9-04, T9-05	5	5,75	16,68	16,7	–	–	–	–	–	–	–	66,7
T2	Χώρισμα γυψοσανίδας · 10 cm T2-01, T2-02, T2-03, T2-04, T2-06, T2-07, T2-08	7	9,75	30,38	87,3	34,2	–	81,2	19,5	–	–	–	–
T2N	Χώρισμα γυψ, – πλευρά ντουλάπας · 8,75 cm T2N-01, T2N-02	2	2,85	8,27	24,8	–	–	23,2	5,7	–	–	–	–
T2A	Χώρισμα γυψοσανίδας 15 · 15 cm T2A-01	1	1,55	4,49	9,0	9,0	–	11,6	3,1	4,5	–	–	–
T7	Τοίχος λεκάνης WC · 25 cm T7-01, T7-02	2	3,95	11,46	15,8	22,9	–	58,0	15,8	–	–	–	–
T6	Τοίχος κλιμακοστασίου · 15 cm T6-01, T6-02, T6-03	3	5,06	15,35	–	–	61,4	37,7	10,1	15,4	–	–	–
T8	Τοίχος shaft · 10 cm T8-01	1	1,35	3,91	7,8	–	–	11,6	2,7	–	–	–	–

ΛΙΣΤΑ ΠΑΡΑΓΓΕΛΙΑΣ (με φύρα: γυψοσανίδες +10 %, προφίλ +5 %)

Γυψοσανίδα κοινή 12,5 mm 1,20 × 3,00	**224,7 m²**	63 φύλλα
Γυψοσανίδα ανθυγρή (H2) 12,5 mm 1,20 × 3,00 – λουτρά: τοίχοι + οροφές (6,1 m² οροφές)	**79,4 m²**	23 φύλλα
Γυψοσανίδα πυράντοχη (F) 12,5 mm 1,20 × 3,00 – κλιμακοστάσιο	**67,6 m²**	19 φύλλα
Προφίλ CW50 (3,00 m)	**152,2 m**	51 τεμ.
Προφίλ CW30 (3,00 m)	**115,7 m**	39 τεμ.
Προφίλ CW100 (3,00 m)	**51,8 m**	18 τεμ.
Προφίλ UW50 (3,00 m)	**37,6 m**	13 τεμ.
Προφίλ UW30 (3,00 m)	**23,8 m**	8 τεμ.
Προφίλ UW100 (3,00 m)	**13,9 m**	5 τεμ.
Προφίλ CD60 (3,00 m) – ψευδοροφές λουτρών	**20,4 m**	7 τεμ.
Προφίλ UD28 (3,00 m) – ψευδοροφές λουτρών	**15,1 m**	6 τεμ.
Πετροβάμβακας 50 / 100 mm (T2A, T6)	**19,8 m²**	
Γυψόκολλα για κολλητή γυψοσανίδα (T9) ≈ 4 kg/m²	**66,7 kg**	3 σακιά 25 kg
Βίδες γυψοσανίδας TN 25 / 35 ≈ 22 τεμ/m² φύλλου	**7.434 τεμ.**	8 κουτιά 1.000
Στόκος αρμών ≈ 0,45 kg/m² τελικής επιφάνειας	**76,0 kg**	4 σακιά 25 kg
Ταινία αρμών ≈ 1,6 m/m² τελικής επιφάνειας	**270,3 m**	4 ρολά 90 m
Αναρτήσεις ψευδοροφής λουτρών (≈ 1,3 / m²)	**8 τεμ.**	
Θερμοτούβλο κάθετων οπών 25 (30 × 25 × 19) – T1	**484 τεμ.**	+5 % σπασίματα
Απλό τούβλο 6οπο 9 × 12 × 19 – T4 έρκερ	**1.409 τεμ.**	+5 % σπασίματα
Θερμοτούβλο κάθετων οπών 10 (30 × 10 × 19) – T5 πυρήνα	**97 τεμ.**	+5 % σπασίματα
Κονίαμα δόμησης	**1,14 m³**	

ΣΗΜΕΙΩΣΕΙΣ ΚΑΤΟΨΗΣ

• Θέσεις τοίχων και ανοιγμάτων όπως η κάτοψη Α-10-2F (Rev.11). Διαστάσεις στο τούβλο / μπετό, χωρίς τη θερμοπρόσοψη (κίτρινη λωρίδα 10 cm).
• ΝΤΟΥΛΑΠΕΣ ΧΩΝΕΥΤΕΣ (R15/R16): δωματίων βάθος 0,60 · πλυντηρίου 0,70. Οι τοίχοι / πεσσοί που τις πλαισιώνουν έχουν ακριβώς το βάθος της ντουλάπας (T2N-02 0,70)· μόνο στον T1-05 περιθώριο +0,03 (ως 1,38). Πίσω και δίπλα σε ντουλάπα καμία επένδυση T3 / T9, ΕΚΤΟΣ παραστάδων κουφωμάτων.
• ΚΟΥΦΩΜΑΤΑ ΑΛΟΥΜΙΝΙΟΥ (R16): τοποθετούνται στη μέση του τοίχου· οι λαμπάδες πρέπει να είναι ισοπαχείς και από τις δύο πλευρές → επένδυση γυψοσανίδας T3 και στις δύο παραστάδες κάθε κουφώματος (T3-06 στον T1-05 μένει, δίπλα στη ντουλάπα).
• T1-05: κόπηκε στο 1,38 (ντουλάπα Υπν.2 0,60 + 0,03). Το W2.06 (1,00×2,40) μετατοπίζεται 7 cm βόρεια: 1,38–2,38 (εγκρίθηκε από τον ιδιοκτήτη 05/11 – να ενημερωθεί ο αρχιτέκτονας).
• Υπν.1: ντουλάπα 0,60 (x 4,30–4,90, y 0,80–3,25) ανάμεσα στον T2-01 και την Κ2. Το κενό προς τον βόρειο τοίχο (x 4,30–4,57 × y 0,165–0,80) ΔΕΝ κτίζεται: γεμίζει με ξυλουργικό που συνεχίζει τη ντουλάπα (βιβλιοθήκη / κομοδίνο). Πόρτα 3,40–4,20.
• ΤΟΙΧΟΙ ΠΟΥ ΒΛΕΠΟΥΝ ΣΕ ΝΤΟΥΛΑΠΑ: 1 φύλλο γυψοσανίδας στην πλευρά της ντουλάπας (T2N-01, T2N-02 · T7-01 πλευρά Υπν.1).
• ΛΟΥΤΡΑ: σχεδιάζονται μόνο πάγκος νιπτήρα βάθους 0,50, λεκάνη και ένα γυάλινο διαχωριστικό ντους 0,70. Ντους 0,70–1,00 (λουτρό 1,00×0,80 · λουτρό γονέων 1,00×0,90). Λουτρό: ντους βόρεια (0,80), γυαλί 0,70 στο y 1,60 από τον T7-01. Λουτρό γονέων: ντους στη δυτική εσοχή (W2.09), γυαλί 0,70 στο x 1,20 από τον νότιο τοίχο.
• ΤΟΙΧΟΙ ΛΕΚΑΝΗΣ Τ7: 2 γυψ. + CW 50 (καζανάκι γυψοσανίδας) + κενό 12 + CW 30 + 2 γυψ. = 25 cm. T7-01: σταθερή η παρειά του λουτροϋ. T7-02: σταθερή η παρειά του Υπν.1.
• ΟΠΟΥ ΠΛΑΚΑΚΙ Ή ΝΤΟΥΛΑΠΑ: χωρίς γυψοσανίδα σε τούβλο / μπετό. Επενδύσεις T3 / T9 σε ενιαίο επίπεδο, χωρίς δόντια.
• ΠΟΡΤΕΣ (R16): ανοίγουν μέσα στον χώρο που εξυπηρετούν. Υπν.1 μεντεσές δυτικά (3,40), λουτρό μεντεσές ανατολικά (6,30), λουτρό γονέων μεντεσές ανατολικά (1,90) ώστε να μένει ελεύθερη η είσοδος του ντους, Υπν.2 μεντεσές νότια (4,25).
• T5-01 κόβεται στην άκρη του εξώστη (x 11,45) με επιστροφή T5-02 στο τοιχείο του ασανσέρ. Υποστυλώματα (σκούρο γκρι) κατά Σ5. Εξώστες από την κάτοψη Α-10-2F.

ΠΑΡΑΔΟΧΕΣ

• Γυψοσανίδες 12,5 mm σε φύλλα 1,20 × 3,00 (ένα φύλλο καθ' ύψος για H = 2,90). Ανθυγρή όπου η πλευρά βλέπει λουτρό / WC, πυράντοχη στον T6.
• Ορθοστάτες CW ανά 60 cm (+1 ανά τοίχο), οδηγοί UW δάπεδο + οροφή. T7: δύο σκελετοί (CW 50 + CW 30). T3: σκελετός 3άρι μίας πλευράς. T9: χωρίς σκελετό, σε γυψόκολλα.
• R15/R16: στην πλευρά ντουλάπας ένα φύλλο (T2N-01, T2N-02, T7-01 προς Υπν.1) – αφαιρέθηκε από τα m² γυψοσανίδας.
• Υπέρθυρα πάνω από τις πόρτες (H – 2,20) προστέθηκαν στο είδος του τοίχου της πόρτας: 5 πόρτες.
• Τούβλα: T1 / T5 θερμομονωτικά κάθετων οπών (30 × 19 → ≈ 16,7 τεμ/m²) · T4 έρκερ απλό τούβλο 6οπο 9 × 12 × 19 δρομικό (≈ 38,5 τεμ/m²). ΠΡΟΣ ΕΠΙΒΕΒΑΙΩΣΗ οι διαστάσεις του προμηθευτή.
• ΛΟΥΤΡΑ: ό,τι είναι μέσα στο λουτρό (τοίχοι και οροφή) με ανθυγρή. Ψευδοροφές λουτρών: 1 × ανθυγρή 12,5 σε CD 60 / UD 28 (Λουτρό 3,06 m² · Λουτρό Γονέων 3,02 m²). Λοιπές ψευδοροφές στο τεύχος ανόψεων.
• Δεν περιλαμβάνονται: σοβάδες, πλακάκια, γωνιόκρανα γυψοσανίδας, κάσες / πρέκια, ηχομονωτικές ταινίες περιμέτρου.
• Όπου πλακάκι ή ντουλάπα: χωρίς γυψοσανίδα σε τούβλο / μπετό – ήδη εξαιρέθηκαν από την προμέτρηση.

ΘΕΡΜΟΠΡΟΣΟΨΗ (ETICS) 10 cm

ύψος ορόφου 3,10 m (με τη μετώπη πλάκας) · ύψη κουφωμάτων από τα label · όπως R14 (τα κουφώματα δεν άλλαξαν)

Περίμετρος όψεων	**47,76 m**
Κουφώματα (9 ανοίγματα)	**−29,61 m²**
Λαμπάδες + ανώφλια (βάθος ≈ 0,15)	**+6,63 m²**
ΚΑΘΑΡΗ ΕΠΙΦΑΝΕΙΑ	**125,1 m²**
Πλάκα EPS γραφιτούχο 10 cm (+5 %) · 263 πλ. 1,00×0,50	**131,3 m²**
Κόλλα – βασικός σοβάς ≈ 9 kg/m² · 46 σακιά	**1.126 kg**
Υαλόπλεγμα 160 g ≈ 1,15 m²/m² · 3 ρολά 50 m²	**143,8 m²**
Βύσματα ETICS ≈ 6 / m²	**750 τεμ.**
Γωνιόκρανα με πλέγμα (κουφώματα)	**46,4 m**
Αστάρι ≈ 0,25 kg/m²	**31 kg**
Τελικός σοβάς ≈ 2,5 kg/m²	**313 kg**