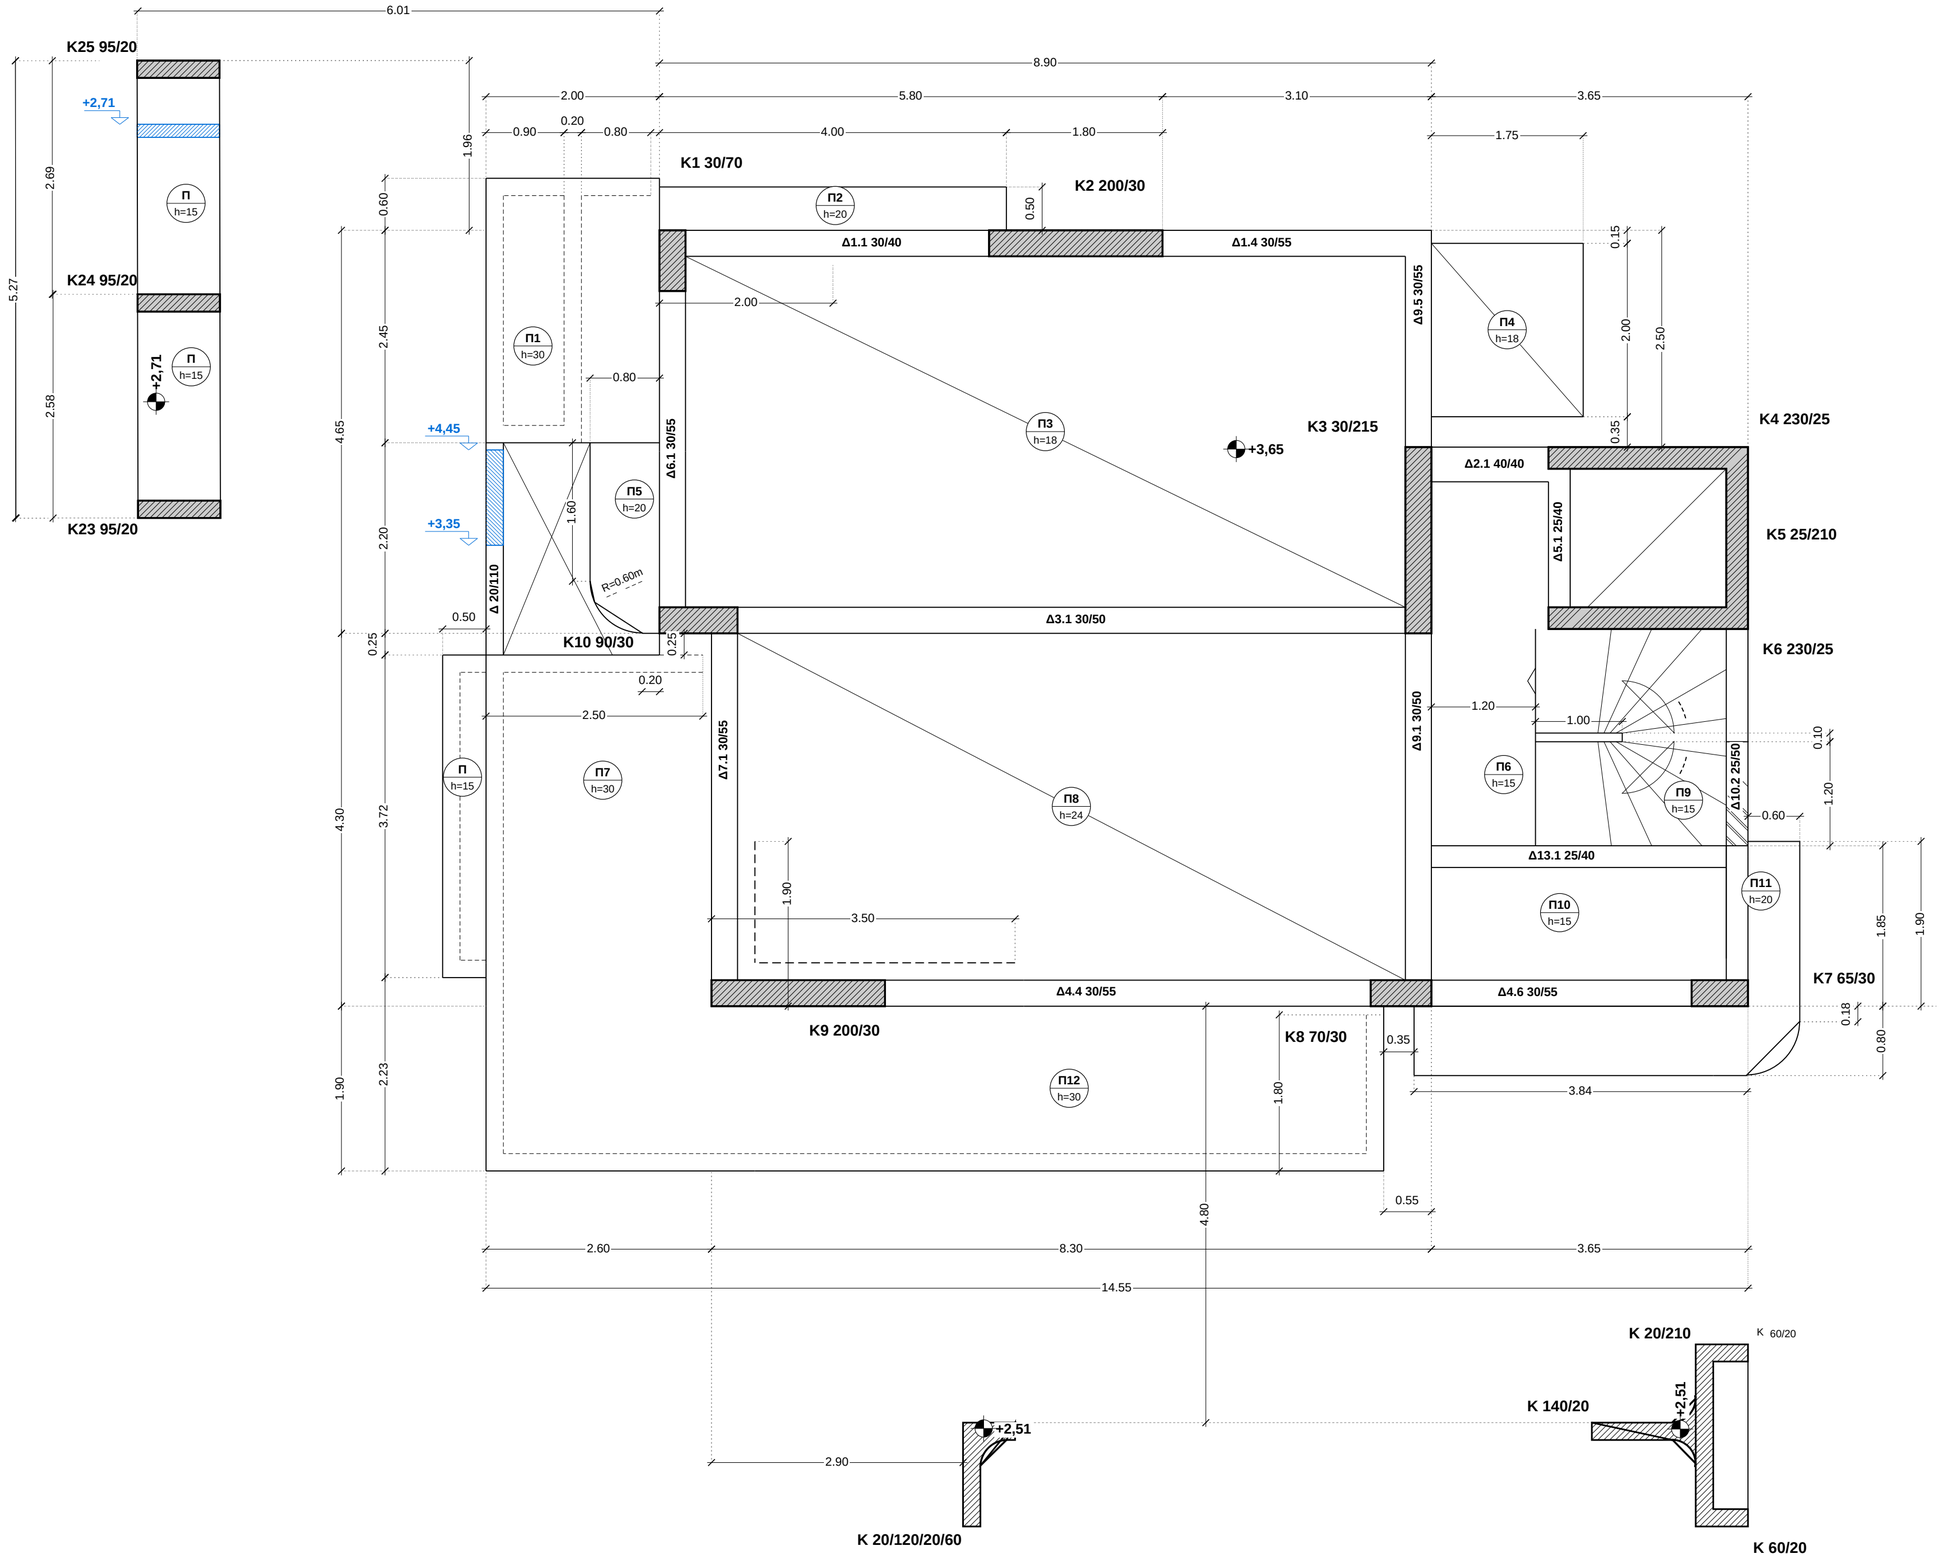


ΚΩΝΣΤΑΝΤΙΝΟΥΠΟΛΕΩΣ 12 & ΑΓ. ΒΑΡΒΑΡΑΣ, ΑΡΓΥΡΟΥΠΟΛΗ – ARKAD Ι.Κ.Ε.
Ξυλότυπος εργοταξίου – χωρίς οπλισμούς

ΟΡΟΦΗ ΙΣΟΓΕΙΟΥ – ΓΕΝΙΚΗ ΔΙΑΤΑΞΗ ΜΕ ΤΑ ΦΥΤΕΥΤΑ **Σ3α**

ΣΤΑΘΜΗ ΑΝΩ ΠΛΑΚΑΣ
+3,65
ΚΛΙΜΑΚΑ 1:50 A2 · 100 %
0 1 2 m

K1 30/70	υποστύλωμα / τοιχείο (cm)
Δ1.1 30/40	δοκός: πλάτος / ύψος (το ύψος μαζί με την πλάκα)
L=3.50	καθαρό μήκος δοκού, παρειά με παρειά
Π3 h=15	πλάκα – πάχος (cm)
+0,30	στάθμη άνω μπετού (m)
μπλε	τομές επί τόπου / φυτευτά και οι στάθμες τους

Διαστάσεις σε m, από γωνία / παρειά κολόνας σε γωνία κολόνας.

ΣΗΜΕΙΩΣΕΙΣ

· Γενική κάτοψη με τα φυτευτά: K23–K25 (δυτικά), τοιχεία εισόδου (νότια). Μεγαλύτερη κλίμακα: Σ3.

Βάση: Σ3_ΕΦ.pdf – ξυλότυπος οροφής ισογείου, Γ. Κόγιας (Drive 19/10/2026).
Οπλισμοί ΜΟΝΟ από το σχέδιο του μελετητή.

Έκδοση R03 – 10/11/2026