
B

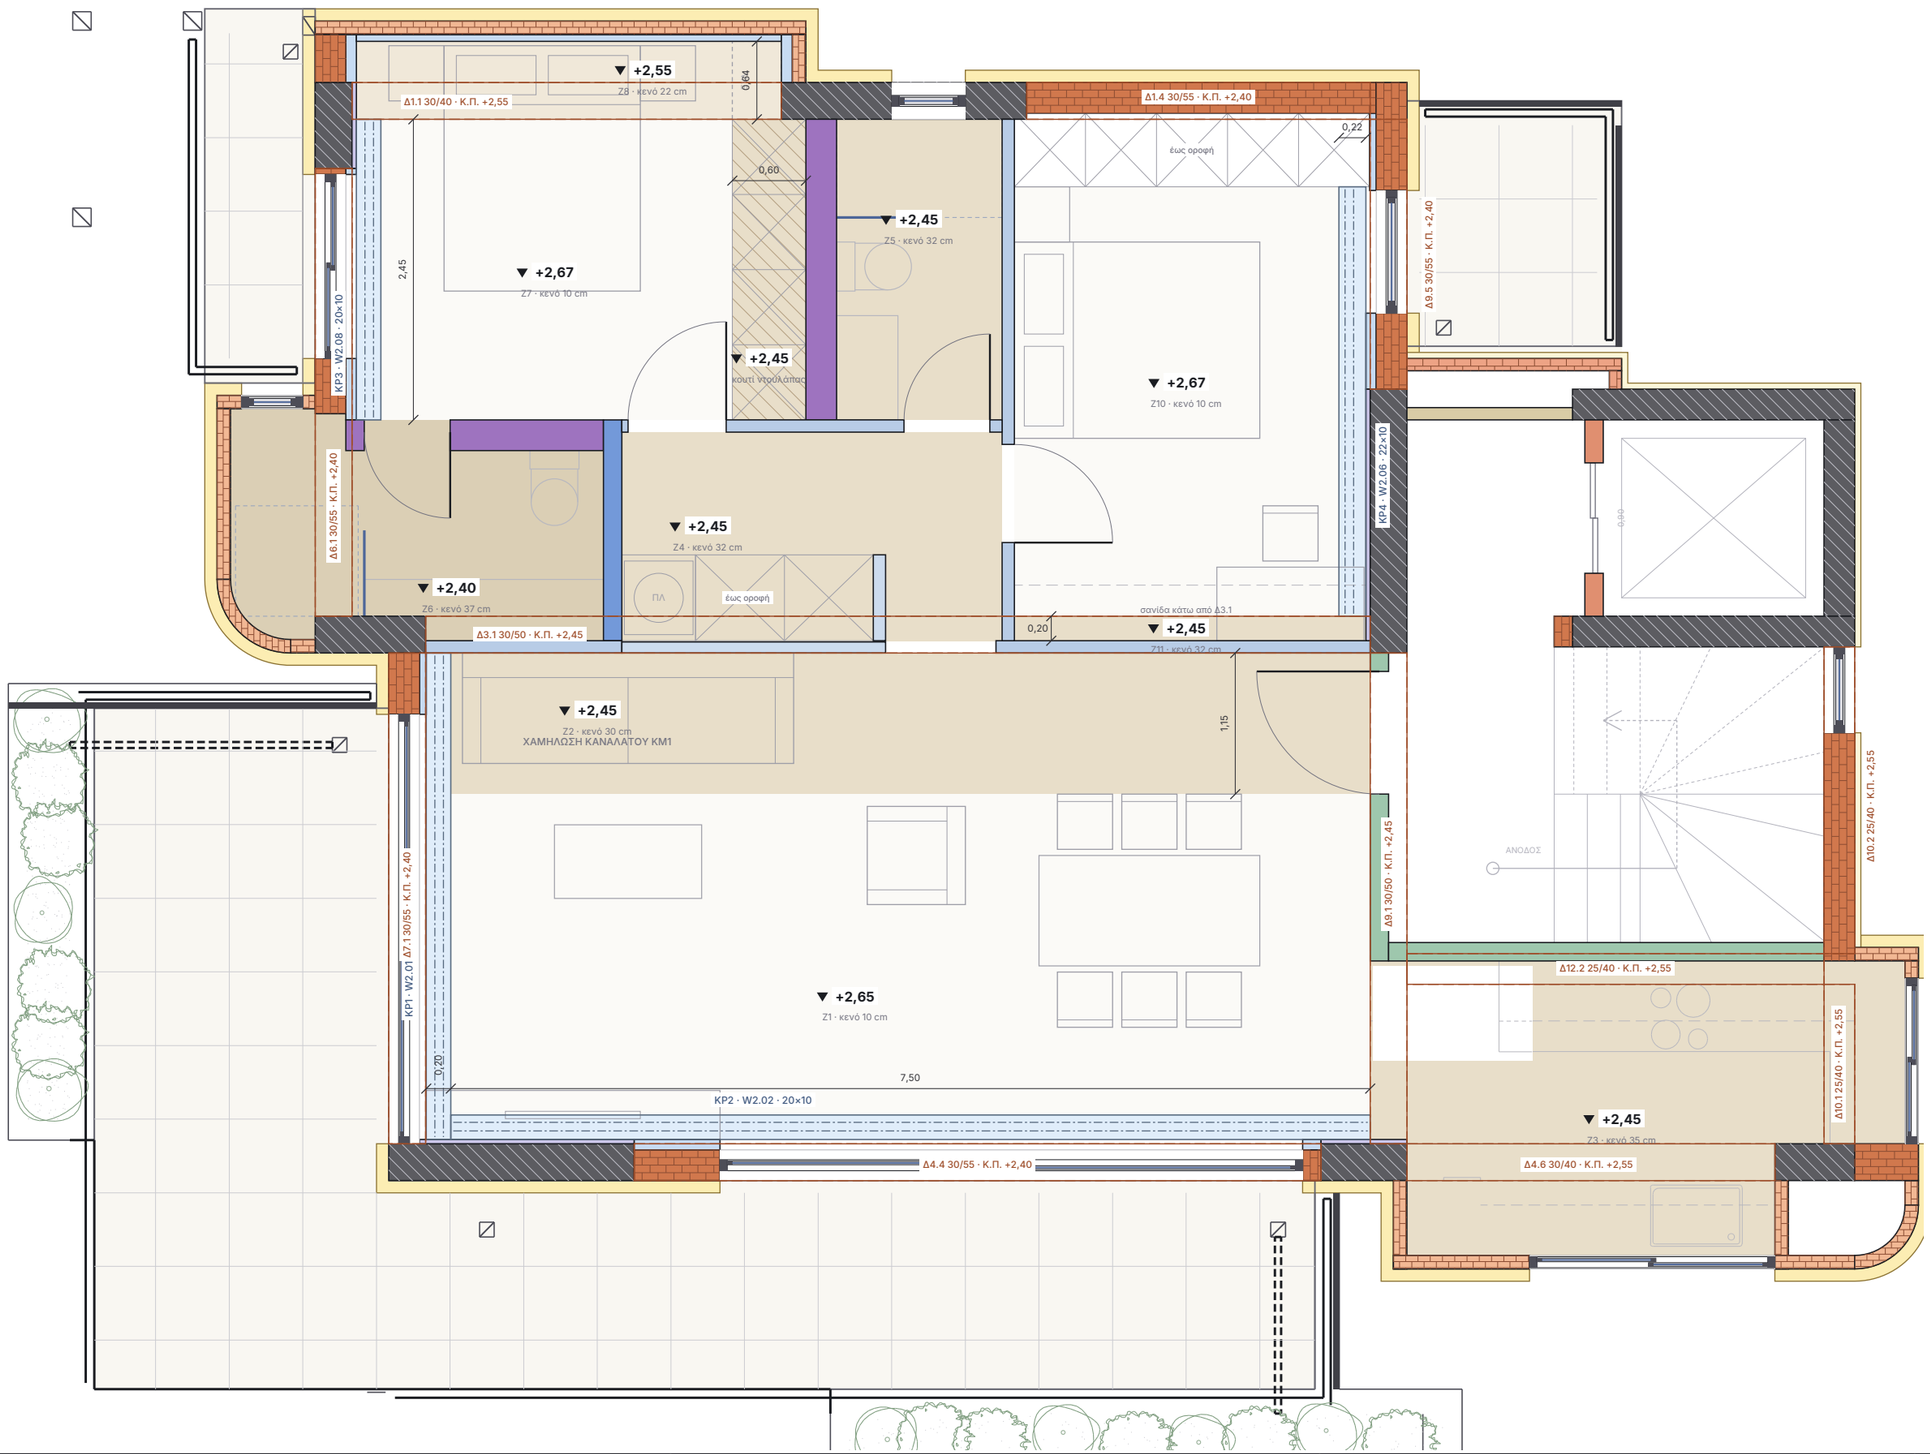

ΣΗΜΕΙΩΣΕΙΣ

Στάθμες από το τελικό δάπεδο του ορόφου (Β΄ +6,90). Πάνω παρειά πλάκας +2,95· κάτω παρειά Π3 h18 +2,77 · Π8 h20 +2,75 · Π10 h15 +2,80.

Κανόνας: πουθενά ψευδοροφή κάτω από κάτω παρειά δοκού· όπου «περασιά» η γυψοσανίδα στη δοκό προσθέτει ≈ 1,5 cm.

Αλλαγές στάθμης MONO: χαμήλωση ΚΜ1 · γραμμή δοκού Δ9.1 (καθιστικό → κουζίνα) · γραμμή Δ1.1 (κεφαλάρι) · μετώπη ντουλάπας Υπν.1 (Π3) · σανίδα κάτω από Δ3.1 στο Υπν.2.

Κουρτινόθηκες: 20 × 10 cm (ΚΡ4 22 cm για το ανοιγοανακλινόμενο W2.06), σε όλο το μήκος του τοίχου, δίπλα (όχι κάτω) από τις δοκούς όψης.


R11: Υπν.1 ως το μέτωπο ντουλάπας 4,20 · λουτρό 5,05–6,40 · ΚΡ4 από 1,35.

ΥΠΟΜΝΗΜΑ

- +2,65 / +2,67 βασική = 10 cm κάτω από την πλάκα (spot σώμα ≤ 75 mm)
- +2,55 περασιά με δοκό 40 (κεφαλάρι Υπν.1)
- +2,45 περασιά με δοκό 50: χαμήλωση ΚΜ1 · χωλ · λουτρό · κουζίνα
- +2,40 περασιά με δοκό 55 (λουτρό γονέων)
- ΚΡ εσοχή κουρτίνας ανοιχτή ως την πλάκα · 2 οδηγοί
- δοκός (Σ5) · Κ.Π. = κάτω παρειά από Τ.Δ.

ΕΡΓΟ	ΘΕΜΑ ΣΧΕΔΙΟΥ	ΒΑΣΗ	ΑΡ. ΣΧΕΔΙΟΥ
ΠΕΝΤΑΟΡΟΦΟ ΚΤΗΡΙΟ ΚΑΤΟΙΚΙΩΝ – ΑΡΓΥΡΟΥΠΟΛΗ Κωνσταντινουπόλεως 12 & Αγ. Βαρβάρας · Ο.Τ. 103-15 Εργοδότης: INTERKAT Α.Ε. · Κατασκευή: ARKAD Ι.Κ.Ε.	**ΑΝΟΨΗ – ΣΤΑΘΜΕΣ · ΔΟΚΟΙ · ΚΟΥΡΤΙΝΕΣ** Στάθμες ψευδοροφής · δοκοί Σ5 · εσοχές κουρτινών Α΄ · Β΄ · Γ΄ ΟΡΟΦΟΣ – Β1 (τυπικός όροφος)	Βάση: τοιχοποιίες Β1 R25 · ξυλότυπος Σ5 (+9,85) · ανόψη R10	**ΑΝ-01** **Κλίμακα 1:50 · Α3** 07/11/2026 · R11

B

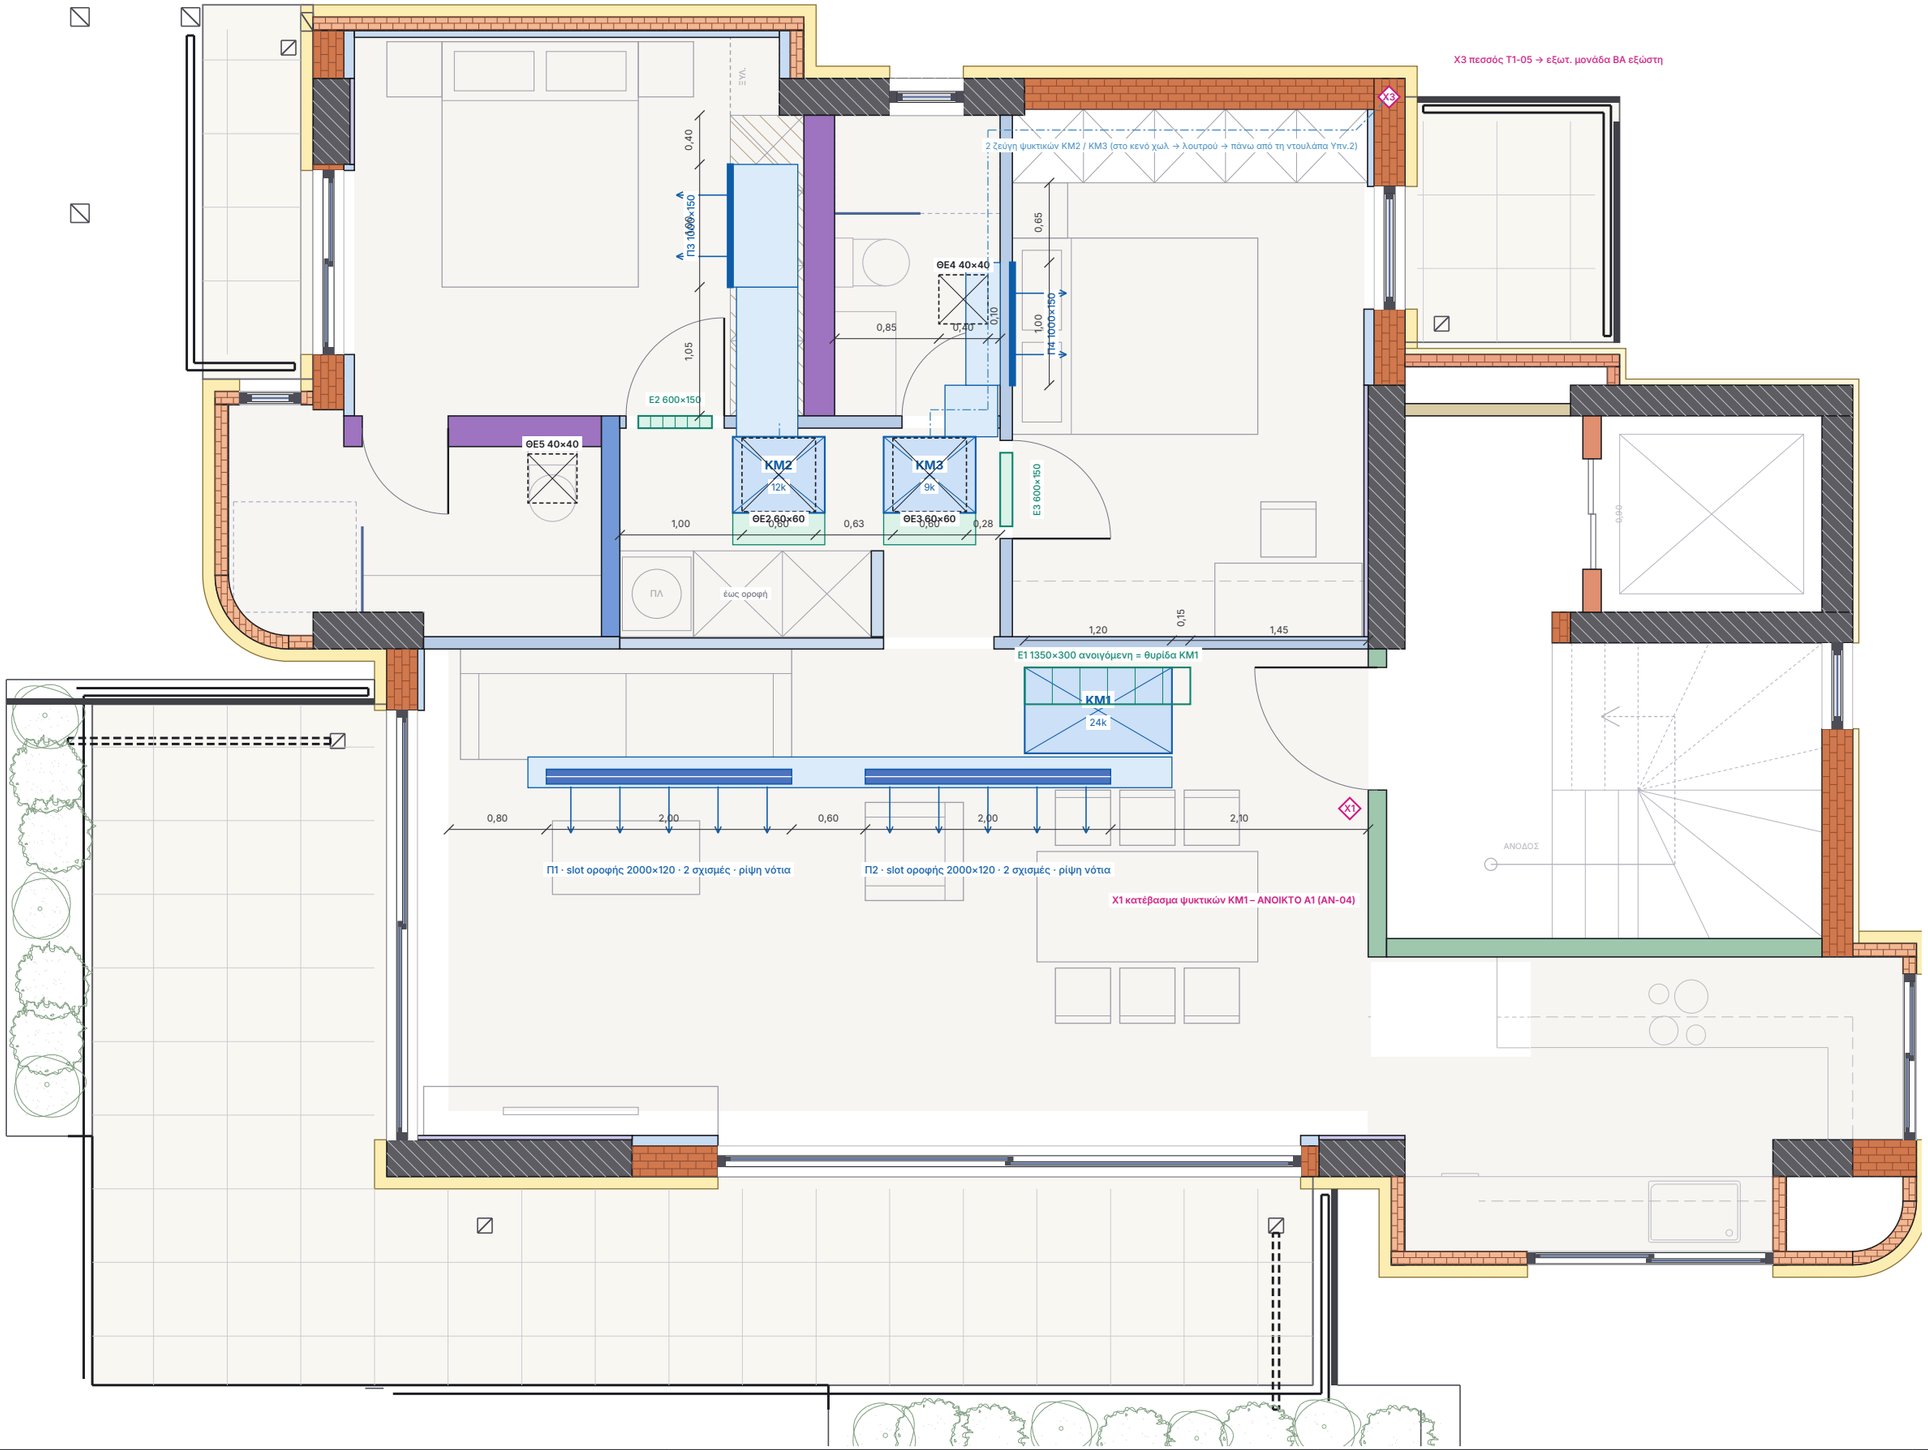

ΣΗΜΕΙΩΣΕΙΣ

Χώρος μονάδων (προδ. 1): χαμήλωση ΚΜ1 +2,45 κάτω από Π8 +2,75 = 30 cm· χωλ +2,45 κάτω από Π3 +2,77 = 32 cm.

ΚΜ1: μονάδα ≤ 245 mm + στηρίγματα 10 mm + σκελετός/γυψοσανίδα 40 mm = 295 ≤ 300 → OPIAKO (5 mm). Μονάδα με πλαϊνά στηρίγματα ανάρτησης· προτιμότερο ύψος ≤ 235 mm.

ΚΜ2 / ΚΜ3: 200 + 10 + 40 = 250 ≤ 320 → περιθώριο 70 mm (κλίση συμπυκνωμάτων / αντλία).

Πρόσβαση: ΚΜ1 από την ανοιγόμενη Ε1 · ΚΜ2 / ΚΜ3 από ΘΕ2 / ΘΕ3 60×60 ακριβώς κάτω από τις μονάδες.

R11: αεραγωγός ΚΜ2 4,25–4,75 και Π3 στο μέτωπο της ντουλάπας 4,20 (ντουλάπα R18 4,20–4,80) · ΘΕ4 έξω από το ντους.

Συμπυκνώματα με αντλία μονάδας μαζί με τα ψυκτικά → σιφώνι / υδρορροή εξώστη (επιβεβαίωση υδραυλικού).

ΥΠΟΜΝΗΜΑ

- ΚΜ καναλάτη μονάδα (slim: ΚΜ1 ≤ 245 mm · ΚΜ2/ΚΜ3 ≤ 200 mm)
- αεραγωγός / plenum προσαγωγής (μονωμένος, στο κενό)
- Π1 / Π2 γραμμικό slot οροφής 2 σχισμών, ρυθμιζόμενη ρίψη
- Π3 / Π4 γραμμικό στόμιο 1000×150 σε μετώπη / τοίχο (εγκεκριμένο)
- Ε στόμιο / κιβώτιο επιστροφής με φίλτρο
- ΘΕ θυρίδα επίσκεψης (αφανής, βαφόμενη)
- Χ κατέβασμα / έξοδος σωληνώσεων – καμία οπή σε σκυρόδεμα

ΕΡΓΟ	ΘΕΜΑ ΣΧΕΔΙΟΥ	ΒΑΣΗ	ΑΡ. ΣΧΕΔΙΟΥ
ΠΕΝΤΑΟΡΟΦΟ ΚΤΗΡΙΟ ΚΑΤΟΙΚΙΩΝ – ΑΡΓΥΡΟΥΠΟΛΗ Κωνσταντινουπόλεως 12 & Αγ. Βαρβάρας · Ο.Τ. 103-15 Εργοδότης: INTERKAT Α.Ε. · Κατασκευή: ARKAD Ι.Κ.Ε.	**ΑΝΟΨΗ – ΚΛΙΜΑΤΙΣΜΟΣ · ΘΥΡΙΔΕΣ** Καναλάτες μονάδες · αεραγωγοί · στόμια · θυρίδες επίσκεψης · ψυκτικά Α΄ · Β΄ · Γ΄ ΟΡΟΦΟΣ – Β1 (τυπικός όροφος)	Βάση: τοιχοποιίες Β1 R25 · ξυλότυπος Σ5 (+9,85) · ανόψη R10	**ΑΝ-02** **Κλίμακα 1:50 · Α3** 07/11/2026 · R11



ΣΗΜΕΙΩΣΕΙΣ

Κατανομή: Υπν. 2 × 2 spots συμμετρικά στην ελεύθερη οροφή · λουτρά 3 (IP65 στο ντους) · κουζίνα μπροστά από τα επάνω ντουλάπια + έρκερ · χωλ / είσοδος στον άξονα της διαδρομής. Σύνολο 24 spots + 2 παροχές + LED3.

Πυρανίχνευση (προδ. 4): σε κάθε κύριο χώρο και στο χωλ· ≥ 0,50 από τοίχους / δοκούς / φωτιστικά, ≥ 1,00 από στόμια προσαγωγής· λουτρά χωρίς ανιχνευτή καπνού (υδρατμοί).

R11 χωλ: ΑΚ4 στον άξονα του διαδρόμου 1,00 (0,50 από τους δύο τοίχους, ανάμεσα στις ΘΕ2 / ΘΕ3)· Χ1 στον άξονα, Χ2 στο κέντρο του περάσματος. Στο R10 ο ΑΚ4 ήταν 0,29 από την ακμή και ≈ 0,30 από spot.

R11: Υ1–Υ4 0,43 από ΚΡ3 / μέτωπο ντουλάπας 4,20 · ΚΡΕΜ1 στο κέντρο της τραπεζαρίας R23.

Οπή spot Ø 75–80 ανάμεσα στα προφίλ CD (όχι πάνω τους)· όπου πέφτει σε προφίλ, μετατόπιση του προφίλ – όχι του spot.

ΥΠΟΜΝΗΜΑ

- χωνευτό spot LED 7–9 W, 2700 K, CRI ≥ 90, UGR < 19, σώμα ≤ 75 mm
- χωνευτό spot IP44 (λουτρά)
- χωνευτό spot IP65 (πάνω από ντους)
- ΚΡΕΜ παροχή οροφής (κουτί + ενίσχυση ανάρτησης)
- ΑΚ ανιχνευτής καπνού (ΕΠ04 · EN 54-7)
- ΑΘ θερμοδιαφορικός ανιχνευτής (κουζίνα · EN 54-5)
- ακτίνα 0,50 m γύρω από ανιχνευτή – κανένας τοίχος / φωτιστικό μέσα
- LED3 κρυφό γραμμικό 3000 K

ΚΑΘΙΣΤΙΚΟ – ΤΡΑΠΕΖΑΡΙΑ: χωρίς spots – παροχές ΚΡΕΜ0 / ΚΡΕΜ1 (απόφαση ιδιοκτήτη R02, επιβεβαίωση 07/11)

ΕΡΓΟ

ΠΕΝΤΑΟΡΟΦΟ ΚΤΗΡΙΟ ΚΑΤΟΙΚΙΩΝ – ΑΡΓΥΡΟΥΠΟΛΗ
Κωνσταντινουπόλεως 12 & Αγ. Βαρβάρας · Ο.Τ. 103-15
Εργοδότης: INTERKAT Α.Ε. · Κατασκευή: ARKAD Ι.Κ.Ε.

ΘΕΜΑ ΣΧΕΔΙΟΥ

ΑΝΟΨΗ – ΦΩΤΙΣΜΟΣ · ΠΥΡΑΝΙΧΝΕΥΣΗ
Χωνευτά spots · παροχές · κρυφό LED · ανιχνευτές · Wi-Fi
Α΄ · Β΄ · Γ΄ ΟΡΟΦΟΣ – Β1 (τυπικός όροφος)

ΒΑΣΗ

Βάση: τοιχοποιίες Β1 R25 · ξυλότυπος Σ5 (+9,85) · ανόψη R10

ΑΡ. ΣΧΕΔΙΟΥ

AN-03
Κλίμακα 1:50 · A3
07/11/2026 · R11

ΣΥΜΜΟΡΦΩΣΗ ΜΕ ΤΙΣ ΠΡΟΔΙΑΓΡΑΦΕΣ (ιδιοκτήτης 07/11/2026)

1 Κλιματισμός — Καναλάτη σε καθιστικό (ΚΜ1 24k), Υπν.1 (ΚΜ2 12k), Υπν.2 (ΚΜ3 9k) · κουζίνα από την ΚΜ1 (ΕΓΚΕΚΡ.) · slot Π1/Π2 στο καθιστικό, γραμμικά Π3/Π4 στα υπνοδωμάτια (ΕΓΚΕΚΡ.) · χώρος 30 / 32 cm – ΚΜ1 οριακή (5 mm) · θυρίδες Ε1 / ΘΕ2 / ΘΕ3.

2 Κουρτίνες — ΚΡ1–ΚΡ4 σε όλα τα ανοίγματα καθιστικού / υπνοδωματίων, 20 (22) × 10 cm, 2 οδηγοί, ανοιχτές ως την πλάκα, δίπλα στις δοκούς όψης.

3 Φωτισμός — 24 χωνευτά spots σε υπνοδωμάτια, λουτρά, χωλ, είσοδο, κουζίνα (IP44/IP65 στα λουτρά) · καθιστικό με ΚΡΕΜ0/ΚΡΕΜ1 (ΕΓΚΕΚΡ.) · κανένα spot κάτω από μονάδα / αεραγωγό / σε θυρίδα · κενό ≥ 88 mm πάνω από κάθε spot.

4 Πυρανίχνευση — ΑΚ1–ΑΚ4 καπνού + ΑΘ5 θερμοδιαφορικός κουζίνας · όλοι ≥ 0,50 από τοίχους / δοκούς / φωτιστικά και ≥ 1,00 από στόμια προσαγωγής.

5 Κατασκευή — Βασική 10 cm κάτω από την πλάκα · μεγαλύτερη καταβίβαση μόνο στις καναλάτες (+2,45) · περασιά με τις δοκούς · μία σανίδα κάτω από τη Δ3.1 στο Υπν.2 (εξαίρεση) · κανένα δόντι.

6 Γενική αρχή — 5 στάθμες σε όλο το διαμέρισμα, κάθε αλλαγή πάνω σε γραμμή δοκού ή μετώπη ντουλάπας.

ΕΓΚΕΚΡΙΜΕΝΕΣ ΑΠΟΚΛΙΣΕΙΣ (ιδιοκτήτης 07/11/2026)

- Καθιστικό – τραπεζαρία χωρίς spots (απόφαση R02· «η νέα προδιαγραφή δεν υπερισχύει»).
- Κουζίνα χωρίς δική της καναλάτη – καλύπτεται από την ΚΜ1 24k.
- Π3 / Π4 υπνοδωματίων: γραμμικά στόμια 1000×150 σε μετώπη / τοίχο, όχι slot.
- Μονάδες slim ≤ 245 mm (ΚΜ1) / ≤ 200 mm (ΚΜ2, ΚΜ3) ως παραδοχή μέχρι την επιλογή μοντέλου.

ΑΛΛΑΓΕΣ R10 → R11

- Βάση: τοιχοποιίες Β1 R25 (Α΄·Β΄·Γ΄) αντί Rev.11 – όλα τα στοιχεία ξαναελέγχθηκαν πάνω στις νέες παρειές.
- Υπν.1: ντουλάπα 4,20–4,80 (R18) → κουτί ντουλάπας, αεραγωγός ΚΜ2, plenum και στόμιο Π3 10 cm δυτικά (Π3 στο x 4,20)· ο αεραγωγός 4,25–4,75 δεν ακουμπά πια τον Τ7-01 (4,80). Spots Υ1–Υ4 στο x 1,765 / 3,77 (0,43 από ΚΡ3 και μέτωπο ντουλάπας).
- Λουτρό +10 cm (Τ7-01 4,80–5,05): ζώνη +2,45 στο 5,05–6,40. Θυρίδα ΘΕ4 έξω από το ντους (5,90–6,30 × 2,10–2,50, πάνω από το plenum Π4) – στο R10 έπεφτε στην είσοδο του ντους / γυαλί.
- Χωλ: ΑΚ4 στον άξονα του διαδρόμου (5,21 · 3,85), 0,50 από τους δύο τοίχους – στο R10 ήταν 0,29 από την ακμή του ανοίγματος και ≈ 0,30 από spot. Spots: Χ1 (3,65 · 3,85) στον άξονα, Χ2 στο κέντρο του περάσματος (5,925 · 4,70). Χωλ 2 spots αντί 3.
- ΚΡΕΜ1 στο κέντρο της τραπεζαρίας R23 (7,60 · 7,25) – ήταν 7,50 · 7,575 (τραπέζι του R14).
- ΚΡ4 από το μέτωπο της ντουλάπας Υπν.2 (1,35) – W2.06 στο 1,38–2,38 (R16). Ε2 πάνω από την πόρτα Υπν.1 3,35–4,15 (R22).

ΑΝΟΙΚΤΑ ΣΗΜΕΙΑ

- Α1 [ΑΠΟΦΑΣΗ] Όδευση ψυκτικών ΚΜ1: στο R08/R09 κατεβαίνουν μέσα στη ντουλάπα εισόδου ΝΤ4 (8,80–9,40 × 6,45–8,15). Στις τοιχοποιίες R22–R25 η ΝΤ4 δεν υπάρχει και η τραπεζαρία (R23) είναι 0,90 από τον τοίχο εισόδου. Η χαμήλωση είναι κλειστή από τις Δ3.1 / Δ9.1 (περασιά +2,45) – οι σωλήνες δεν περνούν πάνω από δοκό χωρίς οπή. Λύσεις: (α) ΝΤ4 ξανά (τραπεζαρία 0,30 δυτικά) · (β) κανάλι γυψοσανίδας 0,30 × 0,30 από δάπεδο ως οροφή στη γωνία 9,10–9,40 × 6,30–6,60 (δίπλα στη νότια παραστάδα της εισόδου), ντυμένο από έπιπλο εισόδου βάθους 0,30. Πρόταση: (β).
- Α2 [ΜΟΝΤΕΛΟ] Μοντέλα καναλάτων: έλεγχος ύψους (≤ 245 / ≤ 200 mm) και θέσης ηλεκτρικού κουτιού / αντλίας της ΚΜ1 – αν δεν φτάνονται από την ανοιγόμενη Ε1 (300 mm), προστίθεται θυρίδα 40×40 στο ανατολικό άκρο της μονάδας.
- Α3 [ΣΤΑΤΙΚΟΣ] Διατομή Δ10.1 (χωρίς ετικέτα στον Σ5 – θεωρήθηκε 25/40). Δεν επηρεάζει τη στάθμη της κουζίνας (+2,45 ≤ 2,55).
- Α4 [ΕΠΙ ΤΟΠΟΥ] Μέτρηση πλακών / δοκών μετά το ξεκαλούπωμα κάθε ορόφου (Α΄ Σ4 · Β΄ Σ5 · Γ΄ Σ6) πριν τη χάραξη – η ανόψη θεωρεί ίδιους δοκούς στους τρεις τυπικούς ορόφους· οι Σ4 / Σ6 να ελεγχθούν.

ΕΛΕΓΧΟΣ ΣΥΓΚΡΟΥΣΕΩΝ & ΣΤΑΘΜΩΝ – 73 έλεγχοι · ΟΚ 68 · ΟΡΙΑΚΟ 1 · ΕΓΚΕΚΡ. 4 · ΑΠΟΚΛΙΣΗ 0

Αυτόματος έλεγχος από το μοντέλο (code/anopseis/checks.py): στάθμες ↔ δοκοί · κενό μονάδων · θυρίδες · spots ↔ ζώνες / θυρίδες / μονάδες / αεραγωγοί / κουρτινόθηκες · ανιχνευτές ↔ τοίχοι / φωτιστικά / στόμια · κουρτινόθηκες ↔ κουφώματα / δοκοί.

ΚΩΔ.	ΚΑΤΑΣΤ.	ΣΤΟΙΧΕΙΟ	ΜΕΤΡΗΣΗ
ΣΤ01	ΟΚ	Ζ3 ΚΟΥΖΙΝΑ ↔ Δ9.1 30/50 (Κ.Π. +2.45)	οροφή +2.45 · περασιά
ΣΤ02	ΟΚ	Ζ3 ΚΟΥΖΙΝΑ ↔ Δ4.6 30/40 (Κ.Π. +2.55)	οροφή +2.45 · κρυμμένη 10 cm
ΣΤ03	ΟΚ	Ζ3 ΚΟΥΖΙΝΑ ↔ Δ12.2 25/40 (Κ.Π. +2.55)	οροφή +2.45 · κρυμμένη 10 cm
ΣΤ04	ΟΚ	Ζ3 ΚΟΥΖΙΝΑ ↔ Δ10.1 25/40 (Κ.Π. +2.55)	οροφή +2.45 · κρυμμένη 10 cm
ΣΤ05	ΟΚ	Ζ4 ΧΩΛ ↔ Δ3.1 30/50 (Κ.Π. +2.45)	οροφή +2.45 · περασιά
ΣΤ06	ΟΚ	Ζ6 ΛΟΥΤΡΟ ΓΟΝΕΩΝ ↔ Δ6.1 30/55 (Κ.Π. +2.40)	οροφή +2.40 · περασιά
ΣΤ07	ΟΚ	Ζ6 ΛΟΥΤΡΟ ΓΟΝΕΩΝ ↔ Δ3.1 30/50 (Κ.Π. +2.45)	οροφή +2.40 · κρυμμένη 5 cm
ΣΤ08	ΟΚ	Ζ8 ΚΕΦΑΛΑΡΙ ΥΠΝ.1 (έρκερ) ↔ Δ1.1 30/40 (Κ.Π. +2.55)	οροφή +2.55 · περασιά
ΣΤ09	ΟΚ	Ζ11 ΣΑΝΙΔΑ ΚΑΤΩ ΑΠΟ Δ3.1 (Υπν.2) ↔ Δ3.1 30/50 (Κ.Π. +2.45)	οροφή +2.45 · περασιά
ΚΛ-ΚΜ1	ΟΡΙΑΚΟ	ΚΜ1 24.000 Btu/h – καθιστικό – τραπεζαρία – κουζίνα	κενό 300 mm · περιθώριο +5 mm
ΘΕ-ΚΜ1	ΟΚ	ΚΜ1 – πρόσβαση συντήρησης	Ε1
ΚΛ-ΚΜ2	ΟΚ	ΚΜ2 12.000 Btu/h – Υπνοδωμάτιο 1	κενό 320 mm · περιθώριο +70 mm
ΘΕ-ΚΜ2	ΟΚ	ΚΜ2 – πρόσβαση συντήρησης	ΘΕ2
ΚΛ-ΚΜ3	ΟΚ	ΚΜ3 9.000 Btu/h – Υπνοδωμάτιο 2	κενό 320 mm · περιθώριο +70 mm
ΘΕ-ΚΜ3	ΟΚ	ΚΜ3 – πρόσβαση συντήρησης	ΘΕ3
ΚΔ-ΚΜ1	ΟΚ	Καθιστικό – τραπεζαρία	ΚΜ1
ΚΔ-ΚΜ2	ΟΚ	Υπνοδωμάτιο 1	ΚΜ2
ΚΔ-ΚΜ3	ΟΚ	Υπνοδωμάτιο 2	ΚΜ3
ΚΔ-ΚΟΥΖ	ΕΓΚΕΚΡ.	Κουζίνα	από την ΚΜ1 (ανοιχτή στο καθιστικό)
ΣΤ-Π1	ΟΚ	Π1 slot οροφής 2000×120 · 2 σχισμές	μέσα
ΣΤ-Π2	ΟΚ	Π2 slot οροφής 2000×120 · 2 σχισμές	μέσα
ΣΤ-Π3	ΕΓΚΕΚΡ.	Π3 γραμμικό 1000×150 · μετώπη ντουλάπας +2,48…+2,63	γραμμικό στόμιο μετώπης / τοίχου
ΣΤ-Π4	ΕΓΚΕΚΡ.	Π4 γραμμικό 1000×150 · τοίχος +2,48…+2,63	γραμμικό στόμιο μετώπης / τοίχου
SP-Υ1	ΟΚ	Υ1 spot (1.765 · 1.550) – ΥΠΝΟΔΩΜΑΤΙΟ 1	κενό 88 mm · άκρη 0.63
SP-Υ2	ΟΚ	Υ2 spot (3.770 · 1.550) – ΥΠΝΟΔΩΜΑΤΙΟ 1	κενό 88 mm · άκρη 0.43
SP-Υ3	ΟΚ	Υ3 spot (1.765 · 2.650) – ΥΠΝΟΔΩΜΑΤΙΟ 1	κενό 88 mm · άκρη 0.60
SP-Υ4	ΟΚ	Υ4 spot (3.770 · 2.650) – ΥΠΝΟΔΩΜΑΤΙΟ 1	κενό 88 mm · άκρη 0.43
SP-Υ5	ΟΚ	Υ5 spot (7.130 · 1.850) – ΥΠΝΟΔΩΜΑΤΙΟ 2	κενό 88 mm · άκρη 0.50
SP-Υ6	ΟΚ	Υ6 spot (8.530 · 1.850) – ΥΠΝΟΔΩΜΑΤΙΟ 2	κενό 88 mm · άκρη 0.50
SP-Υ7	ΟΚ	Υ7 spot (7.130 · 4.250) – ΥΠΝΟΔΩΜΑΤΙΟ 2	κενό 88 mm · άκρη 0.60
SP-Υ8	ΟΚ	Υ8 spot (8.530 · 4.250) – ΥΠΝΟΔΩΜΑΤΙΟ 2	κενό 88 mm · άκρη 0.60
SP-Λ1	ΟΚ	Λ1 spot IP65 (5.600 · 1.250) – ΛΟΥΤΡΟ	κενό 307 mm · άκρη 0.45
SP-Λ2	ΟΚ	Λ2 spot IP44 (5.600 · 2.050) – ΛΟΥΤΡΟ	κενό 307 mm · άκρη 0.55
SP-Λ3	ΟΚ	Λ3 spot IP44 (5.600 · 2.850) – ΛΟΥΤΡΟ	κενό 307 mm · άκρη 0.40
SP-Λ4	ΟΚ	Λ4 spot IP65 (0.470 · 4.150) – ΛΟΥΤΡΟ ΓΟΝΕΩΝ	κενό 358 mm · άκρη 0.36
SP-Λ5	ΟΚ	Λ5 spot IP44 (1.600 · 4.150) – ΛΟΥΤΡΟ ΓΟΝΕΩΝ	κενό 358 mm · άκρη 0.70
SP-Λ6	ΟΚ	Λ6 spot IP44 (2.500 · 4.150) – ΛΟΥΤΡΟ ΓΟΝΕΩΝ	κενό 358 mm · άκρη 0.65

ΚΩΔ.	ΚΑΤΑΣΤ.	ΣΤΟΙΧΕΙΟ	ΜΕΤΡΗΣΗ
SP-Χ1	ΟΚ	Χ1 spot (3.650 · 3.850) – ΧΩΛ	κενό 307 mm · άκρη 0.35
SP-Χ2	ΟΚ	Χ2 spot (5.925 · 4.700) – ΧΩΛ	κενό 307 mm · άκρη 0.35
SP-Ε1	ΟΚ	Ε1 spot (8.800 · 5.500) – ΧΑΜΗΛΩΣΗ ΚΑΝΑΛΑΤΟΥ / ΕΙΣΟΔΟΣ	κενό 287 mm · άκρη 0.35
SP-Ε2	ΟΚ	Ε2 spot (8.800 · 6.050) – ΧΑΜΗΛΩΣΗ ΚΑΝΑΛΑΤΟΥ / ΕΙΣΟΔΟΣ	κενό 287 mm · άκρη 0.25
SP-Μ1	ΟΚ	Μ1 spot (10.950 · 8.400) – ΚΟΥΖΙΝΑ	κενό 337 mm · άκρη 0.74
SP-Μ2	ΟΚ	Μ2 spot (11.850 · 8.400) – ΚΟΥΖΙΝΑ	κενό 337 mm · άκρη 0.74
SP-Μ3	ΟΚ	Μ3 spot (12.750 · 8.400) – ΚΟΥΖΙΝΑ	κενό 337 mm · άκρη 0.74
SP-Μ4	ΟΚ	Μ4 spot (11.200 · 9.620) – ΚΟΥΖΙΝΑ	κενό 287 mm · άκρη 0.44
SP-Μ5	ΟΚ	Μ5 spot (12.200 · 9.620) – ΚΟΥΖΙΝΑ	κενό 287 mm · άκρη 0.44
SP-Μ6	ΟΚ	Μ6 spot (13.550 · 8.600) – ΚΟΥΖΙΝΑ	κενό 337 mm · άκρη 0.21
SP-ΚΑΘ	ΕΓΚΕΚΡ.	Καθιστικό – τραπεζαρία	παροχές ΚΡΕΜ0 / ΚΡΕΜ1 (απόφαση R02)
ΠΥ-ΑΚ1	ΟΚ	ΑΚ1 καπνού (8.24 · 7.17) – καθιστικό – τραπεζαρία (R05: 0,55 από…	τοίχος 0.87 · ΚΡΕΜ1 0.64 · Π2 1.32
ΠΥ-ΑΚ2	ΟΚ	ΑΚ2 καπνού (2.30 · 2.75) – Υπνοδωμάτιο 1	τοίχος 0.50 · Υ3 0.54 · Π3 1.96
ΠΥ-ΑΚ3	ΟΚ	ΑΚ3 καπνού (7.83 · 3.60) – Υπνοδωμάτιο 2	τοίχος 1.25 · Υ8 0.96 · Π4 1.44
ΠΥ-ΑΚ4	ΟΚ	ΑΚ4 καπνού (5.21 · 3.85) – χωλ – άξονας διαδρόμου 1,00, ανάμεσ…	τοίχος 0.50 · Λ3 1.07 · Π4 1.53
ΠΥ-ΑΘ5	ΟΚ	ΑΘ5 θερμοδιαφορικός (11.00 · 8.95) – κουζίνα – θερμοδιαφορικός	τοίχος 1.15 · Μ1 0.55 · Π2 4.58
ΠΥ-ΧΩΡ	ΟΚ	Κάλυψη χώρων	καθιστικό · Υπν.1 · Υπν.2 · χωλ · κουζίνα (Θ…
ΘΕ-ΘΕ2	ΟΚ	ΘΕ2 60×60 – ΚΜ2 (φίλτρο, ηλεκτρικό κουτί, αντλία)	ελεύθερη
ΘΕ-ΘΕ3	ΟΚ	ΘΕ3 60×60 – ΚΜ3 (φίλτρο, ηλεκτρικό κουτί, αντλία)	ελεύθερη
ΘΕ-ΘΕ4	ΟΚ	ΘΕ4 40×40 – λουτρό: plenum / ρύθμιση Π4 · έξω από το ντους (R1…	ελεύθερη
ΘΕ-ΘΕ5	ΟΚ	ΘΕ5 40×40 – λουτρό γονέων: αποχέτευση άνω ορόφου (θέση κατ…	ελεύθερη
ΚΡ-ΚΡ1	ΟΚ	ΚΡ1 W2.01 – καθιστικό – Δ · 20 × 10 cm · οδηγοί 7 / 14 cm	πλήρης · βάθος 10 cm
ΚΡ-ΚΡ2	ΟΚ	ΚΡ2 W2.02 – καθιστικό – Ν · 20 × 10 cm · οδηγοί 7 / 14 cm	πλήρης · βάθος 10 cm
ΚΡ-ΚΡ3	ΟΚ	ΚΡ3 W2.08 – Υπν.1 – Δ · 20 × 10 cm · οδηγοί 7 / 14 cm	πλήρης · βάθος 10 cm
ΚΡ-ΚΡ4	ΟΚ	ΚΡ4 W2.06 – Υπν.2 – Α · 22 × 10 cm · οδηγοί 10 / 17 cm (ανοιγοα…	πλήρης · βάθος 10 cm
ΚΡ-W2.03	ΟΚ	W2.03	δεν απαιτείται – κουζίνα – πάνω από τον ν…
ΚΡ-W2.04	ΟΚ	W2.04	δεν απαιτείται – κουζίνα – έρκερ, πάνω από…
ΚΡ-W2.05	ΟΚ	W2.05	δεν απαιτείται – κλιμακοστάσιο (εκτός διαμ…
ΚΡ-W2.07	ΟΚ	W2.07	δεν απαιτείται – λουτρό (στο τοιχείο Κ2)
ΚΡ-W2.09	ΟΚ	W2.09	δεν απαιτείται – λουτρό γονέων (ντους)
ΣΘ-Ζ1	ΟΚ	Ζ1 +2,65 ↔ Ζ2 +2,45	χαμήλωση καναλάτου ΚΜ1 (προδ. 1/5)
ΣΘ-Ζ1	ΟΚ	Ζ1 +2,65 ↔ Ζ3 +2,45	στη γραμμή της δοκού Δ9.1 (περασιά)
ΣΘ-Ζ7	ΟΚ	Ζ7 +2,67 ↔ Ζ8 +2,55	στη γραμμή της δοκού Δ1.1 (κεφαλάρι έρκε…
ΣΘ-Ζ7	ΟΚ	Ζ7 +2,67 ↔ Ζ9 +2,45	μετώπη ντουλάπας Υπν.1 με το στόμιο Π3
ΣΘ-Ζ10	ΟΚ	Ζ10 +2,67 ↔ Ζ11 +2,45	σανίδα κάτω από τη Δ3.1 (εξαίρεση προδ. …
ΣΘ-ΣΥΝ	ΟΚ	Στάθμες στο διαμέρισμα	+2.40 · +2.45 · +2.55 · +2.65 · +2.67 (βασικ…