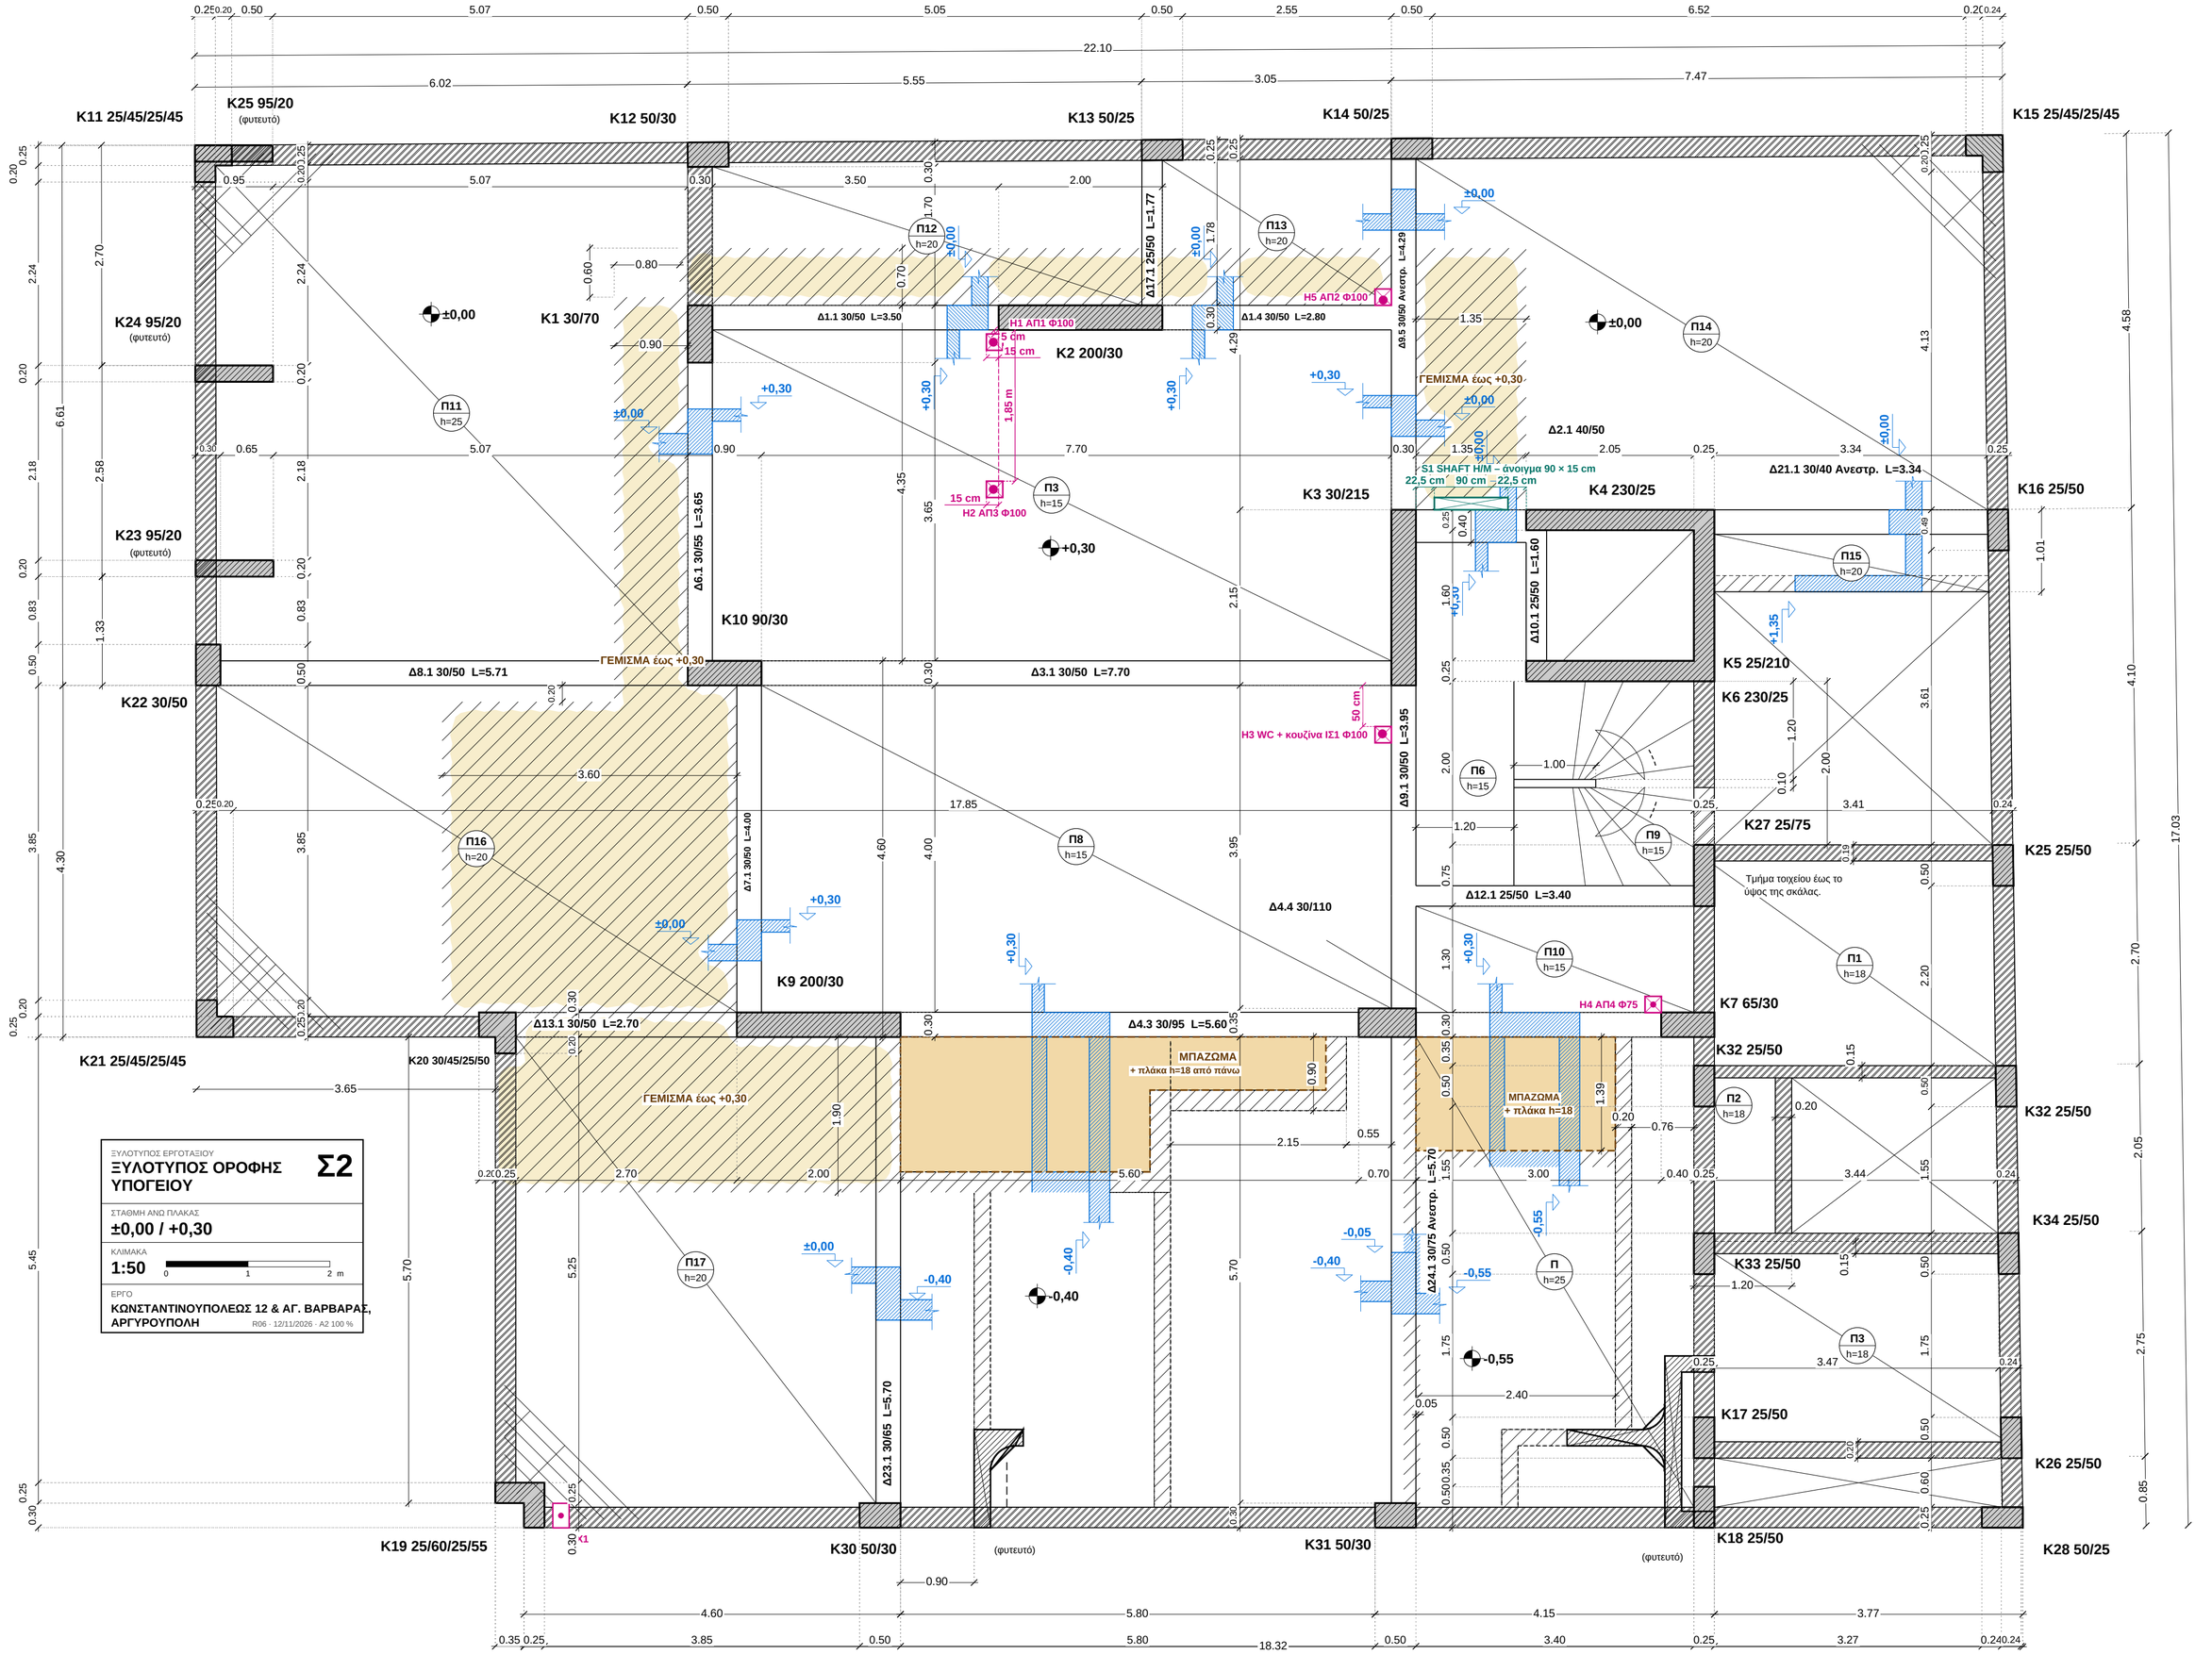

K11 25/45/25/45
K25 95/20
(φυτευτό)
K12 50/30
K13 50/25
K14 50/25
K15 25/45/25/45
K24 95/20
(φυτευτό)
K1 30/70
K2 200/30
K23 95/20
(φυτευτό)
K10 90/30
K3 30/215
K4 230/25
K16 25/50
K22 30/50
K5 25/210
K6 230/25
K27 25/75
K25 25/50
K9 200/30
K7 65/30
K32 25/50
K21 25/45/25/45
K20 30/45/25/50
K34 25/50
K33 25/50
K17 25/50
K26 25/50
K19 25/60/25/55
K30 50/30
(φυτευτό)
K31 50/30
(φυτευτό)
K18 25/50
K28 50/25
Π1 h=18
Π2 h=18
Π3 h=18
Π6 h=15
Π8 h=15
Π9 h=15
Π10 h=15
Π11 h=25
Π12 h=20
Π13 h=20
Π14 h=20
Π15 h=20
Π16 h=20
Π17 h=20
Π3 h=15
Π h=25
Δ1.1 30/50 L=3.50
Δ1.4 30/50 L=2.80
Δ17.1 25/50 L=1.77
Δ9.5 30/50 Ανεστρ. L=4.29
Δ2.1 40/50
Δ21.1 30/40 Ανεστρ. L=3.34
Δ10.1 25/50 L=1.60
Δ6.1 30/55 L=3.65
Δ8.1 30/50 L=5.71
Δ3.1 30/50 L=7.70
Δ9.1 30/50 L=3.95
Δ12.1 25/50 L=3.40
Δ7.1 30/50 L=4.00
Δ13.1 30/50 L=2.70
Δ4.4 30/110
Δ4.3 30/95 L=5.60
Δ24.1 30/75 Ανεστρ. L=5.70
Δ23.1 30/65 L=5.70
Η1 ΑΠ1 Φ100
Η2 ΑΠ3 Φ100
Η3 WC + κουζίνα ΙΣ1 Φ100
Η4 ΑΠ4 Φ75
Η5 ΑΠ2 Φ100
Χ1
S1 SHAFT H/M – άνοιγμα 90 × 15 cm
22.5 cm 90 cm 22.5 cm
ΓΕΜΙΣΜΑ έως +0,30
ΜΠΑΖΩΜΑ
+ πλάκα h=18 από πάνω
ΜΠΑΖΩΜΑ
+ πλάκα h=18
Τμήμα τοιχείου έως το
ύψος της σκάλας.
±0,00
+0,30
-0,40
-0,55
-0,05
1.85 m
15 cm
50 cm
ΞΥΛΟΤΥΠΟΣ ΕΡΓΟΤΑΞΙΟΥ
ΞΥΛΟΤΥΠΟΣ ΟΡΟΦΗΣ ΥΠΟΓΕΙΟΥ
Σ2
ΣΤΑΘΜΗ ΑΝΩ ΠΛΑΚΑΣ
±0,00 / +0,30
ΚΛΙΜΑΚΑ
1:50
0 1 2 m
ΕΡΓΟ
ΚΩΝΣΤΑΝΤΙΝΟΥΠΟΛΕΩΣ 12 & ΑΓ. ΒΑΡΒΑΡΑΣ, ΑΡΓΥΡΟΥΠΟΛΗ
R06 · 12/11/2026 · A2 100 %