
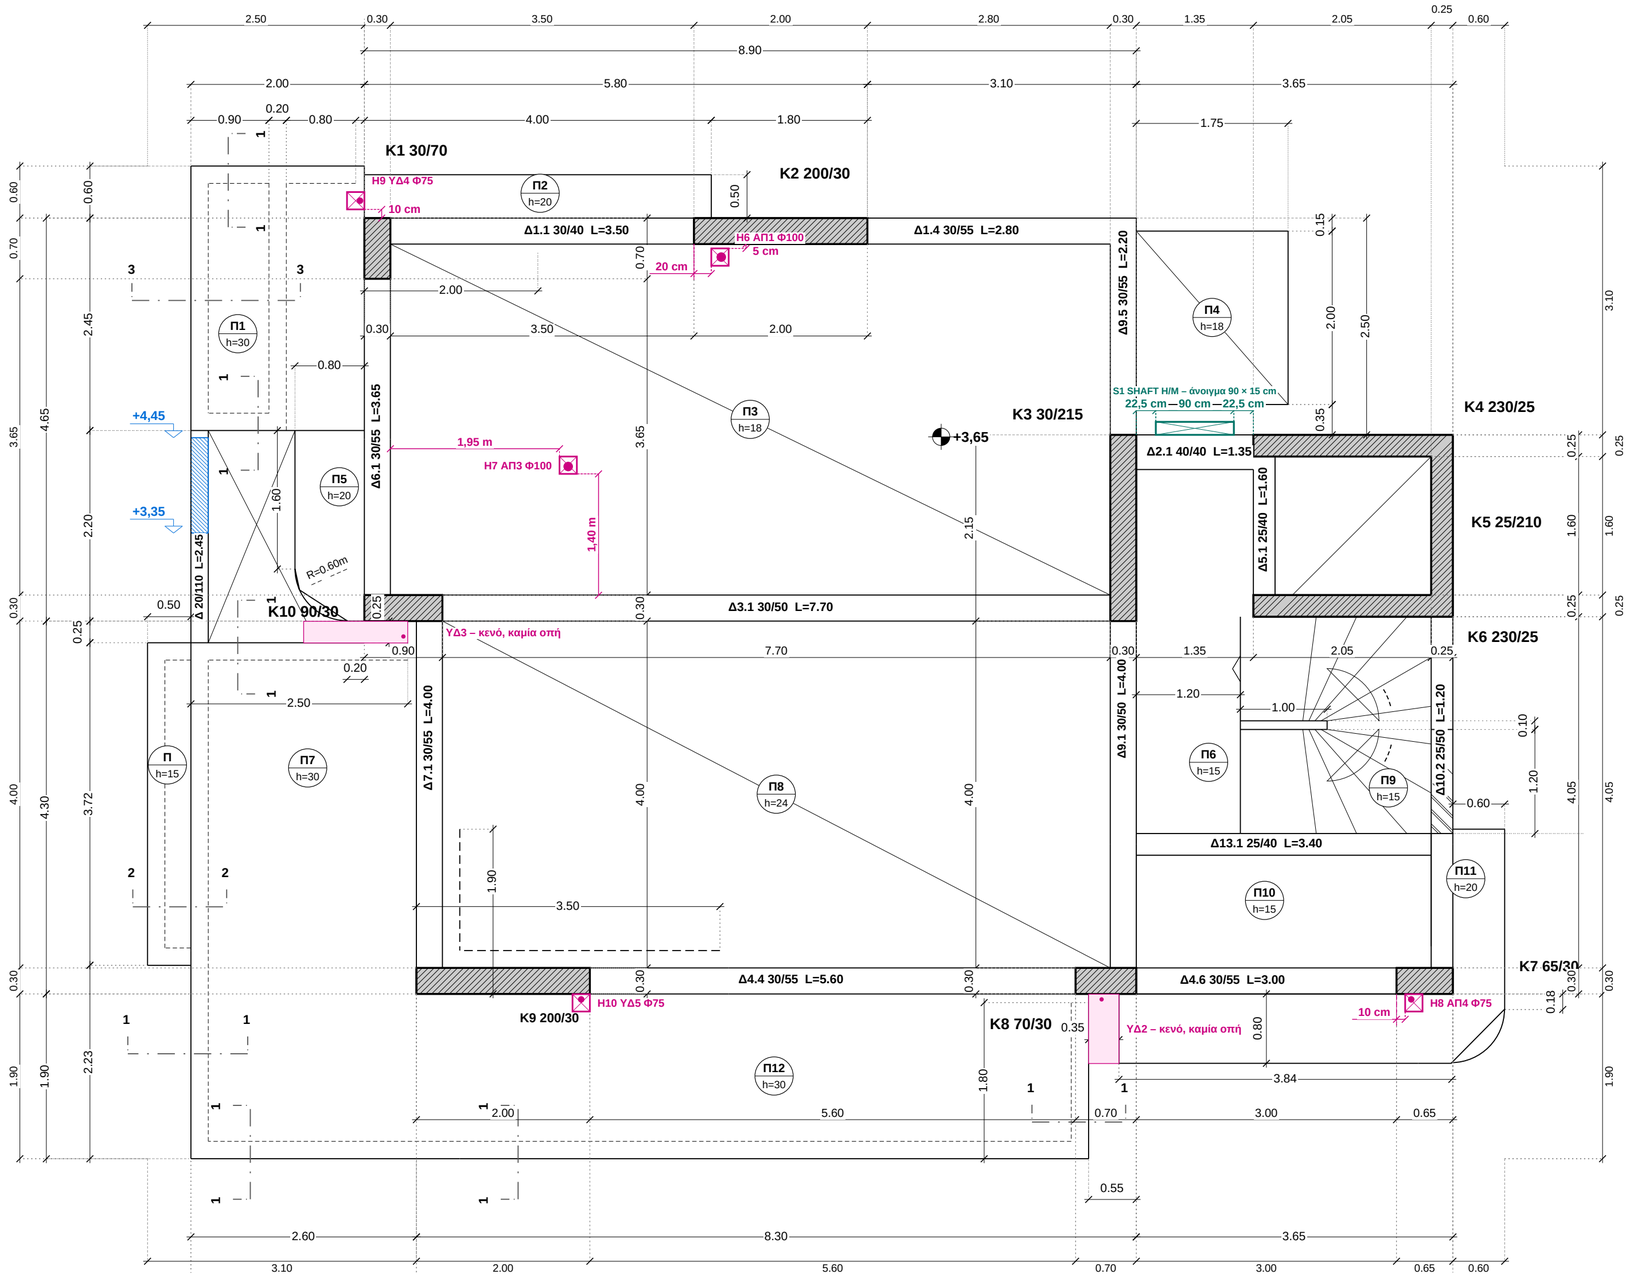



ΤΟΜΕΣ ΜΕΤΩΠΩΝ

(σκαρίφημα χωρίς κλίμακα)


ΤΟΜΗ 1-1

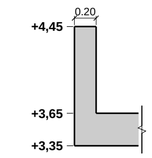

ΤΟΜΗ 2-2

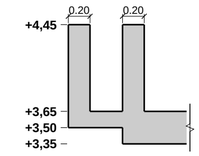

ΤΟΜΗ 3-3

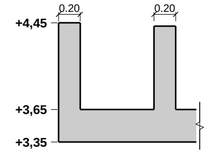

Σ3	ΞΥΛΟΤΥΠΟΣ ΕΡΓΟΤΑΞΙΟΥ **ΞΥΛΟΤΥΠΟΣ ΟΡΟΦΗΣ ΙΣΟΓΕΙΟΥ**	ΣΤΑΘΜΗ ΑΝΩ ΠΛΑΚΑΣ **+3,65**	ΚΛΙΜΑΚΑ **1:50** 0 1 2 m	ΕΡΓΟ **ΚΩΝΣΤΑΝΤΙΝΟΥΠΟΛΕΩΣ 12 & ΑΓ. ΒΑΡΒΑΡΑΣ, ΑΡΓΥΡΟΥΠΟΛΗ**	A2 – εκτύπωση 100 % R06 · 12/11/2026