

ΤΟΜΕΣ ΜΕΤΩΠΩΝ
(σκαρίφημα χωρίς κλίμακα)


ΤΟΜΗ 1-1

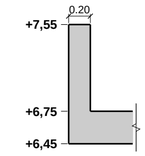


ΤΟΜΗ 2-2

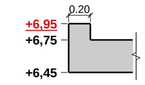

ΤΟΜΗ 3-3

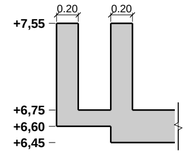

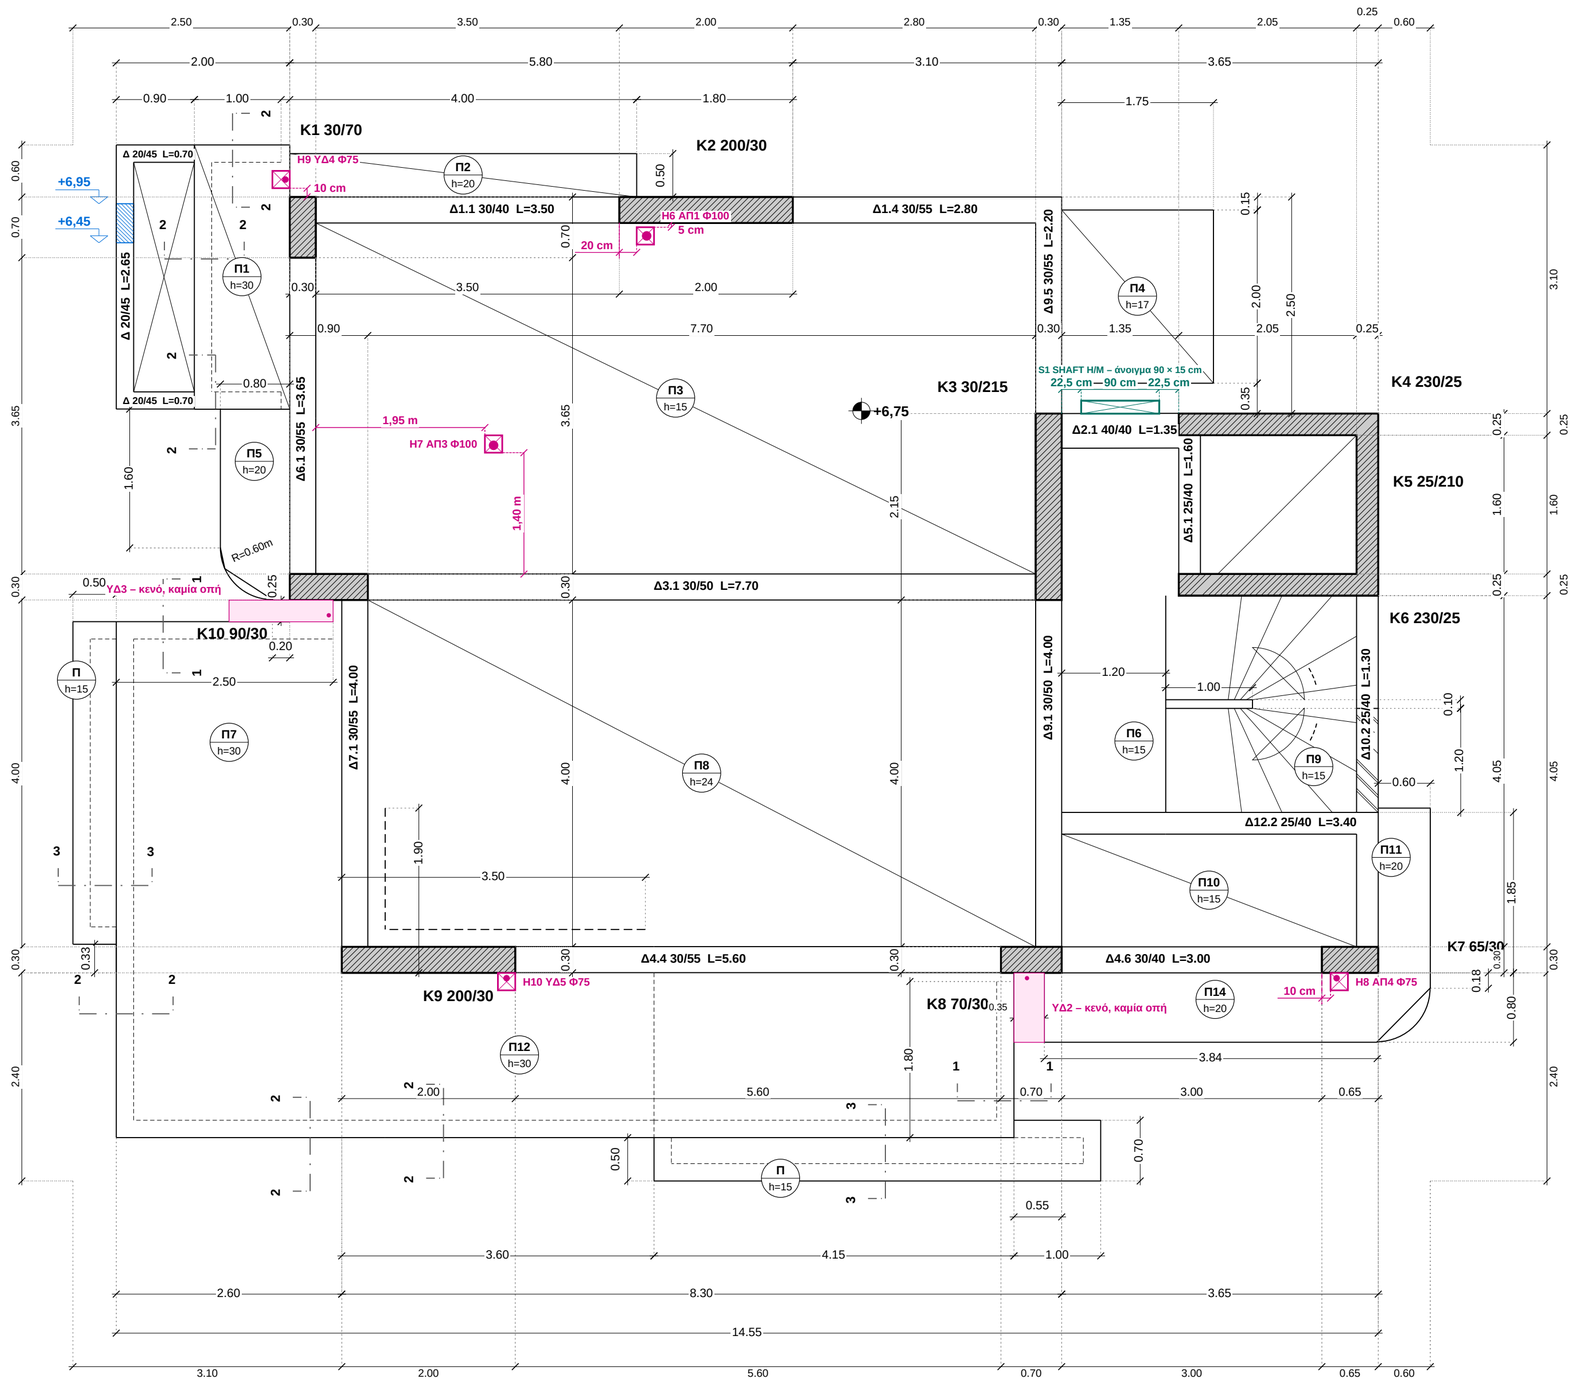

Σ4	ΞΥΛΟΤΥΠΟΣ ΕΡΓΟΤΑΞΙΟΥ	ΣΤΑΘΜΗ ΑΝΩ ΠΛΑΚΑΣ	ΚΛΙΜΑΚΑ	ΕΡΓΟ	
	ΞΥΛΟΤΥΠΟΣ ΟΡΟΦΗΣ Α΄ ΟΡΟΦΟΥ	**+6,75**	**1:50** (0 1 2 m)	**ΚΩΝΣΤΑΝΤΙΝΟΥΠΟΛΕΩΣ 12 & ΑΓ. ΒΑΡΒΑΡΑΣ, ΑΡΓΥΡΟΥΠΟΛΗ**	A2 – εκτύπωση 100 %
					R06 · 12/11/2026