
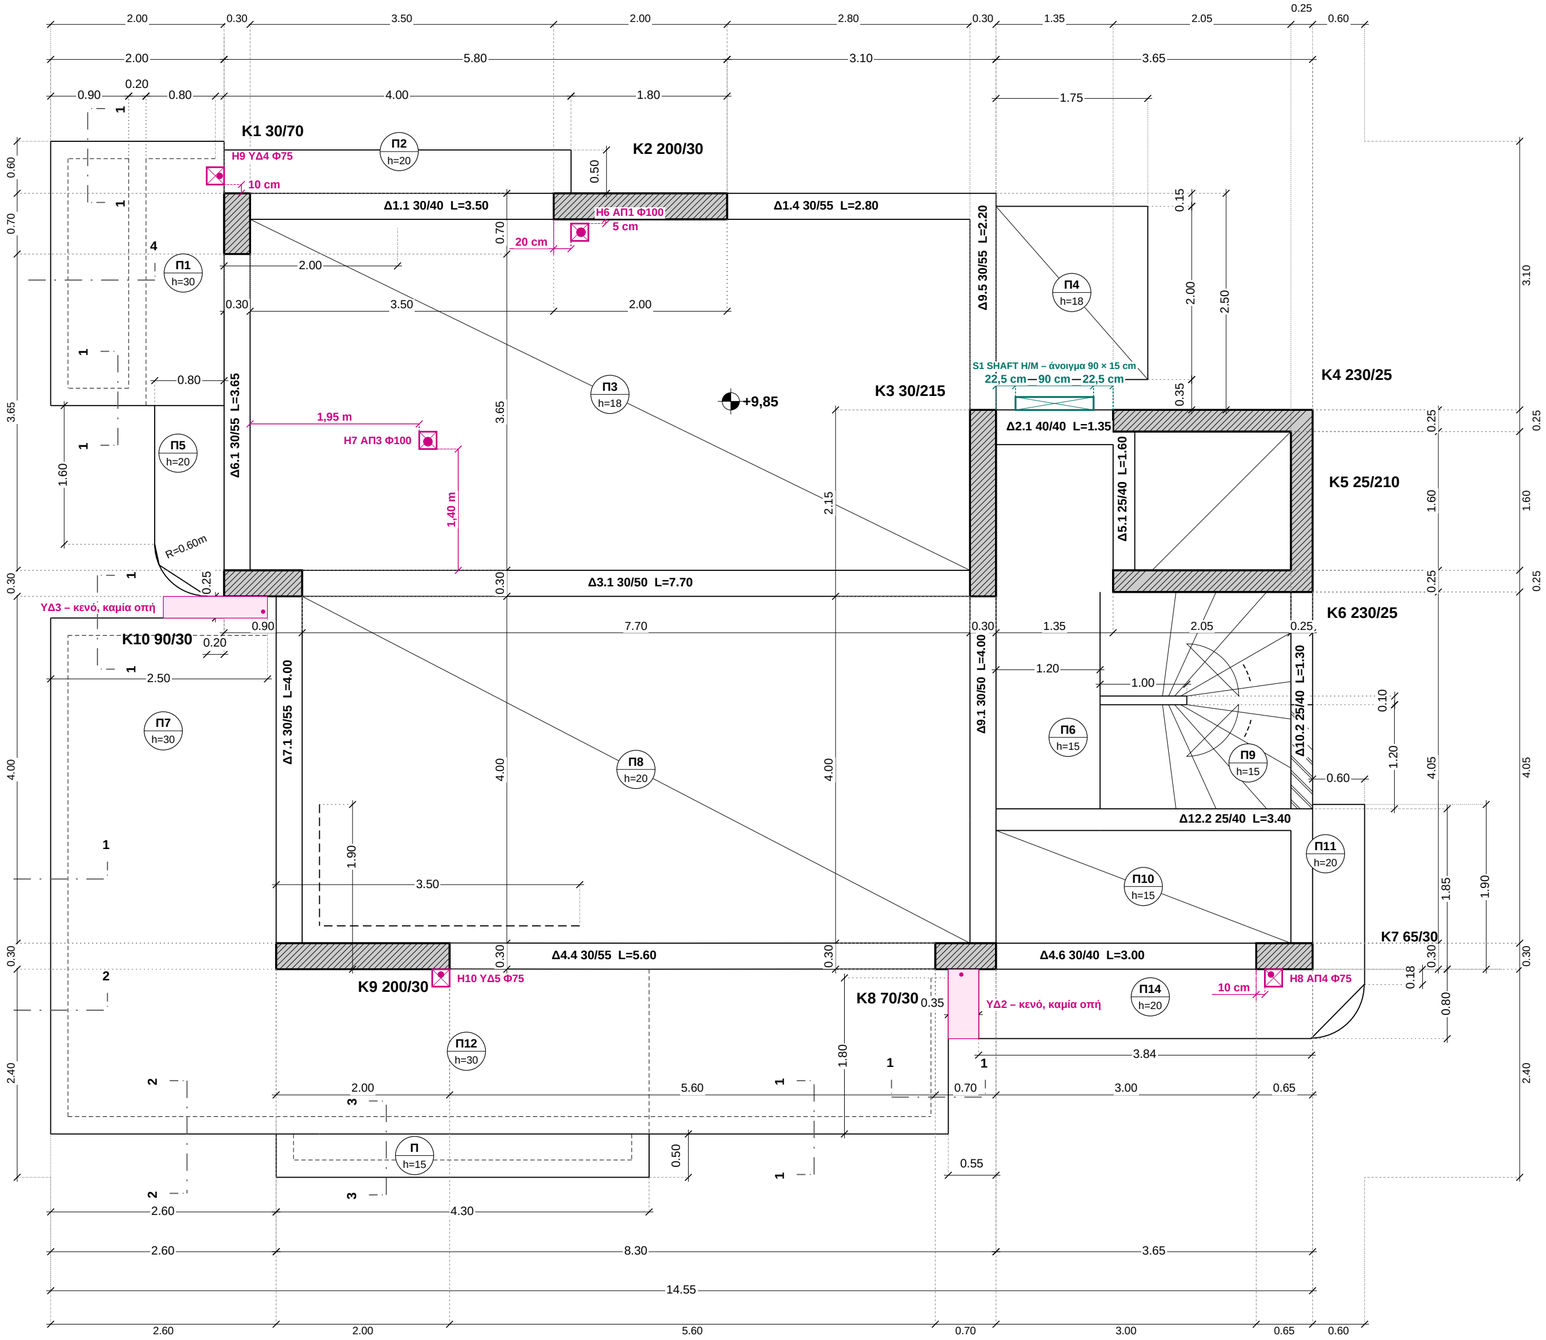



ΤΟΜΕΣ ΜΕΤΩΠΩΝ

(σκαρίφημα χωρίς κλίμακα)

ΤΟΜΗ 1-1

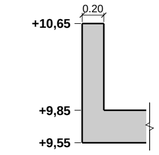


ΤΟΜΗ 2-2

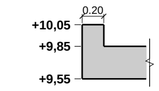

ΤΟΜΗ 3-3



ΤΟΜΗ 4-4

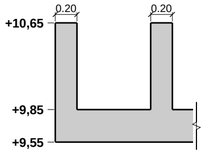

Σ5	ΞΥΛΟΤΥΠΟΣ ΕΡΓΟΤΑΞΙΟΥ	ΣΤΑΘΜΗ ΑΝΩ ΠΛΑΚΑΣ	ΚΛΙΜΑΚΑ	ΕΡΓΟ	
	ΞΥΛΟΤΥΠΟΣ ΟΡΟΦΗΣ Β΄ ΟΡΟΦΟΥ	**+9,85**	**1:50** (0 – 1 – 2 m)	**ΚΩΝΣΤΑΝΤΙΝΟΥΠΟΛΕΩΣ 12 & ΑΓ. ΒΑΡΒΑΡΑΣ, ΑΡΓΥΡΟΥΠΟΛΗ**	A2 – εκτύπωση 100 %
					R06 · 12/11/2026