


**ΤΟΜΕΣ ΜΕΤΩΠΩΝ**
(σκαρίφημα χωρίς κλίμακα)

**ΤΟΜΗ 1-1**

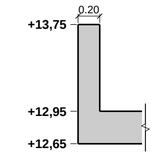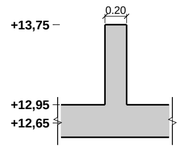


**ΤΟΜΗ 2-2**

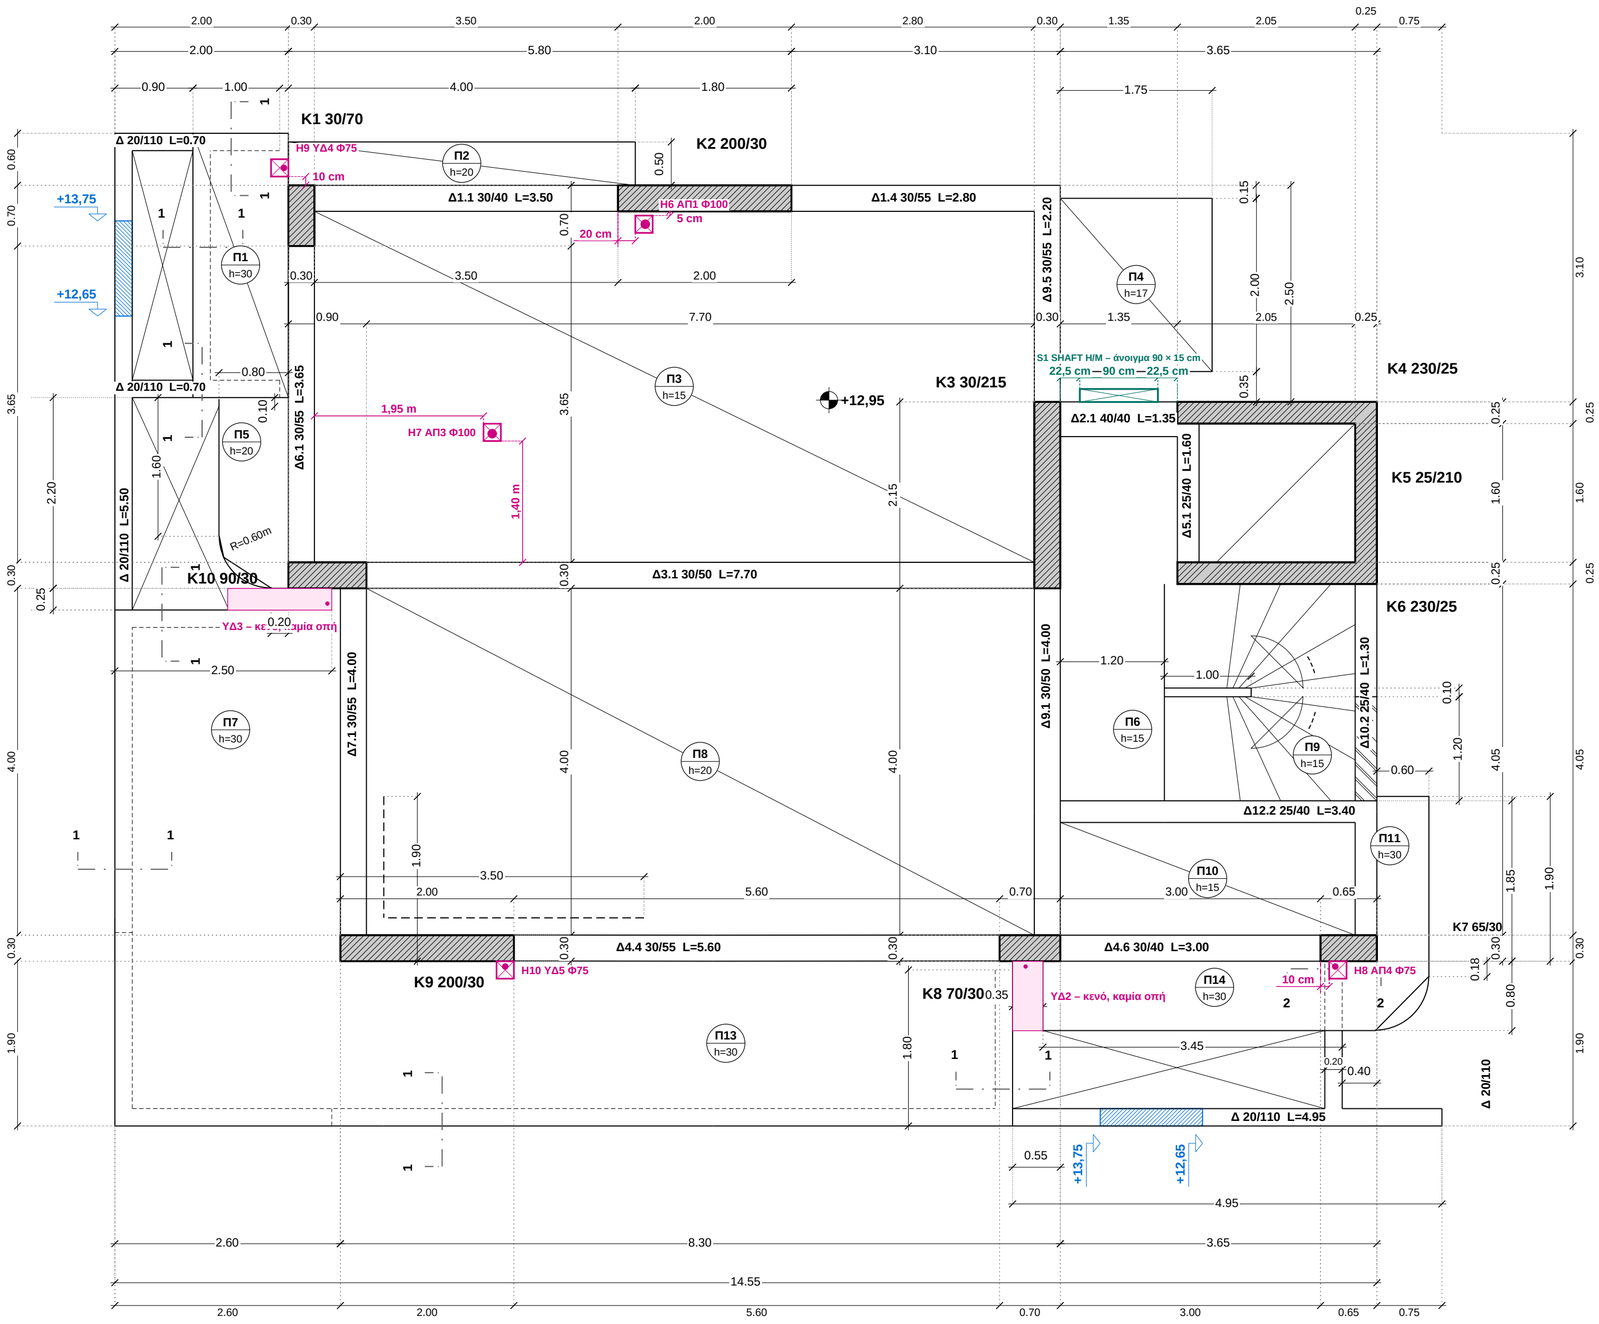


| Σ6 | ΞΥΛΟΤΥΠΟΣ ΕΡΓΟΤΑΞΙΟΥ | ΣΤΑΘΜΗ ΑΝΩ ΠΛΑΚΑΣ | ΚΛΙΜΑΚΑ | ΕΡΓΟ | |
|---|---|---|---|---|---|
| | **ΞΥΛΟΤΥΠΟΣ ΟΡΟΦΗΣ Γ΄ ΟΡΟΦΟΥ** | **+12,95** | **1:50** (0 1 2 m) | **ΚΩΝΣΤΑΝΤΙΝΟΥΠΟΛΕΩΣ 12 & ΑΓ. ΒΑΡΒΑΡΑΣ, ΑΡΓΥΡΟΥΠΟΛΗ** | A2 – εκτύπωση 100 % |
| | | | | | R06 · 12/11/2026 |